

KEALEE

design: field, deliver
4000 WHEELER ROAD — PRELIMINARY SUBDIVISION CONCEPT — LOTS 1-13
ADDRESS
4000 WHEELER ROAD
JURISDICTION
Prince George's County, Maryland
DATE
RSP-95
SCALE
C-001 — Site Development Plan — Existing, Proposed, Grading, Paving and Landscape
SHEET NO.
1 OF 3
PRELIMINARY
COORDINATES
EPCS2248
H NAD83
V NAVD83 (ft)

PLANTING AND PREPARATION	
PLANT TYPE	SITE DEVELOPMENT / FINE GRADING
DESIGNER	C-001 — Site Development Plan — Existing, Proposed, Grading, Paving and Landscape
DESIGNED BY	Kealee Professional Engineer / Surveyor (see divided responsibility)
DESIGNED BY	KEALEE SITE PLAN ENGINEER
CHECKED BY	

REVISIONS		
NO.	DATE	DESCRIPTION

INDEX OF DRAWINGS		
1	C-001	Site Development Plan — Existing, Proposed, Grading, Paving and Landscape
2	C-002	Grading and Drainage Plan
3	C-003	Grading and Drainage Plan

SITE DATA	
TRACT PARCEL ID	RSP-95
GROSS TRACT AREA	230,997 SF
LOT 1 AREA	9,362 SF
LOT 2 AREA	10,094 SF
LOT 3 AREA	10,094 SF
LOT 4 AREA	10,094 SF
LOT 5 AREA	10,094 SF
LOT 6 AREA	10,094 SF
LOT 7 AREA	10,094 SF
LOT 8 AREA	10,094 SF
LOT 9 AREA	10,094 SF
LOT 10 AREA	10,094 SF
LOT 11 AREA	10,094 SF
LOT 12 AREA	10,094 SF
LOT 13 AREA	10,094 SF
NET LOT AREA	10,094 SF
NET LOT FRONTAGE	10,094 SF
LOT 1 FRONTAGE	50 MIN
LOT 2 FRONTAGE	50 MIN
LOT 3 FRONTAGE	50 MIN
LOT 4 FRONTAGE	50 MIN
LOT 5 FRONTAGE	50 MIN
LOT 6 FRONTAGE	50 MIN
LOT 7 FRONTAGE	50 MIN
LOT 8 FRONTAGE	50 MIN
LOT 9 FRONTAGE	50 MIN
LOT 10 FRONTAGE	50 MIN
LOT 11 FRONTAGE	50 MIN
LOT 12 FRONTAGE	50 MIN
LOT 13 FRONTAGE	50 MIN
SEBACKS	REQUIRED PROVIDED
FRONT YARD	25' 25'
REAR YARD	25' 25'
COVERAGE	MAX PROPOSED
LOT COVERAGE	30% 14,004 SF
BUILDING FOOTPRINT	14,004 SF
DATUM	
HORIZONTAL	EPCS2248 NAD83
VERTICAL	NAVD83 (ft)

SITE ANALYSIS	
1. Gross lot area	230,997 SF
2. Area of dwelling	14,004 SF
3. Wetland area	NOT ESTABLISHED
4. Floodplain area	NOT ESTABLISHED
5. Net lot area	10,094 SF
6. TOTAL AREA DISTURBED	100,100 SF (AT LEAST)
7. SWM REQUIRED	YES — DISTURBANCE EXCEEDS 5,000 SF

BUILDING DATA	
LOT 1	151.77
LOT 2	151.77
LOT 3	151.77
LOT 4	151.77
LOT 5	151.77
LOT 6	151.77
LOT 7	151.77
LOT 8	151.77
LOT 9	151.77
LOT 10	151.77
LOT 11	151.77
LOT 12	151.77
LOT 13	151.77


DRAINAGE AREA COMPUTATIONS	
CATCHMENT	AREA SF IMPERV PHE Q POST Q INCREASE WQV CF
LOT 1	151.77 0.0%
LOT 2	151.77 0.0%
LOT 3	151.77 0.0%
LOT 4	151.77 0.0%
LOT 5	151.77 0.0%
LOT 6	151.77 0.0%
LOT 7	151.77 0.0%
LOT 8	151.77 0.0%
LOT 9	151.77 0.0%
LOT 10	151.77 0.0%
LOT 11	151.77 0.0%
LOT 12	151.77 0.0%
LOT 13	151.77 0.0%

SEQUENCE OF CONSTRUCTION	
1. Pre-construction meeting	1 DAY
2. Obtain necessary permits	2 DAYS
3. Install temporary construction entrance and perimeter sediment control	1 DAY
4. Rough grade the lot	2 DAYS
5. Install drainage	5 DAYS
6. Install water, sewer and storm services and the driveway	10 DAYS
7. Final grade and sod on disturbed areas	5 DAYS
8. Remove sediment control once the inspector gives written permission	1 DAY

TOTAL ESTIMATED TIME OF CONSTRUCTION: 8 MONTHS

GENERAL NOTES

1. CONTRACTOR SHALL CONTACT MISS UTILITY AT 811 A MINIMUM OF 48 HOURS BEFORE ANY EXCAVATION OR CONSTRUCTION ACTIVITIES BEGIN.

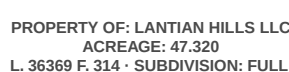


CONCRETE CURB AND GUTTER — PGC DPW&T STD. 300.01 CONCRETE SIDEWALK RAMP TYPE A — PGC DPW&T STD. 305.07

GRAPHIC SCALE — 1" = 40'


Signature _____ DATE _____

LICENSE NO. _____ EXPIRATION DATE _____

SEAL

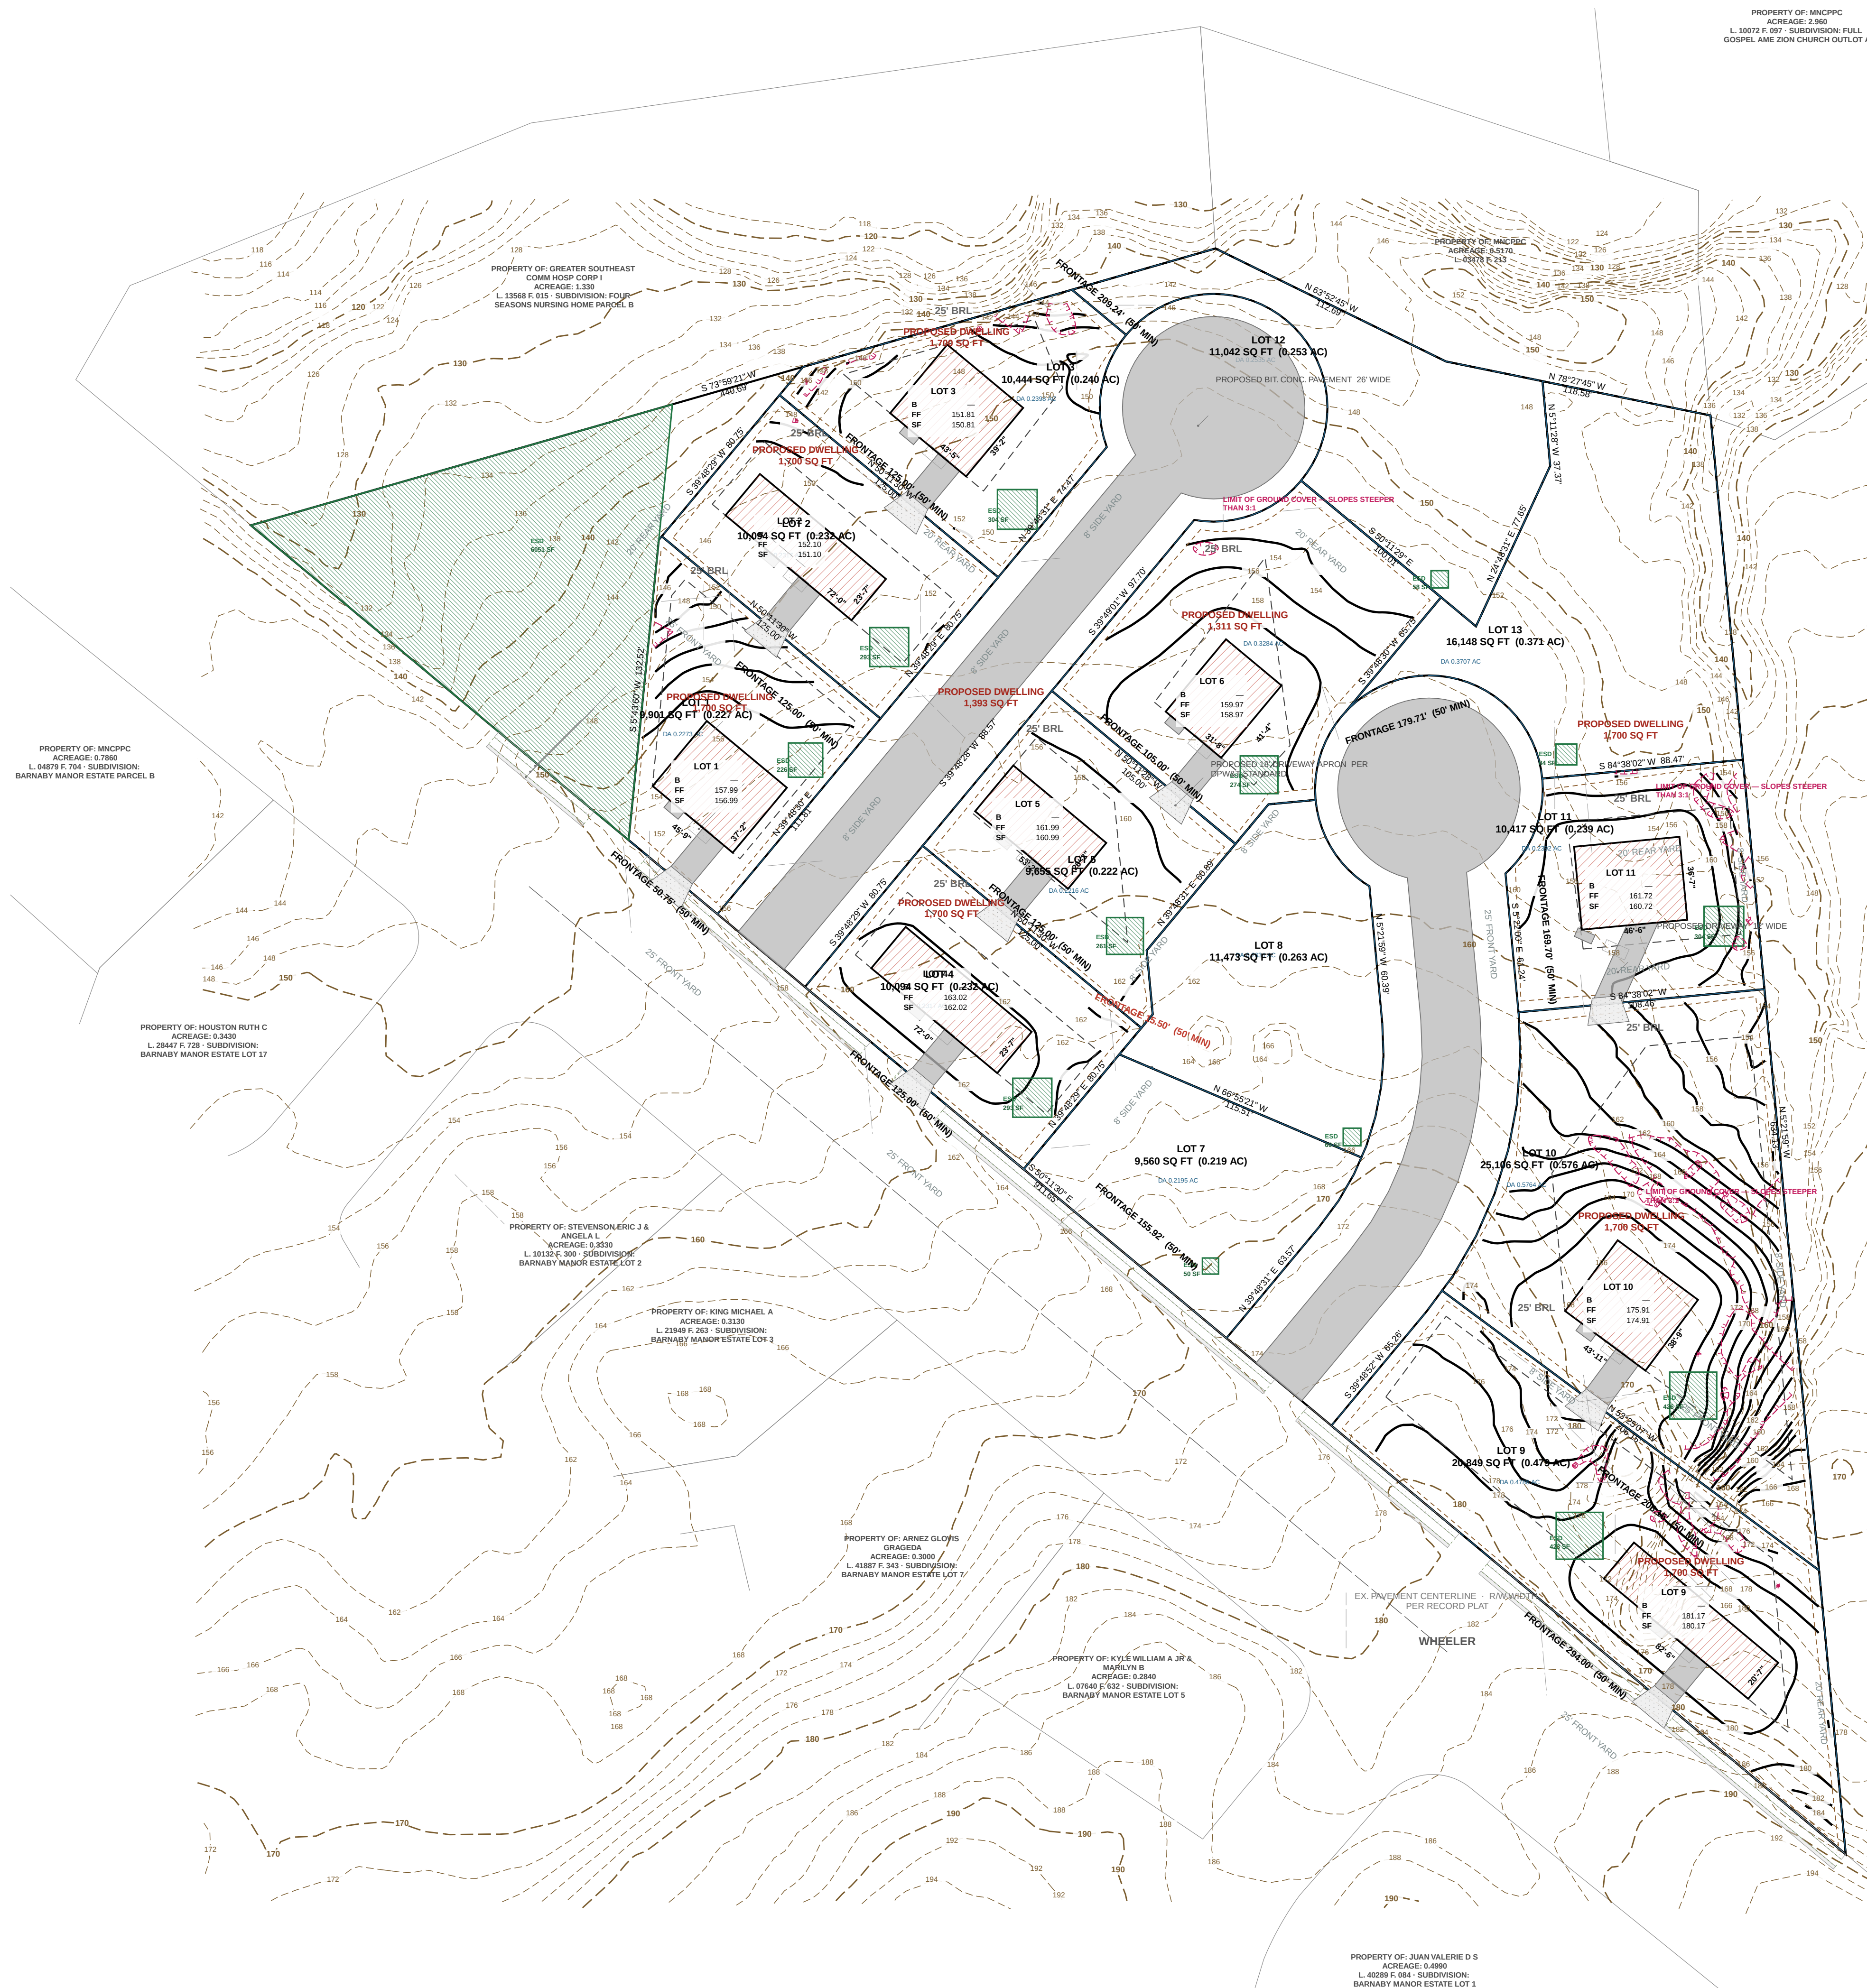

SOILS TABLE						
USDA NRCS SSURGO -- PGC Code Sys: 2-130(a)(13)						
MAP UNIT	MAP UNIT NAME	K-FACTOR	HYDRIC	HYD. GRP	DRAINAGE CLASS	
AuB	Adelphia silt loam, 2 to 5 percent slopes complex	.37	No	C	Moderately well drained	
AcA	Adelphia-Azusa complex, 0 to 2 percent slopes	.43	No	D	Somewhat poorly drained	
ADa	Adelphia-Holmdel complex, 0 to 2 percent slopes	.24	No	B/D	Somewhat poorly drained	
ADb	Adelphia-Holmdel complex, 2 to 5 percent slopes	.24	No	B/D	Somewhat poorly drained	
ADc	Adelphia-Holmdel complex, 5 to 10 percent slopes	.24	No	B/D	Somewhat poorly drained	

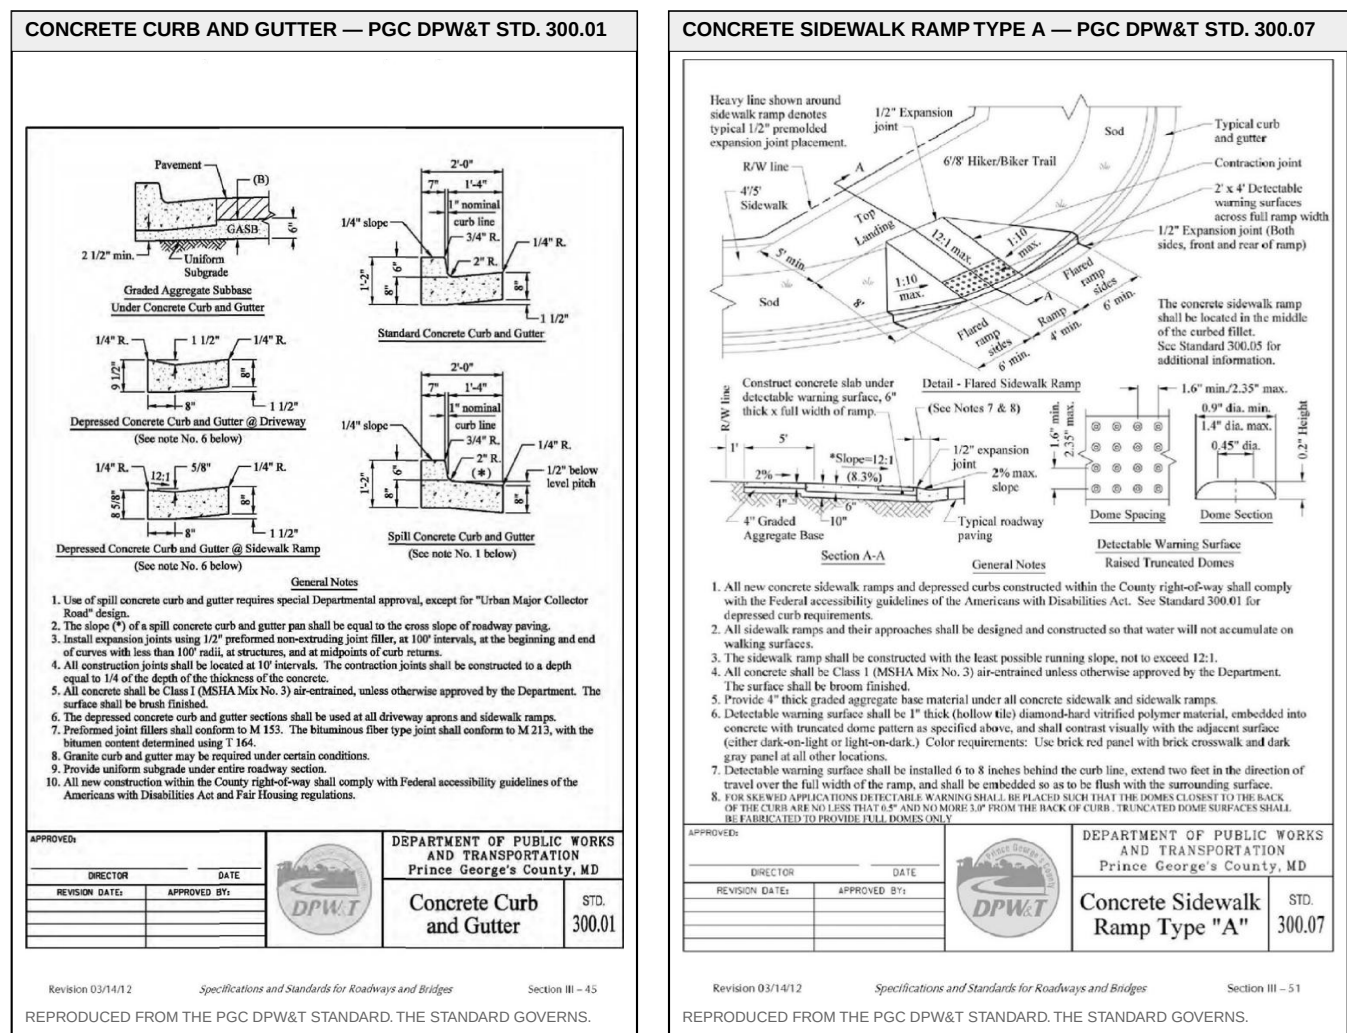

KEALEE	
design, build, deliver	
PROJECT	
4600 WHEELER ROAD — PRELIMINARY SUBDIVISION CONCEPT — LOTS 1-3	
ADDRESS	
4600 WHEELER ROAD	
APPROXIMATION	
Prince George's County, Maryland	
ZONE	
RFR-95	
PANEL	
C-400 — Grading and Drainage Plan	
SCALE	
1" = 40'	
STOWES	
PRELIMINARY	
SHEET NO.	
3 OF 3	
COORDINATES	
EPSG 2248	
NAD 83	
V NAVD83 (net)	

INDEX OF DRAWINGS

1	C-001	Site Development Plan — Existing, Proposed, Grading, Paving and
2	L-100	Landscape and Tree Canopy Plan
3	C-400	Grading and Drainage Plan

SITE DATA		
ZONE	RSF-9B	
TAX/ PARCEL ID	---	
GROSS TRACT AREA	230.097 SF	5.903 AC
LOT 1 AREA	9.303 SF	0.217 AC
LOT 2 AREA	11.474 SF	0.262 AC
LOT 3 AREA	11.474 SF	0.262 AC
LOT 4 AREA	10.094 SF	0.232 AC
LOT 5 AREA	9.805 SF	0.222 AC
LOT 6 AREA	14.304 SF	0.328 AC
LOT 7 AREA	9.500 SF	0.219 AC
LOT 8 AREA	11.474 SF	0.262 AC
LOT 9 AREA	10.094 SF	0.232 AC
LOT 10 AREA	25.100 SF	0.578 AC
LOT 11 AREA	10.417 SF	0.239 AC
LOT 12 AREA	11.474 SF	0.262 AC
LOT 13 AREA	16.148 SF	0.371 AC
NET LOT AREA	160.087 SF	3.682 AC
LOT 1 FRONTAGE	50' MIN	60.78'
LOT 2 FRONTAGE	50' MIN	125.00'
LOT 3 FRONTAGE	50' MIN	125.00'
LOT 4 FRONTAGE	50' MIN	125.00'
LOT 5 FRONTAGE	50' MIN	125.00'
LOT 6 FRONTAGE	50' MIN	150.00'
LOT 7 FRONTAGE	50' MIN	155.00'
LOT 8 FRONTAGE	50' MIN	15.00'
LOT 9 FRONTAGE	50' MIN	204.00'
LOT 10 FRONTAGE	50' MIN	204.10'
LOT 11 FRONTAGE	50' MIN	169.70'
LOT 12 FRONTAGE	50' MIN	209.24'
LOT 13 FRONTAGE	50' MIN	179.71'
SETBACKS	REQUIRED	PROVIDED
FRONT YARD	25'	25'
SIDE YARD	5'	5'
REAR YARD	30'	30'
COVERAGE	MAX	PROPOSED
LOT COVERAGE	30%	0.6%
BUILDING FOOTPRINT		14,404 SF
DATUM		
HORIZONTAL	EPGSD20AB	NAD83
VERTICAL	NAVD83 (mean)	

2. ANALYSIS

1. Census tract area

2. Area of dwelling

3. Wooded area

Impervious area

5. Net site area

6. Wetland disturbance

7. Storm frequency – Sec. 32.17(a)(6)(i)

13,600 SF

2,600 SF

NOT ESTABLISHED

10,000 SF

165,597 SF

175,500 SF

10% DISTURBANCE

EXCEEDS 500 SF

BUILDING DATA

	B	FF	SP	HT	STY
LOOT 1	157.08	157.96	156.99	20	2
LOOT 2	151.97	152.96	150.91	20	2
LOOT 3	155.48	—	155.83	150.91	20
LOOT 4	155.48	—	155.83	150.91	20
LOOT 5	155.48	—	155.83	150.91	20
LOOT 6	155.48	—	155.83	150.91	20
LOOT 7	155.48	—	155.83	150.91	20
LOOT 8	155.48	—	155.83	150.91	20
LOOT 9	155.48	—	155.83	150.91	20
LOOT 10	155.48	—	155.83	150.91	20

Legend: B=Basement; FF=Footprint; HT=Height; STY=Style; A=Column Area EXCEEDS DISTURBANCE AND HAS BEEN RECONSTRUCTED TO MEET THE SET BACK REQUIREMENT

DRAINAGE AREA COMPUTATIONS						
CATCHMENT	AREA SF	IMPRV.	PWE Q	POST Q	INCREASE	WQCF Q
LOF 1	6,902	23.1%	0.58	0.62	0.23	200
LOF 2	10,404	20.7%	0.39	0.63	0.22	239
LOF 3	10,094	20.7%	0.40	0.63	0.23	200
LOF 4	10,094	20.7%	0.39	0.63	0.22	199
LOF 5	9,950	18.0%	0.37	0.57	0.20	175
LOF 6	15,304	11.9%	0.73	0.88	0.37	347
LOF 7	9,950	18.0%	0.37	0.57	0.20	175
LOF 8	11,475	10.0%	0.66	0.64	0.04	40
LOF 9	20,340	10.0%	0.62	1.00	0.23	243
LOF 10	20,340	9.9%	0.97	1.19	0.22	261
LOF 11	10,417	23.9%	0.46	0.94	0.22	239
LOF 12	11,042	0.0%	0.63	0.43	0.00	48
LOF 13	10,410	0.0%	0.52	0.62	0.00	47
TOTAL DRAINAGE	166,082	16.8%	6.81	10.86	4.05	3,176

- | SEQUENCE OF CONSTRUCTION | | |
|--|--|----------|
| 1. Pre-construction meeting | | 1 DAY |
| 2. Obtain necessary permits | | 2 DAYS |
| 3. Notify Mass Utility at 811 at least 48 hours prior to any excavation | | 1 DAY |
| 4. Install stabilized construction entrance and perimeter sediment control | | 2 DAYS |
| 5. Rough grade the lot | | 2 DAYS |
| 6. Construct dwelling | | 6 MONTHS |
| 7. Install water, sewer and storm services and the driveway | | 10 DAYS |
| 8. Fine grade and stabilize all disturbed areas | | 5 DAYS |
| 9. Remove sediment control once the inspector gives written permission | | 1 DAY |
| TOTAL ESTIMATED DUE OF CONSTRUCTION: 8 MONTHS. | | |

GENERAL NOTES

1. EXISTING PAVEMENT SHALL BE MAINTAINED AS WELL AS POSSIBLE FOR 48 HOURS PRIOR TO ANY EXCAVATION, FILLING, OR REMOVAL OF EXISTING PAVEMENT. EXISTING PAVEMENT SHALL BE REPAIRED TO ORIGINAL CONDITION.
2. ALL EXISTING AND PROPOSED UTILITIES SHOWN PER P&C CODE SHALL BE MAINTAINED.
3. PROPOSED GRADE SHOWN EXISTING GRADE SHOWN DASHED
4. ROUGH EARTHWORK GRADES AND UTILITY ELEVATIONS SHOWN TO TOP OF CURB
5. BOUNDARY SHOWN IS THE RECORDED PLAT OF SUBDIVISION - 6000 HUNTERS HOLE - (PRELIMINARY SUBDIVISION CONCEPT) LONE STAR ASP 89-01-001-0000-0000-0000 - PARCELS 4, 5, 6, 794

- LEGEND
 - PROPERTY BOUNDARY
 - BBL – BUILDING RESTRICTION LINE
 - PROPOSED STRUCTURE
 - EXISTING CONTOUR – 2 FT INTERNAL NAVD83
 - PROPOSED CONTOUR – 2 FT INTERNAL
 - STREET CENTRELINE
 - PROPOSED PAVEMENT – DRIVEWAY / WALK
 - EASEMENT
 - SANITARY DRAIN (40C) – HEAVIEST
 - WATER SERVICE (WAC)
 - STORM DRAIN – TRUNK RCP
 - STORM – HOUSE CONNECTION TO TRUNK
 - MANHOLE MANHOLE – INVERT AND GRADE SECTION
 - RETURN WALL – TICKS ON THE RETAINED SIDE
 - LINE OF GRADE CURVE – TICKS ON THE EXPOSED SIDE
 - 100-YR FLOODPLAIN LIMIT: EXISTING GROUND – FFS-7707: WSSC DUNED, UNITED
 - 100-YR FLOODPLAIN LIMIT: 100-YR GROUND – SAME ELEVATION, DEGRADED SURFACE
 - ESD – STORMWATER PAVEMENT

PLAT OF RECORD
4600 WHEELER ROAD — PRELIMINARY SUBDIVISION CONCEPT, Zone RSMF, 2025, SE-1796. Parcel 2665579 — PARCEL A FOUR SEASONS NURSING HOME, owner of record ETHIOPIAN ORTHODOX TEWAHADO CHURCH, and 1149454, L. 89554 F. 597. PLAT A12-7290 OF RECORD, 2025 (2025-17) supersedes the GIS outline drawn here). GIS 2309656 sq ft, recorded 5 115479 ac, assessment 5.303 ac. PRELIMINARY. Outer boundary from the Prince...

- [illegible]

SEAL SIGNATURE _____ DATE _____
 LICENSE NO. _____ EXPIRATION DATE _____

REQUIRED NOTE(S) DO NOT FIT THIS SHEET: GRADING CERTIFICATE; STABILIZATION COMPLIANCE PREAMBLE; STANDARD STABILIZATION NOTE. THEY ARE REQUIRED AND ARE NOT ON ANY SHEET IN THIS SET.