

KEALEE

design, build, deliver

PROJECT
Porter Subdivision — LOT 1 & LOT 2
ADDRESS
1005 Rollins Ave
JURISDICTION
prince georges md
ZONE
RSF-65
SHEET
C-000 — Cover Sheet, Approvals and General Notes
SCALE
1" = 20'
STATUS
PRELIMINARY
SHEET NO.
1 OF 11
COORDINATES
EPSG:2248
H: NAD83
V: NAVD83 (feet)

SITE DATA		
ZONE	RSF-65	
TAX / PARCEL ID		
GROSS LOT AREA	21,826 SF	0.501 AC
LOT FRONTAGE	45' MIN	65.00'
SETBACKS	REQUIRED	PROVIDED
FRONT YARD	23'	23'
SIDE YARD	8'	8'
REAR YARD	20'	20'
COVERAGE	MAX	PROPOSED
LOT COVERAGE	35%	5.5%
BUILDING FOOTPRINT	—	1,196 SF
DATUM		
HORIZONTAL	EPSG:2248	NAD83
VERTICAL	NAVD83 (feet)	

SITE ANALYSIS	
1. Gross tract area	21,826 SF
2. Area of dwelling	1,196 SF
3. Wooded area	NOT ESTABLISHED
4. Floodplain area	NOT ESTABLISHED
5. Net tract area	21,826 SF
6. TOTAL AREA DISTURBED	NOT QUANTIFIED

SEQUENCE OF CONSTRUCTION	
1. Preconstruction meeting	1 DAY
2. Obtain necessary permits	2 DAYS
3. Notify Miss Utility at B11 at least 48 hours prior to any excavation	1 DAY
4. Construct stabilized construction entrance and perimeter sediment control	2 DAYS
5. Rough grade, construct dwelling, utilities and driveway	12 MONTHS
6. Fine grade and stabilize all disturbed areas	1 DAY
7. Remove sediment control devices when written permission has been granted	1 DAY
TOTAL ESTIMATED TIME OF CONSTRUCTION: 12 MONTHS	

- GENERAL NOTES
- CONTRACTOR SHALL CONTACT MISS UTILITY AT B11 A MINIMUM OF 48 HOURS PRIOR TO ANY EXCAVATION.
 - ALL EXISTING AND PROPOSED UTILITIES SHOWN PER PCC CODE SEC. 32-106.
 - PROPOSED GRADE SHOWN SOLID; EXISTING GRADE SHOWN DASHED.
 - ROUGH EARTHWORK GRADES AND UTILITY ELEVATIONS SHOWN TO TENTHS OF A FOOT.
 - BOUNDARY SHOWN IS COMPILED JURISDICTION GIS, NOT A BOUNDARY SURVEY.

PLAT OF RECORD
PORTER SUBDIVISION, LOTS 1 AND 2 — Plat Book PM 231, p. 50 (M&A, C2381, 19950), Sewer Pressure (SP) Elevation District, Prince Georges County, Maryland. The Map To: GLE B2, 200 May 202 SE 06, Zone R-65 as recorded (RSP-65 under the 2022 (revised), Scale 1" = 20', November 2007 M, NSPC Record File S-20623, State of Maryland Maryland State Plane Coordinate System (NAD 83), Lot 1 = 9,599 sq ft (0.2203 ac), Lot 2 = 8,008 sq ft (0.1838 ac), 4,219 sq ft (0.0969 ac) dedicated to public use.

- NOTES OF RECORD
- Development of the property shall be in accordance with the approved Stormwater Management Control Plan (L220-2006-00), or any approved revision thereto.
 - Approval of this plat is based upon a reasonable expectation that public water and sewer service will be available when needed, and is conditioned on fulfilling all of the Washington Suburban Sanitary Commission authorization DA 4519 Z-05 commitments.
 - The applicant, his heirs, successors and/or assignees shall utilize an existing driveway design, constructed per OPWA standards and requirements. Separate, standard residential driveway aprons shall be provided along Rollins Avenue. If deemed appropriate by OPWA upon the issuance of street construction permits.
 - ADJOINING PROPERTIES, per the recorded plat, LOTS 13, 14 AND 15 (Addition to Pleasant Park, Plat Book VJ 185, The PG) — northwest, LOT 12 (Addition to Pleasant Park, Plat Book VJ 185, The PG) — southwest, OUTLOT A (Addition to Pleasant Park, Plat Book VJ 185, The PG) — northwest, JEAN M. YOUNG L. 1, 6, 7, 8,

KEALEE

design, build, deliver

PROJECT
Porter Subdivision — LOT 1 & LOT 2
ADDRESS
1005 Rollins Ave
JURISDICTION
prince georges md
ZONE
RSF-65
SHEET
C-100 — Existing Conditions and Boundary Plan
SCALE
1" = 20'
STATUS
PRELIMINARY
SHEET NO.
2 OF 11
COORDINATES
EPSG:2248
H: NAD83
V: NAVD83 (feet)

SITE DATA		
ZONE	RSF-65	
TAX / PARCEL ID		
GROSS LOT AREA	21,826 SF	0.501 AC
LOT FRONTAGE	45' MIN	65.00'
SETBACKS	REQUIRED	PROVIDED
FRONT YARD	23'	23'
SIDE YARD	8'	8'
REAR YARD	20'	20'
COVERAGE	MAX	PROPOSED
LOT COVERAGE	35%	5.5%
BUILDING FOOTPRINT	—	1,196 SF
DATUM		
HORIZONTAL	EPSG:2248	NAD83
VERTICAL	NAVD83 (feet)	

SITE ANALYSIS	
1. Gross tract area	21,826 SF
2. Area of dwelling	1,196 SF
3. Wooded area	NOT ESTABLISHED
4. Floodplain area	NOT ESTABLISHED
5. Net tract area	21,826 SF
6. TOTAL AREA DISTURBED	NOT QUANTIFIED

SEQUENCE OF CONSTRUCTION	
1. Preconstruction meeting	1 DAY
2. Obtain necessary permits	2 DAYS
3. Notify Miss Utility at B11 at least 48 hours prior to any excavation	1 DAY
4. Construct stabilized construction entrance and perimeter sediment control	2 DAYS
5. Rough grade, construct dwelling, utilities and driveway	12 MONTHS
6. Fine grade and stabilize all disturbed areas	1 DAY
7. Remove sediment control devices when written permission has been granted	1 DAY
TOTAL ESTIMATED TIME OF CONSTRUCTION: 12 MONTHS	

- GENERAL NOTES
- CONTRACTOR SHALL CONTACT MISS UTILITY AT B11 A MINIMUM OF 48 HOURS PRIOR TO ANY EXCAVATION.
 - ALL EXISTING AND PROPOSED UTILITIES SHOWN PER PCC CODE SEC. 32-106.
 - PROPOSED GRADE SHOWN SOLID; EXISTING GRADE SHOWN DASHED.
 - ROUGH EARTHWORK GRADES AND UTILITY ELEVATIONS SHOWN TO TENTHS OF A FOOT.
 - BOUNDARY SHOWN IS COMPILED JURISDICTION GIS, NOT A BOUNDARY SURVEY.

PLAT OF RECORD
PORTER SUBDIVISION, LOTS 1 AND 2 — Plat Book PM 231, p. 50 (M&A, C2381, 19950), Sewer Pressure (SP) Elevation District, Prince Georges County, Maryland. The Map To: GFE B2, 200 May 202 SE 06, Zone R-65 as recorded (RSP-65 under the 2022 (revised), Scale 1" = 20', November 2007 M, NSPC Record File S-20523), State of Maryland, Maryland State Plane Coordinate System (NAD 83). Lot 1 = 9,599 sq ft (0.2203 ac); Lot 2 = 8,008 sq ft (0.1838 ac); 4,219 sq ft (0.0969 ac) dedicated to public use.

- NOTES OF RECORD
- Development of the property shall be in accordance with the approved Stormwater Management Concept Plan (2/20/2006-05), or any approved revision thereto.
 - Approval of this plat is based upon a reasonable expectation that public water and sewer service will be available when needed, and is conditioned on fulfilling all of the Washington Suburban Sanitary Commission authorization DA 4519 Z-05 commitments.
 - The applicant, his heirs, successors and/or assignees shall utilize an existing driveway design, constructed per OPWA standards and requirements. Separate, standard residential driveway aprons shall be provided along Rollins Avenue. If deemed appropriate by OPWA upon the issuance of street construction permits.
 - ADJOINING PROPERTIES, per the recorded plat, LOTS 13, 14 AND 15 (Addition to Pleasant Park, Plat Book VJ 185, The PG) — northwest, LOT 12 (Addition to Pleasant Park, Plat Book VJ 185, The PG) — southwest, OUTLOT A (Addition to Pleasant Park, Plat Book VJ 185, The PG) — northwest, JEAN M. YOUNG L. 5, 6, 7, 8, 9 — northwest, MARYLAND W. DAVIS L. 1, 2, 3, 4, 5, 6, 7, 8 — northwest, Rollins Avenue, PATRICIA L. PIERRE L.L. 1, 2, 3, 4, 5, 6, 7, 8, 9, 10 — across Rollins Avenue, VALLE GARCIA SUBDIVISION (P.B. WWW 15, P. 41) — across Rollins Avenue, EDWARD B. ROLLINS, TRUSTEE, ET AL. (LJ 1278 F-105) — east.
- PUE — Public Utility Easement — RPF — Iron Pipe Found — For Public Water and Sewer Only
The surveyor certifies, under declaration and approval signatures of the recorded plat are NOT reproduced here; they shall be the responsibility of the surveyor.

LEGEND	
-----	PROPERTY BOUNDARY
-----	BRL — BUILDING RESTRICTION LINE
-----	PROPOSED STRUCTURE
-----	EXISTING CONTOUR — PGATLAS 2 FT (2023), NAVD83
-----	STREET CENTRELINE
-----	PROPOSED PAVEMENT — DRIVEWAY / WALK
-----	EASEMENT



PRINCE GEORGE'S COUNTY SOIL CONSERVATION DISTRICT APPROVAL
SEDIMENT CONTROL, GRADING, SOILS & DRAINAGE

SIGNATURE DATE

DPE SITEROAD PLAN REVIEW DIVISION APPROVAL

SIGNATURE DATE

REVISIONS
— NONE —

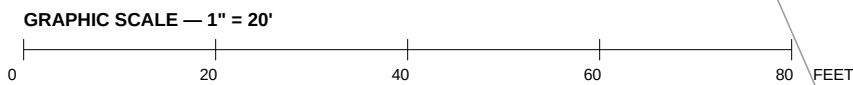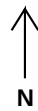

KEALEE

design, build, deliver

PROJECT
Porter Subdivision — LOT 1 & LOT 2
ADDRESS
1005 Rollins Ave
JURISDICTION
prince georges md
ZONE
RSF-65
SHEET
C-200 — Overall Site and Zoning Plan
SCALE
1" = 20'
STATUS
PRELIMINARY
SHEET NO.
3 OF 11
COORDINATES
EPSG:2248
H: NAD83
V: NAVD83 (feet)

SITE DATA		
ZONE	RSF-65	
TAX / PARCEL ID		
GROSS LOT AREA	21,826 SF	0.501 AC
LOT FRONTAGE	45' MIN	65.00'
SETBACKS	REQUIRED	PROVIDED
FRONT YARD	23'	23'
SIDE YARD	8'	8'
REAR YARD	20'	20'
COVERAGE	MAX	PROPOSED
LOT COVERAGE	35%	5.5%
BUILDING FOOTPRINT	—	1,196 SF
DATUM		
HORIZONTAL	EPSG:2248	NAD83
VERTICAL	NAVD83 (feet)	

SITE ANALYSIS	
1. Gross tract area	21,826 SF
2. Area of dwelling	1,196 SF
3. Wooded area	NOT ESTABLISHED
4. Floodplain area	NOT ESTABLISHED
5. Net tract area	21,826 SF
6. TOTAL AREA DISTURBED	NOT QUANTIFIED

SEQUENCE OF CONSTRUCTION	
1. Preconstruction meeting	1 DAY
2. Obtain necessary permits	2 DAYS
3. Notify Miss Utility at B11 at least 48 hours prior to any excavation	1 DAY
4. Construct stabilized construction entrance and perimeter sediment control	2 DAYS
5. Rough grade, construct dwelling, utilities and driveway	12 MONTHS
6. Fine grade and stabilize all disturbed areas	1 DAY
7. Remove sediment control devices when written permission has been granted	1 DAY
TOTAL ESTIMATED TIME OF CONSTRUCTION: 12 MONTHS	

- GENERAL NOTES
- CONTRACTOR SHALL CONTACT MISS UTILITY AT B11 A MINIMUM OF 48 HOURS PRIOR TO ANY EXCAVATION.
 - ALL EXISTING AND PROPOSED UTILITIES SHOWN PER PCC CODE SEC. 32-106.
 - PROPOSED GRADE: SHOWN SOLID; EXISTING GRADE: SHOWN DASHED.
 - ROUGH EARTHWORK GRADES AND UTILITY ELEVATIONS SHOWN TO TENTHS OF A FOOT.
 - BOUNDARY SHOWN IS COMPILED JURISDICTION GIS, NOT A BOUNDARY SURVEY.

PLAT OF RECORD
PORTER SUBDIVISION, LOTS 1 AND 2 — Plat Book PM 231, p. 50 (M&A, C2381, 19950), Sewer Pressure (SP) Elevation District, Prince Georges County, Maryland, Tax Map 73, GFE B3, 200 May 202 SE 06, Zone R-65 as recorded (RSP-65 under the 2022 rewrite), Scale 1" = 20', November 2007 M, NSPC Record File S-0823, House of Delegates Maryland State Plane Coordinate System (NAD 83), Lot 1 = 9,599 sq ft (0.2203 ac), Lot 2 = 8,008 sq ft (0.1838 ac), 4,219 sq ft (0.0969 ac) dedicated to public use.

- NOTES OF RECORD
- Development of the property shall be in accordance with the approved Stormwater Management Concept Plan (1220-2006-00), or any approved revision thereto.
 - Approval of this plat is based upon a reasonable expectation that public water and sewer service will be available when needed, and is conditioned on fulfilling all of the Washington Suburban Sanitary Commission authorization DA 4519 Z-05 commitments.
 - The applicant, his heirs, successors and/or assignees shall utilize an existing driveway design, constructed per OPWA's standards and requirements. Separate, standard residential driveway aprons shall be provided along Rollins Avenue. If deemed appropriate by OPWA, upon the issuance of street construction permits.
 - ADJOINING PROPERTIES, per the recorded plat, LOTS 13, 14 AND 15 (Addition to Pleasant Park, Plat Book VJ 185, Plat 78) — northwest, LOT 12 (Addition to Pleasant Park, Plat Book VJ 185, Plat 78) — southwest, OUTLOT A (Addition to Pleasant Park, Plat Book VJ 185, Plat 78) — northwest, JEAN M. YOUNG L. 1, 6377-1-089 — northwest, MARYLAND W. DAVIS L. 1, 1401-1-047 — north, Rollins Avenue, PATRICIA L. PIERRE L.L. 1, 1786-1-721 — across Rollins Avenue, VALLE GARCIA SUBDIVISION (P.B. WWW 15, P. 41) — across Rollins Avenue, EDWARD B. ROLLINS, TRUSTEE, ET AL, L. 1, 1791-1-105 — east.
- PUE — Public Utility Easement IPE — Iron Pipe Found For Public Water and Sewer Only
The surveyor certifies, under declaration and approval signatures of the recorded plat and NOT reproduced here, they shall be the responsibility of the surveyor.

LEGEND	
-----	PROPERTY BOUNDARY
-----	BRL — BUILDING RESTRICTION LINE
-----	PROPOSED STRUCTURE
-----	EXISTING CONTOUR — PGATLAS 2 FT (2023), NAVD83
-----	STREET CENTRELINE
-----	PROPOSED PAVEMENT — DRIVEWAY / WALK
-----	EASEMENT



PRINCE GEORGE'S COUNTY SOIL CONSERVATION DISTRICT APPROVAL
SEDIMENT CONTROL, GRADING, SOILS & DRAINAGE

SIGNATURE _____ DATE _____

DPE SITEROAD PLAN REVIEW DIVISION APPROVAL

SIGNATURE _____ DATE _____

REVISIONS
— NONE —

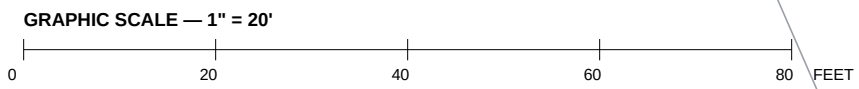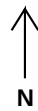

KEALEE

design, build, deliver

PROJECT
Porter Subdivision — LOT 1 & LOT 2
ADDRESS
1005 Rollins Ave
JURISDICTION
prince georges md
ZONE
RSF-65
SHEET
C-300 — Demolition Plan
SCALE
1" = 20'
STATUS
PRELIMINARY
SHEET NO.
4 OF 11
COORDINATES
EPSG:2248
H: NAD83
V: NAVD83 (feet)

SITE DATA		
ZONE	RSF-65	
TAX / PARCEL ID		
GROSS LOT AREA	21,826 SF	0.501 AC
LOT FRONTAGE	45' MIN	65.00'
SETBACKS	REQUIRED	PROVIDED
FRONT YARD	23'	23'
SIDE YARD	8'	8'
REAR YARD	20'	20'
COVERAGE	MAX	PROPOSED
LOT COVERAGE	35%	5.5%
BUILDING FOOTPRINT	—	1,196 SF
DATUM		
HORIZONTAL	EPSG:2248	NAD83
VERTICAL	NAVD83 (feet)	

SITE ANALYSIS	
1. Gross tract area	21,826 SF
2. Area of dwelling	1,196 SF
3. Wooded area	NOT ESTABLISHED
4. Floodplain area	NOT ESTABLISHED
5. Net tract area	21,826 SF
6. TOTAL AREA DISTURBED	NOT QUANTIFIED

SEQUENCE OF CONSTRUCTION	
1. Preconstruction meeting	1 DAY
2. Obtain necessary permits	2 DAYS
3. Notify Miss Utility at B11 at least 48 hours prior to any excavation	1 DAY
4. Construct stabilized construction entrance and perimeter sediment control	2 DAYS
5. Rough grade, construct dwelling, utilities and driveway	12 MONTHS
6. Fine grade and stabilize all disturbed areas	1 DAY
7. Remove sediment control devices when written permission has been granted	1 DAY
TOTAL ESTIMATED TIME OF CONSTRUCTION: 12 MONTHS	

- GENERAL NOTES
- CONTRACTOR SHALL CONTACT MISS UTILITY AT B11 A MINIMUM OF 48 HOURS PRIOR TO ANY EXCAVATION.
 - ALL EXISTING AND PROPOSED UTILITIES SHOWN PER PCC CODE SEC. 32-106.
 - PROPOSED GRADE SHOWN SOLID; EXISTING GRADE SHOWN DASHED.
 - ROUGH EARTHWORK GRADES AND UTILITY ELEVATIONS SHOWN TO TENTHS OF A FOOT.
 - BOUNDARY SHOWN IS COMPILED JURISDICTION GIS, NOT A BOUNDARY SURVEY.

PLAT OF RECORD
PORTER SUBDIVISION, LOTS 1 AND 2 — Plat Book PM 231, p. 50 (M&A, C2381, 19950), Sewer Pressure (SP) Elevation District, Prince Georges County, Maryland. The Map To: G16 B2, 200 May 202 SE 06, Zone R-65 as recorded (RSP-65 under the 2022 (revised), Scale 1" = 20', November 2007 M, NSPC Record No. S-20523), State of Maryland, Maryland State Plane Coordinate System (NAD 83). Lot 1 = 9,599 sq ft (0.2203 ac); Lot 2 = 8,008 sq ft (0.1838 ac); 4,219 sq ft (0.0969 ac) dedicated to public use.

- NOTES OF RECORD
- Development of the property shall be in accordance with the approved Stormwater Management Concept Plan (1220-2006-00), or any approved revision thereto.
 - Approval of this plat is based upon a reasonable expectation that public water and sewer service will be available when needed, and is conditioned on fulfilling all of the Washington Suburban Sanitary Commission authorization DA 4519 Z-05 commitments.
 - The applicant, his heirs, successors and/or assignees shall utilize an existing driveway design, constructed per OPWA standards and requirements. Separate, standard residential driveway aprons shall be provided along Rollins Avenue. If deemed appropriate by OPWA upon the issuance of street construction permits.
 - ADJOINING PROPERTIES, per the recorded plat, LOTS 13, 14 AND 15 (Addition to Pleasant Park, Plat Book VJ 185, The 70) — northwest, LOT 12 (Addition to Pleasant Park, Plat Book VJ 185, The 70) — southwest, OUTLOT A (Addition to Pleasant Park, Plat Book VJ 185, The 70) — northwest, JEAN M. YOUNG L. 1, 6, 7, 8, 9, 10 — northwest, MARYLAND W. DAVIS L. 1, 2, 3, 4, 5, 6, 7, 8, 9, 10 — northwest, PATRICIA L. PIERRE L. 1, 2, 3, 4, 5, 6, 7, 8, 9, 10 — northwest, ROLLINS AVENUE, PATRICIA L. PIERRE L. 1, 2, 3, 4, 5, 6, 7, 8, 9, 10 — northwest, ROLLINS AVENUE, EDWARD B. ROLLINS, TRUSTEE ET AL. (LJ 1278 F-105) — northwest.
- PUE — Public Utility Easement IPE — Iron Pipe Found For Public Water and Sewer Only
- The surveyor certifies, under declaration and approval signatures of the recorded plat are NOT reproduced here; they shall be the responsibility of the surveyor.

LEGEND	
-----	PROPERTY BOUNDARY
-----	BRL — BUILDING RESTRICTION LINE
-----	PROPOSED STRUCTURE
-----	EXISTING CONTOUR — PGATLAS 2 FT (2023), NAVD83
-----	STREET CENTRELINE
-----	PROPOSED PAVEMENT — DRIVEWAY / WALK
-----	EASEMENT



PRINCE GEORGE'S COUNTY SOIL CONSERVATION DISTRICT APPROVAL
SEDIMENT CONTROL, GRADING, SOILS & DRAINAGE

SIGNATURE _____ DATE _____

DPE SITEROAD PLAN REVIEW DIVISION APPROVAL

SIGNATURE _____ DATE _____

REVISIONS
— NONE —

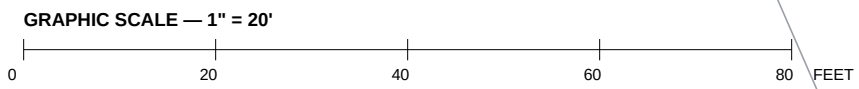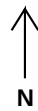

KEALEE

design, build, deliver

PROJECT
Porter Subdivision — LOT 1 & LOT 2
ADDRESS
1005 Rollins Ave
JURISDICTION
prince georges md
ZONE
RSF-65
SHEET
C-400 — Grading and Drainage Plan
SCALE
1" = 20'
STATUS
PRELIMINARY
SHEET NO.
5 OF 11
COORDINATES
EPSG:2248
H: NAD83
V: NAVD83 (feet)

SITE DATA		
ZONE	RSF-65	
TAX / PARCEL ID		
GROSS LOT AREA	21,826 SF	0.501 AC
LOT FRONTAGE	45' MIN	65.00'
SETBACKS	REQUIRED	PROVIDED
FRONT YARD	23'	23'
SIDE YARD	8'	8'
REAR YARD	20'	20'
COVERAGE	MAX	PROPOSED
LOT COVERAGE	35%	5.5%
BUILDING FOOTPRINT	—	1,196 SF
DATUM		
HORIZONTAL	EPSG:2248	NAD83
VERTICAL	NAVD83 (feet)	

SITE ANALYSIS	
1. Gross tract area	21,826 SF
2. Area of dwelling	1,196 SF
3. Wooded area	NOT ESTABLISHED
4. Floodplain area	NOT ESTABLISHED
5. Net tract area	21,826 SF
6. TOTAL AREA DISTURBED	NOT QUANTIFIED

SEQUENCE OF CONSTRUCTION	
1. Pre-constructed meeting	1 DAY
2. Obtain necessary permits	2 DAYS
3. Notify Miss Utility at B11 at least 48 hours prior to any excavation	1 DAY
4. Construct stabilized construction entrance and perimeter sediment control	2 DAYS
5. Rough grade, construct dwelling, utilities and driveway	12 MONTHS
6. Fine grade and stabilize all disturbed areas	1 DAY
7. Remove sediment control devices when written permission has been granted	1 DAY
TOTAL ESTIMATED TIME OF CONSTRUCTION: 12 MONTHS	

- GENERAL NOTES
- CONTRACTOR SHALL CONTACT MISS UTILITY AT B11 A MINIMUM OF 48 HOURS PRIOR TO ANY EXCAVATION.
 - ALL EXISTING AND PROPOSED UTILITIES SHOWN PER PGC CODE SEC. 32-106.
 - PROPOSED GRADE: SHOWN SOLID; EXISTING GRADE: SHOWN DASHED.
 - ROUGH EARTHWORK GRADES AND UTILITY ELEVATIONS SHOWN TO TENTHS OF A FOOT.
 - BOUNDARY SHOWN IS COMPILED JURISDICTION GIS, NOT A BOUNDARY SURVEY.

PLAT OF RECORD
PORTER SUBDIVISION, LOTS 1 AND 2 — Plat Book PM 231, p. 50 (M&A, C2381, 19950), Sewer Pressure (SP) Elevation Station: Prince Georges County, Maryland, Map 75, GFE 82, 200 May 202 SE 06, Zone R 65 as recorded (RSP 65 under the 2022 (revised), Scale 1" = 20', November 2007 M, NSPC Record File S-0823), State of Maryland State Plane Coordinate System (NAD 83), Lot 1 = 9,589 sq ft (0.2203 ac), Lot 2 = 8,008 sq ft (0.1838 ac), 4,219 sq ft (0.0969 ac) dedicated to PUBLIC USE.

- NOTES OF RECORD
- Development of the property shall be in accordance with the approved Stormwater Management Control Plan (1220-2000-00), or any approved revision thereto.
 - Approval of this plan is based upon a reasonable expectation that public water and sewer service will be available when needed, and is conditioned on fulfilling all of the Washington Suburban Sanitary Commission authorization DA 4519 2-06 commitments.
 - The applicant, his heirs, successors and/or assignees shall utilize an existing driveway design, constructed per OPWA standards and requirements. Separate, standard residential driveway aprons shall be provided along Rollins Avenue, if deemed appropriate by OPWA, upon the issuance of street construction permits.
 - ADJOINING PROPERTIES, per the recorded plat, LOTS 13, 14 AND 15 (Addition to Pleasant Park, Plat Book VJ 185, Plat 78) — northwest, LOT 12 (Addition to Pleasant Park, Plat Book VJ 185, Plat 78) — southwest, OUTLOT A (Addition to Pleasant Park, Plat Book VJ 185, Plat 78) — northwest, JEAN M. YOUNG L 14577 1-89 — northwest, MARYLAND W. DAVIS L 11415 P 47 — northwest, Rollins Avenue, PATRICIA L. PIERRE L 11786 F 721 — across Rollins Avenue, VALLE GARCIA SUBDIVISION (PA, WWW 15 P 41) — across Rollins Avenue, EDWARD B. ROLLINS, TRUSTEE ET AL L 13787 F 105 —, PUE — Public Utility Easement — RPF — Iron Pipe Found — For Public Water and Sewer Only.
- The surveyor certifies, under declaration and approval signatures of the recorded plat and NOT reproduced here, they shall be the consequences of the plat and NOT the surveyor.

LEGEND	
-----	PROPERTY BOUNDARY
- - - - -	BRL — BUILDING RESTRICTION LINE
-----	PROPOSED STRUCTURE
-----	EXISTING CONTOUR — PGATLAS 2 FT (2023), NAVD83
-----	STREET CENTRELINE
-----	PROPOSED PAVEMENT — DRIVEWAY / WALK
-----	EASEMENT

PRINCE GEORGE'S COUNTY SOIL CONSERVATION DISTRICT APPROVAL

SEDIMENT CONTROL, GRADING, SOILS & DRAINAGE

SIGNATURE _____ DATE _____

DPE SITEROAD PLAN REVIEW DIVISION APPROVAL

SIGNATURE _____ DATE _____

GRADING CERTIFICATE

I HEREBY CERTIFY THAT THIS PLAN CONFORMS TO THE REQUIREMENTS OF SUBTITLE 32, DIVISION 2 OF THE CODE OF PRINCE GEORGE'S COUNTY WATER RESOURCES PROTECTION AND GRADING CODE, AND THAT I OR MY STAFF HAVE INSPECTED THIS SITE, AND THAT DRAINAGE FLOWS FROM UPHILL PROPERTIES ONTO THIS SITE, AND FROM THIS SITE ONTO DOWNHILL PROPERTIES, HAVE BEEN ADDRESSED IN SUBSTANTIAL ACCORDANCE WITH APPLICABLE CODES, SIGNED, SEALED AND DATED BY A PROFESSIONAL ENGINEER LICENSED IN THE STATE OF MARYLAND.

Prinace Georges County DPE, Site Rough Grading Design Review Checklist, Item A-10

STABILIZATION COMPLIANCE PREAMBLE
Stabilization practices on all projects must be in compliance with the requirements of COMAR 26.17.01 by January 9, 2013, regardless of when an erosion and sediment control plan was approved. COMAR 26.17.01.09(C), Grandfathering of approved plans.

STANDARD STABILIZATION NOTE
Following initial soil disturbance or re-disturbance, permanent or temporary stabilization must be completed within: a) Three (3) calendar days as to the surface of all perimeter dikes, swales, ditches, perimeter slopes, and all slopes steeper than 3 horizontal to 1 vertical (3:1); and b) Seven (7) calendar days as to all other disturbed or graded areas on the project site not under active grading.

2013 Maryland Erosion and Sedimentation for Soil Erosion and Sediment Control, "Standard Stabilization Note" (adopted by COMAR 26.17.01.09A(2)).

REVISIONS
— NONE —

GRAPHIC SCALE — 1" = 20'

0 20 40 60 80 FEET

GRAPHIC SCALE — 1" = 20'

0 20 40 60 80 FEET

KEALEE

design, build, deliver

PROJECT
Porter Subdivision — LOT 1 & LOT 2
ADDRESS
1005 Rollins Ave
JURISDICTION
prince georges md
ZONE
RSF-65
SHEET
C-500 — Utility Plan
SCALE
1" = 20'
STATUS
PRELIMINARY
SHEET NO.
6 OF 11
COORDINATES
EPSG:2248
H: NAD83
V: NAVD83 (feet)

SITE DATA		
ZONE	RSF-65	
TAX / PARCEL ID		
GROSS LOT AREA	21,826 SF	0.501 AC
LOT FRONTAGE	45' MIN	65.00'
SETBACKS	REQUIRED	PROVIDED
FRONT YARD	23'	23'
SIDE YARD	8'	8'
REAR YARD	20'	20'
COVERAGE	MAX	PROPOSED
LOT COVERAGE	35%	5.5%
BUILDING FOOTPRINT	—	1,196 SF
DATUM		
HORIZONTAL	EPSG:2248	NAD83
VERTICAL	NAVD83 (feet)	

SITE ANALYSIS	
1. Gross tract area	21,826 SF
2. Area of dwelling	1,196 SF
3. Wooded area	NOT ESTABLISHED
4. Floodplain area	NOT ESTABLISHED
5. Net tract area	21,826 SF
6. TOTAL AREA DISTURBED	NOT QUANTIFIED

SEQUENCE OF CONSTRUCTION	
1. Preconstruction meeting	1 DAY
2. Obtain necessary permits	2 DAYS
3. Notify Miss Utility at B11 at least 48 hours prior to any excavation	1 DAY
4. Construct stabilized construction entrance and perimeter sediment control	2 DAYS
5. Rough grade, construct dwelling, utilities and driveway	12 MONTHS
6. Fine grade and stabilize all disturbed areas	1 DAY
7. Remove sediment control devices when written permission has been granted	1 DAY
TOTAL ESTIMATED TIME OF CONSTRUCTION: 12 MONTHS	

- GENERAL NOTES**
- CONTRACTOR SHALL CONTACT MISS UTILITY AT B11 A MINIMUM OF 48 HOURS PRIOR TO ANY EXCAVATION.
 - ALL EXISTING AND PROPOSED UTILITIES SHOWN PER PCC CODE SEC. 32-106.
 - PROPOSED GRADE SHOWN SOLID; EXISTING GRADE SHOWN DASHED.
 - ROUGH EARTHWORK GRADES AND UTILITY ELEVATIONS SHOWN TO TENTHS OF A FOOT.
 - BOUNDARY SHOWN IS COMPILED JURISDICTION GIS, NOT A BOUNDARY SURVEY.

PLAT OF RECORD
PORTER SUBDIVISION, LOTS 1 AND 2 — Plat Book PM 231, p. 50 (M&A, C2381, 19950), Sewer Pressure (SP) Elevation District, Prince Georges County, Maryland. The Map To: GFE B2, 200 May 202 SE 06, Zone R-65 as recorded (RSP-65 under the 2022 (revised), Scale 1" = 20', November 2007 M, NSPC Record No. S-20623), State of Maryland, Maryland State Plane Coordinate System (NAD 83). Lot 1 = 9,589 sq ft (0.2203 ac); Lot 2 = 8,008 sq ft (0.1838 ac); 4,219 sq ft (0.0969 ac) dedicated to public use.

- NOTES OF RECORD**
- Development of the property shall be in accordance with the approved Stormwater Management Control Plan (1220-2006-00), or any approved revision thereto.
 - Approval of this plat is based upon a reasonable expectation that public water and sewer service will be available when needed, and is conditioned on fulfilling all of the Washington Suburban Sanitary Commission authorization DA 4519 Z-05 commitments.
 - The applicant, his heirs, successors and/or assignees shall utilize an existing driveway design, constructed per OPWA standards and requirements. Separate, standard residential driveway aprons shall be provided along Rollins Avenue. If deemed appropriate by OPWA upon the issuance of street construction permits.
 - ADJOINING PROPERTIES, per the recorded plat, LOTS 13, 14 AND 15 (Addition to Pleasant Park, Plat Book VJ 185, The 78) — northwest, LOT 12 (Addition to Pleasant Park, Plat Book VJ 185, The 78) — southwest, OUTLOT A (Addition to Pleasant Park, Plat Book VJ 185, The 78) — northwest, JEAN M. YOUNG L. 1, 6, 7, 8, 9, 10 — northwest, MARYLAND W. DAVIS L. 1, 2, 3, 4, 5, 6, 7, 8, 9, 10 — northwest, PATRICIA L. PIERRE L. 1, 2, 3, 4, 5, 6, 7, 8, 9, 10 — northwest, ROLLINS AVENUE, VALLE CARSON SUBDIVISION (P&S, WWW L. P. 41) — across Rollins Avenue, EDWARD B. ROLLINS, TRUSTEE, ET AL. L. 1, 2, 3, 4, 5, 6, 7, 8, 9, 10 — northwest, PUE — Public Utility Easement — PUE — Iron Pipe Found — For Public Water and Sewer Only

The surveyor certifies, under declaration and approval signatures of the recorded plat are NOT reproduced here; they shall be the responsibility of the surveyor.

LEGEND

- PROPERTY BOUNDARY
BRL — BUILDING RESTRICTION LINE
PROPOSED STRUCTURE
EXISTING CONTOUR — PGATLAS 2 FT (2023), NAVD83
STREET CENTRELINE
PROPOSED PAVEMENT — DRIVEWAY / WALK
EASEMENT


PRINCE GEORGE'S COUNTY SOIL CONSERVATION DISTRICT APPROVAL
SEDIMENT CONTROL, GRADING, SOILS & DRAINAGE

SIGNATURE DATE

DPE SITEROAD PLAN REVIEW DIVISION APPROVAL

SIGNATURE DATE

REVISIONS
NONE

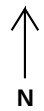

GRAPHIC SCALE — 1" = 20'
0 20 40 60 80 FEET

KEALEE

design, build, deliver

PROJECT
Porter Subdivision — LOT 1 & LOT 2
ADDRESS
1005 Rollins Ave
JURISDICTION
prince georges md
ZONE
RSF-65
SHEET
C-600 — Stormwater Management Plan
SCALE
1" = 20'
STATUS
PRELIMINARY
SHEET NO.
7 OF 11
COORDINATES
EPSG:2248
H: NAD83
V: NAVD83 (feet)

SITE DATA		
ZONE	RSF-65	
TAX / PARCEL ID		
GROSS LOT AREA	21,826 SF	0.501 AC
LOT FRONTAGE	45' MIN	65.00'
SETBACKS	REQUIRED	PROVIDED
FRONT YARD	23'	23'
SIDE YARD	8'	8'
REAR YARD	20'	20'
COVERAGE	MAX	PROPOSED
LOT COVERAGE	35%	5.5%
BUILDING FOOTPRINT	—	1,196 SF
DATUM		
HORIZONTAL	EPSG:2248	NAD83
VERTICAL	NAVD83 (feet)	

SITE ANALYSIS	
1. Gross tract area	21,826 SF
2. Area of dwelling	1,196 SF
3. Wooded area	NOT ESTABLISHED
4. Floodplain area	NOT ESTABLISHED
5. Net tract area	21,826 SF
6. TOTAL AREA DISTURBED	NOT QUANTIFIED

SEQUENCE OF CONSTRUCTION	
1. Preconstruction meeting	1 DAY
2. Obtain necessary permits	2 DAYS
3. Notify Miss Utility at B11 at least 48 hours prior to any excavation	1 DAY
4. Construct stabilized construction entrance and perimeter sediment control	2 DAYS
5. Rough grade, construct dwelling, utilities and driveway	12 MONTHS
6. Fine grade and stabilize all disturbed areas	1 DAY
7. Remove sediment control devices when written permission has been granted	1 DAY
TOTAL ESTIMATED TIME OF CONSTRUCTION: 12 MONTHS	

- GENERAL NOTES
- CONTRACTOR SHALL CONTACT MISS UTILITY AT B11 A MINIMUM OF 48 HOURS PRIOR TO ANY EXCAVATION.
 - ALL EXISTING AND PROPOSED UTILITIES SHOWN PER PCC CODE SEC. 32-106.
 - PROPOSED GRADE SHOWN SOLID; EXISTING GRADE SHOWN DASHED.
 - ROUGH EARTHWORK GRADES AND UTILITY ELEVATIONS SHOWN TO TENTHS OF A FOOT.
 - BOUNDARY SHOWN IS COMPILED JURISDICTION GIS, NOT A BOUNDARY SURVEY.

PLAT OF RECORD
PORTER SUBDIVISION, LOTS 1 AND 2 — Plat Book PM 231, p. 50 (M&A, C2381, 19950), Sewer Pressure (SP) Elevation District, Prince Georges County, Maryland. The Map 73, G16 B3, 200 May 202 SE 06, Zone R-65 as recorded (RSP-65 under the 2022 (revised), Scale 1" = 20', November 2007 M, NSPC Record File S-20623, State of Maryland, Maryland State Plane Coordinate System (NAD 83), Lot 1 = 9,599 sq ft (0.2203 ac), Lot 2 = 8,008 sq ft (0.1838 ac), 4,219 sq ft (0.0969 ac) dedicated to public use.

- NOTES OF RECORD
- Development of the property shall be in accordance with the approved Stormwater Management Concept Plan (12/20/2006/00), or any approved revision thereto.
 - Approval of this plat is based upon a reasonable expectation that public water and sewer service will be available when needed, and is conditioned on fulfilling all of the Washington Suburban Sanitary Commission authorization DA 4519 Z-05 commitments.
 - The applicant, his heirs, successors and/or assignees shall utilize an existing driveway design, constructed per OPWA standards and requirements. Separate, standard residential driveway aprons shall be provided along Rollins Avenue. If deemed appropriate by OPWA upon the issuance of street construction permits.
 - ADJOINING PROPERTIES, per the recorded plat, LOTS 13, 14 AND 15 (Addition to Pleasant Park, Plat Book VJ 185, The PG) — northwest, LOT 12 (Addition to Pleasant Park, Plat Book VJ 185, The PG) — southwest, OUTLOT A (Addition to Pleasant Park, Plat Book VJ 185, Plat 78) — northwest, JEAN M. YOUNG L. 5, 677 (S&B) — northwest, MARY AND W. DAVIS L. 1, 145 (P & T) — across Rollins Avenue, PATRICIA L. PIERRE L.L. 1, 1786 (F721) — across Rollins Avenue, VALLE GARCIA SUBDIVISION (P&B, WWW L.S. P-41) — across Rollins Avenue, EDWARD B. ROLLINS, TRUSTEE, ET AL. L. 1, 1776 (F-105) —, PUE — Public Utility Easement — RPF — Iron Pipe Found — For Public Water and Sewer Only
- The surveyor certifies, under declaration and approval signatures of the recorded plat are NOT reproduced here; they shall be the responsibility of the surveyor.

- LEGEND
- PROPERTY BOUNDARY
 - BRL — BUILDING RESTRICTION LINE
 - PROPOSED STRUCTURE
 - EXISTING CONTOUR — PGATLAS 2 FT (2023), NAVD83
 - STREET CENTRELINE
 - PROPOSED PAVEMENT — DRIVEWAY / WALK
 - EASEMENT



PRINCE GEORGE'S COUNTY SOIL CONSERVATION DISTRICT APPROVAL
SEDIMENT CONTROL, GRASSING, SOILS & DRAINAGE

SIGNATURE DATE

DPE SITEROAD PLAN REVIEW DIVISION APPROVAL

SIGNATURE DATE

REVISIONS
— NONE —

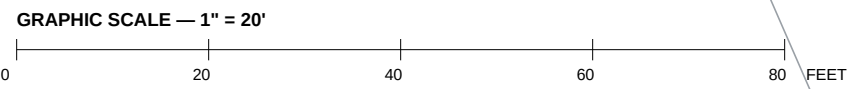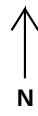

KEALEE

design, build, deliver

PROJECT
Porter Subdivision — LOT 1 & LOT 2
ADDRESS
1005 Rollins Ave
JURISDICTION
prince georges md
ZONE
RSF-65
SHEET
C-700 — Sediment and Erosion Control Plan
SCALE
1" = 20'
STATUS
PRELIMINARY
SHEET NO.
8 OF 11
COORDINATES
EPSG:2248
H: NAD83
V: NAVD83 (feet)

SITE DATA		
ZONE	RSF-65	
TAX / PARCEL ID		
GROSS LOT AREA	21,826 SF	0.501 AC
LOT FRONTAGE	45' MIN	65.00'
SETBACKS	REQUIRED	PROVIDED
FRONT YARD	23'	23'
SIDE YARD	8'	8'
REAR YARD	20'	20'
COVERAGE	MAX	PROPOSED
LOT COVERAGE	35%	5.5%
BUILDING FOOTPRINT	—	1,196 SF
DATUM		
HORIZONTAL	EPSG:2248	NAD83
VERTICAL	NAVD83 (feet)	

SITE ANALYSIS	
1. Gross tract area	21,826 SF
2. Area of dwelling	1,196 SF
3. Wooded area	NOT ESTABLISHED
4. Floodplain area	NOT ESTABLISHED
5. Net tract area	21,826 SF
6. TOTAL AREA DISTURBED	NOT QUANTIFIED

SEQUENCE OF CONSTRUCTION	
1. Preconstruction meeting	1 DAY
2. Obtain necessary permits	2 DAYS
3. Notify Min. Utility at 811 at least 48 hours prior to any excavation	1 DAY
4. Construct stabilized construction entrance and perimeter sediment control	2 DAYS
5. Rough grade, construct dwelling, utilities and driveway	12 MONTHS
6. Fine grade and stabilize all disturbed areas	1 DAY
7. Remove sediment control devices when written permission has been granted	1 DAY
TOTAL ESTIMATED TIME OF CONSTRUCTION: 12 MONTHS	

- GENERAL NOTES
- CONTRACTOR SHALL CONTACT MISS UTILITY AT 811 A MINIMUM OF 48 HOURS PRIOR TO ANY EXCAVATION.
 - ALL EXISTING AND PROPOSED UTILITIES SHOWN PER PCC CODE SEC. 32-106.
 - PROPOSED GRADE: SHOWN SOLID; EXISTING GRADE: SHOWN DASHED.
 - ROUGH EARTHWORK GRADES AND UTILITY ELEVATIONS SHOWN TO TENTHS OF A FOOT.
 - BOUNDARY SHOWN IS COMPILED JURISDICTION GIS, NOT A BOUNDARY SURVEY.

PLAT OF RECORD
PORTER SUBDIVISION, LOTS 1 AND 2 — Plat Book PM 231, p. 50 (M&A, C2383, 19950), Sewer Pressure (SP) Elevation Sheet, Prince Georges County, Maryland, Tax Map 73, GSE 63, 200 May 202 SE 06, Zone R-65 as recorded (RSP-65 under the 2022 rewrite), Scale: 1" = 20', November 2007 M. NSPC Record File S-08233, Sheet of bearings, Maryland State Plane Coordinate System (NAD 83), Lot 1 = 9,589 sq ft (0.2203 ac), Lot 2 = 8,008 sq ft (0.1838 ac), 4,219 sq ft (0.0969 ac) dedicated to PARKWAY.

NOTES OF RECORD
1. Development of this property shall be in accordance with the approved Stormwater Management Control Plan 4-220-2000-00, or any approved revision thereto.
2. Approval of this plat is based upon a reasonable expectation that public water and sewer service will be available when needed, and is conditioned on fulfilling all of the Washington Suburban Sanitary Commission authorization DA 4519 Z-05 commitments.
3. The applicant, his heirs, successors and/or assignees shall utilize an existing driveway design, constructed per OPWA standards and requirements. Separate, standard residential driveway aprons shall be provided along Rollins Avenue. If deemed appropriate by OPWA upon the issuance of street construction permits.
4. ADDJONING PROPERTIES, per the recorded plat, LOTS 13, 14 AND 15 (Addition to Pleasant Park, Plat Book VJ 185, Plat 78) — northwest, LOT 12 (Addition to Pleasant Park, Plat Book VJ 185, Plat 78) — southwest, OUTLOT A (Addition to Pleasant Park, Plat Book VJ 185, Plat 78) — northwest, JEAN M. YOUNG L. 5-877 (S-889) — northwest, MARY AND W. DAVIS L. 1-145 (P-47) — north, Rollins Avenue, PATRICIA L. PIERRE L.L. 1-786 (F-721) — across Rollins Avenue, VALLE CARSON SUBDIVISION (P.R. WWW 15, P-41) — across Rollins Avenue, EDWARD B. ROLLINS, TRUSTEES ET AL. L-1378 (F-105) —, PUE — Public Utility Easement — RPP — Iron Pipe Found — For Public Water and Sewer Only
The surveyor certifies, under declaration and approval signatures of the recorded plat and NOT reproduced here, they abide by the requirements set forth in this plat.

LEGEND	
— — — — —	PROPERTY BOUNDARY
- - - - - BRL	BUILDING RESTRICTION LINE
— — — — —	PROPOSED STRUCTURE
— — — — —	EXISTING CONTOUR — PGATLAS 2 FT (2023), NAVD83
- - - - -	STREET CENTRELINE
— — — — —	PROPOSED PAVEMENT — DRIVEWAY / WALK
- - - - -	EASEMENT

PRINCE GEORGE'S COUNTY SOIL CONSERVATION DISTRICT APPROVAL

SEDIMENT CONTROL, GRADING, SOILS & DRAINAGE

SIGNATURE _____ DATE _____

DPE SITEROAD PLAN REVIEW DIVISION APPROVAL

SIGNATURE _____ DATE _____

STABILIZATION COMPLIANCE PREAMBLE



Stabilization practices on all projects must be in compliance with the requirements of COMAR 26.17.01 by January 9, 2013, regardless of when an erosion and sediment control plan was approved. COMAR 26.17.01.02(5), Compliance of approved plans.

STANDARD STABILIZATION NOTE

Following initial soil disturbance or re-disturbance, permanent or temporary stabilization must be completed within a) Three (3) calendar days to the surface of all perimeter ditches, swales, ditches, perimeter slopes, and all slopes steeper than 3 horizontal to 1 vertical (3:1); and b) Seven (7) calendar days to all other disturbed or graded areas on the project site not under active grading.
2011 Maryland Standards and Specifications for Soil Erosion and Sediment Control, "Standard Stabilization Note" (adopted by COMAR 26.17.01.06A(1)).

REVISIONS

— NONE —

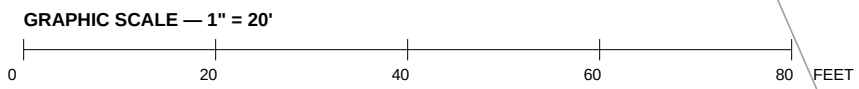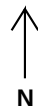

KEALEE

design, build, deliver

PROJECT
Porter Subdivision — LOT 1 & LOT 2
ADDRESS
1005 Rollins Ave
JURISDICTION
prince georges md
ZONE
RSF-65
SHEET
C-800 — Road, Driveway and Paving Plan
SCALE
1" = 20'
STATUS
PRELIMINARY
SHEET NO.
9 OF 11
COORDINATES
EPSG:2248
H: NAD83
V: NAVD83 (feet)

SITE DATA		
ZONE	RSF-65	
TAX / PARCEL ID		
GROSS LOT AREA	21,826 SF	0.501 AC
LOT FRONTAGE	45' MIN	65.00'
SETBACKS	REQUIRED	PROVIDED
FRONT YARD	23'	23'
SIDE YARD	8'	8'
REAR YARD	20'	20'
COVERAGE	MAX	PROPOSED
LOT COVERAGE	35%	5.5%
BUILDING FOOTPRINT	—	1,196 SF
DATUM		
HORIZONTAL	EPSG:2248	NAD83
VERTICAL	NAVD83 (feet)	

SITE ANALYSIS	
1. Gross tract area	21,826 SF
2. Area of dwelling	1,196 SF
3. Wooded area	NOT ESTABLISHED
4. Floodplain area	NOT ESTABLISHED
5. Net tract area	21,826 SF
6. TOTAL AREA DISTURBED	NOT QUANTIFIED

SEQUENCE OF CONSTRUCTION	
1. Preconstruction meeting	1 DAY
2. Obtain necessary permits	2 DAYS
3. Notify Miss Utility at B11 at least 48 hours prior to any excavation	1 DAY
4. Construct stabilized construction entrance and perimeter sediment control	2 DAYS
5. Rough grade, construct dwelling, utilities and driveway	12 MONTHS
6. Fine grade and stabilize all disturbed areas	1 DAY
7. Remove sediment control devices when written permission has been granted	1 DAY
TOTAL ESTIMATED TIME OF CONSTRUCTION: 12 MONTHS	

- GENERAL NOTES
- CONTRACTOR SHALL CONTACT MISS UTILITY AT B11 A MINIMUM OF 48 HOURS PRIOR TO ANY EXCAVATION.
 - ALL EXISTING AND PROPOSED UTILITIES SHOWN PER PCC CODE SEC. 32-106.
 - PROPOSED GRADE SHOWN SOLID; EXISTING GRADE SHOWN DASHED.
 - ROUGH EARTHWORK GRADES AND UTILITY ELEVATIONS SHOWN TO TENTHS OF A FOOT.
 - BOUNDARY SHOWN IS COMPILED JURISDICTION GIS, NOT A BOUNDARY SURVEY.

PLAT OF RECORD
PORTER SUBDIVISION, LOTS 1 AND 2 — Plat Book PM 231, p. 50 (M&A, C2381, 19950), Sewer Pressure (SP) Elevation District, Prince Georges County, Maryland. The Map To: GLE B2, 200 May 202 SE 06, Zone R-65 as recorded (RSP-65 under the 2022 (revised), Scale 1" = 20', November 2007 M, NSPC Record File S-20523), State of Maryland Maryland State Plane Coordinate System (NAD 83), Lot 1 = 9,599 sq ft (0.2203 ac), Lot 2 = 8,008 sq ft (0.1838 ac), 4,219 sq ft (0.0969 ac) dedicated to public use.

- NOTES OF RECORD
- Development of the property shall be in accordance with the approved Stormwater Management Control Plan (12/20/2006/00), or any approved revision thereto.
 - Approval of this plat is based upon a reasonable expectation that public water and sewer service will be available when needed, and is conditioned on fulfilling all of the Washington Suburban Sanitary Commission authorization DA 4519 Z-05 commitments.
 - The applicant, his heirs, successors and/or assignees shall utilize an existing driveway design, constructed per OPWA standards and requirements. Separate, standard residential driveway aprons shall be provided along Rollins Avenue. If deemed appropriate by OPWA upon the issuance of street construction permits.
 - ADJOINING PROPERTIES, per the recorded plat, LOTS 13, 14 AND 15 (Addition to Pleasant Park, Plat Book VJ 185, The 70) — northwest, LOT 12 (Addition to Pleasant Park, Plat Book VJ 185, The 70) — southwest, OUTLOT A (Addition to Pleasant Park, Plat Book VJ 185, The 70) — northwest, JEAN M. YOUNG L. 1, 6, 7, 8, 9, 10 — northwest, MARYLAND W. DAVIS L. 1, 2, 3, 4, 5, 6, 7, 8, 9, 10 — northwest, PATRICIA L. PIERRE L. 1, 2, 3, 4, 5, 6, 7, 8, 9, 10 — northwest, ROLLINS AVENUE, VALLE CARSON SUBDIVISION (P&S, WWW L. 1, 2, 3, 4, 5, 6, 7, 8, 9, 10) — across Rollins Avenue, EDWARD B. ROLLINS, TRUSTEE, ET AL. L. 1, 2, 3, 4, 5, 6, 7, 8, 9, 10 —, PUE — Public Utility Easement — RPF — Iron Pipe Found — For Public Water and Sewer Only

The surveyor certifies, under declaration and approval signatures of the recorded plat are NOT reproduced here; they shall be the responsibility of the surveyor.

LEGEND

- PROPERTY BOUNDARY
BRL — BUILDING RESTRICTION LINE
PROPOSED STRUCTURE
EXISTING CONTOUR — PGATLAS 2 FT (2023), NAVD83
STREET CENTRELINE
PROPOSED PAVEMENT — DRIVEWAY / WALK
EASEMENT

PRINCE GEORGE'S COUNTY SOIL CONSERVATION DISTRICT APPROVAL

SEDIMENT CONTROL, GRADING, SOILS & DRAINAGE

SIGNATURE DATE

DPE SITEROAD PLAN REVIEW DIVISION APPROVAL

SIGNATURE DATE

REVISIONS

NOTE

GRAPHIC SCALE — 1" = 20'

0 20 40 60 80 FEET

KEALEE

design, build, deliver

PROJECT
Porter Subdivision — LOT 1 & LOT 2
ADDRESS
1005 Rollins Ave
JURISDICTION
prince georges md
ZONE
RSF-65
SHEET
C-900 — Civil Details
SCALE
1" = 20'
STATUS
PRELIMINARY
SHEET NO.
10 OF 11
COORDINATES
EPSG:2248
H: NAD83
V: NAVD83 (feet)

SITE DATA		
ZONE	RSF-65	
TAX / PARCEL ID		
GROSS LOT AREA	21,826 SF	0.501 AC
LOT FRONTAGE	45' MIN	65.00'
SETBACKS	REQUIRED	PROVIDED
FRONT YARD	23'	23'
SIDE YARD	8'	8'
REAR YARD	20'	20'
COVERAGE	MAX	PROPOSED
LOT COVERAGE	35%	5.5%
BUILDING FOOTPRINT	—	1,196 SF
DATUM		
HORIZONTAL	EPSG:2248	NAD83
VERTICAL	NAVD83 (feet)	

SITE ANALYSIS	
1. Gross tract area	21,826 SF
2. Area of dwelling	1,196 SF
3. Wooded area	NOT ESTABLISHED
4. Floodplain area	NOT ESTABLISHED
5. Net tract area	21,826 SF
6. TOTAL AREA DISTURBED	NOT QUANTIFIED

SEQUENCE OF CONSTRUCTION	
1. Preconstruction meeting	1 DAY
2. Obtain necessary permits	2 DAYS
3. Notify Miss Utility at B11 at least 48 hours prior to any excavation	1 DAY
4. Construct stabilized construction entrance and perimeter sediment control	2 DAYS
5. Rough grade, construct dwelling, utilities and driveway	12 MONTHS
6. Fine grade and stabilize all disturbed areas	1 DAY
7. Remove sediment control devices when written permission has been granted	1 DAY
TOTAL ESTIMATED TIME OF CONSTRUCTION: 12 MONTHS	

- GENERAL NOTES
- CONTRACTOR SHALL CONTACT MISS UTILITY AT B11 A MINIMUM OF 48 HOURS PRIOR TO ANY EXCAVATION.
 - ALL EXISTING AND PROPOSED UTILITIES SHOWN PER PCC CODE SEC. 32.106.
 - PROPOSED GRADE SHOWN SOLID; EXISTING GRADE SHOWN DASHED.
 - ROUGH EARTHWORK GRADES AND UTILITY ELEVATIONS SHOWN TO TENTHS OF A FOOT.
 - BOUNDARY SHOWN IS COMPILED JURISDICTION GIS, NOT A BOUNDARY SURVEY.

PLAT OF RECORD
PORTER SUBDIVISION, LOTS 1 AND 2 — Plat Book PM 231, p. 50 (M&A, C2381, 19950), Sewer Pressure (SP) Elevation District, Prince Georges County, Maryland. The Map To: GLE B2, 200 May 202 SE 06, Zone R-65 as recorded (RSP-65 under the 2022 (revised), Scale 1" = 20', November 2007 M, NSPC Record File S-20623), State of Maryland, Maryland State Plane Coordinate System (NAD 83). Lot 1 = 9,599 sq ft (0.2203 ac); Lot 2 = 8,008 sq ft (0.1838 ac); 4,219 sq ft (0.0969 ac) dedicated to public use.

- NOTES OF RECORD
- Development of the property shall be in accordance with the approved Stormwater Management Control Plan (1220-2000-00), or any approved revision thereto.
 - Approval of this plat is based upon a reasonable expectation that public water and sewer service will be available when needed, and is conditioned on fulfilling all of the Washington Suburban Sanitary Commission authorization DA 4519 Z-05 commitments.
 - The applicant, his heirs, successors and/or assignees shall utilize an existing driveway design, constructed per OPWA standards and requirements. Separate, standard residential driveway aprons shall be provided along Rollins Avenue. If deemed appropriate by OPWA upon the issuance of street construction permits.
 - ADJOINING PROPERTIES, per the recorded plat, LOTS 13, 14 AND 15 (Addition to Pleasant Park, Plat Book VJ 185, The PG) — northwest, LOT 12 (Addition to Pleasant Park, Plat Book VJ 185, The PG) — southwest, OUTLOT A (Addition to Pleasant Park, Plat Book VJ 185, The PG) — northwest, JEAN M. YOUNG L. 1, 6, 7, 8,192

KEALEE

design, build, deliver

PROJECT
Porter Subdivision — LOT 1 & LOT 2
ADDRESS
1005 Rollins Ave
JURISDICTION
prince georges md
ZONE
RSF-65
SHEET
L-100 — Landscape and Tree Canopy Plan
SCALE
1" = 20'
STATUS
PRELIMINARY
SHEET NO.
11 OF 11
COORDINATES
EPSG:2248
H: NAD83
V: NAVD83 (feet)

SITE DATA		
ZONE	RSF-65	
TAX / PARCEL ID		
GROSS LOT AREA	21,826 SF	0.501 AC
LOT FRONTAGE	45' MIN	65.00'
SETBACKS	REQUIRED	PROVIDED
FRONT YARD	23'	23'
SIDE YARD	8'	8'
REAR YARD	20'	20'
COVERAGE	MAX	PROPOSED
LOT COVERAGE	35%	5.5%
BUILDING FOOTPRINT	—	1,196 SF
DATUM		
HORIZONTAL	EPSG:2248	NAD83
VERTICAL	NAVD83 (feet)	

SITE ANALYSIS	
1. Gross tract area	21,826 SF
2. Area of dwelling	1,196 SF
3. Wooded area	NOT ESTABLISHED
4. Floodplain area	NOT ESTABLISHED
5. Net tract area	21,826 SF
6. TOTAL AREA DISTURBED	NOT QUANTIFIED

SEQUENCE OF CONSTRUCTION	
1. Preconstruction meeting	1 DAY
2. Obtain necessary permits	2 DAYS
3. Notify Miss Utility at B11 at least 48 hours prior to any excavation	1 DAY
4. Construct stabilized construction entrance and perimeter sediment control	2 DAYS
5. Rough grade, construct dwelling, utilities and driveway	12 MONTHS
6. Fine grade and stabilize all disturbed areas	1 DAY
7. Remove sediment control devices when written permission has been granted	1 DAY
TOTAL ESTIMATED TIME OF CONSTRUCTION: 12 MONTHS	

- GENERAL NOTES
- CONTRACTOR SHALL CONTACT MISS UTILITY AT B11 A MINIMUM OF 48 HOURS PRIOR TO ANY EXCAVATION.
 - ALL EXISTING AND PROPOSED UTILITIES SHOWN PER PCC CODE SEC. 32-106.
 - PROPOSED GRADE SHOWN SOLID, EXISTING GRADE SHOWN DASHED.
 - ROUGH EARTHWORK GRADES AND UTILITY ELEVATIONS SHOWN TO TENTHS OF A FOOT.
 - BOUNDARY SHOWN IS COMPILED JURISDICTION GIS, NOT A BOUNDARY SURVEY.

PLAT OF RECORD
PORTER SUBDIVISION, LOTS 1 AND 2 — Plat Book PM 231, p. 50 (M&A, C2381, 19950), Sewer Pressure (SP) Elevation District, Prince Georges County, Maryland, Tax Map 73, GFE B3, 200 May 202 SE 06, Zone R-65 as recorded (RSP-65 under the 2022 rework), Scale 1" = 20', November 2007 M, NSPC Record File S-20623, Sheet of bearings Maryland State Plane Coordinate System (NAD 83), Lot 1 = 9,588 sq ft (0.2203 ac), Lot 2 = 8,008 sq ft (0.1838 ac), 4,219 sq ft (0.0969 ac) dedicated to public use.

- NOTES OF RECORD
- Development of the property shall be in accordance with the approved Stormwater Management Concept Plan 41220-2000-00, or any approved revision thereto.
 - Approval of this plat is based upon a reasonable expectation that public water and sewer service will be available when needed, and is conditioned on fulfilling all of the Washington Suburban Sanitary Commission authorization DA 4519 Z-05 commitments.
 - The applicant, his heirs, successors and/or assignees shall utilize an existing driveway design, constructed per OPWA standards and requirements. Separate, standard residential driveway aprons shall be provided along Rollins Avenue. If deemed appropriate by OPWA upon the issuance of street construction permits.
 - ADJOINING PROPERTIES, per the recorded plat, LOTS 13, 14 AND 15 (Addition to Pleasant Park, Plat Book VJ 185, Page 78) — northwest, LOT 12 (Addition to Pleasant Park, Plat Book VJ 185, Page 78) — southwest, OUTLOT A (Addition to Pleasant Park, Plat Book VJ 185, Page 78) — northwest, JEAN M. YOUNG L. 5,637 (5,637) — northwest, MARY AND W. DAVIS L. 1,145 (1,145) — north, Rollins Avenue, PATRICIA L. PIERRE L.L. 1,786 (1,786) — across Rollins Avenue, VALLE GARCIA SUBDIVISION (P.B. WWW 15, P. 41) — across Rollins Avenue, EDWARD B. ROLLINS, TRUSTEE, ET AL, L. 1,276 (1,276) — east, PUE — Public Utility Easement — BPF — Iron Pipe Found — For Public Water and Sewer Only.

The surveyor certifies, under declaration and approval signatures of the recorded plat are NOT reproduced here; they shall be the responsibility of the surveyor.

LEGEND	
-----	PROPERTY BOUNDARY
-----	BRL — BUILDING RESTRICTION LINE
-----	PROPOSED STRUCTURE
-----	EXISTING CONTOUR — PGATLAS 2 FT (2023), NAVD83
-----	STREET CENTRELINE
-----	PROPOSED PAVEMENT — DRIVEWAY / WALK
-----	EASEMENT

PRINCE GEORGE'S COUNTY SOIL CONSERVATION DISTRICT APPROVAL
SEDIMENT CONTROL, GRADING, SOILS & DRAINAGE

SIGNATURE _____ DATE _____

DPE SITEROAD PLAN REVIEW DIVISION APPROVAL

SIGNATURE _____ DATE _____

REVISIONS
— NONE —

