
N

SCALE 1" = 60' · GRAPHIC: |————————| = 120 FT

LEGEND — red parcels with dark-red buildings at the street line: mixed use (retail at grade, dwellings above) · dashed grey: surface parking · yellow: townhouse lots · blue: two-family (duplex) lots · violet: two-over-two (stacked) bays · grey: private street strip 40 ft · green: woodland conservation (approved TCP) · red: slopes >25% (dashed = graded banks, regraded) · blue band: 50-ft stream buffer · olive: Primary Management Area, light blue: wetlands and their 25-ft buffer, pink dashed: slopes 15–25%, dashed green: forest conservation easement (all from the approved plan where one is supplied)

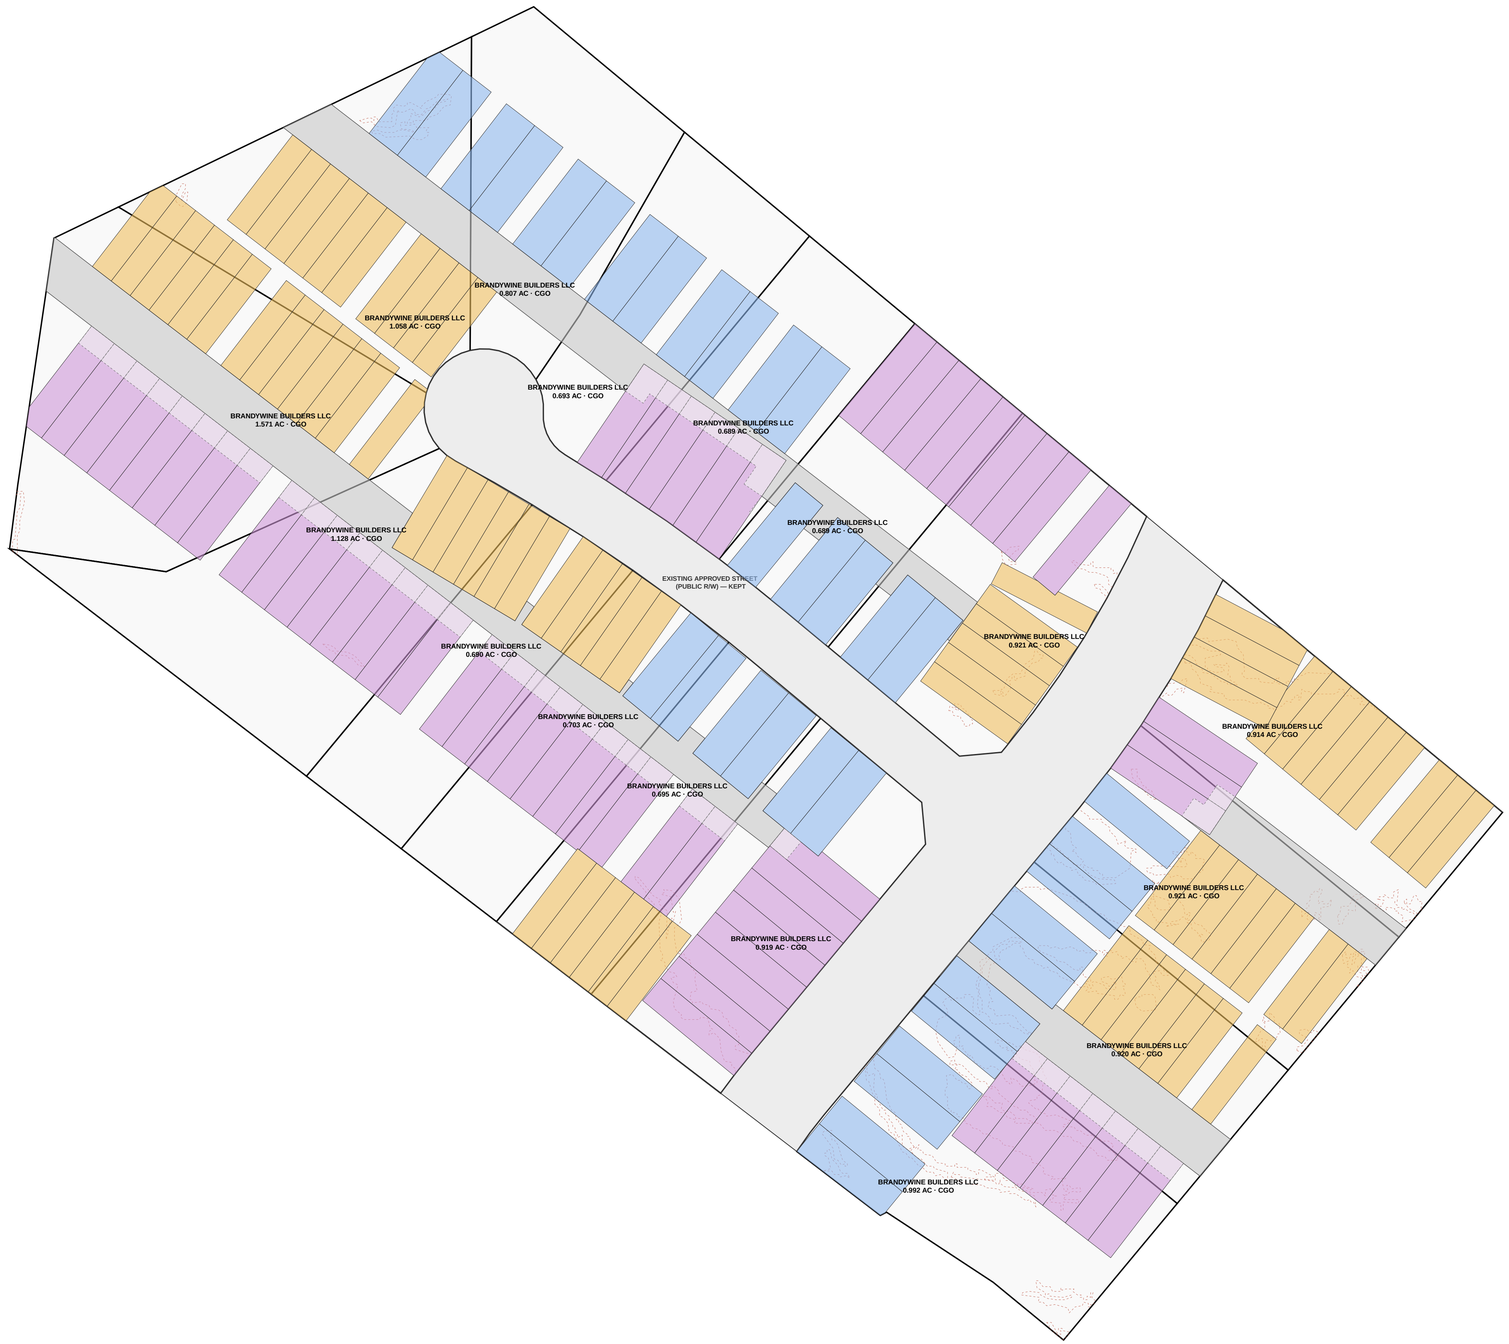

KEALEE

ATTACHED HOUSING YIELD STUDY — PRELIMINARY, NOT A SITE PLAN

THE PARCELS ARE ZONED RE. THIS STUDY APPLIES THE CGO TABLE AS THE REZONING THE OWNER WOULD SEEK; NOTHING HERE IS PERMITTED UNTIL THE COUNCIL APPROVES A ZONING MAP AMENDMENT. THE APPROVED TCP'S WOODLAND CONSERVATION (3.31 AC) IS NOT RESERVED: A NEW TCP2 IS PART OF THE REZONING AND THE SEC. 25-121 REQUIREMENT IS MET BY AFFORESTATION, FEE-IN-LIEU OR OFF-SITE BANKING.

Aragona Village Blocks EE and DD (16 approved SFD lots) — rezoned CGO, converted to townhouses, two-over-twos and duplexes

Zone CGO · certified intensity table Sec. 27-4203 · generated 2026-09-17

PARCELS (PGAtlas Address/Property — owner of record, assessment)

Acct 4007985 · · BRANDYWINE BUILDERS LLC · 0.806 ac assessed / 0.807 ac GIS · plat 05230085 · L.26757 F.002
Acct 4007993 · · BRANDYWINE BUILDERS LLC · 0.693 ac assessed / 0.693 ac GIS · plat 05230085 · L.26757 F.002
Acct 4008009 · · BRANDYWINE BUILDERS LLC · 0.689 ac assessed / 0.689 ac GIS · plat 05230085 · L.26757 F.002
Acct 4008082 · · BRANDYWINE BUILDERS LLC · 0.689 ac assessed / 0.689 ac GIS · plat 05230086 · L.26757 F.002
Acct 4008090 · · BRANDYWINE BUILDERS LLC · 0.921 ac assessed / 0.921 ac GIS · plat 05230086 · L.26757 F.002
Acct 4007977 · · BRANDYWINE BUILDERS LLC · 1.05 ac assessed / 1.058 ac GIS · plat 05230085 · L.26757 F.002
Acct 4007969 · · BRANDYWINE BUILDERS LLC · 1.57 ac assessed / 1.571 ac GIS · plat 05230085 · L.26757 F.002
Acct 4007951 · · BRANDYWINE BUILDERS LLC · 1.13 ac assessed / 1.128 ac GIS · plat 05230085 · L.26757 F.002
Acct 4007944 · · BRANDYWINE BUILDERS LLC · 0.692 ac assessed / 0.690 ac GIS · plat 05230085 · L.26757 F.002
Acct 4008074 · · BRANDYWINE BUILDERS LLC · 0.702 ac assessed / 0.703 ac GIS · plat 05230086 · L.26757 F.002
Acct 4008066 · · BRANDYWINE BUILDERS LLC · 0.697 ac assessed / 0.695 ac GIS · plat 05230086 · L.26757 F.002
Acct 4008058 · · BRANDYWINE BUILDERS LLC · 0.922 ac assessed / 0.919 ac GIS · plat 05230086 · L.26757 F.002
Acct 4008041 · · BRANDYWINE BUILDERS LLC · 0.919 ac assessed / 0.914 ac GIS · plat 05230086 · L.26757 F.002
Acct 4008033 · · BRANDYWINE BUILDERS LLC · 0.919 ac assessed / 0.921 ac GIS · plat 05230086 · L.26757 F.002
Acct 4008025 · · BRANDYWINE BUILDERS LLC · 0.919 ac assessed / 0.920 ac GIS · plat 05230086 · L.26757 F.002
Acct 4008017 · · BRANDYWINE BUILDERS LLC · 0.993 ac assessed / 0.992 ac GIS · plat 05230086 · L.26757 F.002

Tract 623,303 sf (14.309 ac). Boundary is the county parcel layer — not a survey.

WHAT CANNOT BE BUILT ON (county layers, clipped to the tract)

Woodland conservation (approved TCP areas) 0.00 ac · slopes >25% in bodies 0.00 ac (graded banks 0.80 ac, regraded) · 15–25% 2.02 ac (built with grading) · stream buffer 0.00 ac · floodplain 0.00 ac · wetlands 0.00 ac
Developable 623,303 sf (14.309 ac).

The Primary Management Area, the woodland conservation threshold and any expanded buffers are set by an approved Natural Resources Inventory and TCP, not by these layers. A 50-ft stream buffer and slopes over 25% are the minimum that would be taken; the NRI may take more.

CGO STANDARDS BY DWELLING TYPE (Sec. 27-4203)

Townhouse: 20 du/ac net · lot ˝e 20 ft wide · coverage ˝d 65% · yards 10/8/15 ft · height ˝d 50 ft
Two-family (duplex): 40 du/ac net · lot ˝e 20 ft wide · coverage ˝d 65% · yards 10/8/15 ft · height ˝d 50 ft
Two-over-two (stacked, 2 units per bay): 48 du/ac net · lot ˝e 50 ft wide · coverage ˝d 70% · yards 10/8/15 ft · height ˝d 86 ft
Mixed use (retail below, dwellings above): 48 du/ac net · lot ˝e 50 ft wide · coverage ˝d 70% · yards 10/8/15 ft · height ˝d 86 ft

YIELD — THIS LAYOUT

Townhouse: 74 bays ˝ 74 du · 20.86 du/ac on 3.548 net ac (cap 20) OVER · lot coverage 44.4% (cap 65%) · parking 148 at 2/du ASSUMED — front-load garage + driveway on the lot
Two-family (duplex): 34 bays ˝ 34 du · 13.92 du/ac on 2.443 net ac (cap 40) ˚ · lot coverage 44.4% (cap 65%) · parking 68 at 2/du ASSUMED — garage + driveway on each lot
Two-over-two (stacked, 2 units per bay): 59 bays ˝ 118 du · 31.37 du/ac on 3.762 net ac (cap 48) ˚ · lot coverage 48% (cap 70%) · parking 177 at 1.5/du ASSUMED — one garage space per unit + surface bays along the street
Parking: 40 surface spaces drawn (dashed) + 334 in garages and driveways = 374 against 393 required at the assumed ratios.

TOTAL 226 DWELLING UNITS in 167 bays · 15.79 du/ac gross on the 14.309-ac tract

CEILINGS if the whole developable ground were one type (× 0.8 for streets, parking, open space):
Townhouse: 228 du
Two-family (duplex): 457 du
Two-over-two (stacked, 2 units per bay): 549 du

STORMWATER MANAGEMENT (ESD, MDE Ch. 5)

Impervious 298,896 sf (48%), Rv 0.4816, ESDv 25,014 cf at P_E 1.0 in ˝ 31,268 sf of micro-bioretention. Reserved for stormwater: 0 sf.
The 0 sf reserved is short of the 62,536 sf (practice × 2) the drawn programme wants; add micro-bioretention in the parking lots and along the streets, or reduce impervious cover.
Micro-bioretention in every surface parking lot island and a bioswale along each private street, credited under ESD; rooftop disconnection is not available over parking. Design per the DPIE stormwater concept approval that precedes the DSP.

UNIT ASSUMPTIONS

Townhouse: 20 × 90 ft lot, 20 × 40 ft footprint, 1 du per bay, sticks of ˝d 6
Two-family (duplex): 30 × 90 ft lot, 30 × 40 ft footprint, 1 du per bay, sticks of ˝d 2
Two-over-two (stacked, 2 units per bay): 24 × 100 ft lot, 24 × 48 ft footprint, 2 du per bay, sticks of ˝d 8
Mixed use (retail below, dwellings above): 100 × 200 ft lot, 100 × 70 ft footprint, 22 du per bay, 7,000 sf retail, 5 storeys ˝H 62 ft
Private streets in 40-ft strips (26-ft pavement, walk one side), each teeing off GUNPOWDER — the existing public right-of-way — with no new access to any other road. Visitor parking, open space and the Landscape Manual 4.7 buffer to the RE lots are DSP work not drawn here.

APPROVALS

CGO: townhouse, two-family and multifamily (two-over-two) dwellings are listed uses with their own intensity standards in the certified Sec. 27-4203 table; a Detailed Site Plan is the approval path for residential in the commercial zones (confirm the use table entry for each type — the use table is not carried by this engine).
Sec. 27-6300 parking, Sec. 27-6400 landscaping (Landscape Manual 4.7 buffers against the RE lots), Sec. 25-121 woodland conservation, Sec. 24 subdivision (a preliminary plan of subdivision creates fee-simple townhouse and duplex lots; two-over-twos are condominium or fee-simple with a DSP), stormwater concept (DPIE), WSSC hydraulic planning analysis.

This is a yield study prepared by the Kealee site-plan engine from county GIS and the certified zoning table. It is not a Detailed Site Plan, not a survey and not a determination of what the Planning Board will approve.