

ESTATES AT INDIAN HEAD — LOTS 1-6

200-205 ESTATES COURT, ACCOKEEK, MD 20607 · PLAT BOOK PM 228 PLAT 83 · TAX MAP 151 F-3 · WSSC 220SE01 · ELECTION DIST. 5 · COUNCIL DIST. 9 · ZONE RR
Stormwater management by Environmental Site Design to the Maximum Extent Practicable (MDE Design Manual Ch. 5; PGC Subtitle 32). Layout per the approved 2009 Street Tree & Lighting Plan, DPW&T 9399-2009-00.

PRINCE GEORGE'S COUNTY BMP SUMMARY TABLE — ESD BY POINT OF INVESTIGATION (A-15, C-9)

BMP	PRACTICE	MDE	LOCATION	OWNERSHIP / MAINT.	POI	DA SF	IMP SF	%	HSG	P,E IN	Rv	ESDv REQ CF	ESDv PROV CF	Rev REQ CF	SURFACE SF	COORDINATES (NAD 83)
ESD-1	Micro-bioretentment	M-6	Lot 1	Private — lot owner (maintenance agreement)	POI-1	19,999	4,500	22.5	C	1.2	0.253	505	505	55	525	N 367,417 E 1,311,443
ESD-2	Micro-bioretentment	M-6	Lot 2	Private — lot owner (maintenance agreement)	POI-1	20,015	2,422	12.1	C	1.0	0.159	265	265	34	330	N 367,396 E 1,311,250
ESD-3	Micro-bioretentment	M-6	Lot 3	Private — lot owner (maintenance agreement)	POI-1	20,051	3,008	15.0	C	1.0	0.185	309	309	40	386	N 367,378 E 1,311,388
ESD-4	Micro-bioretentment	M-6	Lot 4	Private — lot owner (maintenance agreement)	POI-1	20,021	2,062	10.3	C	1.0	0.143	238	238	31	298	N 367,217 E 1,311,299
ESD-5	Micro-bioretentment	M-6	Lot 5	Private — lot owner (maintenance agreement)	POI-1	20,235	2,489	12.3	C	1.0	0.161	271	272	35	340	N 367,173 E 1,311,331
ESD-6	Micro-bioretentment	M-6	Lot 6	Private — lot owner (maintenance agreement)	POI-1	29,536	2,511	8.5	C	1.0	0.127	311	311	40	389	N 367,082 E 1,310,950
ESD-5	Roadside dry swales w/ check dams (99' L)	M-8	Estates Ct RW, both sides	Public — DPPE	POI-1	36,041	21,216	58.9	C	2.0	0.580	3,483	5,992	226	3,995	N 367,342 E 1,311,097
	SUBTOTAL POI-1				POI-1							5,382	7,892			
TOTAL	7 ESD practices					165,898	38,208					5,382	7,892	461	6,263	

P E from MDE Stormwater Design Manual (2000, Supp. 1 2009), Ch. 5, Table 5.3 — rainfall targets for ESD; HSG C governing. $R_v = 0.05 + 0.009-I$; $ESD_v = P E - R_v A/12$; $Rev = S - R_v A/12$ ($S = 0.13$ in, HSG C), met within ESDv. M-8 provided = 6 cf per ft (4-ft bottom, 6" ponding, 2.5' media at n 0.40)

SITE DATA

ITEM	DATA
Project	Estates at Indian Head, Lots 1-6 and Estates Court
Location	S. side of MD 210, ±3,000 ft E of MD 210 / MD 373; 200-205 Estates Ct., Accokeek 20607
Record	Plan Book PM 228 Plat 83 (final plat 5-08283); Tax Map 151 F-3; WSSC 2007 22050E1
Accounts	3987666, 3987674, 3987682, 3987690, 3987708, 3987716
Owner	General Waldman Revocable Trust, 1-32063 F 0-043
Zone / use	RR (no change) – a single-family detached dwellings
Tract	165,019 sq. ft of record (3.788 ac) = plat 171,505 sq less Outlot A (6,486 sf, conveyed 1.51565 F.455)
Public dedication	WSSC 600' RW, 35,173 sq ft of record – rural open space, 24' pavement, cul-de-sac
Water / sewer	W-15 (UNSC) – mains from Henrietta Dr via 30' WSSC ecm; 1.51789 F 399 and prop. Lot 4 ecm
Watershed	Piscataway Creek, MD 021402030798; not tier; not CBCA; FEMA Zone X
Master plan	2013 Subregion 5 Master Plan & SMA; Planning Area 84; Council District 9; Election Dist. 5
Map	NAD 83 MD State Plane (US IR); NAVD 88 (N-NCPP- 2.4); 2009 spot grades on WSSC data

APPROVALS OF RECORD

CASE	STATUS
NRI-015-06	Approved — current
TCP1-018-06	Current
TCP2-016-09	Approved — current
5-08238	Final plat, PM 228 @ 83 — recorded
DPW&T 9399-2009-00	Street tree & lighting plan (2009) — layout followed
L.51799 F.399	30' WSSC easement (Outlot A, Lot 20) — recorded 2025

GENERAL NOTES


1. Boundary per recorded plat PM 228 at §3; lot lines reproduce the plat to the second decimal. A Maryland license surveyor shall confirm the boundary and provide a written report.
2. Horizontal datum: Maryland State Plane NAD 83 (US ft). Vertical datum: NAVD 88 (M-NCPLC 2-ft contour). 2009 spot grades are on WSSC datum (= NAVD 88 + 1.6 ft, to be confirmed by the full-surface) DRIE prefers NGVD 29 – the survey shall state the conversion.
3. Easements include: 10' easement for Utility Service Lines (see Utility Map); 10' easement for Stormwater Flow; 10' easement for 10' stormwater flow; street lights. Lot 4 is front-lot garage (garage to curtil-dw) c/o DEPE easement.
4. Estates Court is a rural open section (DPW&T Std. 500.1 / 600.02 / 600.04): 24 pavement, shoulders, roadside swales; driveways cross the swale
5. Entrance to MD 210 (SHA) with 50' turns: enter the 500' / 600' area permit and sight-distance analysis required. MD 210 auxiliary lanes shown for SHA review; RV dedication may be required.
6. The proposed driveway crosses the 30' WSSC easement through the recorded 30' WSSC easement (L51799 F.399) and a 30' WSSC easement to be granted across Lot 4. Record discrepancies in the easement description to be resolved with WSSC.
7. Approvals of record NR-015-06, PCT-018-06 and PCT-016-09 are current. No streams, wetlands, floodplain, PMA or Chesapeake Bay Critical Area On the property.
8. Contact Miss Utility (811) at least 48 hours before any excavation.


DPIE CONCEPT PLAN DESIGN REVIEW CHECKLIST (08/25/2021) — C = SHOWN · X = N/A · O = OUTSTANDING


ITEM	REQUIREMENT	REF.	C/X/O	RESPONSE / WHERE SHOWN	SHEET
A-1	Plan is labeled as Site Development Concept Plan (aka Concept Plan from MDE step 1)		C	Everywhere is titled SITE DEVELOPMENT CONCEPT PLAN.	ALL
A-2	Plan sheet size does not exceed 30" x 42" and all sheets are printed on same size paper.	5.3.2	C	All sheets 24" x 36" (ARCH D).	ALL
A-3	5-inch, full-height open area is provided on the right-hand side of the plan for County approval check.	2.2.1.A	C	5-inch full-height strip at the right edge, kept clear for DPW.	ALL
A-4	If more than 4 plan sheets: composite plan showing match lines and sheet numbers (scale not to exceed 1"=200'; key map on each plan sheet).	2.2.1.C	X	7 sheets: the whole site is on each plan sheet at one scale, so no match lines; key map in every title block.	ALL
A-5	Match lines have a minimum length of 4 inches and identify the matching sheet number.	2.2.1.M	X	No match lines – the entire site fits one viewport.	
A-6	Vicinity map at a minimum scale of 1"=2,000' with north arrow and scale, upper right hand corner of cover sheet.	2.2.1.B	C	Vicinity map at 1" = 2,000' with north arrow and bar scale; upper right.	C-000
A-7	A bar scale is provided on every sheet.		C	Graphic bar scale in every plan viewport.	ALL
A-8	Three grid ticks are provided as described in the manual.	2.2.1.E	C	Three State Plane grid ticks with N/E values on each plan.	C-000
A-9	Horizontal (MD Coordinate System, NAD 83) and vertical (NGVD 29 preferred) datum is stated on the plan.		C	Horizontal Maryland State Plane, NAD 83 (EPSG 2248); US F. vertical NAVD 89 (NAD 83) (EPSG 2249); 2000 spot grade WSSC datum noted. NGVD 29 conversion to be stated by the full-run surveyor.	ALL
A-10	General notes about the project are provided.		C	General notes on the cover sheet.	C-000
A-11	The entire property is shown at a maximum plan scale of 1 inch = 500 feet (preferred) within the plan set.	5.3.2	C	Entire property at 1" = 30'.	C-000
A-12	All existing structures and site features including cultural features, historic sites and easements, and any visible foundations or ruins are shown.	5.3.2	C	Existing structures, adjoining houses, fences, sheds, well, easements of record shown; no historic sites or ruins.	C-100
A-13	Topographic contours at maximum 2 foot interval, extending at least 100 feet beyond the property.	3.2-182	C	M-NCPPC 2-ft contours; 100 ft beyond the property.	
A-14	All existing utilities and utility easements are shown.		C	WSSC easement L51799 F.399 and the proposed Lot 4 WSSC easement; public utility easements along the frontage; existing mains in Henrietta Rd noted (see 103s to verify on WSSC 2205201).	C-000
A-15	The County BMP Summary Table is provided. Preferred location is on the cover sheet.	5.3.1	C	County BMP Summary Table, 7 practices.	C-000
B-1	Banks of all regulated streams or a centerline if the banks are too close together to graphically show.	MDE 5.7	X	No streams on site. NCI-015-06 approved (current); TCP1-018-06 and TCP2-019-09 (current).	
B-2	Location of streams and stream buffers and/or enhanced buffers per MNCPPC and SCD criteria.	MDE 5.7	X	No streams, no stream buffers.	
B-3	Location of wetlands and/or wetlands of special state concern and appropriate wetland buffers.	MDE 5.7	X	No wetlands on or within 100 ft (DNR, NRI).	
B-4	Delineation of the 100-year floodplain, per Techno-Gram 004-2020.	MDE 5.7	X	FEMA Zone X; No 100-yr floodplain on or within 100 ft.	
B-5	Location of steep slopes (15% and greater) clearly shown on the plan and in the legend.	M-NCPPC	C	Slopes 15-25%; 2.75% to >25%; 50% – shown and in the legend.	C-100
B-6	The Primary Management Area is delineated.	MDE 5.7	X	No PMA on the plan.	
B-7	Existing woodland is delineated on the property.	MDE 5.7	C	Woodland per approved NRI-015-06 and TCP2-016-09 (current); woodland conservation per the approved TCP2.	C-100
B-8	Existing environmental features extend off the property 100 feet in all directions.	MNCPPC	C	Environmental layers drawn 100 ft beyond the property.	
B-9	Soil types and soil boundaries from USDA NRCS Soil Survey (Dec. 2009) are listed.		C	Soil types and boundaries from USDA NRCS (PGLatals Soil Survey); CwE (HSG C); UdgHr (HSG –); Bd (HSG C); Bd (HSG C).	C-100
B-10	Plan identifies TMDL watershed (sediment, nitrogen, phosphorus) and Tier I water/watershed.		C	Chesapeake Bay TMDL (nitrogen, phosphorus, sediment) applies; MD 12.12.13 watershed 021402030798, Piscataway Creek (021402033). Tier I: no.	C-000
B-11	Highly erodible soils identified.		C	Beltsville soil (om K 0.37) is highly erodible where slopes are 15% or more; those areas are stabilized within 3 days.	C-000
B-12	Springs and seeps noted.	MDE 5.7	X	None observed or mapped.	
B-13	Bedrock and Marblow Bay outcrops noted.	MDE 5.7	X	No bedrock or Marblow bay mapped (PGAtals); geotechnical report to be confirmed (E-2).	
B-14	Chesapeake Bay Critical Area delineated.	MDE 5.7	X	Not in the Chesapeake Bay Critical Area.	


CHECKLIST (CONT.)

C#	REQUIREMENT	REF.	C/X/O	RESPONSE / WHERE SHOWN	SHEET
C-1	Project layout is shown, including roads, buildings, parking, sidewalks and other improvements and associated grading.	C-32-182	C	Estates Court, 6 dwellings, driveways and courts, entrance at MD 210, grading.	C-200
C-2	Preliminary locations of ESD and structural stormwater practices, grading for slopes where slopes exceed 15%.	C-32-182	C	7 ESD practices (micro-bioretentation M-6 per lot; roadside dry swales M-8).	C-400
C-3	Preliminary locations of storm drain inlets and culverts; entrance and off-site structures located beyond project limits (easements may be required).	5.2.4.2.B / C-32-182.A.6	C	Open section -- no inlets; 6 driveway culverts (15" RCP) with end sections; swales culvert at the entrance to the MD 210 roadside ditch (SHA).	C-400
C-4	Limit of Disturbance shown for all site work, incl. water, sewer, storm drain, SWM, road improvements, sediment control.	C-32-182	C	LOD 22.317 of incl. manas, easement work off site, sediment control and stockpile.	C-500
C-5	Existing easements shown and any required offsets proposed easement.		C	Recorded WSSC easement (Outer A, Lot 20) and proposed Lot 2 WSSC easement, private SWM easements over ESD practices.	C-300
C-6	Locations, names and widths of existing and ultimate rights-of-way of adjacent streets and alleys; public vs. private noted.		C	MD 210 (variable R/W, SHA, Estates Ct (60' public), Henrietta Dr and Jennifer Dr (50' public), 30' R/W in common L1042 & F 725 (private).	C-200
C-7	Existing and proposed water well and septic field locations are shown.		C	No wells or septic; proposed (public water and sewer). Existing well on Parcel 199 (15608 Indian Head Hwy), off site, shown.	C-100
C-8	Proposed public dedication area including any proposed parking is shown and labeled.		C	Estates Court public dedication 36,041 sf (plat PH 228 @ 83); no parkland.	C-200
C-9	Point(s) of investigation shown; ESD, computations and BMP Summary Table broken out to show ESD Required is Provided within each POI.		C	1 POI(s); ESD required vs. provided tabulated per POI.	C-400
C-10	The ultimate 100-year stormwater overflow path is shown throughout the site using flow arrows.		C	100-yr overflow arrows from every practice to its POI (11).	C-400
C-11	Drainage areas to each device, offsite drainage onto the site, and to site outfalls; inter-area analysis for no increase in 100-yr discharge.		C	C Drainage areas to each practice; off-site area onto the site @ 4.9 ac; no diversion between POIs.	C-400
C-12	Where grading blocks a drainage course, ponding limits before and after grading are shown.		X	No fill across a drainage course.	
D-1	Report addresses natural resource protection, natural flow patterns, impervious reduction, ESC integration, ESD planning to the MEP.	MODE 5.11	O	SWM concept narrative (ESD to the MEP, flow patterns, ESC integration) -- to accompany the plans.	
D-2	If in the Chesapeake Bay Critical Area, discussion of flow requirements are met; preliminary computations.		X	Not in the Chesapeake Bay Critical Area.	
D-3	Outfalls located outside the site, to existing storm drain or 100-yr floodplain; otherwise the discharge area is described.		O	Narrative: outfalls at the POIs; swales discharge to the MD 210 roadside ditch; receiving discharge area.	
D-4	Stabilization at downstream outfall and upstream inflow evaluated; measures against gully formation discussed.		O	Narrative: outfall stabilization (level spreaders / riprap) at each POI.	
D-5	Photographs of the stream at the downstream outfall and upstream property line; eroded slopes.		X	No stream at the outfalls.	
D-6	If outfall is to an existing SWM facility, its capacity for the added area and flow is documented.		X	No existing SWM facility receives the site.	
D-7	If rezoned to higher imperviousness, effects on downstream properties analysed.		X	No rezoning (RR remains RR).	
D-8	Floodplain ordinance discussion (drainage courses, buildings within 25 ft of floodplain, dams, downstream crossings).		X	No floodplain or drainage course on or downstream within the site; no dams.	
D-9	If a waiver of water quality or quantity is requested, the basis is provided.		X	No waiver requested.	
D-10	Computations: ESD/WQ required and provided; 100-yr existing and proposed runoff; downstream storm drain analysis with 10-yr control if inadequate.	5.3.3 / 5.2.6.1 / 5.2.4.2 / TG 002-2019	O	ESD/computations are on the cover; 100-yr existing/proposed runoff at each POI and downstream analysis to follow in the report.	
E-1	A Geotechnical Report for SWM is provided (Chesapeake Bay Critical Area and feasibility).	5.3.3 / TG 004-2018	O	Geotechnical report for SWM (borings and Sec. 12-1311 infiltration tests at each practice) -- to be submitted.	
E-2	Geotechnical Report addresses Marlboro and Christiansa cays, sulfidic and diatomaceous soils.	5.3.3 / TG 005-2018 / PGSCD 1-8	O	Geotechnical report to address Marlboro/Christiansa cays, sulfidic and diatomaceous soils.	
E-3	Affidavit of Public Informational mailing is provided with second submission.	C-32-182(g)	O	Affidavit of the adjacent-owner mailing (within 7 days of submit) -- with second submission.	
E-4	A Draft Natural Resource Inventory is provided with initial submission (approved copy required prior to approval).	C-32-182(a)	C	NR1-013-06 approved (current); TCP1-018-06 and TCP2-016-09 (current).	

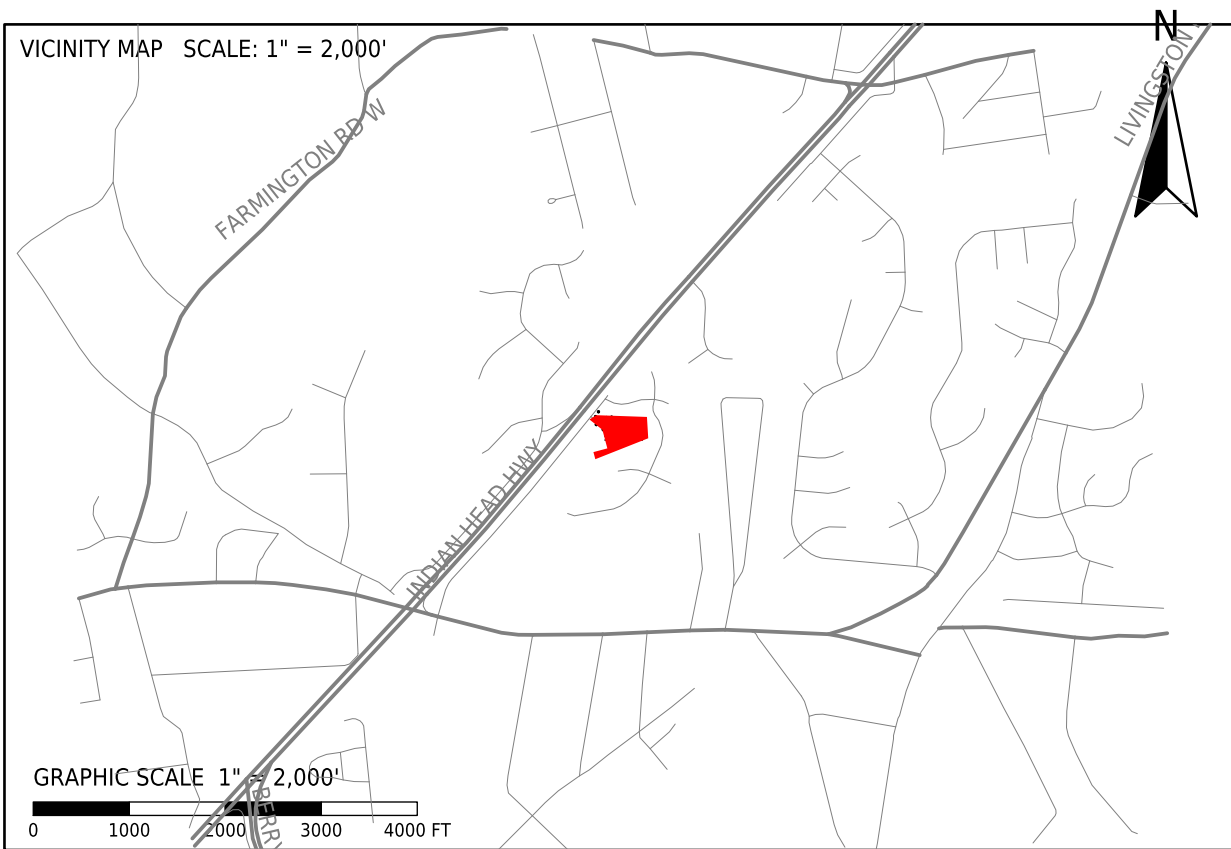


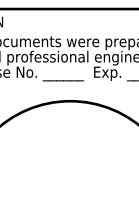PLAN TYPE			
SITE DEVELOPMENT CONCEPT PLAN			
PROJECT			
ESTATES AT INDIAN HEAD - LOTS 1 - A			
200-205 ESTATES COURT, ACCOKEE, MD 20607			
PLAT BOOK PM 228 PLAT 83 TAX MAP 151 F.3 - WSSC			
2020501			
ELECTION DIST. 5 COUNCIL DIST. 9 ZONE RR			
OWNER / APPLICANT			
GERALD WALDMAN REVOCABLE TRUST, 400 N. FLAGLER DR., WEST PALM BEACH, FL 33401 (L 32062 F 043)			
ENGINEER OF RECORD			
W.J. MEKINS, INC. - BILL MEKINS, JR. 3101 RITCHIE ROAD, WEST PALM BEACH, MD 20647 - 301.706.5115			
SHEET TITLE			
COVER SHEET - BMP SUMMARY, DPIE CHECKLIST AND NOTES			
KEY MAP			
			
SCALE			
AS NOTED			
DATUM: NAD 83 MD STATE PLANE (US FT) / NAD83 BB			
REVISIONS			
NO.	DATE	DESCRIPTION	CONCESSION SUBMISSION 1
1	2026-09-30		
PROFESSIONAL CERTIFICATION			
I hereby certify that these documents were prepared or approved by me, and that I am a duly licensed professional engineer under the laws of the State of Maryland. License No. _____ Exp. _____			
			
CONCESSION SUBMISSION 1 - NOT SEALED			
DATE 2026-09-30 JOB KEA-EIH-2026			
PREPARED BY: KATIE SPATOL ENGINEER/CDD/PLT			
SHEET INDEX			
C-000 COVER SHEET - BMP SUMMARY, DPIE CHECKLIST AND NOTES			
C-100 EXISTING CONDITIONS AND ENVIRONMENTAL FEATURES			
C-200 WATER MANAGEMENT AND DRAINAGE PLAN			
C-300 UTILITY, STREET LIGHT AND STREET TREE PLAN			
C-400 WINTER MAINTENANCE AND DE-ICE PLAN			
C-500 SEWAGE AND EROSION CONTROL PLAN			
C-600 DRAINAGE AREA MAP			

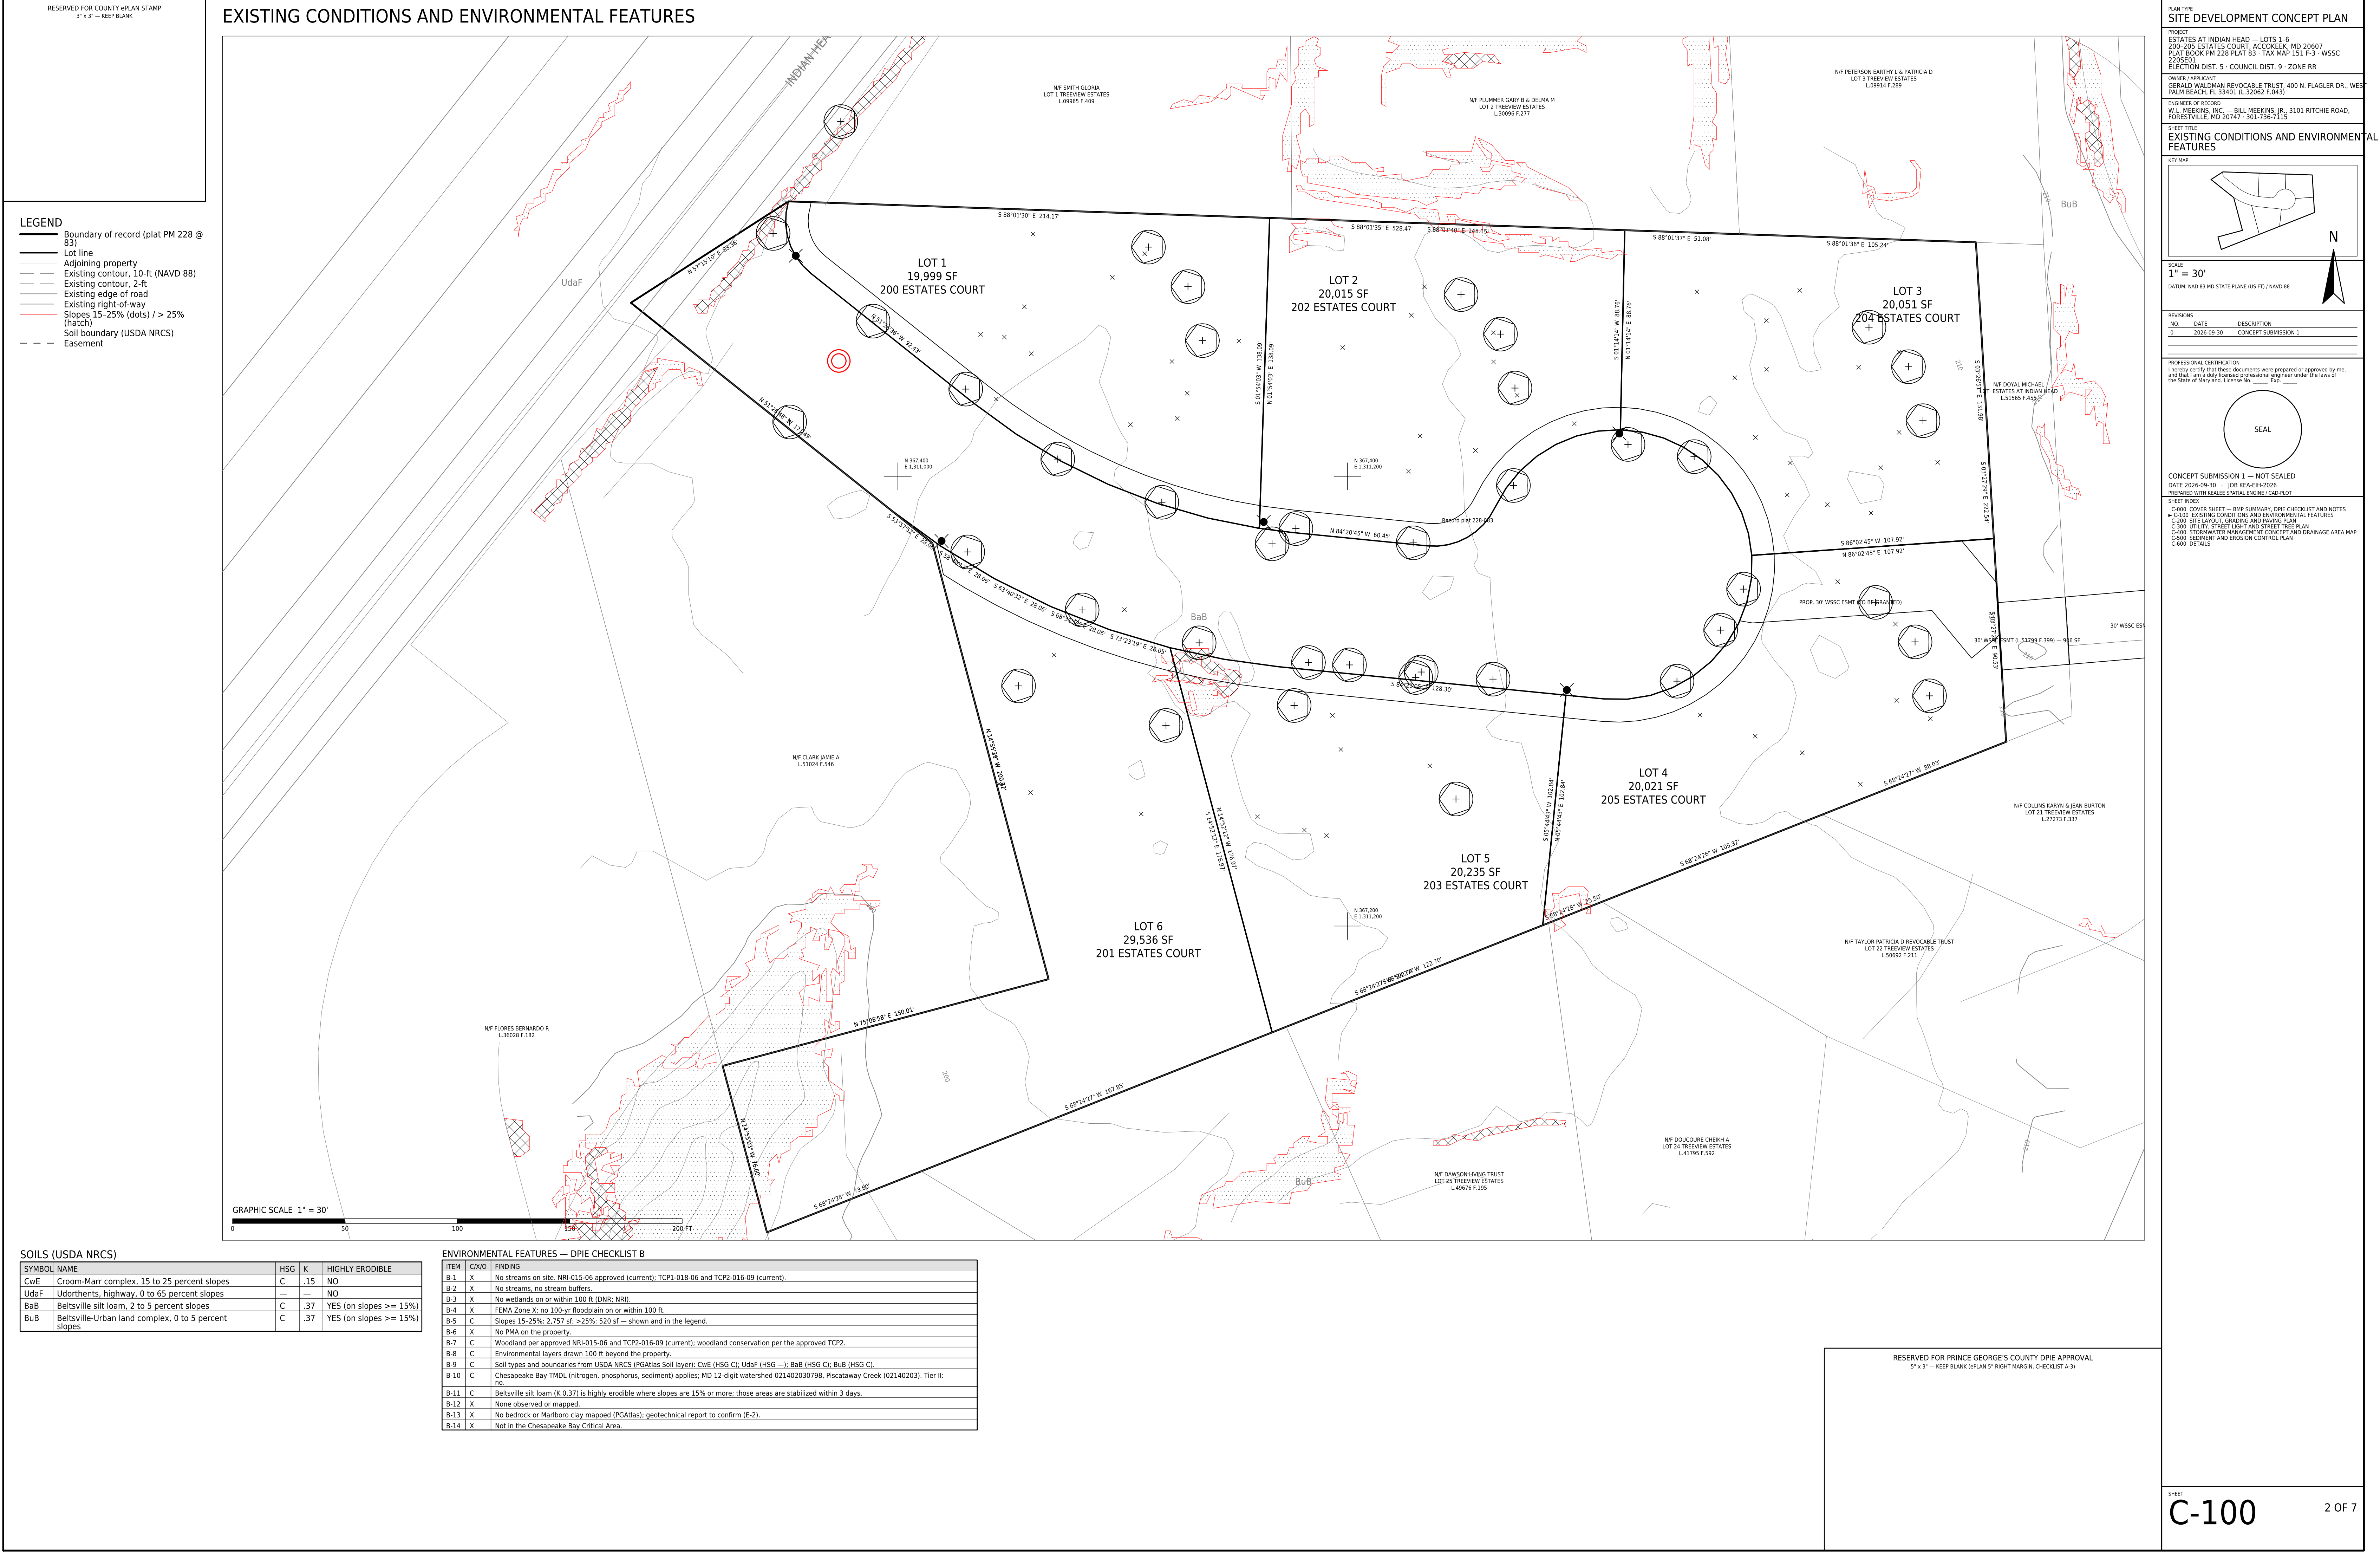

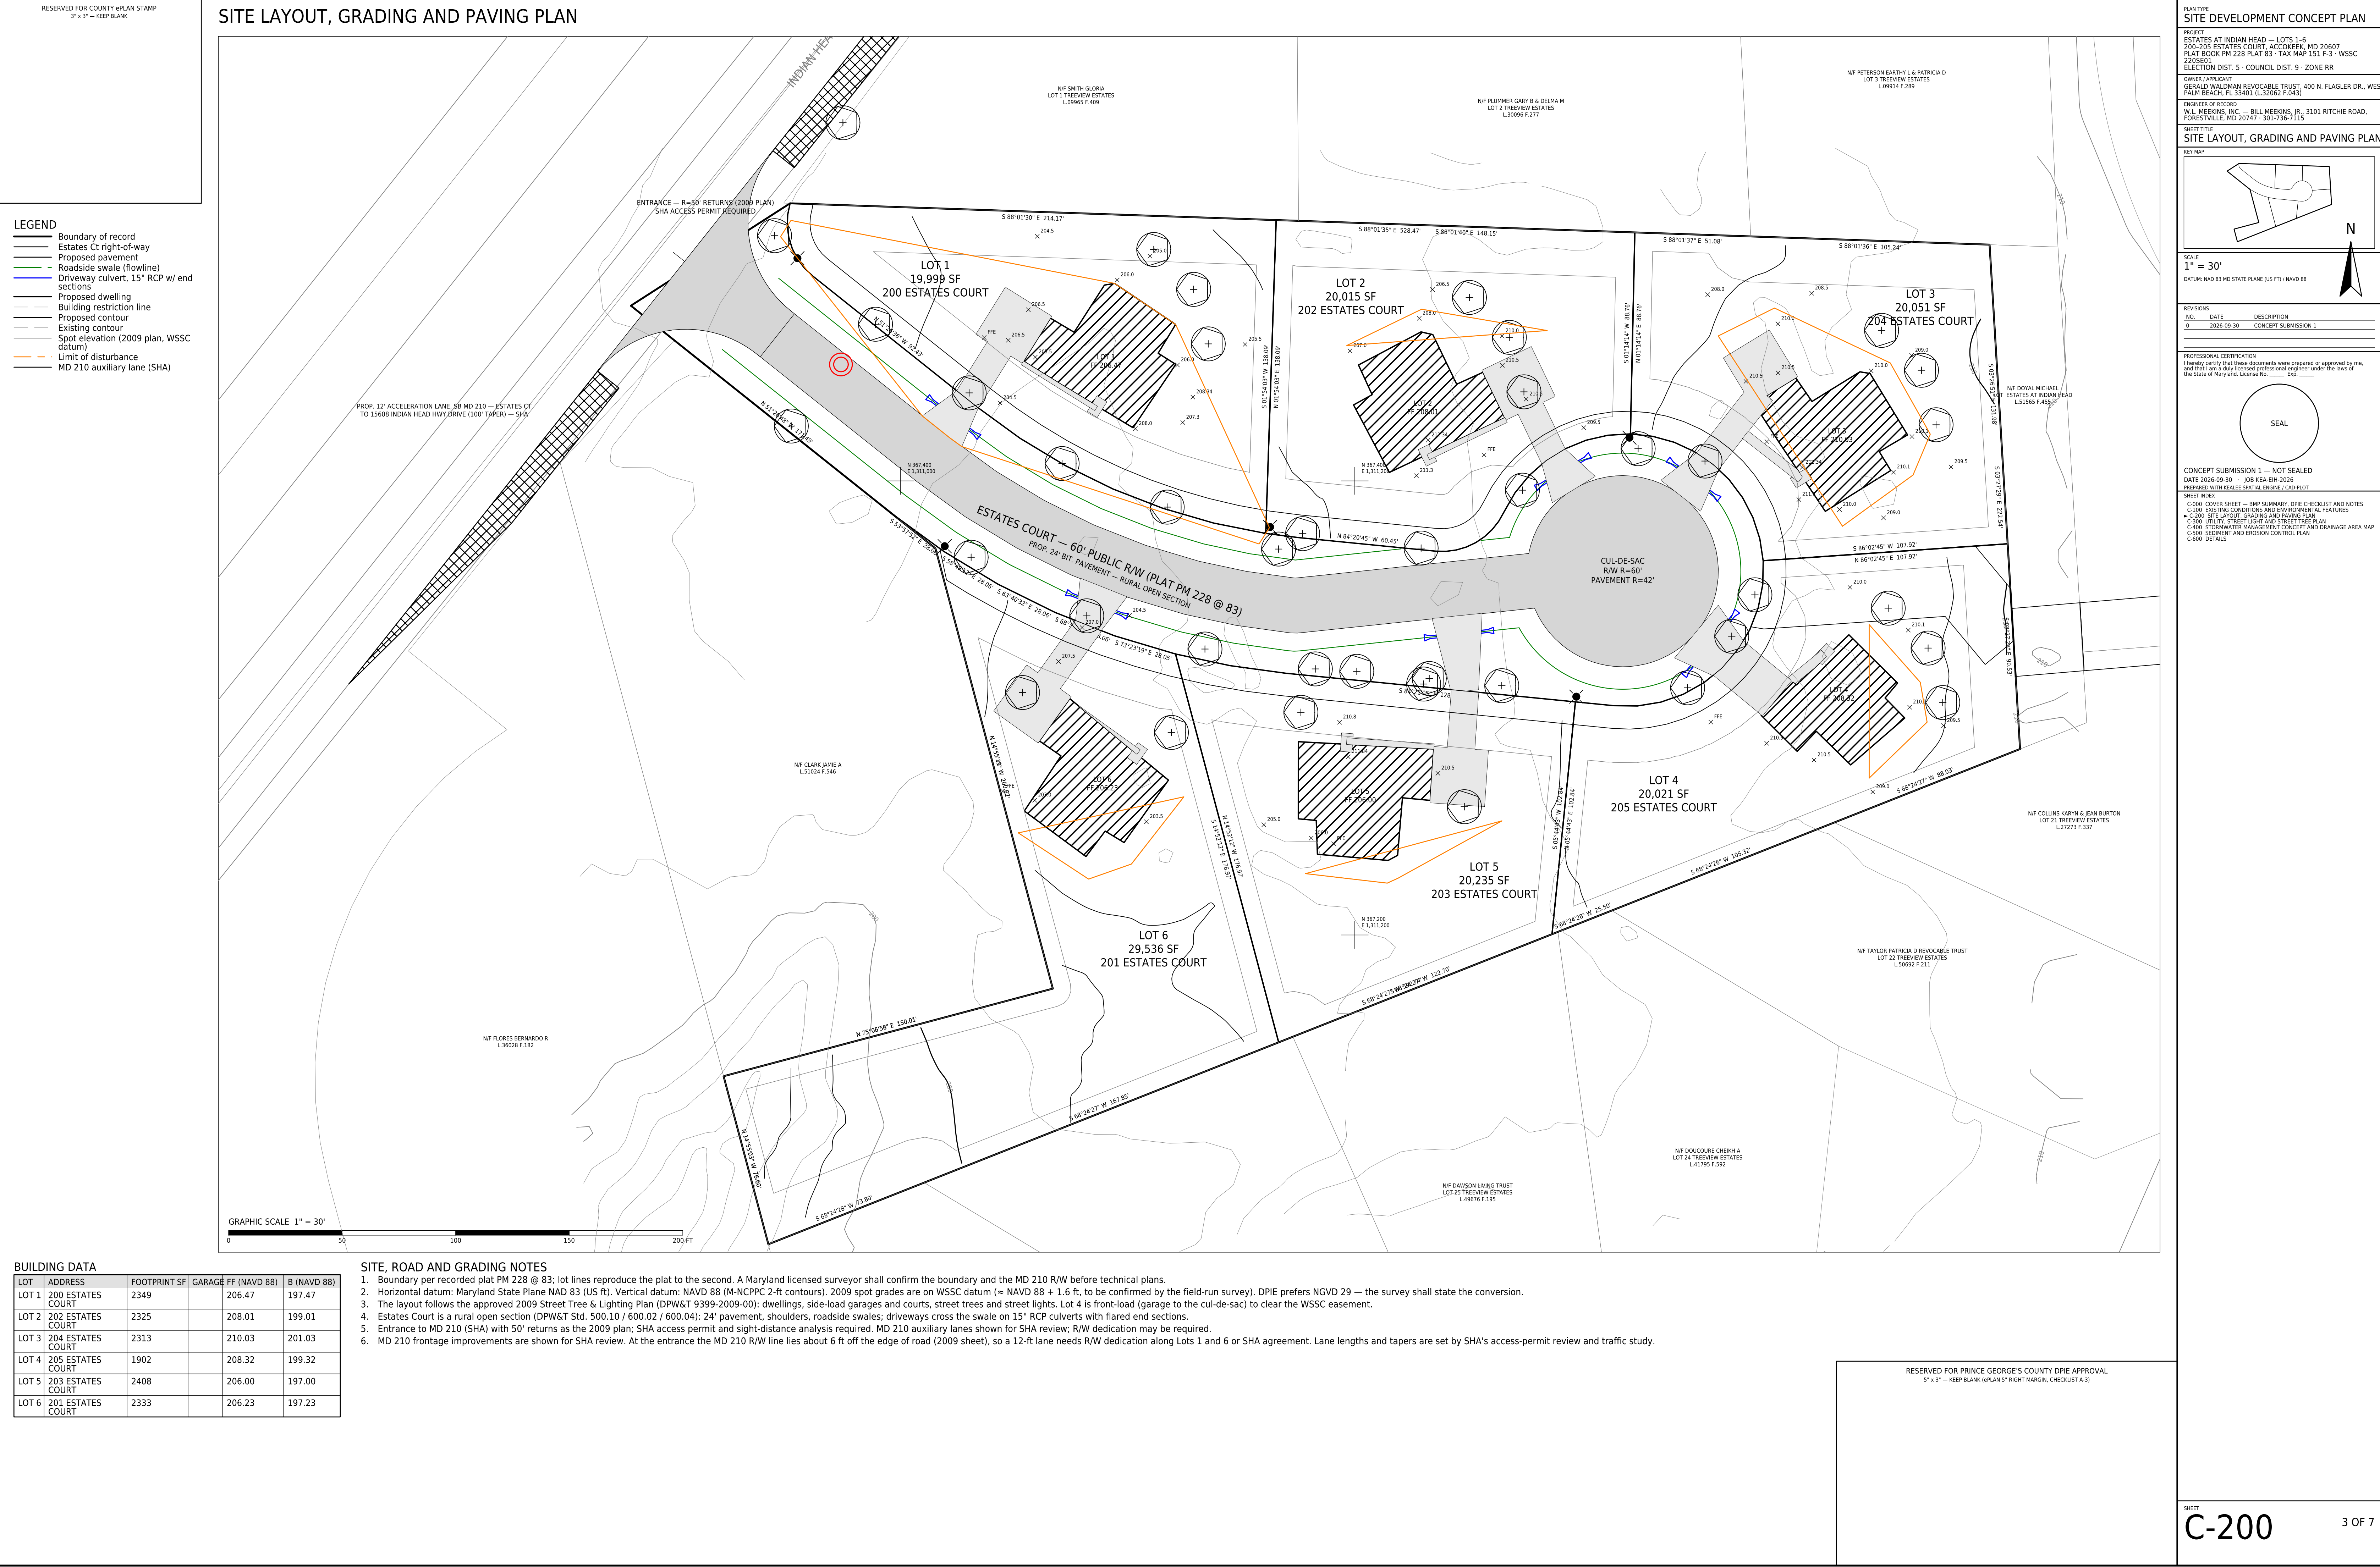

- Proposed 8" water main
- Proposed 8" sanitary sewer
- House connection
- - - WSSC easement (recorded / proposed)
- Street tree — Red Maple (2009 plan)
- Street light (2009 plan)

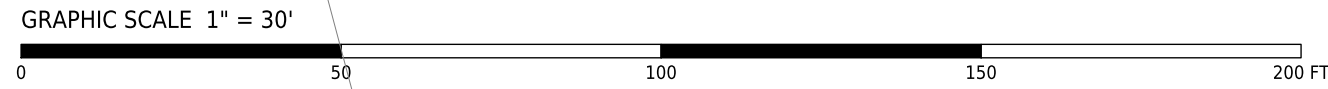


SYMBOL	QTY	ITEM	SIZE / TYPE	STANDARD
TREE	16	ACER RUBRUM — RED MAPLE	2 1/2"-3" CAL., B&B	DPW&T 600.02 / 600.04
LIGHT	5	STREET LIGHT (SMECO)	100 W HPS COLONIAL POST-TOSS, TYPE IV, BLACK FINGERGLASS	DPW&T 500.10

1. Water and sewer by WSSC (W-3-S-3). Mains from the existing WSSC mains in Henrietta Drive through the recorded 30' WSSC easement (L.51799 F.399, Outlot A and Lot 20) and a 30' WSSC easement to be granted across Lot 4 along the Lot 3/4 line.
2. Sizes and inverts of the Henrietta Drive mains to be verified on WSSC 200' sheet 220SE01 before technical design.
3. Street lights and street trees follow the approved 2009 Street Tree & Lighting Plan (DPW&T 9399-2009; light permit 09.09399); electric service by SMECO.
4. Keep street trees 10 ft from water meters and storm structures and 15 ft from street lights (DPW&T 600.02).
5. Contact Miss Utility (811) at least 48 hours before excavation.

RESERVED FOR PRINCE GEORGE'S COUNTY DPIE APPROVAL
5" x 3" — KEEP BLANK (ePLAN 5" RIGHT MARGIN, CHECKLIST A-3)

STORMWATER MANAGEMENT CONCEPT AND DRAINAGE AREA MAP

- LEGEND
- ESD practice — micro-bioretenction (M-6)
 - Roadside dry swale (M-8)
 - Drainage area to practice
 - Off-site area draining onto site
 - 100-yr overflow path
 - Point of investigation
 - Driveway culvert

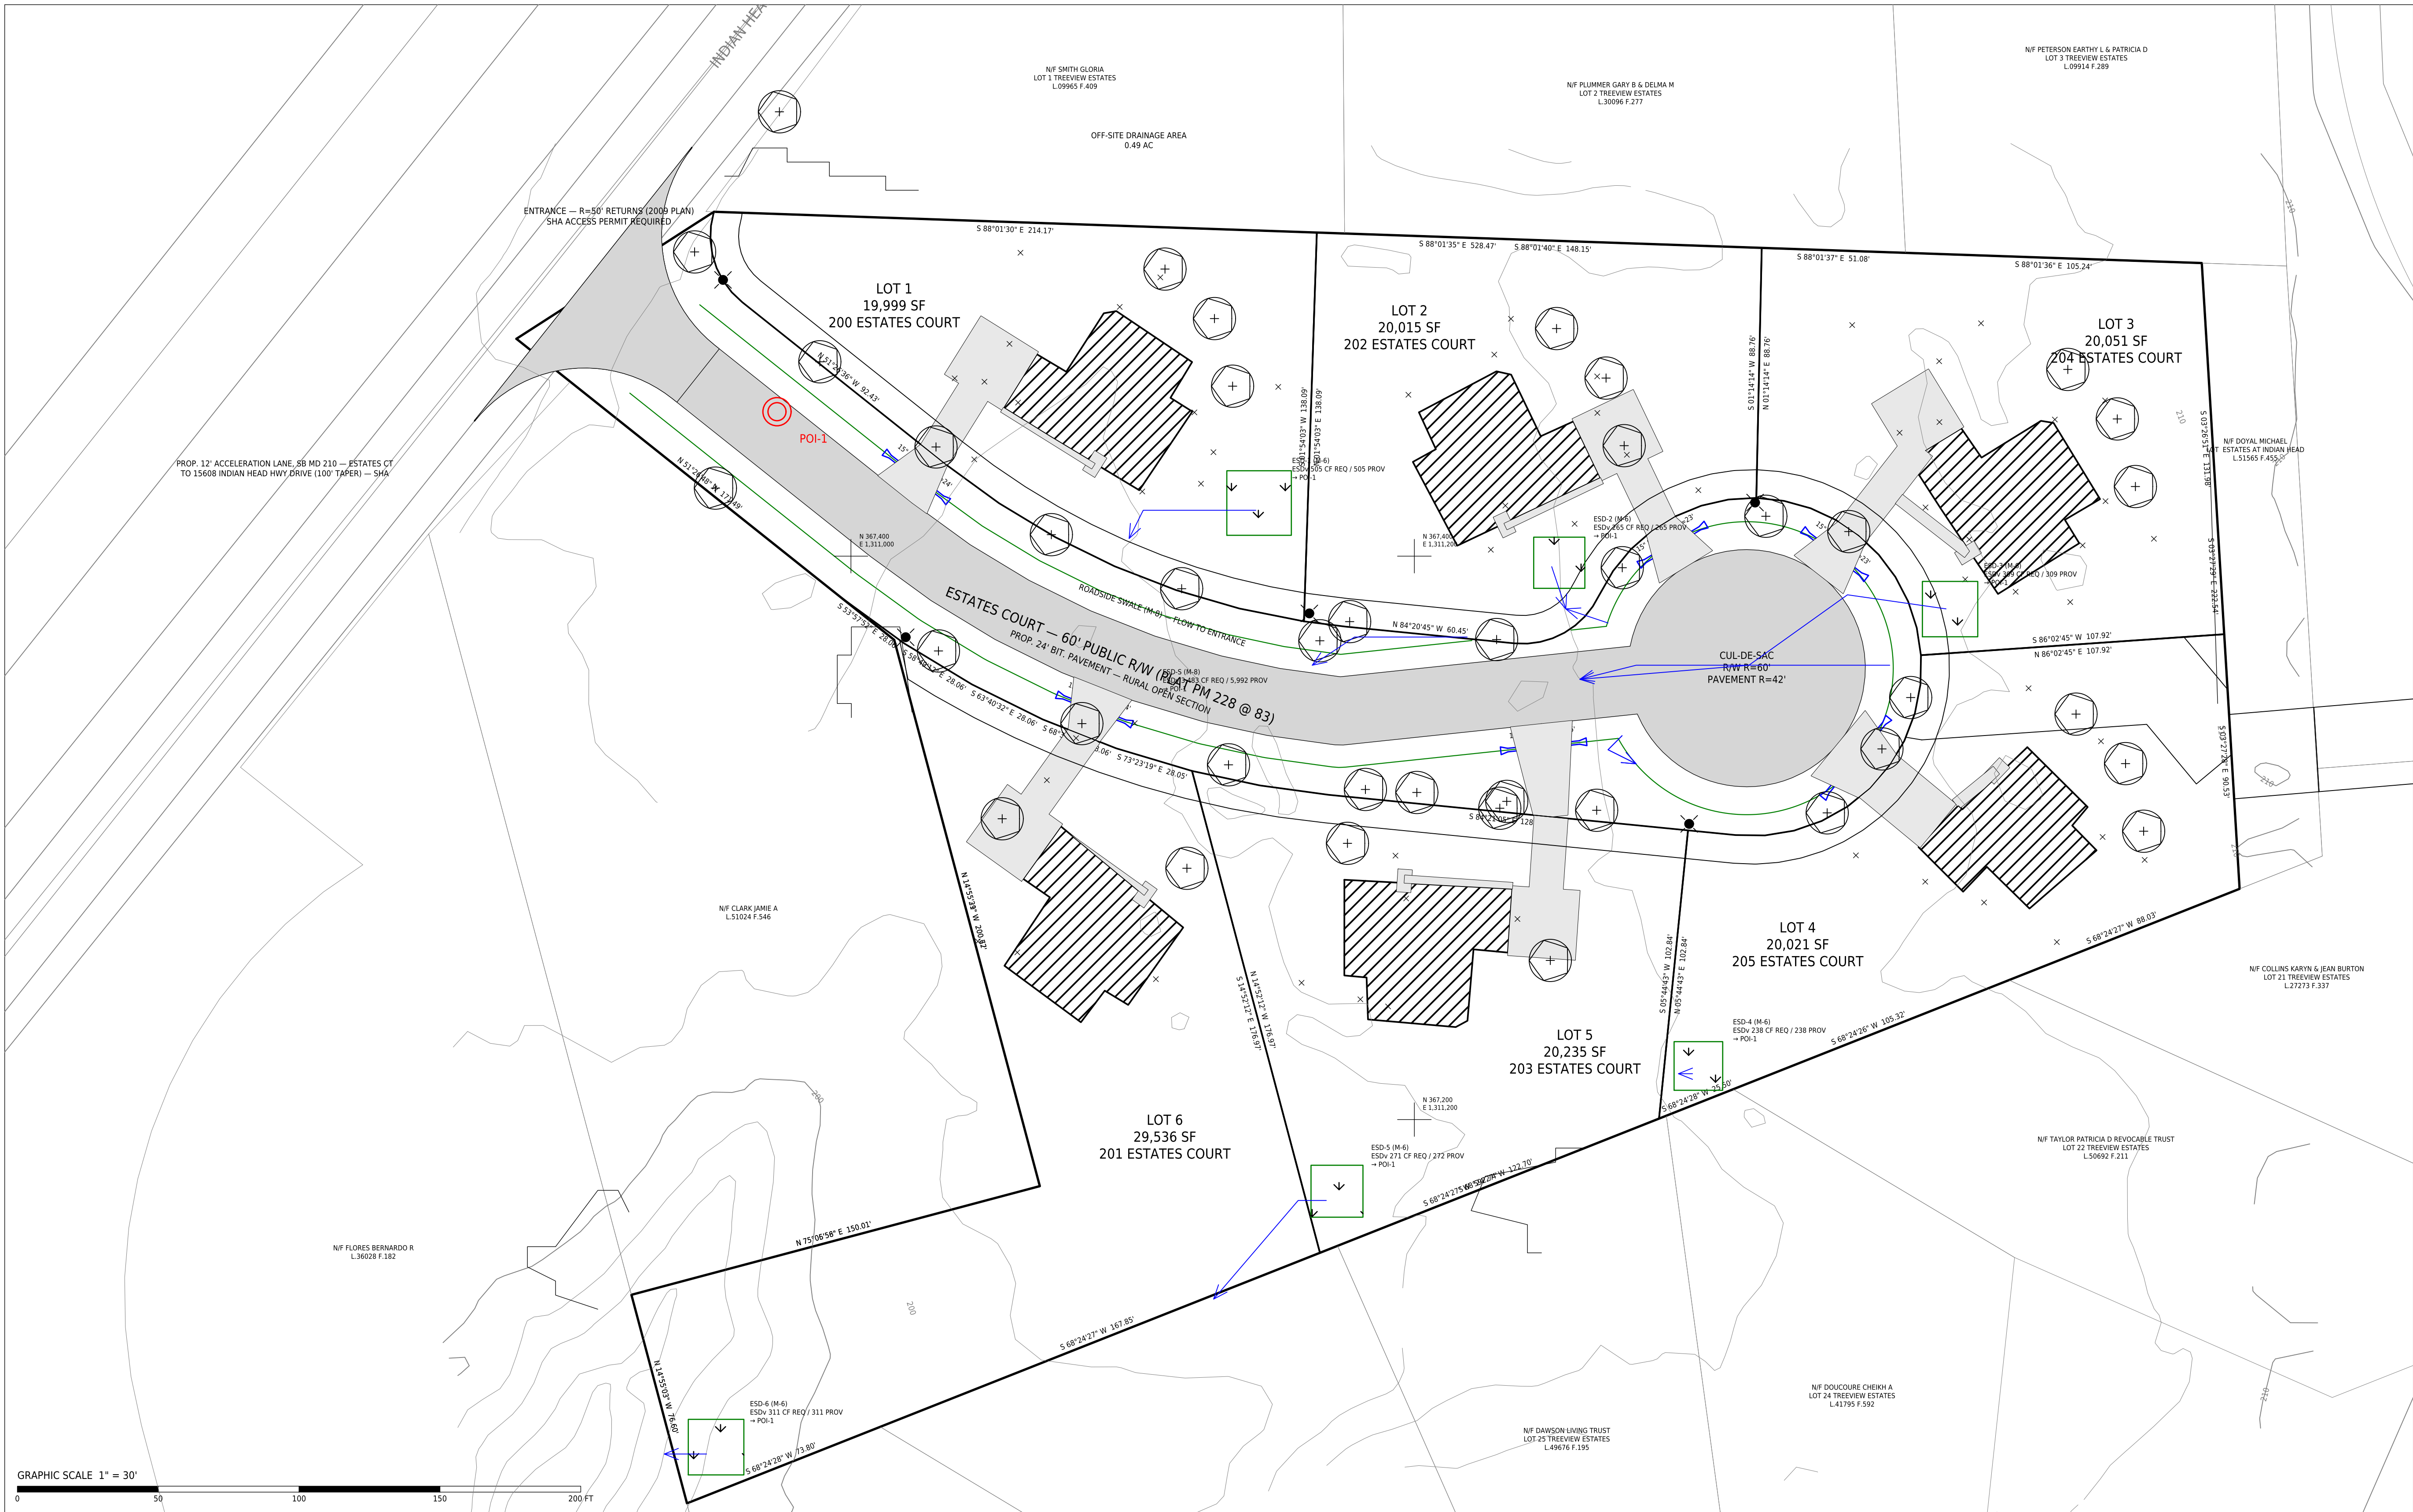

ESD PER PRACTICE (FULL TABLE ON C-000)

BMP	MDE	LOCATION	POI	DA SF	%I	P_E	ESDv REQ	ESDv PROV
ESD-1	M-6	Lot 1	POI-1	19,999	22.5	1.2	505	505
ESD-2	M-6	Lot 2	POI-1	20,015	12.1	1.0	265	265
ESD-3	M-6	Lot 3	POI-1	20,051	15.0	1.0	309	309
ESD-4	M-6	Lot 4	POI-1	20,021	10.3	1.0	238	238
ESD-5	M-6	Lot 5	POI-1	20,235	12.3	1.0	271	272
ESD-6	M-6	Lot 6	POI-1	29,536	8.5	1.0	311	311
ESD-5	M-8	Estates Ct R/W, both sides	POI-1	36,041	58.9	2.0	3,483	5,992

POINTS OF INVESTIGATION (C-9)

POI	LOCATION	SHARE	ESDv REQ	ESDv PROV
POI-1	N 367,451 E 1,310,974	100%	5,382	7,892

SWM NOTES

- SWM by Environmental Site Design to the MEP (Md. Stormwater Management Act of 2007; MDE Design Manual Ch. 5; PCG Subtitle 32). Target rainfall P_E from MDE Table 5.3 for HSG C at each drainage area's imperviousness.
- Each lot drains to one micro-bioretenction cell (M-6): 12-in max. ponding; 2.5-ft filter media; underdrain to a stable outfall. Estates Court drains to roadside dry swales (M-8) with check dams.
- Rooftop and non-rooftop disconnection (N-1, N-2) to be credited at technical design. Infiltration credit only where Sec. 32-131 borings show ≥ 0.52 in/hr.
- Private ESD practices: maintenance agreement recorded before permit; public swales in the R/W maintained by DPPE.
- D8 flow routing on a 5-ft surface interpolated from the existing 2-ft contours; exit points clustered at 120 ft; POIs carrying under 4% of the site omitted. Concept-level — reset from the field-run survey.


PLAN TYPE
SITE DEVELOPMENT CONCEPT PLAN

PROJECT
ESTATES AT INDIAN HEAD — LOTS 1-6
200-205 ESTATES COURT, ACCOKEEK, MD 20607
PLAT BOOK PW 228 PLAT 83 TAX MAP 151 F-3 - WSSC
220501
ELECTION DIST. 5 COUNCIL DIST. 9 ZONE RR

OWNER / APPLICANT
GERALD WALDMAN REVOCABLE TRUST, 400 N. FLAGLER DR., WEST PALM BEACH, FL 33401 (L32062 F.043)

ENGINEER OF RECORD
W.L. MECKINS, INC. — BILL MECKINS, JR., 3101 RITCHIE ROAD, FORESTVILLE, MD 20747 301-736-7115

SHEET TITLE
STORMWATER MANAGEMENT CONCEPT AND DRAINAGE AREA MAP

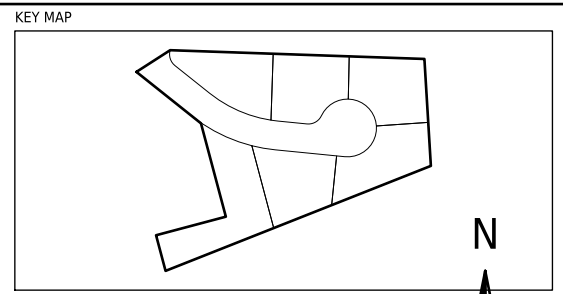

SCALE
1" = 30'

DATUM: NAD 83 MD STATE PLANE (US FT) / NAD83


REVISIONS	NO.	DATE	DESCRIPTION
1	2026-09-30	CONCEPT SUBMISSION 1	

PROFESSIONAL CERTIFICATION
I hereby certify that these documents were prepared or approved by me, and that I am a duly licensed professional engineer under the laws of the State of Maryland. License No. _____ E.O. _____




CONCEPT SUBMISSION 1 — NOT SEALED

DATE 2026-09-30 JOB KEA-EH-2026
DRAWN WITH SCALE 3/32"=1' ENGINEER / C-000-001


SHEET INDEX
C-000 COVER SHEET — BMP SUMMARY, DPPE CHECKLIST AND NOTES
C-100 EXISTING CONDITIONS AND ENVIRONMENTAL FEATURES
C-200 SITE LAYOUT, GRADING AND PAVING PLAN
C-300 UTILITY, STREET LIGHT AND STREET TREE PLAN
C-400 STORMWATER MANAGEMENT CONCEPT AND DRAINAGE AREA MAP
C-500 SEDIMENT AND EROSION CONTROL PLAN
C-600 DETAILS

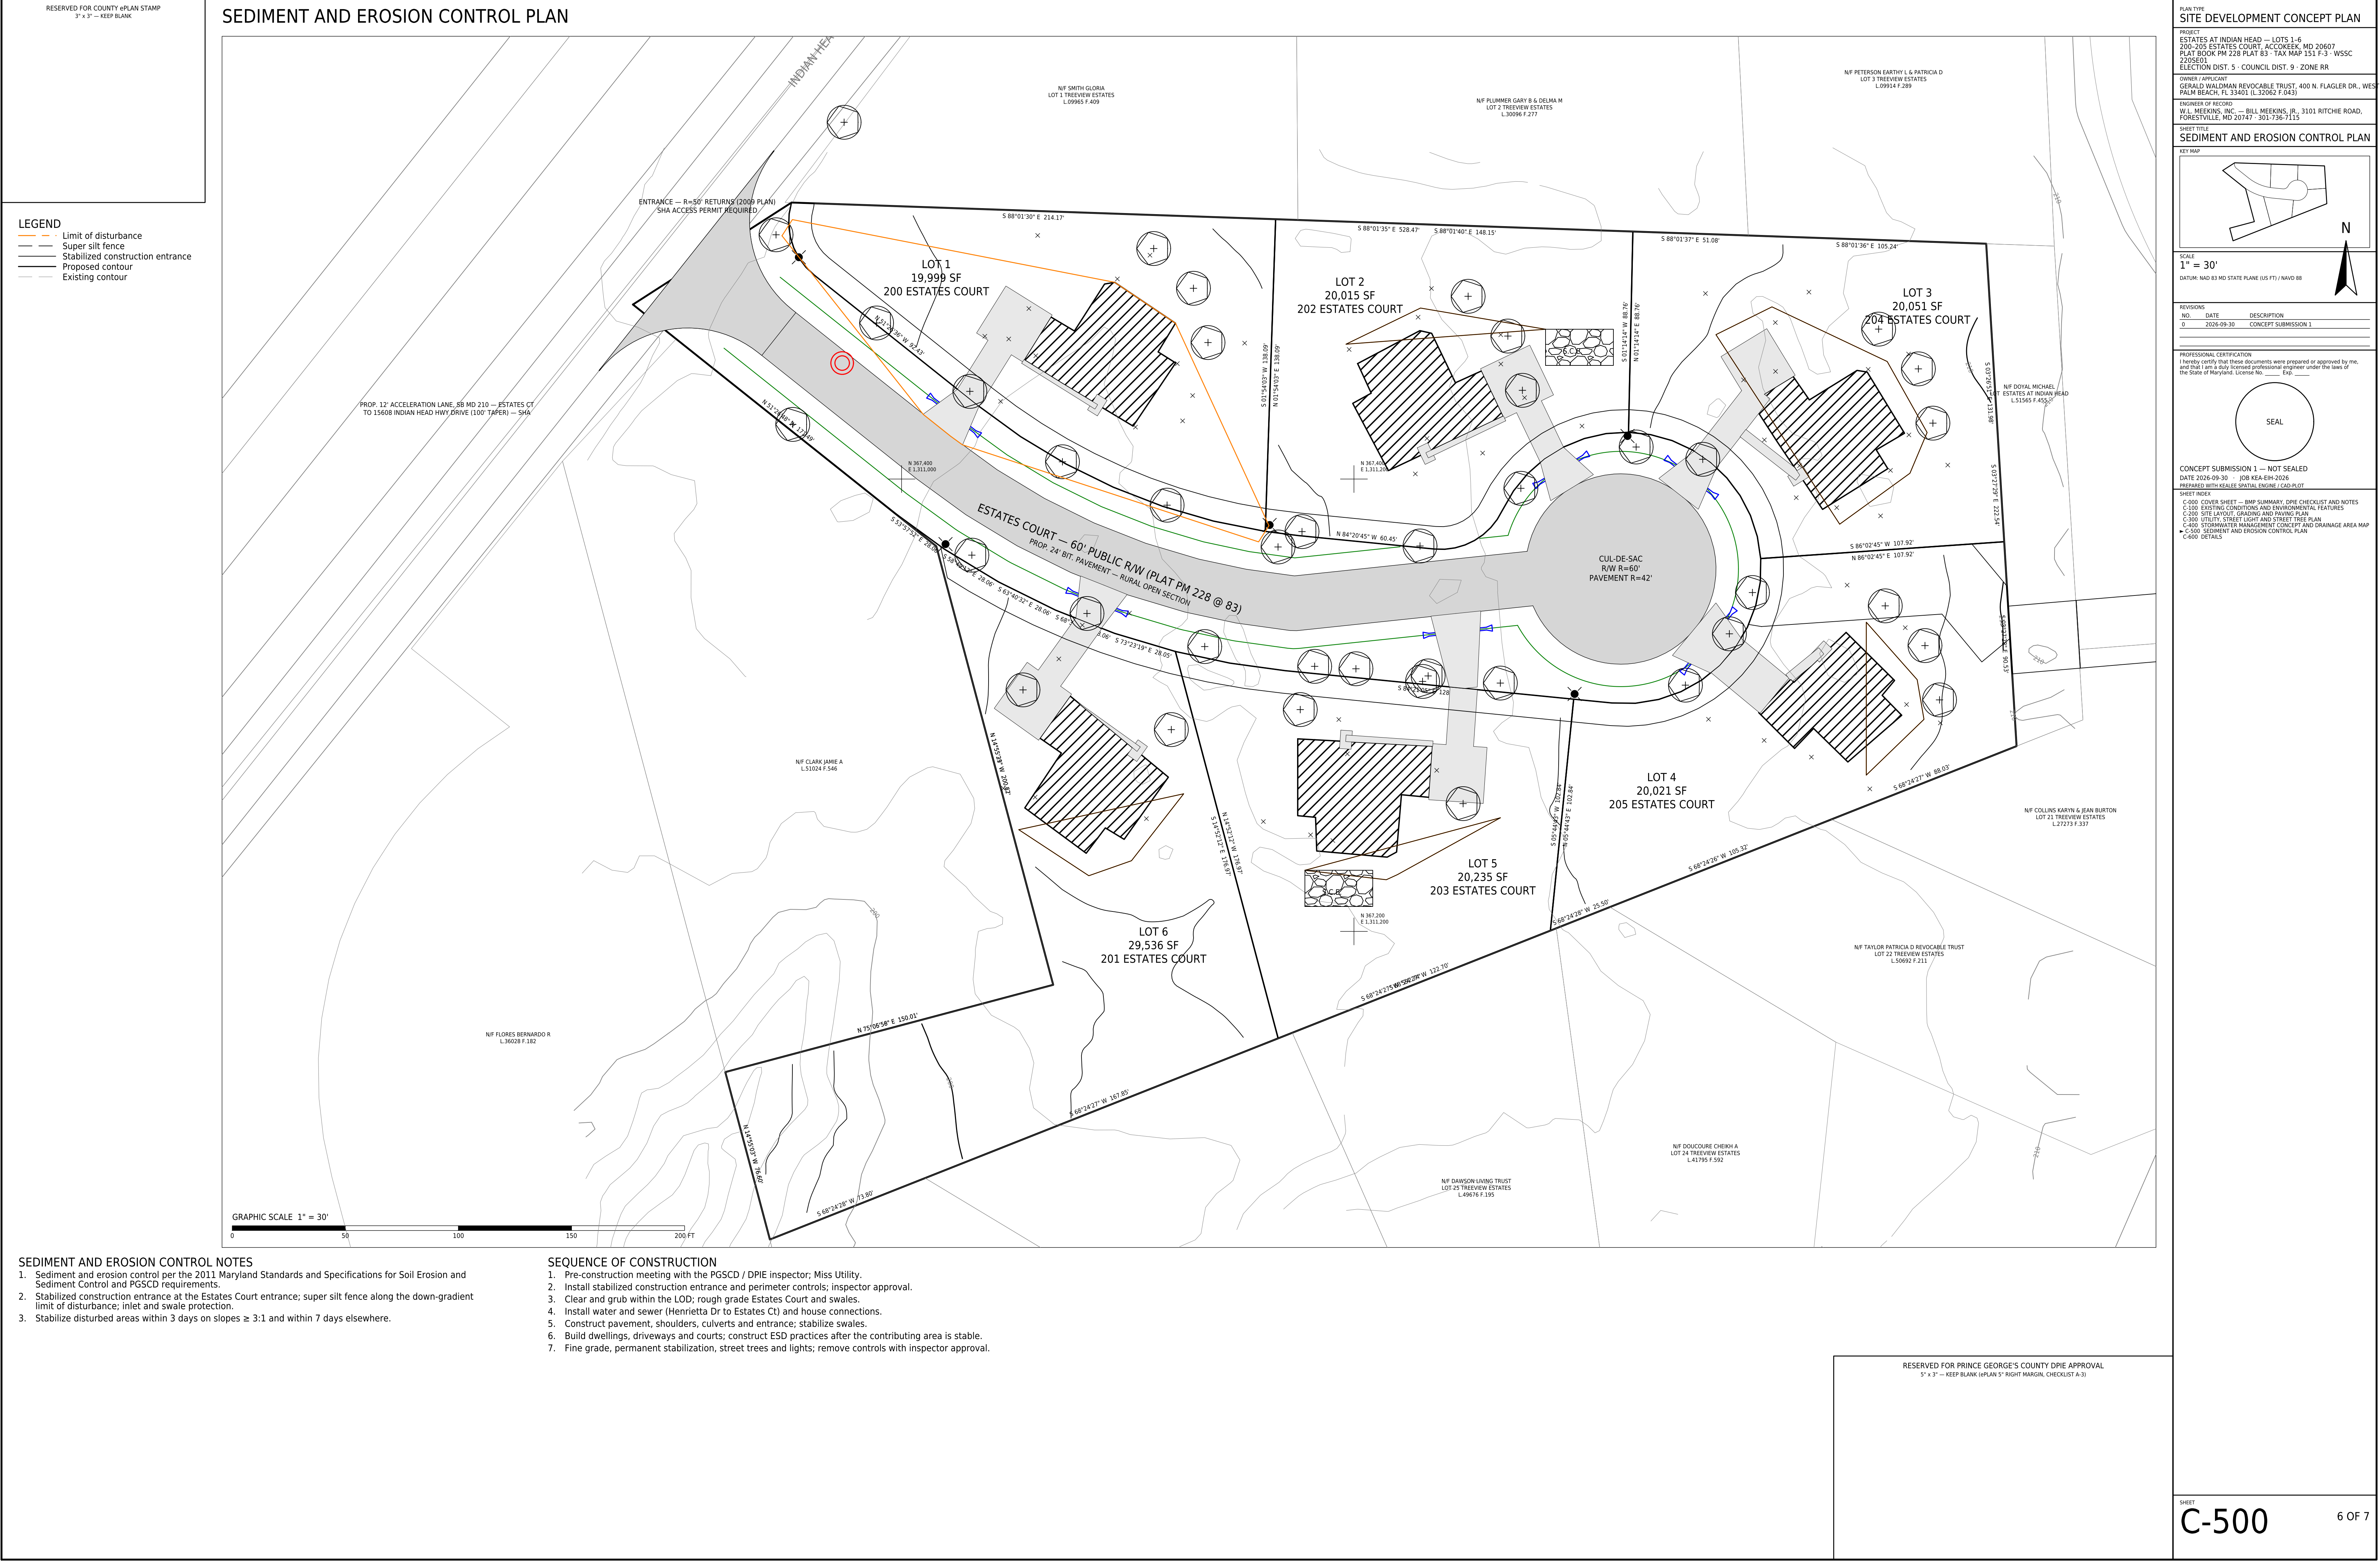

DETAILS

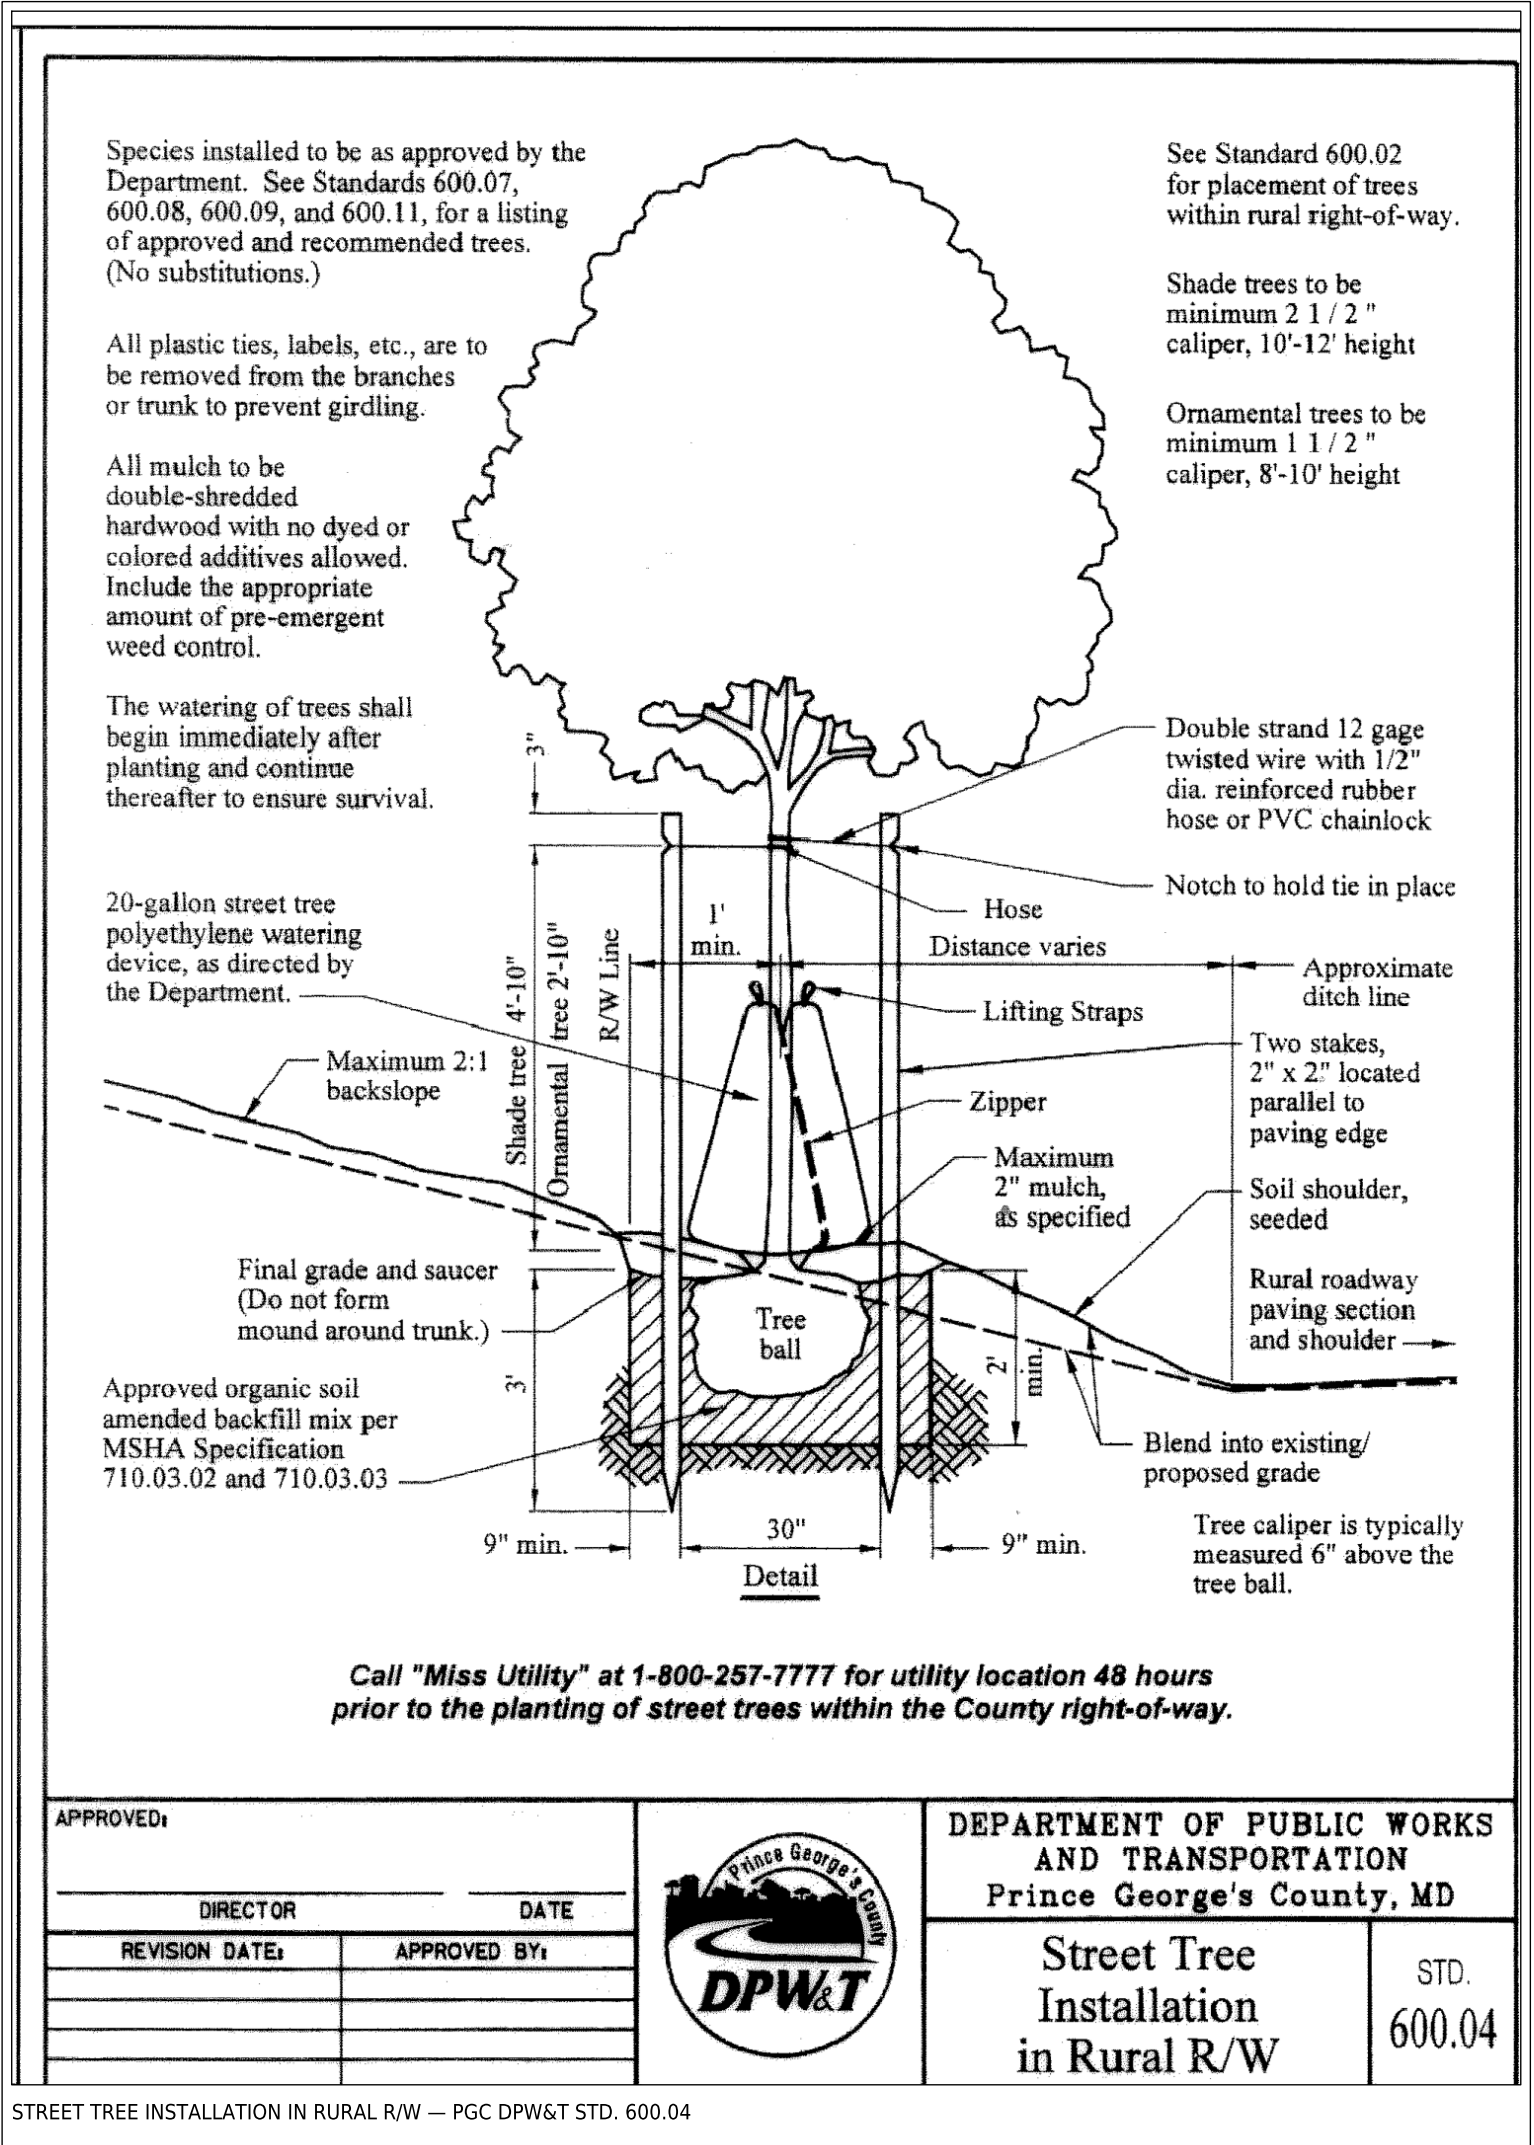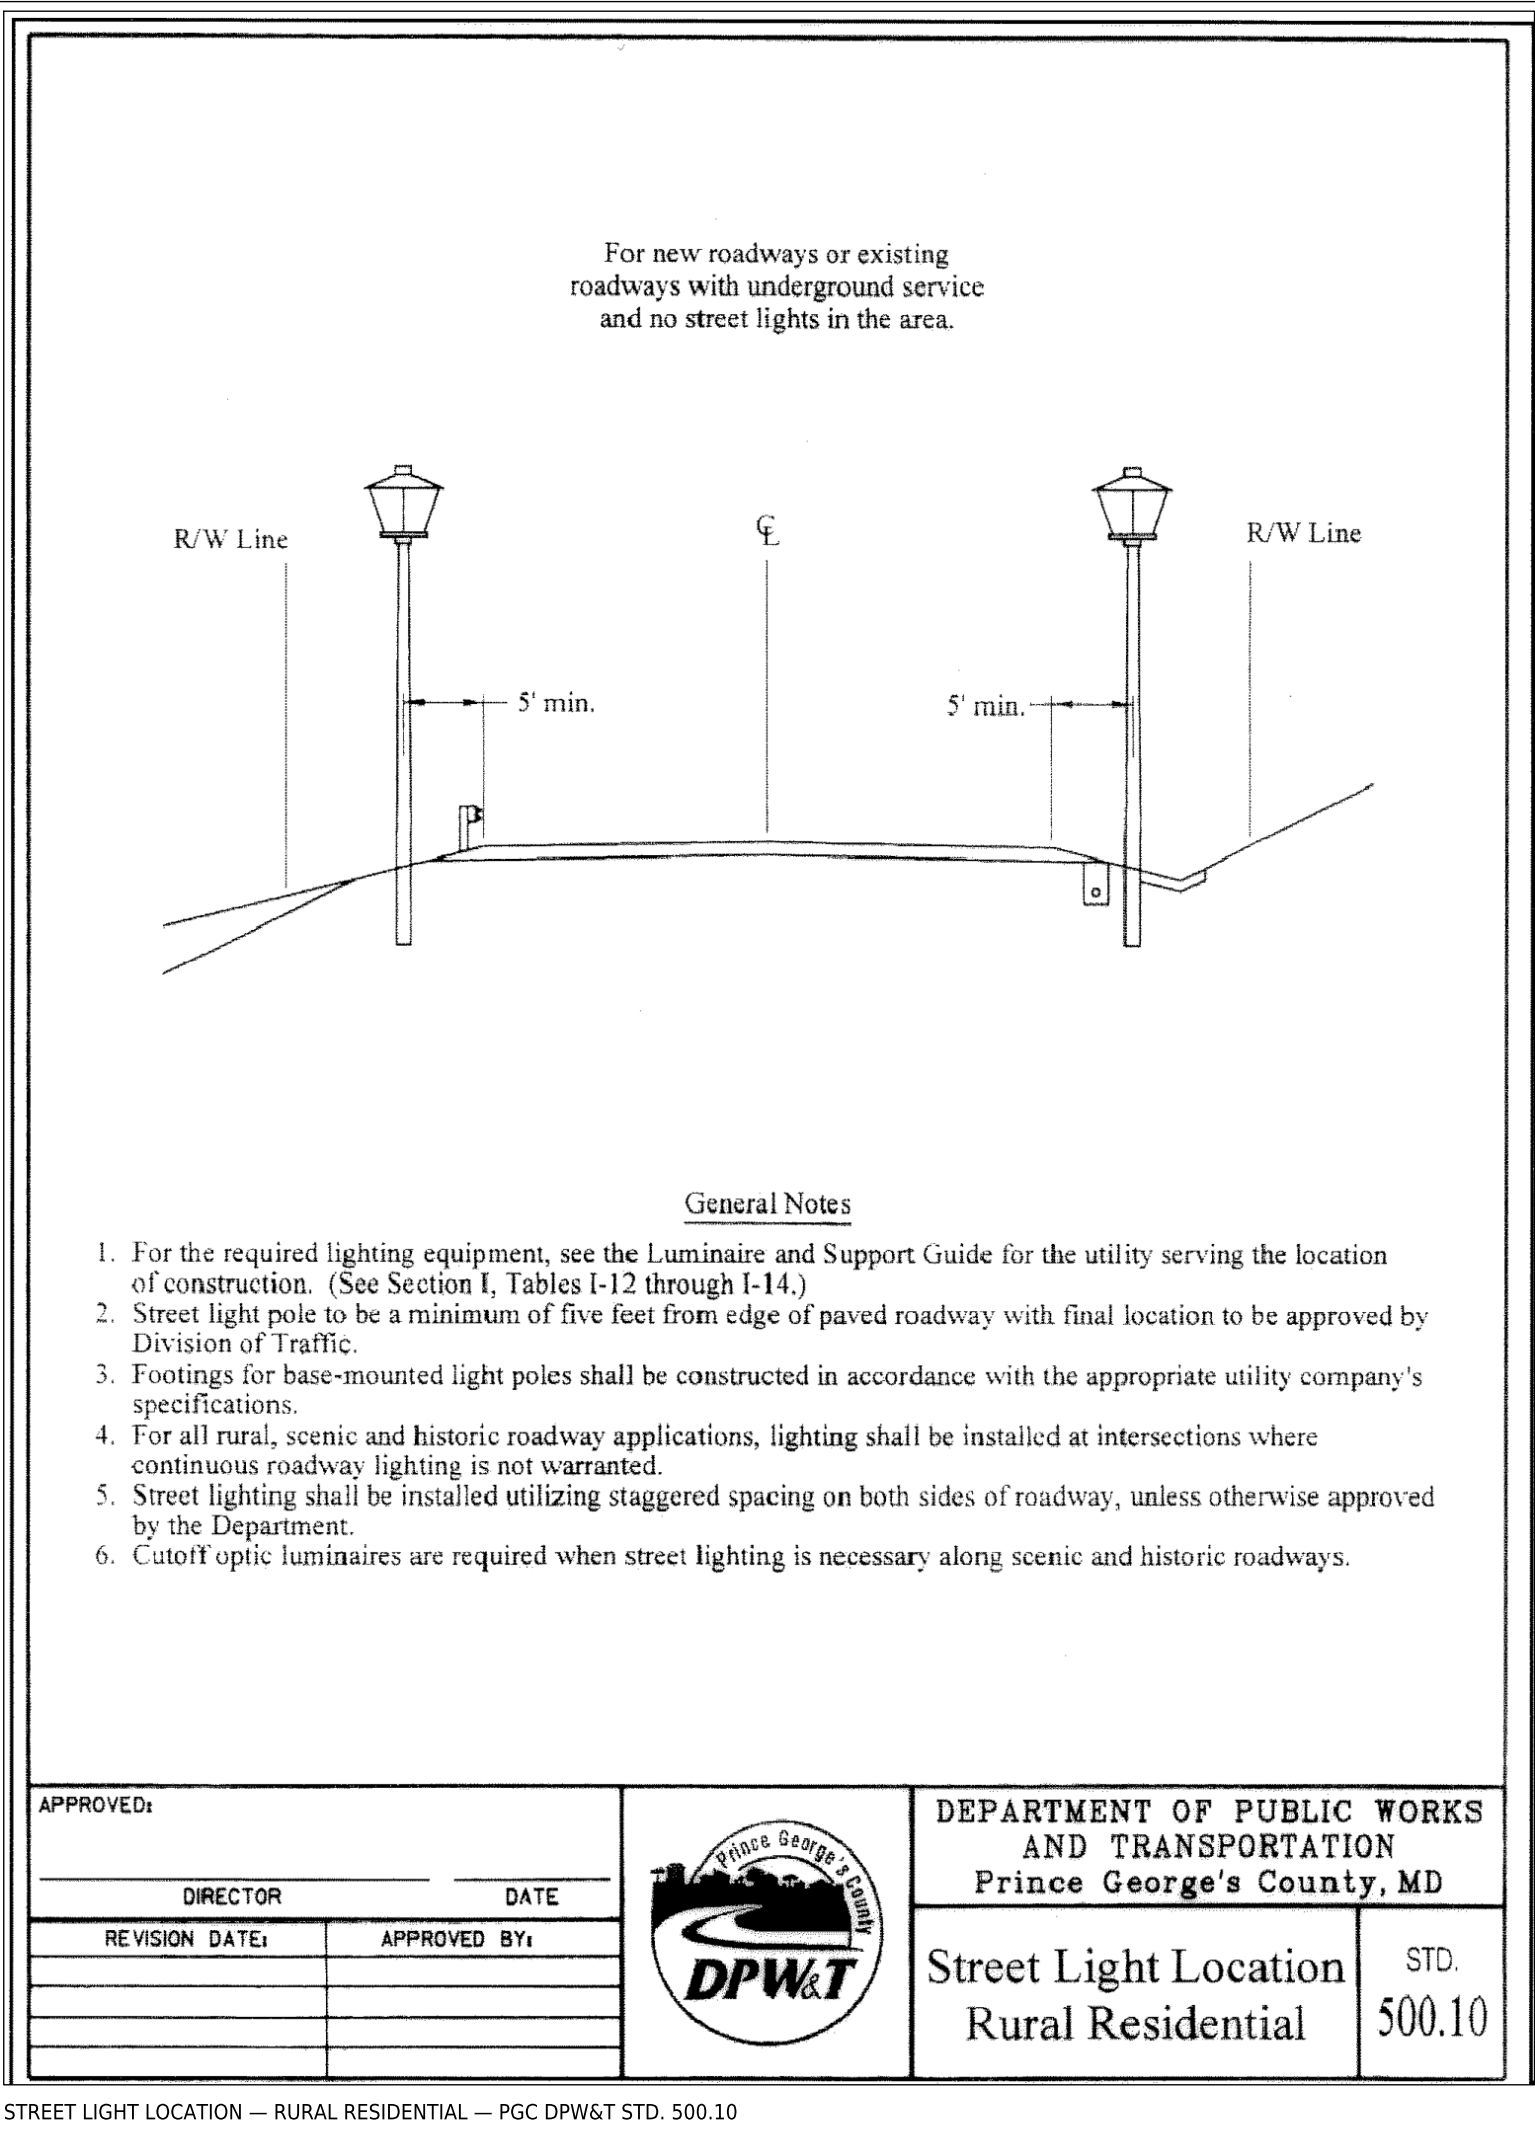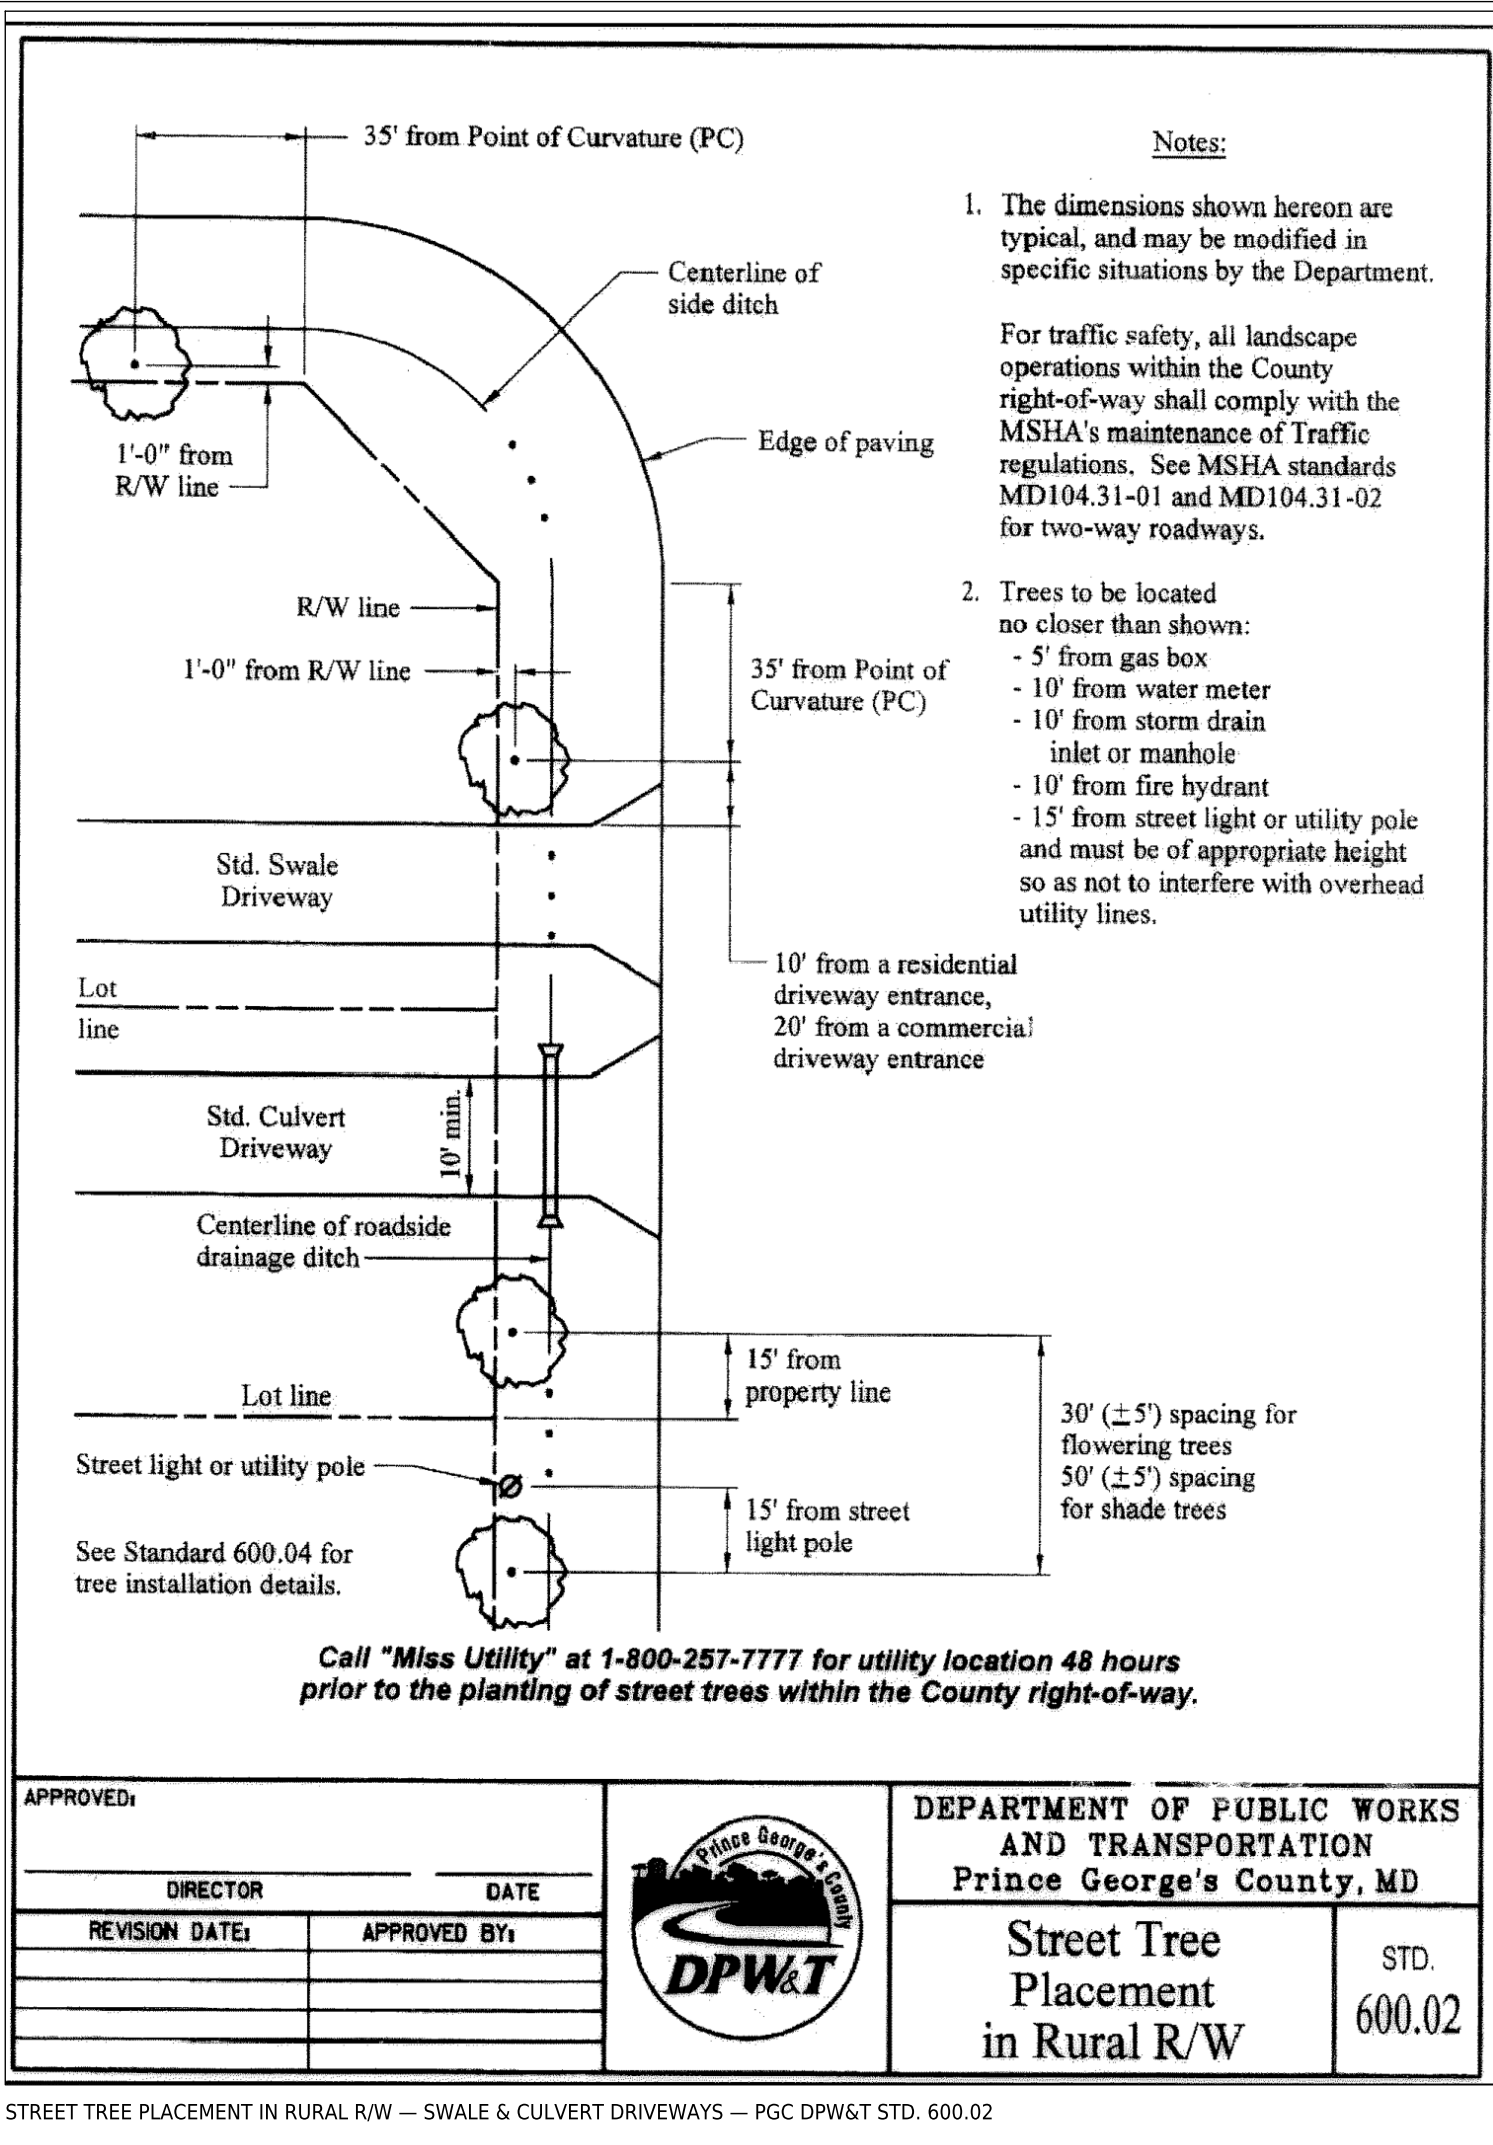


ESTATES COURT — TYPICAL SECTION (RURAL OPEN SECTION, 60' R/W)

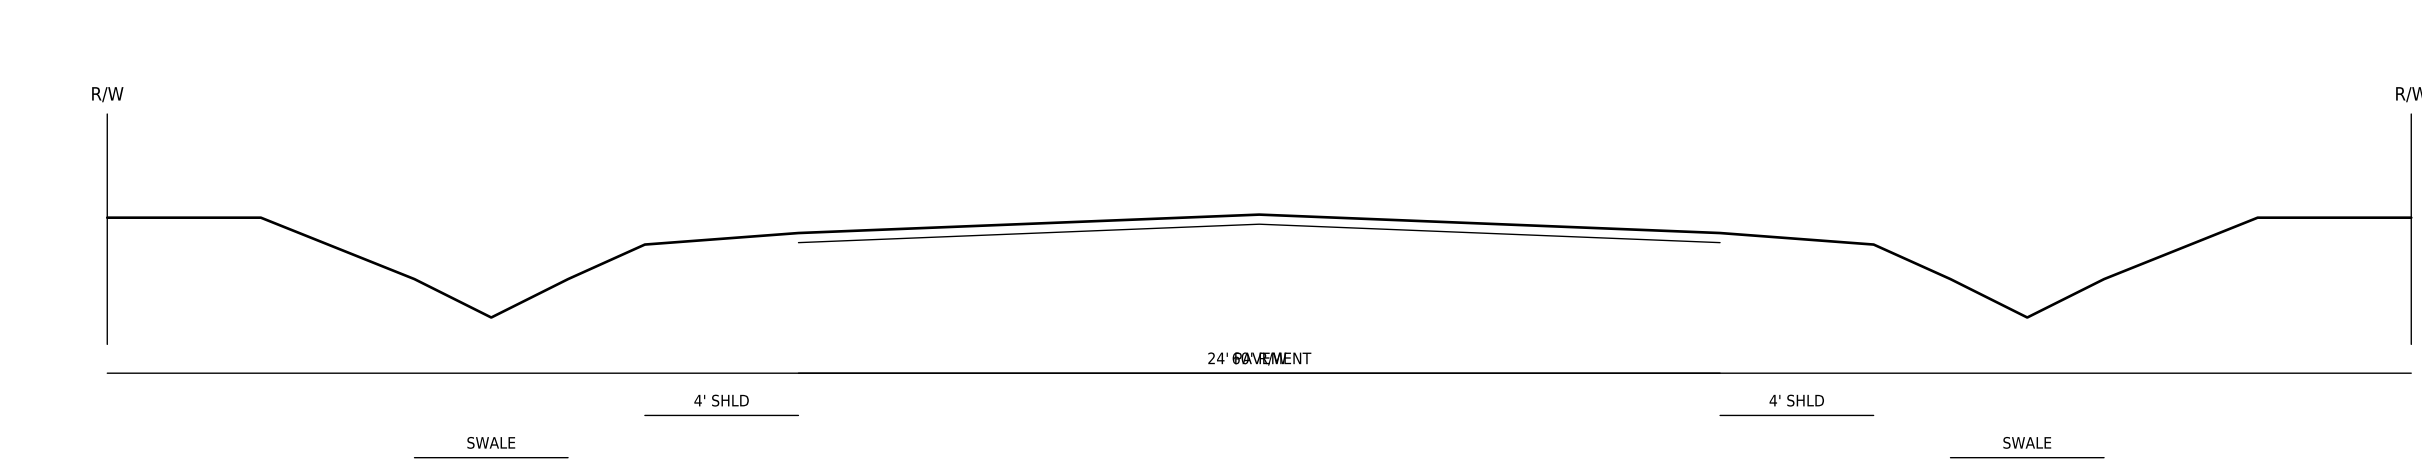


1.1/2" SURFACE + 2.1/2" BASE BIT. CONC. ON 6" GAB (DPW&T PAVEMENT SCHEDULE FOR RURAL RESIDENTIAL — CONFIRM)
CROSS SLOPE 2%; 4-FT STABILIZED SHOULDERS, SWALE FLOWLINE 20 FT OFF CENTRELINE, 3:1 SIDE SLOPES
DRIVEWAYS CROSS THE SWALE ON 15" RCP CULVERTS WITH FLARED END SECTIONS (DPW&T STD. 600.02)

MICRO-BIORETENTION (M-6) — TYPICAL SECTION

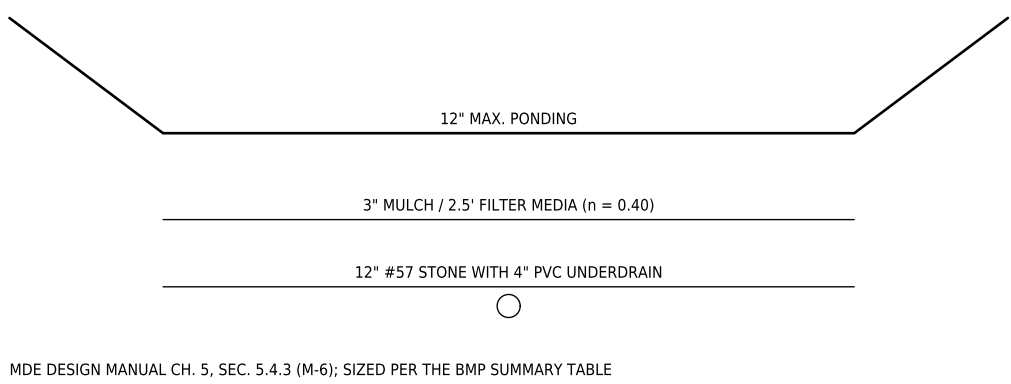

DRY SWALE (M-8) WITH CHECK DAM

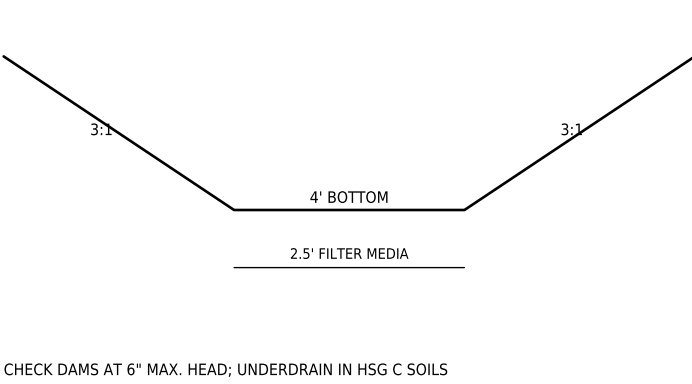

PLAN TYPE
SITE DEVELOPMENT CONCEPT PLAN

PROJECT
ESTATES AT INDIAN HEAD — LOTS 1-6
200-205 ESTATES COURT, ACCOKEEK, MD 20607
PLAT BOOK PM 226 PLAT 83 TAX MAP 151 P-3 WSSC
2206E01
ELECTION DIST. 5 - COUNCIL DIST. 9 - ZONE RR

OWNER / APPLICANT
GERALD WALDMAN REVOCABLE TRUST, 400 N. FLAGLER DR., WEST
PALM BEACH, FL 33401 (L-32062.F-043)

ENGINEER OF RECORD
W.L. MEEKINS, INC. — BILL MEEKINS, JR., 3101 RITCHIE ROAD,
FONTSVILLE, MD 20747 - 301-736-7115

SHEET TITLE
DETAILS

KEY MAP

SCALE
AS NOTED
DATUM: NAD 83 MD STATE PLANE (US FT) / NAVD 88

REVISIONS

NO.	DATE	DESCRIPTION
0	2026-09-30	CONCEPT SUBMISSION 1

PROFESSIONAL CERTIFICATION
I hereby certify that these documents were prepared or approved by me,
and that I am a duly licensed professional engineer under the laws of
the State of Maryland. License No. _____ Exp. _____

SEAL

CONCEPT SUBMISSION 1 — NOT SEALED
DATE 2026-09-30 JOB KEA-EH-2026
PREPARED WITH KRAUSE SPOTIAL ENGINE / CAD-PILOT

SHEET INDEX
C-600 COVER SHEET — BMP SUMMARY, DPE CHECKLIST AND NOTES
C-200 SITE SUSTAINING CONDITIONS AND ENVIRONMENTAL FEATURES
C-300 SITE EROSION, GRADING AND PAVING PLAN
C-300 UTILITY, STREET LIGHT AND STREET TREE PLAN
C-400 STORMWATER MANAGEMENT CONCEPT AND DRAINAGE AREA MAP
C-500 SEDIMENT AND EROSION CONTROL PLAN
C-600 DETAILS