

ESTATES AT INDIAN HEAD — LOTS 1-6

200-205 ESTATES COURT, ACCOKEEK, MD 20607 · PLAT BOOK PM 228 PLAT 83 · TAX MAP 151 F-3 · WSSC 220SE01 · ELECTION DIST. 5 · COUNCIL DIST. 9 · ZONE RR

Stormwater management by Environmental Site Design to the Maximum Extent Practicable (MDE Design Manual Ch. 5; PGC Subtitle 32). New submittal; base layout from the prior 2009 Street Tree & Lighting Plan, DPW&T 9399-2009-00.

PRINCE GEORGE'S COUNTY BMP SUMMARY TABLE — ESD BY POINT OF INVESTIGATION (A-15, C-9)

BMP	PRACTICE	MDE	LOCATION	OWNERSHIP / MAINT.	POI	DA SF	IMP SF	%	HSG	P	E	In	Rv	ESDv REQ CF	ESDv PROV CF	Rev REQ CF	SURFACE SF	COORDINATES (NAD 83)
ESD-1	Micro-bioretentation	M-6	Lot 1	Private — lot owner (maintenance agreement)	POI-1	19,999	4,500	22.5	C	1.2	0.253	505		55	55	525		N 367,417 E 1,311,443
ESD-2	Micro-bioretentation	M-6	Lot 2	Private — lot owner (maintenance agreement)	POI-1	20,015	2,422	12.1	C	1.0	0.159	265		265	34	330		N 367,396 E 1,311,250
ESD-3	Micro-bioretentation	M-6	Lot 3	Private — lot owner (maintenance agreement)	POI-1	20,051	3,008	15.0	C	1.0	0.185	309		309	40	386		N 367,378 E 1,311,388
ESD-4	Micro-bioretentation	M-6	Lot 4	Private — lot owner (maintenance agreement)	POI-1	20,021	2,062	10.3	C	1.0	0.143	238		238	31	298		N 367,217 E 1,311,299
ESD-5	Micro-bioretentation	M-6	Lot 5	Private — lot owner (maintenance agreement)	POI-1	20,235	2,489	12.3	C	1.0	0.161	271		272	35	340		N 367,173 E 1,311,171
ESD-6	Micro-bioretentation	M-6	Lot 6	Private — lot owner (maintenance agreement)	POI-1	29,536	2,511	8.5	C	1.0	0.127	311		311	40	389		N 367,082 E 1,310,950
ESD-5	Roadside dry swales w/ check dams (099 LF)	M-8	Estates Ct R/W, both sides	Public — DPJE	POI-1	36,041	21,216	58.9	C	2.0	0.580	3,483		5,992	226	3,995		N 367,342 E 1,311,097
SUBTOTAL POI-1					POI-1									5,382	7,892			
TOTAL 7 ESD practices						165,898	38,208			5,382	7,892				461	6,263		

P E from MDE Stormwater Design Manual (2000, Supp. 1 2009), Ch. 5, Table 5.3 — rainfall targets for ESD; HSG C governing. $R_v = 0.05 + 0.009I$; $ESD_v = P E - R_v A/12$; $Rev = S - R_v A/12$ ($S = 0.13$ in, HSG C), met within ESDv. M-8 provided = 6 cf per ft (4-ft bottom, 6" ponding, 2.5' media at n 0.40)

SITE DATA

ITEM	DATA
Project	Estates at Indian Head, Lots 1-6 and Estates Court
Location	S. side of MD 210, ±3,000 ft E of MD 210 / MD 373; 200-205 Estates Ct., Accokeek 20607
Record	Plan Book PM 228 Plat 83 (final plat 5-08283); Tax Map 151 F-3; WSSC 2007 22050E1
Accounts	3987666, 3987674, 3987682, 3987690, 3987708, 3987716
Owner	General Waldman Revocable Trust, L 32063 F 0-043
Zone / use	RR (no change) – a single-family detached dwellings
Tract	165,019 sq. ft of record (3.788 ac) = plat 171,505 sq less Outlot A (6,486 sf, conveyed L 15165 F 4-55)
Public dedication	WSSC 600' RW, 35,173 sq ft of record – rural open space, 24' pavement, cul-de-sac
Water / sewer	W-15 (UNSC) – mains from Henrietta Dr via 30' WSSC ecm; L 15169 F 399 and prop. Lot 4 ecm
Watershed	Piscataway Creek, MD 021402030798; not tier; not CBCA; FEMA Zone X
Master plan	2013 Subregion 5 Master Plan & SMA; Planning Area 84; Council District 9; Election Dist. 5
Map	NAD 83 MD State Plane (US IR); NAVD 88 (N-NCPP- 2.4); 2009 spot grades on WSSC data

APPROVALS OF RECORD

CASE	STATUS
NRI-015-06	Prior approval – base work; updated NRI required
TCPI-018-06	Prior approval – base work
TCPI-016-09	Prior approval – base work; revision or new TCP per M-NCPPC
5-08238	Final plat, PM 228 @ 93 – recorded
DW5&T 9399-2009-08	Street tree & lighting plan (2009) – base layout; re-revision to current standards
L51799 F.399	30' WSSC easement (Outlot A, Lot 20) – recorded 2025

GENERAL NOTES


1. Boundary per recorded plat PM 228 @ 83; lot lines reproduce the plat to the second.
2. Horizontal datum: Maryland State Plane NAD 83 (US ft). Vertical datum: NAVD 88 (MNCPPC 2' contours). 2009 spot grades are on WSSC datum = 1.6'.
3. The base layout is the 2009 Street Tree & Lighting Plan (DPWGT 9399-2009-00), resubmitted for review under current requirements; dwellings, side-lawn garages and courts, street trees and street lights. Lot 4 is front-lawn (garage to the cul-de-sac) to clear the WSSC easement.
4. The 4' x 4' topographic sheet DPWGT Std. 500.10 / 600.02 / 600.04; 24' pavement, shoulders, roadside swales; driveways cross the swale on 15' RCP culverts with flared ends.
5. Entrance to MD 210 (SHA) with 50' returns as the main plan; SHA access permit and sight-distance analysis required. MD 210 auxiliary lanes shown for SHA review. R/W dedication may be required.
6. Record discrepancies between the current plan and the recorded 30' WSSC easement (L15799 399) and a 30' WSSC easement to be granted across Lot 4. Record discrepancies in the easement description to be resolved with WSSC.
7. NEW SUBMITTAL (2026). Prior approvals NRI-015-06, TCP1-018-06, TCP2-016-09 and DPWGT 9399-2009-00 are used as base work only and do not carry over. The current plan is approved only for the proposed changes to the easement approved after the concept approval. Sec 1-182(a) and (b) and TCP2-016-09 revision or new plan / letter of exemption as MNCPPC Environmental Planning determinations; street tree and lighting plan re-reviewed to current DPWGT/TDPE standards as required by ESD to the MD current Subtitle 32.
8. Address: 2009 Chesapeake, PM # or Chesapeake Bay Blvd. The lot area on the property (prior NRI-015-06; updated NRI wetlands).
9. Contact Miss MUI (811) at least 48 hours before any excavation.

DPIE CONCEPT PLAN DESIGN REVIEW CHECKLIST (08/25/2021) — C = SHOWN · X = N/A · O = OUTSTANDING

ITEM	PLAN REQUIREMENT	REF.	C/O	RESPONSE / WHERE SHOWN	SHEET
A-1	Plan is labeled as Site Development Concept Plan (aka Concept Plan from MDE Step 1).			Every sheet is titled SITE DEVELOPMENT CONCEPT PLAN.	ALL
A-2	Plan sheet size does not exceed 30" x 42" and all sheets are printed on same size paper.	5.3.2	C	All sheets 24" x 36" (ARCH D).	ALL
A-3	A 5-inch, full-height open area is provided on the right-hand side of the drawing for County approval logs.	2.2.1.0	C	5-inch full-height strip at the right edge, kept clear for County approval logs.	ALL
A-4	If more than 4 plan sheets: composite plan showing match lines and sheet numbers (scale not to exceed 1"=200'); key map on each plan sheet.	2.2.1.0	C	7-sheets: the whole site is on each plan sheet at one scale, so no match lines; key map in every title block.	ALL
A-5	Match lines have a minimum length of 4 inches and identify the matching sheet number.	2.2.1.M	X	No match lines – the entire site fits one viewport.	
A-6	Vicinity map at a minimum scale of 1"=2,000' with north arrow and scale, upper right hand corner of cover sheet.	2.2.1.B	C	Vicinity map at 1" = 2,000' with north arrow and bar scale, upper right corner.	C-000
A-7	A bar scale is provided on every sheet.	2.2.1.E	C	Graphic bar scale in every plan viewport.	C-000
A-8	Three grid ticks are provided as described in the manual.	2.2.1.R	C	Three State Plane grid ticks with N/E values on each plan.	ALL
A-9	Horizontal (MD Coordinate System, NAD 83) and vertical (NGVD 29 preferred) station is stated on the plan.		C	Horizontal Maryland State Plane, NAD 83 (EPSG 2248), US ft; vertical NAVD 88 (MWPCP 2-ft); 2009 spot heights WSSC datum as noted.	ALL
A-10	General notes about the project are provided.		C	General notes on the cover sheet.	C-000
A-11	The entire property shown at a maximum plan scale of 1 inch = 50 feet (preferred) within the plan sheet.	5.3.2	C	Entire property at 1" = 30'.	C-000
A-12	All existing structures and site features including cultural features, historic sites and easements, and any visible foundations or runs are shown.	5.3.2	C	Existing structures, adjoining houses, fences, sheds, well, easements of record shown; no historic sites or runs.	C-100
A-13	Topographic contours at maximum 2 foot interval, extending at least 100 feet beyond the property.	3.2-182	C	M-NCPPC 2-ft contours, 100 feet beyond the property.	C-100
A-14	All existing utilities and utility easements are shown.		C	WSSC easement L 51799 F 399 and the proposed Lot 4 WSSC easement; public utility easements along the frontage; existing main in Henrietta Dr noted (sizes to verify on WSSC 220501).	C-300
A-15	The County BMP Summary Table is provided. Preferred location is on the cover sheet.	5.3.1	C	County BMP Summary Table, 7 practices.	C-000
B-1	Bank(s) of all regulated streams or a centerline if the banks are too close together to graphically show.	MDE 5.7	X	No streams on map. New submittal: prior NRI-0156 (with TCP1-018-06, TCP2-016-09) is base work only. Updated/revised NRI to be provided in draft with this submission; approved copy required before concept approval (See TCP-182(a)).	
B-2	Location of stream and stream buffers and/or enhanced buffers per MNCPPC and SCD criteria.	MDE 5.7	X	No streams, no stream buffers.	
B-3	Location of wetlands and/or wetlands of special state concern and appropriate wetland buffers.	MDE 5.7	X	No wetlands on or within 100 ft (DNR, NRI).	
B-4	Delineation of the 100-year floodplain, per Tech-Grm 004-2020.	MDE 5.7	X	FEMA Zone X, to 100-year floodplain (on within 100 ft.	
B-5	Location of steep slopes (15% and greater) clearly shown on the plan and in the legend.	M-NCPPC	C	Slopes 15-25%: 2,757 sf; >25%: 520 sf – shown and in the legend.	C-100
B-6	The Primary Management Area is delineated.	MDE 5.7	X	No PMA on the property.	
B-7	Existing woodland is delineated on the property.	MDE 5.7	X	No woodland conservation shown on this concept. Prior NRI-0156 (b) TCP2-016-09 are base work only; woodland per the updated NRI, with a TCP2 revision or new TCP2 / letter of exemption as M-NCPPC determines.	C-100
B-8	Existing environmental features extend off the property 100 feet in all directions.	MNCPPC	C	Environmental layers drawn 100 ft beyond the property.	C-100
B-9	Soils types and soil boundaries from USDA NRCS Soil Survey (Dec. 2009 or latest).		C	Soil types and boundaries from USDA NRCS (PGAtlas Soil layer): CwS (HSG C), UdaS (HSG -), BaB (HSG C), BaB (HSG C).	C-100
B-10	Plan notes identify TMDL watershed (sediment, nitrogen, phosphorus) and Tier I waters/waterways.		C	C Chesapeake Bay TMDL (nitrogen, phosphorus, sediment) applies; MD 12.12 watershed 02140203079, Piscataway Creek (021402039). Tier I: no.	C-000
B-11	Highly erodible soils (K 0.37) is highly erodible where slopes are 15% or more; those areas are stabilized within 3 days.	MDE 5.7	C	Beltsville soil (ZM 0.37) is highly erodible where slopes are 15% or more; those areas are stabilized within 3 days.	C-000
B-12	Springs and seeps noted.	MDE 5.7	X	None observed or mapped.	
B-13	Bedrock and Marlboro Clay outcrops noted.	MDE 5.7	X	No bedrock or Marlboro clay mapped (PGAtlas); geotechnical report to confirm (E-2).	
B-14	Chesapeake Bay Critical Areas delineated.	MDE 5.7	X	Not in the Chesapeake Bay Critical Area.	


CHECKLIST (CONT.)

C#	REQUIREMENT	REF.	C/X/O	RESPONSE / WHERE SHOWN	SHEET
C-1	Project layout is shown, including roads, buildings, parking, sidewalks and other improvements and associated grading.	C-2-182	C	Estates Court, 6 dwellings, driveways and courts, entrance at MD 210, grading.	C-200
C-2	Preliminary locations of ESD and structural stormwater practices; grading for drains where slopes exceed 15%.	C-2-182	C	7 ESD practices (micro-bioretenion M-6 per lot; roadside dry swales M-8).	C-240
C-3	Preliminary locations of storm drain inlets and culverts; entrance and outfall structures located beyond project limits (assessments may be required after final design).	5.2.4.2.B / 32-162.A.6	C	Open section – no inlets; 6 driveway culverts (15' RCP) with end structures; swales outlet at the entrance to the MD 210 roadside ditch (SHA).	C-400
C-4	Limit of Disturbance shown for all site work, incl. water, sewer, storm drain, SWM, road improvements, sediment control, stockpile.	C-2-182	C	LOD 22,317 sf incl. mains, easement work off site, sediment control and stockpile.	C-500
C-5	Existing easements shown and any required off-site proposed easements.	C-2-182	C	Recorded WSSC easement (Outlet A, Lot 20) and proposed Lot 1 WSSC easement; private SWM easements over ESD practices.	C-300
C-6	Locations, names and widths of existing and ultimate rights-of-way of adjacent streets and alleys; public vs. private noted.	C-2-182	C	MD 210 (variable RW, SHA, Estates Ct (660' public), Henrietta Dr and Jennifer Dr (50' public), 30' RW in common L 1014 E F 725 (private).	C-200
C-7	Existing and proposed water well and septic field locations are shown.	C-2-182	C	No wells or septic proposed (public water and sewer). Existing well on Parcel 19 (15600 Indian Head Hwy), off site, shown.	C-100
C-8	Proposed public dedication area including any proposed parkland is shown and labeled.	C-2-182	C	Estates Court public dedication 36,041 sf (plat PM 228 @ E3), no parkland.	C-200
C-9	Points of investigation shown. ESDV computations and BMP Summary Table broken out to show ESD Required is Provided within each POI.	C-2-182	C	7 POIs; ESDV required vs. provided tabulated per POI.	C-400
C-10	The ultimate 100-year stormwater overflow path is shown throughout the site using flow arrows.	C-2-182	C	100-yr overflow arrows from every practice to its POI (13).	C-400
C-11	Drainage areas to each device, offsite drainage onto the site, and to site outfalls; diverted areas analysed for no increase in 100-yr discharge.	C-2-182	C	Drainage area to each practice; off-site area onto the site is 0.4 ac; no diversion between POIs.	C-400
C-12	Where grading blocks a drainage course, reporting limits before and after grading are shown.	C-2-182	X	No fill across a drainage course.	C-200
D-1	Respond addresses natural resource protection, natural flow patterns, impervious reduction, ESC integration, ESD planning to the MEP.	MODE 5.11	O	SWM concept narrative (ESD to the MEP, flow patterns, ESC integration) – to accompany the plans.	C-500
D-2	If in the Chesapeake Bay Critical Area, discussion of how requirements are met; preliminary flow calculations.	MODE 5.11	X	Not in the Chesapeake Bay Critical Area.	C-500
D-3	Outfalls located outside the site, to existing storm drain or 100-yr floodplain; otherwise the discharge area is described.	MODE 5.11	O	Narrative: outfalls at the POIs; swales discharge to the MD 210 roadside ditch; describe receiving areas.	C-400
D-4	Stabilization at downstream outfall and upstream inflow evaluated; measures against gully formation discussed.	MODE 5.11	O	Narrative: outfall stabilization (level spreaders / riprap) at each POI.	C-400
D-5	Photographs of the stream at the downstream outfall and upstream property line; eroded slopes.	MODE 5.11	X	No stream at the outfalls.	C-400
D-6	If outfall is to an existing SWM facility, its capacity for the added area and flow is documented.	MODE 5.11	X	No existing SWM facility receives the site.	C-400
D-7	If rezoned to higher imperviousness, effects on downstream properties analysed.	MODE 5.11	X	No rezoning (RR remains RR).	C-400
D-8	Floodplain ordinance discussion (drainage courses, buildings within 25 ft of floodplain, dams, downstream crossings).	MODE 5.11	X	No floodplain or drainage course on or downstream within the site; no dams.	C-400
D-9	If a waiver of water quality or quantity is requested, the basis is provided.	MODE 5.11	X	No waiver requested.	C-400
D-10	Computations: ESD/WQBW required and proposed; runoff; ESD/WQBW required and proposed; runoff; downstream storm drain analysis with 10-yr credit if no dam project.	5.3.3 / 5.2.6.1 / 5.2.4.2 / TG 002-2013	O	ESDV computations are on the cover. 100 yr existing proposed runoff at each POI and downstream analysis to follow in the report.	C-400
E-1	A Geotechnical Report for SWM is provided to support concept development and feasibility.	5.3.3 / TG 004-2018	O	Geotechnical report for SWM (borings and Sec. 32-131 infiltration tests at each practice) – to be submitted.	C-500
E-2	Geotechnical Report addresses Marlboro and Christina clays, sulfidic and diatomaceous soils.	5.3.3 / TG 005-2018 / PGSCD I-8	O	Geotechnical report to address Marlboro/Christiana clays, sulfidic and diatomaceous soils.	C-500
E-3	Affidavit of Public Information mailing is provided with second submission.	C-2-182(g)	O	Affidavit of the adjacent-owner mailing (within 7 days of submission) – with second submission.	C-500
E-4	A draft Natural Resource Inventory is provided with initial submission (approved copy required prior to approval).	C-2-182(a)	O	New submission: prior NRI-015-06 with TCPI 018-06, (TCP-016-09) is base work only. Updated/revised NRI to be provided in draft with this submission; approved copy required before concept approval. (Sec. 32-135(a)).	C-500

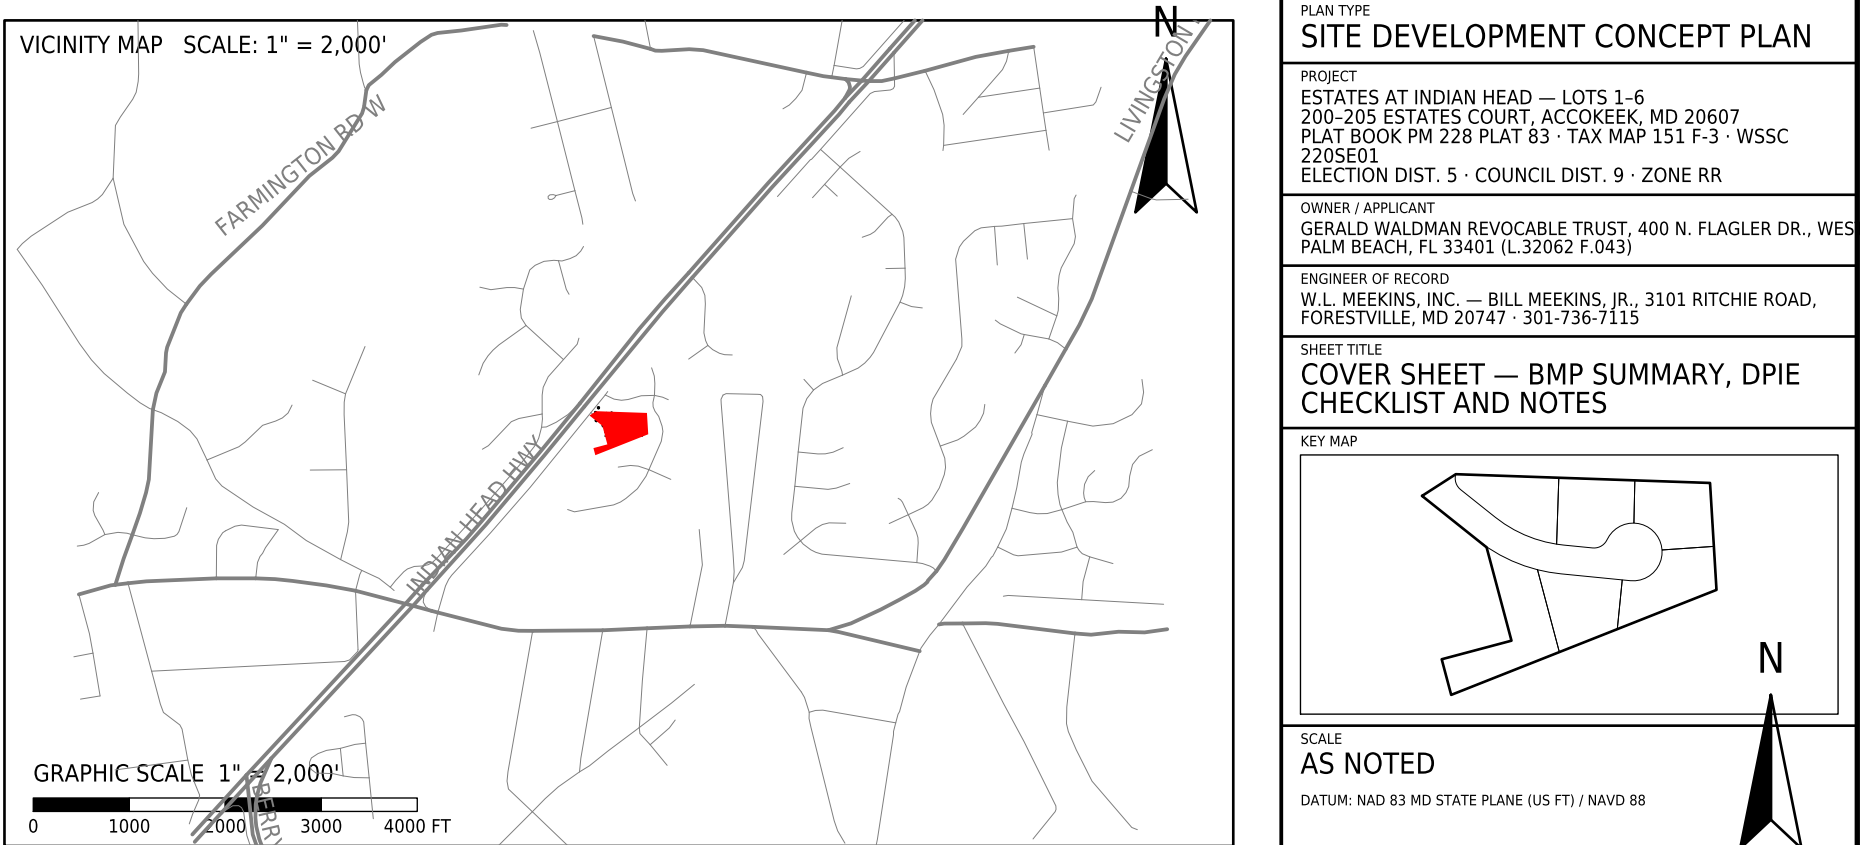

REVISIONS		
NO.	DATE	DESCRIPTION
0	2026-09-30	CONCEPT SUBMISSION 1


PROFESSIONAL CERTIFICATION
I hereby certify that these documents were prepared or approved by me
and that I am a duly licensed professional engineer under the laws of
the State of Maryland. License No. _____ Exp. _____

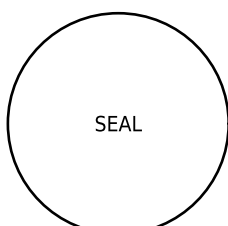



CONCEPT SUBMISSION 1 — NOT SEALED
DATE 2026-09-30 · JOB KEA-EIH-2026
PREPARED WITH KEALIFE SPATIAL ENGINE / CAD-PLOT

SHEET INDEX

► C-000 COVER SHEET — BMP SUMMARY, DPIE CHECKLIST AND NOTES
C-100 EXISTING CONDITIONS AND ENVIRONMENTAL FEATURES
C-200 SITE LAYOUT, GRADING AND DRAINAGE PLAN
C-300 UTILITY, STREET LIGHT AND STREET TREE PLAN
C-400 STORMWATER MANAGEMENT CONCEPT AND DRAINAGE AREA MAP
C-500 SEDIMENT AND EROSION CONTROL PLAN
C-600 DETAILS

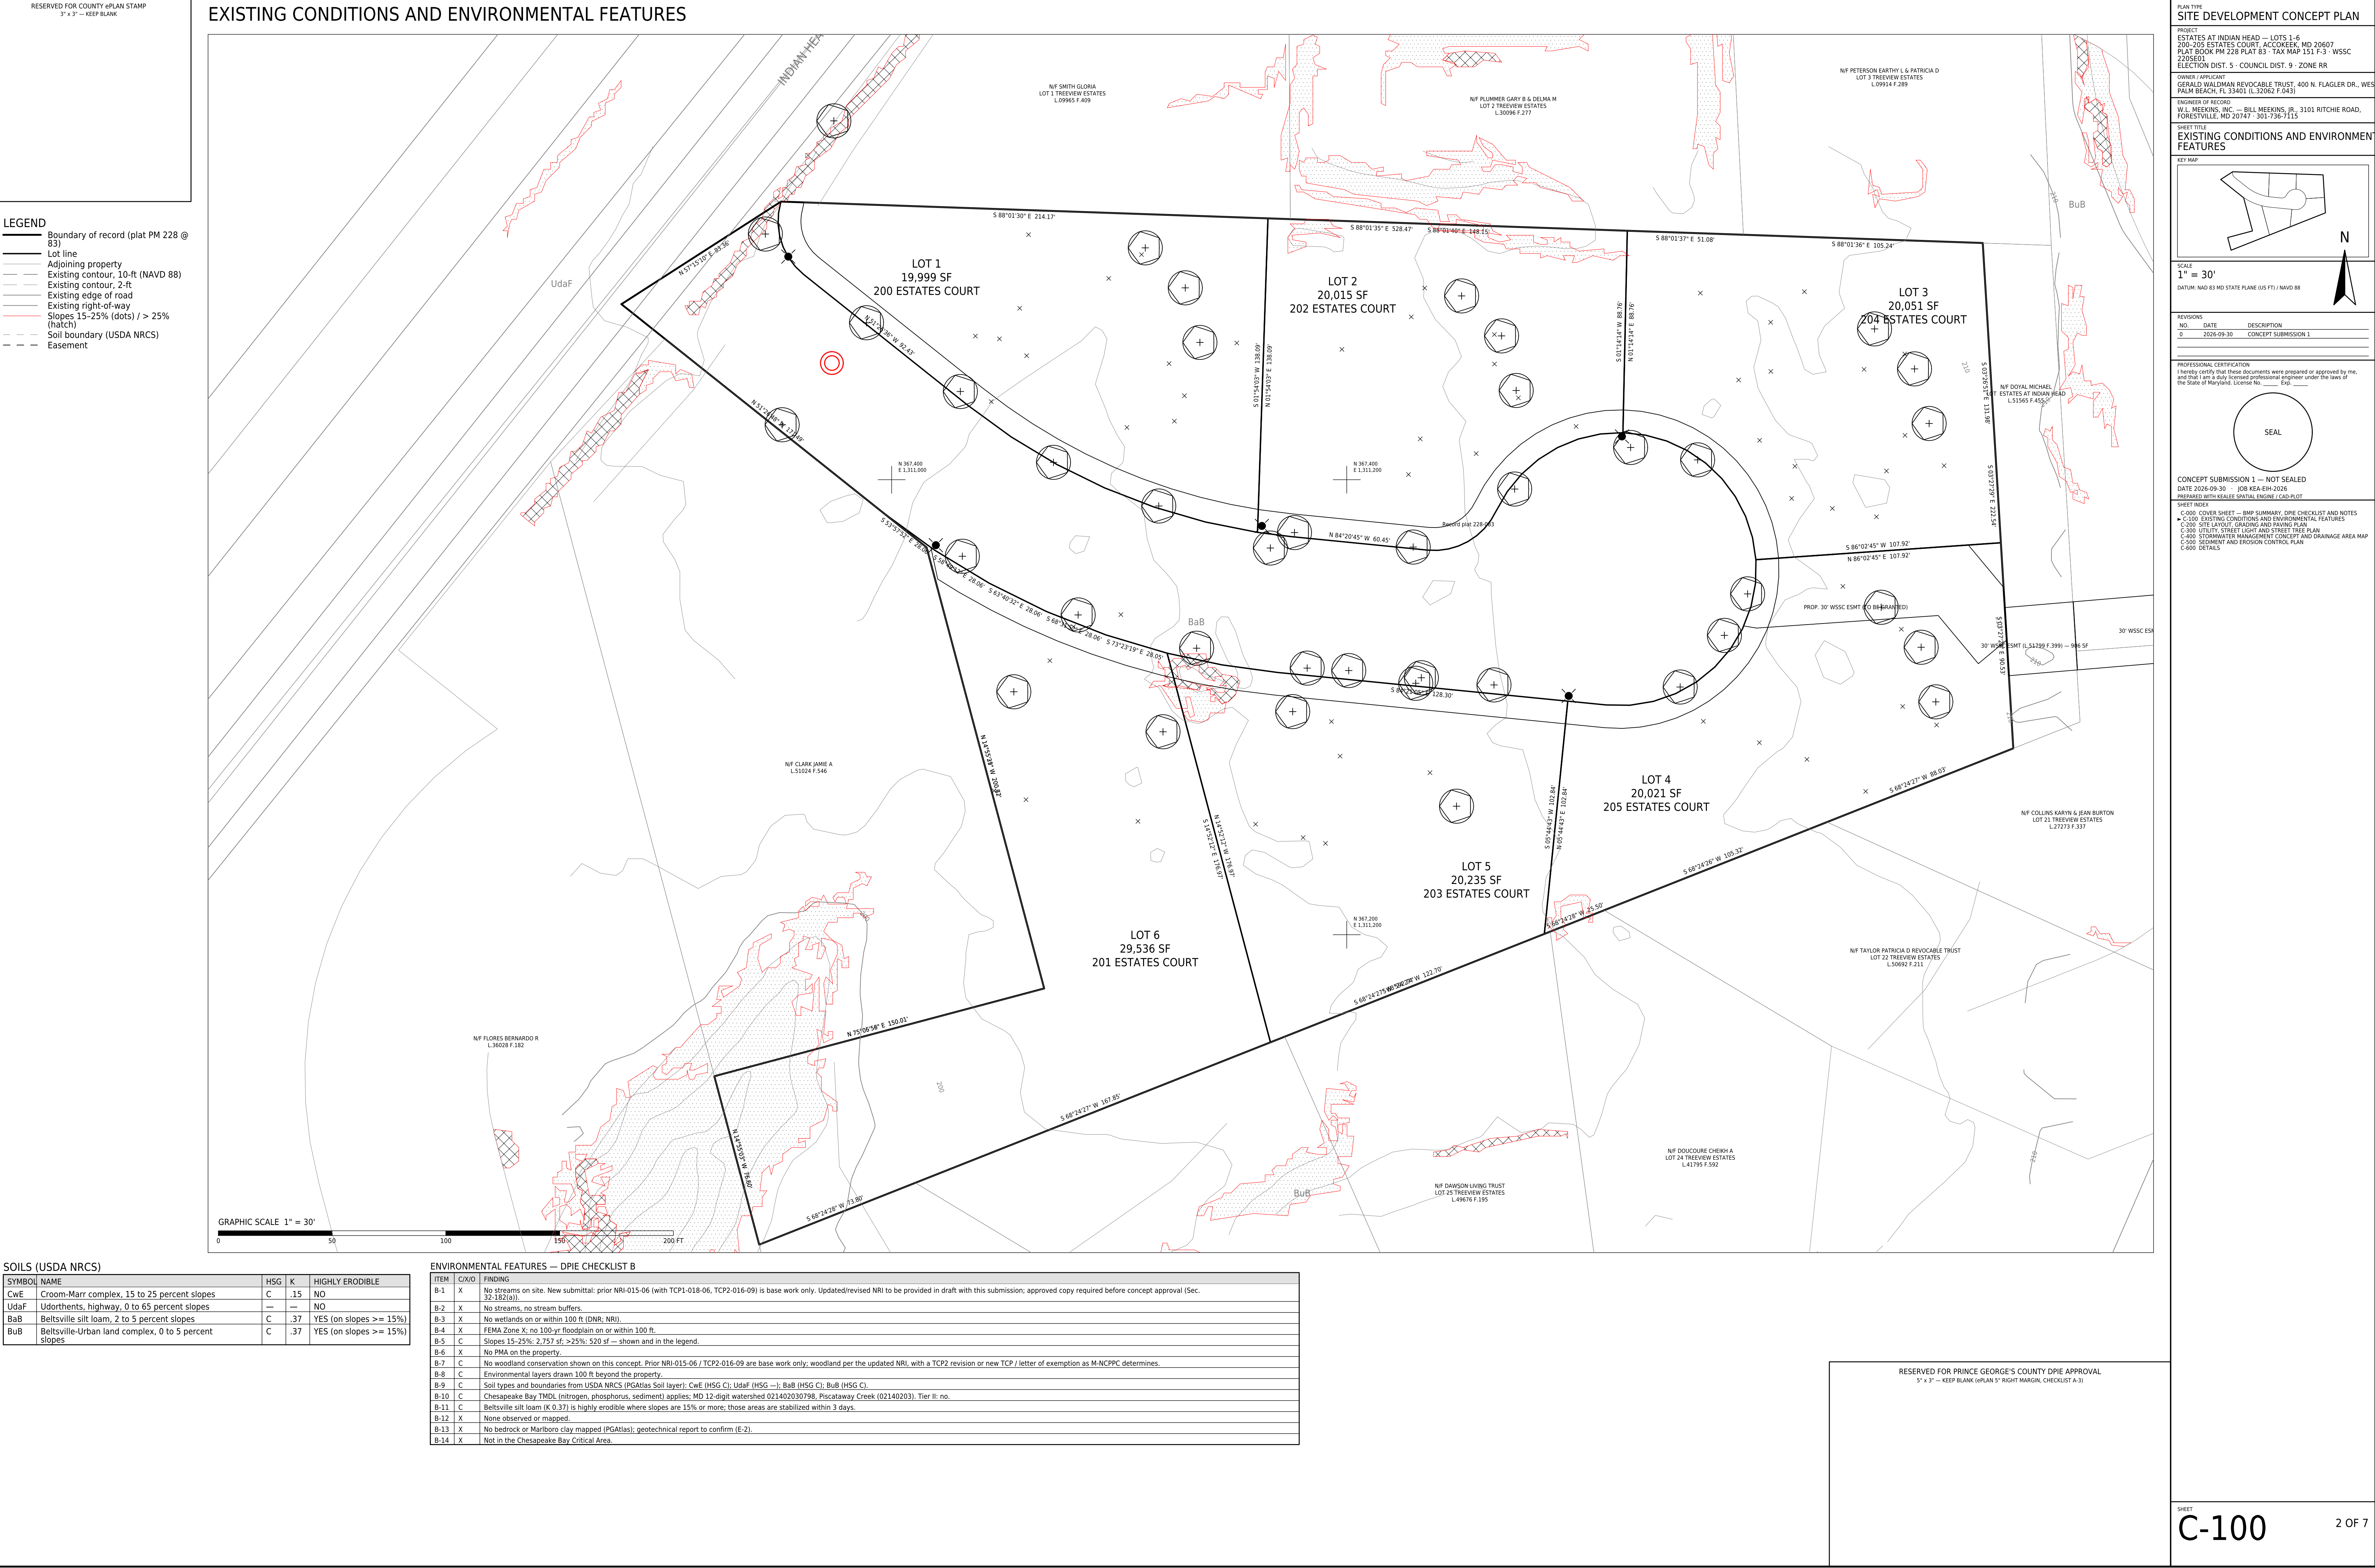

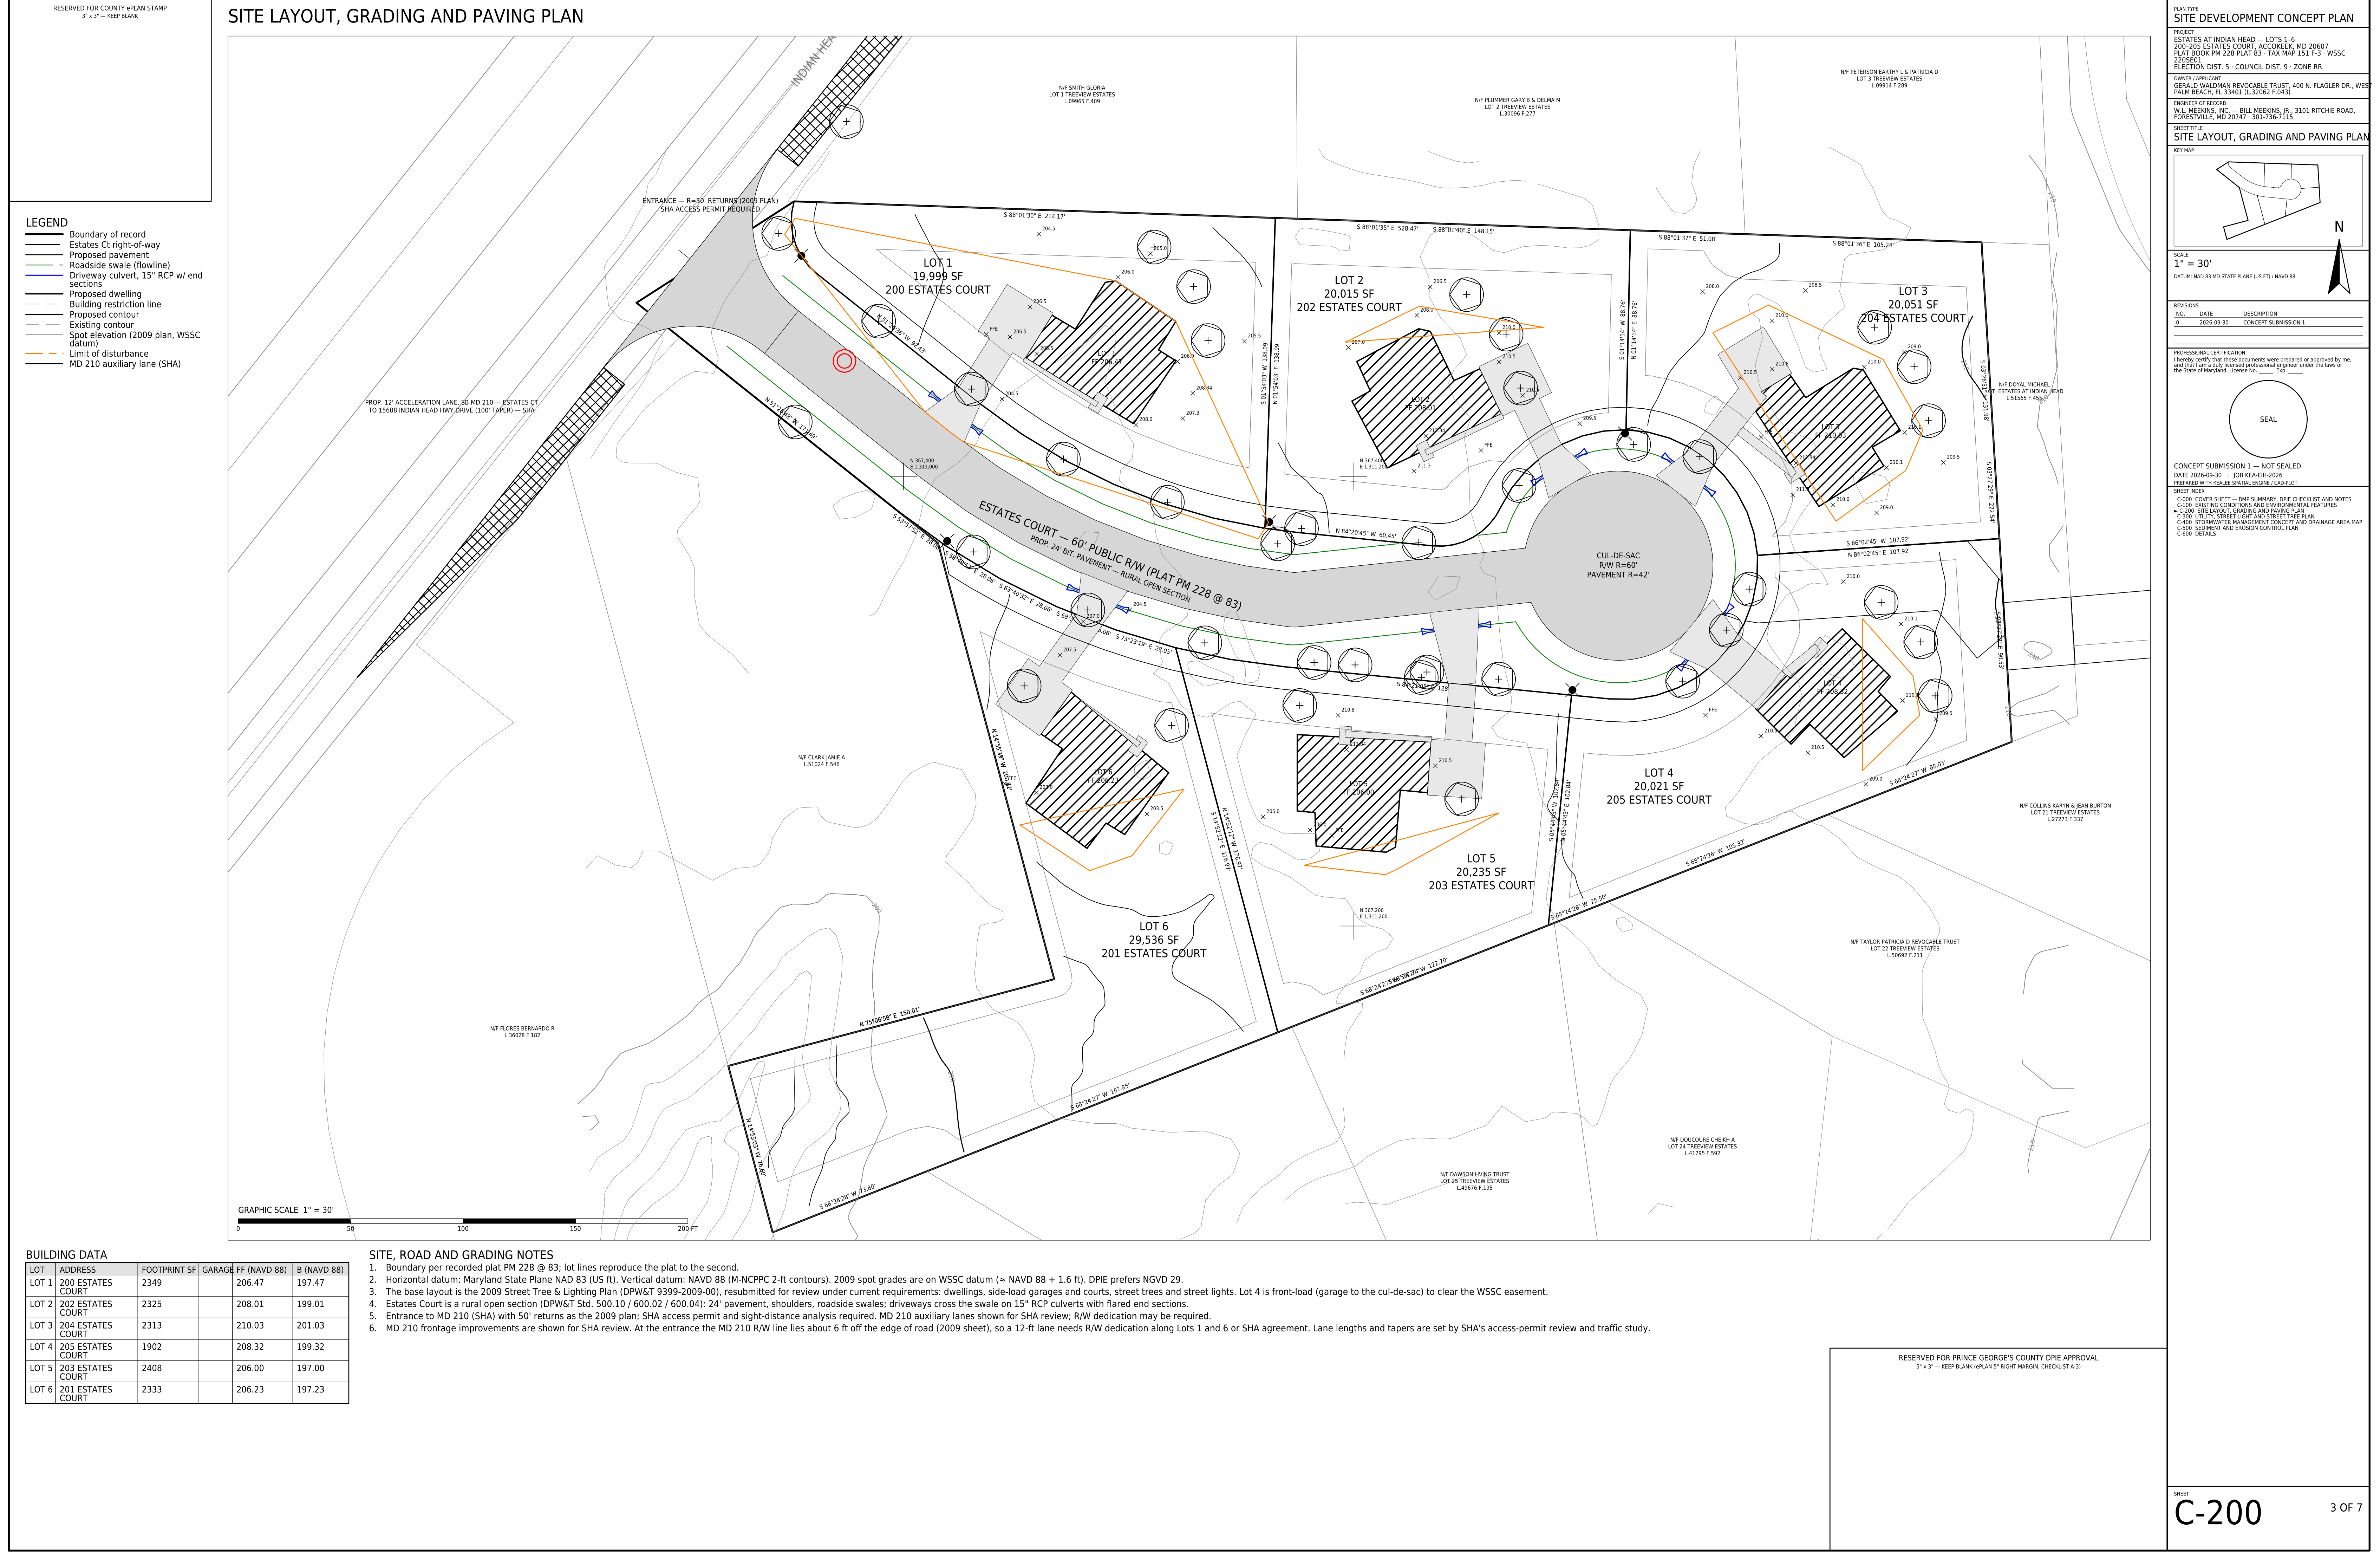

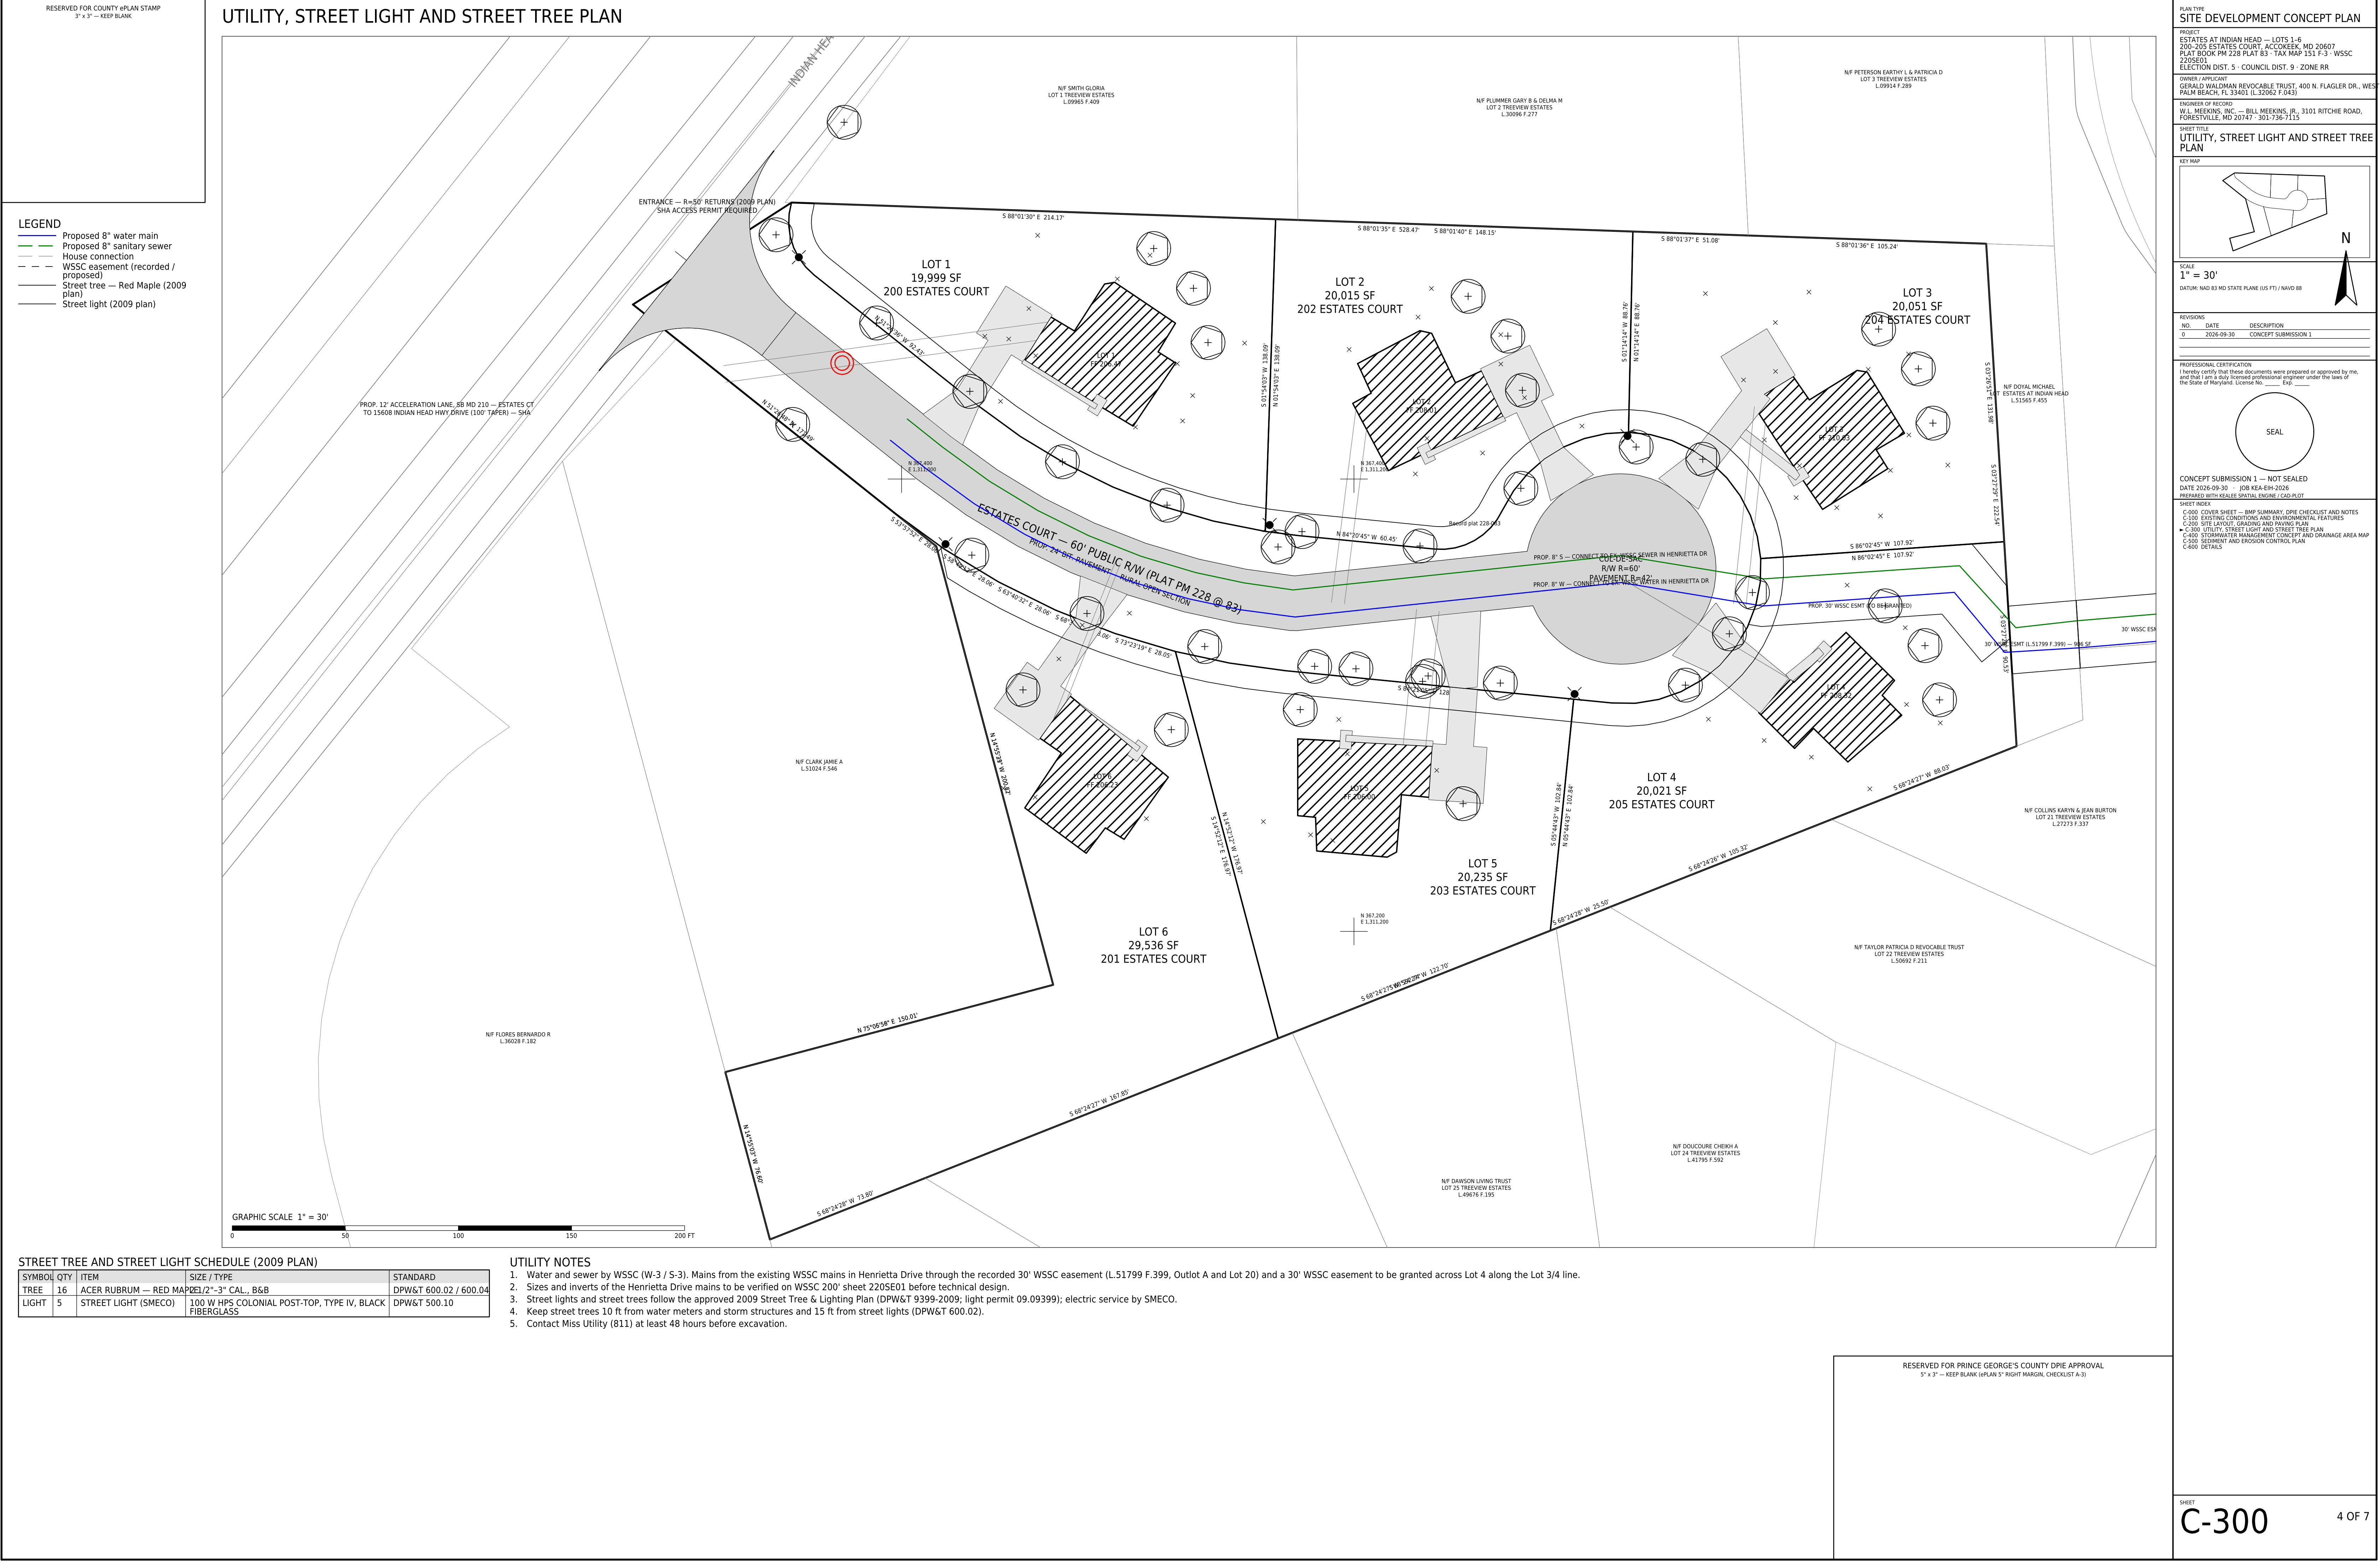


RESERVED FOR COUNTY ePLAN STAMP
3" x 3" — KEEP BLANK

STORMWATER MANAGEMENT CONCEPT AND DRAINAGE AREA MAP

LEGEND

- ESD practice — micro-bioretenction (M-6)
- Roadside dry swale (M-8)
- Drainage area to practice
- Off-site area draining onto site
- 100-yr overflow path
- Point of investigation
- Driveway culvert

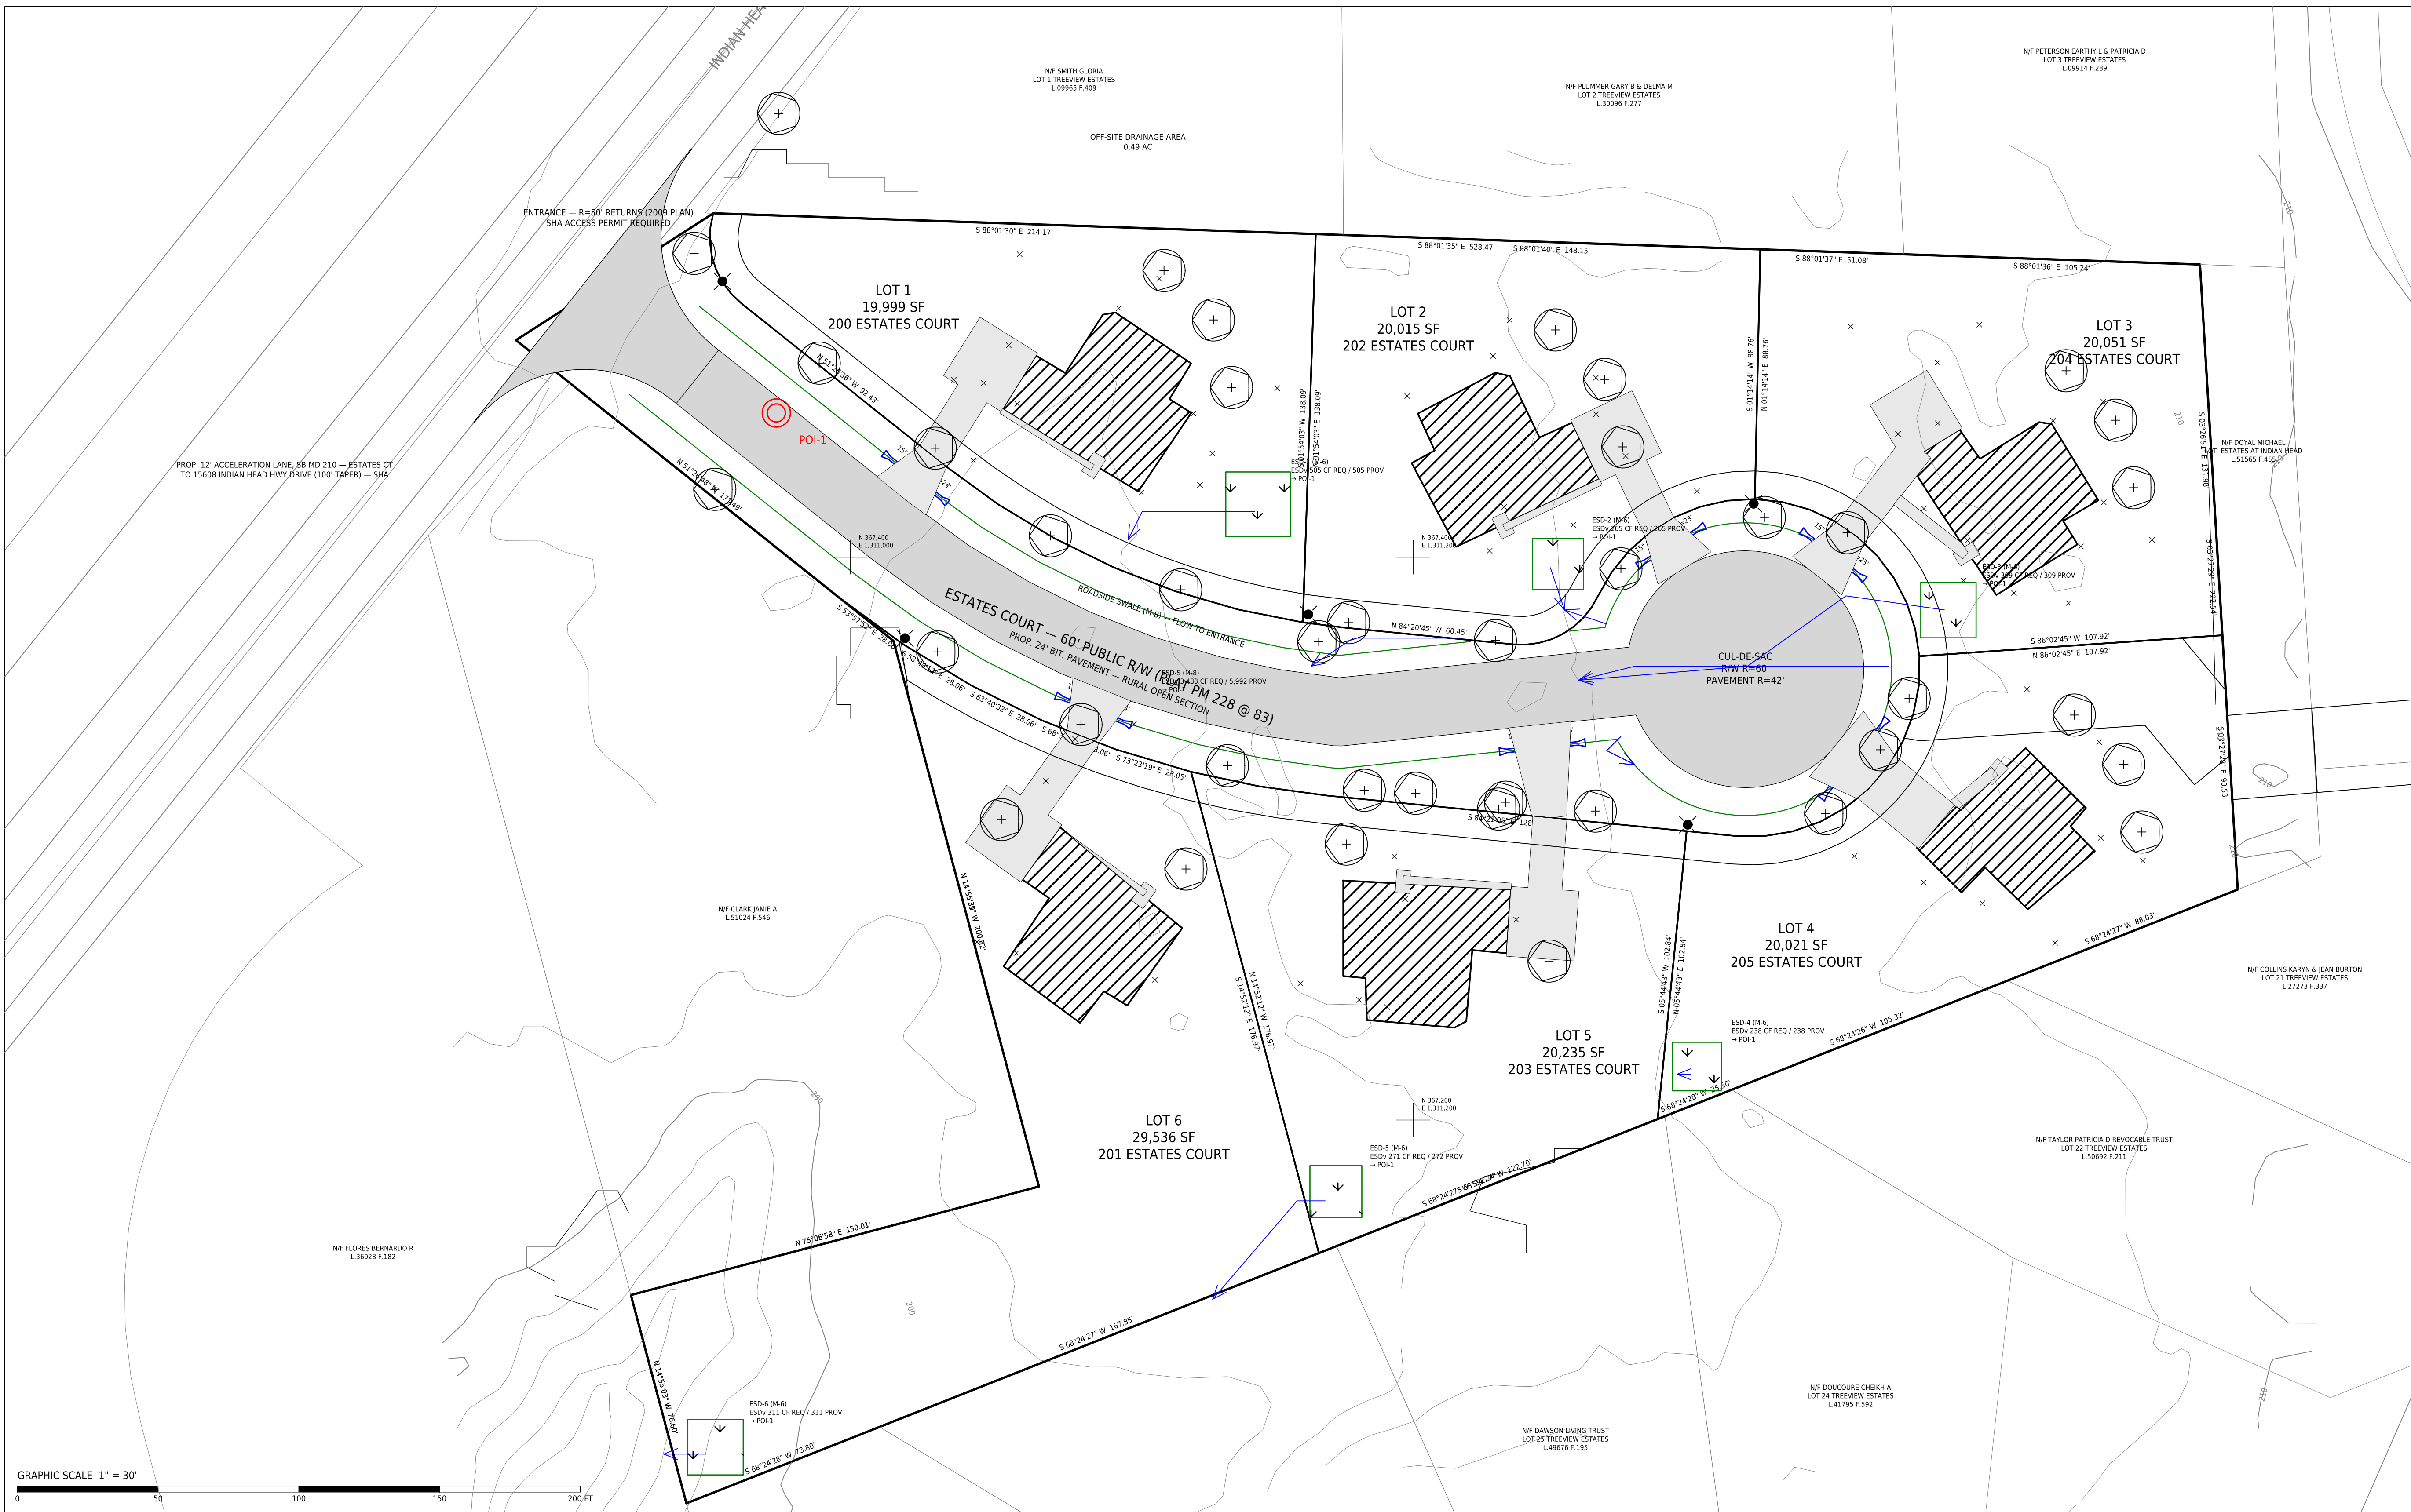

ESD PER PRACTICE (FULL TABLE ON C-000)

BMP	MDE	LOCATION	POI	DA SF	%I	P_E	ESDv REQ	ESDv PROV
ESD-1	M-6	Lot 1	POI-1	19,999	22.5	1.2	505	505
ESD-2	M-6	Lot 2	POI-1	20,015	12.1	1.0	265	265
ESD-3	M-6	Lot 3	POI-1	20,051	15.0	1.0	309	309
ESD-4	M-6	Lot 4	POI-1	20,021	10.3	1.0	238	238
ESD-5	M-6	Lot 5	POI-1	20,235	12.3	1.0	271	272
ESD-6	M-6	Lot 6	POI-1	29,536	8.5	1.0	311	311
ESD-5	M-8	Estates Ct R/W, both sides	POI-1	36,041	58.9	2.0	3,483	5,992

POINTS OF INVESTIGATION (C-9)

POI	LOCATION	SHARE	ESDv REQ	ESDv PROV
POI-1	N 367,451 E 1,310,974	100%	5,382	7,892

SWM NOTES

- SWM by Environmental Site Design to the MEP (Md. Stormwater Management Act of 2007; MDE Design Manual Ch. 5; PCG Subtitle 32). Target rainfall P_E from MDE Table 5.3 for HSG C at each drainage area's imperviousness.
- Each lot drains to one micro-bioretenction cell (M-6): 12-in max. ponding; 2.5-ft filter media; underdrain to a stable outfall. Estates Court drains to roadside dry swales (M-8) with check dams.
- Rooftop and non-rooftop disconnection (N-1, N-2) to be credited at technical design. Infiltration credit only where Sec. 32-131 borings show ≥ 0.52 in/hr.
- Private ESD practices: maintenance agreement recorded before permit; public swales in the R/W maintained by DPPE.
- D8 flow routing on a 5-ft surface interpolated from the existing 2-ft contours; exit points clustered at 120 ft; POIs carrying under 4% of the site omitted.

PLAN TYPE SITE DEVELOPMENT CONCEPT PLAN


PROJECT
ESTATES AT INDIAN HEAD — LOTS 1-6
200-205 ESTATES COURT, ACCOKEEK, MD 20607
PLAT BOOK PM 228 PLAT 83 — TAX MAP 151 F-3 — WSSC
220501
ELECTION DIST. 5 — COUNCIL DIST. 9 — ZONE RR

OWNER / APPLICANT
GERALD WALDMAN REVOCABLE TRUST, 400 N. FLAGLER DR., WEST
PALM BEACH, FL 33403 (L32062 F.043)

ENGINEER OF RECORD
W.L. MECKINS, INC. — BILL MECKINS, JR., 3101 RITCHIE ROAD,
FORESTVILLE, MD 20747 — 301-736-7115

SHEET TITLE STORMWATER MANAGEMENT CONCEPT AND DRAINAGE AREA MAP

KEY MAP

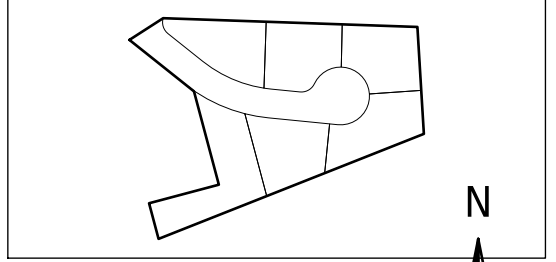

SCALE
1" = 30'

DATUM: NAD 83 MD STATE PLANE (US FT) / NAD83

REVISIONS		
NO.	DATE	DESCRIPTION
0	2026-09-30	CONCEPT SUBMISSION 1

PROFESSIONAL CERTIFICATION
I hereby certify that these documents were prepared or approved by me,
and that I am a duly licensed professional engineer under the laws of
the State of Maryland. License No. _____ E.O. _____



CONCEPT SUBMISSION 1 — NOT SEALED

DATE 2026-09-30 — JOB KEA-EH-2026

PREPARED WITH SCALE 3/32" = 1' (US FT) / 1:3840


SHEET INDEX
C-000 COVER SHEET — BMP SUMMARY, DPE CHECKLIST AND NOTES
C-100 EXISTING CONDITIONS AND ENVIRONMENTAL FEATURES
C-200 SITE LAYOUT, GRADING AND PAVING PLAN
C-300 UTILITY, STREET LIGHT AND STREET TREE PLAN
C-400 STORMWATER MANAGEMENT CONCEPT AND DRAINAGE AREA MAP
C-500 SEDIMENT AND EROSION CONTROL PLAN
C-600 DETAILS

RESERVED FOR PRINCE GEORGE'S COUNTY DPE APPROVAL
3" x 3" — KEEP BLANK (UPAN 5' RIGHT MARGIN, CHECKLIST A-3)




SHEET

C-400


5 OF 7

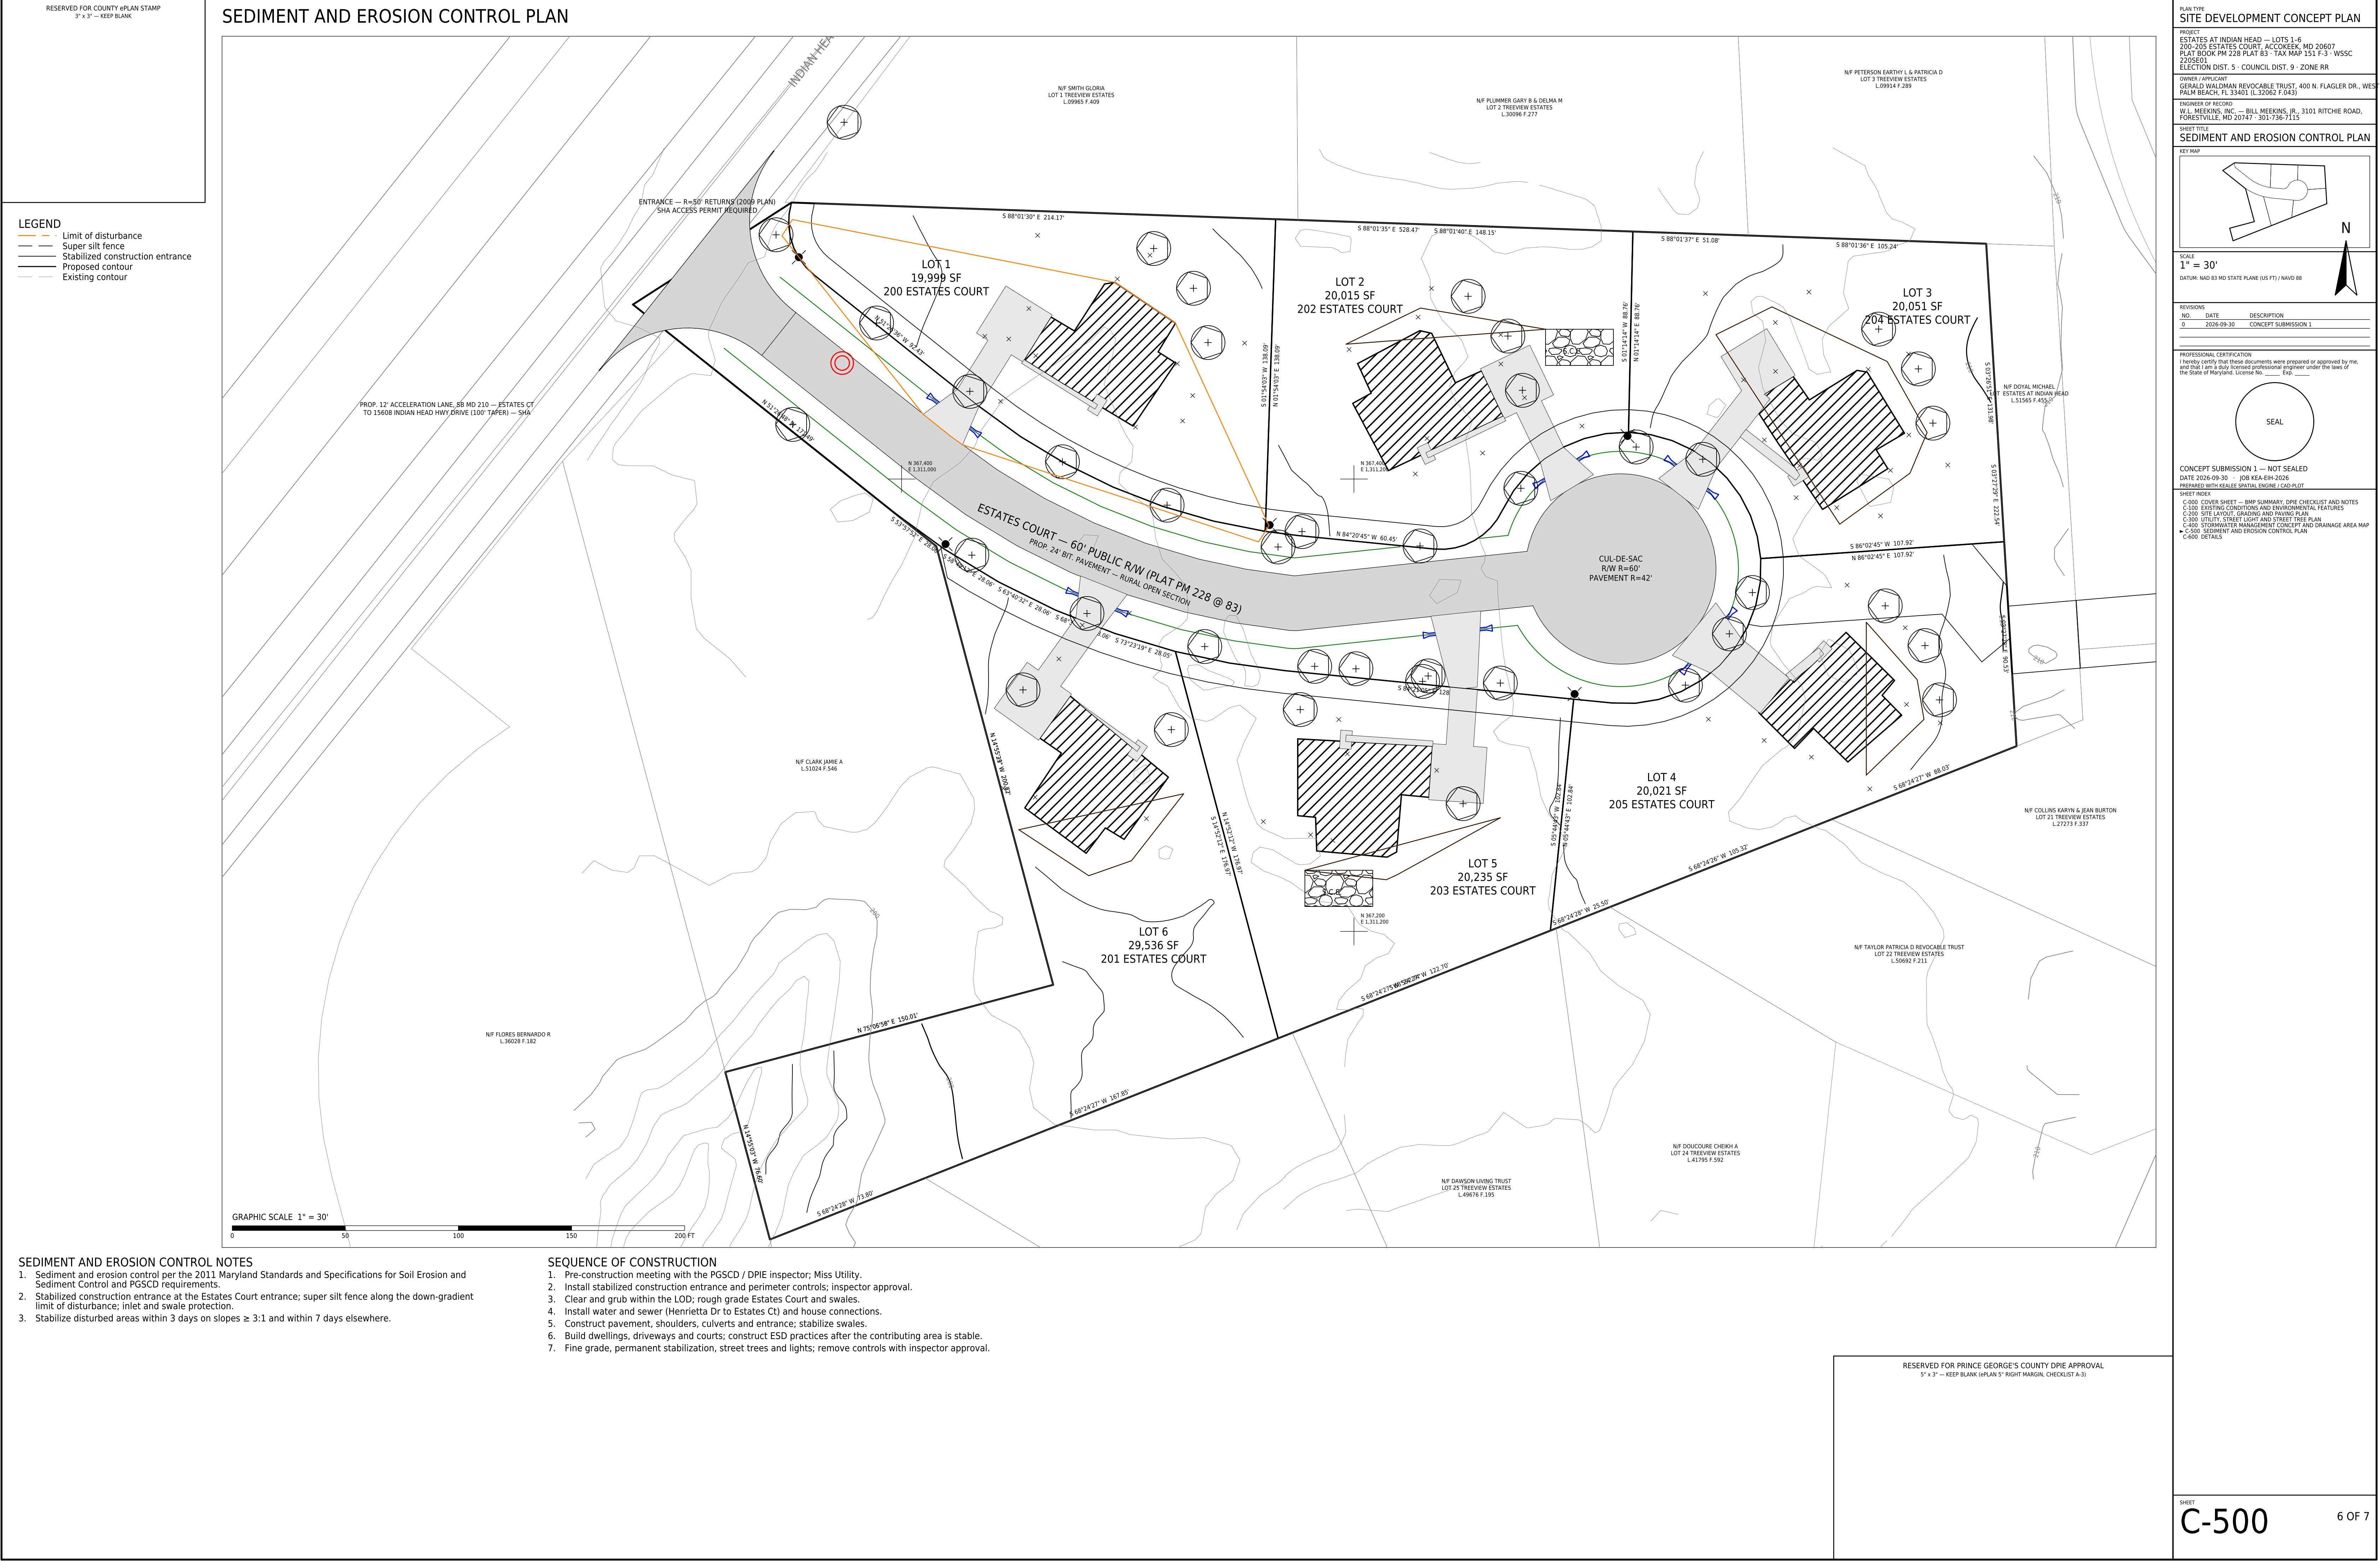

DETAILS

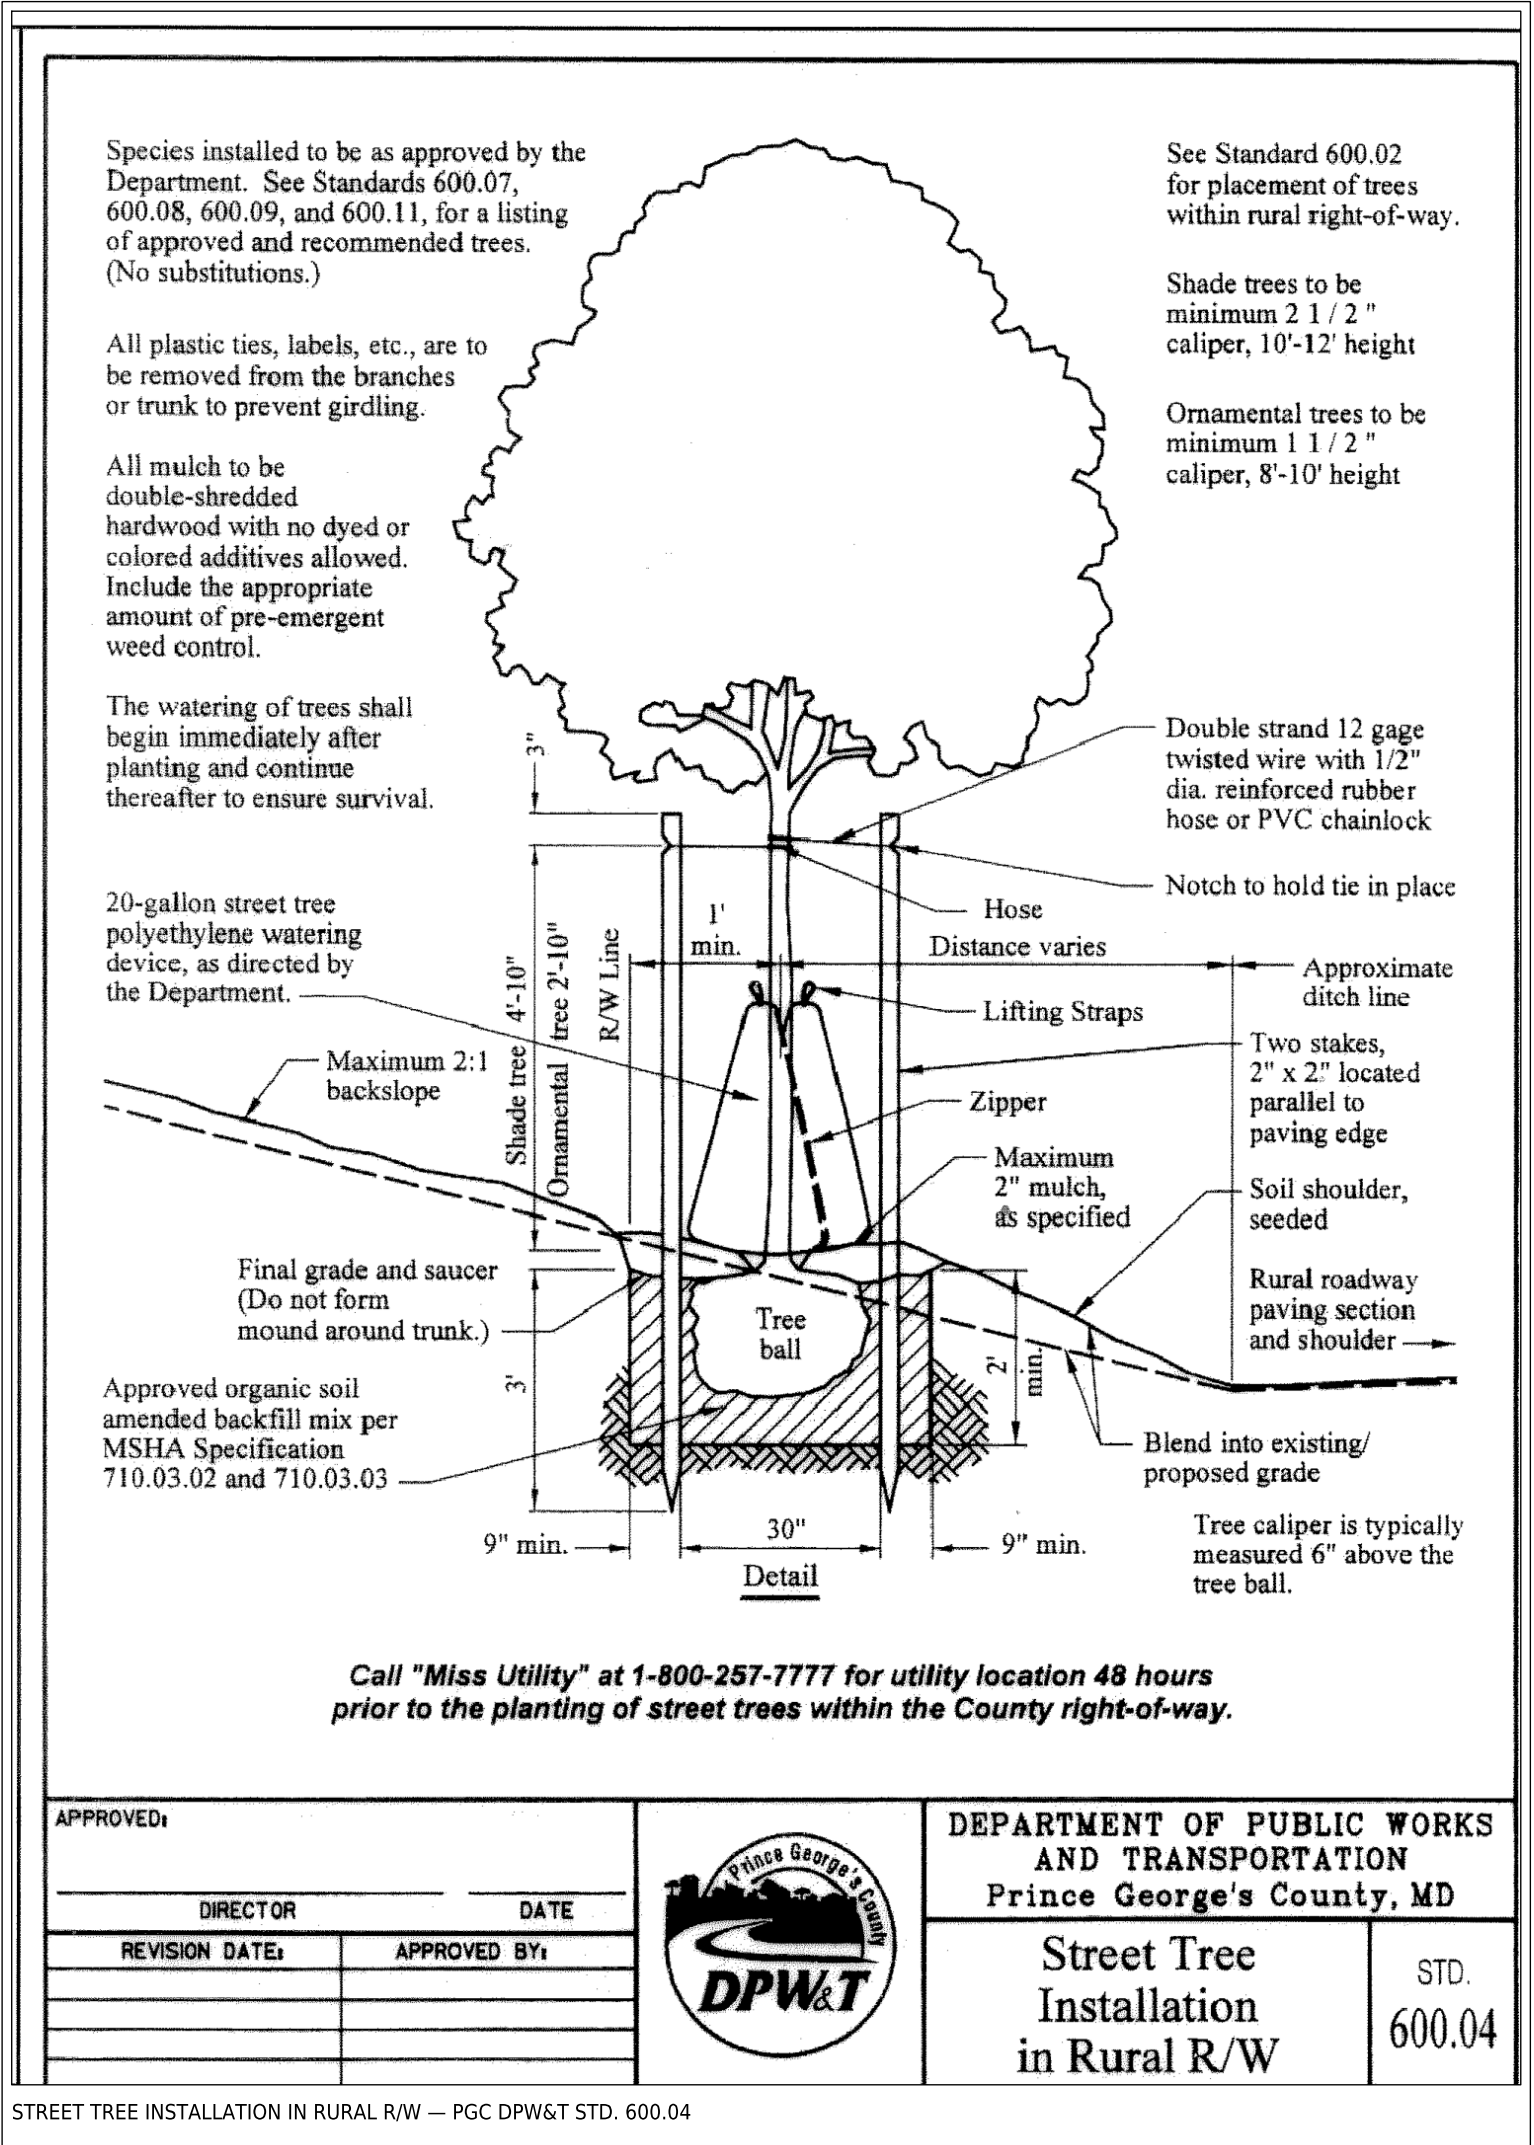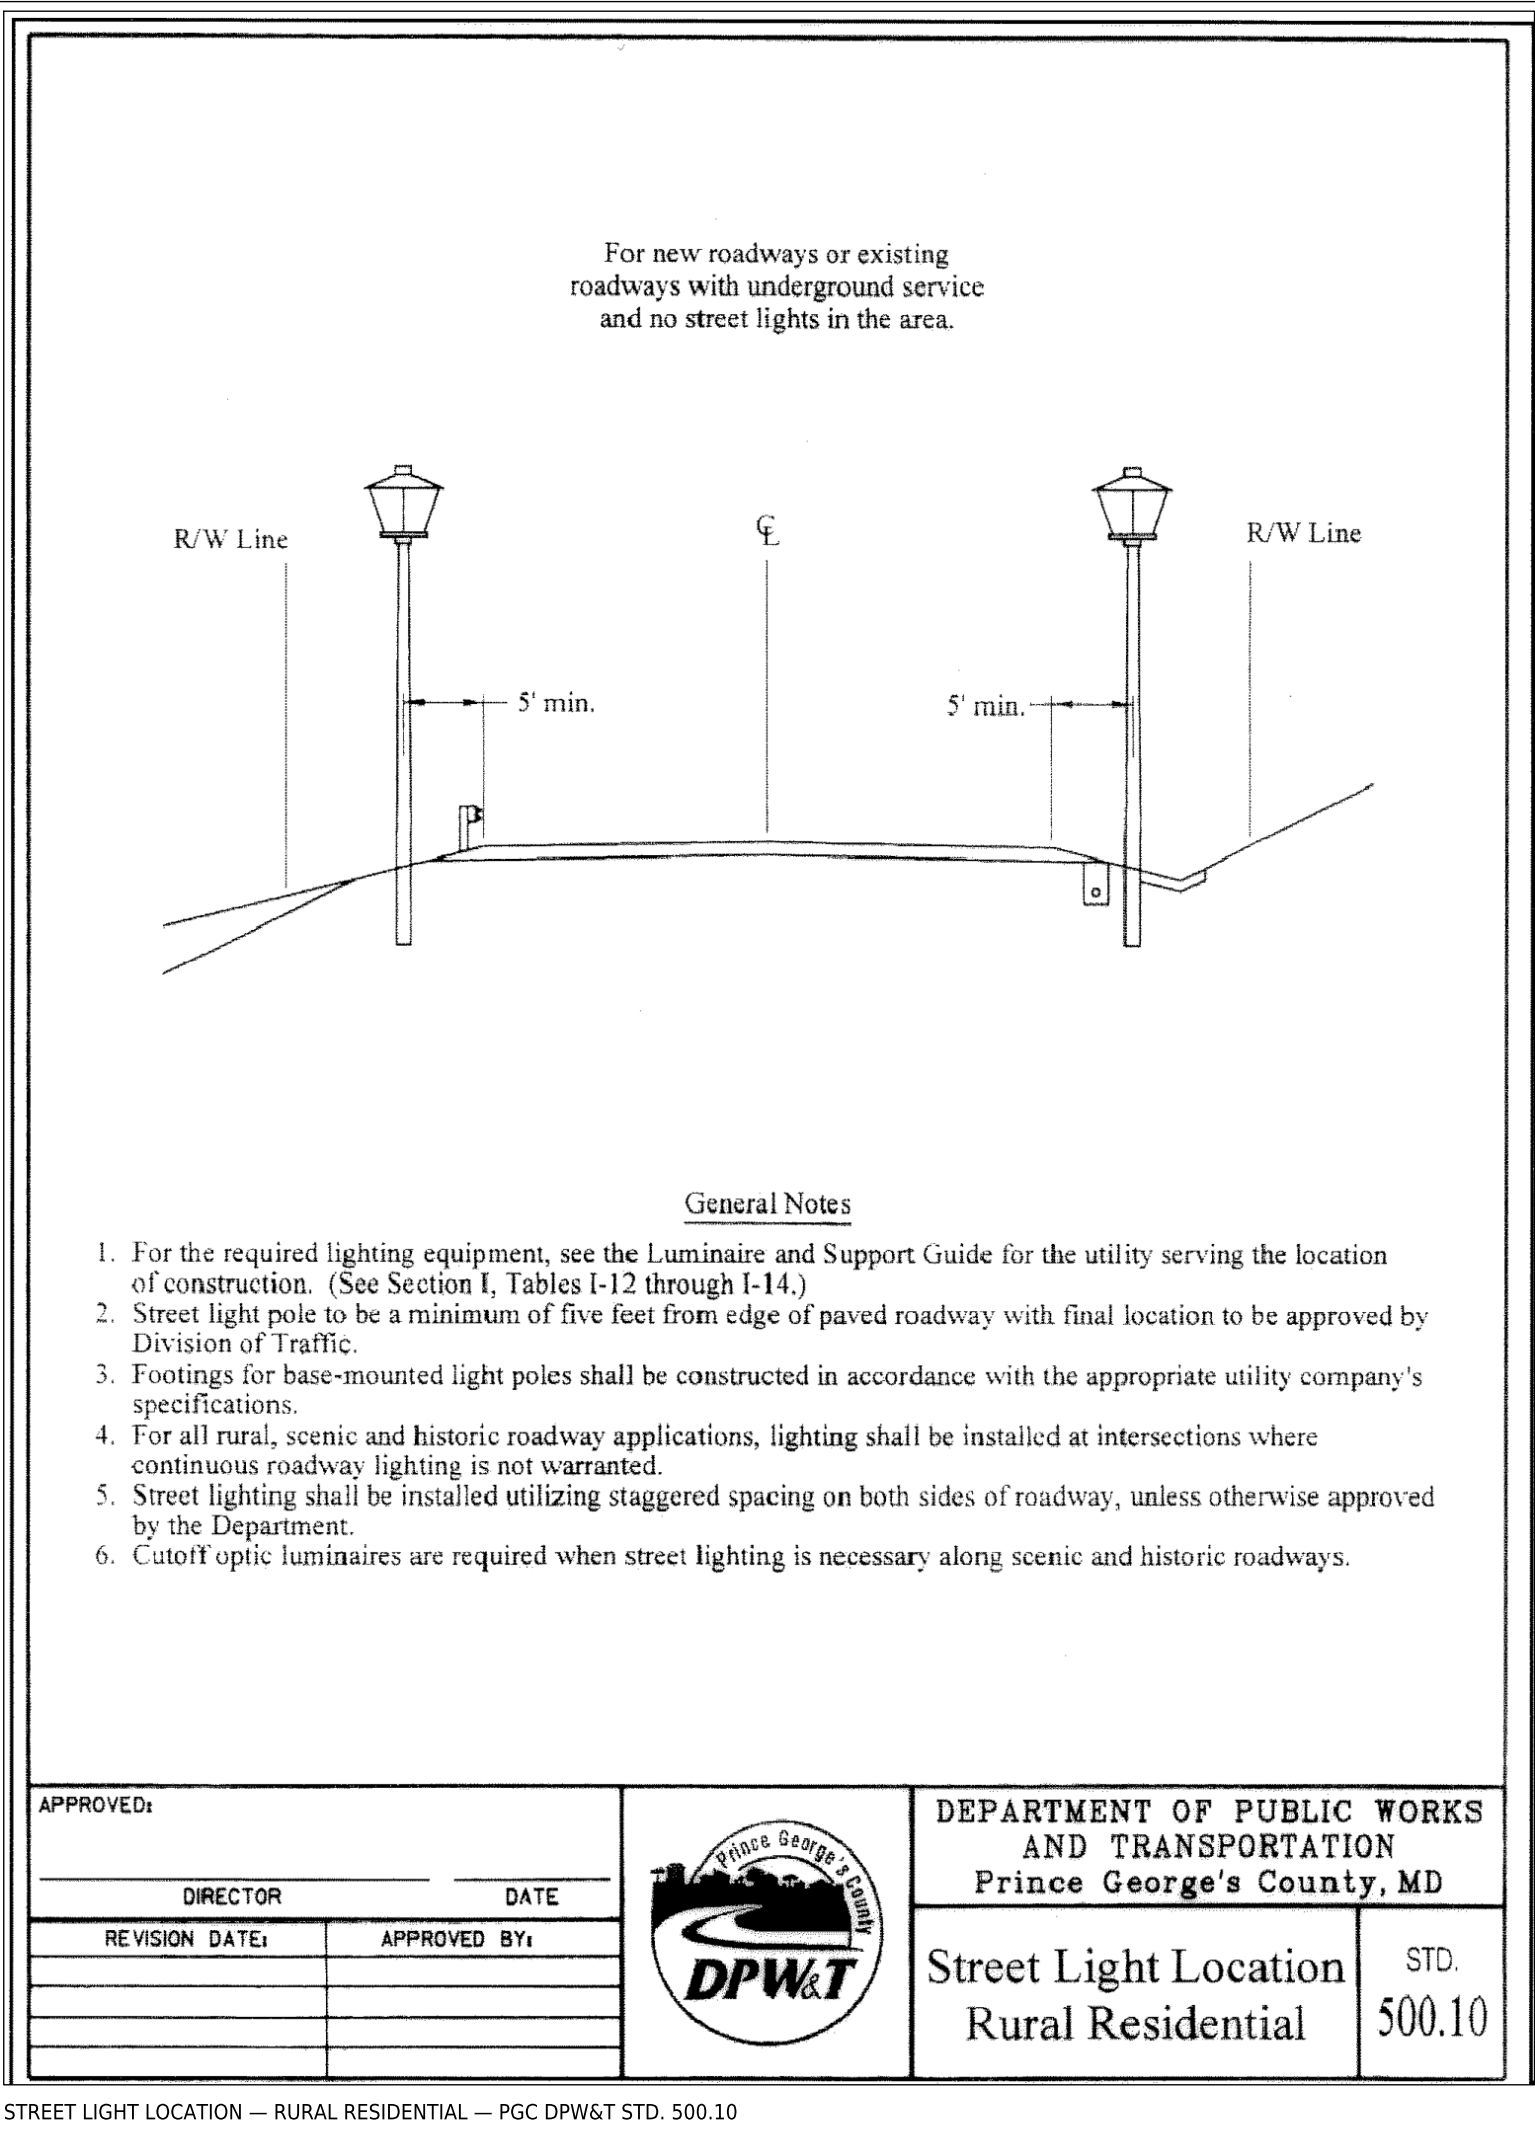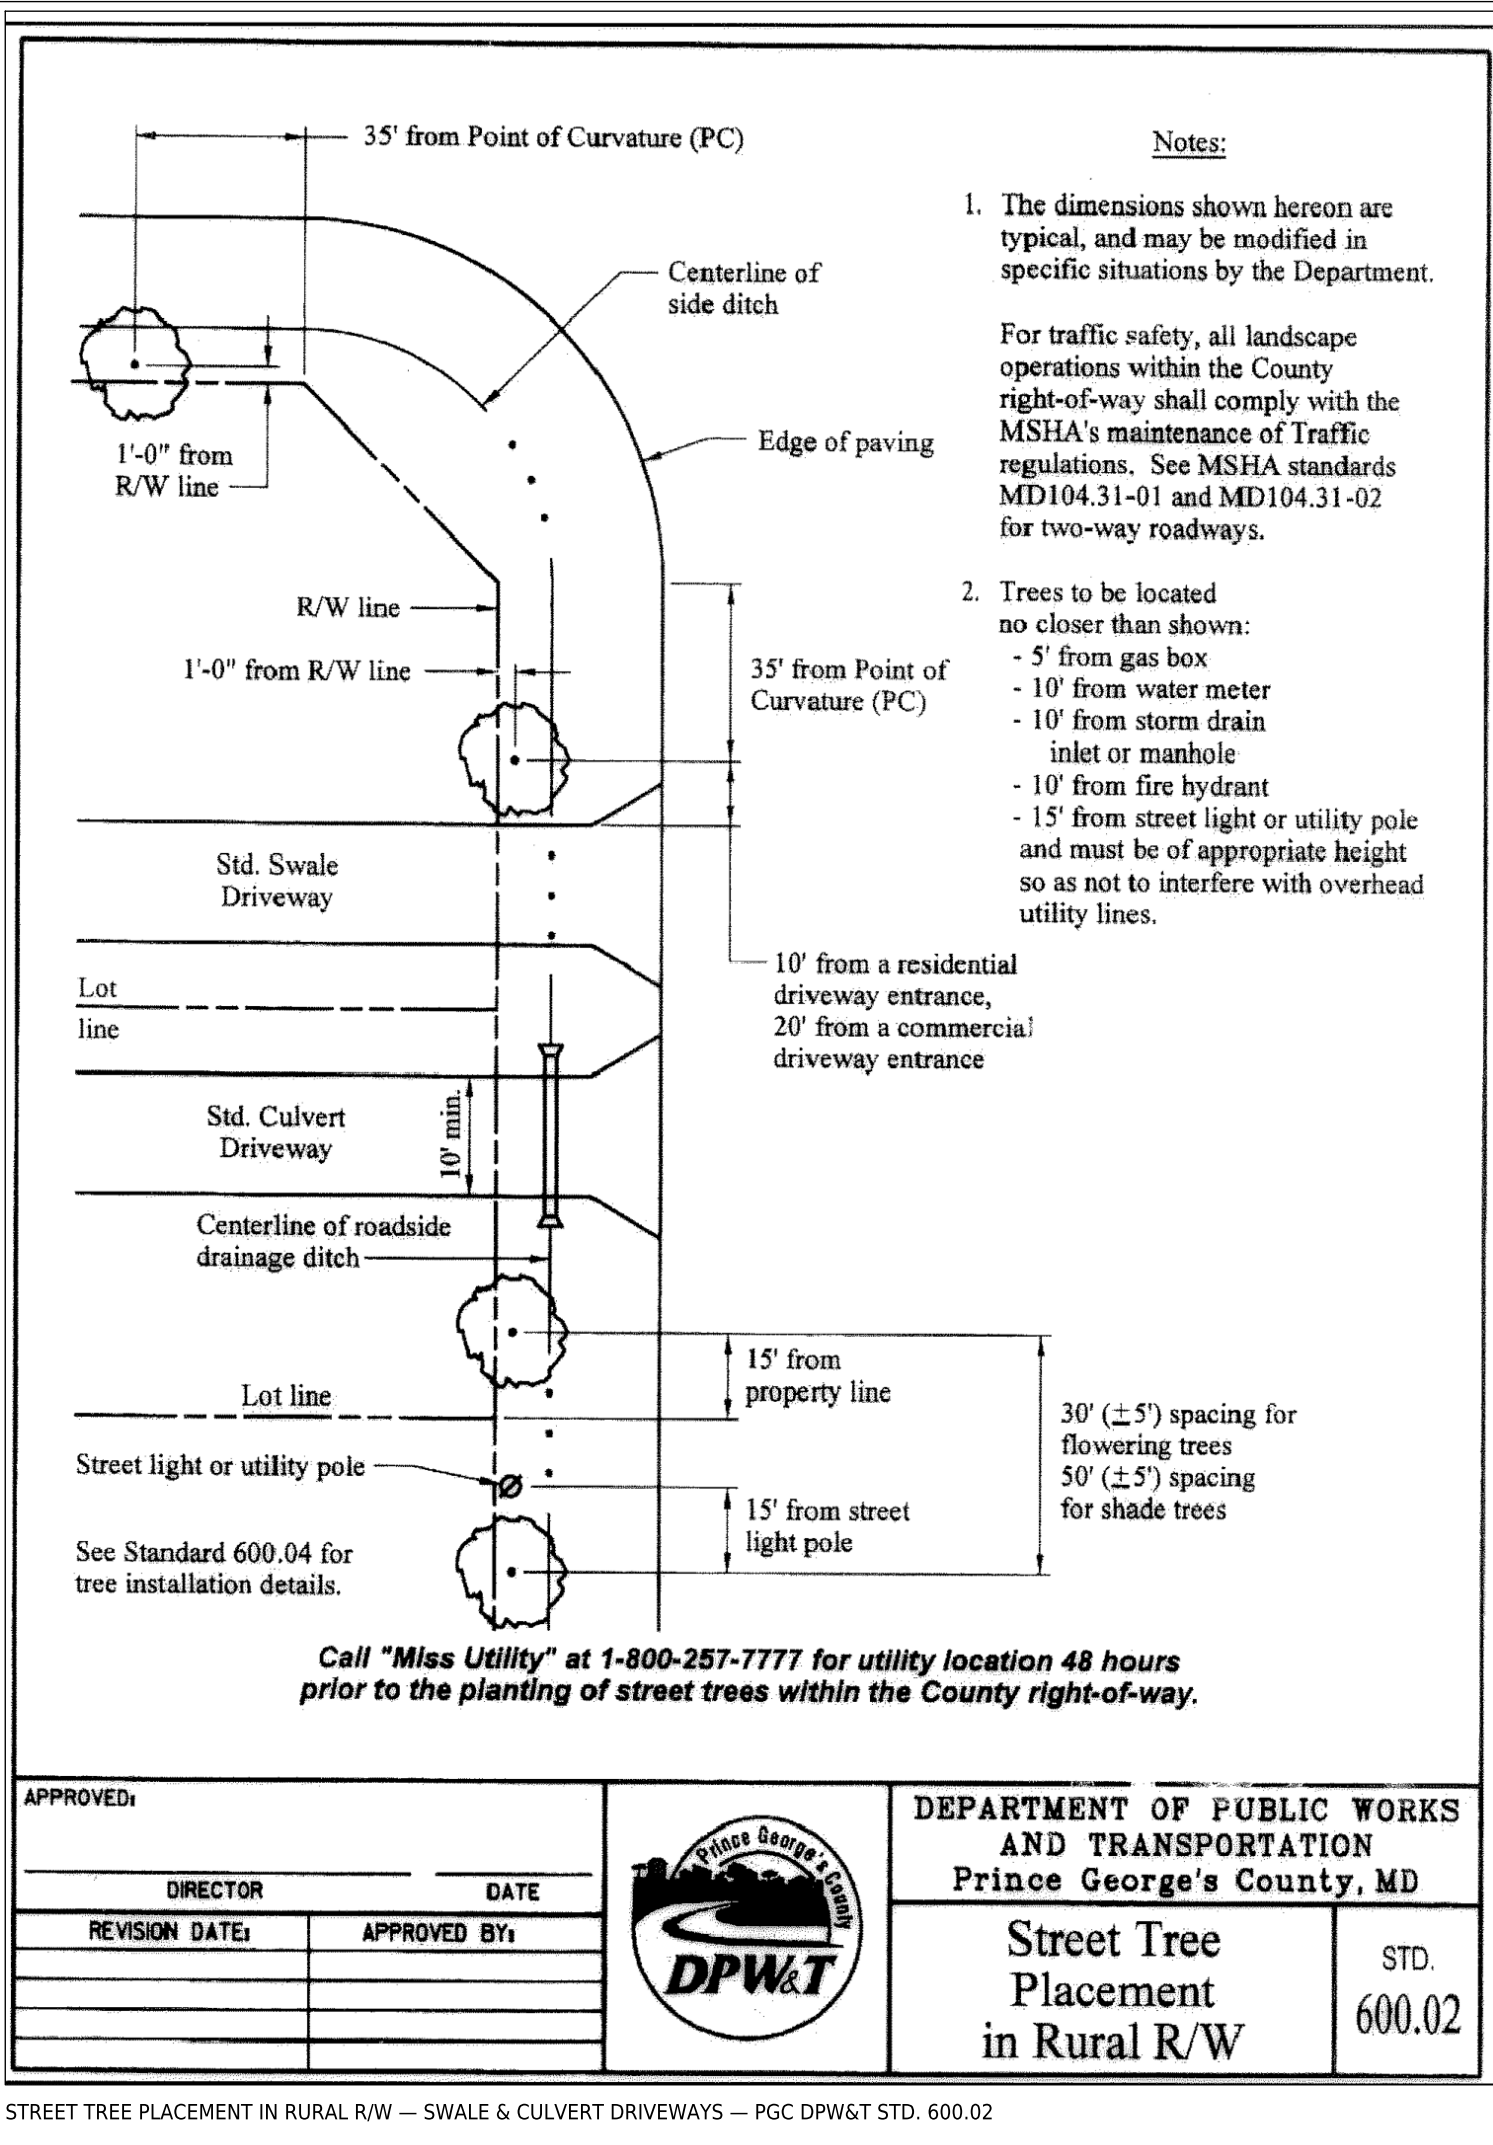


ESTATES COURT — TYPICAL SECTION (RURAL OPEN SECTION, 60' R/W)

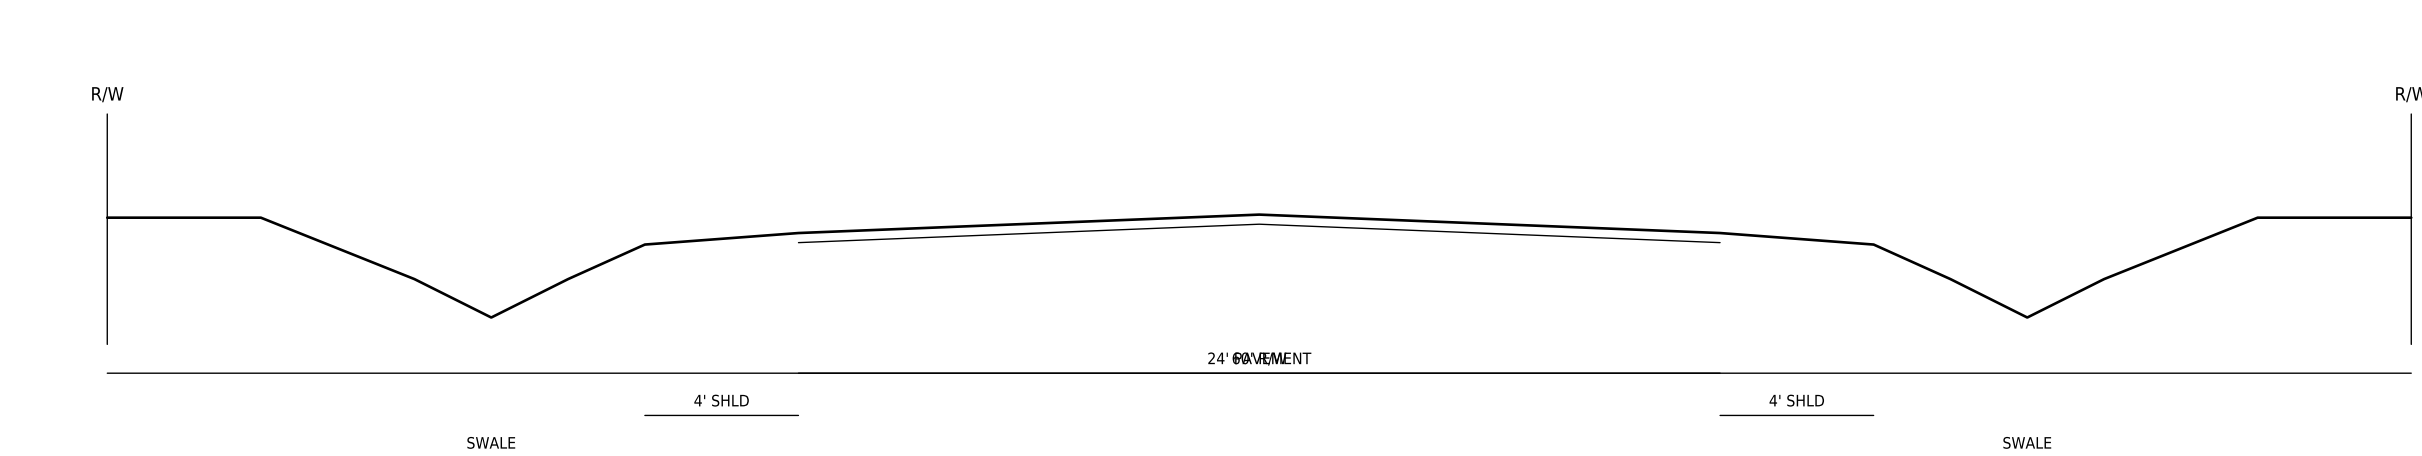


1.1/2" SURFACE + 2.1/2" BASE BIT. CONC. ON 6" GAB (DPW&T PAVEMENT SCHEDULE FOR RURAL RESIDENTIAL — CONFIRM)
CROSS SLOPE 2%; 4-FT STABILIZED SHOULDERS, SWALE FLOWLINE 20 FT OFF CENTRELINE, 3:1 SIDE SLOPES
DRIVEWAYS CROSS THE SWALE ON 15" RCP CULVERTS WITH FLARED END SECTIONS (DPW&T STD. 600.02)

MICRO-BIORETENTION (M-6) — TYPICAL SECTION

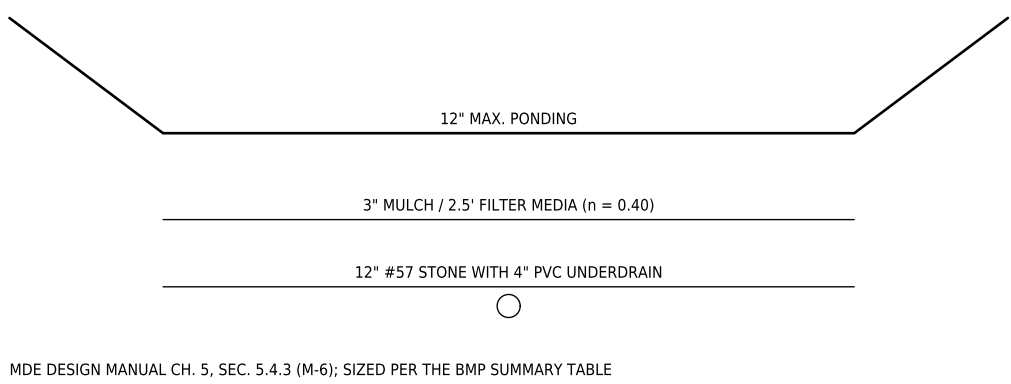

DRY SWALE (M-8) WITH CHECK DAM

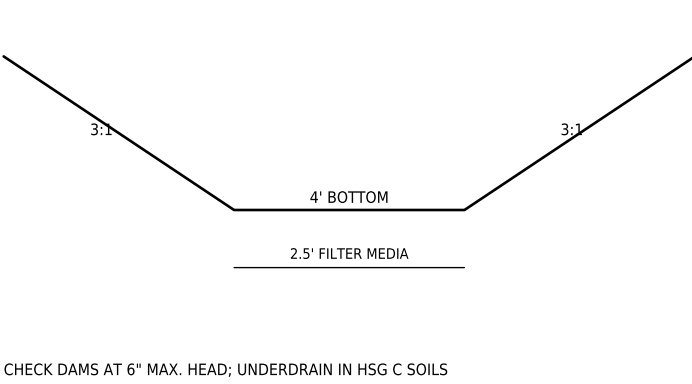

PLAN TYPE
SITE DEVELOPMENT CONCEPT PLAN

PROJECT
ESTATES AT INDIAN HEAD — LOTS 1-6
200-205 ESTATES COURT, ACCOKEEK, MD 20607
PLAT BOOK PM 226 PLAT 83 TAX MAP 151 P-3 WSSC
2206E01
ELECTION DIST. 5 - COUNCIL DIST. 9 - ZONE RR

OWNER / APPLICANT
GERALD WALDMAN REVOCABLE TRUST, 400 N. FLAGLER DR., WEST
PALM BEACH, FL 33401 (L-32062.F-043)

ENGINEER OF RECORD
W.L. MEEKINS, INC. — BILL MEEKINS, JR., 3101 RITCHIE ROAD,
FORESTVILLE, MD 20747 - 301-736-7115

SHEET TITLE
DETAILS

KEY MAP

SCALE
AS NOTED
DATUM: NAD 83 MD STATE PLANE (US FT) / NAVD 88

REVISIONS

NO.	DATE	DESCRIPTION
0	2026-09-30	CONCEPT SUBMISSION 1

PROFESSIONAL CERTIFICATION
I hereby certify that these documents were prepared or approved by me,
and that I am a duly licensed professional engineer under the laws of
the State of Maryland. License No. _____ Exp. _____

SEAL

CONCEPT SUBMISSION 1 — NOT SEALED
DATE 2026-09-30 JOB KEA-EH-2026
PREPARED WITH KRAUSE SPOTIAL ENGINE / CAD-PILOT

SHEET INDEX
C-600 COVER SHEET — BMP SUMMARY, DPE CHECKLIST AND NOTES
C-200 EXISTING CONDITIONS AND ENVIRONMENTAL FEATURES
C-300 SITE EROSION, GRADING AND PAVING PLAN
C-300 UTILITY, STREET LIGHT AND STREET TREE PLAN
C-400 STORMWATER MANAGEMENT CONCEPT AND DRAINAGE AREA MAP
C-500 SEDIMENT AND EROSION CONTROL PLAN
C-600 DETAILS