


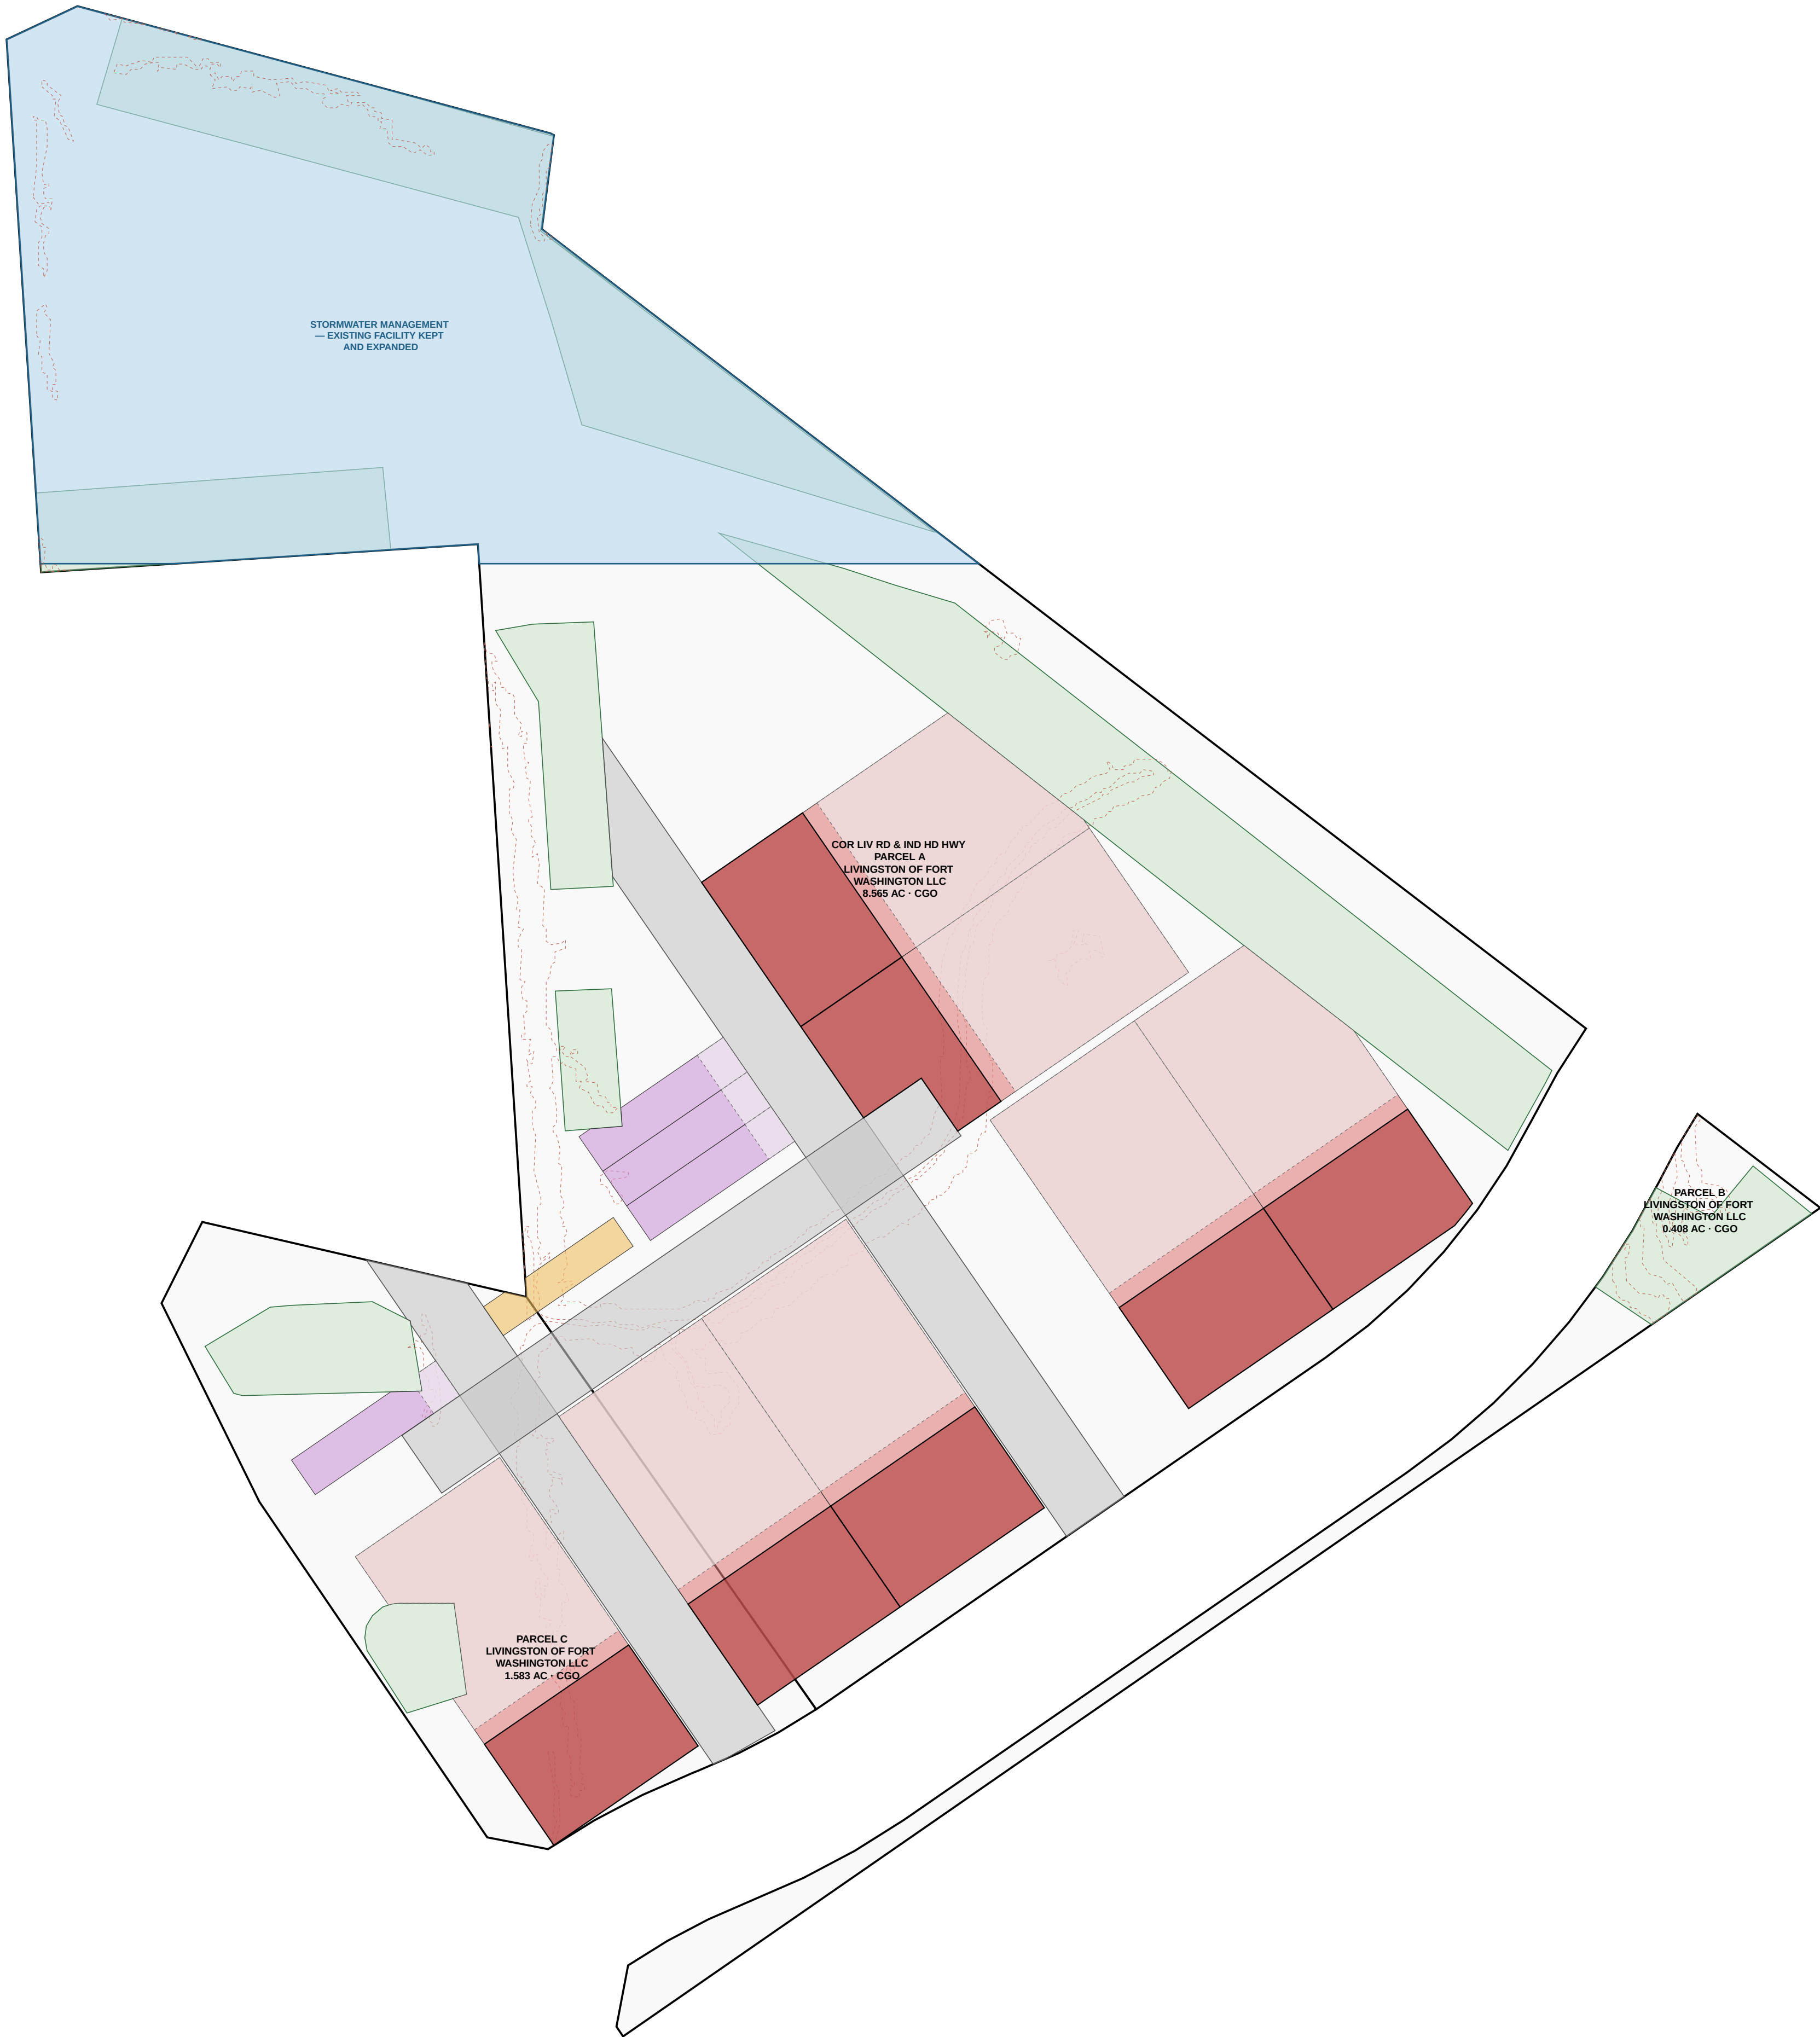

KEALEE

ATTACHED HOUSING YIELD STUDY — PRELIMINARY, NOT A SITE PLAN

Livingston of Fort Washington (11901 Gunpowder Dr / 12000 Livingston Rd) — CGO mixed-use concept

Zone CGO - certified intensity table Sec. 27-4203 - generated 2026-09-17

PARCELS (PGAtlas Address/Property — owner of record, assessment)

Act 0412007 · COR LIV RD & IND HD HWY PARCEL A · LIVINGSTON OF FORT WASHINGTON LLC · 8.568 ac assessed / 8.565 ac GIS · plat 05267017 · L 20797 F529

Act 5770967 · PARCEL B · LIVINGSTON OF FORT WASHINGTON LLC · 0.408 ac assessed / 0.408 ac GIS · plat 05267017 · L 20797 F529

Act 5770375 · PARCEL C · LIVINGSTON OF FORT WASHINGTON LLC · 1.583 ac assessed / 1.583 ac GIS · plat 05267017 · L 20797 F529

Tract 459.822 sf (10.556 ac). Boundary is the county parcel layer — not a survey.

WHAT CANNOT BE BUILT ON (county layers, clipped to the tract)

Woodland conservation (approved TCP areas) 1.86 ac · slopes >25% in bores 0.00 ac (graded banks 0.59 ac, regraded) · 15–25% 0.41 ac (built with grading) · stream buffer 0.00 ac · floodplain 0.00 ac · wetlands 0.00 ac

Reserved for stormwater management (the approved DSP's facility and its expansion) 107,627 sf.

Developable 304,662 sf (6.994 ac).

The Primary Management Area, the woodland conservation threshold and any expanded buffers are set by an approved Natural Resources Inventory and TCP; not by these layers. A 50-ft stream buffer and slopes over 25% are the minimum that would be taken; the NRI may use more.

CGO STANDARDS BY DWELLING TYPE (Sec. 27-4203)

Townhouse: 20 du/ac net · lot 'e 20 ft wide · coverage 'd 65% · yards 10/8/15 ft · height 'd 50 ft

Two-family (duplex): 40 du/ac net · lot 'e 20 ft wide · coverage 'd 65% · yards 10/8/15 ft · height 'd 50 ft

Two-over-two (stacked, 2 units per bay): 48 du/ac net · lot 'e 50 ft wide · coverage 'd 70% · yards 10/8/15 ft · height 'd 66 ft

Mixed use (retail below, dwellings above): 48 du/ac net · lot 'e 50 ft wide · coverage 'd 70% · yards 10/8/15 ft · height 'd 86 ft

YIELD — THIS LAYOUT

Townhouse: 1 bays 1' 1 du · 18.97 du/ac on 0.053 net ac (cap 20') · lot coverage 44.4% (cap 65%) · parking 2 at 2/ds ASSUMED — front-load garage + driveway on the lot

Two-over-two (stacked, 2 units per bay): 4 bays 1' 8 du · 27.98 du/ac on 0.286 net ac (cap 48') · lot coverage 48% (cap 70%) · parking 12 at 1.5/ds ASSUMED — one garage space per unit + surface bays along the street

Mixed use (retail below, dwellings above): 7 bays 1' 154 du + 45,000 sf retail · 37.6 du/ac on 4.086 net ac (cap 48') · lot coverage 35% (cap 70%) · 62 ft high (cap 86 ft) · parking 427 at 1.5/ds ASSUMED — surface lot behind the building on its parcel (1.5/ds + 4 per 1,000 sf retail, assumed)

Parking 243 surface spaces drawn (dashed) + 10 in garages and driveways = 253 against 441 required at the assumed ratios.

TOTAL 163 DWELLING UNITS in 12 bays · 15.44 du/ac gross on the 10.556-ac tract · 49,000 sf retail at grade

CEILINGS if the whole developable ground were one type (= 0.8 for streets, parking, open space):

Townhouse: 111 du

Two-family (duplex): 223 du

Two-over-two (stacked, 2 units per bay): 269 du

STORMWATER MANAGEMENT (ESD, WDE Ch. 5)

Impervious 153,041 sf (33.3%), Rv 0.3495, ESDv 13,394 cf at P, E 1.0 in 1' 16,743 sf of micro-bioretenment. Reserved for stormwater: 107,627 sf.

The 107,627 sf reserved (existing facility and its expansion) exceeds twice the 16,743 sf of practice the drawn programme needs at P, E 1.0 in; the balance is forebay, access, freeboard and the higher P, E the soils may require.

Micro-bioretenment in every surface parking lot island and a bioswale along each private street, credited under ESD; rooftop disconnection is not available over parking. Design per the DPE stormwater concept approval that precedes the DSP.

UNIT ASSUMPTIONS

Townhouse: 20 × 90 ft lot, 20 × 40 ft footprint, 1 du per bay, sticks of 'd 8

Two-family (duplex): 30 × 90 ft lot, 30 × 40 ft footprint, 1 du per bay, sticks of 'd 2

Two-over-two (stacked, 2 units per bay): 24 × 100 ft lot, 24 × 48 ft footprint, 2 du per bay, sticks of 'd 8

Mixed use (retail below, dwellings above): 100 × 200 ft lot, 100 × 70 ft footprint, 22 du per bay, 7,000 sf retail, 5 storeys 'H 62 ft

Private streets in 40-ft strips (25-ft pavement, with one side), each being off GUNPOWDER — the existing public right-of-way — with no new access to any other road. Visitor parking, open space and the Landscape Manual 4.7 buffer to the RE lots are DSP work not drawn here.

APPROVALS

CGO townhouse, two-family and multifamily (two-over-two) dwellings are listed uses with their own intensity standards in the certified Sec. 27-4203 table; a Detailed Site Plan is the approval path for residential in the commercial zones (confirm the use table entry for each type — the use table is not carried by this engine).

Sec. 27-5300 parking, Sec. 27-6400 landscaping (Landscape Manual 4.7 buffers against the RE lots), Sec. 25-121 woodland conservation, Sec. 24 subdivision (a preliminary plan of subdivision creates fee-simple townhouse and duplex lots, two-over-tens are condominium or fee-simple with a DSP), stormwater concept (DPE), WSSC hydraulic planning analysis.

This is a yield study prepared by the Kealee site-plan engine from county GIS and the certified zoning table. It is not a Detailed Site Plan, not a survey and not a determination of what the Planning Board will approve.