

KEALEE

design, build, deliver

PROJECT  
1009 Rollins Ave  
ADDRESS  
1009 Rollins Ave  
JURISDICTION  
prince georges md  
ZONE  
RSF-65  
SHEET  
C-000 — Cover Sheet, Approvals and General Notes  
SCALE  
1" = 10'  
STATUS  
PRELIMINARY  
SHEET NO.  
1 OF 11  
COORDINATES  
EPSG:2248  
H: NAD83  
V: NAVD83 (feet)

| SITE DATA          |                  |          |
|--------------------|------------------|----------|
| ZONE               | RSF-65           |          |
| TAX / PARCEL ID    | 1009 Rollins Ave |          |
| GROSS LOT AREA     | 8,009 SF         | 0.184 AC |
| LOT FRONTAGE       | 45' MIN          | 134.65'  |
| SETBACKS           | REQUIRED         | PROVIDED |
| FRONT YARD         | 23'              | 23'      |
| SIDE YARD          | 8'               | 8'       |
| REAR YARD          | 20'              | 20'      |
| COVERAGE           | MAX              | PROPOSED |
| LOT COVERAGE       | 35%              | 14.9%    |
| BUILDING FOOTPRINT | —                | 1,196 SF |
| DATUM              |                  |          |
| HORIZONTAL         | EPSG:2248        |          |
| VERTICAL           | NAVD83 (feet)    |          |

| SITE ANALYSIS           |                 |
|-------------------------|-----------------|
| 1. Gross tract area     | 8,009 SF        |
| 2. Area of dwelling     | 1,196 SF        |
| 3. Wooded area          | NOT ESTABLISHED |
| 4. Floodplain area      | NOT ESTABLISHED |
| 5. Net tract area       | 8,009 SF        |
| 6. TOTAL AREA DISTURBED | NOT QUANTIFIED  |

| SEQUENCE OF CONSTRUCTION                                                     |           |
|------------------------------------------------------------------------------|-----------|
| 1. Pre-construction meeting                                                  | 1 DAY     |
| 2. Obtain necessary permits                                                  | 2 DAYS    |
| 3. Notify Miss Utility at 811 at least 48 hours prior to any excavation      | 1 DAY     |
| 4. Construct stabilized construction entrance and perimeter sediment control | 2 DAYS    |
| 5. Rough grade, construct dwelling, utilities and driveway                   | 12 MONTHS |
| 6. Fine grade and stabilize all disturbed areas                              | 1 DAY     |
| 7. Remove sediment control devices when written permission has been granted  | 1 DAY     |
| TOTAL ESTIMATED TIME OF CONSTRUCTION: 12 MONTHS                              |           |

GENERAL NOTES

- CONTRACTOR SHALL CONTACT MISS UTILITY AT 811 A MINIMUM OF 48 HOURS PRIOR TO ANY EXCAVATION.
- ALL EXISTING AND PROPOSED UTILITIES SHOWN PER PCC CODE SEC. 32.106.
- PROPOSED GRADE SHOWN SOLID; EXISTING GRADE SHOWN DASHED.
- ROUGH EARTHWORK GRADES AND UTILITY ELEVATIONS SHOWN TO TENTHS OF A FOOT.
- BOUNDARY SHOWN IS COMPILED JURISDICTION GIS, NOT A BOUNDARY SURVEY.

PLAT OF RECORD

Porter Subdivision, Plat Book PM 231 p.50

NOTES OF RECORD

- BASES OF RECORD: Maryland State Plane Coordinate System (NAD 83).
- BOUNDARY OF RECORD transcribed from the recorded plat; traverse closes 1.60708, 8009 SF computed against 8,009 SF recorded.
- A transcription is not a field survey. Monumentation is not verified here.

The surveyor certifies, under declaration and approval signatures of the recorded plat are NOT reproduced here; they appear in the monumentation set to this platting.

LEGEND

- PROPERTY BOUNDARY
- BRL — BUILDING RESTRICTION LINE
- PROPOSED STRUCTURE
- EXISTING CONTOUR — PGATLAS 2 FT (2023), NAVD83
- STREET CENTRELINE
- PROPOSED PAVEMENT — DRIVEWAY / WALK
- EASEMENT

PRINCE GEORGES COUNTY SOIL CONSERVATION DISTRICT APPROVAL

SEDIMENT CONTROL, GRADING, SOILS & DRAINAGE


SIGNATURE DATE

DPE SITE/ROAD PLAN REVIEW DIVISION APPROVAL

SIGNATURE DATE

REVISIONS

— NONE —

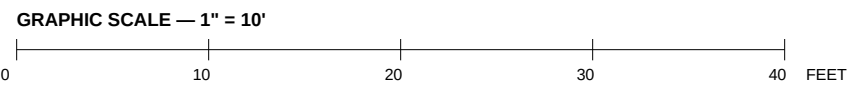



KEALEE

design, build, deliver

PROJECT  
1009 Rollins Ave  
ADDRESS  
1009 Rollins Ave  
JURISDICTION  
prince georges md  
ZONE  
RSF-65  
SHEET  
C-100 — Existing Conditions and Boundary Plan  
SCALE  
1" = 10'  
STATUS  
PRELIMINARY  
SHEET NO.  
2 OF 11  
COORDINATES  
EPSG:2248  
H: NAD83  
V: NAVD83 (feet)

| SITE DATA          |                  |          |
|--------------------|------------------|----------|
| ZONE               | RSF-65           |          |
| TAX / PARCEL ID    | 1009 Rollins Ave |          |
| GROSS LOT AREA     | 8,009 SF         | 0.184 AC |
| LOT FRONTAGE       | 45' MIN          | 134.65'  |
| SETBACKS           | REQUIRED         | PROVIDED |
| FRONT YARD         | 23'              | 23'      |
| SIDE YARD          | 8'               | 8'       |
| REAR YARD          | 20'              | 20'      |
| COVERAGE           | MAX              | PROPOSED |
| LOT COVERAGE       | 35%              | 14.9%    |
| BUILDING FOOTPRINT | —                | 1,196 SF |
| DATUM              |                  |          |
| HORIZONTAL         | EPSG:2248        |          |
| VERTICAL           | NAVD83 (feet)    |          |

| SITE ANALYSIS           |                 |
|-------------------------|-----------------|
| 1. Gross tract area     | 8,009 SF        |
| 2. Area of dwelling     | 1,196 SF        |
| 3. Wooded area          | NOT ESTABLISHED |
| 4. Floodplain area      | NOT ESTABLISHED |
| 5. Net tract area       | 8,009 SF        |
| 6. TOTAL AREA DISTURBED | NOT QUANTIFIED  |

| SEQUENCE OF CONSTRUCTION                                                     |           |
|------------------------------------------------------------------------------|-----------|
| 1. Pre-construction meeting                                                  | 1 DAY     |
| 2. Obtain necessary permits                                                  | 2 DAYS    |
| 3. Notify Miss Utility at 811 at least 48 hours prior to any excavation      | 1 DAY     |
| 4. Construct stabilized construction entrance and perimeter sediment control | 2 DAYS    |
| 5. Rough grade, construct dwelling, utilities and driveway                   | 12 MONTHS |
| 6. Fine grade and stabilize all disturbed areas                              | 1 DAY     |
| 7. Remove sediment control devices when written permission has been granted  | 1 DAY     |
| TOTAL ESTIMATED TIME OF CONSTRUCTION: 12 MONTHS                              |           |

- GENERAL NOTES**
- CONTRACTOR SHALL CONTACT MISS UTILITY AT 811 A MINIMUM OF 48 HOURS PRIOR TO ANY EXCAVATION.
  - ALL EXISTING AND PROPOSED UTILITIES SHOWN PER PCC CODE SEC. 32.106.
  - PROPOSED GRADE SHOWN SOLID; EXISTING GRADE SHOWN DASHED.
  - ROUGH EARTHWORK GRADES AND UTILITY ELEVATIONS SHOWN TO TENTHS OF A FOOT.
  - BOUNDARY SHOWN IS COMPILED JURISDICTION GIS, NOT A BOUNDARY SURVEY.

- PLAT OF RECORD**  
Paper Subdivision, Plat Book PM 231 p.50
- NOTES OF RECORD**
- BASES OF RECORD: Maryland State Plane Coordinate System (NAD 83).
  - BOUNDARY OF RECORD transcribed from the recorded plat; traverse closes 1.60708, 8009 SF computed against 8,009 SF recorded.
  - A transcription is not a field survey. Monumentation is not verified here.

The surveyor certifies, under declaration and approval signatures of the recorded plat are NOT reproduced here; they appear in the monumentation set to this platting.

- LEGEND**
- PROPERTY BOUNDARY
  - BRL — BUILDING RESTRICTION LINE
  - PROPOSED STRUCTURE
  - EXISTING CONTOUR — PGATLAS 2 FT (2023), NAVD83
  - STREET CENTRELINE
  - PROPOSED PAVEMENT — DRIVEWAY / WALK
  - EASEMENT

PRINCE GEORGES COUNTY SOIL CONSERVATION DISTRICT APPROVAL


SEDIMENT CONTROL, GRADING, SOILS & DRAINAGE

SIGNATURE DATE

DPE SITE/ROAD PLAN REVIEW DIVISION APPROVAL

SIGNATURE DATE

REVISIONS  
— NONE —

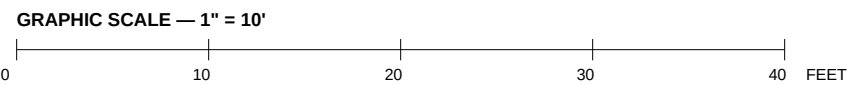



KEALEE

design, build, deliver

PROJECT  
1009 Rollins Ave  
ADDRESS  
1009 Rollins Ave  
JURISDICTION  
prince georges md  
ZONE  
RSF-65  
SHEET  
C-200 — Overall Site and Zoning Plan  
SCALE  
1" = 10'  
STATUS  
PRELIMINARY  
SHEET NO.  
3 OF 11  
COORDINATES  
EPSG:2248  
H: NAD83  
V: NAVD83 (feet)

| SITE DATA          |                  |          |
|--------------------|------------------|----------|
| ZONE               | RSF-65           |          |
| TAX / PARCEL ID    | 1009 Rollins Ave |          |
| GROSS LOT AREA     | 8,009 SF         | 0.184 AC |
| LOT FRONTAGE       | 45' MIN          | 134.65'  |
| SETBACKS           | REQUIRED         | PROVIDED |
| FRONT YARD         | 23'              | 23'      |
| SIDE YARD          | 8'               | 8'       |
| REAR YARD          | 20'              | 20'      |
| COVERAGE           | MAX              | PROPOSED |
| LOT COVERAGE       | 35%              | 14.9%    |
| BUILDING FOOTPRINT | —                | 1,196 SF |
| DATUM              |                  |          |
| HORIZONTAL         | EPSG:2248        |          |
| VERTICAL           | NAVD83 (feet)    |          |

| SITE ANALYSIS           |                 |
|-------------------------|-----------------|
| 1. Gross tract area     | 8,009 SF        |
| 2. Area of dwelling     | 1,196 SF        |
| 3. Wooded area          | NOT ESTABLISHED |
| 4. Floodplain area      | NOT ESTABLISHED |
| 5. Net tract area       | 8,009 SF        |
| 6. TOTAL AREA DISTURBED | NOT QUANTIFIED  |

| SEQUENCE OF CONSTRUCTION                                                     |           |
|------------------------------------------------------------------------------|-----------|
| 1. Pre-construction meeting                                                  | 1 DAY     |
| 2. Obtain necessary permits                                                  | 2 DAYS    |
| 3. Notify Miss Utility at 811 at least 48 hours prior to any excavation      | 1 DAY     |
| 4. Construct stabilized construction entrance and perimeter sediment control | 2 DAYS    |
| 5. Rough grade, construct dwelling, utilities and driveway                   | 12 MONTHS |
| 6. Fine grade and stabilize all disturbed areas                              | 1 DAY     |
| 7. Remove sediment control devices when written permission has been granted  | 1 DAY     |
| TOTAL ESTIMATED TIME OF CONSTRUCTION: 12 MONTHS                              |           |

- GENERAL NOTES**
- CONTRACTOR SHALL CONTACT MISS UTILITY AT 811 A MINIMUM OF 48 HOURS PRIOR TO ANY EXCAVATION.
  - ALL EXISTING AND PROPOSED UTILITIES SHOWN PER PGC CODE SEC. 32.106.
  - PROPOSED GRADE SHOWN SOLID; EXISTING GRADE SHOWN DASHED.
  - ROUGH EARTHWORK GRADES AND UTILITY ELEVATIONS SHOWN TO TENTHS OF A FOOT.
  - BOUNDARY SHOWN IS COMPILED JURISDICTION GIS, NOT A BOUNDARY SURVEY.

- PLAT OF RECORD**  
Paper Subdivision, Plat Book PM 231 p.50
- NOTES OF RECORD**
- BASES OF RECORD: Maryland State Plane Coordinate System (NAD 83).
  - BOUNDARY OF RECORD transcribed from the recorded plat; traverse closes 1.60706, 8009 SF computed against 8,009 SF recorded.
  - A transcription is not a field survey. Monumentation is not verified here.

The surveyor certifies, under declaration and approval signatures of the recorded plat are NOT reproduced here; they appear in the monumentation set to this platting.

- LEGEND**
- PROPERTY BOUNDARY
  - BRL — BUILDING RESTRICTION LINE
  - PROPOSED STRUCTURE
  - EXISTING CONTOUR — PGATLAS 2 FT (2023), NAVD83
  - STREET CENTRELINE
  - PROPOSED PAVEMENT — DRIVEWAY / WALK
  - EASEMENT

PRINCE GEORGE'S COUNTY SOIL CONSERVATION DISTRICT APPROVAL


SEDIMENT CONTROL, GRADING, SOILS & DRAINAGE

SIGNATURE DATE

DPE SITEROAD PLAN REVIEW DIVISION APPROVAL

SIGNATURE DATE

REVISIONS  
— NONE —

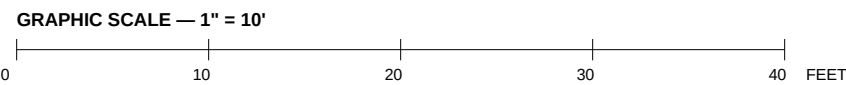



KEALEE

design, build, deliver

PROJECT  
1009 Rollins Ave  
ADDRESS  
1009 Rollins Ave  
JURISDICTION  
prince georges md  
ZONE  
RSF-65  
SHEET  
C-300 — Demolition Plan  
SCALE  
1" = 10'  
STATUS  
PRELIMINARY  
SHEET NO.  
4 OF 11  
COORDINATES  
EPSG:2248  
H: NAD83  
V: NAVD83 (feet)

| SITE DATA          |                  |          |
|--------------------|------------------|----------|
| ZONE               | RSF-65           |          |
| TAX / PARCEL ID    | 1009 Rollins Ave |          |
| GROSS LOT AREA     | 8,009 SF         | 0.184 AC |
| LOT FRONTAGE       | 45' MIN          | 134.65'  |
| SETBACKS           | REQUIRED         | PROVIDED |
| FRONT YARD         | 23'              | 23'      |
| SIDE YARD          | 8'               | 8'       |
| REAR YARD          | 20'              | 20'      |
| COVERAGE           | MAX              | PROPOSED |
| LOT COVERAGE       | 35%              | 14.9%    |
| BUILDING FOOTPRINT | —                | 1,196 SF |
| DATUM              |                  |          |
| HORIZONTAL         | EPSG:2248        | NAD83    |
| VERTICAL           | NAVD83 (feet)    |          |

| SITE ANALYSIS           |                 |
|-------------------------|-----------------|
| 1. Gross tract area     | 8,009 SF        |
| 2. Area of dwelling     | 1,196 SF        |
| 3. Wooded area          | NOT ESTABLISHED |
| 4. Floodplain area      | NOT ESTABLISHED |
| 5. Net tract area       | 8,009 SF        |
| 6. TOTAL AREA DISTURBED | NOT QUANTIFIED  |

| SEQUENCE OF CONSTRUCTION                                                     |           |
|------------------------------------------------------------------------------|-----------|
| 1. Pre-construction meeting                                                  | 1 DAY     |
| 2. Obtain necessary permits                                                  | 2 DAYS    |
| 3. Notify Miss Utility at 811 at least 48 hours prior to any excavation      | 1 DAY     |
| 4. Construct stabilized construction entrance and perimeter sediment control | 2 DAYS    |
| 5. Rough grade, construct dwelling, utilities and driveway                   | 12 MONTHS |
| 6. Fine grade and stabilize all disturbed areas                              | 1 DAY     |
| 7. Remove sediment control devices when written permission has been granted  | 1 DAY     |
| TOTAL ESTIMATED TIME OF CONSTRUCTION: 12 MONTHS                              |           |

- GENERAL NOTES**
- CONTRACTOR SHALL CONTACT MISS UTILITY AT 811 A MINIMUM OF 48 HOURS PRIOR TO ANY EXCAVATION.
  - ALL EXISTING AND PROPOSED UTILITIES SHOWN PER PGC CODE SEC. 32.106.
  - PROPOSED GRADE SHOWN SOLID; EXISTING GRADE SHOWN DASHED.
  - ROUGH EARTHWORK GRADES AND UTILITY ELEVATIONS SHOWN TO TENTHS OF A FOOT.
  - BOUNDARY SHOWN IS COMPILED JURISDICTION GIS, NOT A BOUNDARY SURVEY.

- PLAT OF RECORD**  
Porter Subdivision, Plat Book PM 231 p.50
- NOTES OF RECORD**
- BASES OF RECORD: Maryland State Plane Coordinate System (NAD 83).
  - BOUNDARY OF RECORD transcribed from the recorded plat; traverse closes 1.62708, 8009 SF computed against 8,009 SF recorded.
  - A transcription is not a field survey. Monumentation is not verified here.

The surveyor certifies, under declaration and approval signatures of the recorded plat are NOT reproduced here; they appear in the monumentation set to this plan.

- LEGEND**
- PROPERTY BOUNDARY
  - BRL — BUILDING RESTRICTION LINE
  - PROPOSED STRUCTURE
  - EXISTING CONTOUR — PGATLAS 2 FT (2023), NAVD83
  - STREET CENTRELINE
  - PROPOSED PAVEMENT — DRIVEWAY / WALK
  - EASEMENT

PRINCE GEORGE'S COUNTY SOIL CONSERVATION DISTRICT APPROVAL


SEDIMENT CONTROL, GRADING, SOILS & DRAINAGE

SIGNATURE DATE

DPE SITEROAD PLAN REVIEW DIVISION APPROVAL

SIGNATURE DATE

REVISIONS  
— NONE —

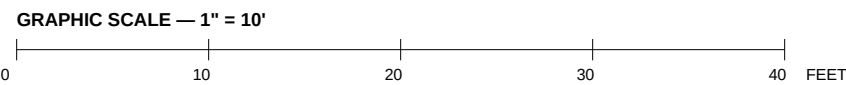



KEALEE

design, build, deliver

PROJECT  
1009 Rollins Ave  
ADDRESS  
1009 Rollins Ave  
JURISDICTION  
prince georges md  
ZONE  
RSF-65  
SHEET  
C-400 — Grading and Drainage Plan  
SCALE  
1" = 10'  
STATUS  
PRELIMINARY  
SHEET NO.  
5 OF 11  
COORDINATES  
EPSG:2248  
H: NAD83  
V: NAVD83 (feet)

| SITE DATA          |                  |          |          |
|--------------------|------------------|----------|----------|
| ZONE               | RSF-65           |          |          |
| TAX / PARCEL ID    | 1009 Rollins Ave |          |          |
| GROSS LOT AREA     | 8,009 SF         | 0.184 AC |          |
| LOT FRONTAGE       | 45' MIN          | 134.65'  |          |
| SETBACKS           |                  | REQUIRED | PROVIDED |
| FRONT YARD         | 23'              | 23'      |          |
| SIDE YARD          | 8'               | 8'       |          |
| REAR YARD          | 20'              | 20'      |          |
| COVERAGE           |                  | MAX      | PROPOSED |
| LOT COVERAGE       | 35%              | 14.9%    |          |
| BUILDING FOOTPRINT | —                | 1,196 SF |          |
| DATUM              |                  |          |          |
| HORIZONTAL         | EPSG:2248        | NAD83    |          |
| VERTICAL           | NAVD83 (feet)    |          |          |

| SITE ANALYSIS           |                 |
|-------------------------|-----------------|
| 1. Gross tract area     | 8,009 SF        |
| 2. Area of dwelling     | 1,196 SF        |
| 3. Wooded area          | NOT ESTABLISHED |
| 4. Floodplain area      | NOT ESTABLISHED |
| 5. Net tract area       | 8,009 SF        |
| 6. TOTAL AREA DISTURBED | NOT QUANTIFIED  |

| SEQUENCE OF CONSTRUCTION                                                     |           |
|------------------------------------------------------------------------------|-----------|
| 1. Pre-construction meeting                                                  | 1 DAY     |
| 2. Obtain necessary permits                                                  | 2 DAYS    |
| 3. Notify Miss Utility at 811 at least 48 hours prior to any excavation      | 1 DAY     |
| 4. Construct stabilized construction entrance and perimeter sediment control | 2 DAYS    |
| 5. Rough grade, construct dwelling, utilities and driveway                   | 12 MONTHS |
| 6. Fine grade and stabilize all disturbed areas                              | 1 DAY     |
| 7. Remove sediment control devices when written permission has been granted  | 1 DAY     |
| 8. Final cleanup                                                             | 1 DAY     |
| TOTAL ESTIMATED TIME OF CONSTRUCTION: 12 MONTHS                              |           |

- GENERAL NOTES**
- CONTRACTOR SHALL CONTACT MISS UTILITY AT 811 A MINIMUM OF 48 HOURS PRIOR TO ANY EXCAVATION.
  - ALL EXISTING AND PROPOSED UTILITIES SHOWN PER PCC CODE SEC. 32.106.
  - PROPOSED GRADE: SHOWN SOLID; EXISTING GRADE: SHOWN DASHED.
  - ROUGH EARTHWORK GRADES AND UTILITY ELEVATIONS SHOWN TO TENTHS OF A FOOT.
  - BOUNDARY SHOWN IS COMPILED JURISDICTION GIS, NOT A BOUNDARY SURVEY.

- PLAT OF RECORD**  
Porter Subdivision, Plat Book PM 231 p.50
- NOTES OF RECORD**
- BASES OF RECORD: Maryland State Plane Coordinate System (NAD 83).
  - BOUNDARY OF RECORD transcribed from the recorded plat; traverse closes 1.66708, 8009 SF computed against 8,009 SF recorded.
  - A transcription is not a field survey. Monumentation is not verified here.

The surveyor certifies, under declaration and approval signatures of the recorded plat are NOT reproduced here; they appear in that instrument, not in this drawing.

- LEGEND**
- PROPERTY BOUNDARY
  - BRL — BUILDING RESTRICTION LINE
  - PROPOSED STRUCTURE
  - EXISTING CONTOUR — PGATLAS 2 FT (2023), NAVD83
  - STREET CENTRELINE
  - PROPOSED PAVEMENT — DRIVEWAY / WALK
  - EASEMENT

PRINCE GEORGE'S COUNTY SOIL CONSERVATION DISTRICT APPROVAL

SEDIMENT CONTROL, GRADING, SOILS & DRAINAGE

SIGNATURE DATE

DPE SITEROAD PLAN REVIEW DIVISION APPROVAL

SIGNATURE DATE



**GRADING CERTIFICATE**  
I HEREBY CERTIFY THAT THIS PLAN CONFORMS TO THE REQUIREMENTS OF SUBTITLE 32, DIVISION 2 OF THE CODE OF PRINCE GEORGE'S COUNTY WATER RESOURCES PROTECTION AND GRADING CODE AND THAT I OR MY STAFF HAVE INSPECTED THIS SITE AND THAT DRAINAGE FLOWS FROM UPHILL PROPERTIES ONTO THIS SITE, AND FROM THIS SITE ONTO DOWNHILL PROPERTIES, HAVE BEEN ADDRESSED IN SUBSTANTIAL ACCORDANCE WITH APPLICABLE CODES, SIGNED, SEALED AND DATED BY A PROFESSIONAL ENGINEER LICENSED IN THE STATE OF MARYLAND.

Prince George's County CPE, Site Rough Grading Design Review Checklist, Item A-10

**STABILIZATION COMPLIANCE PREAMBLE**  
Stabilization practices on all projects must be in compliance with the requirements of COMAR 26.17.01 by January 9, 2013, regardless of when an erosion and sediment control plan was approved. COMAR 26.17.01.05(C), Grandfathering of approved plans

**STANDARD STABILIZATION NOTE**  
Following initial soil disturbance or redistribution, permanent or temporary stabilization must be completed within: a) Three (3) calendar days as to the surface of all perimeter ditches, swales, ditches, perimeter slopes, and all slopes steeper than 3 horizontal to 1 vertical (3:1); and b) Seven (7) calendar days as to all other disturbed or graded areas on the project site not under active grading.  
2013 Maryland Standards and Specifications for Soil Erosion and Sediment Control, "Standard Stabilization Note" (adopted by COMAR 26.17.01.05A(2))

REVISIONS  
— NONE —

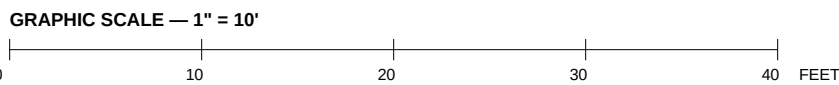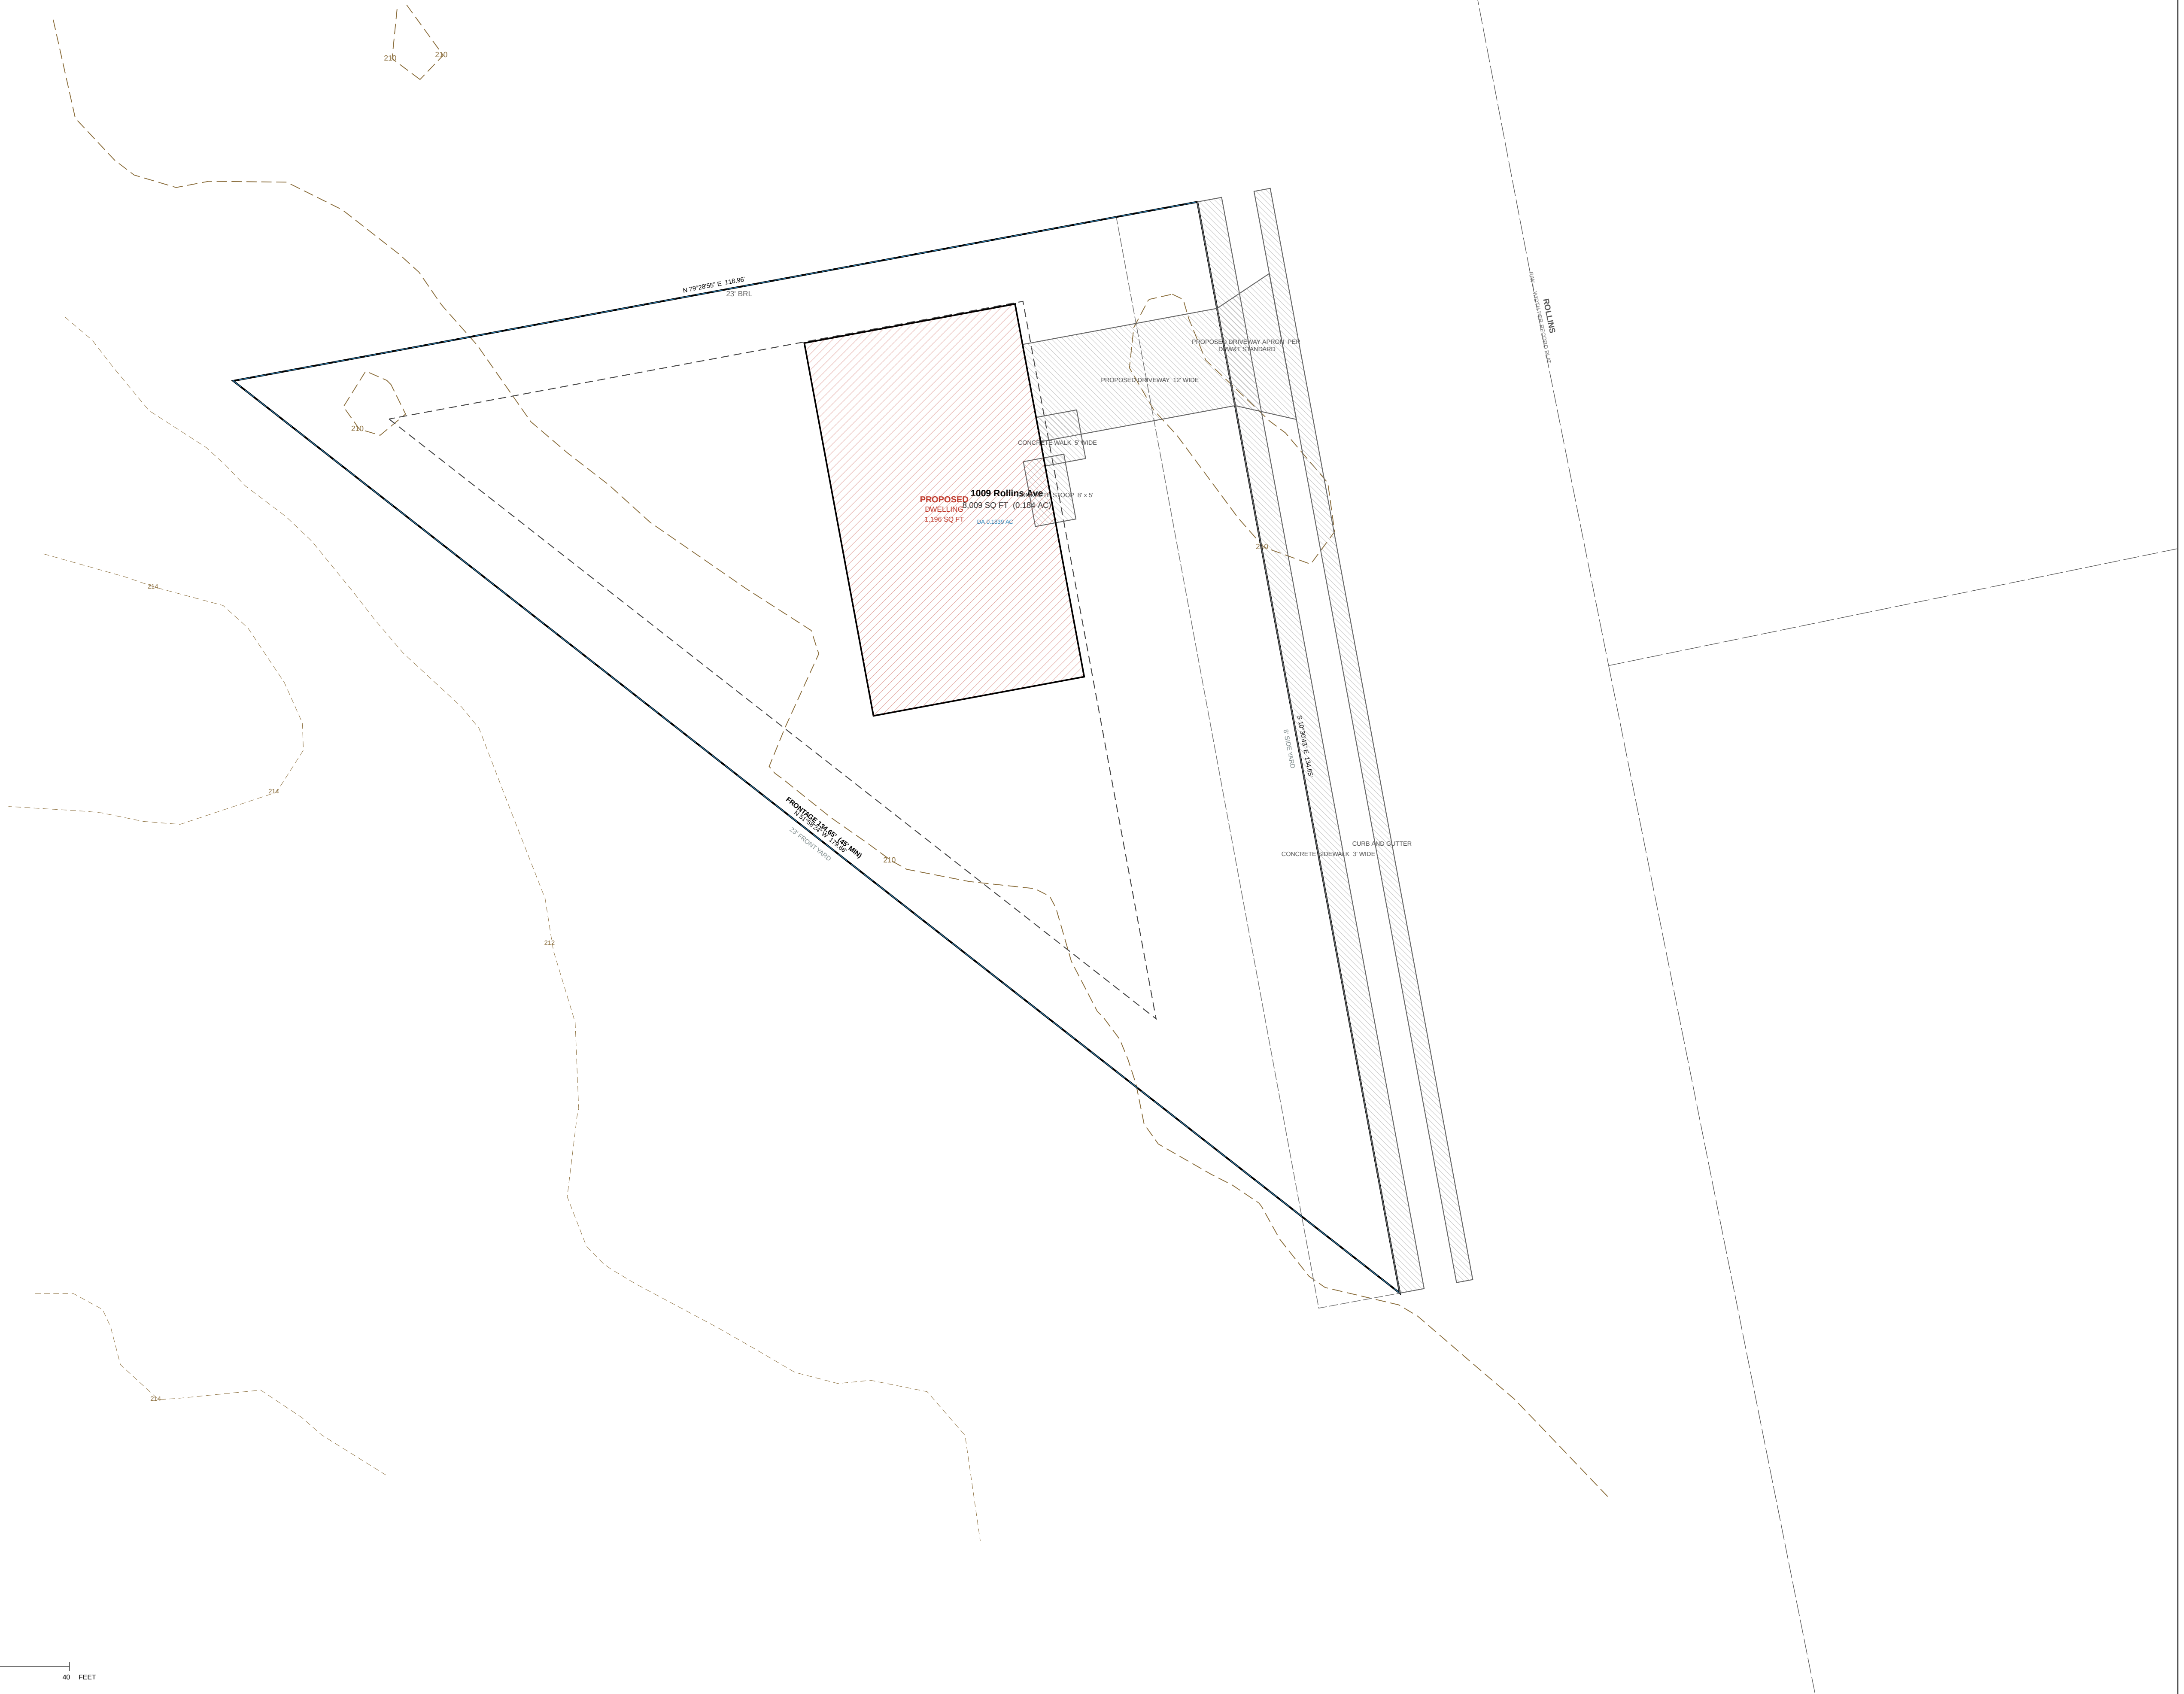



KEALEE

design, build, deliver

PROJECT

1009 Rollins Ave

ADDRESS

1009 Rollins Ave

JURISDICTION

prince georges md

ZONE

RSF-65

SHEET

C-500 — Utility Plan

SCALE

1" = 10'

STATUS

PRELIMINARY

SHEET NO.

6 OF 11

COORDINATES

EPSG:2248

H: NAD83

V: NAVD83 (feet)

| SITE DATA          |                  |          |
|--------------------|------------------|----------|
| ZONE               | RSF-65           |          |
| TAX / PARCEL ID    | 1009 Rollins Ave |          |
| GROSS LOT AREA     | 8,009 SF         | 0.184 AC |
| LOT FRONTAGE       | 45' MIN          | 134.65'  |
| SETBACKS           | REQUIRED         | PROVIDED |
| FRONT YARD         | 23'              | 23'      |
| SIDE YARD          | 8'               | 8'       |
| REAR YARD          | 20'              | 20'      |
| COVERAGE           | MAX              | PROPOSED |
| LOT COVERAGE       | 35%              | 14.9%    |
| BUILDING FOOTPRINT | —                | 1,196 SF |
| DATUM              |                  |          |
| HORIZONTAL         | EPSG:2248        |          |
| VERTICAL           | NAVD83 (feet)    |          |

| SITE ANALYSIS           |                 |
|-------------------------|-----------------|
| 1. Gross tract area     | 8,009 SF        |
| 2. Area of dwelling     | 1,196 SF        |
| 3. Wooded area          | NOT ESTABLISHED |
| 4. Floodplain area      | NOT ESTABLISHED |
| 5. Net tract area       | 8,009 SF        |
| 6. TOTAL AREA DISTURBED | NOT QUANTIFIED  |

| SEQUENCE OF CONSTRUCTION                                                     |           |
|------------------------------------------------------------------------------|-----------|
| 1. Pre-construction meeting                                                  | 1 DAY     |
| 2. Obtain necessary permits                                                  | 2 DAYS    |
| 3. Notify Miss Utility at 811 at least 48 hours prior to any excavation      | 1 DAY     |
| 4. Construct stabilized construction entrance and perimeter sediment control | 2 DAYS    |
| 5. Rough grade, construct dwelling, utilities and driveway                   | 12 MONTHS |
| 6. Fine grade and stabilize all disturbed areas                              | 1 DAY     |
| 7. Remove sediment control devices when written permission has been granted  | 1 DAY     |
| TOTAL ESTIMATED TIME OF CONSTRUCTION: 12 MONTHS                              |           |

| GENERAL NOTES                                                                                  |  |
|------------------------------------------------------------------------------------------------|--|
| 1. CONTRACTOR SHALL CONTACT MISS UTILITY AT 811 A MINIMUM OF 48 HOURS PRIOR TO ANY EXCAVATION. |  |
| 2. ALL EXISTING AND PROPOSED UTILITIES SHOWN PER PGC CODE SEC. 32.106.                         |  |
| 3. PROPOSED GRADE SHOWN SOLID; EXISTING GRADE SHOWN DASHED.                                    |  |
| 4. ROUGH EARTHWORK GRADES AND UTILITY ELEVATIONS SHOWN TO TENTHS OF A FOOT.                    |  |
| 5. BOUNDARY SHOWN IS COMPILED JURISDICTION GIS, NOT A BOUNDARY SURVEY.                         |  |

| PLAT OF RECORD   |  |
|---|--|
| Porter Subdivision, Plat Book PM 231 p.50                                                                                      |  |
| NOTES OF RECORD   |  |
| 1. BASIS OF RECORDING: Maryland State Plane Coordinate System (NAD 83).                                                        |  |
| 2. BOUNDARY OF RECORD transcribed from the recorded plat; traverse closes 1.60708, 8009 SF computed against 8,009 SF recorded. |  |
| 3. A transcription is not a field survey. Monumentation is not verified here.                                                  |  |

The surveyor certifies, under declaration and approval signatures of the recorded plat are NOT reproduced here; they appear in the monumentation set to this platting.

| LEGEND    |                                                |
|-----------|------------------------------------------------|
| -----     | PROPERTY BOUNDARY                              |
| ----- BRL | BRL — BUILDING RESTRICTION LINE                |
| -----     | PROPOSED STRUCTURE                             |
| -----     | EXISTING CONTOUR — PGATLAS 2 FT (2023), NAVD83 |
| -----     | STREET CENTRELINE                              |
| -----     | PROPOSED PAVEMENT — DRIVEWAY / WALK            |
| -----     | EASEMENT                                       |

PRINCE GEORGE'S COUNTY SOIL CONSERVATION DISTRICT APPROVAL

SEDIMENT CONTROL, GRADING, SOILS & DRAINAGE


|           |      |
|-----------|------|
| SIGNATURE | DATE |
|-----------|------|

DPE SITEROAD PLAN REVIEW DIVISION APPROVAL

|           |      |
|-----------|------|
| SIGNATURE | DATE |
|-----------|------|

REVISIONS

— NONE —

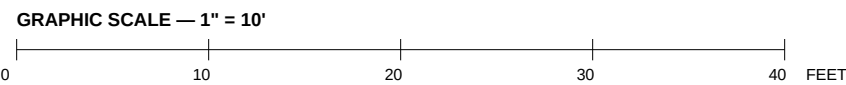



KEALEE

design, build, deliver

PROJECT  
1009 Rollins Ave  
ADDRESS  
1009 Rollins Ave  
JURISDICTION  
prince georges md  
ZONE  
RSF-65  
SHEET  
C-600 — Stormwater Management Plan  
SCALE  
1" = 10'  
STATUS  
PRELIMINARY  
SHEET NO.  
7 OF 11  
COORDINATES  
EPSG:2248  
H: NAD83  
V: NAVD83 (feet)

| SITE DATA          |                  |          |
|--------------------|------------------|----------|
| ZONE               | RSF-65           |          |
| TAX / PARCEL ID    | 1009 Rollins Ave |          |
| GROSS LOT AREA     | 8,009 SF         | 0.184 AC |
| LOT FRONTAGE       | 45' MIN          | 134.65'  |
| SETBACKS           | REQUIRED         | PROVIDED |
| FRONT YARD         | 23'              | 23'      |
| SIDE YARD          | 8'               | 8'       |
| REAR YARD          | 20'              | 20'      |
| COVERAGE           | MAX              | PROPOSED |
| LOT COVERAGE       | 35%              | 14.9%    |
| BUILDING FOOTPRINT | —                | 1,196 SF |
| DATUM              |                  |          |
| HORIZONTAL         | EPSG:2248        |          |
| VERTICAL           | NAVD83 (feet)    |          |

| SITE ANALYSIS           |                 |
|-------------------------|-----------------|
| 1. Gross tract area     | 8,009 SF        |
| 2. Area of dwelling     | 1,196 SF        |
| 3. Wooded area          | NOT ESTABLISHED |
| 4. Floodplain area      | NOT ESTABLISHED |
| 5. Net tract area       | 8,009 SF        |
| 6. TOTAL AREA DISTURBED | NOT QUANTIFIED  |

| SEQUENCE OF CONSTRUCTION                                                     |           |
|------------------------------------------------------------------------------|-----------|
| 1. Pre-construction meeting                                                  | 1 DAY     |
| 2. Obtain necessary permits                                                  | 2 DAYS    |
| 3. Notify Miss Utility at 811 at least 48 hours prior to any excavation      | 1 DAY     |
| 4. Construct stabilized construction entrance and perimeter sediment control | 2 DAYS    |
| 5. Rough grade, construct dwelling, utilities and driveway                   | 12 MONTHS |
| 6. Fine grade and stabilize all disturbed areas                              | 1 DAY     |
| 7. Remove sediment control devices when written permission has been granted  | 1 DAY     |
| TOTAL ESTIMATED TIME OF CONSTRUCTION: 12 MONTHS                              |           |

- GENERAL NOTES**
- CONTRACTOR SHALL CONTACT MISS UTILITY AT 811 A MINIMUM OF 48 HOURS PRIOR TO ANY EXCAVATION.
  - ALL EXISTING AND PROPOSED UTILITIES SHOWN PER PGC CODE SEC. 32.106.
  - PROPOSED GRADE SHOWN SOLID; EXISTING GRADE SHOWN DASHED.
  - ROUGH EARTHWORK GRADES AND UTILITY ELEVATIONS SHOWN TO TENTHS OF A FOOT.
  - BOUNDARY SHOWN IS COMPILED JURISDICTION GIS, NOT A BOUNDARY SURVEY.

- PLAT OF RECORD**  
Paper Subdivision, Plat Book PM 231 p.50
- NOTES OF RECORD**
- BASES OF RECORD: Maryland State Plane Coordinate System (NAD 83).
  - BOUNDARY OF RECORD transcribed from the recorded plat; traverse closes 1.60708, 8009 SF computed against 8,009 SF recorded.
  - A transcription is not a field survey. Monumentation is not verified here.

The surveyor certifies, under declaration and approval signatures of the recorded plat are NOT reproduced here; they appear in the monumentation set to this platting.

- LEGEND**
- PROPERTY BOUNDARY
  - BRL — BUILDING RESTRICTION LINE
  - PROPOSED STRUCTURE
  - EXISTING CONTOUR — PGATLAS 2 FT (2023), NAVD83
  - STREET CENTRELINE
  - PROPOSED PAVEMENT — DRIVEWAY / WALK
  - EASEMENT

PRINCE GEORGE'S COUNTY SOIL CONSERVATION DISTRICT APPROVAL


SEDIMENT CONTROL, GRADING, SOILS & DRAINAGE

SIGNATURE DATE

DPE SITEROAD PLAN REVIEW DIVISION APPROVAL

SIGNATURE DATE

REVISIONS  
— NONE —

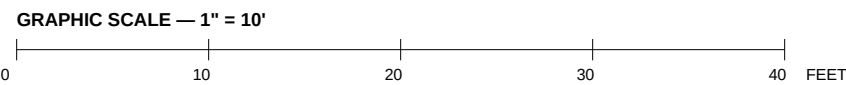



KEALEE

design, build, deliver

PROJECT  
1009 Rollins Ave  
ADDRESS  
1009 Rollins Ave  
JURISDICTION  
prince georges md  
ZONE  
RSF-65  
SHEET  
C-700 — Sediment and Erosion Control Plan  
SCALE  
1" = 10'  
STATUS  
PRELIMINARY  
SHEET NO.  
8 OF 11  
COORDINATES  
EPSG:2248  
H: NAD83  
V: NAVD83 (feet)

| SITE DATA          |                  |          |
|--------------------|------------------|----------|
| ZONE               | RSF-65           |          |
| TAX / PARCEL ID    | 1009 Rollins Ave |          |
| GROSS LOT AREA     | 8,009 SF         | 0.184 AC |
| LOT FRONTAGE       | 45' MIN          | 134.65'  |
| SETBACKS           | REQUIRED         | PROVIDED |
| FRONT YARD         | 23'              | 23'      |
| SIDE YARD          | 8'               | 8'       |
| REAR YARD          | 20'              | 20'      |
| COVERAGE           | MAX              | PROPOSED |
| LOT COVERAGE       | 35%              | 14.9%    |
| BUILDING FOOTPRINT | —                | 1,196 SF |
| DATUM              |                  |          |
| HORIZONTAL         | EPSG:2248        | NAD83    |
| VERTICAL           | NAVD83 (feet)    |          |

| SITE ANALYSIS           |                 |
|-------------------------|-----------------|
| 1. Gross tract area     | 8,009 SF        |
| 2. Area of dwelling     | 1,196 SF        |
| 3. Wooded area          | NOT ESTABLISHED |
| 4. Floodplain area      | NOT ESTABLISHED |
| 5. Net tract area       | 8,009 SF        |
| 6. TOTAL AREA DISTURBED | NOT QUANTIFIED  |

| SEQUENCE OF CONSTRUCTION                                                     |           |
|------------------------------------------------------------------------------|-----------|
| 1. Pre-construction meeting                                                  | 1 DAY     |
| 2. Obtain necessary permits                                                  | 2 DAYS    |
| 3. Notify Miss UM89 at 811 at least 48 hours prior to any excavation         | 1 DAY     |
| 4. Construct stabilized construction entrance and perimeter sediment control | 2 DAYS    |
| 5. Rough grade, construct dwelling, utilities and driveway                   | 12 MONTHS |
| 6. Fine grade and stabilize all disturbed areas                              | 1 DAY     |
| 7. Remove sediment control devices when written permission has been granted  | 1 DAY     |
| TOTAL ESTIMATED TIME OF CONSTRUCTION: 12 MONTHS                              |           |

**GENERAL NOTES**

- CONTRACTOR SHALL CONTACT MISS UTILITY AT 811 A MINIMUM OF 48 HOURS PRIOR TO ANY EXCAVATION.
- ALL EXISTING AND PROPOSED UTILITIES SHOWN PER PCC CODE SEC. 22.106.
- PROPOSED GRADE: SHOWN SOLID; EXISTING GRADE: SHOWN DASHED.
- ROUGH EARTHWORK GRADES AND UTILITY ELEVATIONS SHOWN TO TENTHS OF A FOOT.
- BOUNDARY SHOWN IS COMPILED JURISDICTION GIS, NOT A BOUNDARY SURVEY.

**PLAT OF RECORD**  
Porter Subdivision, Plat Book PM 231 p.50

**NOTES OF RECORD**

- BASES OF RECORD: Maryland State Plane Coordinate System (NAD 83).
- BOUNDARY OF RECORD transcribed from the recorded plat; traverse closes 1.60708, 8009 SF computed against 8,009 SF recorded.
- A transcription is not a field survey Monumentation is not verified here.

The surveyor certifies, under declaration and approval signatures of the recorded plat are NOT reproduced here; they appear in the monumentation, not in this drawing.

| LEGEND |                                                |
|--------|------------------------------------------------|
| -----  | PROPERTY BOUNDARY                              |
| -----  | BRL — BUILDING RESTRICTION LINE                |
| -----  | PROPOSED STRUCTURE                             |
| -----  | EXISTING CONTOUR — PGATLAS 2 FT (2023), NAVD83 |
| -----  | STREET CENTRELINE                              |
| -----  | PROPOSED PAVEMENT — DRIVEWAY / WALK            |
| -----  | EASEMENT                                       |

PRINCE GEORGE'S COUNTY SOIL CONSERVATION DISTRICT APPROVAL

SEDIMENT CONTROL, GRADING, SOILS & DRAINAGE

SIGNATURE DATE

DPE SITEROAD PLAN REVIEW DIVISION APPROVAL

SIGNATURE DATE

STABILIZATION COMPLIANCE PREAMBLE

Stabilization practices on all projects must be in compliance with the requirements of COMAR 26.17.01 by January 9, 2013, regardless of when an erosion and sediment control plan was approved.

COMAR 26.17.01.02(2), Governing body of approved plans.


**STANDARD STABILIZATION NOTE**

Following initial soil disturbance or re-disturbance, permanent or temporary stabilization must be completed within: a.) Three (3) calendar days as to the surface of all perimeter dikes, swales, ditches, perimeter slopes, and all slopes steeper than 1:1 vertical (3:1 and 5:1); seven (7) calendar days as to all other disturbed or graded areas on the project site not under active grading.

2013 Maryland Standards and Specifications for Soil Erosion and Sediment Control, "Standard Stabilization Note" (adopted by COMAR 26.17.01.02A(2)).

REVISIONS

— NONE —

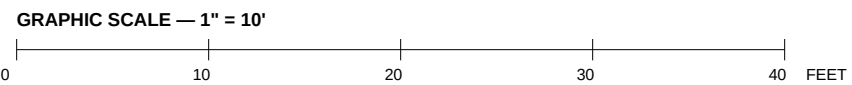



KEALEE

design, build, deliver

PROJECT  
1009 Rollins Ave  
ADDRESS  
1009 Rollins Ave  
JURISDICTION  
prince georges md  
ZONE  
RSF-65  
SHEET  
C-800 — Road, Driveway and Paving Plan  
SCALE  
1" = 10'  
STATUS  
PRELIMINARY  
SHEET NO.  
9 OF 11  
COORDINATES  
EPSG:2248  
H: NAD83  
V: NAVD83 (feet)

| SITE DATA          |                  |          |
|--------------------|------------------|----------|
| ZONE               | RSF-65           |          |
| TAX / PARCEL ID    | 1009 Rollins Ave |          |
| GROSS LOT AREA     | 8,009 SF         | 0.184 AC |
| LOT FRONTAGE       | 45' MIN          | 134.65'  |
| SETBACKS           | REQUIRED         | PROVIDED |
| FRONT YARD         | 23'              | 23'      |
| SIDE YARD          | 8'               | 8'       |
| REAR YARD          | 20'              | 20'      |
| COVERAGE           | MAX              | PROPOSED |
| LOT COVERAGE       | 35%              | 14.9%    |
| BUILDING FOOTPRINT | —                | 1,196 SF |
| DATUM              |                  |          |
| HORIZONTAL         | EPSG:2248        |          |
| VERTICAL           | NAVD83 (feet)    |          |

| SITE ANALYSIS           |                 |
|-------------------------|-----------------|
| 1. Gross tract area     | 8,009 SF        |
| 2. Area of dwelling     | 1,196 SF        |
| 3. Wooded area          | NOT ESTABLISHED |
| 4. Floodplain area      | NOT ESTABLISHED |
| 5. Net tract area       | 8,009 SF        |
| 6. TOTAL AREA DISTURBED | NOT QUANTIFIED  |

| SEQUENCE OF CONSTRUCTION                                                     |           |
|------------------------------------------------------------------------------|-----------|
| 1. Pre-construction meeting                                                  | 1 DAY     |
| 2. Obtain necessary permits                                                  | 2 DAYS    |
| 3. Notify Miss Utility at 811 at least 48 hours prior to any excavation      | 1 DAY     |
| 4. Construct stabilized construction entrance and perimeter sediment control | 2 DAYS    |
| 5. Rough grade, construct dwelling, utilities and driveway                   | 12 MONTHS |
| 6. Fine grade and stabilize all disturbed areas                              | 1 DAY     |
| 7. Remove sediment control devices when written permission has been granted  | 1 DAY     |
| TOTAL ESTIMATED TIME OF CONSTRUCTION: 12 MONTHS                              |           |

- GENERAL NOTES**
- CONTRACTOR SHALL CONTACT MISS UTILITY AT 811 A MINIMUM OF 48 HOURS PRIOR TO ANY EXCAVATION.
  - ALL EXISTING AND PROPOSED UTILITIES SHOWN PER PGC CODE SEC. 32.106.
  - PROPOSED GRADE SHOWN SOLID; EXISTING GRADE SHOWN DASHED.
  - ROUGH EARTHWORK GRADES AND UTILITY ELEVATIONS SHOWN TO TENTHS OF A FOOT.
  - BOUNDARY SHOWN IS COMPILED JURISDICTION GIS, NOT A BOUNDARY SURVEY.

- PLAT OF RECORD**  
Paper Subdivision, Plat Book PM 231 p.50
- NOTES OF RECORD**
- BASES OF RECORD: Maryland State Plane Coordinate System (NAD 83).
  - BOUNDARY OF RECORD transcribed from the recorded plat; traverse closes 1.60708, 8009 SF computed against 8,009 SF recorded.
  - A transcription is not a field survey. Monumentation is not verified here.

The surveyor certifies, under declaration and approval signatures of the recorded plat are NOT reproduced here; they appear in the monumentation set to this plan.

- LEGEND**
- PROPERTY BOUNDARY
  - BRL — BUILDING RESTRICTION LINE
  - PROPOSED STRUCTURE
  - EXISTING CONTOUR — PGATLAS 2 FT (2023), NAVD83
  - STREET CENTRELINE
  - PROPOSED PAVEMENT — DRIVEWAY / WALK
  - EASEMENT

PRINCE GEORGES COUNTY SOIL CONSERVATION DISTRICT APPROVAL

SEDIMENT CONTROL, GRADING, SOILS & DRAINAGE

SIGNATURE DATE

DPE SITE/ROAD PLAN REVIEW DIVISION APPROVAL

SIGNATURE DATE

REVISIONS  
— NONE —

GRAPHIC SCALE — 1" = 10'  
0 10 20 30 40 FEET



KEALEE

design, build, deliver

PROJECT

1009 Rollins Ave

ADDRESS

1009 Rollins Ave

JURISDICTION

prince georges md

ZONE

RSF-65

SHEET

C-900 — Civil Details

SCALE

1" = 10'

STATUS

PRELIMINARY

SHEET NO.

10 OF 11

COORDINATES

EPSG:2248

H: NAD83

V: NAVD83 (feet)

| SITE DATA          |                  |          |
|--------------------|------------------|----------|
| ZONE               | RSF-65           |          |
| TAX / PARCEL ID    | 1009 Rollins Ave |          |
| GROSS LOT AREA     | 8,009 SF         | 0.184 AC |
| LOT FRONTAGE       | 45' MIN          | 134.65'  |
| SETBACKS           | REQUIRED         | PROVIDED |
| FRONT YARD         | 23'              | 23'      |
| SIDE YARD          | 8'               | 8'       |
| REAR YARD          | 20'              | 20'      |
| COVERAGE           | MAX              | PROPOSED |
| LOT COVERAGE       | 35%              | 14.9%    |
| BUILDING FOOTPRINT | —                | 1,196 SF |
| DATUM              |                  |          |
| HORIZONTAL         | EPSG:2248        | NAD83    |
| VERTICAL           | NAVD83 (feet)    |          |

| SITE ANALYSIS           |                 |
|-------------------------|-----------------|
| 1. Gross tract area     | 8,009 SF        |
| 2. Area of dwelling     | 1,196 SF        |
| 3. Wooded area          | NOT ESTABLISHED |
| 4. Floodplain area      | NOT ESTABLISHED |
| 5. Net tract area       | 8,009 SF        |
| 6. TOTAL AREA DISTURBED | NOT QUANTIFIED  |

| SEQUENCE OF CONSTRUCTION                                                     |           |
|------------------------------------------------------------------------------|-----------|
| 1. Pre-construction meeting                                                  | 1 DAY     |
| 2. Obtain necessary permits                                                  | 2 DAYS    |
| 3. Notify Miss Utility at 811 at least 48 hours prior to any excavation      | 1 DAY     |
| 4. Construct stabilized construction entrance and perimeter sediment control | 2 DAYS    |
| 5. Rough grade, construct dwelling, utilities and driveway                   | 12 MONTHS |
| 6. Fine grade and stabilize all disturbed areas                              | 1 DAY     |
| 7. Remove sediment control devices when written permission has been granted  | 1 DAY     |
| TOTAL ESTIMATED TIME OF CONSTRUCTION: 12 MONTHS                              |           |

| GENERAL NOTES                                                                                  |  |
|------------------------------------------------------------------------------------------------|--|
| 1. CONTRACTOR SHALL CONTACT MISS UTILITY AT 811 A MINIMUM OF 48 HOURS PRIOR TO ANY EXCAVATION. |  |
| 2. ALL EXISTING AND PROPOSED UTILITIES SHOWN PER PGC CODE SEC. 32.106.                         |  |
| 3. PROPOSED GRADE SHOWN SOLID; EXISTING GRADE SHOWN DASHED.                                    |  |
| 4. ROUGH EARTHWORK GRADES AND UTILITY ELEVATIONS SHOWN TO TENTHS OF A FOOT.                    |  |
| 5. BOUNDARY SHOWN IS COMPILED JURISDICTION GIS, NOT A BOUNDARY SURVEY.                         |  |

| PLAT OF RECORD   |  |
|---|--|
| Porter Subdivision, Plat Book PM 231 p.50                                                                                      |  |
| NOTES OF RECORD   |  |
| 1. BASIS OF RECORDING: Maryland State Plane Coordinate System (NAD 83).                                                        |  |
| 2. BOUNDARY OF RECORD transcribed from the recorded plat; traverse closes 1.60708, 8009 SF computed against 8,009 SF recorded. |  |
| 3. A transcription is not a field survey. Monumentation is not verified here.                                                  |  |

The surveyor certifies, under declaration and approval signatures of the recorded plat are NOT reproduced here; they appear in the monumentation set to this platting.

| LEGEND    |                                                |
|-----------|------------------------------------------------|
| -----     | PROPERTY BOUNDARY                              |
| ----- BRL | BRL — BUILDING RESTRICTION LINE                |
| -----     | PROPOSED STRUCTURE                             |
| -----     | EXISTING CONTOUR — PGATLAS 2 FT (2023), NAVD83 |
| -----     | STREET CENTRELINE                              |
| -----     | PROPOSED PAVEMENT — DRIVEWAY / WALK            |
| -----     | EASEMENT                                       |

PRINCE GEORGES COUNTY SOIL CONSERVATION DISTRICT APPROVAL

SEDIMENT CONTROL, GRADING, SOILS & DRAINAGE


|           |      |
|-----------|------|
| SIGNATURE | DATE |
|-----------|------|

DPE SITE/ROAD PLAN REVIEW DIVISION APPROVAL

|           |      |
|-----------|------|
| SIGNATURE | DATE |
|-----------|------|

REVISIONS

— NONE —

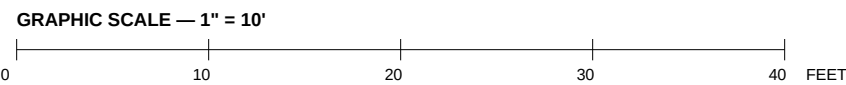



KEALEE

design, build, deliver

PROJECT  
1009 Rollins Ave  
ADDRESS  
1009 Rollins Ave  
JURISDICTION  
prince georges md  
ZONE  
RSF-65  
SHEET  
L-100 — Landscape and Tree Canopy Plan  
SCALE  
1" = 10'  
STATUS  
PRELIMINARY  
SHEET NO.  
11 OF 11  
COORDINATES  
EPSG:2248  
H: NAD83  
V: NAVD83 (feet)

| SITE DATA          |                  |          |
|--------------------|------------------|----------|
| ZONE               | RSF-65           |          |
| TAX / PARCEL ID    | 1009 Rollins Ave |          |
| GROSS LOT AREA     | 8,009 SF         | 0.184 AC |
| LOT FRONTAGE       | 45' MIN          | 134.65'  |
| SETBACKS           | REQUIRED         | PROVIDED |
| FRONT YARD         | 23'              | 23'      |
| SIDE YARD          | 8'               | 8'       |
| REAR YARD          | 20'              | 20'      |
| COVERAGE           | MAX              | PROPOSED |
| LOT COVERAGE       | 35%              | 14.9%    |
| BUILDING FOOTPRINT | —                | 1,196 SF |
| DATUM              |                  |          |
| HORIZONTAL         | EPSG:2248        |          |
| VERTICAL           | NAVD83 (feet)    |          |

| SITE ANALYSIS           |                 |
|-------------------------|-----------------|
| 1. Gross tract area     | 8,009 SF        |
| 2. Area of dwelling     | 1,196 SF        |
| 3. Wooded area          | NOT ESTABLISHED |
| 4. Floodplain area      | NOT ESTABLISHED |
| 5. Net tract area       | 8,009 SF        |
| 6. TOTAL AREA DISTURBED | NOT QUANTIFIED  |

| SEQUENCE OF CONSTRUCTION                                                     |           |
|------------------------------------------------------------------------------|-----------|
| 1. Pre-construction meeting                                                  | 1 DAY     |
| 2. Obtain necessary permits                                                  | 2 DAYS    |
| 3. Notify Miss Utility at 811 at least 48 hours prior to any excavation      | 1 DAY     |
| 4. Construct stabilized construction entrance and perimeter sediment control | 2 DAYS    |
| 5. Rough grade, construct dwelling, utilities and driveway                   | 12 MONTHS |
| 6. Fine grade and stabilize all disturbed areas                              | 1 DAY     |
| 7. Remove sediment control devices when written permission has been granted  | 1 DAY     |
| TOTAL ESTIMATED TIME OF CONSTRUCTION: 12 MONTHS                              |           |

- GENERAL NOTES
- CONTRACTOR SHALL CONTACT MISS UTILITY AT 811 A MINIMUM OF 48 HOURS PRIOR TO ANY EXCAVATION.
  - ALL EXISTING AND PROPOSED UTILITIES SHOWN PER PGC CODE SEC. 32.106.
  - PROPOSED GRADE SHOWN SOLID; EXISTING GRADE SHOWN DASHED.
  - ROUGH EARTHWORK GRADES AND UTILITY ELEVATIONS SHOWN TO TENTHS OF A FOOT.
  - BOUNDARY SHOWN IS COMPILED JURISDICTION GIS, NOT A BOUNDARY SURVEY.

- PLAT OF RECORD
- Plat Book PM 231 p.50
- NOTES OF RECORD
- BASES OF RECORD: Maryland State Plane Coordinate System (NAD 83).
  - BOUNDARY OF RECORD transcribed from the recorded plat; traverse closes 1.60708, 8009 SF computed against 8,009 SF recorded.
  - A transcription is not a field survey. Monumentation is not verified here.

The surveyor certifies, under declaration and approval signatures of the recorded plat are NOT reproduced here; they appear in the monumentation set to this plan.

- LEGEND
- PROPERTY BOUNDARY
  - BRL — BUILDING RESTRICTION LINE
  - PROPOSED STRUCTURE
  - EXISTING CONTOUR — PGATLAS 2 FT (2023), NAVD83
  - STREET CENTRELINE
  - PROPOSED PAVEMENT — DRIVEWAY / WALK
  - EASEMENT

PRINCE GEORGES COUNTY SOIL CONSERVATION DISTRICT APPROVAL

SEDIMENT CONTROL, GRADING, SOILS & DRAINAGE


SIGNATURE DATE

DPE SITE/ROAD PLAN REVIEW DIVISION APPROVAL

SIGNATURE DATE

REVISIONS

— NONE —

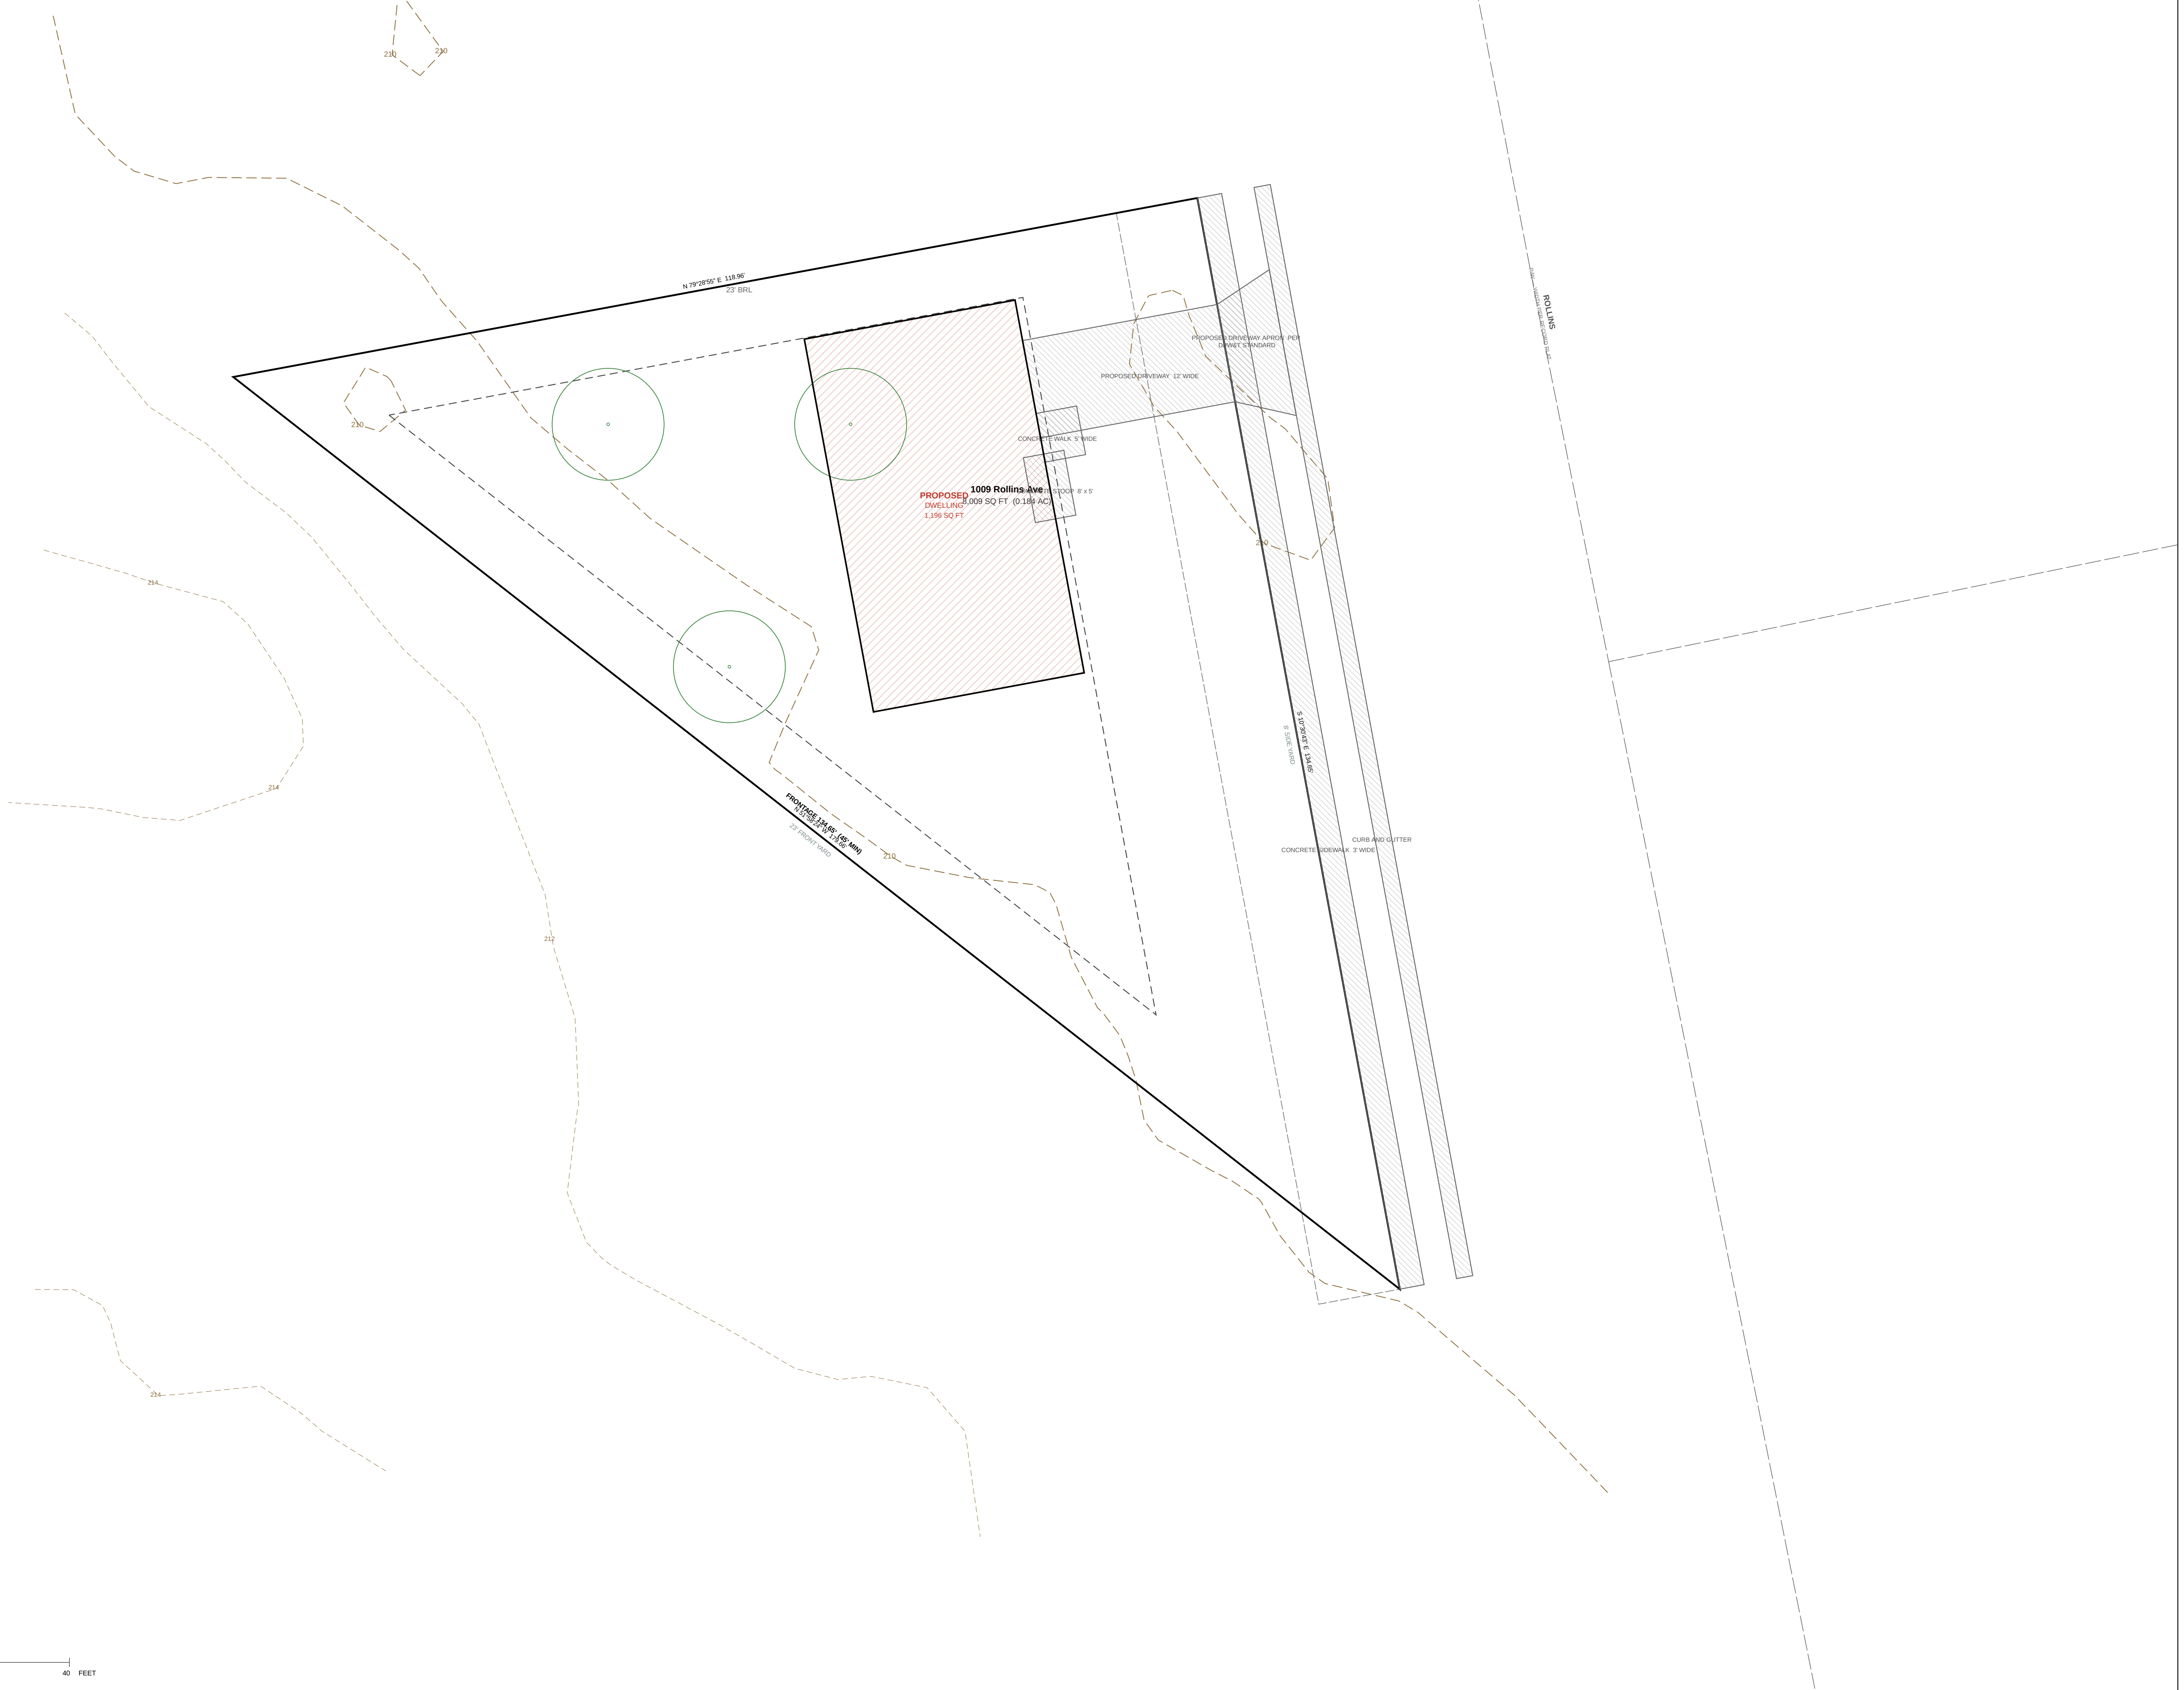

GRAPHIC SCALE — 1" = 10'

0 10 20 30 40 FEET