

KEALEE

design, build, deliver

PROJECT
1005 Rollins Ave
ADDRESS
1005 Rollins Ave
JURISDICTION
prince georges md
ZONE
RSF-65

SHEET
C-100 — Existing Conditions and Boundary Plan

SCALE
1" = 20'

STATUS
PRELIMINARY

SHEET NO.
1 OF 5

COORDINATES
EPSG:2248

H: NAD83
V: NAVD83 (feet)

PROFESSIONAL RESPONSIBILITY
Maryland Licensed Surveyor

certifies: boundary_determination, topographic_survey

SEAL AND SIGNATURE

All content on this sheet falls within one professional scope.

SITE DATA		
ZONE	RSF-65	
TAX / PARCEL ID	34854	
GROSS LOT AREA	9,596 SF	0.220 AC
LOT FRONTAGE	45' MIN	65.07'
SETBACKS	REQUIRED	PROVIDED
FRONT YARD	25'	25'
SIDE YARD	8'	8'
REAR YARD	20'	20'
COVERAGE	MAX	PROPOSED
LOT COVERAGE	35%	17.1%
BUILDING FOOTPRINT	—	1,640 SF
DATUM		
HORIZONTAL	EPSG:2248	NAD83
VERTICAL	NAVD83 (feet)	

SITE ANALYSIS	
1. Gross tract area	9,596 SF
2. Area of dwelling	1,640 SF
3. Wooded area	NOT ESTABLISHED
4. Floodplain area	NOT ESTABLISHED
5. Net tract area	9,596 SF
6. TOTAL AREA DISTURBED	NOT QUANTIFIED

SEQUENCE OF CONSTRUCTION	
1. Pre-construction meeting	1 DAY
2. Obtain necessary permits	2 DAYS
3. Notify Miss Utility at 811 at least 48 hours prior to any excavation	1 DAY
4. Construct stabilized construction entrance and perimeter sediment control	2 DAYS
5. Rough grade; construct dwelling, utilities and driveway	12 MONTHS
6. Fine grade and stabilize all disturbed areas	1 DAY
7. Remove sediment control devices when written permission has been granted	1 DAY
TOTAL ESTIMATED TIME OF CONSTRUCTION: 12 MONTHS	

GENERAL NOTES	
1. CONTRACTOR SHALL CONTACT MISS UTILITY AT 811 A MINIMUM OF 48 HOURS PRIOR TO ANY EXCAVATION.	
2. ALL EXISTING AND PROPOSED UTILITIES SHOWN PER PGC CODE SEC. 30-106.	
3. PROPOSED GRADE SHOWN SOLID. EXISTING GRADE SHOWN DASHED.	
4. ROUGH EARTHWORK GRADES AND UTILITY ELEVATIONS SHOWN TO TENTHS OF A FOOT.	
5. BOUNDARY SHOWN IS COMPILED JURISDICTION GIS, NOT A BOUNDARY SURVEY.	

PLAT OF RECORD
PORTER SUBDIVISION, LOTS 1 AND 2 — Plot Book PM 231, p. 50 (MSA, C2381, 19950), Seat Pleasant (MD) Election District, Prince Georges County, Maryland, Tax Map 73, Code R3, 2004 May 202 SE 06, Zone R-95 as recorded (RSPF-65 under the 2022 reversion), Scale 1" = 20', November 2007. M. NSPPC Record File S-20623, Proposed by Capital Development Design, Inc., Beltsville, Maryland. Basis of bearings: Maryland State Plane Coordinate System (NAD 83). Lot 1 = 9,596 sq ft (0.2203 ac). Lot 2 = 6,009 sq ft (0.138 ac). 4,215 sq ft (0.096 ac) dedicated to public use.

NOTES OF RECORD
1. Development of this property shall be in accordance with the approved Stormwater Management Control Plan 12-220-2005-05, or any approved successor thereafter.
2. Approval of this plat is based upon a reasonable expectation that public water and sewer service will be available when needed, and is conditioned on fulfilling all of the Washington Suburban Sanitary Commission authorization DA 4023 2-05 commitments.
3. The applicant, his heirs, successors and/or assignees shall utilize an existing driveway design, constructed per CPMAT standards and requirements. Separate, standard residential driveway aprons shall be provided along Edison Avenue, if deemed appropriate by DPWS, upon the issuance of street construction permits.
PUE — Public Utility Easement I/PF — Iron Pipe Found For Public Water and Sewer Only
The surveyor certifies: owner dedication and approved signatures of the recorded plat are NOT reproduced here; they appear in the instrument, not in this drawing.

LEGEND	
-----	PROPERTY BOUNDARY
- - - - -	BRL — BUILDING RESTRICTION LINE
-----	PROPOSED STRUCTURE
-----	EXISTING CONTOUR — PGATLAS 2 FT (2023), NAVD83
-----	STREET CENTRELINE
-----	PROPOSED PAVEMENT — DRIVEWAY / WALK
-----	EASEMENT

PRINCE GEORGE'S COUNTY SOIL CONSERVATION DISTRICT APPROVAL

SIGNATURE	DATE
-----------	------

DPE SITE/ROAD PLAN REVIEW DIVISION APPROVAL

SIGNATURE	DATE
-----------	------

REVISIONS

— NONE —

SOILS TABLE USDA NRCS SO-BRO — required by POC Code Sec. 30-130(a)(13)

MAP UNIT	MAP UNIT NAME	K-FACTOR	HYDRIC	HYD. GROUP	DRAINAGE CLASS
AaB	Adelphia silt loam, 2 to 5 percent slopes complex	37	No	C	Moderately well-drained
ACA	Adelphia-Aquasco complex, 0 to 2 percent slopes	43	No	D	Somewhat poorly drained
ACB	Adelphia-Aquasco complex, 3 to 5 percent slopes	37	No	C	Moderately well-drained
ADA	Adelphia-Harford complex, 0 to 2 percent slopes	24	No	BD	Somewhat poorly drained
AGA	Adelphia-Harford complex, 0 to 3 percent slopes	37	No	C	Moderately well-drained
AaB	Adelphia-Harford complex, 2 to 5 percent slopes	24	No	BD	Somewhat poorly drained
AaB	Adelphia-Harford complex, 2 to 5 percent slopes	37	No	C	Moderately well-drained
AaC	Adelphia-Harford complex, 5 to 10 percent slopes	24	No	BD	Somewhat poorly drained

SOURCE AND ACCURACY
Parcel boundary — Jurisdiction gis — Prince Georges County / M-AC/PPC — PGAtlas Property — level 1
Existing contours — Prince Georges County / M-NC/PPC — PGAtlas — level 1
Contours: PGAtlas Elevation/MapServer1 — Contour = 2' (2023), 2 ft interval, NAVD83 (feet)

GRAPHIC SCALE — 1" = 20'

0 20 40 60 80 FEET

KEALEE

design, build, deliver

PROJECT
1005 Rollins Ave
ADDRESS
1005 Rollins Ave
JURISDICTION
prince georges md
ZONE
RSF-65

SHEET
C-200 — Overall Site and Zoning Plan

SCALE
1" = 20'

STATUS
PRELIMINARY

SHEET NO.
2 OF 5

COORDINATES
EPSG:2248

H: NAD83

V: NAVD83 (feet)

PROFESSIONAL RESPONSIBILITY

Maryland Professional Engineer

certifies: sng_signed

SEAL AND SIGNATURE

Architect

certifies: architectural_footprint

SEAL AND SIGNATURE

This sheet carries content from more than one professional discipline. Each seal below applies only to the subjects listed beside it. No professional certifies content outside their stated scope, and the sheet is not divided into separate drawings for that purpose.

SITE DATA		
ZONE	RSF-65	
TAX / PARCEL ID	348854	
GROSS LOT AREA	9,596 SF	0.220 AC
LOT FRONTAGE	45 MIN	65.07
SETBACKS	REQUIRED	PROVIDED
FRONT YARD	25	25
SIDE YARD	8'	8'
REAR YARD	20'	20'
COVERAGE	MAX	PROPOSED
LOT COVERAGE	35%	17.1%
BUILDING FOOTPRINT	—	1,640 SF
DATUM		
HORIZONTAL	EPSG:2248	NAD83
VERTICAL	NAVD83 (feet)	

SITE ANALYSIS		
1. Gross lot area		9,596 SF
2. Area of dwelling		1,640 SF
3. Wooded area		NOT ESTABLISHED
4. Floodplain area		NOT ESTABLISHED
5. Net tract area		9,596 SF
6. TOTAL AREA DISTURBED		NOT QUANTIFIED

SEQUENCE OF CONSTRUCTION		
1. Pre-construction meeting		1 DAY
2. Obtain necessary permits		2 DAYS
3. Notify Mass Utility at B11 at least 48 hours prior to any excavation		1 DAY
4. Construct stabilized construction entrance and perimeter sediment control		2 DAYS
5. Rough grade, construct dwelling, utilities and driveway		12 MONTHS
6. Fine grade and establish all disturbed areas		1 DAY
7. Remove sediment control devices when written permission has been granted		1 DAY
TOTAL ESTIMATED TIME OF CONSTRUCTION: 12 MONTHS		

GENERAL NOTES

- CONTRACTOR SHALL CONTACT MSS UTILITY AT B11 A MINIMUM OF 48 HOURS PRIOR TO ANY EXCAVATION.
- ALL EXISTING AND PROPOSED UTILITIES SHOWN PER PGC CODE SEC. 30.106.
- PROPOSED GRADE SHOWN SOLID; EXISTING GRADE SHOWN DASHED.
- ROUGH EARTHWORK, GRADES AND UTILITY ELEVATIONS SHOWN TO TENTHS OF A FOOT.
- BOUNDARY SHOWN IS COMPILED JURISDICTION GIS, NOT A BOUNDARY SURVEY.

PLAT OF RECORD

PORTER SUBDIVISION, LOTS 1 AND 2 — Plat Book PM 211, p. 50 (MSA, C2381, 19550), State Preceptor (LBM) Election District, Prince George's County, Maryland, Tax Map T3, GSR RS, 200 May 202 SE 86, Zone R-55 as recorded (RSF-65 under the 2022 rewrite), Scale 1" = 20', November 2007 M. NSPC: Record File S-05121. Prepared by Capital Development Design, Inc., Bethesda, Maryland. Basis of bearings: Maryland State Plane Coordinate System (NAD 83), Lot 1 = 9,596 sq ft (0.2203 ac), Lot 2 = 8,008 sq ft (0.1838 ac), 4,734 sq ft (0.10860 ac) dedicated to public use.

NOTES OF RECORD

- Development of this property shall be in accordance with the approved Stormwater Management Concept Plan 41250-2008-00, or any approved revisions thereto.
- Approval of this plat is based upon a reasonable representation that public water and sewer service will be available when needed, and is conditioned on fulfilling all of the Washington Suburban Sanitary Commission authorization on 404.2 (2) (b) commitments.
- The applicant, his heirs, successors and or assigns shall utilize an existing driveway design, constructed per DPWET standards and requirements. Separate, standard residential driveway approvals shall be provided along Rollins Avenue, if deemed appropriate by DPWAST upon the issuance of street construction permits.

PUE — Public Utility Easement IPF — Iron Pipe Found For Public Water and Sewer Only

The surveyor certifies, under declaration and approval signatures of the recorded plat and NOT reproduced here, they shall be the true and correct copy of the plat.

LEGEND

- PROPERTY BOUNDARY
- BRL — BUILDING RESTRICTION LINE
- PROPOSED STRUCTURE
- EXISTING CONTOUR — PGATLAS 2 FT (2023), NAVD83
- STREET CENTRELINE
- PROPOSED PAVEMENT — DRIVEWAY / WALK
- EASEMENT

PRINCE GEORGE'S COUNTY SOIL CONSERVATION DISTRICT APPROVAL

SEDIMENT CONTROL, CRACKING, SOILS & DRAINAGE

SIGNATURE DATE

DPE STEREOAD PLAN REVIEW DIVISION APPROVAL

SIGNATURE DATE

REVISIONS

— NONE —

SOILS TABLE

USDA NRCS SOILS — required by POC Code Sec. 30-130(a)(13)

MAP UNIT	MAP UNIT NAME	K-FACTOR	HYDRIC	HYD. GROUP	DRAINAGE CLASS
A8B	Adelphi silt loam, 2 to 5 percent slopes complex	37	No	C	Moderately well-drained
ACA	Adelphi Aquasol complex, 0 to 2 percent slopes	43	No	D	Somewhat poorly drained
ACA	Adelphi Aquasol complex, 2 to 5 percent slopes	37	No	C	Moderately well-drained
ADA	Adelphi Aquasol complex, 0 to 2 percent slopes	24	No	BD	Somewhat poorly drained
ADA	Adelphi Aquasol complex, 0 to 2 percent slopes	37	No	C	Moderately well-drained
A8B	Adelphi Aquasol complex, 2 to 5 percent slopes	24	No	BD	Somewhat poorly drained
A8B	Adelphi Aquasol complex, 2 to 5 percent slopes	37	No	C	Moderately well-drained
A8C	Adelphi Aquasol complex, 5 to 10 percent slopes	24	No	BD	Somewhat poorly drained

SOURCE AND ACCURACY
Parcel boundary — Jurisdiction gis — Prince George's County / M-ACR/C — PGAtlas Property — level 1
Existing contours — Prince George's County / M-NCR/C — PGAtlas — level 1
Contours: PGAtlas Elevation/MapServer1 — Contour = 2 ft (2023), 2 ft interval, NAVD83 (feet)

GRAPHIC SCALE — 1" = 20'

0 20 40 60 80 FEET

KEALEE

design, build, deliver

PROJECT

1005 Rollins Ave

ADDRESS

1005 Rollins Ave

JURISDICTION

prince georges md

ZONE

RSF-65

SHEET

C-500 — Utility Plan

SCALE

1" = 20'

STATUS

PRELIMINARY

SHEET NO.

4 OF 5

COORDINATES

EPSG:2248

H: NAD83

V: NAVD83 (feet)

PROFESSIONAL RESPONSIBILITY

Maryland Professional Engineer

certified utility design

SEAL AND SIGNATURE

All content on this sheet falls within one professional scope.

SITE DATA

ZONE	RSF-65
TAX / PARCEL ID	34854
GROSS LOT AREA	9,596 SF 0.220 AC
LOT FRONTAGE	45' MIN 65.07'
SETBACKS	REQUIRED PROVIDED
FRONT YARD	25' 25'
SIDE YARD	8' 8'
REAR YARD	20' 20'
COVERAGE	MAX PROPOSED
LOT COVERAGE	35% 17.1%
BUILDING FOOTPRINT	— 1,640 SF
DATUM	
HORIZONTAL	EPSG:2248 NAD83
VERTICAL	NAVD83 (feet)

SITE ANALYSIS

1. Gross tract area	9,596 SF
2. Area of dwelling	1,640 SF
3. Wooded area	NOT ESTABLISHED
4. Floodplain area	NOT ESTABLISHED
5. Net tract area	9,596 SF
6. TOTAL AREA DISTURBED	NOT QUANTIFIED

SEQUENCE OF CONSTRUCTION

1. Pre-construction meeting	1 DAY
2. Obtain necessary permits	2 DAYS
3. Notify Miss Utility at 811 at least 48 hours prior to any excavation	1 DAY
4. Construct stabilized construction entrance and perimeter sediment control	2 DAYS
5. Rough grade, construct dwelling, utilities and driveway	12 MONTHS
6. Fine grade and stabilize all disturbed areas	1 DAY
7. Remove sediment control devices when written permission has been granted	1 DAY
TOTAL ESTIMATED TIME OF CONSTRUCTION:	12 MONTHS

GENERAL NOTES

- CONTRACTOR SHALL CONTACT MISS UTILITY AT 811 A MINIMUM OF 48 HOURS PRIOR TO ANY EXCAVATION.
- ALL EXISTING AND PROPOSED UTILITIES SHOWN PER PGC CODE SEC. 30-106.
- PROPOSED GRADE SHOWN SOLID. EXISTING GRADE SHOWN DASHED.
- ROUGH EARTHWORK GRADES AND UTILITY ELEVATIONS SHOWN TO TENTHS OF A FOOT.
- BOUNDARY SHOWN IS COMPILED JURISDICTION GIS, NOT A BOUNDARY SURVEY.

PLAT OF RECORD

PORTER SUBDIVISION, LOTS 1 AND 2 — Plot Book PM 231, p. 50 (MSA, C2381, 19950), Seat Pleasant (MD) Election District, Prince George's County, Maryland, 7th Map 75, G16 R3, 2008 May 202 SE 06, Zone R-95 as recorded (RSF-65 under the 2022 reversion), Scale 1" = 20', November 2007. M. NSPPC Record File S-08123, Proposed by Capital Development Design, Inc., Beltsville, Maryland. Basis of bearings: Maryland State Plane Coordinate System (NAD 83). Lot 1 = 9,596 sq ft (0.2203 ac). Lot 2 = 6,009 sq ft (0.138 ac). 4,215 sq ft (0.0969 ac) dedicated to public use.

NOTES OF RECORD

- Development of this property shall be in accordance with the approved Stormwater Management Concept Plan 12-200-200-00, or any approved revision thereto.
- Approval of this plat is based upon a reasonable expectation that public water and sewer service will be available when needed, and is conditioned on fulfillment of the Washington Suburban Sanitary Commission authorization DA-4023-2-06 commitments.
- The applicant, his heirs, successors and/or assignees shall utilize an existing driveway design, constructed per CPMAT standards and requirements. Separate, standard residential driveway aprons shall be provided along Edison Avenue, if deemed appropriate by DPWS, upon the issuance of street construction permits.

PUE — Public Utility Easement I/PF — Iron Pipe Found For Public Water and Sewer Only

The surveyor certifies, under declaration and approved signature of the recorded plat are NOT reproduced here; they appear in the instrument, not in this drawing.

LEGEND

- PROPERTY BOUNDARY
- BRL — BUILDING RESTRICTION LINE
- PROPOSED STRUCTURE
- EXISTING CONTOUR — PGATLAS 2 FT (2023), NAVD83
- STREET CENTRELINE
- PROPOSED PAVEMENT — DRIVEWAY / WALK
- EASEMENT

PRINCE GEORGE'S COUNTY SOIL CONSERVATION DISTRICT APPROVAL

SIGNATURE	DATE
-----------	------

DPE SITE/ROAD PLAN REVIEW DIVISION APPROVAL

SIGNATURE	DATE
-----------	------

REVISIONS


— NONE —

SOILS TABLE

MAP UNIT	MAP UNIT NAME	K-FACTOR	HYDRIC	HYD. GROUP	DRAINAGE CLASS
AaB	Adelphia silt loam, 2 to 5 percent slopes complex	37	No	C	Moderately well-drained
ACA	Adelphia-Aquasco complex, 0 to 2 percent slopes	43	No	D	Somewhat poorly drained
ACB	Adelphia-Aquasco complex, 2 to 5 percent slopes	37	No	C	Moderately well-drained
ADA	Adelphia-Hydrus complex, 0 to 2 percent slopes	24	No	BD	Somewhat poorly drained
AGA	Adelphia-Hydrus complex, 0 to 3 percent slopes	37	No	C	Moderately well-drained
AaB	Adelphia-Hydrus complex, 2 to 5 percent slopes	24	No	BD	Somewhat poorly drained
AaB	Adelphia-Hydrus complex, 2 to 5 percent slopes	37	No	C	Moderately well-drained
AaC	Adelphia-Hydrus complex, 5 to 10 percent slopes	24	No	BD	Somewhat poorly drained

SOURCE AND ACCURACY
Parcel boundary — Jurisdiction gis — Prince George's County / M-ACPPC — PGAtlas Property — level 1
Existing contours — Prince George's County / M-NCPPC — PGAtlas — level 1
Contours: PGAtlas Elevation/MapServer1 — Contour = 2 ft (2023), 2 ft interval, NAVD83 (feet)

GRAPHIC SCALE — 1" = 20'

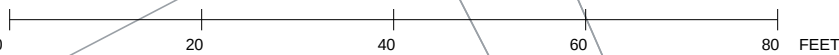

KEALEE

design, build, deliver

PROJECT

1005 Rollins Ave

ADDRESS

1005 Rollins Ave

JURISDICTION

prince georges md

ZONE

RSF-65

SHEET

L-100 — Landscape and Tree Canopy Plan

SCALE

1" = 20'

STATUS

PRELIMINARY

SHEET NO.

5 OF 5

COORDINATES

EPSG:2248

H: NAD83

V: NAVD83 (feet)

PROFESSIONAL RESPONSIBILITY

Qualified Environmental Professional

certified: tree_conservation

SEAL AND SIGNATURE

All content on this sheet falls within one professional scope.

SITE DATA

ZONE	RSF-65
TAX / PARCEL ID	34854
GROSS LOT AREA	9,596 SF 0.220 AC
LOT FRONTAGE	45' MIN 65.07'
SETBACKS	REQUIRED PROVIDED
FRONT YARD	25' 25'
SIDE YARD	8' 8'
REAR YARD	20' 20'
COVERAGE	MAX PROPOSED
LOT COVERAGE	35% 17.1%
BUILDING FOOTPRINT	— 1,640 SF
DATUM	
HORIZONTAL	EPSG:2248 NAD83
VERTICAL	NAVD83 (feet)

SITE ANALYSIS

1. Gross tract area	9,596 SF
2. Area of dwelling	1,640 SF
3. Wooded area	NOT ESTABLISHED
4. Floodplain area	NOT ESTABLISHED
5. Net tract area	9,596 SF
6. TOTAL AREA DISTURBED	NOT QUANTIFIED

SEQUENCE OF CONSTRUCTION

1. Pre-construction meeting	1 DAY
2. Obtain necessary permits	2 DAYS
3. Notify Miss Utility at 811 at least 48 hours prior to any excavation	1 DAY
4. Construct stabilized construction entrance and perimeter sediment control	2 DAYS
5. Rough grade, construct dwelling, utilities and driveway	12 MONTHS
6. Fine grade and stabilize all disturbed areas	1 DAY
7. Remove sediment control devices when written permission has been granted	1 DAY
TOTAL ESTIMATED TIME OF CONSTRUCTION:	12 MONTHS

GENERAL NOTES

- CONTRACTOR SHALL CONTACT MISS UTILITY AT 811 A MINIMUM OF 48 HOURS PRIOR TO ANY EXCAVATION.
- ALL EXISTING AND PROPOSED UTILITIES SHOWN PER PGC CODE SEC. 30-106.
- PROPOSED GRADE SHOWN SOLID. EXISTING GRADE SHOWN DASHED.
- ROUGH EARTHWORK GRADES AND UTILITY ELEVATIONS SHOWN TO TENTHS OF A FOOT.
- BOUNDARY SHOWN IS COMPILED JURISDICTION GIS, NOT A BOUNDARY SURVEY.

PLAT OF RECORD

PORTER SUBDIVISION, LOTS 1 AND 2 — Plot Book PM 231, p. 50 (MSA, C2381, 19950), Seat Pleasant (MD) Election District, Prince George's County, Maryland, Tax Map 73, Code R3, 2008 May 202 SE 06, Zone R-95 as recorded (RSPF-65 under the 2022 reweight), Scale 1" = 20', November 2007. M. NSPPC Record File S-20623, Proposed by Capital Development Design, Inc., Beltsville, Maryland. Basis of bearings: Maryland State Plane Coordinate System (NAD 83). Lot 1 = 9,596 sq ft (0.2203 ac). Lot 2 = 6,009 sq ft (0.138 ac). 4,215 sq ft (0.0966 ac) dedicated to public use.

NOTES OF RECORD

- Development of this property shall be in accordance with the approved Stormwater Management Concept Plan 12-220-200-05, or any approved successor thereafter.
- Approval of this plat is based upon a reasonable expectation that public water and sewer service will be available when needed, and is conditioned on fulfillment of the Washington Suburban Sanitary Commission authorization DA 4023 2-05 commitments.
- The applicant, his heirs, successors and/or assignees shall utilize an existing driveway design, constructed per CPMAT standards and requirements. Separate, standard residential driveway aprons shall be provided along Edison Avenue. If deemed appropriate by DPWS, upon the issuance of street construction permits.

PUE — Public Utility Easement IFF — Iron Pipe Found For Public Water and Sewer Only

The surveyor certifies: owner dedication and approved signatures of the recorded plat are NOT reproduced here; they appear in the instrument, not in this drawing.

LEGEND

- PROPERTY BOUNDARY
- BRL — BUILDING RESTRICTION LINE
- PROPOSED STRUCTURE
- EXISTING CONTOUR — PGATLAS 2 FT (2023), NAVD83
- STREET CENTRELINE
- PROPOSED PAVEMENT — DRIVEWAY / WALK
- EASEMENT

PRINCE GEORGE'S COUNTY SOIL CONSERVATION DISTRICT APPROVAL

SIGNATURE	DATE
-----------	------

DPE SITE/ROAD PLAN REVIEW DIVISION APPROVAL

SIGNATURE	DATE
-----------	------

REVISIONS

— NONE —

SOILS TABLE

MAP UNIT	MAP UNIT NAME	K-FACTOR	HYDRIC	HYD. GROUP	DRAINAGE CLASS
AaB	Adelphia silt loam, 2 to 5 percent slopes complex	37	No	C	Moderately well-drained
ACA	Adelphia-Aquasco complex, 0 to 2 percent slopes	43	No	D	Somewhat poorly drained
ACB	Adelphia-Aquasco complex, 3 to 5 percent slopes	37	No	C	Moderately well-drained
ADA	Adelphia-Harford complex, 0 to 2 percent slopes	24	No	BD	Somewhat poorly drained
ADA	Adelphia-Harford complex, 0 to 3 percent slopes	37	No	C	Moderately well-drained
AaB	Adelphia-Harford complex, 2 to 5 percent slopes	24	No	BD	Somewhat poorly drained
AaB	Adelphia-Harford complex, 2 to 5 percent slopes	37	No	C	Moderately well-drained
AaC	Adelphia-Harford complex, 5 to 10 percent slopes	24	No	BD	Somewhat poorly drained

SOURCE AND ACCURACY
Parcel boundary — Jurisdiction gis — Prince George's County / M-ACPPC — PGAtlas Property — level 1
Existing contours — Prince George's County / M-NCPPC — PGAtlas — level 1
Contours: PGAtlas Elevation/MapServer1 — Contour = 2 ft (2023), 2 ft interval, NAVD83 (feet)

GRAPHIC SCALE — 1" = 20'

