

KEALEE

design, build, deliver

PROJECT
1009 Rollins Ave
ADDRESS
1009 Rollins Ave
JURISDICTION
prince georges md
ZONE
RSF-65

SHEET

C-100 — Existing Conditions and Boundary Plan

SCALE

1" = 10'

STATUS

PRELIMINARY

SHEET NO.

1 OF 5

COORDINATES

EPSG:2248

H: NAD83

V: NAVD83 (feet)

PROFESSIONAL RESPONSIBILITY

Maryland Licensed Surveyor
certifies boundary determination, topographic survey

SEAL AND SIGNATURE

All content on this sheet falls within one professional scope.

SITE DATA			
ZONE	RSF-65		
TAX / PARCEL ID	348855		
GROSS LOT AREA	8,007 SF	0.184 AC	
LOT FRONTAGE	45' MIN	134.64'	
SETBACKS	REQUIRED	PROVIDED	
FRONT YARD	25'	25'	
SIDE YARD	8'	8'	
REAR YARD	20'	20'	
COVERAGE	MAX	PROPOSED	
LOT COVERAGE	35%	12.8%	
BUILDING FOOTPRINT	—	1,025 SF	
DATUM			
HORIZONTAL	EPSG:2248	NAD83	
VERTICAL	NAVD83 (feet)		

SITE ANALYSIS	
1. Gross tract area	8,007 SF
2. Area of dwelling	1,025 SF
3. Wooded area	NOT ESTABLISHED
4. Floodplain area	NOT ESTABLISHED
5. Net tract area	8,007 SF
6. TOTAL AREA DISTURBED	NOT QUANTIFIED

SEQUENCE OF CONSTRUCTION	
1. Pre-construction meeting	1 DAY
2. Obtain necessary permits	2 DAYS
3. Notify Miss Utility at 811 at least 48 hours prior to any excavation	1 DAY
4. Construct stabilized construction entrance and perimeter sediment control	2 DAYS
5. Rough grade, construct dwelling, utilities and driveway	12 MONTHS
6. Fine grade and stabilize all disturbed areas	1 DAY
7. Remove sediment control devices when written permission has been granted	1 DAY
TOTAL ESTIMATED TIME OF CONSTRUCTION: 12 MONTHS	

GENERAL NOTES	
1. CONTRACTOR SHALL CONTACT MISS UTILITY AT 811 A MINIMUM OF 48 HOURS PRIOR TO ANY EXCAVATION.	
2. ALL EXISTING AND PROPOSED UTILITIES SHOWN PER POC CODE SEC. 30-106.	
3. PROPOSED GRADE SHOWN SOLID. EXISTING GRADE SHOWN DASHED.	
4. ROUGH EARTHWORK GRADES AND UTILITY ELEVATIONS SHOWN TO TENTHS OF A FOOT.	
5. BOUNDARY SHOWN IS COMPILED JURISDICTION GIS, NOT A BOUNDARY SURVEY.	

PLAT OF RECORD
PORTER SUBDIVISION, LOTS 1 AND 2 — Plot Book PM 231, p. 50 (MSA, C2381, 19950), Seat Pleasant (MD) Election District, Prince George's County, Maryland. Tax Map 73, Unit R3, 2004 May 202 SE 06, Zone R-95 as recorded (RSP-45 under the 2022 reversion). Scale 1" = 20', November 2007. M. NCPSP Record File S-04213, Proposed by Capital Development Design, Inc., Beltsville, Maryland. Basis of bearings: Maryland State Plane Coordinate System (NAD 83). Lot 1 = 9,588 sq ft (0.2203 ac). Lot 2 = 8,007 sq ft (0.184 ac). 42.25 sq ft (0.0096 ac) dedicated to public use.

NOTES OF RECORD
1. Development of this property shall be in accordance with the approved Stormwater Management Control Plan 12220-250-05, or any approved revision thereto.
2. Approval of this plan is based upon a reasonable expectation that public water and sewer service will be available when needed, and is conditioned on lifting of all of the Washington Suburban Sanitary Commission authorization DA 4023 2-05 commitments.
3. The applicant, his heirs, successors and/or assignees shall utilize an abutting driveway design, constructed per CPMAT standards and requirements. Separate, standard residential driveway aprons shall be provided along Rollins Avenue. If deemed appropriate by DPWS, upon the issuance of street construction permits.
PUE — Public Utility Easement I/PF — Iron Pipe Found For Public Water and Sewer Only
The surveyor certifies, under declaration and approved signature of the recorded plat are NOT reproduced here; they appear in the instruments, not in this drawing.

LEGEND	
— — — — —	PROPERTY BOUNDARY
- - - - -	BRL — BUILDING RESTRICTION LINE
—	PROPOSED STRUCTURE
- - - - -	EXISTING CONTOUR — PGATLAS 2 FT (2023), NAVD83
—	STREET CENTRELINE
—	PROPOSED PAVEMENT — DRIVEWAY / WALK
- - - - -	EASEMENT

PRINCE GEORGE'S COUNTY SOIL CONSERVATION DISTRICT APPROVAL

SIGNATURE	DATE
-----------	------

DPE SITE/ROAD PLAN REVIEW DIVISION APPROVAL

SIGNATURE	DATE
-----------	------

REVISIONS

— NONE —

SOILS TABLE USDA NRCS SSURGO — required by POC Code Sec. 30-130(a)(13)

MAP UNIT	MAP UNIT NAME	K-FACTOR	HYDRIC	HYD. GROUP	DRAINAGE CLASS
AaB	Adelphia silt loam, 2 to 5 percent slopes complex	37	No	C	Moderately well drained
ACA	Adelphia-Aquasco complex, 0 to 2 percent slopes	43	No	D	Somewhat poorly drained
ACB	Adelphia-Aquasco complex, 0 to 2 percent slopes	37	No	C	Moderately well drained
ADA	Adelphia-Hairdel complex, 0 to 2 percent slopes	24	No	BD	Somewhat poorly drained
ADB	Adelphia-Hairdel complex, 0 to 2 percent slopes	37	No	C	Moderately well drained
AaB	Adelphia-Hairdel complex, 2 to 5 percent slopes	24	No	BD	Somewhat poorly drained
AaB	Adelphia-Hairdel complex, 2 to 5 percent slopes	37	No	C	Moderately well drained
AaC	Adelphia-Hairdel complex, 5 to 10 percent slopes	24	No	BD	Somewhat poorly drained


SOURCE AND ACCURACY
Parcel boundary — Jurisdiction gis — Prince George's County / M-NCPPC — PGAtlas Property — level 1
Existing contours — Prince George's County / M-NCPPC — PGAtlas — level 1
Contours: PGAtlas Elevation/MapServer1 — Contour = 2 Ft (2023), 2 ft interval, NAVD83 (feet)

GRAPHIC SCALE — 1" = 10'

0 10 20 30 40 FEET

SOILS TABLE					
USDA NRCS SSURGO — required by POC Code Sec. 30-130(a)(13)					
MAP UNIT	MAP UNIT NAME	K-FACTOR	HYDRIC	HYD. GROUP	DRAINAGE CLASS
AaB	Adelphia silt loam, 2 to 5 percent slopes complex	37	No	C	Moderately well drained
ACA	Adelphia-Aquasco complex, 0 to 2 percent slopes	43	No	D	Somewhat poorly drained
AA	Adelphia-Aquasco complex, 0 to 2 percent slopes	37	No	C	Moderately well drained
ADA	Adelphia-Hairdel complex, 0 to 2 percent slopes	24	No	BD	Somewhat poorly drained
AGA	Adelphia-Hairdel complex, 0 to 2 percent slopes	37	No	C	Moderately well drained
AB	Adelphia-Hairdel complex, 2 to 5 percent slopes	24	No	BD	Somewhat poorly drained
AB	Adelphia-Hairdel complex, 2 to 5 percent slopes	37	No	C	Moderately well drained
AC	Adelphia-Hairdel complex, 5 to 10 percent slopes	24	No	BD	Somewhat poorly drained

SOURCE AND ACCURACY
Parcel boundary — Jurisdiction gis — Prince George's County / M-ACPPC — PGAtlas Property — level 1
Existing contours — Prince George's County / M-NCPPC — PGAtlas — level 1
Contours: PGAtlas ElevationMapServer1 — Contour = 2 Ft (2023), 2 ft interval, NAVD83 (feet)

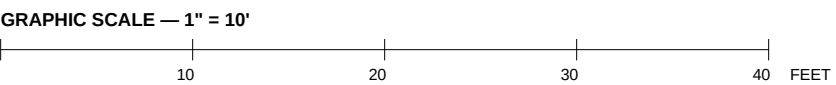

KEALEE

design, build, deliver

PROJECT
1009 Rollins Ave

ADDRESS
1009 Rollins Ave

JURISDICTION
prince georges md

ZONE
RSF-65

SHEET
C-200 — Overall Site and Zoning Plan

SCALE
1" = 10'

STATUS
PRELIMINARY

SHEET NO.
2 OF 5

COORDINATES
EPSG:2248

H: NAD83

V: NAVD83 (feet)

PROFESSIONAL RESPONSIBILITY

Maryland Professional Engineer

certificat: sig_49949

SEAL AND SIGNATURE

SEAL AND SIGNATURE

Architect

certificat: architectural_footprint

SEAL AND SIGNATURE

SEAL AND SIGNATURE

REVISIONS

— NONE —

KEALEE

design, build, deliver

PROJECT
1009 Rollins Ave

ADDRESS
1009 Rollins Ave

JURISDICTION
prince georges md

ZONE
RSF-65

SHEET
C-400 — Grading and Drainage Plan

SCALE
1" = 10'

STATUS
PRELIMINARY

SHEET NO.
3 OF 5

COORDINATES
EPSG:2248

H: NAD83

V: NAVD83 (feet)

PROFESSIONAL RESPONSIBILITY

Maryland Professional Engineer

certificat: shermawar_design

SEAL AND SIGNATURE

All content on this sheet falls within one professional scope.

SITE DATA			
ZONE	RSF-65		
TAX / PARCEL ID	348855		
GROSS LOT AREA	8,007 SF	0.184 AC	
LOT FRONTAGE	45' MIN	134.64'	
SETBACKS	REQUIRED	PROVIDED	
FRONT YARD	25'	25'	
SIDE YARD	8'	8'	
REAR YARD	20'	20'	
COVERAGE	MAX	PROPOSED	
LOT COVERAGE	35%	12.8%	
BUILDING FOOTPRINT	—	1,025 SF	
DATUM			
HORIZONTAL	EPSG:2248	NAD83	
VERTICAL	NAVD83 (feet)		

SITE ANALYSIS	
1. Gross tract area	8,007 SF
2. Area of dwelling	1,025 SF
3. Wooded area	NOT ESTABLISHED
4. Floodplain area	NOT ESTABLISHED
5. Net tract area	8,007 SF
6. TOTAL AREA DISTURBED	NOT QUANTIFIED

SEQUENCE OF CONSTRUCTION	
1. Pre construction meeting	1 DAY
2. Obtain necessary permits	2 DAYS
3. Notify Miss Utility at 811 at least 48 hours prior to any excavation	1 DAY
4. Construct stabilized construction entrance and perimeter sediment control	2 DAYS
5. Rough grade; construct dwelling, utilities and driveway	12 MONTHS
6. Fine grade and stabilize all disturbed areas	1 DAY
7. Remove sediment control devices when written permission has been granted	1 DAY
TOTAL ESTIMATED TIME OF CONSTRUCTION: 12 MONTHS	

GENERAL NOTES	
1. CONTRACTOR SHALL CONTACT MISS UTILITY AT 811 A MINIMUM OF 48 HOURS PRIOR TO ANY EXCAVATION.	
2. ALL EXISTING AND PROPOSED UTILITIES SHOWN PER POC CODE SEC. 30-106.	
3. PROPOSED GRADE SHOWN SOLID. EXISTING GRADE SHOWN DASHED.	
4. ROUGH EARTHWORK GRADES AND UTILITY ELEVATIONS SHOWN TO TENTHS OF A FOOT.	
5. BOUNDARY SHOWN IS COMPILED JURISDICTION GIS, NOT A BOUNDARY SURVEY.	

PLAT OF RECORD
PORTER SUBDIVISION, LOTS 1 AND 2 — Plot Book PM 231, p. 50 (MSA, C2381, 19950), Seat
Porter (1991) (Elevation Station: Prince Georges County, Maryland, No. 179, 17918, 2004 May 20)
SE 106, Zone R-105 at recording (RSP-45 under the 2022 event), Scale 1" = 20', November 2007, M.
NCPPC Record File S-20623, Proposed by Capital Development Design, Inc., Baltimore, Maryland, Basis
of bearings: Maryland State Plane Coordinate System (NAD 83), Lot 1 = 9,588 sq ft (0.2203 ac), Lot 2 =
8,008 sq ft (0.1838 ac), 4,215 sq ft (0.0965 ac) dedicated to public use.

NOTES OF RECORD
1. Development of this property shall be in accordance with the approved Stormwater Management
Control Plan (12/25/2020) or any approved revision thereto.
2. Approval of this plan is based upon a reasonable expectation that public water and sewer service will be
available when needed, and is conditioned on lifting of all of the Washington Suburban Sanitary Commission
authorization DA 4023 2.06 commitments.
3. The applicant, his heirs, successors and/or assignees shall utilize an abutting driveway design,
constructed per CPMAT standards and requirements. Separate, standard residential driveway systems shall
be provided along Eastern Avenue. If deemed appropriate by CPWS, upon the issuance of direct
construction permits.

PUE — Public Utility Easement IPF — Iron Pipe Fittings For Public Water and Sewer Only
The surveyor certifies, under declaration and approved signatures of the recorded plat are NOT reproduced here; they
appear in the instrument, not in this drawing.

LEGEND	
—	PROPERTY BOUNDARY
- - - -	BRL — BUILDING RESTRICTION LINE
—	PROPOSED STRUCTURE
—	EXISTING CONTOUR — PGATLAS 2 FT (2023), NAVD83
—	STREET CENTRELINE
—	PROPOSED PAVEMENT — DRIVEWAY / WALK
- - - -	EASEMENT

PRINCE GEORGE'S COUNTY SOIL CONSERVATION DISTRICT APPROVAL
SEMI-ANNUAL CERTIFICATION, CONSIDERING, SOILS, E, DRAINAGE

SIGNATURE	DATE
-----------	------

DPE SITE/ROAD PLAN REVIEW DIVISION APPROVAL

SIGNATURE	DATE
-----------	------

GRADING CERTIFICATE
I HEREBY CERTIFY THAT THIS PLAN CONFORMS TO THE REQUIREMENTS OF SUBTITLE 30,
DIVISION 2 OF THE CODE OF PRINCE GEORGE'S COUNTY WATER RESOURCES PROTECTION
AND GRADING CODE AND THAT I OR MY STAFF HAVE INSPECTED THIS SITE AND THAT
DRAINAGE FLOWS FROM UPHILL PROPERTIES ONTO THIS SITE, AND FROM THIS SITE ONTO
DOWNHILL PROPERTIES, HAVE BEEN ADDRESSED IN A SUEWATWAL ACCORDANCE WITH
APPLICABLE CODES, SIGNED, SEALED AND DATED BY A PROFESSIONAL ENGINEER
LICENSED IN THE STATE OF MARYLAND.

Prince George's County DPE, Site Rough Grading Design Review Checklist, Item A-10

STABILIZATION COMPLIANCE PREAMBLE
Stabilization practices on all projects must be in compliance with the requirements of COMAR
26.17.03, by January 9, 2013, regardless of when an erosion and sediment control plan was approved.
COMAR 26.17.03.05(2), Grandfathering of approved plans

STANDARD STABILIZATION NOTE
Following initial soil disturbance or re-disturbance, permanent or temporary stabilization must be
completed within: a) Three (3) calendar days as to the surface of all perimeter dikes, swales, ditches,
perimeter slopes, and all slopes steeper than 3 horizontal to 1 vertical (3:1), and b) Seven (7) calendar
days as to all other disturbed or graded areas on the project site not under active grading.
2011 Maryland Standards and Specifications for Soil Erosion and Sediment Control, "Standard Stabilization
Note" (adopted by COMAR 26.17.03.05A(3))

REVISIONS
— NONE —

SOILS TABLE

MAP UNIT	MAP UNIT NAME	K-FACTOR	HYDRIC	HYD. GROUP	DRAINAGE CLASS
A8B	Adelphia silt loam, 2 to 5 percent slopes complex	37	No	C	Moderately well drained
ACA	Adelphia Aquascon complex, 0 to 2 percent slopes	43	No	D	Somewhat poorly drained
ACB	Adelphia Aquascon complex, 0 to 2 percent slopes	37	No	C	Moderately well drained
ADA	Adelphia Hainsdel complex, 0 to 2 percent slopes	24	No	BD	Somewhat poorly drained
ADB	Adelphia Hainsdel complex, 0 to 2 percent slopes	37	No	C	Moderately well drained
A8B	Adelphia Hainsdel complex, 2 to 5 percent slopes	24	No	BD	Somewhat poorly drained
A8B	Adelphia Hainsdel complex, 2 to 5 percent slopes	37	No	C	Moderately well drained
A8C	Adelphia Hainsdel complex, 5 to 10 percent slopes	24	No	BD	Somewhat poorly drained

SOURCE AND ACCURACY
Parcel boundary — Jurisdiction gis — Prince George's County / M-NCPPC — PGAtlas Property — level 1
Existing contours — Prince George's County / M-NCPPC — PGAtlas — level 1
Contours: PGAtlas Elevation/MapServer1 — Contour = 2 Ft (2023), 2 ft interval, NAVD83 (feet)



KEALEE

design, build, deliver

PROJECT
1009 Rollins Ave
ADDRESS
1009 Rollins Ave
JURISDICTION
prince georges md
ZONE
RSF-65

SHEET
C-500 — Utility Plan
SCALE
1" = 10'
STATUS
PRELIMINARY
SHEET NO.
4 OF 5

COORDINATES
EPSG:2248
H: NAD83
V: NAVD83 (feet)

PROFESSIONAL RESPONSIBILITY
Maryland Professional Engineer
certificat_utilty_design

SEAL AND SIGNATURE

All content on this sheet falls within one professional scope.

SITE DATA			
ZONE	RSF-65		
TAX / PARCEL ID	348855		
GROSS LOT AREA	8,007 SF	0.184 AC	
LOT FRONTAGE	45' MIN	134.64'	
SETBACKS	REQUIRED	PROVIDED	
FRONT YARD	25'	25'	
SIDE YARD	8'	8'	
REAR YARD	20'	20'	
COVERAGE	MAX	PROPOSED	
LOT COVERAGE	35%	12.8%	
BUILDING FOOTPRINT	—	1,025 SF	
DATUM			
HORIZONTAL	EPSG:2248	NAD83	
VERTICAL	NAVD83 (feet)		

SITE ANALYSIS	
1. Gross tract area	8,007 SF
2. Area of dwelling	1,025 SF
3. Wooded area	NOT ESTABLISHED
4. Floodplain area	NOT ESTABLISHED
5. Net tract area	8,007 SF
6. TOTAL AREA DISTURBED	NOT QUANTIFIED

SEQUENCE OF CONSTRUCTION	
1. Pre-construction meeting	1 DAY
2. Obtain necessary permits	2 DAYS
3. Notify Miss Utility at 811 at least 48 hours prior to any excavation	1 DAY
4. Construct stabilized construction entrance and perimeter sediment control	2 DAYS
5. Rough grade, construct dwelling, utilities and driveway	12 MONTHS
6. Fine grade and stabilize all disturbed areas	1 DAY
7. Remove sediment control devices when written permission has been granted	1 DAY
TOTAL ESTIMATED TIME OF CONSTRUCTION: 12 MONTHS	

- GENERAL NOTES**
- CONTRACTOR SHALL CONTACT MISS UTILITY AT 811 A MINIMUM OF 48 HOURS PRIOR TO ANY EXCAVATION.
 - ALL EXISTING AND PROPOSED UTILITIES SHOWN PER POC CODE SEC. 30-106.
 - PROPOSED GRADE SHOWN SOLID. EXISTING GRADE SHOWN DASHED.
 - ROUGH EARTHWORK GRADES AND UTILITY ELEVATIONS SHOWN TO TENTHS OF A FOOT.
 - BOUNDARY SHOWN IS COMPILED JURISDICTION GIS, NOT A BOUNDARY SURVEY.

PLAT OF RECORD
PORTER SUBDIVISION, LOTS 1 AND 2 — Plot Book PM 231, p. 50 (MSA, C2381, 19950), Seat Pleasant (Belt) Election District, Prince George's County, Maryland, Tax Map 73, G16 R3, 2020 May 202 SE 06, Zone R-95 as recorded (RSP-45 under the 2022 rewrite), Scale 1" = 20', November 2007. M. NCPPC Record File S-08213, Proposed by Capital Development Design, Inc., Beltsville, Maryland. Basis of bearings: Maryland State Plane Coordinate System (NAD 83). Lot 1 = 9,588 sq ft (0.2203 ac). Lot 2 = 8,007 sq ft (0.184 ac). 4,215 sq ft (0.0965 ac) dedicated to public use.

- NOTES OF RECORD**
- Development of this property shall be in accordance with the approved Stormwater Management Control Plan (C220-2050-05, or any approved revision thereafter).
 - Approval of this plat is based upon a reasonable expectation that public water and sewer service will be available when needed, and is conditioned on fulfillment of the Washington Suburban Sanitary Commission authorization DA-4023-2-05 commitments.
 - The applicant, his heirs, successors and/or assignees shall utilize an abutting driveway design constructed per CPMAT standards and requirements. Separate, standard residential driveway aprons shall be provided along Rollins Avenue, if deemed appropriate by DPWSD, upon the issuance of street construction permits.

PUE — Public Utility Easement IPF — Iron Pipe Found For Public Water and Sewer Only
The surveyor certifies, under declaration and approved signature of the recorded plat are NOT reproduced here; they appear in the instrument, not in this drawing.

LEGEND

- PROPERTY BOUNDARY
- BRL — BUILDING RESTRICTION LINE
- PROPOSED STRUCTURE
- EXISTING CONTOUR — PGATLAS 2 FT (2023), NAVD83
- STREET CENTRELINE
- PROPOSED PAVEMENT — DRIVEWAY / WALK
- EASEMENT

PRINCE GEORGE'S COUNTY SOIL CONSERVATION DISTRICT APPROVAL

SIGNATURE DATE

DPE SITE/ROAD PLAN REVIEW DIVISION APPROVAL

SIGNATURE DATE

REVISIONS

— NONE —

SOILS TABLE

MAP UNIT	MAP UNIT NAME	K-FACTOR	HYDRIC	HYD. GROUP	DRAINAGE CLASS
AaB	Adelphia silt loam, 2 to 5 percent slopes complex	37	No	C	Moderately well drained
ACA	Adelphia-Aquasco complex, 0 to 2 percent slopes	43	No	D	Somewhat poorly drained
ACB	Adelphia-Aquasco complex, 0 to 2 percent slopes	37	No	C	Moderately well drained
ADA	Adelphia-Hairdel complex, 0 to 2 percent slopes	24	No	BD	Somewhat poorly drained
ADB	Adelphia-Hairdel complex, 0 to 2 percent slopes	37	No	C	Moderately well drained
AaB	Adelphia-Hairdel complex, 2 to 5 percent slopes	24	No	BD	Somewhat poorly drained
AaB	Adelphia-Hairdel complex, 2 to 5 percent slopes	37	No	C	Moderately well drained
AaC	Adelphia-Hairdel complex, 5 to 10 percent slopes	24	No	BD	Somewhat poorly drained

SOURCE AND ACCURACY
Parcel boundary — Jurisdiction gis — Prince George's County / M-NCPPC — PGAtlas Property — level 1
Existing contours — Prince George's County / M-NCPPC — PGAtlas — level 1
Contours: PGAtlas Elevation/MapServer1 — Contour = 2 Ft (2023), 2 ft interval, NAVD83 (feet)

GRAPHIC SCALE — 1" = 10'

0 10 20 30 40 FEET

KEALEE

design, build, deliver

PROJECT
1009 Rollins Ave
ADDRESS
1009 Rollins Ave
JURISDICTION
prince georges md
ZONE
RSF-65

SHEET

L-100 — Landscape and Tree Canopy Plan

SCALE

1" = 10'

STATUS

PRELIMINARY

SHEET NO.

5 OF 5

COORDINATES

EPSG:2248

H: NAD83

V: NAVD83 (feet)

PROFESSIONAL RESPONSIBILITY

Qualified Environmental Professional

certified tree conservation

SEAL AND SIGNATURE

All content on this sheet falls within one professional scope.

SITE DATA	
ZONE	RSF-65
TAX / PARCEL ID	348855
GROSS LOT AREA	8,007 SF 0.184 AC
LOT FRONTAGE	45' MIN 134.64'
SETBACKS	REQUIRED PROVIDED
FRONT YARD	25' 25'
SIDE YARD	8' 8'
REAR YARD	30' 30'
COVERAGE	MAX PROPOSED
LOT COVERAGE	35% 12.8%
BUILDING FOOTPRINT	— 1,025 SF
DATUM	
HORIZONTAL	EPSG:2248 NAD83
VERTICAL	NAVD83 (feet)

SITE ANALYSIS	
1. Gross tract area	8,007 SF
2. Area of dwelling	1,025 SF
3. Wooded area	NOT ESTABLISHED
4. Floodplain area	NOT ESTABLISHED
5. Net tract area	8,007 SF
6. TOTAL AREA DISTURBED	NOT QUANTIFIED

SEQUENCE OF CONSTRUCTION	
1. Pre-construction meeting	1 DAY
2. Obtain necessary permits	2 DAYS
3. Notify Miss Utility at 811 at least 48 hours prior to any excavation	1 DAY
4. Construct stabilized construction entrance and perimeter sediment control	2 DAYS
5. Rough grade, construct dwelling, utilities and driveway	12 MONTHS
6. Fine grade and stabilize all disturbed areas	1 DAY
7. Remove sediment control devices when written permission has been granted	1 DAY
TOTAL ESTIMATED TIME OF CONSTRUCTION: 12 MONTHS	

GENERAL NOTES	
1. CONTRACTOR SHALL CONTACT MISS UTILITY AT 811 A MINIMUM OF 48 HOURS PRIOR TO ANY EXCAVATION.	
2. ALL EXISTING AND PROPOSED UTILITIES SHOWN PER PGC CODE SEC. 30-106.	
3. PROPOSED GRADE SHOWN SOLID. EXISTING GRADE SHOWN DASHED.	
4. ROUGH EARTHWORK GRADES AND UTILITY ELEVATIONS SHOWN TO TENTHS OF A FOOT.	
5. BOUNDARY SHOWN IS COMPILED JURISDICTION GIS, NOT A BOUNDARY SURVEY.	

PLAT OF RECORD
PORTER SUBDIVISION, LOTS 1 AND 2 — Plat Book PM 231, p. 50 (MSA, C2381, 19950), Seat Pleasant (Belt) Election District, Prince George's County, Maryland. Tax Map 73, Unit B3, 2004 May 202 SE 06, Zone R-95 as recorded (RSP-45 under the 2022 reversion). Scale 1" = 20', November 2007. M. NCPPC Record File S-08123, Proposed by Capital Development Design, Inc., Beltsville, Maryland. Basis of bearings: Maryland State Plane Coordinate System (NAD 83). Lot 1 = 9,588 sq ft (0.2203 ac). Lot 2 = 8,007 sq ft (0.184 ac). 42.25 sq ft (0.00096 ac) dedicated to public use.

NOTES OF RECORD
1. Development of this property shall be in accordance with the approved Stormwater Management Control Plan (2220-2050-05, or any approved revision thereafter).
2. Approval of this plan is based upon a reasonable expectation that public water and sewer service will be available when needed, and is conditioned on fulfillment of the Washington Suburban Sanitary Commission authorization DA-4023-2-05 commitments.
3. The applicant, his heirs, successors and/or assignees shall utilize an abutting driveway design constructed per CPMAT standards and requirements. Separate standard residential driveway aprons shall be provided along Eastern Avenue. If deemed appropriate by DPWS, upon the issuance of street construction permits.
PUE — Public Utility Easement I/PF — Iron Pipe Found For Public Water and Sewer Only
The surveyor certifies, under declaration and approved signature of the recorded plat are NOT reproduced here; they appear in the instrument, not in this drawing.

LEGEND	
— — — — —	PROPERTY BOUNDARY
- - - - -	BRL — BUILDING RESTRICTION LINE
—	PROPOSED STRUCTURE
- - - - -	EXISTING CONTOUR — PGATLAS 2 FT (2023), NAVD83
—	STREET CENTRELINE
—	PROPOSED PAVEMENT — DRIVEWAY / WALK
- - - - -	EASEMENT

PRINCE GEORGE'S COUNTY SOIL CONSERVATION DISTRICT APPROVAL

SIGNATURE	DATE
-----------	------

DPE SITE/ROAD PLAN REVIEW DIVISION APPROVAL

SIGNATURE	DATE
-----------	------

SIGNATURE	DATE
-----------	------

REVISIONS

— NONE —

SOILS TABLE

MAP UNIT	MAP UNIT NAME	K-FACTOR	HYDRIC	HYD. GROUP	DRAINAGE CLASS
AaB	Adelphia silt loam, 2 to 5 percent slopes complex	37	No	C	Moderately well drained
ACA	Adelphia-Aquasco complex, 0 to 2 percent slopes	43	No	D	Somewhat poorly drained
ACA	Adelphia-Aquasco complex, 0 to 2 percent slopes	37	No	C	Moderately well drained
ADA	Adelphia-Hairdel complex, 0 to 2 percent slopes	24	No	BD	Somewhat poorly drained
ADA	Adelphia-Hairdel complex, 0 to 2 percent slopes	37	No	C	Moderately well drained
AaB	Adelphia-Hairdel complex, 2 to 5 percent slopes	24	No	BD	Somewhat poorly drained
AaB	Adelphia-Hairdel complex, 2 to 5 percent slopes	37	No	C	Moderately well drained
AaC	Adelphia-Hairdel complex, 5 to 10 percent slopes	24	No	BD	Somewhat poorly drained

SOURCE AND ACCURACY
Parcel boundary — Jurisdiction gis — Prince George's County / M-ACPPC — PGAtlas Property — level 1
Existing contours — Prince George's County / M-NCPPC — PGAtlas — level 1
Contours: PGAtlas Elevation/MapServer1. — Contour = 2 Ft (2023), 2 ft interval, NAVD83 (feet)

GRAPHIC SCALE — 1" = 10'

0 10 20 30 40 FEET