



PROJECT
Porter Subdivision — LOT 1 & LOT 2
ADDRESS
1005 Rollins Ave
JURISDICTION
prince georges md
ZONE
RSF-65
SHEET
C-000 — Cover Sheet, Approvals and
SCALE
1" = 20'
STATUS
PRELIMINARY
SHEET NO.
1 OF 6
COORDINATES
EPSG:2248
H: NAD83
V: NAVD88 (feet)

SITE DATA		
ZONE	RSF-65	
TAX / PARCEL ID	—	
GROSS LOT AREA	21,826 SF	0.501 AC
LOT FRONTAGE	45 MIN	65.00'
SETBACKS	REQUIRED	PROVIDED
FRONT YARD	23'	8'
SIDE YARD	8'	8'
REAR YARD	20'	20'
COVERAGE	MAX	PROPOSED
LOT COVERAGE	35%	5.5%
BUILDING FOOTPRINT	—	1,195 SF
DATUM		
HORIZONTAL	EPSG-2248	NAD83
VERTICAL	NAVD88 (feet)	

SITE ANALYSIS

- | | |
|-------------------------|-----------------|
| 1. Gross tract area | 21,826 SF |
| 2. Area of dwelling | 1,196 SF |
| 3. Wooded area | NOT ESTABLISHED |
| 4. Floodplain area | NOT ESTABLISHED |
| 5. Net tract area | 21,826 SF |
| 6. TOTAL AREA DISTURBED | NOT QUANTIFIED |

SEQUENCE OF CONSTRUCTION

- | | |
|--|-----------|
| 1. Pre-construction meeting | 1 DAY |
| 2. Obtain necessary permits | 2 DAYS |
| 3. Notify Miss Utility at 811 at least 48 hours prior to any excavation | 1 DAY |
| 4. Construct stabilized construction entrance and perimeter sediment control | 2 DAYS |
| 5. Rough grade; construct dwelling, utilities and driveway | 12 MONTHS |
| 6. Fine grade and stabilize all disturbed areas | 1 DAY |
| 7. Remove sediment control devices when written permission has been granted by the inspector | 1 DAY |
| TOTAL ESTIMATED TIME OF CONSTRUCTION: 12 MONTHS | |

GENERAL NOTES

- [illegible]

PLAT OF RECORD

PORTER SUBDIVISION, LOTS 1 AND 2 — Plat Book PM 231, p. 50 (MSA_C2381_19050). Seat Pleasant (18th) Election District, Prince George's County, Maryland. Tax Map #73, Grid B3, 200 Map 202 SE 06, Zone R-55 as recorded (R5F-65 under the 2022 rewrite). Scale 1" = 70', November 2007. M-NCPPC Record File 5-09121. Basis of bearings: Maryland State Plane Coordinate System (NAD 83). Lot 1 = 9,998 sq ft (0.2203 ac); Lot 2 = 8,006 sq ft (0.1838 ac); 4,219 sq ft (0.0969 ac) dedicated to public use.

NOTES OF RECORD

5. Development of this property shall be in accordance with the approved Stormwater Management Ordinance, 2008-2009.
6. Approval of this plat is based upon a reasonable expectation that public water and sewer service will be available when needed, and is conditioned on fulfilling all of the Washington Suburban Sanitary Commission's requirements for service.
7. The applicant, his heirs, successors and/or assignees shall utilize an abutting driveway design, constructed per DPWAT standards and requirements. Separate, standard residential driveway aprons shall be constructed per DPWAT standards, if deemed appropriate by DPWAT upon the issuance of street construction permits.
8. **ADJOINING PROPERTIES**, per the recorded plat, LOTS 13, 14 AND 15 – adjacent to Pleasant Park, Plat 10, 1997-1998, and LOTS 13, 14 AND 15 – adjacent to Pleasant Park, Plat 10, 1997-1998, are located to the southwest; OULTON A (adjacent to Pleasant Park, Plat Book W33, 1976) – northwest; JEAN M. YOUNG JR. 14377-5589 – northwest; MATTHEW W. DADGE, II 14345-6734 – across from LOTS 13, 14 AND 15 – northwest; and LOTS 13, 14 AND 15 – adjacent to Pleasant Park, Plat 10, 1997-1998, are located to the east.
9. **ADJOINING PROPERTIES**, per the recorded plat, LOTS 13, 14 AND 15 – adjacent to Pleasant Park, Plat 10, 1997-1998, are located to the southwest; OULTON A (adjacent to Pleasant Park, Plat Book W33, 1976) – northwest; JEAN M. YOUNG JR. 14377-5589 – northwest; MATTHEW W. DADGE, II 14345-6734 – across from LOTS 13, 14 AND 15 – northwest; and LOTS 13, 14 AND 15 – adjacent to Pleasant Park, Plat 10, 1997-1998, are located to the east.

The surveyor certificate, owner dedication and approval signatures of the recorded plat are NOT reproduced here; they attach to that instrument, not to this drawing.

LEGEND

- PROPERTY BOUNDARY
 - - - - - BRL — BUILDING RESTRICTION LINE
 ——— PROPOSED STRUCTURE
 ——— EXISTING CONTOUR — PGATLAS 2 FT (2023), NAVD88
 - - - - - STREET CENTRELINE
 ——— PROPOSED PAVEMENT — DRIVEWAY / WALK
 - - - - - EASEMENT


PRINCE GEORGE'S COUNTY SOIL CONSERVATION DISTRICT APPROVAL
SEDIMENT CONTROL, GRADING, SOILS & DRAINAGE

SIGNATURE _____ DATE _____

DPIE SITE/ROAD PLAN REVIEW DIVISION APPROVAL _____

SIGNATURE _____ DATE _____

REVISIONS

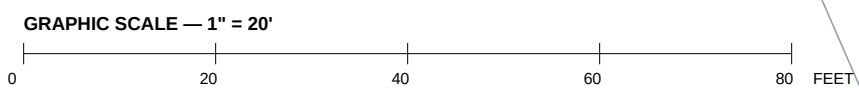



PROJECT
Porter Subdivision — LOT 1 & LOT 2
ADDRESS
1005 Rollins Ave
JURISDICTION
prince georges md
ZONE
RSF-65
SHEET
C-100 — Existing Conditions and Bo
SCALE
1" = 20'
STATUS
PRELIMINARY
SHEET NO.
2 OF 6
COORDINATES
EPSG:2248
H: NAD83
V: NAVD88 (feet)

SITE DATA		
ZONE	RSF-65	
TAX / PARCEL ID	—	
GROSS LOT AREA	21,826 SF	0.501 AC
LOT FRONTAGE	45 MIN	65.00'
SETBACKS	REQUIRED	PROVIDED
FRONT YARD	23'	8'
SIDE YARD	8'	8'
REAR YARD	20'	20'
COVERAGE	MAX	PROPOSED
LOT COVERAGE	35%	5.5%
BUILDING FOOTPRINT	—	1,196 SF
DATUM		
HORIZONTAL	EPSG-2248	NAD83
VERTICAL	NAVD88 (feet)	

SITE ANALYSIS	
1. Gross tract area	21,826 SF
2. Area of dwelling	1,196 SF
3. Wooded area	NOT ESTABLISHED
4. Floodplain area	NOT ESTABLISHED
5. Net tract area	21,826 SF
6. TOTAL AREA DISTURBED	NOT QUANTIFIED

SEQUENCE OF CONSTRUCTION	
1. Pre-construction meeting	1 DAY
2. Obtain necessary permits	2 DAYS
3. Notify Miss Utility at 811 at least 48 hours prior to any excavation	1 DAY
4. Construct stabilized construction entrance and perimeter sediment control	2 DAYS
5. Rough grade, construct driveway, utilities and driveway	12 MONTHS
6. Fine grade and stabilize at disturbed areas	1 DAY
7. Remove sediment control devices when written permission has been granted by the inspector	1 DAY
TOTAL ESTIMATED TIME OF CONSTRUCTION: 12 MONTHS	

GENERAL NOTES

[illegible]

PLAT OF RECORD

PORTER SUBDIVISION, LOTS 1 AND 2 — Plat Book PM 231, p. 50 (MSA, C2381_19050). Seat Pleasant (18th) Election District, Prince George's County, Maryland. Tax Map 73, Grid B3; 200 Map 202 SE 06, Zone R-55 at recording (RSF-65 under the 2022 rewrite). Slice 1' = 20', November 2007. M-NCPPC Record File 5-09121. Basis of bearings: Maryland State Plane Coordinate System (NAD 83). Lot 1 = 9,598 sq ft (0.2203 ac); Lot 2 = 8,008 sq ft (0.1838 ac); 4,219 sq ft (0.0969 ac) dedicated to public use.

NOTES OF RECORD

1. Development of this property shall be in accordance with the approved Stormwater Management Plan for the 2005-2010 period.
2. Approval of this plat is based upon a reasonable expectation that public water and sewer service will be available when needed, and is conditioned on fulfillment of all of the Washington Suburban Sanitary Commission's requirements for water and sewer service.
3. The applicant, his heirs, successors and/or assignees shall utilize an abutting driveway design, constructed per DPW's standards and requirements. Separate, standard residential driveway aprons shall be required for all lots 4, 5, 8

The surveyor certificate, owner dedication and approval signatures of the recorded plat are NOT reproduced here; they attach to that instrument, not to this drawing.

LEGEND

- PROPERTY BOUNDARY
 - - - - - BRL — BUILDING RESTRICTION LINE
 ——— PROPOSED STRUCTURE
 ——— EXISTING CONTOUR — PGATLAS 2 FT (2023), NAVD88
 - - - - - STREET CENTRELINE
 ——— PROPOSED PAVEMENT — DRIVEWAY / WALK
 - - - - - EASEMENT


PRINCE GEORGE'S COUNTY SOIL CONSERVATION DISTRICT APPROVAL
SEDIMENT CONTROL, GRADING, SOILS & DRAINAGE

SIGNATURE _____ DATE _____

DPIE SITE/ROAD PLAN REVIEW DIVISION APPROVAL _____

SIGNATURE _____ DATE _____

REVISIONS
— NONE —

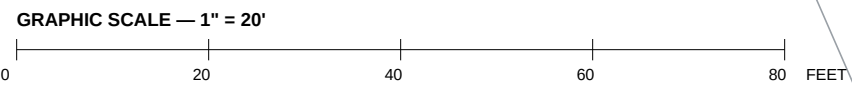

KEALEE

design, build, deliver

PROJECT
Porter Subdivision — LOT 1 & LOT 2
ADDRESS
1005 Rollins Ave
JURISDICTION
prince georges md
ZONE
RSF-65
SHEET
C-200 — Overall Site and Zoning Plan
SCALE
1" = 20'
STATUS
PRELIMINARY
SHEET NO.
3 OF 6
COORDINATES
EPSG:2248
H: NAD83
V: NAVD83 (feet)

SITE DATA		
ZONE	RSF-65	
TAX PARCEL ID		
GROSS LOT AREA	21,826 SF	0.501 AC
LOT FRONTAGE	45' MIN	65.00'
SETBACKS	REQUIRED	PROVIDED
FRONT YARD	23'	23'
SIDE YARD	8'	8'
REAR YARD	20'	20'
COVERAGE	MAX	PROPOSED
LOT COVERAGE	35%	5.5%
BUILDING FOOTPRINT	—	1,196 SF
DATA		
HORIZONTAL	EPSG:2248	NAD83
VERTICAL	NAVD83 (feet)	

SITE ANALYSIS		
1. Gross tract area	21,826 SF	
2. Area of dwelling	1,196 SF	
3. Wooded area	NOT ESTABLISHED	
4. Floodplain area	NOT ESTABLISHED	
5. Net tract area	21,826 SF	
6. TOTAL AREA DISTURBED	NOT QUANTIFIED	

SEQUENCE OF CONSTRUCTION		
1. Pre-construction meeting		1 DAY
2. Obtain necessary permits		2 DAYS
3. Notify MVA US81 at B11 at least 48 hours prior to any excavation		1 DAY
4. Construct stabilized construction entrance and perimeter sediment control		2 DAYS
5. Rough grade; construct dwelling, utilities and driveway		12 MONTHS
6. Fine grade and stabilize all disturbed areas		1 DAY
7. Remove sediment control devices when written permission has been granted		1 DAY
TOTAL ESTIMATED TIME OF CONSTRUCTION: 12 MONTHS		

GENERAL NOTES

- CONTRACTOR SHALL CONTACT MISS UTILITY AT B11 A MINIMUM OF 48 HOURS PRIOR TO ANY EXCAVATION. FIELD VERIFY LOCATION AND DEPTH BY TEST PIT BEFORE CONSTRUCTION.
- ALL EXISTING AND PROPOSED UTILITIES SHOWN PER PGD CODE SEC. 32.106.
- PROPOSED GRADE SHOWN SOLID. EXISTING GRADE SHOWN DASHED.
- ROUGH EARTHWORK GRADES AND UTILITY ELEVATIONS SHOWN TO TENTHS OF A FOOT.
- BOUNDARY SHOWN IS THE RECORDED PLAT OF SUBDIVISION — PORTER SUBDIVISION, LOTS 1 AND 2 — PLAT BOOK PM 231, P. 50 (MSA, C2381, 19050). SEAT PLEASANT (LITHO) ELECTION DISTRICT, PRINCE GEORGES COUNTY, MARYLAND. TAX MAP "3, GRID B3, 200 MAP 202 SE 06, ZONE R-55 AT RECORDING (RSP-45 UNDER THE 2002 REWRITE). SCALE 1" = 30'. NOVEMBER 2007. IN NAD83 RECORD FILE 5-50621. BASIS OF BEARINGS: MARYLAND STATE PLANE COORDINATE SYSTEM (NAD 83). LOT 1 = 9,599 SQ FT (0.2203 AC); LOT 2 = 8,008 SQ FT (0.1838 AC); 4,219 SQ FT (0.0969 AC) DEDICATED TO PUBLIC USE. TRANSFERRED AND CHECKED FOR CLOSURE. THE PLAT IS THE BOUNDARY SURVEY. NO FIELD TOPOGRAPHY IS INCLUDED. EXISTING GRADE IS COUNTY LEARN CONTOUR MAPPING.
- CONNECT TO EXISTING PAVEMENT, CURB AND GUTTER, DRIVEWAY AND SIDEWALK IN LINE AND GRADE.

PLAT OF RECORD

PORTER SUBDIVISION, LOTS 1 AND 2 — PLAT BOOK PM 231, P. 50 (MSA, C2381, 19050). SEAT PLEASANT (LITHO) ELECTION DISTRICT, PRINCE GEORGES COUNTY, MARYLAND. TAX MAP "3, GRID B3, 200 MAP 202 SE 06, ZONE R-55 AT RECORDING (RSP-45 UNDER THE 2002 REWRITE). SCALE 1" = 30'. NOVEMBER 2007. IN NAD83 RECORD FILE 5-50621. BASIS OF BEARINGS: MARYLAND STATE PLANE COORDINATE SYSTEM (NAD 83). LOT 1 = 9,599 sq ft (0.2203 ac); Lot 2 = 8,008 sq ft (0.1838 ac); 4,219 sq ft (0.0969 ac) dedicated to public use.

NOTES OF RECORD

- Development of this property shall be in accordance with the approved Stormwater Management Concept Plan 4125D-2008-05, or any approved revisions thereto.
- Approval of this plat is based upon a reasonable representation that public water and sewer service will be available when needed, and is conditioned on fulfilling all of the Washington Suburban Sanitary Commission authorization for 456.2 Z-5B covenants.
- The applicant, his heirs, successors and or assigns shall utilize an abutting driveway design, constructed per DPW&T standards and requirements. Separate, standard residential driveway approvals shall be provided along Rollins Avenue, if deemed appropriate by DPW&T upon the issuance of street construction permits.
- ADJOINING PROPERTIES, per the recorded plat: LOTS 13, 14 AND 15 (Addition to Pleasant Park, Plat Book V2 LBS, Plat 76) — northwest LOT 12 (Addition to Pleasant Park, Plat Book V2 LBS, Plat 76) — southeast OUTLOT A (Addition to Pleasant Park, Plat Book V2 LBS, Plat 76) — northwest, JEAN M. YOUNG, L. 5, 6, 7, 



design, build, deliver

PROJECT
Porter Subdivision — LOT 1 & LOT 2
ADDRESS
1005 Rollins Ave
JURISDICTION
prince georges md
ZONE
RSF-65
SHEET
L-100 — Landscape and Tree Canopy
SCALE
1" = 20'
STATUS
PRELIMINARY
SHEET NO.
6 OF 6
COORDINATES
EPSG:2248
H: NAD83
V: NAVD83 (feet)

SITE DATA		
ZONE	RSF-65	
TAX / PARCEL ID	—	
GROSS LOT AREA	21,826 SF	0.501 AC
LOT FRONTAGE	45 MIN	65.00'
SETBACKS	REQUIRED	PROVIDED
FRONT YARD	23'	8'
SIDE YARD	8'	8'
REAR YARD	20'	20'
COVERAGE	MAX	PROPOSED
LOT COVERAGE	35%	5.5%
BUILDING FOOTPRINT	— 1,195 SF	
DATUM		
HORIZONTAL	EPSG-2248	NAD83
VERTICAL	NAVD88 (feet)	

- | | |
|-------------------------|-----------------|
| 1. Gross tract area | 21,826 SF |
| 2. Area of dwelling | 1,196 SF |
| 3. Wooded area | NOT ESTABLISHED |
| 4. Floodplain area | NOT ESTABLISHED |
| 5. Net tract area | 21,826 SF |
| 6. TOTAL AREA DISTURBED | NOT QUANTIFIED |

- | | |
|--|-----------|
| 1. Pre-construction meeting | 1 DAY |
| 2. Obtain necessary permits | 2 DAYS |
| 3. Notify Miss Utility at 811 at least 48 hours prior to any excavation | 1 DAY |
| 4. Construct stabilized construction entrance and perimeter sediment control | 2 DAYS |
| 5. Rough grade; construct dwelling, utilities and driveway | 12 MONTHS |
| 6. Fine grade and stabilize all disturbed areas | 1 DAY |
| 7. Remove sediment control devices when written permission has been granted by the inspector | 1 DAY |
| TOTAL ESTIMATED TIME OF CONSTRUCTION: 12 MONTHS | |

- [illegible]

PORTER SUBDIVISION, LOTS 1 AND 2 — Plat Book PM 231, p. 50 (MSA_C2381_19050). Seat Pleasant (18th) Election District, Prince George's County, Maryland. Tax Map 73, Grid B3; 200 Map 200 SE 06, Zone R-95 at recording (RSF-65 under the 2022 rewire). Scale 1" = 20', November 2007. M-NCPPC Record File 5-09121. Basis of bearings: Maryland State Plane Coordinate System (NAD 83). Lot 1 = 9,598 sq ft (0.2203 ac); Lot 2 = 8,008 sq ft (0.1838 ac); 4,219 sq ft (0.0969 ac) dedicated to public use.

- D. Development of this project shall be in accordance with the approved Stormwater Management Plan (SWMP) dated 06-09-2008.
- E. Approval of this plat is based upon a reasonable expectation that public water and sewer service will be available when needed; and is conditioned on all rights of the Washington Suburban Sanitary Commission being fully satisfied.
- F. The applicant, his heirs, successors or assignees shall utilize an adjoining driveway fronted, constructed per DPWAT standards and requirements. Separate, standard residential driveway aprons shall be installed at the intersection of the driveway with the street, as deemed appropriate by DPWAT upon the issuance of street construction permits.
- G. ADDING PROPERTIES: per the recorded plat, LOTS 13, 14 AND 15 (to addition; Pleasant Park, Plat # 27, 1998), LOT 16 (to addition; Pleasant Park, Plat # 27, 1998), LOT 17 (to addition; Pleasant Park, Plat # 27, 1998), LOT 18 (to addition; Pleasant Park, Plat # 27, 1998), LOT 19 (to addition; Pleasant Park, Plat # 27, 1998), LOT 20 (to addition; Pleasant Park, Plat # 27, 1998), LOT 21 (to addition; Pleasant Park, Plat # 27, 1998), LOT 22 (to addition; Pleasant Park, Plat # 27, 1998), LOT 23 (to addition; Pleasant Park, Plat # 27, 1998), LOT 24 (to addition; Pleasant Park, Plat # 27, 1998), LOT 25 (to addition; Pleasant Park, Plat # 27, 1998), LOT 26 (to addition; Pleasant Park, Plat # 27, 1998), LOT 27 (to addition; Pleasant Park, Plat # 27, 1998), LOT 28 (to addition; Pleasant Park, Plat # 27, 1998), LOT 29 (to addition; Pleasant Park, Plat # 27, 1998), LOT 30 (to addition; Pleasant Park, Plat # 27, 1998), LOT 31 (to addition; Pleasant Park, Plat # 27, 1998), LOT 32 (to addition; Pleasant Park, Plat # 27, 1998), LOT 33 (to addition; Pleasant Park, Plat # 27, 1998), LOT 34 (to addition; Pleasant Park, Plat # 27, 1998), LOT 35 (to addition; Pleasant Park, Plat # 27, 1998), LOT 36 (to addition; Pleasant Park, Plat # 27, 1998), LOT 37 (to addition; Pleasant Park, Plat # 27, 1998), LOT 38 (to addition; Pleasant Park, Plat # 27, 1998), LOT 39 (to addition; Pleasant Park, Plat # 27, 1998), LOT 40 (to addition; Pleasant Park, Plat # 27, 1998), LOT 41 (to addition; Pleasant Park, Plat # 27, 1998), LOT 42 (to addition; Pleasant Park, Plat # 27, 1998), LOT 43 (to addition; Pleasant Park, Plat # 27, 1998), LOT 44 (to addition; Pleasant Park, Plat # 27, 1998), LOT 45 (to addition; Pleasant Park, Plat # 27, 1998), LOT 46 (to addition; Pleasant Park, Plat # 27, 1998), LOT 47 (to addition; Pleasant Park, Plat # 27, 1998), LOT 48 (to addition; Pleasant Park, Plat # 27, 1998), LOT 49 (to addition; Pleasant Park, Plat # 27, 1998), LOT 50 (to addition; Pleasant Park, Plat # 27, 1998), LOT 51 (to addition; Pleasant Park, Plat # 27, 1998), LOT 52 (to addition; Pleasant Park, Plat # 27, 1998), LOT 53 (to addition; Pleasant Park, Plat # 27, 1998), LOT 54 (to addition; Pleasant Park, Plat # 27, 1998), LOT 55 (to addition; Pleasant Park, Plat # 27, 1998), LOT 56 (to addition; Pleasant Park, Plat # 27, 1998), LOT 57 (to addition; Pleasant Park, Plat # 27, 1998), LOT 58 (to addition; Pleasant Park, Plat # 27, 1998), LOT 59 (to addition; Pleasant Park, Plat # 27, 1998), LOT 60 (to addition; Pleasant Park, Plat # 27, 1998), LOT 61 (to addition; Pleasant Park, Plat # 27, 1998), LOT 62 (to addition; Pleasant Park, Plat # 27, 1998), LOT 63 (to addition; Pleasant Park, Plat # 27, 1998), LOT 64 (to addition; Pleasant Park, Plat # 27, 1998), LOT 65 (to addition; Pleasant Park, Plat # 27, 1998), LOT 66 (to addition; Pleasant Park, Plat # 27, 1998), LOT 67 (to addition; Pleasant Park, Plat # 27, 1998), LOT 68 (to addition; Pleasant Park, Plat # 27, 1998), LOT 69 (to addition; Pleasant Park, Plat # 27, 1998), LOT 70 (to addition; Pleasant Park, Plat # 27, 1998), LOT 71 (to addition; Pleasant Park, Plat # 27, 1998), LOT 72 (to addition; Pleasant Park, Plat # 27, 1998), LOT 73 (to addition; Pleasant Park, Plat # 27, 1998), LOT 74 (to addition; Pleasant Park, Plat # 27, 1998), LOT 75 (to addition; Pleasant Park, Plat # 27, 1998), LOT 76 (to addition; Pleasant Park, Plat # 27, 1998), LOT 77 (to addition; Pleasant Park, Plat # 27, 1998), LOT 78 (to addition; Pleasant Park, Plat # 27, 1998), LOT 79 (to addition; Pleasant Park, Plat # 27, 1998), LOT 80 (to addition; Pleasant Park, Plat # 27, 1998), LOT 81 (to addition; Pleasant Park, Plat # 27, 1998), LOT 82 (to addition; Pleasant Park, Plat # 27, 1998), LOT 83 (to addition; Pleasant Park, Plat # 27, 1998), LOT 84 (to addition; Pleasant Park, Plat # 27, 1998), LOT 85 (to addition; Pleasant Park, Plat # 27, 1998), LOT 86 (to addition; Pleasant Park, Plat # 27, 1998), LOT 87 (to addition; Pleasant Park, Plat # 27, 1998), LOT 88 (to addition; Pleasant Park, Plat # 27, 1998), LOT 89 (to addition; Pleasant Park, Plat # 27, 1998), LOT 90 (to addition; Pleasant Park, Plat # 27, 1998), LOT 91 (to addition; Pleasant Park, Plat # 27, 1998), LOT 92 (to addition; Pleasant Park, Plat # 27, 1998), LOT 93 (to addition; Pleasant Park, Plat # 27, 1998), LOT 94 (to addition; Pleasant Park, Plat # 27, 1998), LOT 95 (to addition; Pleasant Park, Plat # 27, 1998), LOT 96 (to addition; Pleasant Park, Plat # 27, 1998), LOT 97 (to addition; Pleasant Park, Plat # 27, 1998), LOT 98 (to addition; Pleasant Park, Plat # 27, 1998), LOT 99 (to addition; Pleasant Park, Plat # 27, 1998), LOT 100 (to addition; Pleasant Park, Plat # 27, 1998).

The surveyor certificate, owner dedication and approval signatures of the recorded plat are NOT reproduced here; they attach to that instrument, not to this drawing.

- PROPERTY BOUNDARY
 - - - - - BRL — BUILDING RESTRICTION LINE
 ——— PROPOSED STRUCTURE
 ——— EXISTING CONTOUR — PGATLAS 2 FT (2023), NAVD83
 - - - - - STREET CENTRELINE
 ——— PROPOSED PAVEMENT — DRIVEWAY / WALK
 - - - - - EASEMENT

SIGNATURE _____ DATE _____

SIGNATURE _____ DATE _____

— none —

A horizontal number line representing distance in feet. It has tick marks at 0, 20, 40, 60, and 80. The word "FEET" is written at the right end of the line.