

KEALEE

design, build, deliver

PROJECT
1005 Rollins Ave
ADDRESS
1005 Rollins Ave
JURISDICTION
prince georges md
ZONE
RSF-65

SHEET
C-200 — Overall Site and Zoning Plan

SCALE
1" = 10'

STATUS
PRELIMINARY

SHEET NO.
2 OF 5

COORDINATES
EPSG:2248

H: NAD83
V: NAVD83 (feet)

PROFESSIONAL RESPONSIBILITY

Maryland Professional Engineer

certifies: sht_c-200

SEAL AND SIGNATURE

Architect

certifies: architectural_footprint

SEAL AND SIGNATURE

This sheet carries content from more than one professional discipline. Each seal below applies only to the subjects listed beside it. No professional certifies content outside their stated scope, and the sheet is not divided into separate drawings for that purpose.

SITE DATA		
ZONE	RSF-65	
TAX / PARCEL ID	348854	
GROSS LOT AREA	9,596 SF	0.220 AC
SETBACKS	REQUIRED	PROVIDED
FRONT YARD	25	25
SIDE YARD	8	8
REAR YARD	20	20
COVERAGE	MAX	PROPOSED
LOT COVERAGE	35%	17.1%
BUILDING FOOTPRINT	—	1,640 SF
DATUM		
HORIZONTAL	EPSG:2248	
VERTICAL	NAVD83 (feet)	

SITE ANALYSIS		
1. Gross tract area		9,596 SF
2. Area of dwelling		1,640 SF
3. Wooded area		NOT ESTABLISHED
4. Floodplain area		NOT ESTABLISHED
5. Net tract area		9,596 SF
6. TOTAL AREA DISTURBED		NOT QUANTIFIED

SEQUENCE OF CONSTRUCTION		
1. Pre-construction meeting		1 DAY
2. Obtain necessary permits		2 DAYS
3. Notify Miss Utility at B11 at least 48 hours prior to any excavation		1 DAY
4. Construct stabilized construction entrance and perimeter sidewalk control		2 DAYS
5. Rough grade; construct dwelling, utilities and driveway		12 MONTHS
6. Fine grade and stabilize all disturbed areas		1 DAY
7. Remove sediment control devices when written permission has been granted		1 DAY
TOTAL ESTIMATED TIME OF CONSTRUCTION: 12 MONTHS		

GENERAL NOTES		
1. CONTRACTOR SHALL CONTACT MISS UTILITY AT B11 A MINIMUM OF 48 HOURS PRIOR TO ANY EXCAVATION.		
2. ALL EXISTING AND PROPOSED UTILITIES SHOWN PER POC CODE SEC. 30-106.		
3. PROPOSED GRADE SHOWN SOLID, EXISTING GRADE SHOWN DASHED.		
4. ROUGH EARTHWORK GRADES AND UTILITY ELEVATIONS SHOWN TO TENTHS OF A FOOT.		
5. BOUNDARY SHOWN IS COMPILED JURISDICTION GIS, NOT A BOUNDARY SURVEY.		

LEGEND	
—	PROPERTY BOUNDARY
- - - - -	BRL — BUILDING RESTRICTION LINE
- - - - -	PROPOSED STRUCTURE
- - - - -	EXISTING CONTOUR — PGATLAS 2 FT (2023), NAVD83
- - - - -	STREET CENTRELINE
- - - - -	PROPOSED PAVEMENT — DRIVEWAY / WALK
- - - - -	EASEMENT

PRINCE GEORGE'S COUNTY SOIL CONSERVATION DISTRICT APPROVAL

SEDIMENT CONTROL, GRADING, SOILS & DRAINAGE

SIGNATURE

DATE

DPE SITE/ROAD PLAN REVIEW DIVISION APPROVAL

SIGNATURE

DATE

REVISIONS

— NONE —

SOILS TABLE

USDA NRCS SSURGO — required by POC Code Sec. 30-130(a)(13)

MAP UNIT	MAP UNIT NAME	K-FACTOR	HYDRIC	HYD. GROUP	DRAINAGE CLASS
AaB	Adelphia silt loam, 2 to 5 percent slopes complex	37	No	C	Moderately well drained
ACA	Adelphia-Aquasco complex, 0 to 2 percent slopes	43	No	D	Somewhat poorly drained
ACB	Adelphia-Aquasco complex, 0 to 2 percent slopes	37	No	C	Moderately well drained
ADA	Adelphia-Haindel complex, 0 to 2 percent slopes	24	No	BD	Somewhat poorly drained
ADB	Adelphia-Haindel complex, 0 to 2 percent slopes	37	No	C	Moderately well drained
AIB	Adelphia-Haindel complex, 2 to 5 percent slopes	24	No	BD	Somewhat poorly drained
ABD	Adelphia-Haindel complex, 2 to 5 percent slopes	37	No	C	Moderately well drained
AIC	Adelphia-Haindel complex, 5 to 10 percent slopes	24	No	BD	Somewhat poorly drained

SOURCE AND ACCURACY
Parcel boundary — Jurisdiction gis — Prince George's County / M-ACPPC — PGAtlas Property — level 1
Existing contours — Prince George's County / M-NCPPC — PGAtlas — level 1
Contours: PGAtlas Elevation/MapServer1 — Contour = 2 Ft (2023), 2 ft interval, NAVD83 (feet)

GRAPHIC SCALE — 1" = 10'

0 10 20 30 40 FEET

KEALEE

design, build, deliver

PROJECT
1005 Rollins Ave

ADDRESS
1005 Rollins Ave

JURISDICTION
prince georges md

ZONE
RSF-65

SHEET
C-400 — Grading and Drainage Plan

SCALE
1" = 10'

STATUS
PRELIMINARY

SHEET NO.
3 OF 5

COORDINATES
EPSG:2248

H: NAD83

V: NAVD83 (feet)

PROFESSIONAL RESPONSIBILITY

Maryland Professional Engineer

certificat: kealee_maryland_design

SEAL AND SIGNATURE

All content on this sheet falls within one professional scope.

SITE DATA

ZONE RSF-65

TAX / PARCEL ID 34854

GROSS LOT AREA 9,596 SF 0.220 AC

SETBACKS REQUIRED PROVIDED

FRONT YARD 25' 25'

SIDE YARD 8' 8'

REAR YARD 20' 20'

COVERAGE MAX PROPOSED

LOT COVERAGE 35% —

BUILDING FOOTPRINT — —

DATUM

HORIZONTAL EPSG:2248 NAD83

VERTICAL NAVD83 (feet)

SITE ANALYSIS

1. Gross tract area 9,596 SF

2. Area of dwelling NOT ESTABLISHED

3. Wooded area NOT ESTABLISHED

4. Floodplain area NOT ESTABLISHED

5. Net tract area 9,596 SF

6. TOTAL AREA DISTURBED NOT QUANTIFIED

SEQUENCE OF CONSTRUCTION

1. Pre-construction meeting 1 DAY

2. Obtain necessary permits 2 DAYS

3. Notify Miss Utility at 811 at least 48 hours prior to any excavation 1 DAY

4. Construct stabilized construction entrance and perimeter sediment control 2 DAYS

5. Rough grade; construct dwelling, utilities and driveway 12 MONTHS

6. Fine grade and stabilize all disturbed areas 1 DAY

7. Remove sediment control devices when written permission has been granted 1 DAY

TOTAL ESTIMATED TIME OF CONSTRUCTION: 12 MONTHS

GENERAL NOTES

1. CONTRACTOR SHALL CONTACT MISS UTILITY AT 811 A MINIMUM OF 48 HOURS PRIOR TO ANY EXCAVATION.

2. ALL EXISTING AND PROPOSED UTILITIES SHOWN PER PGC CODE SEC. 32.106.

3. PROPOSED GRADE SHOWN SOLID EXISTING GRADE SHOWN DASHED.

4. ROUGH EARTHWORK GRADES AND UTILITY ELEVATIONS SHOWN TO TENTHS OF A FOOT.

5. BOUNDARY SHOWN IS COMPILED JURISDICTION GIS, NOT A BOUNDARY SURVEY.

LEGEND

PROPERTY BOUNDARY

BRL — BUILDING RESTRICTION LINE

PROPOSED STRUCTURE

EXISTING CONTOUR — PGTLAS 2 FT (2023), NAVD83

STREET CENTRELINE

PROPOSED PAVEMENT — DRIVEWAY / WALK

EASEMENT

PRINCE GEORGE'S COUNTY SOIL CONSERVATION DISTRICT APPROVAL

SEDIMENT CONTROL, GRADING, SOILS & DRAINAGE

SIGNATURE DATE

DPE SITEROAD PLAN REVIEW DIVISION APPROVAL

SIGNATURE DATE

GRADING CERTIFICATE

I HEREBY CERTIFY THAT THIS PLAN CONFORMS TO THE REQUIREMENTS OF SUBTITLE 32, DIVISION 2 OF THE CODE OF PRINCE GEORGE'S COUNTY WATER RESOURCES PROTECTION AND GRADING CODE AND THAT I OR MY STAFF HAVE INSPECTED THIS SITE AND THAT DRAINAGE FLOWS FROM UPLAND PROPERTIES ONTO THIS SITE, AND FROM THIS SITE ONTO DOWNHILL PROPERTIES, HAVE BEEN ADDRESSED IN SUBSTANTIAL ACCORDANCE WITH APPLICABLE CODES, SIGNED, SEALED AND DATED BY A PROFESSIONAL ENGINEER LICENSED IN THE STATE OF MARYLAND.

PRINCE GEORGE'S COUNTY (PGC), See Rough Grading Design Review Checklist, Item A-10

STABILIZATION COMPLIANCE PREAMBLE

Stabilization practices on all projects must be in compliance with the requirements of COMAR 26.17.01 by January 9, 2013, regardless of when an erosion and sediment control plan was approved.

COMAR 26.17.01.02(B)(2), Covering/Seeding of exposed plans

STANDARD STABILIZATION NOTE

Following initial soil disturbance or re-disturbance, permanent or temporary stabilization must be completed within: a.) Three (3) calendar days as to the surface of all perimeter dikes, swales, ditches, perimeter slopes, and all slopes steeper than 3 horizontal to 1 vertical (3:1), and b.) Seven (7) calendar days as to all other disturbed or graded areas on the project site not under active grading.

2013 Maryland Standards and Specifications for Soil Erosion and Sediment Control, "Standard Stabilization Note" (adopted by COMAR 26.17.01.02A(2))

REVISIONS

NOTE

SOILS TABLE

USDA NRCS SSURGO — required by POC Code Sec. 32-130(a)(13)

MAP UNIT	MAP UNIT NAME	K-FACTOR	HYDRIC	HYD. GROUP	DRAINAGE CLASS
AaB	Adelphia silt loam, 2 to 5 percent slopes complex	37	No	C	Moderately well drained
ACA	Adelphia Aquascon complex, 0 to 2 percent slopes	43	No	D	Somewhat poorly drained
ACA	Adelphia Aquascon complex, 0 to 2 percent slopes	37	No	C	Moderately well drained
ADA	Adelphia Hainsdel complex, 0 to 2 percent slopes	24	No	BD	Somewhat poorly drained
ADA	Adelphia Hainsdel complex, 0 to 2 percent slopes	37	No	C	Moderately well drained
AaB	Adelphia Hainsdel complex, 2 to 5 percent slopes	24	No	BD	Somewhat poorly drained
AaB	Adelphia Hainsdel complex, 2 to 5 percent slopes	37	No	C	Moderately well drained
AaC	Adelphia Hainsdel complex, 5 to 10 percent slopes	24	No	BD	Somewhat poorly drained

SOURCE AND ACCURACY

Parcel boundary — Jurisdiction gis — Prince George's County / M-ACPPC — PGALas Property — level 1

Existing contours — Prince George's County / M-NCPPC — PGALas — level 1

Contours: PGALas Elevation/MapServer1 — Contour = 2 Ft (2023), 2 ft interval, NAVD83 (feet)

GRAPHIC SCALE — 1" = 10'

0 10 20 30 40 FEET

KEALEE

design, build, deliver

PROJECT
1005 Rollins Ave
ADDRESS
1005 Rollins Ave
JURISDICTION
prince georges md
ZONE
RSF-65
SHEET
C-500 — Utility Plan
SCALE
1" = 10'
STATUS
PRELIMINARY
SHEET NO.
4 OF 5
COORDINATES
EPSG:2248
H: NAD83
V: NAVD83 (feet)

PROFESSIONAL RESPONSIBILITY

Maryland Professional Engineer

certificat_utilty_design

SEAL AND SIGNATURE

All content on this sheet falls within one professional scope.

SITE DATA		
ZONE	RSF-65	
TAX / PARCEL ID	34854	
GROSS LOT AREA	9,596 SF	0.220 AC
SETBACKS	REQUIRED	PROVIDED
FRONT YARD	25'	25'
SIDE YARD	8'	8'
REAR YARD	20'	20'
COVERAGE	MAX	PROPOSED
LOT COVERAGE	35%	—
BUILDING FOOTPRINT	—	—
DATUM		
HORIZONTAL	EPSG:2248	NAD83
VERTICAL	NAVD83 (feet)	

SITE ANALYSIS

1. Gross tract area	9,596 SF
2. Area of dwelling	NOT ESTABLISHED
3. Wooded area	NOT ESTABLISHED
4. Floodplain area	NOT ESTABLISHED
5. Net tract area	9,596 SF
6. TOTAL AREA DISTURBED	NOT QUANTIFIED

SEQUENCE OF CONSTRUCTION

1. Pre-construction meeting	1 DAY
2. Obtain necessary permits	2 DAYS
3. Notify Miss Utility at 811 at least 48 hours prior to any excavation	1 DAY
4. Construct stabilized construction entrance and perimeter sediment control	2 DAYS
5. Rough grade; construct dwelling, utilities and driveway	12 MONTHS
6. Fine grade and stabilize all disturbed areas	1 DAY
7. Remove sediment control devices when written permission has been granted	1 DAY
TOTAL ESTIMATED TIME OF CONSTRUCTION:	12 MONTHS

GENERAL NOTES

- CONTRACTOR SHALL CONTACT MISS UTILITY AT 811 A MINIMUM OF 48 HOURS PRIOR TO ANY EXCAVATION.
- ALL EXISTING AND PROPOSED UTILITIES SHOWN PER PGC CODE SEC. 32.106.
- PROPOSED GRADE SHOWN SOLID EXISTING GRADE SHOWN DASHED.
- ROUGH EARTHWORK GRADES AND UTILITY ELEVATIONS SHOWN TO TENTHS OF A FOOT.
- BOUNDARY SHOWN IS COMPILED JURISDICTION GIS, NOT A BOUNDARY SURVEY.

LEGEND

- PROPERTY BOUNDARY
- BRL — BUILDING RESTRICTION LINE
- PROPOSED STRUCTURE
- EXISTING CONTOUR — PG&LAS 2 FT (2023), NAVD83
- STREET CENTRELINE
- PROPOSED PAVEMENT — DRIVEWAY / WALK
- EASEMENT

PRINCE GEORGE'S COUNTY SOIL CONSERVATION DISTRICT APPROVAL

SEDIMENT CONTROL, GRADING, SOILS & DRAINAGE

SIGNATURE	DATE
-----------	------

DPE SITEROAD PLAN REVIEW DIVISION APPROVAL

SIGNATURE	DATE
-----------	------

REVISIONS

— NONE —

SOILS TABLE


USDA NRCS SSURGO — required by POC Code Sec. 32-130a(13)

MAP UNIT	MAP UNIT NAME	K-FACTOR	HYDRIC	HYD. GROUP	DRAINAGE CLASS
AaB	Adelphia silt loam, 2 to 5 percent slopes complex	37	No	C	Moderately well drained
ACA	Adelphia-Aquasco complex, 0 to 2 percent slopes	43	No	D	Somewhat poorly drained
ACA	Adelphia-Aquasco complex, 0 to 2 percent slopes	37	No	C	Moderately well drained
ADA	Adelphia-Hairdel complex, 0 to 2 percent slopes	24	No	BD	Somewhat poorly drained
ADA	Adelphia-Hairdel complex, 0 to 2 percent slopes	37	No	C	Moderately well drained
AaB	Adelphia-Hairdel complex, 2 to 5 percent slopes	24	No	BD	Somewhat poorly drained
AaB	Adelphia-Hairdel complex, 2 to 5 percent slopes	37	No	C	Moderately well drained
AaC	Adelphia-Hairdel complex, 5 to 10 percent slopes	24	No	BD	Somewhat poorly drained

SOURCE AND ACCURACY

Parcel boundary — Jurisdiction gis — Prince George's County / M-NCPPC — PG&Las Property — level 1
Existing contours — Prince George's County / M-NCPPC — PG&Las — level 1
Contours: PG&Las Elevation/MapServer1 — Contour = 2 Ft (2023), 2 ft interval, NAVD83 (feet)

GRAPHIC SCALE — 1" = 10'

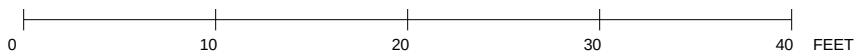

KEALEE

design, build, deliver

PROJECT
1005 Rollins Ave

ADDRESS
1005 Rollins Ave

JURISDICTION
prince georges md

ZONE
RSF-65

SHEET
L-100 — Landscape and Tree Canopy Plan

SCALE
1" = 10'

STATUS
PRELIMINARY

SHEET NO.
5 OF 5

COORDINATES
EPSG:2248

H: NAD83

V: NAVD83 (feet)

PROFESSIONAL RESPONSIBILITY

Qualified Environmental Professional

certified tree_conservation

SEAL AND SIGNATURE

All content on this sheet falls within one professional scope.

SITE DATA

ZONE

TAX / PARCEL ID

GROSS LOT AREA

SETBACKS

FRONT YARD

SIDE YARD

REAR YARD

COVERAGE

LOT COVERAGE

BUILDING FOOTPRINT

DATUM

HORIZONTAL

VERTICAL

SITE ANALYSIS

1. Gross tract area

2. Area of dwelling

3. Wooded area

4. Floodplain area

5. Net tract area

6. TOTAL AREA DISTURBED

SEQUENCE OF CONSTRUCTION

1. Pre-construction meeting

2. Obtain necessary permits

3. Notify Miss Utility at 811 at least 48 hours prior to any excavation

4. Construct stabilized construction entrance and perimeter sediment control

5. Rough grade; construct dwelling, utilities and driveway

6. Fine grade and stabilize all disturbed areas

7. Remove sediment control devices when written permission has been granted

TOTAL ESTIMATED TIME OF CONSTRUCTION: 12 MONTHS

GENERAL NOTES

1. CONTRACTOR SHALL CONTACT MISS UTILITY AT 811 A MINIMUM OF 48 HOURS PRIOR TO ANY EXCAVATION.

2. ALL EXISTING AND PROPOSED UTILITIES SHOWN PER PGC CODE SEC. 32.106.

3. PROPOSED GRADE SHOWN SOLID EXISTING GRADE SHOWN DASHED.

4. ROUGH EARTHWORK GRADES AND UTILITY ELEVATIONS SHOWN TO TENTHS OF A FOOT.

5. BOUNDARY SHOWN IS COMPILED JURISDICTION GIS, NOT A BOUNDARY SURVEY.

LEGEND

PROPERTY BOUNDARY

BRL — BUILDING RESTRICTION LINE

PROPOSED STRUCTURE

EXISTING CONTOUR — PG&LAS 2 FT (2023), NAVD83

STREET CENTRELINE

PROPOSED PAVEMENT — DRIVEWAY / WALK

EASEMENT

PRINCE GEORGE'S COUNTY SOIL CONSERVATION DISTRICT APPROVAL

SEDIMENT CONTROL, GRADING, SOILS & DRAINAGE

SIGNATURE

DATE

DPE SITEROAD PLAN REVIEW DIVISION APPROVAL

SIGNATURE

DATE

REVISIONS

NOTE

SOILS TABLE

USDA NRCS SSURGO — required by POC Code Sec. 32-130(a)(13)

MAP UNIT	MAP UNIT NAME	K-FACTOR	HYDRIC	HYD. GROUP	DRAINAGE CLASS
AaB	Adelphia silt loam, 2 to 5 percent slopes complex	37	No	C	Moderately well drained
ACA	Adelphia-Aquasco complex, 0 to 2 percent slopes	43	No	D	Somewhat poorly drained
ACA	Adelphia-Aquasco complex, 0 to 2 percent slopes	37	No	C	Moderately well drained
ADA	Adelphia-Haindel complex, 0 to 2 percent slopes	24	No	BD	Somewhat poorly drained
ADA	Adelphia-Haindel complex, 0 to 2 percent slopes	37	No	C	Moderately well drained
AaB	Adelphia-Haindel complex, 2 to 5 percent slopes	24	No	BD	Somewhat poorly drained
AaB	Adelphia-Haindel complex, 2 to 5 percent slopes	37	No	C	Moderately well drained
AaC	Adelphia-Haindel complex, 5 to 10 percent slopes	24	No	BD	Somewhat poorly drained

SOURCE AND ACCURACY

Parcel boundary — Jurisdiction gis — Prince George's County / M-NCPPC — PG&LAS Property — level 1

Existing contours — Prince George's County / M-NCPPC — PG&LAS — level 1

Contours: PG&LAS Elevation/MapServer1 — Contour = 2 Ft (2023), 2 ft interval, NAVD83 (feet)

GRAPHIC SCALE — 1" = 10'

0 10 20 30 40 FEET