



KEALEE

Design, build, deliver

PROJECT
4600 WHEELER ROAD — PRELIMINARY SUBDIVISION CONCEPT — LOTS 1–14 (proposed)

ADDRESS
4600 WHEELER ROAD

JURISDICTION
Prince George's County, Maryland

ZONE
RSF-95

SHEET
C-001 — Site Development Plan — Existing, Proposed, Grading, Paving and Landscape

SCALE
1" = 100'

STATUS
PRELIMINARY

SHEET NO.
1 OF 3

COORDINATES
EPSG:2248
H: NAD83
V: NAVD88 (feet)

PLAN TYPE AND PREPARATION

PLAN TYPE SITE DEVELOPMENT / FINE GRADING

SHEET C-001 — Site Development Plan — Existing, Proposed, Grading, Paving and Landscape

DISCIPLINE Maryland Professional Engineer / Surveyor (see divided responsibility)

DRAWN BY KEALEE SITE-PLAN ENGINEER

DESIGNED BY

CHECKED BY

REVISIONS

NO.	DATE	DESCRIPTION

INDEX OF DRAWINGS

- 1 C-001 Site Development Plan — Existing, Proposed, Grading, Paving and Landscape and Tree Canopy Plan
- 2 L-100 Landscape and Tree Canopy Plan
- 3 C-400 Grading and Drainage Plan

SITE DATA

ZONE	RSF-95
TAX / PARCEL ID	230,997 SF
GROSS TRACT AREA	5,303 AC
LOT 1 (proposed) AREA	9,836 SF 0.226 AC
LOT 2 (proposed) AREA	11,907 SF 0.273 AC
LOT 3 (proposed) AREA	9,854 SF 0.226 AC
LOT 4 (proposed) AREA	12,933 SF 0.297 AC
LOT 5 (proposed) AREA	10,814 SF 0.248 AC
LOT 6 (proposed) AREA	13,335 SF 0.306 AC
LOT 7 (proposed) AREA	14,154 SF 0.325 AC
LOT 8 (proposed) AREA	14,032 SF 0.322 AC
LOT 9 (proposed) AREA	9,530 SF 0.219 AC
LOT 10 (proposed) AREA	9,746 SF 0.224 AC
LOT 11 (proposed) AREA	9,823 SF 0.226 AC
LOT 12 (proposed) AREA	13,953 SF 0.320 AC
LOT 13 (proposed) AREA	12,075 SF 0.277 AC
LOT 14 (proposed) AREA	17,383 SF 0.399 AC
NET LOT AREA	169,374 SF 3.888 AC
LOT 1 (proposed) FRONTAGE	50' MIN
LOT 2 (proposed) FRONTAGE	50' MIN
LOT 3 (proposed) FRONTAGE	50' MIN
LOT 4 (proposed) FRONTAGE	50' MIN
LOT 5 (proposed) FRONTAGE	50' MIN
LOT 6 (proposed) FRONTAGE	50' MIN
LOT 7 (proposed) FRONTAGE	50' MIN
LOT 8 (proposed) FRONTAGE	50' MIN
LOT 9 (proposed) FRONTAGE	50' MIN
LOT 10 (proposed) FRONTAGE	50' MIN
LOT 11 (proposed) FRONTAGE	50' MIN
LOT 12 (proposed) FRONTAGE	50' MIN
LOT 13 (proposed) FRONTAGE	50' MIN
LOT 14 (proposed) FRONTAGE	50' MIN
SETBACKS	REQUIRED PROVIDED
FRONT YARD	25' 25'
SIDE YARD	6' 6'
REAR YARD	20' 20'
COVERAGE	MAX PROPOSED
LOT COVERAGE	30% 7.4%
BUILDING FOOTPRINT	— 12,541 SF
DATUM	
HORIZONTAL	EPSG:2248 NAD83
VERTICAL	NAVD88 (feet)

SITE ANALYSIS

1. Gross tract area 230,997 SF
2. Area of dwelling 12,541 SF
3. Wooded area NOT ESTABLISHED
4. Floodplain area NOT ESTABLISHED
5. Net lot area 169,374 SF
6. TOTAL AREA DISTURBED 115,032 SF (AT LEAST)
7. SWM REQUIRED — Sec. 32-174(a)(3) YES — DISTURBANCE EXCEEDS 5,000 SF

BUILDING DATA

	G	B	FF	SF	HT	STY
LOT 1 (proposed)	155.63	—	155.96	154.96	20'	2
LOT 2 (proposed)	149.62	—	149.95	148.95	20'	2
LOT 3 (proposed)	153.00	—	153.33	152.33	20'	2
LOT 4 (proposed)	157.64	—	157.97	156.97	20'	2
LOT 5 (proposed)	159.65	—	159.98	158.98	20'	2
LOT 6 (proposed)	169.37	—	169.70	168.70	20'	2
LOT 7 (proposed)	163.93	—	164.26	163.26	20'	2
LOT 8 (proposed)	163.93	—	164.26	163.26	20'	2
LOT 9 (proposed)	163.93	—	164.26	163.26	20'	2
LOT 10 (proposed)	163.93	—	164.26	163.26	20'	2
LOT 11 (proposed)	163.93	—	164.26	163.26	20'	2

G: garage slab; B: basement; FF: finished floor; SF: subfloor; HT: height; STY: storeys. A DASH IS NOT ZERO; the elevation has not been established and must be set from a field-run topographic survey before construction.

DRAINAGE AREA COMPUTATIONS

CATCHMENT	AREA SF	IMPERV.	PPE Q	POST Q	INCREASE	WQV CF
LOT 1 (proposed)	9,836	25.3%	0.38	0.65	0.27	228
LOT 2 (proposed)	11,907	17.6%	0.46	0.68	0.22	207
LOT 3 (proposed)	9,854	0.0%	0.38	0.38	0.00	41
LOT 4 (proposed)	12,933	9.3%	0.50	0.63	0.13	145
LOT 5 (proposed)	10,814	19.8%	0.42	0.65	0.23	206
LOT 6 (proposed)	13,335	18.9%	0.51	0.79	0.28	245
LOT 7 (proposed)	14,154	17.1%	0.55	0.80	0.25	240
LOT 8 (proposed)	14,032	14.9%	0.54	0.77	0.23	215
LOT 9 (proposed)	9,530	17.0%	0.37	0.54	0.17	162
LOT 10 (proposed)	9,746	8.6%	0.38	0.47	0.09	103
LOT 11 (proposed)	9,823	10.0%	0.38	0.48	0.10	114
LOT 12 (proposed)	13,953	0.0%	0.54	0.54	0.00	58
LOT 13 (proposed)	12,075	0.0%	0.47	0.47	0.00	50
LOT 14 (proposed)	17,383	0.0%	0.67	0.67	0.00	72
PROJECT TOTAL	169,374	10.9%	6.55	8.52	1.97	2,066

Peak flows are summed for catchments; Q in cfs. WQV is the required water-quality volume.

PROFESSIONAL CERTIFICATION

I HEREBY CERTIFY THAT THESE DOCUMENTS WERE PREPARED OR APPROVED BY ME, AND THAT I AM A DULY LICENSED PROFESSIONAL ENGINEER UNDER THE LAWS OF THE STATE OF MARYLAND.

SIGNATURE

DATE

LICENSE NO.

EXPIRATION DATE


REVISIONS

— NONE —

SOILS STABLE USDA NRCS SSURGO — PGC Code Sec. 32-133(a)(13)

MAP UNIT	MAP UNIT NAME	K-FACT	HYRIC	HYD. GRP	DRAINAGE CLASS
AaB	Adelphia silt loam, 2 to 5 percent slopes complex	37	No	C	Moderately well drained
AcA	Adelphia-Aquasco complex, 0 to 2 percent slopes	43	No	D	Somewhat poorly drained
AdA	Adelphia-Holmdel complex, 0 to 2 percent slopes	24	No	B/D	Somewhat poorly drained
AdB	Adelphia-Holmdel complex, 2 to 5 percent slopes	24	No	B/D	Somewhat poorly drained
AdC	Adelphia-Holmdel complex, 5 to 10 percent slopes	24	No	B/D	Somewhat poorly drained

CONCRETE CURB AND GUTTER — PGC DPW&T STD. 300.01

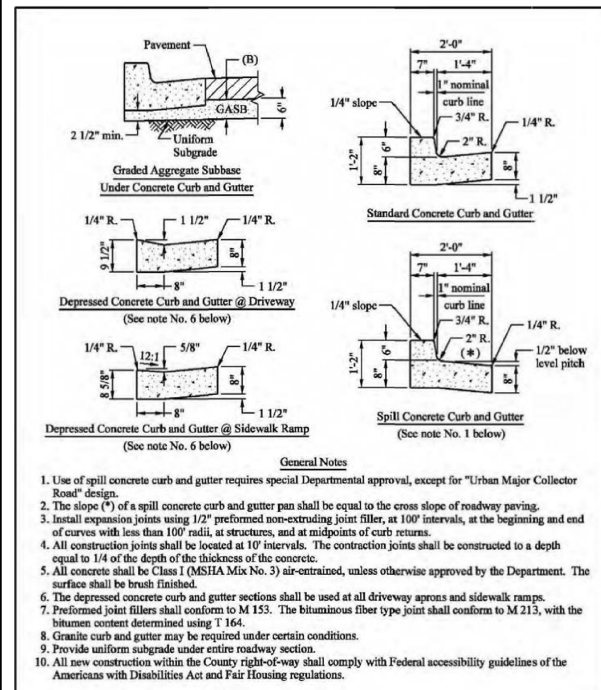

1. Use of gullies, concrete curb and gutter systems, and Department approval, except for "Other Major Collector Road" only.

2. The design of a gully, concrete curb and gutter shall be based on the cross slope of roadway paving.

3. The design of a gully, concrete curb and gutter shall be based on the cross slope of roadway paving, and shall be based on the cross slope of roadway paving, and shall be based on the cross slope of roadway paving.

4. All proposed gully and gutter systems shall be based on the cross slope of roadway paving, and shall be based on the cross slope of roadway paving, and shall be based on the cross slope of roadway paving.

GRAPHIC SCALE — 1" = 100'

0 100 200 300 400 FEET

CONCRETE SIDEWALK RAMP TYPE A — PGC DPW&T STD. 300.07

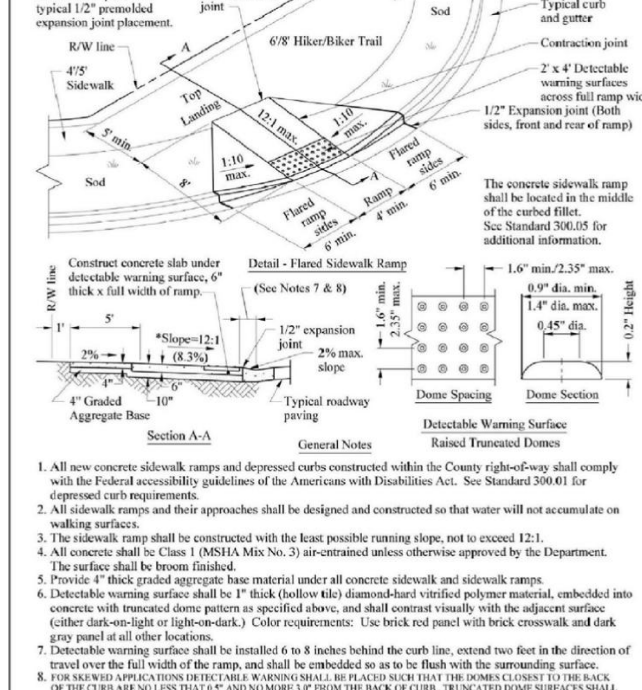

1. All new concrete sidewalk ramps and depressed curbs constructed within the County right-of-way shall comply with the Federal accessibility guidelines of the Americans with Disabilities Act. See Standard 300.01 for Department curb requirements.

2. All sidewalk ramps and curb structures shall be designed and constructed so that water will not accumulate on ramping surfaces.

3. The sidewalk ramp shall be constructed with the base parallel to the curb, and to meet 12.1.

4. All sidewalk ramps shall be based on the cross slope of roadway paving, and shall be based on the cross slope of roadway paving, and shall be based on the cross slope of roadway paving.

REPRODUCED FROM THE PGC DPW&T STANDARD THE STANDARD GOVERNS.

REPRODUCED FROM THE PGC DPW&T STANDARD THE STANDARD GOVERNS.



KEALEE

Design, build, deliver

PROJECT
4600 WHEELER ROAD — PRELIMINARY SUBDIVISION CONCEPT — LOTS 1-14 (proposed)
ADDRESS
4600 WHEELER ROAD
JURISDICTION
Prince George's County, Maryland
ZONE
RSF-95
SHEET
L-100 — Landscape and Tree Canopy Plan
SCALE
1" = 100'
STATUS
PRELIMINARY
SHEET NO.
2 OF 3
COORDINATES
EPSG:2248
H: NAD83
V: NAVD88 (feet)

PLAN TYPE AND PREPARATION

PLAN TYPE SITE DEVELOPMENT / FINE GRADING
SHEET L-100 — Landscape and Tree Canopy Plan
DISCIPLINE Landscape Architect / Qualified Professional
DRAWN BY KEALEE SITE-PLAN ENGINE
DESIGNED BY
CHECKED BY

REVISIONS

NO.	DATE	DESCRIPTION

INDEX OF DRAWINGS

- 1 C-001 Site Development Plan — Existing, Proposed, Grading, Paving and
2 L-100 Landscape and Tree Canopy Plan
3 C-400 Grading and Drainage Plan

SITE DATA

ZONE	RSF-95
TAX / PARCEL ID	230,997 SF
GROSS TRACT AREA	5,303 AC
LOT 1 (proposed) AREA	9,836 SF
LOT 2 (proposed) AREA	11,907 SF
LOT 3 (proposed) AREA	9,854 SF
LOT 4 (proposed) AREA	12,933 SF
LOT 5 (proposed) AREA	10,814 SF
LOT 6 (proposed) AREA	13,335 SF
LOT 7 (proposed) AREA	14,154 SF
LOT 8 (proposed) AREA	14,032 SF
LOT 9 (proposed) AREA	9,530 SF
LOT 10 (proposed) AREA	9,746 SF
LOT 11 (proposed) AREA	9,823 SF
LOT 12 (proposed) AREA	13,953 SF
LOT 13 (proposed) AREA	12,075 SF
LOT 14 (proposed) AREA	17,383 SF
NET LOT AREA	169,374 SF
LOT 1 (proposed) FRONTAGE	50' MIN
LOT 2 (proposed) FRONTAGE	50' MIN
LOT 3 (proposed) FRONTAGE	50' MIN
LOT 4 (proposed) FRONTAGE	50' MIN
LOT 5 (proposed) FRONTAGE	50' MIN
LOT 6 (proposed) FRONTAGE	50' MIN
LOT 7 (proposed) FRONTAGE	50' MIN
LOT 8 (proposed) FRONTAGE	50' MIN
LOT 9 (proposed) FRONTAGE	50' MIN
LOT 10 (proposed) FRONTAGE	50' MIN
LOT 11 (proposed) FRONTAGE	50' MIN
LOT 12 (proposed) FRONTAGE	50' MIN
LOT 13 (proposed) FRONTAGE	50' MIN
LOT 14 (proposed) FRONTAGE	50' MIN
SETBACKS	REQUIRED PROVIDED
FRONT YARD	25' 25'
SIDE YARD	6' 6'
REAR YARD	20' 20'
COVERAGE	MAX PROPOSED
LOT COVERAGE	30% 7.4%
BUILDING FOOTPRINT	— 12,541 SF
DATUM	—
HORIZONTAL	EPSG:2248 NAD83
VERTICAL	NAVD88 (feet)

SITE ANALYSIS

1. Gross tract area 230,997 SF
2. Area of dwelling 12,541 SF
3. Wooded area NOT ESTABLISHED
4. Floodplain area NOT ESTABLISHED
5. Net lot area 169,374 SF
6. TOTAL AREA DISTURBED 115,032 SF (AT LEAST)
7. SWM REQUIRED — Sec. 32-174(a)(3) YES — DISTURBANCE EXCEEDS 5,000 SF

BUILDING DATA

	G	B	FF	SF	HT	STY
LOT 1 (proposed)	155.63	—	155.96	154.96	20'	2
LOT 2 (proposed)	149.62	—	149.95	148.95	20'	2
LOT 3 (proposed)	153.00	—	153.33	152.33	20'	2
LOT 4 (proposed)	157.64	—	157.97	156.97	20'	2
LOT 5 (proposed)	159.65	—	159.98	158.98	20'	2
LOT 6 (proposed)	169.37	—	169.70	168.70	20'	2
LOT 7 (proposed)	163.93	—	164.26	163.26	20'	2
LOT 8 (proposed)	161.64	—	161.97	160.97	20'	2
LOT 9 (proposed)	159.62	—	159.95	158.95	20'	2
LOT 10 (proposed)	163.90	—	164.23	163.23	20'	2

G: garage slab, B: basement, FF: finished floor, SF: subfloor, HT: height, STY: stories, A DASH IS NOT ZERO; the elevation has not been established and must be set from a field-run geomatic survey before construction.

DRAINAGE AREA COMPUTATIONS

CATCHMENT	AREA SF	IMPERV.	PPE Q	POST Q	INCREASE	WQV CF
LOT 1 (proposed)	9,836	25.3%	0.38	0.65	0.27	228
LOT 2 (proposed)	11,907	17.6%	0.46	0.68	0.22	207
LOT 3 (proposed)	9,854	0.0%	0.38	0.38	0.00	41
LOT 4 (proposed)	12,933	9.3%	0.50	0.63	0.13	145
LOT 5 (proposed)	10,814	19.8%	0.42	0.65	0.23	206
LOT 6 (proposed)	13,335	18.9%	0.51	0.79	0.28	245
LOT 7 (proposed)	14,154	17.1%	0.55	0.80	0.25	240
LOT 8 (proposed)	14,032	14.9%	0.54	0.77	0.23	215
LOT 9 (proposed)	9,530	17.0%	0.37	0.54	0.17	162
LOT 10 (proposed)	9,746	8.6%	0.38	0.47	0.09	103
LOT 11 (proposed)	9,823	10.0%	0.38	0.48	0.10	114
LOT 12 (proposed)	13,953	0.0%	0.54	0.54	0.00	58
LOT 13 (proposed)	12,075	0.0%	0.47	0.47	0.00	50
LOT 14 (proposed)	17,383	0.0%	0.67	0.67	0.00	72
PROJECT TOTAL	169,374	10.9%	6.55	8.52	1.97	2,066

Peak flows are summed for catchments; Q in cfs. WQV is the required water-quality volume.

PROFESSIONAL CERTIFICATION

I HEREBY CERTIFY THAT THESE DOCUMENTS WERE PREPARED OR APPROVED BY ME, AND THAT I AM A DULY LICENSED PROFESSIONAL ENGINEER UNDER THE LAWS OF THE STATE OF MARYLAND.

SIGNATURE

DATE


SEAL

LICENSE NO.

EXPIRATION DATE

REVISIONS

— NONE —

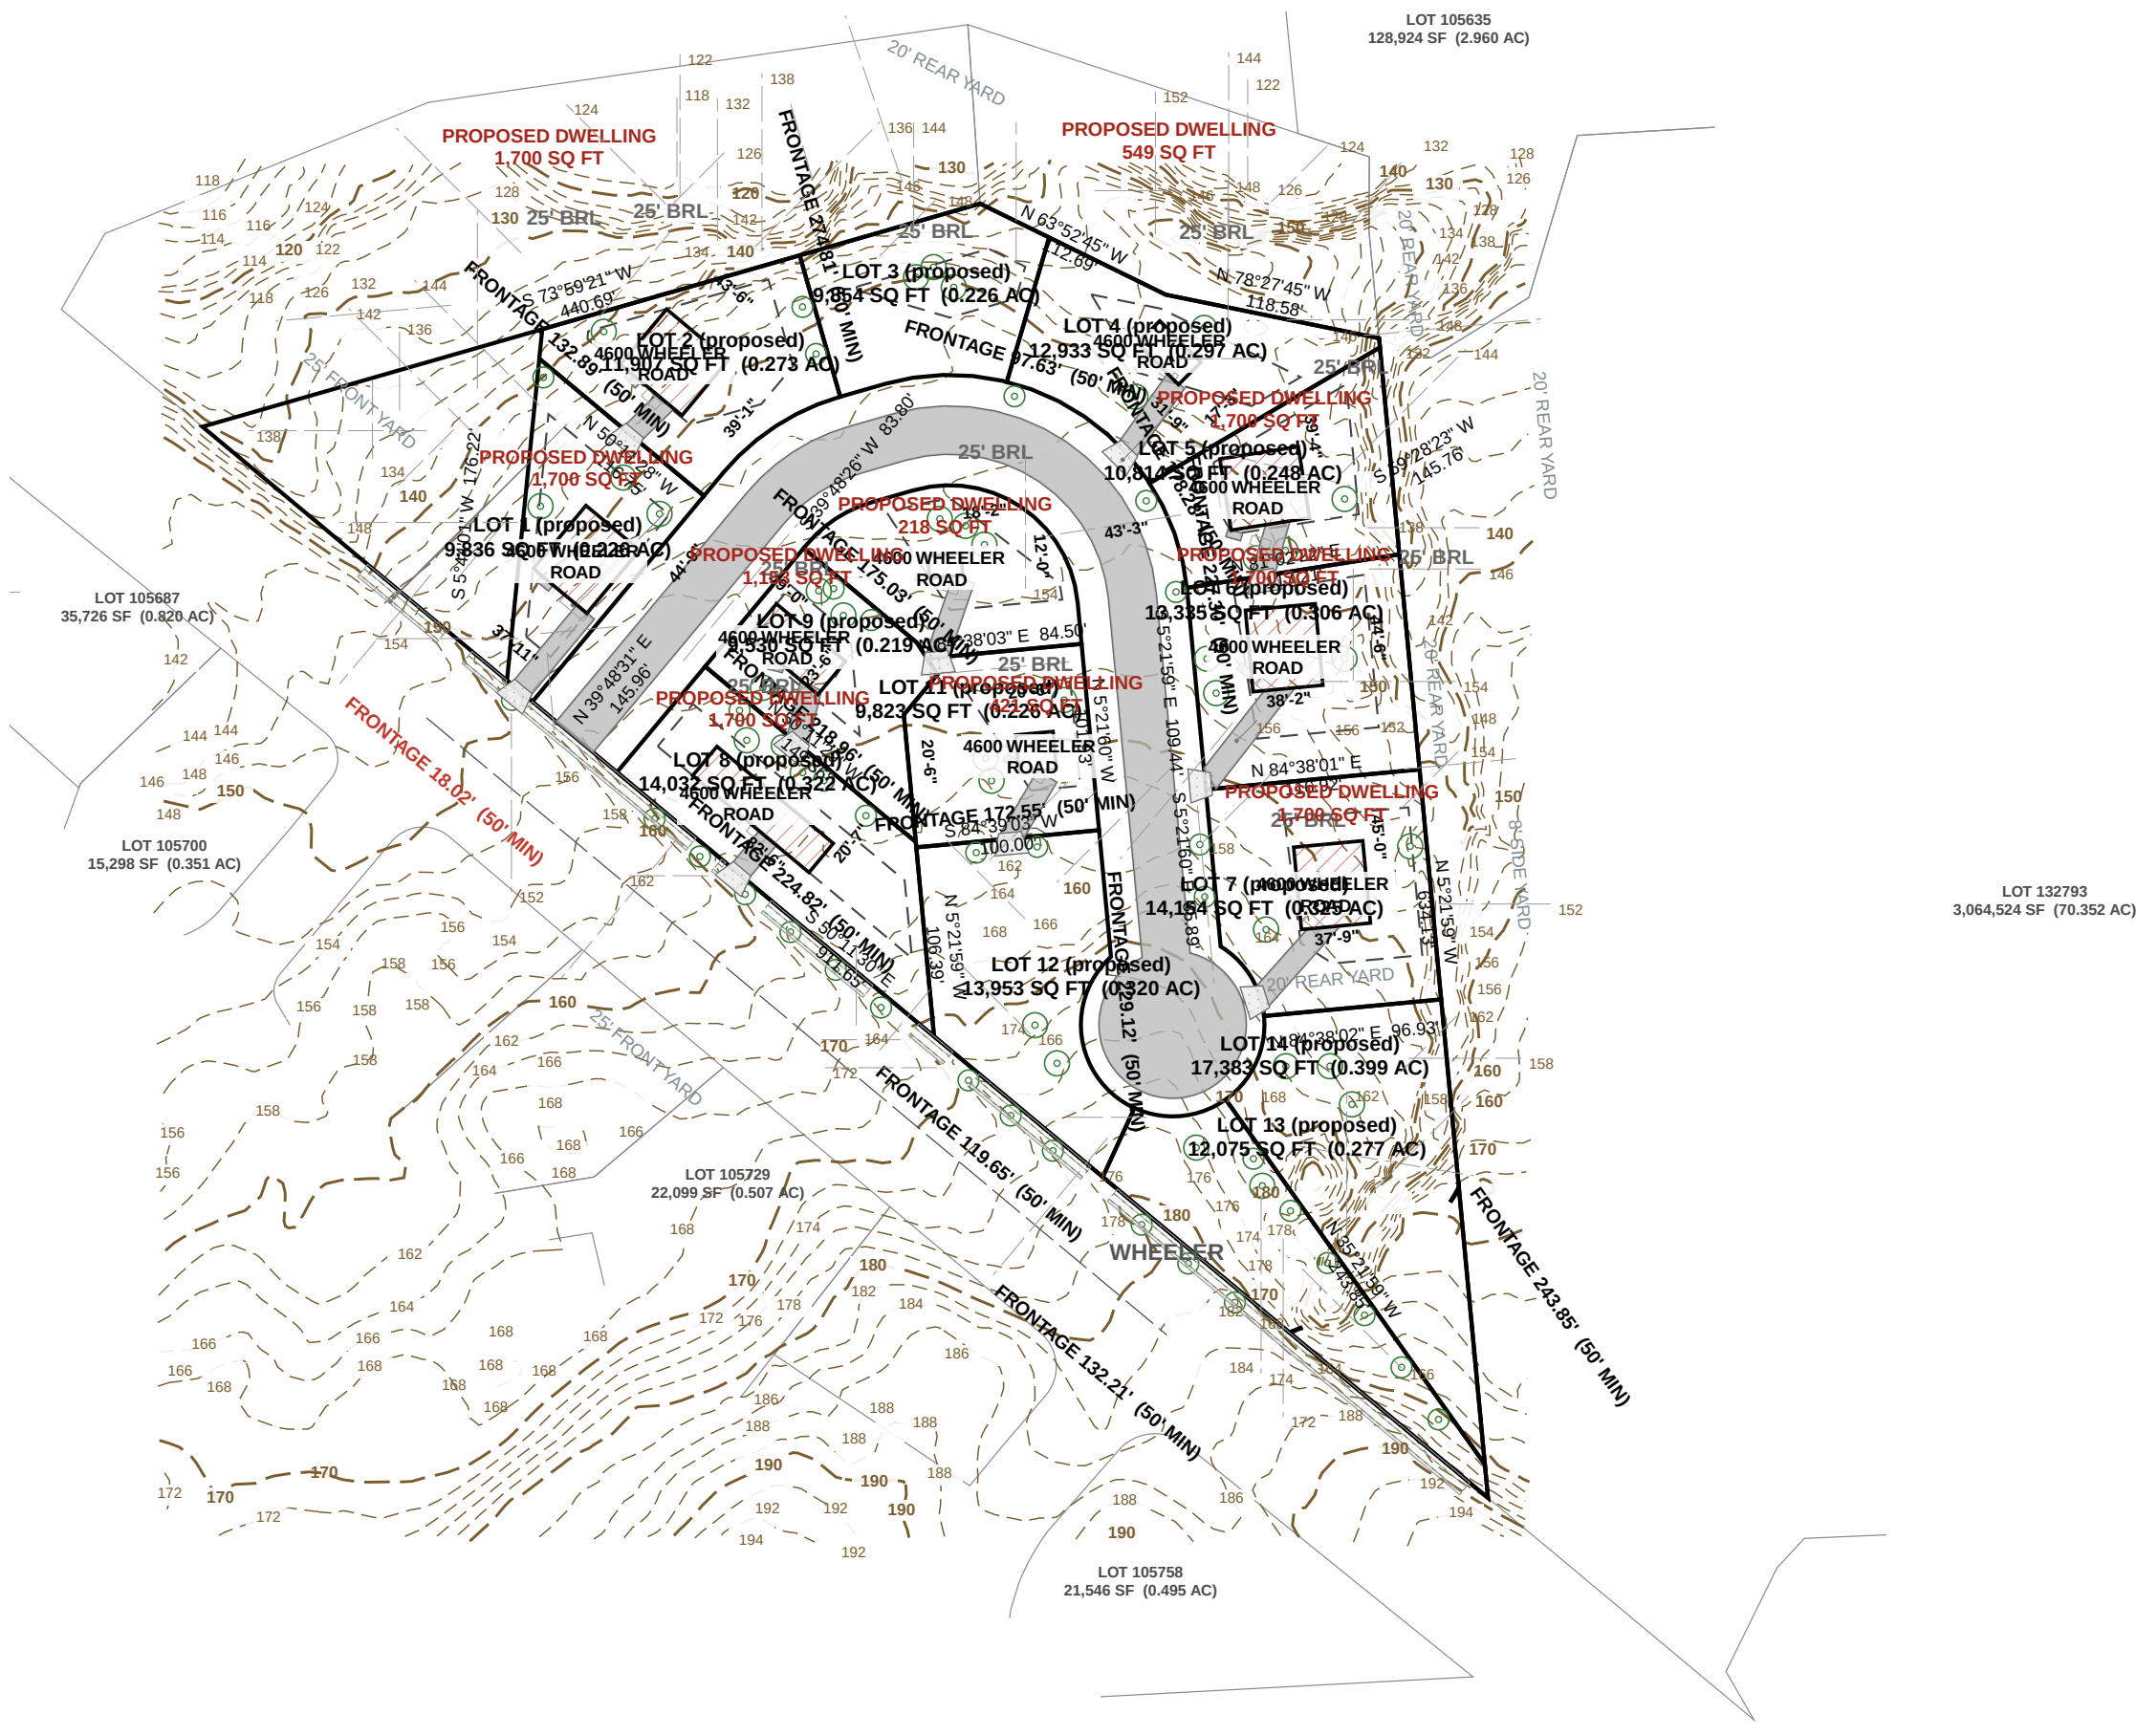

TREE CANOPY SCHEDULE

Sec. 25-128 Table 1 as amended by CB-021-2024 — 20% of NET tract area on RSF-95, met within 1-ft. Per lot planting per Landscape Manual Sec. 4.1(c)(1). Street trees in the right-of-way count toward canopy under Sec. 25-129.

LOT	NET AREA SF	CANOPY REQ 20% SF	SHADE PROV / REQ	ORN-EVGN PROV / REQ	STREET TREES	10-YR CANOPY PROVIDED
LOT 1 (proposed)	9,836	1,967	3/3	0/2 SHORT	1	NOT ESTABLISHED
LOT 2 (proposed)	11,907	2,381	1/3 SHORT	0/2 SHORT	1	NOT ESTABLISHED
LOT 3 (proposed)	9,854	1,971	3/3	0/2 SHORT	2	NOT ESTABLISHED
LOT 4 (proposed)	12,933	2,587	2/3 SHORT	0/2 SHORT	1	NOT ESTABLISHED
LOT 5 (proposed)	10,814	2,163	3/3	0/2 SHORT	1	NOT ESTABLISHED
LOT 6 (proposed)	13,335	2,667	3/3	0/2 SHORT	1	NOT ESTABLISHED
LOT 7 (proposed)	14,154	2,831	2/3 SHORT	0/2 SHORT	2	NOT ESTABLISHED
LOT 8 (proposed)	14,032	2,806	2/3 SHORT	0/2 SHORT	6	NOT ESTABLISHED
LOT 9 (proposed)	9,530	1,906	3/3	0/2 SHORT	4	NOT ESTABLISHED

* 6 further rows(s) — see the accompanying schedule

TEN-YEAR CANOPY IS CREDITED PER SPECIES FROM THE PRINCE GEORGE'S COUNTY LANDSCAPE MANUAL. NO SPECIES HAS BEEN SELECTED ON THIS SET. SO THE CANOPY PROVIDED IS NOT ESTABLISHED AND THE SCHEDULE IS NOT YET BALANCED. EXISTING TREES PRESERVED ALSO COUNT.


NO TREE IS PLANTED WITHIN A STORM DRAIN EASEMENT; THE 60 FT 54% EASEMENT CARRIES THE 42 IN RCP MAIN AND THE 10 FT REAR EASEMENT CARRIES THE DRAINAGE SWALE. BOTH ARE SHOWN ON THIS SHEET AND BOTH ARE EXCLUDED FROM PLANTABLE AREA.

A MAJOR OR THE CANOPY REQUIREMENT IS AVAILABLE UNDER SEC. 25-130.

PER LOT PLANTING IS SHORT ON EVERY LOT AS DRAWN. LANDSCAPE MANUAL, SEC. 4.1(c)(1) REQUIRES A MAJOR SHADE AND 3 ORNAMENTAL, OR EVERGREEN TREES ON A LOT OF 20,000 SF OR MORE, AND 3 AND 1 ON A LOT OF 9,500 TO 19,999 SF. NO ORNAMENTAL, OR EVERGREEN TREES ARE DRAWN. AT LEAST ONE SHADE TREE MUST STAND ON THE SOUTH OR WEST SIDE WITHIN 30 FT OF THE DWELING, AND AT LEAST ONE REQUIRED TREE IN THE FRONT YARD. SPECIES AND FINAL LOCATIONS BY THE LANDSCAPE ARCHITECT.

THE CANOPY REQUIREMENT MUST BE MET ON-SITE UNLESS A VARIANCE IS APPROVED, AND WHERE A GRADING PERMIT IS THE ONLY APPLICATION THE CANOPY NOTES ARE LONG ON THE GRADING PLAN — ENVIRONMENTAL TECHNICAL MANUAL PART D, SEC. 3.0.

CONCRETE CURB AND GUTTER — PGC DPW&T STD. 300.01

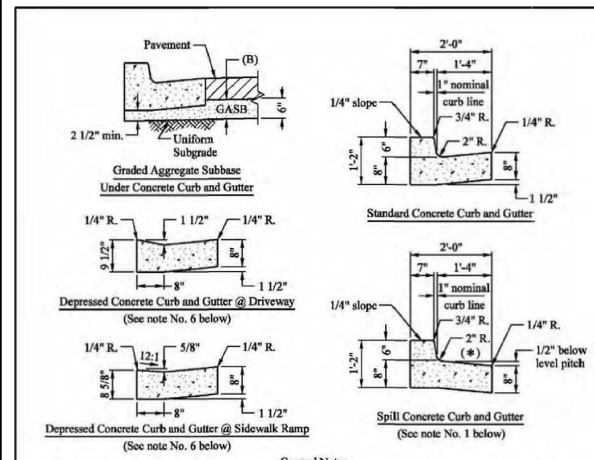


1. Use of gullies, concrete curb and gutter requires special Department approval, except for "Urban Major Collector" and "Urban Minor Collector".
2. The gully shall be 18" wide, 18" deep, and 18" high, with a 1/2" slope to the curb face.
3. All concrete curb and gutter shall be 18" high, 18" wide, and 18" deep, with a 1/2" slope to the curb face.
APPROVED: [Signature] DATE: [Date]
REVISION: [Signature] DATE: [Date]

DEPARTMENT OF PUBLIC WORKS AND TRANSPORTATION
Prince George's County, MD
Concrete Curb and Gutter
300.01

Version: 03/2012
Specification and Standards for Roadways and Bridges
Section B - 61
REPRODUCED FROM THE PGC DPW&T STANDARD THE STANDARD GOVERNS.

CONCRETE SIDEWALK RAMP TYPE A — PGC DPW&T STD. 300.07

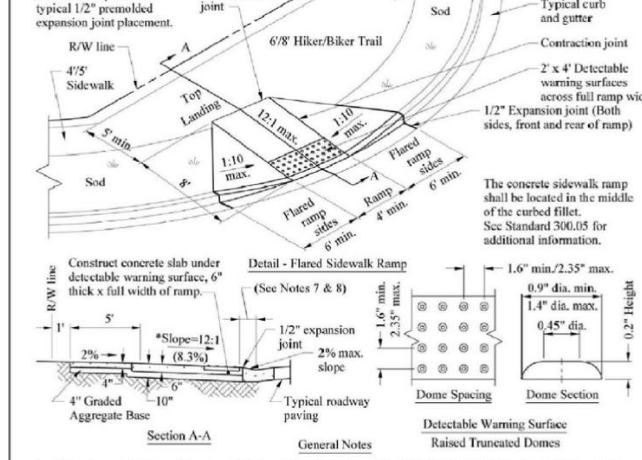


1. All new concrete sidewalk ramps and depressed curbs constructed within the County right-of-way shall comply with the Federal accessibility guidelines of the Americans with Disabilities Act. See Section 300.01 for depressed curb requirements.
2. All sidewalk ramps and front approaches shall be designed and constructed so that water will not accumulate on sidewalk ramp surfaces.
3. The sidewalk ramp shall be constructed with the base parallel to the curb face, and to exceed 12.5% slope.
4. All concrete shall be Class II (MSHA No. 1) air-entrained, unless otherwise approved by the Department. The surface shall be broom finish.
5. The sidewalk ramp shall be 18" wide, 18" high, and 18" deep, with a 1/2" slope to the curb face.
APPROVED: [Signature] DATE: [Date]
REVISION: [Signature] DATE: [Date]

DEPARTMENT OF PUBLIC WORKS AND TRANSPORTATION
Prince George's County, MD
Concrete Sidewalk Ramp Type "A"
300.07

Version: 03/2012
Specification and Standards for Roadways and Bridges
Section B - 61
REPRODUCED FROM THE PGC DPW&T STANDARD THE STANDARD GOVERNS.

GRAPHIC SCALE — 1" = 100'

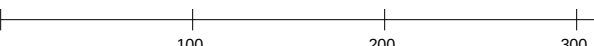



KEALEE

Design, build, deliver

PROJECT
4600 WHEELER ROAD — PRELIMINARY SUBDIVISION CONCEPT — LOTS 1-14 (proposed)

ADDRESS
4600 WHEELER ROAD

JURISDICTION
Prince George's County, Maryland

ZONE
RSF-95

SHEET
C-400 — Grading and Drainage Plan

SCALE
1" = 100'

STATUS
PRELIMINARY

SHEET NO.
3 OF 3

COORDINATES
EPSG:2248
H: NAD83
V: NAVD88 (feet)

PLAN TYPE AND PREPARATION

PLAN TYPE SITE DEVELOPMENT / FINE GRADING
SHEET C-400 — Grading and Drainage Plan
DISCIPLINE Maryland Professional Engineer
DRAWN BY KEALEE SITE-PLAN ENGINEER
DESIGNED BY
CHECKED BY

REVISIONS

NO.	DATE	DESCRIPTION

INDEX OF DRAWINGS

- 1 C-001 Site Development Plan — Existing, Proposed, Grading, Paving and
2 L-100 Landscape and Tree Canopy Plan
3 C-400 Grading and Drainage Plan

SITE DATA

ZONE	RSF-95
TAX / PARCEL ID	230,997 SF
GROSS TRACT AREA	5,303 AC
LOT 1 (proposed) AREA	9,836 SF 0.226 AC
LOT 2 (proposed) AREA	11,907 SF 0.273 AC
LOT 3 (proposed) AREA	9,854 SF 0.226 AC
LOT 4 (proposed) AREA	12,933 SF 0.297 AC
LOT 5 (proposed) AREA	10,814 SF 0.248 AC
LOT 6 (proposed) AREA	13,335 SF 0.306 AC
LOT 7 (proposed) AREA	14,154 SF 0.325 AC
LOT 8 (proposed) AREA	14,032 SF 0.322 AC
LOT 9 (proposed) AREA	9,530 SF 0.219 AC
LOT 10 (proposed) AREA	9,746 SF 0.224 AC
LOT 11 (proposed) AREA	9,823 SF 0.226 AC
LOT 12 (proposed) AREA	13,953 SF 0.320 AC
LOT 13 (proposed) AREA	12,075 SF 0.277 AC
LOT 14 (proposed) AREA	17,383 SF 0.399 AC
NET LOT AREA	169,374 SF 3.888 AC
LOT 1 (proposed) FRONTAGE	50' MIN
LOT 2 (proposed) FRONTAGE	50' MIN
LOT 3 (proposed) FRONTAGE	50' MIN
LOT 4 (proposed) FRONTAGE	50' MIN
LOT 5 (proposed) FRONTAGE	50' MIN
LOT 6 (proposed) FRONTAGE	50' MIN
LOT 7 (proposed) FRONTAGE	50' MIN
LOT 8 (proposed) FRONTAGE	50' MIN
LOT 9 (proposed) FRONTAGE	50' MIN
LOT 10 (proposed) FRONTAGE	50' MIN
LOT 11 (proposed) FRONTAGE	50' MIN
LOT 12 (proposed) FRONTAGE	50' MIN
LOT 13 (proposed) FRONTAGE	50' MIN
LOT 14 (proposed) FRONTAGE	50' MIN
SETBACKS	REQUIRED PROVIDED
FRONT YARD	25' 25'
SIDE YARD	5' 5'
REAR YARD	20' 20'
COVERAGE	MAX PROPOSED
LOT COVERAGE	30% 7.4%
BUILDING FOOTPRINT	— 12,541 SF
DATUM	
HORIZONTAL	EPSG:2248 NAD83
VERTICAL	NAVD88 (feet)

SITE ANALYSIS

1. Gross tract area 230,997 SF
2. Area of dwelling 12,541 SF
3. Wooded area NOT ESTABLISHED
4. Floodplain area NOT ESTABLISHED
5. Net lot area 169,374 SF
6. TOTAL AREA DISTURBED 115,032 SF (AT LEAST)
7. SWM REQUIRED — Sec. 32-174(a)(3) YES — DISTURBANCE EXCEEDS 5,000 SF

BUILDING DATA

	G	B	FF	SF	HT	STY
LOT 1 (proposed)	155.63	—	155.96	154.96	20'	2
LOT 2 (proposed)	149.62	—	149.95	148.95	20'	2
LOT 4 (proposed)	153.00	—	153.33	152.33	20'	2
LOT 5 (proposed)	157.64	—	157.97	156.97	20'	2
LOT 6 (proposed)	159.65	—	159.98	158.98	20'	2
LOT 7 (proposed)	169.27	—	169.70	168.70	20'	2
LOT 8 (proposed)	163.93	—	164.26	163.26	20'	2
LOT 9 (proposed)	161.84	—	161.97	160.97	20'	2
LOT 10 (proposed)	159.62	—	159.95	158.95	20'	2
LOT 11 (proposed)	163.90	—	164.23	163.23	20'	2

G garage slab; B basement; FF finished floor; SF subfloor; HT height; STY stories. A DASH IS NOT ZERO; the elevation has not been established and must be set from a field-run topographic survey before construction.

DRAINAGE AREA COMPUTATIONS

CATCHMENT	AREA SF	IMPERV.	PPE Q	POST Q	INCREASE	WQV CF
LOT 1 (proposed)	9,836	25.3%	0.38	0.65	0.27	228
LOT 2 (proposed)	11,907	17.6%	0.46	0.68	0.22	207
LOT 3 (proposed)	9,854	0.0%	0.38	0.38	0.00	41
LOT 4 (proposed)	12,933	9.3%	0.50	0.63	0.13	145
LOT 5 (proposed)	10,814	19.8%	0.42	0.65	0.23	206
LOT 6 (proposed)	13,335	18.9%	0.51	0.79	0.28	245
LOT 7 (proposed)	14,154	17.1%	0.55	0.80	0.25	240
LOT 8 (proposed)	14,032	14.9%	0.54	0.77	0.23	215
LOT 9 (proposed)	9,530	17.0%	0.37	0.54	0.17	162
LOT 10 (proposed)	9,746	8.6%	0.38	0.47	0.09	103
LOT 11 (proposed)	9,823	10.0%	0.38	0.48	0.10	114
LOT 12 (proposed)	13,953	0.0%	0.54	0.54	0.00	58
LOT 13 (proposed)	12,075	0.0%	0.47	0.47	0.00	50
LOT 14 (proposed)	17,383	0.0%	0.67	0.67	0.00	72
PROJECT TOTAL	169,374	10.9%	6.55	8.52	1.97	2,066


Peak flows are summed for catchments; Q in cfs; WQV is the required water-quality volume.

PROFESSIONAL CERTIFICATION

I HEREBY CERTIFY THAT THESE DOCUMENTS WERE PREPARED OR APPROVED BY ME, AND THAT I AM A DULY LICENSED PROFESSIONAL ENGINEER UNDER THE LAWS OF THE STATE OF MARYLAND.

SIGNATURE	DATE
LICENSE NO.	EXPIRATION DATE
SEAL	


IF REQUIRED NOTE(S) DO NOT FIT THIS SHEET, GRADING CERTIFICATE; STABILIZATION COMPLIANCE PREAMBLE; STANDARD STABILIZATION NOTE. THEY ARE REQUIRED AND ARE NOT ON ANY SHEET IN THIS SET.

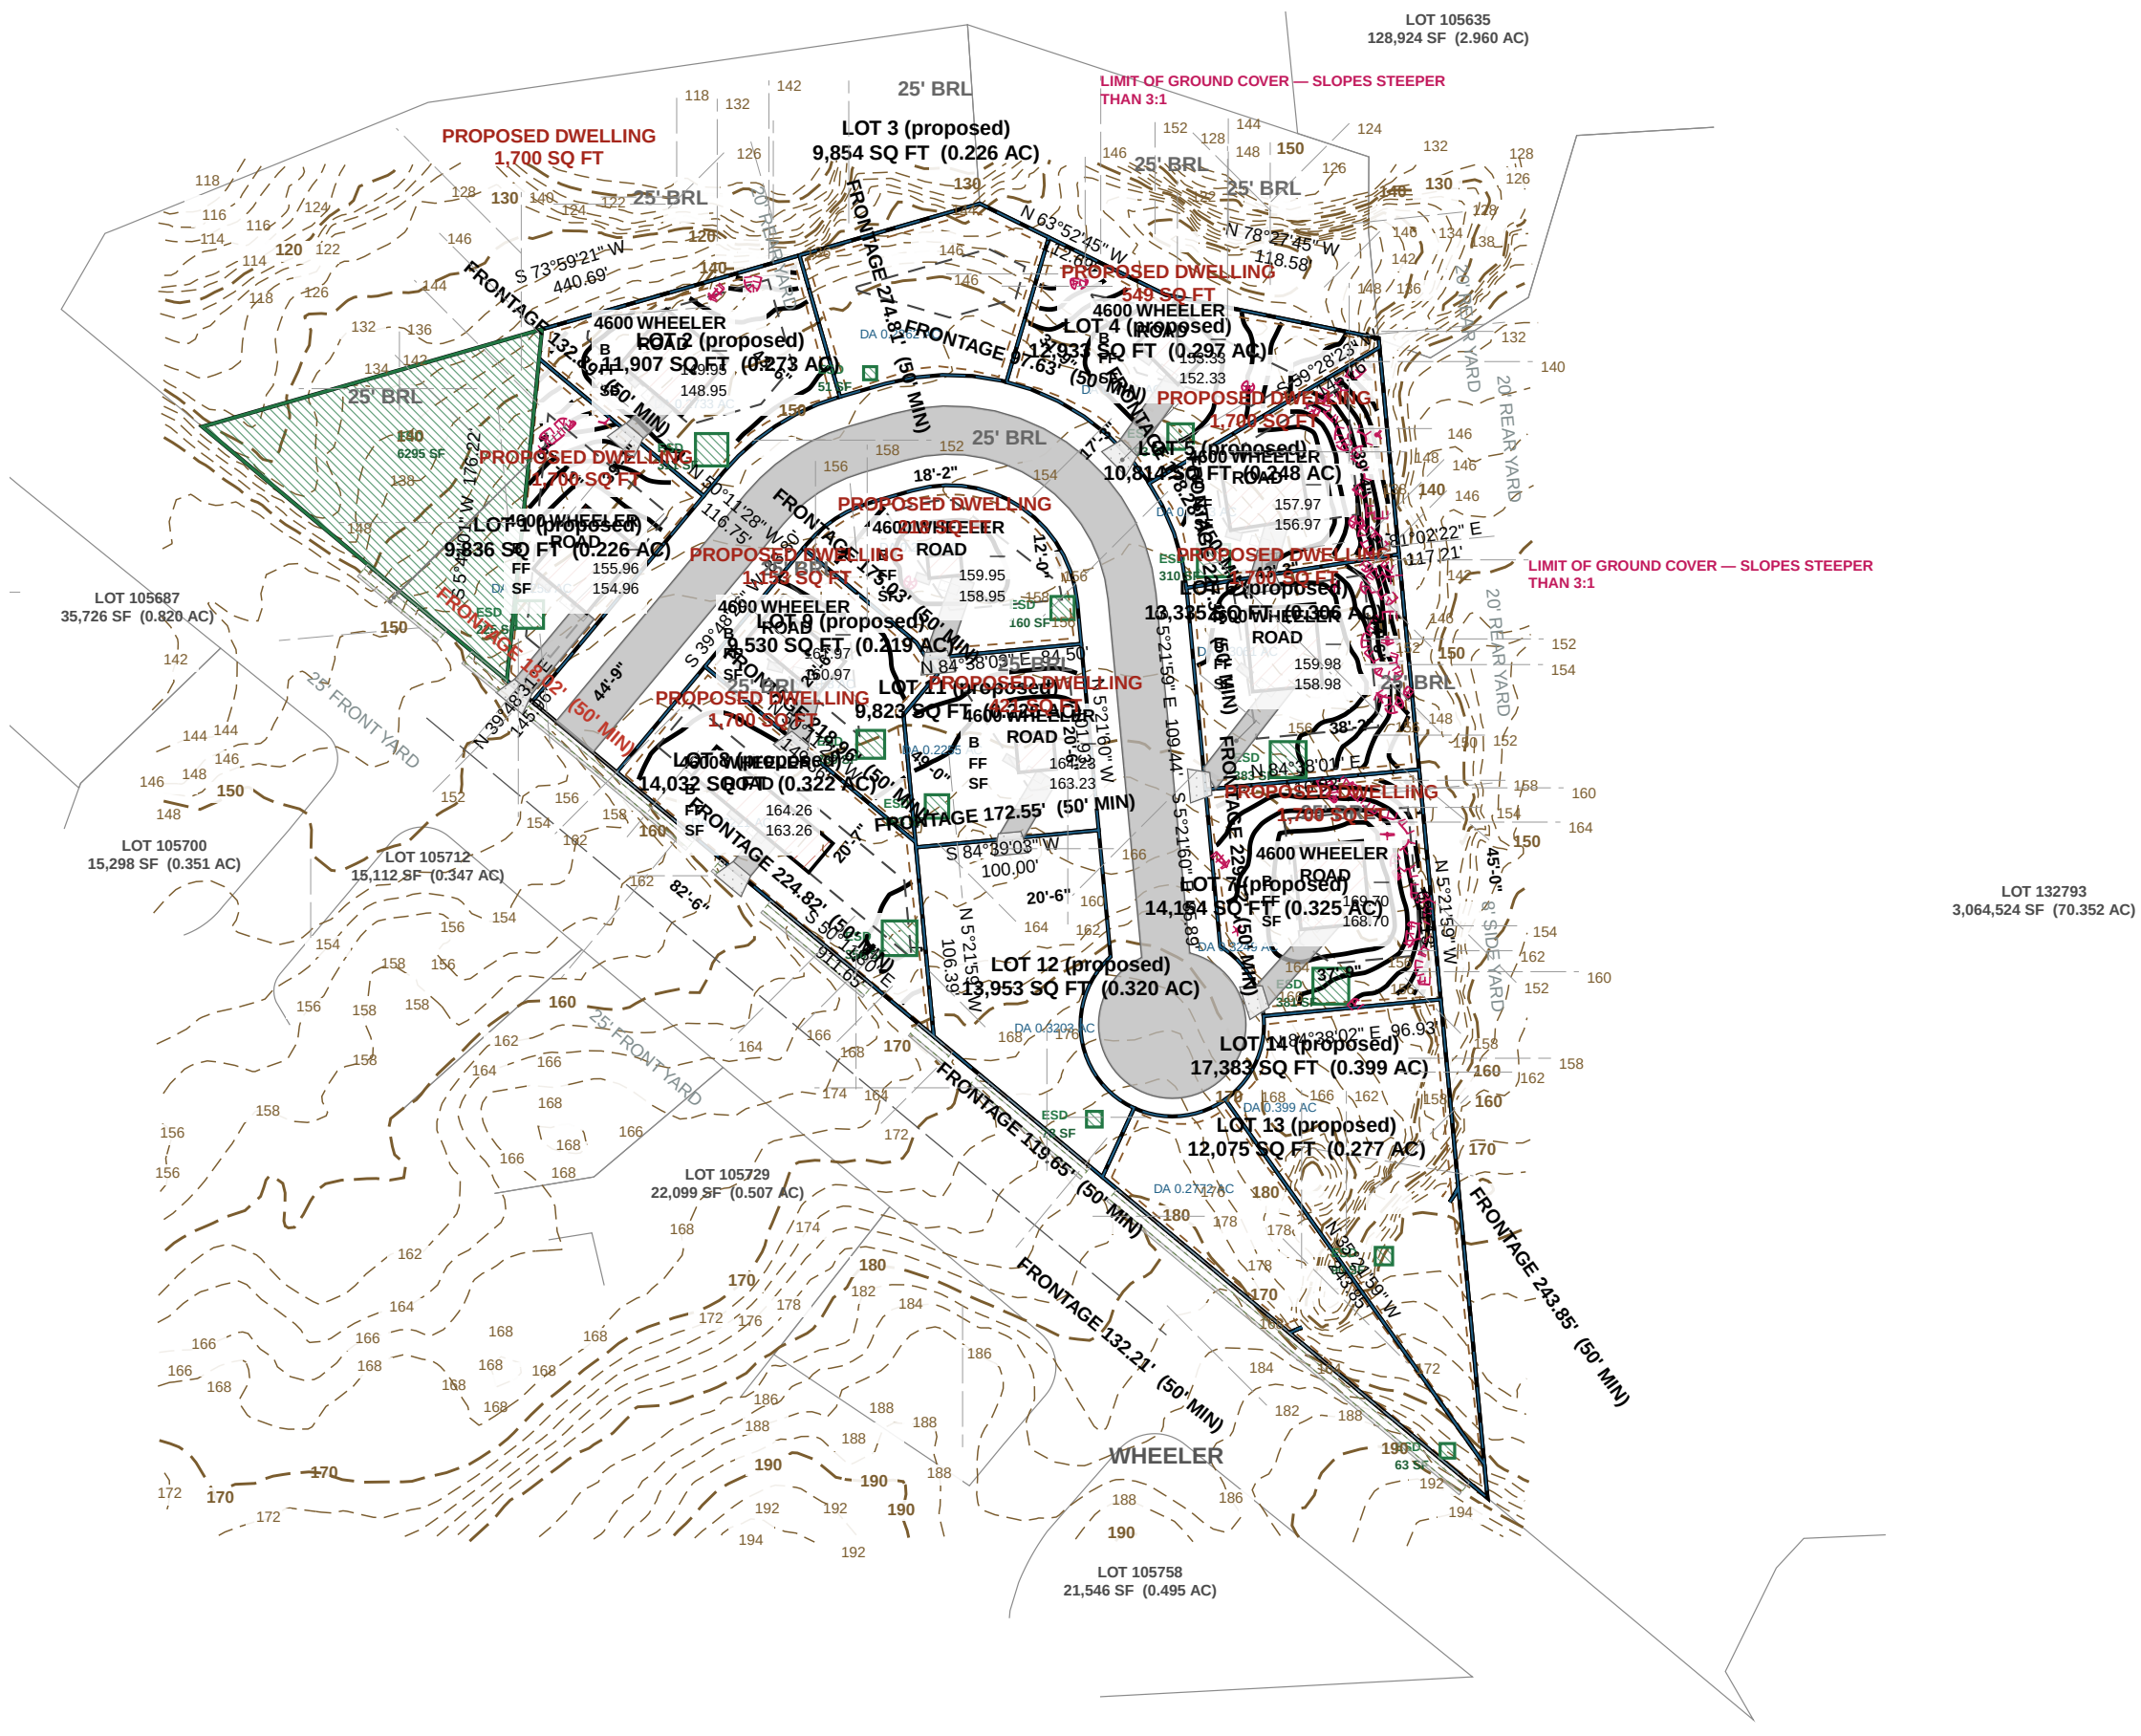

SOILS STABLE USDA NRCS SSURGO — PGC Code Sec. 32-133(a)(13)

MAP UNIT	MAP UNIT NAME	K-FACT	HYDRIC	HYD. GRP	DRAINAGE CLASS
AaB	Adelphia silt loam, 2 to 5 percent slopes complex	37	No	C	Moderately well drained
AcA	Adelphia-Aquasco complex, 0 to 2 percent slopes	43	No	D	Somewhat poorly drained
AdA	Adelphia-Holmdel complex, 0 to 2 percent slopes	24	No	B/D	Somewhat poorly drained
AdB	Adelphia-Holmdel complex, 2 to 5 percent slopes	24	No	B/D	Somewhat poorly drained
AdC	Adelphia-Holmdel complex, 5 to 10 percent slopes	24	No	B/D	Somewhat poorly drained

CONCRETE CURB AND GUTTER — PGC DPW&T STD. 300.01

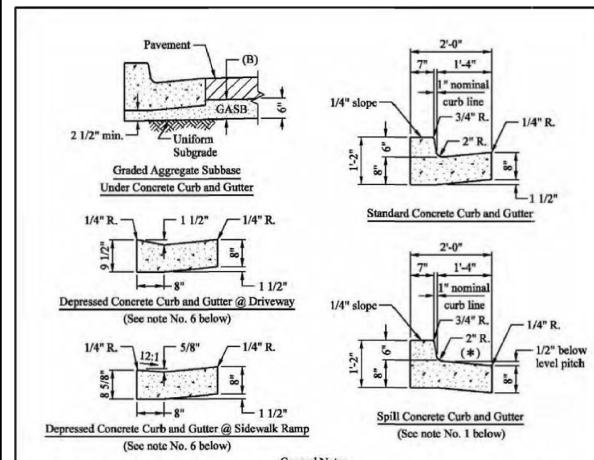


1. Use of gullies, concrete curb and gutter systems, and drainage systems, except for "Urban Major Collector Road" design.
2. The design of gullies, concrete curb and gutter shall be such as to provide for the proper drainage of storm water.
3. The design of gullies, concrete curb and gutter shall be such as to provide for the proper drainage of storm water.
4. All proposed gullies shall be located at 10' intervals. The concrete curb shall be constructed to a depth of 12" below the finished grade.
5. All concrete shall be Class (ASTM A638, No. 3) unadorned, unless otherwise approved by the Department. The concrete shall be finished with a broom.
6. The concrete curb and gutter shall be installed in a trench 12" deep and 12" wide, with the bottom of the trench 12" below the finished grade.
APPROVED	DATE	DEPARTMENT OF PUBLIC WORKS AND TRANSPORTATION Prince George's County, MD
DESIGNED BY	APPROVED BY	Concrete Curb and Gutter
300.01		

REPRODUCED FROM THE PGC DPW&T STANDARD THE STANDARD GOVERNS.

CONCRETE SIDEWALK RAMP TYPE A — PGC DPW&T STD. 300.07

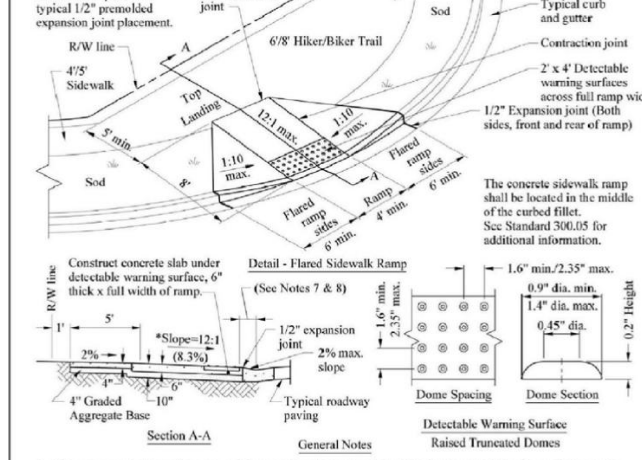

1. All new concrete sidewalk ramps and depressed curbs constructed within the County right-of-way shall comply with the Federal accessibility guidelines of the Americans with Disabilities Act. See Standard 300.01 for additional requirements.
2. All sidewalk ramps and curb systems shall be designed and constructed so that water will not accumulate on the sidewalk surface.
3. The sidewalk ramp shall be constructed with the base material having a slope of 1:12.
4. All concrete shall be Class (ASTM A638, No. 3) unadorned, unless otherwise approved by the Department.
5. The concrete sidewalk ramp shall be installed in a trench 12" deep and 12" wide, with the bottom of the trench 12" below the finished grade.
APPROVED	DATE	DEPARTMENT OF PUBLIC WORKS AND TRANSPORTATION Prince George's County, MD
DESIGNED BY	APPROVED BY	Concrete Sidewalk Ramp Type "A"
300.07		

REPRODUCED FROM THE PGC DPW&T STANDARD THE STANDARD GOVERNS.