


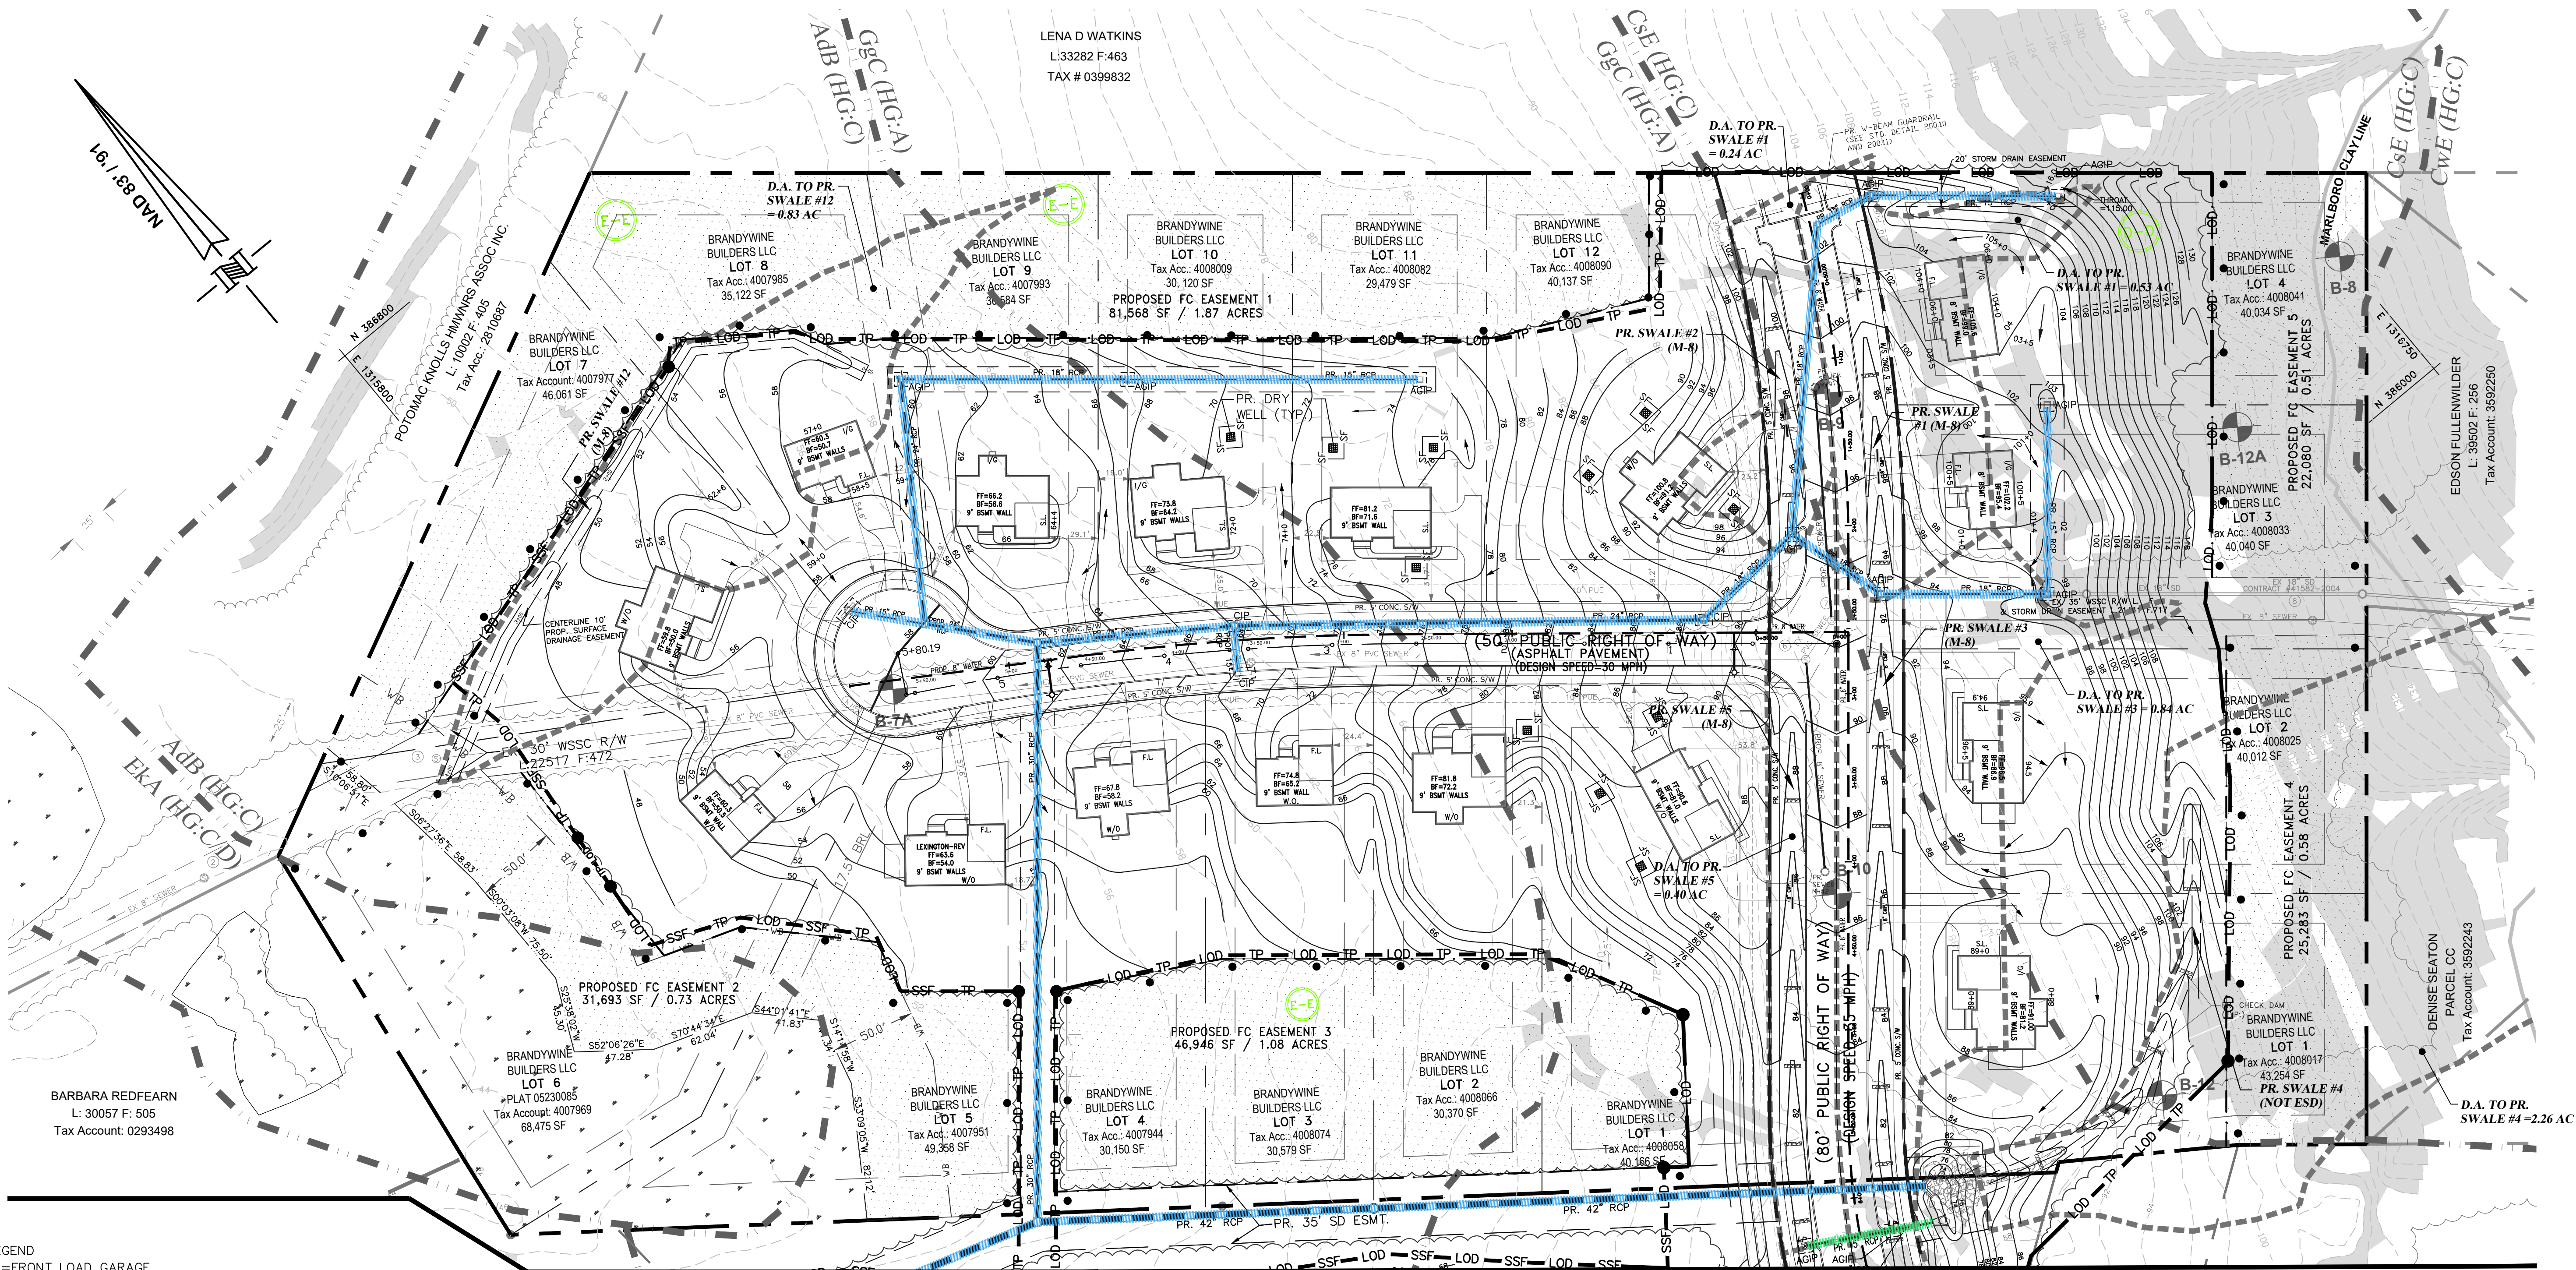

LEGEND
FL=FRONT LOAD GARAGE
SL=SIDE LOAD GARAGE
I/G=IN GROUND BASEMENT
W/O=WALK OUT BASEMENT

LEGEND

TITLE	SYMBOL	PROPERTY BOUNDARY	---
SOILS DIVIDE	---	EXISTING 10' CONTOUR	---
LIMIT OF DISTURBANCE	---	EXISTING 2' CONTOUR	---
SOILS LABELS	CsE	WETLAND BUFFER	WB
WETLAND	---	TREE LINE	---
SOIL BORINGS	B-7	PRIMARY MANAGEMENT AREA BOUNDARY	PMA
FOREST CONSERVATION (FC)	---	EX. SEWER EASEMENT	---
DRY WELL	---	ROAD CENTER LINE	---
PR. INLET PROTECTION (AT GRADE)	ACIP	EX. SEWER PIPE	---
PR. CURB INLET PROTECTION	CIP	PR. SILT FENCE	SF
PR. LOD & TREE PROTECTION	TP LOD	PR. LIMIT OF DISTURBANCE	LOD
PR. SSF & LOD	SSF LOD	DRAINAGE AREA TO ESD	---
PR. FOREST CONSERVATION SIGN	---	STEEP SLOPES (15% OR GREATER)	---

FOREST CONSERVATION AREAS	
NO	AREA
1	81,568 SF OR 1.87 AC
2	31,693 SF OR 0.73 AC
3	46,946 SF OR 1.08 AC
4	22,080 SF OR 0.51 AC
5	25,283 SF OR 0.58 AC

BRANDYWINE BUILDERS RESPONSIBILITY	---
LIVINGSTON OF FORT WASHINGTON, LLC RESPONSIBILITY	---
SHARED RESPONSIBILITY	---

* LIVINGSTON OF FORT WASHINGTON IS RESPONSIBLE FOR ALL ON-SITE SHOPPING CENTER STORM DRAIN SYSTEM WHICH IS NOT REQUIRED TO BE BUILT IN THIS PHASE.

REVISIONS	BY



ELITE ENGINEERING, LLC
Engineers * Landscape Architects
6305 IVY LANE SUITE 370
GREENBELT, MD, 20770
(240)206-8055

ARAGONA VILLAGE / LIVINGSTON OF FORT WASHINGTON

STORM DRAIN EXHIBIT

FORT WASHINGTON, PRINCE GEORGES COUNTY, MD
TAX MAP 13, GRID 92
5TH ELECTION DISTRICT

DRAWN AT
CHECKED AM
DATE 6/2/2020
SCALE AS SHOWN

DRAWING

1 OF 2

PROFESSIONAL CERTIFICATION: I HEREBY CERTIFY THAT THESE DOCUMENTS WERE PREPARED OR APPROVED BY ME, AND THAT I AM A DULY LICENSED PROFESSIONAL ENGINEER UNDER THE LAWS OF THE STATE OF MARYLAND, LICENSE NO. 11432, EXPIRATION 04/29/2021.