


EXHIBIT D

MATCH LINE SEE SHEET #2

MATCH LINE SEE SHEET #2

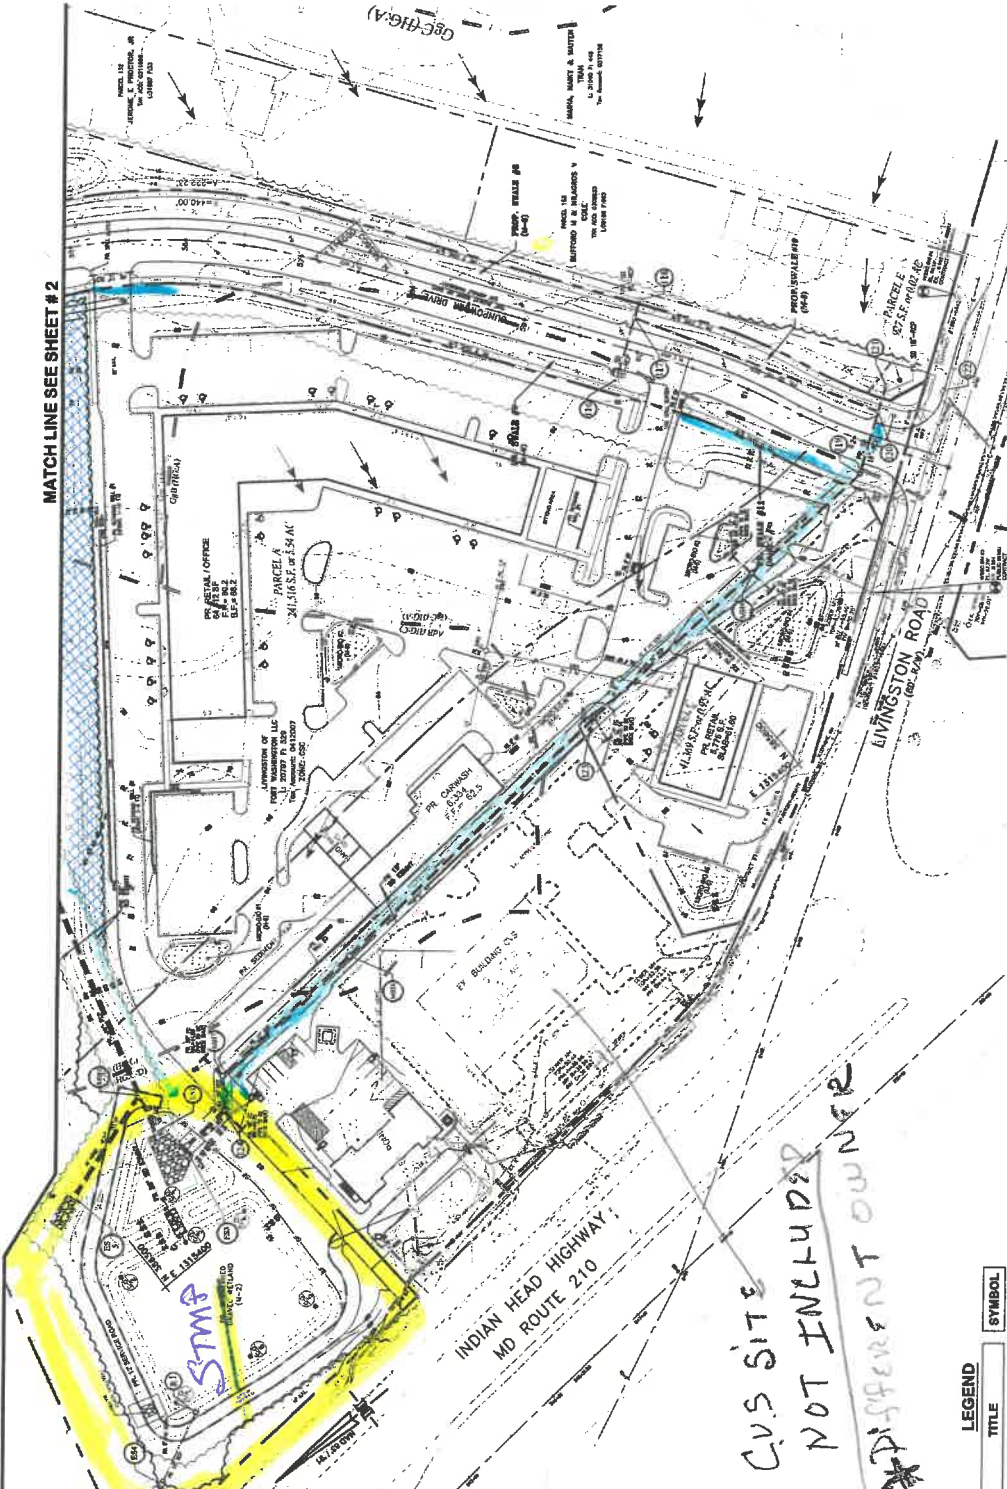

TYPICAL STREET SECTION - GUNPOWDER DR



TYPICAL STREET SECTION - SCHOONER COURT



LEGEND	TITLE	SYMBOL
PROPERTY BOUNDARY		
EXISTING CONTOUR		
EXISTING CONTOUR		
WETLAND BUFFER		
SOILS DIVIDE		
WETLAND		
SOILS LABELS		
SECONDARY OVERFLOW PATH FOR THE 100-YEAR STORM		
FLOODPLAIN LIMITS		
RIP RAP		

NOT TO SCALE

SCALE 1" = 50'

REVISIONS	BY



ELITE ENGINEERING, LLC
 Engineers & Landscapers Architects
 5305 Ivy Lane Suite 370
 Greenbelt, Maryland 20770
 (240) 206-8055



ARAGONA VILLAGE - PHASE II
STORM DRAIN AND PAVING PLAN
STORM DRAIN PLAN VIEW
 11-12-2020

DESIGNED	
CHECKED	
DATE	06/27/2023
SCALE	AS SHOWN
DRAWING	

SDP-3