

KEALEE

Design, build, deliver

PROJECT
Indian Queen East — LOT 53 & LOT 54 & LOT 55 & LOT 56
ADDRESS
9588 Fort Foote Rd · 9584 Fort Foote Rd · 9580 Fort Foote Rd · 9576 Fort Foote Rd
JURISDICTION
Prince George's County, Maryland
ZONE
RSF-95
SHEET
C-001 — Site Development Plan — Existing, Proposed, Grading, Paving and Landscape
SCALE
1" = 30'
STATUS
PRELIMINARY
SHEET NO.
1 OF 3
COORDINATES
EPSG:2248
H: NAD83
V: NAVD88 (feet)

PLAN TYPE AND PREPARATION

PLAN TYPE SITE DEVELOPMENT / FINE GRADING
SHEET C-001 — Site Development Plan — Existing, Proposed, Grading, Paving and Landscape
DISCIPLINE Maryland Professional Engineer / Surveyor (see divided responsibility)
DRAWN BY KEALEE SITE-PLAN ENGINEER
DESIGNED BY
CHECKED BY

REVISIONS

NO.	DATE	DESCRIPTION

SITE DATA

ZONE	RSF-95
TAX / PARCEL ID	—
GROSS TRACT AREA	75,178 SF 1.726 AC
LOT 53 AREA	12,389 SF 0.284 AC
LOT 54 AREA	23,371 SF 0.537 AC
LOT 55 AREA	25,733 SF 0.591 AC
LOT 56 AREA	13,690 SF 0.314 AC
NET LOT AREA	75,184 SF 1.726 AC
LOT 53 FRONTAGE	50' MIN 83.07'
LOT 54 FRONTAGE	50' MIN 173.55'
LOT 55 FRONTAGE	50' MIN 131.07'
LOT 56 FRONTAGE	50' MIN 84.20'
SETBACKS	REQUIRED PROVIDED
FRONT YARD	30' 30'
SIDE YARD	8' 8'
REAR YARD	20' 20'
COVERAGE	MAX PROPOSED
LOT COVERAGE	30% 6.4%
BUILDING FOOTPRINT	— 4,784 SF
DATUM	
HORIZONTAL	EPSG:2248 NAD83
VERTICAL	NAVD88 (feet)

SITE ANALYSIS

1. Gross tract area	75,178 SF
2. Area of dwelling	4,784 SF
3. Wooded area	NOT ESTABLISHED
4. Floodplain area	NOT ESTABLISHED
5. Net lot area	75,184 SF
6. TOTAL AREA DISTURBED	41,662 SF (AT LEAST)
7. SWM REQUIRED — Sec. 32-174(a)(3)	YES — DISTURBANCE EXCEEDS 5,000 SF

BUILDING DATA

	G	B	FF	SF	HT	STY
9588 Fort Foote Rd	58.89	50.22	59.22	58.22	20'	2
9584 Fort Foote Rd	55.64	46.97	55.97	54.97	20'	2
9580 Fort Foote Rd	55.67	47.00	56.00	55.00	20'	2
9576 Fort Foote Rd	60.68	52.01	61.01	60.01	20'	2

G: garage slab · B: basement · FF: finished floor · SF: subfloor · HT: height · STY: storeys. A DASH IS NOT ZERO; the elevation has not been established and must be set from a field-run topographic survey before construction.

DRAINAGE AREA COMPUTATIONS

CATCHMENT	AREA SF	IMPERV.	PRE Q	POST Q	INCREASE	WQV CF
LOT 53	12,389	15.1%	0.49	0.69	0.20	182
LOT 54	23,371	9.4%	0.92	1.16	0.24	263
LOT 55	25,733	8.2%	1.01	1.24	0.23	266
LOT 56	13,690	14.2%	0.54	0.75	0.21	203
PROJECT TOTAL	75,184	10.9%	2.96	3.84	0.88	924

Peak flows are summed for catchments; Q in cfs. WQV is the required water-quality volume.

SEQUENCE OF CONSTRUCTION

1. Pre-construction meeting 1 DAY
2. Obtain necessary permits 2 DAYS
3. Notify Miss Utility at 811 at least 48 hours prior to any excavation 1 DAY
4. Install stabilized construction entrance and perimeter sediment control 2 DAYS
5. Rough grade the lot 5 DAYS
6. Construct dwelling 6 MONTHS
7. Install water, sewer and storm services and the driveway 10 DAYS
8. Fine grade and stabilize all disturbed areas 5 DAYS
9. Remove sediment control once the inspector gives written permission 1 DAY

TOTAL ESTIMATED TIME OF CONSTRUCTION: 8 MONTHS

GENERAL NOTES

1. CONTRACTOR SHALL CONTACT MISS UTILITY AT 811 A MINIMUM OF 48 HOURS PRIOR TO ANY EXCAVATION, FIELD-VERIFY LOCATION AND DEPTH BY TEST PIT BEFORE CONSTRUCTION.
2. ALL EXISTING AND PROPOSED UTILITIES SHOWN PER PGC CODE SEC. 32-106.
3. PROPOSED GRADE SHOWN SOLID; EXISTING GRADE SHOWN DASHED.
4. ROUGH EARTHWORK GRADES AND UTILITY ELEVATIONS SHOWN TO TENTHS OF A FOOT.
5. BOUNDARY SHOWN IS THE RECORDED PLAT OF SUBDIVISION — INDIAN QUEEN EAST — BLOCK "E" AND PARTS OF BLOCKS D & F PLAT BOOK WWW 65, P. 60 (MSA: 33299, 33299), 32TH ELECTION DISTRICT, PRINCE GEORGE'S COUNTY, MARYLAND, TAX MAP 113, BLOCK F, GRID E4, PLAT DATED 6 JUNE 1987, APPROVED 26 JUNE 1987 BY THE MARYLAND NATIONAL CAPITAL PARK & PLANNING COMMISSION, PRINCE GEORGE'S COUNTY PLANNING BOARD, M-NCPPC RECORD FILE 5197863. SCALE 1" = 100'. SURVEYOR: W. L. WICKENS, REGISTERED LAND SURVEYOR NO. 384. TOTAL SUBDIVISION AREA 20,981.1 ACRES. PLAT LEGEND: FOR PUBLIC SEWER & WATER SYSTEMS ONLY. TRANSFERRED AND CHECKED FOR CLOSURE. THE PLAT IS THE BOUNDARY SURVEY. NO FIELD TOPOGRAPHY IS INCLUDED; EXISTING GRADE IS COUNTY LIDAR CONTOUR MAPPING.
6. CONNECT TO EXISTING PAVEMENT, CURB AND GUTTER, DRIVEWAY AND SIDEWALK IN LINE AND GRADE.
7. NO DRIVEWAY CULVERT IS REQUIRED; THIS FRONTAGE IS AN EXISTING CURB AND GUTTER SECTION, NOT AN OPEN DITCH SECTION. GUTTER FLOW IS CARRIED THROUGH EACH ENTRANCE BY THE DEPRESSIONED CURB AT THE APRON PER DPW&T STD. 300.01, NOTE 8. ON LOT DRAINAGE IS COLLECTED BY THE REAR-YARD SWALE IN THE REAR DRAINAGE EASEMENT AND CROSSES NO DRIVEWAY OR APRON.

PROFESSIONAL CERTIFICATION

I HEREBY CERTIFY THAT THESE DOCUMENTS WERE PREPARED OR APPROVED BY ME, AND THAT I AM A DULY LICENSED PROFESSIONAL ENGINEER UNDER THE LAWS OF THE STATE OF MARYLAND.

SIGNATURE	DATE
LICENSE NO.	EXPIRATION DATE
SEAL	

REVISIONS

— NONE —

LOT 212710
925,520 SF (0.147 AC)

LOT 212977
42,893 SF (0.985 AC)

LOT 213010
12,124 SF (0.278 AC)

LOT 213008
12,378 SF (0.284 AC)

LOT 213093
13,704 SF (0.315 AC)

LOT 213092
10,671 SF (0.245 AC)

LOT 213091
9,002 SF (0.207 AC)

SOILS TABLE USDA NRCS SURROG — PGC Code Sec. 32-133(a)(13)

MAP UNIT	MAP UNIT NAME	K-FACT	HYDRIC	HYD. GRP	DRAINAGE CLASS
AaB	Adelphia silt loam, 2 to 5 percent slopes complex	37	No	C	Moderately well drained
AcA	Adelphia-Aquasco complex, 0 to 2 percent slopes	43	No	D	Somewhat poorly drained
AdA	Adelphia-Holmdel complex, 0 to 2 percent slopes	24	No	B/D	Somewhat poorly drained
AdB	Adelphia-Holmdel complex, 2 to 5 percent slopes	24	No	B/D	Somewhat poorly drained
AdC	Adelphia-Holmdel complex, 5 to 10 percent slopes	24	No	B/D	Somewhat poorly drained

DRAINAGE SWALE SCHEDULE Rational method, NOAA Atlas 14 · NWS-552361 0.041, 7' bottom, 3:1 sides


REACH	LENGTH	GRADE	D.A. (AC)	Q10 (CFS)	Q100 (CFS)	DEPTH	V100 (FPS)	INV IN	INV OUT	CUT
ST-1 — ST-2	110'	3.01%	0.2844	0.59	0.78	0.18'	1.73	50.20	46.90	1.0'
ST-4 — ST-3	157'	4.98%	0.3143	0.65	0.86	0.16'	2.12	60.30	52.50	1.0'
ST-3 — ST-2	177'	3.17%	0.9051	1.87	2.47	0.33'	2.51	52.50	46.90	1.0'

GRADE CONTROL SCHEDULE


POINT	LOT	DESCRIPTION	GROUND	SWALE INV
ST-1	LOT 53	Swale grade break / invert control	51.20	50.20
ST-2	LOT 54	Swale grade break / invert control	47.90	46.90
ST-3	LOT 55	Swale grade break / invert control	53.50	52.50
ST-4	LOT 56	Swale grade break / invert control	61.30	60.30
OUT	—	Swale grade break / invert control	48.90	—

SYSTEM AT THE LOW POINT: 1.7260 AC, Q10 3.57 CFS, Q100 4.71 CFS.
MAX VELOCITY 2.61 FPS AT Q100 — WITHIN THE 5 FPS PERMISSIBLE FOR ESTABLISHED GRASS, 0.5 FT FREEBOARD THROUGHOUT.
THE SWALE DISCHARGES TO THE RECORDED 54RS STORM DRAIN EASEMENT, ALONGSIDE THE 40" RCP CL IV EXTENDING THE FORT FOOTE ROAD CULVERT INLET.
THAT MAIN IS BURIED, OD 4.17 FT, 1.5 FT MIN COVER OVER THE CROWN — FINISHED GRADE OVER IT SHALL BE NO LOWER THAN INVERT + 5.67 FT FILL WHERE EXISTING GROUND IS LOWER.
SWALE GRADES AND INVERTS TO BE SET FROM THE FIELD-RUN TOPOGRAPHIC SURVEY, ESTABLISH SOD BEFORE THE CONTRIBUTING AREA IS STABILISED.


CONCRETE CURB AND GUTTER — PGC DPW&T STD. 300.01

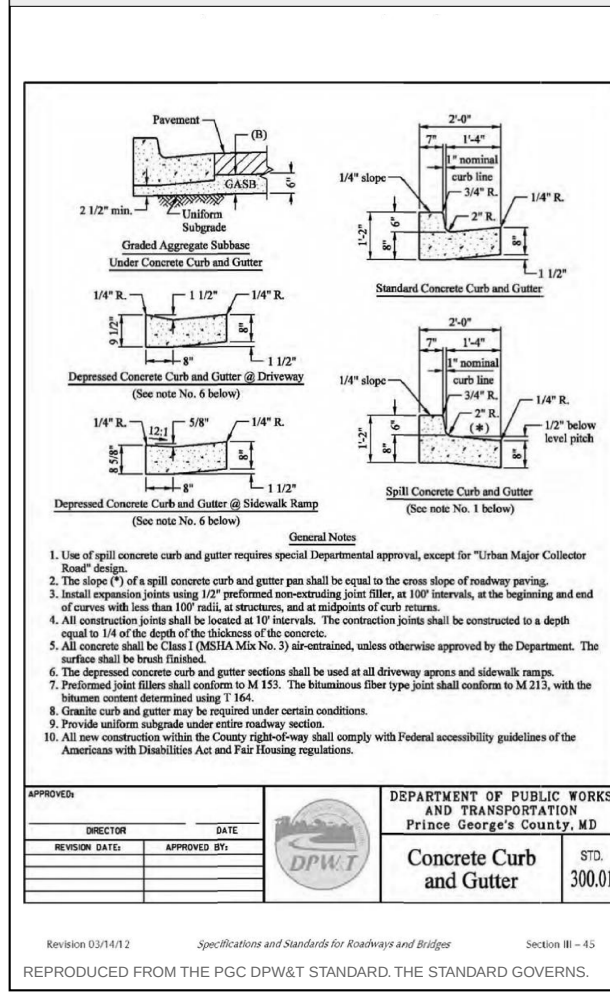

CONCRETE SIDEWALK RAMP TYPE A — PGC DPW&T STD. 300.07

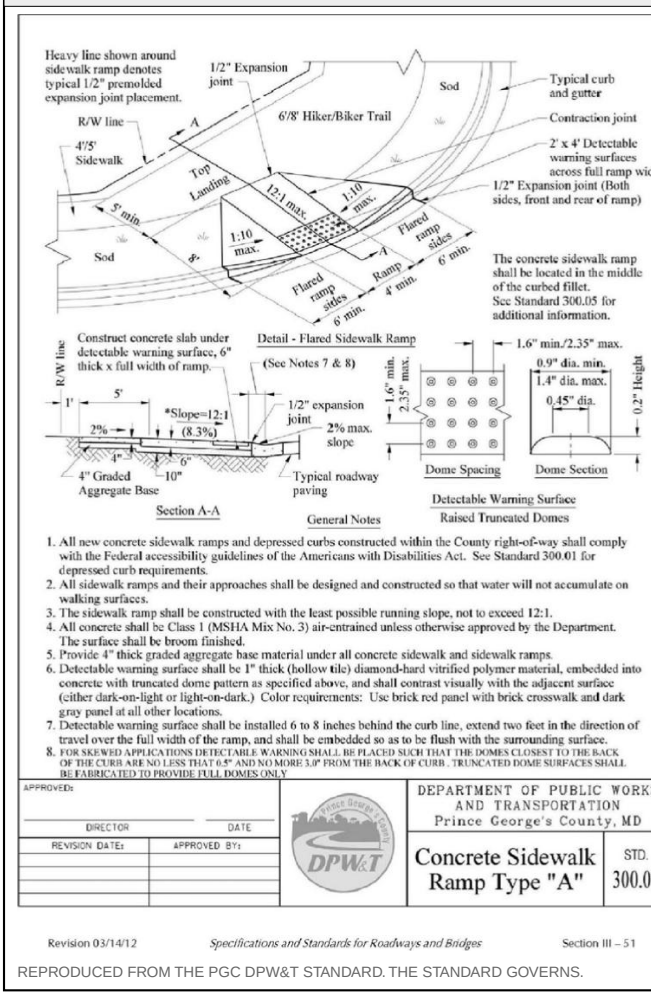

FIELD TOPOGRAPHIC SURVEY — EXISTING CONTOURS — SURVEYED — BM H31A EL. 61.09

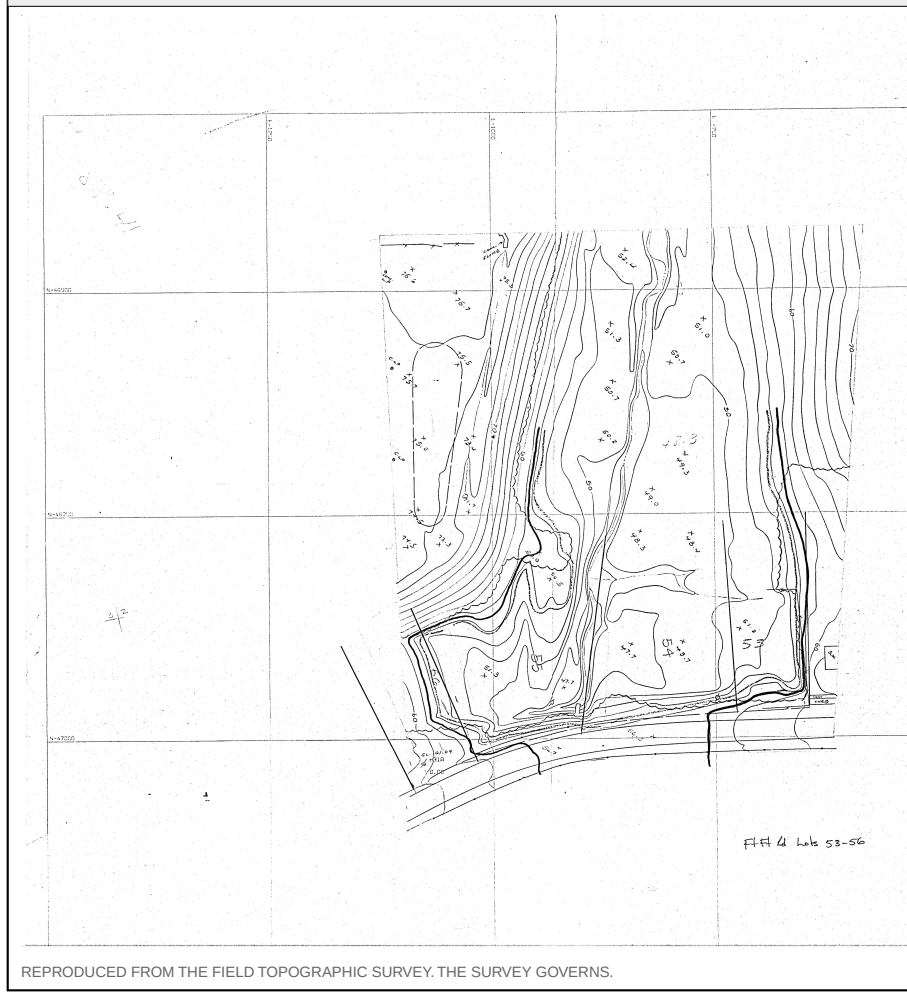

GRAPHIC SCALE — 1" = 30'

0 30 60 90 120 FEET

KEALEE

Design, build, deliver

PROJECT
Indian Queen East — LOT 53 & LOT 54 & LOT 55 & LOT 56
ADDRESS
9588 Fort Foote Rd · 9584 Fort Foote Rd · 9580 Fort Foote Rd · 9576 Fort Foote Rd
JURISDICTION
Prince George's County, Maryland
ZONE
RSF-95
SHEET
L-100 — Landscape and Tree Canopy Plan
SCALE
1" = 30'
STATUS
PRELIMINARY
SHEET NO.
2 OF 3
COORDINATES
EPSG:2248
H: NAD83
V: NAVD88 (feet)

PLAN TYPE AND PREPARATION

PLAN TYPE SITE DEVELOPMENT / FINE GRADING
SHEET L-100 — Landscape and Tree Canopy Plan
DISCIPLINE Landscape Architect / Qualified Professional
DRAWN BY KEALEE SITE-PLAN ENGINE
DESIGNED BY
CHECKED BY

REVISIONS

NO.	DATE	DESCRIPTION

SITE DATA

ZONE	RSF-95
TAX / PARCEL ID	—
GROSS TRACT AREA	75,178 SF 1.726 AC
LOT 53 AREA	12,389 SF 0.284 AC
LOT 54 AREA	23,371 SF 0.537 AC
LOT 55 AREA	25,733 SF 0.591 AC
LOT 56 AREA	13,690 SF 0.314 AC
NET LOT AREA	75,184 SF 1.726 AC
LOT 53 FRONTAGE	50' MIN 83.07'
LOT 54 FRONTAGE	50' MIN 173.55'
LOT 55 FRONTAGE	50' MIN 131.07'
LOT 56 FRONTAGE	50' MIN 84.20'
SETBACKS	REQUIRED PROVIDED
FRONT YARD	30' 30'
SIDE YARD	8' 8'
REAR YARD	20' 20'
COVERAGE	MAX PROPOSED
LOT COVERAGE	30% 6.4%
BUILDING FOOTPRINT	— 4,784 SF
DATUM	
HORIZONTAL	EPSG:2248 NAD83
VERTICAL	NAVD88 (feet)

SITE ANALYSIS

1. Gross tract area	75,178 SF
2. Area of dwelling	4,784 SF
3. Wooded area	NOT ESTABLISHED
4. Floodplain area	NOT ESTABLISHED
5. Net lot area	75,184 SF
6. TOTAL AREA DISTURBED	41,662 SF (AT LEAST)
7. SWM REQUIRED — Sec. 32-174(a)(3)	YES — DISTURBANCE EXCEEDS 5,000 SF

BUILDING DATA

	G	B	FF	SF	HT	STY
9588 Fort Foote Rd	58.89	50.22	59.22	58.22	20'	2
9584 Fort Foote Rd	55.64	46.97	55.97	54.97	20'	2
9580 Fort Foote Rd	55.67	47.00	56.00	55.00	20'	2
9576 Fort Foote Rd	60.68	52.01	61.01	60.01	20'	2

G: garage slab · B: basement · FF: finished floor · SF: subfloor · HT: height · STY: stories · A DASH IS NOT ZERO; the elevation has not been established and must be set from a field run topographic survey before construction.

DRAINAGE AREA COMPUTATIONS

CATCHMENT	AREA SF	IMPERV.	PRE Q	POST Q	INCREASE	WQV CF
LOT 53	12,389	15.1%	0.49	0.69	0.20	182
LOT 54	23,371	9.4%	0.92	1.16	0.24	263
LOT 55	25,733	8.2%	1.01	1.24	0.23	266
LOT 56	13,690	14.2%	0.54	0.75	0.21	203
PROJECT TOTAL	75,184	10.9%	2.96	3.84	0.88	924

Peak flows are summed for catchments; Q in cfs. WQV is the required water-quality volume.

SEQUENCE OF CONSTRUCTION

1. Pre-construction meeting
2. Obtain necessary permits
3. Notify Miss Utility at 811 at least 48 hours prior to any excavation
4. Install stabilized construction entrance and perimeter sediment control
5. Rough grade the lot
6. Construct dwelling
7. Install water, sewer and storm services and the driveway
8. Fine grade and stabilize all disturbed areas
9. Remove sediment control once the inspector gives written permission

TOTAL ESTIMATED TIME OF CONSTRUCTION: 8 MONTHS

GENERAL NOTES

1. CONTRACTOR SHALL CONTACT MISS UTILITY AT 811 A MINIMUM OF 48 HOURS PRIOR TO ANY EXCAVATION, FIELD-VERIFY LOCATION AND DEPTH BY TEST PIT BEFORE CONSTRUCTION.
2. ALL EXISTING AND PROPOSED UTILITIES SHOWN PER PG&C CODE SEC. 32-106.
3. PROPOSED GRADE SHOWN SOLID; EXISTING GRADE SHOWN DASHED.
4. ROUGH EARTHWORK GRADES AND UTILITY ELEVATIONS SHOWN TO TENTHS OF A FOOT.
5. BOUNDARY SHOWN IS THE RECORDED PLAT OF SUBDIVISION — INDIAN QUEEN EAST — BLOCK "E" AND PARTS OF BLOCKS D & F PLAT BOOK WWW (S. P. 40) (MSA: 33,299, 33,299), 32TH ELECTION DISTRICT, PRINCE GEORGE'S COUNTY, MARYLAND, TAX MAP 113, BLOCK F, GRID E4, PLAT DATED 6 JUNE 1987, APPROVED 28 JUNE 1987 BY THE MARYLAND NATIONAL CAPITAL PARK & PLANNING COMMISSION, PRINCE GEORGE'S COUNTY PLANNING BOARD, M-NCPPC RECORD FILE 5197863. SCALE 1" = 100'. SURVEYOR W. L. WICKENS, REGISTERED LAND SURVEYOR NO. 384, TOTAL SUBDIVISION AREA 20,981.1 ACRES. PLAT LEGEND: FOR PUBLIC SEWER & WATER SYSTEMS ONLY. TRANSFERRED AND CHECKED FOR CLOSURE. THE PLAT IS THE BOUNDARY SURVEY, NO FIELD TOPOGRAPHY IS INCLUDED; EXISTING GRADE IS COUNTY LIDAR CONTOUR MAPPING.
6. CONNECT TO EXISTING PAVEMENT, CURB AND GUTTER, DRIVEWAY AND SIDEWALK IN LINE AND GRADE.
7. NO DRIVEWAY CULVERT IS REQUIRED THIS FRONTAGE IS AN EXISTING CURB AND GUTTER SECTION, NOT AN OPEN DITCH SECTION; GUTTER FLOW IS CARRIED THROUGH EACH ENTRANCE BY THE DEPRESSIONED CURB AT THE APRON PER DPW&T STD. 300.03 NOTE 6. ON LOT DRAINAGE IS COLLECTED BY THE REAR-YARD SWALE IN THE REAR DRAINAGE EASEMENT AND CROSSES NO DRIVEWAY OR APRON.


PROFESSIONAL CERTIFICATION

I HEREBY CERTIFY THAT THESE DOCUMENTS WERE PREPARED OR APPROVED BY ME, AND THAT I AM A DULY LICENSED PROFESSIONAL ENGINEER UNDER THE LAWS OF THE STATE OF MARYLAND.

SIGNATURE	DATE
LICENSE NO.	EXPIRATION DATE
SEAL	

REVISIONS

— NONE —

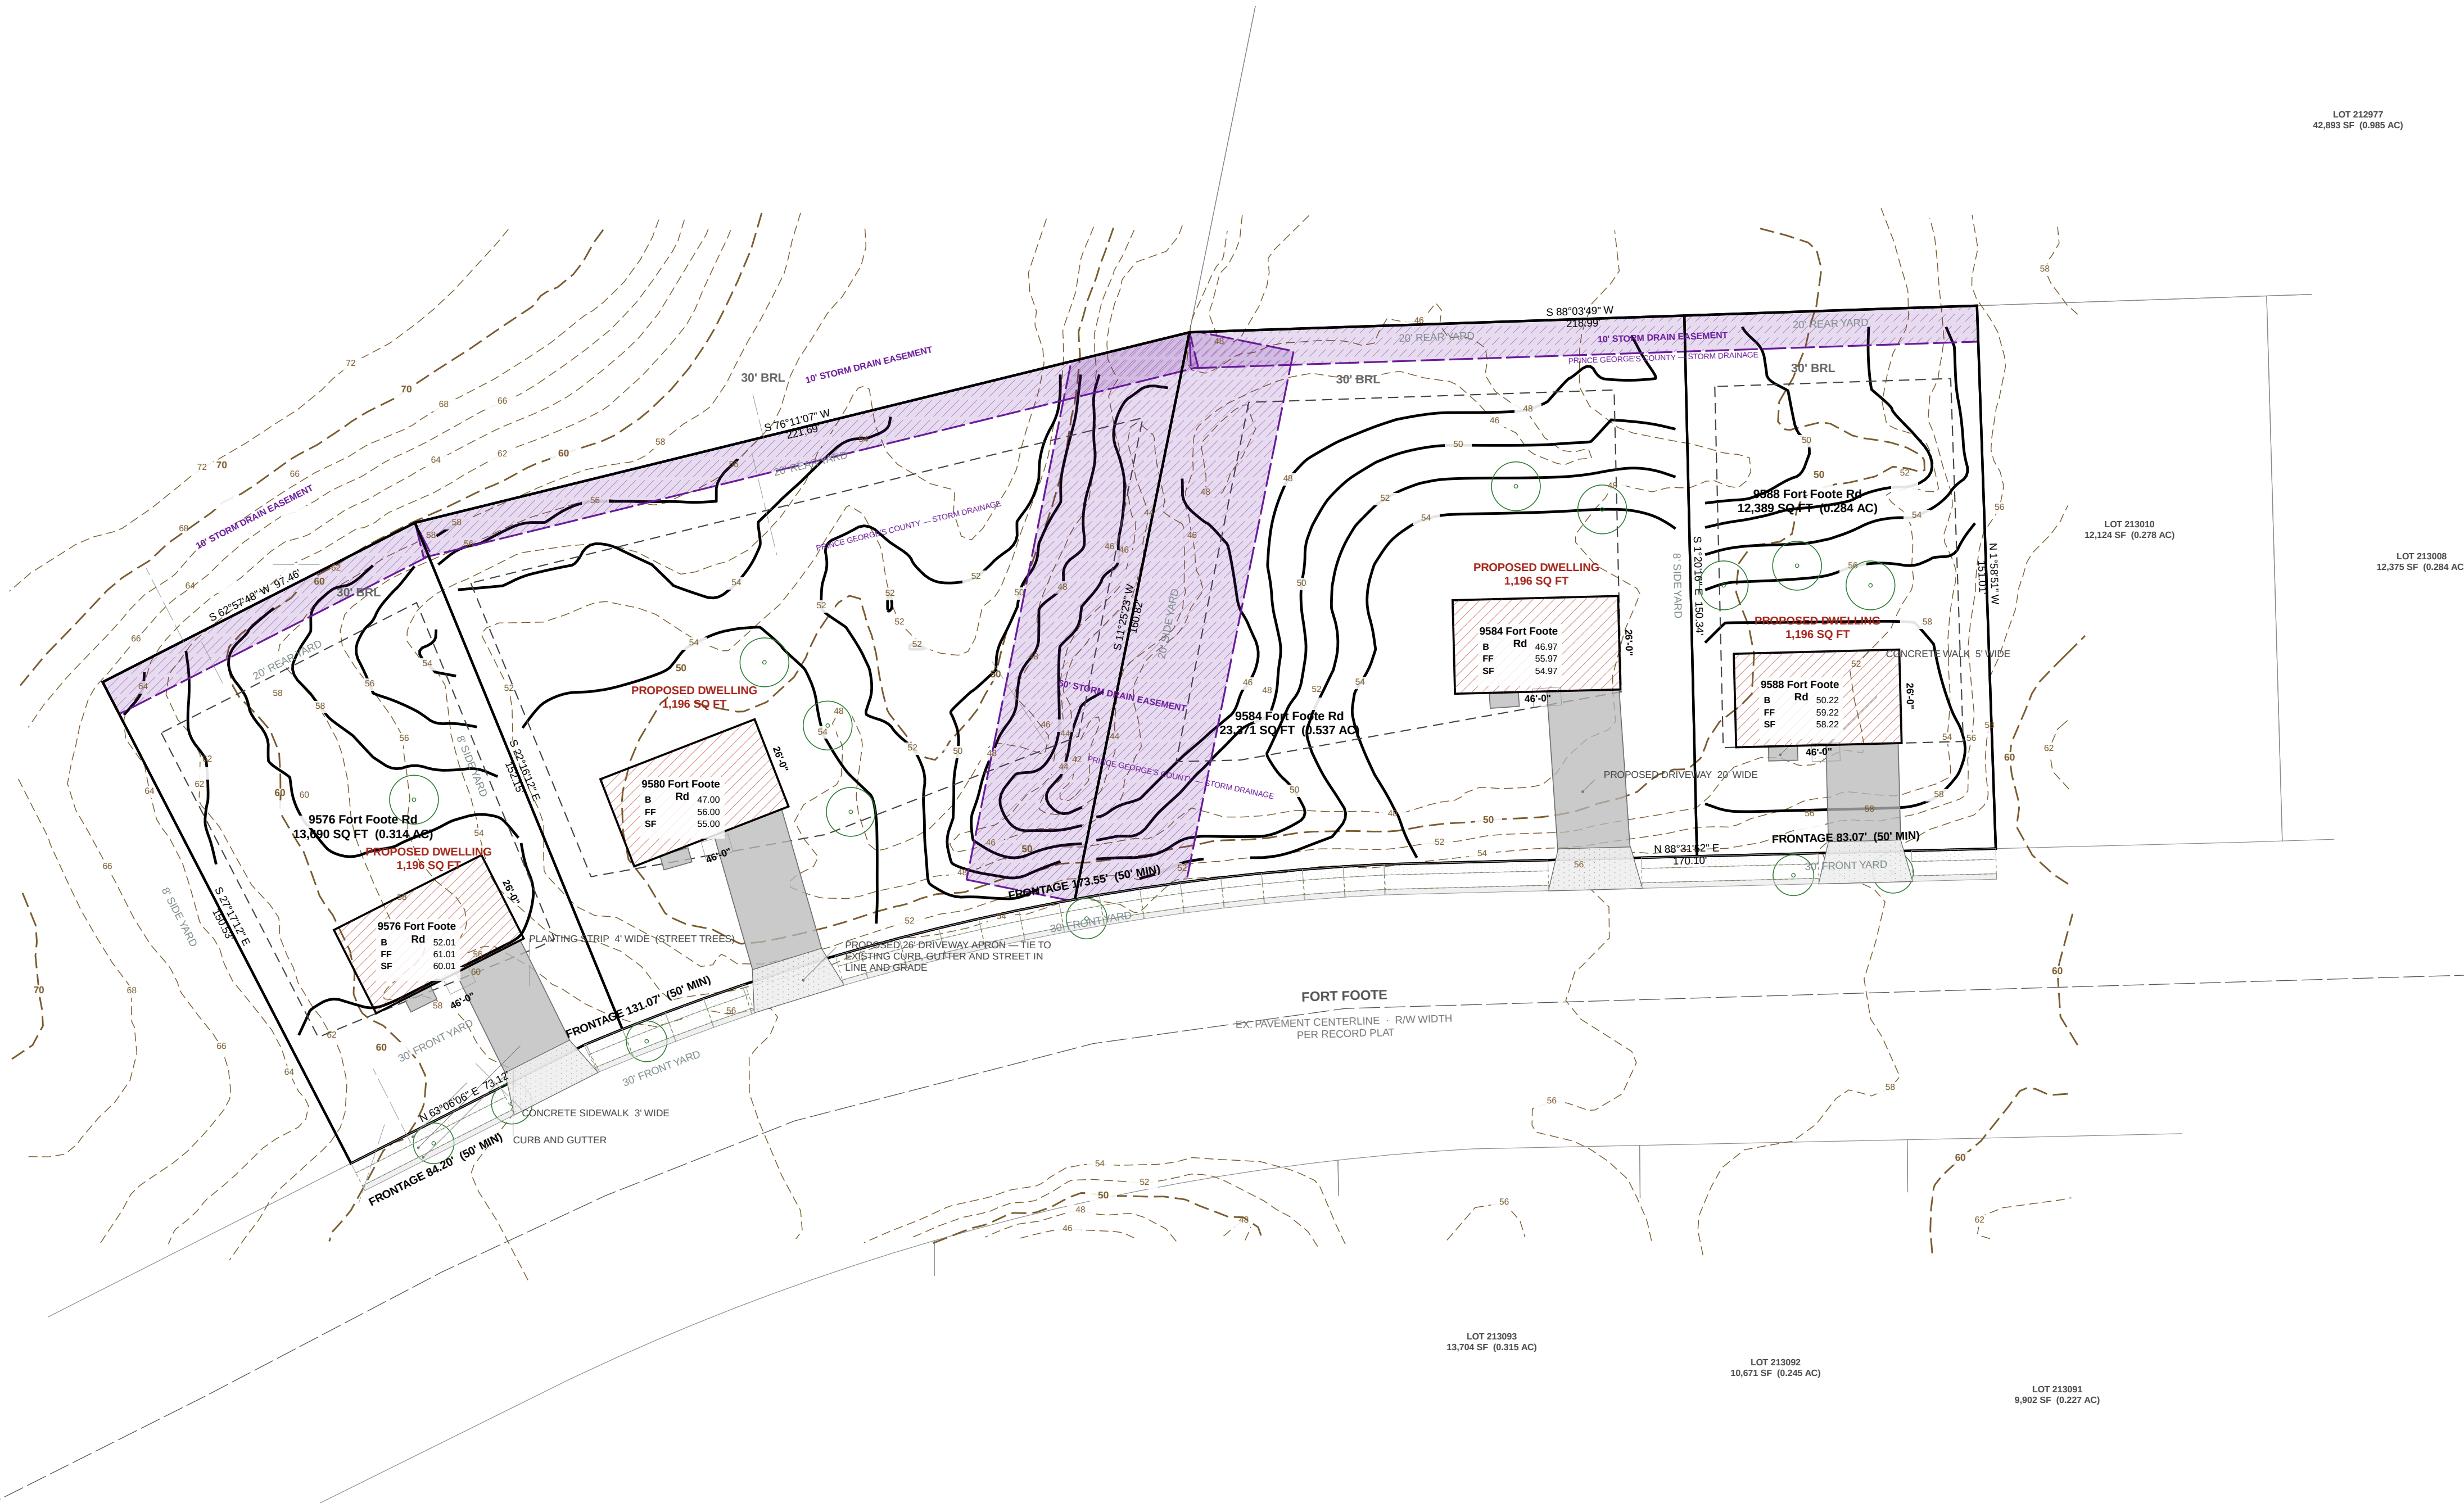

TREE CANOPY SCHEDULE


Sec. 25-128 Table 1 as amended by CB-021-2024 — 20% of NET tract area on RSF-95, met within 8' Per lot planting per Landscape Manual Sec. 4.1(c)(3). Street trees in the right-of-way count toward canopy under Sec. 25-129.

LOT	NET AREA SF	CANOPY REQ 20% SF	SHADE PROV / REQ	ORN-EVON PROV / REQ	STREET TREES	10-YR CANOPY PROVIDED
LOT 53	12,389	2,478	3 / 3	0 / 2 SHORT	2	NOT ESTABLISHED
LOT 54	23,371	4,674	2 / 4 SHORT	0 / 3 SHORT	1	NOT ESTABLISHED
LOT 55	25,733	5,147	3 / 4 SHORT	0 / 3 SHORT	1	NOT ESTABLISHED
LOT 56	13,690	2,738	1 / 3 SHORT	0 / 2 SHORT	2	NOT ESTABLISHED
TOTAL	75,184	15,037	9 / 14	0 / 10	6	—

TEN-YEAR CANOPY IS CREDITED FOR SPECIES FROM THE PRINCE GEORGE'S COUNTY LANDSCAPE MANUAL, NO SPECIES HAS BEEN SELECTED ON THIS SET, SO THE CANOPY PROVIDED IS NOT ESTABLISHED AND THE SCHEDULE IS NOT YET BALANCED. EXISTING TREES PRESERVED ALSO COUNT. NO TREE IS PLANTED WITHIN A STORM DRAIN EASEMENT; THE 60 FT 54/55 EASEMENT CARRIES A 42 IN RCP MAIN AND THE 10 FT REAR EASEMENT CARRIES THE DRAINAGE SWALE; BOTH ARE SHOWN ON THIS SHEET AND BOTH ARE EXCLUDED FROM PLANTABLE AREA.

A WARNING OF THE CANOPY REQUIREMENT IS AVAILABLE UNDER SEC. 25-130. PER LOT PLANTING IS SHOWN ON EVERY LOT AS DRAWN, LANDSCAPE MANUAL, SEC. 4.3(a)(3) REQUIRES 4 MAJOR SHADE AND 3 ORNAMENTAL, OR EVERGREEN TREES ON A LOT OF 20,000 SF OR MORE, AND 3 AND 3 ON A LOT OF 5,000 TO 19,999 SF, NO ORNAMENTAL, OR EVERGREEN TREES ARE DRAWN, AT LEAST ONE SHADE TREE MUST STAND ON THE SOUTH OR WEST SIDE WITHIN 30 FT OF THE DWELLING, AND AT LEAST ONE REQUIRED TREE IN THE FRONT YARD. SPECIES AND FINAL LOCATIONS BY THE LANDSCAPE ARCHITECT. THE CANOPY REQUIREMENT MUST BE MET ON-SITE UNLESS A VARIANCE IS APPROVED, AND WHERE A GRADING PERMIT IS THE ONLY APPLICATION THE CANOPY NOTES BELONG ON THE GRADING PLAN — ENVIRONMENTAL TECHNICAL MANUAL PART D, SEC. 3.0.


CONCRETE CURB AND GUTTER — PGC DPW&T STD. 300.01

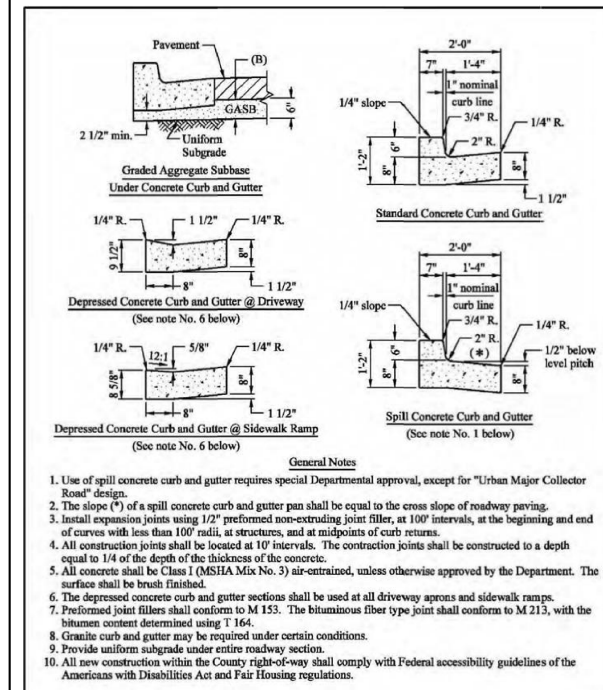

APPROVED	DATE	DESIGNED BY	DATE

REPRODUCED FROM THE PGC DPW&T STANDARD. THE STANDARD GOVERNS.


CONCRETE SIDEWALK RAMP TYPE A — PGC DPW&T STD. 300.07

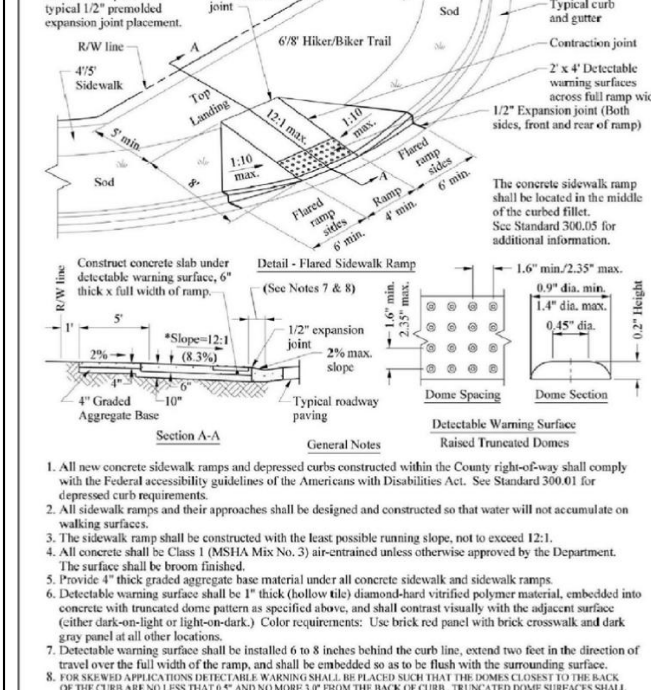

APPROVED	DATE	DESIGNED BY	DATE

REPRODUCED FROM THE PGC DPW&T STANDARD. THE STANDARD GOVERNS.


FIELD TOPOGRAPHIC SURVEY — EXISTING CONTOURS — SURVEYED — BM H31A EL. 61.09

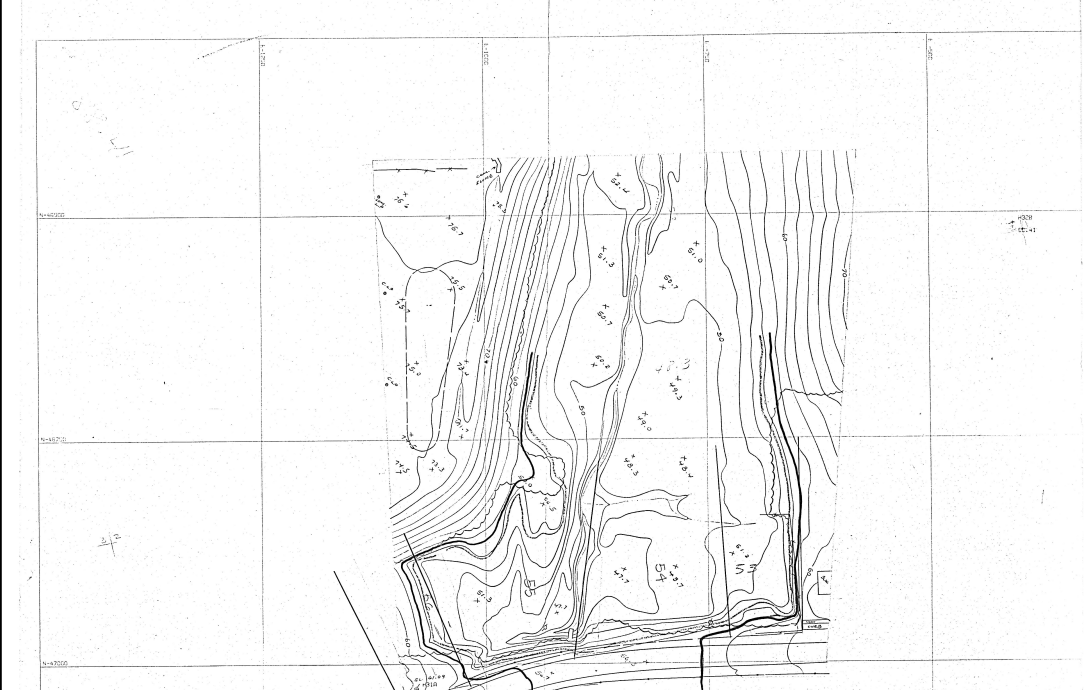

APPROVED	DATE	DESIGNED BY	DATE

REPRODUCED FROM THE FIELD TOPOGRAPHIC SURVEY. THE SURVEY GOVERNS.

GRAPHIC SCALE — 1" = 30'

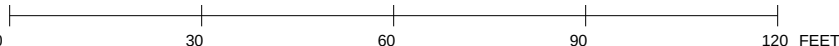

KEALEE

Design, build, deliver

PROJECT
Indian Queen East — LOT 53 & LOT 54 & LOT 55 & LOT 56
ADDRESS
9588 Fort Foote Rd · 9584 Fort Foote Rd · 9580 Fort Foote Rd · 9576 Fort Foote Rd
JURISDICTION
Prince George's County, Maryland
ZONE
RSF-95
SHEET
C-400 — Grading and Drainage Plan
SCALE
1" = 30'
STATUS
PRELIMINARY
SHEET NO.
3 OF 3
COORDINATES
EPSG:2248
H: NAD83
V: NAVD88 (feet)

PLAN TYPE AND PREPARATION

PLAN TYPE SITE DEVELOPMENT / FINE GRADING
SHEET C-400 — Grading and Drainage Plan
DISCIPLINE Maryland Professional Engineer
DRAWN BY KEALEE SITE-PLAN ENGINEER
DESIGNED BY
CHECKED BY

REVISIONS

NO.	DATE	DESCRIPTION

SITE DATA

ZONE	RSF-95
TAX / PARCEL ID	—
GROSS TRACT AREA	75,178 SF 1.726 AC
LOT 53 AREA	12,389 SF 0.284 AC
LOT 54 AREA	23,371 SF 0.537 AC
LOT 55 AREA	25,733 SF 0.591 AC
LOT 56 AREA	13,690 SF 0.314 AC
NET LOT AREA	75,184 SF 1.726 AC
LOT 53 FRONTAGE	50' MIN 83.07'
LOT 54 FRONTAGE	50' MIN 173.55'
LOT 55 FRONTAGE	50' MIN 131.07'
LOT 56 FRONTAGE	50' MIN 84.20'
SETBACKS	REQUIRED PROVIDED
FRONT YARD	30' 30'
SIDE YARD	8' 8'
REAR YARD	20' 20'
COVERAGE	MAX PROPOSED
LOT COVERAGE	30% 6.4%
BUILDING FOOTPRINT	— 4,784 SF
DATUM	
HORIZONTAL	EPSG:2248 NAD83
VERTICAL	NAVD88 (feet)

SITE ANALYSIS

1. Gross tract area	75,178 SF
2. Area of dwelling	4,784 SF
3. Wooded area	NOT ESTABLISHED
4. Floodplain area	NOT ESTABLISHED
5. Net lot area	75,184 SF
6. TOTAL AREA DISTURBED	41,662 SF (AT LEAST)
7. SWM REQUIRED — Sec. 32-174(a)(3)	YES — DISTURBANCE EXCEEDS 5,000 SF

BUILDING DATA

	G	B	FF	SF	HT	STY
9588 Fort Foote Rd	58.89	50.22	59.22	58.22	20'	2
9584 Fort Foote Rd	55.64	46.97	55.97	54.97	20'	2
9580 Fort Foote Rd	55.67	47.00	56.00	55.00	20'	2
9576 Fort Foote Rd	60.68	52.01	61.01	60.01	20'	2

G: garage slab · B: basement · FF: finished floor · SF: subfloor · HT: height · STY: STORIES. A DASH IS NOT ZERO; the elevation has not been established and must be set from a field-run topographic survey before construction.

DRAINAGE AREA COMPUTATIONS

CATCHMENT	AREA SF	IMPERV.	PRE Q	POST Q	INCREASE	WQV CF
LOT 53	12,389	15.1%	0.49	0.69	0.20	182
LOT 54	23,371	9.4%	0.92	1.16	0.24	263
LOT 55	25,733	8.2%	1.01	1.24	0.23	266
LOT 56	13,690	14.2%	0.54	0.75	0.21	203
PROJECT TOTAL	75,184	10.9%	2.96	3.84	0.88	924

Peak flows are summed for catchments; Q in cfs. WQV is the required water-quality volume.

SEQUENCE OF CONSTRUCTION

1. Pre-construction meeting 1 DAY
2. Obtain necessary permits 2 DAYS
3. Notify Miss Utility at 811 at least 48 hours prior to any excavation 1 DAY
4. Install stabilized construction entrance and perimeter sediment control 2 DAYS
5. Rough grade the lot 5 DAYS
6. Construct dwelling 6 MONTHS
7. Install water, sewer and storm services and the driveway 10 DAYS
8. Fine grade and stabilize all disturbed areas 5 DAYS
9. Remove sediment control once the supervisor gives written permission 1 DAY

TOTAL ESTIMATED TIME OF CONSTRUCTION: 8 MONTHS

GENERAL NOTES

1. CONTRACTOR SHALL CONTACT MISS UTILITY AT 811 A MINIMUM OF 48 HOURS PRIOR TO ANY EXCAVATION, FIELD-VERIFY LOCATION AND DEPTH BY TEST PIT BEFORE CONSTRUCTION.
2. ALL EXISTING AND PROPOSED UTILITIES SHOWN PER PGC CODE SEC. 32-106.
3. PROPOSED GRADE SHOWN SOLID; EXISTING GRADE SHOWN DASHED.
4. ROUGH EARTHWORK GRADES AND UTILITY ELEVATIONS SHOWN TO TENTHS OF A FOOT.
5. BOUNDARY SHOWN IS THE RECORDED PLAT OF SUBDIVISION — INDIAN QUEEN EAST — BLOCK "E" AND PARTS OF BLOCKS D & F PLAT BOOK WWW 65, P. 60 (MSA 33299, 32359, 32374 ELECTION DISTRICT, PRINCE GEORGE'S COUNTY, MARYLAND, TAX MAP 113, BLOCK F, GRID E4, PLAT DATED 6 JUNE 1967, APPROVED 26 JUNE 1967 BY THE MARYLAND NATIONAL CAPITAL PARK & PLANNING COMMISSION, PRINCE GEORGE'S COUNTY PLANNING BOARD, M-NCPPC RECORD FILE 5197863. SCALE 1" = 100'. SURVEYOR W. L. WICKENS, REGISTERED LAND SURVEYOR NO. 384, TOTAL SUBDIVISION AREA 20,981.1 ACRES. PLAT LEGEND: FOR PUBLIC SEWER & WATER SYSTEMS ONLY. TRANSFERRED AND CHECKED FOR CLOSURE. THE PLAT IS THE BOUNDARY SURVEY NO FIELD TOPOGRAPHY IS INCLUDED; EXISTING GRADE IS COUNTY LIDAR CONTOUR MAPPING.
6. CONNECT TO EXISTING PAVEMENT, CURB AND GUTTER, DRIVEWAY AND SIDEWALK IN LINE AND GRADE.
7. NO DRIVEWAY CULVERT IS REQUIRED THIS FRONTAGE IS AN EXISTING CURB AND GUTTER SECTION, NOT AN OPEN DITCH SECTION. GUTTER FLOW IS CARRIED THROUGH EACH ENTRANCE BY THE DEPRESSIONED CURB AT THE APRON PER DPW&T STD. 300.01 NOTE 6. ON LOT DRAINAGE IS COLLECTED BY THE REAR-YARD SWALE IN THE REAR DRAINAGE EASEMENT AND CROSSES NO DRIVEWAY OR APRON.

PROFESSIONAL CERTIFICATION

I HEREBY CERTIFY THAT THESE DOCUMENTS WERE PREPARED OR APPROVED BY ME, AND THAT I AM A DULY LICENSED PROFESSIONAL ENGINEER UNDER THE LAWS OF THE STATE OF MARYLAND.

SIGNATURE	DATE
LICENSE NO.	EXPIRATION DATE
SEAL	

IF REQUIRED NOTE(S) DO NOT FIT THIS SHEET: GRADING CERTIFICATE; STABILIZATION COMPLIANCE PREAMBLE; STANDARD STABILIZATION NOTE. THEY ARE REQUIRED AND ARE NOT ON ANY SHEET IN THIS SET.

LOT 212710
925,520 SF (0.147 AC)

LOT 212977
42,893 SF (0.985 AC)

LOT 213010
12,124 SF (0.278 AC)

LOT 213008
12,378 SF (0.284 AC)

LOT 213093
13,704 SF (0.315 AC)

LOT 213092
10,671 SF (0.245 AC)

LOT 213091
9,002 SF (0.207 AC)

SOILS TABLE

USDA NRCS SSURGO — PGC Code Sec. 32-133(a)(13)

MAP UNIT	MAP UNIT NAME	K-FACT	HYDRIC	HYD. GRP	DRAINAGE CLASS
AaB	Adelphia silt loam, 2 to 5 percent slopes complex	37	No	C	Moderately well drained
ACA	Adelphia-Aquasco complex, 0 to 2 percent slopes	43	No	D	Somewhat poorly drained
ADA	Adelphia-Holmdel complex, 0 to 2 percent slopes	24	No	B/D	Somewhat poorly drained
ADB	Adelphia-Holmdel complex, 2 to 5 percent slopes	24	No	B/D	Somewhat poorly drained
ADC	Adelphia-Holmdel complex, 5 to 10 percent slopes	24	No	B/D	Somewhat poorly drained

DRAINAGE SWALE COMPUTATIONS

REACH	LENGTH	GRADE	D.A. (AC)	Q10 (CFS)	Q100 (CFS)	DEPTH	V100 (FPS)	INV IN	INV OUT	CUT
ST-1 — ST-2	110'	3.01%	0.2844	0.59	0.78	0.18'	1.73	50.20	46.90	1.0'
ST-4 — ST-3	157'	4.98%	0.3143	0.65	0.86	0.16'	2.12	60.30	52.50	1.0'
ST-3 — ST-2	177'	3.17%	0.9051	1.87	2.47	0.33'	2.51	52.50	46.90	1.0'

GRADE CONTROL TABLE

POINT	LOT	DESCRIPTION	GROUND	SWALE INV
ST-1	LOT 53	Swale grade break / invert control	51.20	50.20
ST-2	LOT 54	Swale grade break / invert control	47.90	46.90
ST-3	LOT 55	Swale grade break / invert control	53.50	52.50
ST-4	LOT 56	Swale grade break / invert control	61.30	60.30
OUT	—	Swale grade break / invert control	48.90	—

SYSTEM AT THE LOW POINT: 1.7260 AC, Q10 3.57 CFS, Q100 4.71 CFS.
MAX VELOCITY 2.61 FPS AT Q100 — WITHIN THE 5 FPS PERMISSIBLE FOR ESTABLISHED GRASS, 0.5 FT FREEBOARD THROUGHOUT.
THE SWALE DISCHARGES TO THE RECORDED 5485 STORM DRAIN EASEMENT, ALONGSIDE THE 40" RCP CL IV EXTENDING THE FORT FOOTE ROAD CULVERT INLET.
THAT MAIN IS BURIED, OD 43.17 FT, 1.5 FT MIN COVER OVER THE CROWN — FINISHED GRADE OVER IT SHALL BE NO LOWER THAN INVERT + 5.67 FT FILL WHERE EXISTING GROUND IS LOWER.
SWALE GRADES AND INVERTS TO BE SET FROM THE FIELD-RUN TOPOGRAPHIC SURVEY. ESTABLISH SOD BEFORE THE CONTRIBUTING AREA IS STABILIZED.

CONCRETE CURB AND GUTTER — PGC DPW&T STD. 300.01

CONCRETE CURB AND GUTTER — PGC DPW&T STD. 300.01

1. Use of gull concrete curb and gutter requires special Department approval, except for "Thin Major Collector".

2. The curb height of gull concrete curb and gutter shall be equal to the curb slope of roadway grading.

3. All concrete curb and gutter shall be constructed with 100% concrete, with no aggregate or other materials.

4. All concrete curb and gutter shall be constructed with 100% concrete. The concrete shall be constructed to a depth of 12" below the curb face.

5. All concrete curb and gutter shall be constructed to a depth of 12" below the curb face.

6. The concrete curb and gutter shall be constructed to a depth of 12" below the curb face.

constructed to a depth of 12" below the curb