

Prince George's County, Maryland

SHEET	TITLE
-------	-------

C-000	Cover Sheet, Approvals and General Notes
C-100	Existing Conditions and Boundary Plan
C-200	Overall Site and Zoning Plan
C-300	Demolition Plan
C-400	Grading and Drainage Plan
C-500	Utility Plan
C-600	Stormwater Management Plan
C-700	Sediment and Erosion Control Plan
C-800	Road, Driveway and Paving Plan
C-900	Civil Details
L-100	Landscape and Tree Canopy Plan

PLAN TYPE AND PREPARATION	
PLAN TYPE	SITE DEVELOPMENT / FINE GRADING
SHEET	C-000 --- Cover Sheet, Approvals and General Notes
DISCIPLINE	Realize (Coordinator)
DRAWN BY	KEALEE SITE-PLAN ENGINE
DESIGNED BY	
DATE	

NO.	DATE

2	C-100	Existing Conditions and Boundary Plan
3	C-200	Overall Site and Zoning Plan
4	C-300	Demolition Plan
5	C-400	Grading and Drainage Plan
6	C-500	Utility Plan
7	C-600	Stormwater Management Plan
8	C-700	Sediment and Erosion Control Plan
9	C-800	Road, Driveway and Parking Plan
10	C-900	Civil Details
11	L-100	Landscape and Tree Canopy Plan

TAX / PARCEL ID	TRACT
-----------------	-------

GROSS TRACT AREA	782.369 SF	17.961 AC
TRACT AREA	782.368 SF	17.961 AC
STATUS OF THIS SET	782.368 SF	17.961 AC
MINIMUM FRONT SETBACK FOR CONSTRUCTION NOT REQUIRED FOR PERMIT		
SETBACKS	REQUIRED	PROVIDED
FRONT YARD	—	—
SIDE YARD	—	—
REAR YARD	—	—
COVERAGE	MAX	PROPOSED
LOT COVERAGE	—	7.8%
BUILDING FOOTPRINT	—	60.89 SF
DATUM		
HORIZONTAL	EPSG:2248	NAD83
VERTICAL	NAVD83	NAVD83

1. Gross lot area	782,368 SF
2. Area of dwelling	60,896 SF
3. Wooded area	NOT EST.
4. Floodplain area	NOT EST.
5. Net lot area	782,368 SF
6. TOTAL AREA DISTURBED	0 SF
7. SWM REQUIRED — Sec. 32-174(a)(3)	EXEMPT

BUILDING DATA	G	R	FF	SF	HT	STY
L07 1	-	-	-	-	-	-
L07 2	-	-	-	-	-	-
L07 3	-	-	-	-	-	-
L07 4	-	-	-	-	-	-
L07 5	-	-	-	-	-	-
L07 6	-	-	-	-	-	-
L07 7	-	-	-	-	-	-
L07 8	-	-	-	-	-	-
L07 9	-	-	-	-	-	-
L07 10	-	-	-	-	-	-
L07 11	-	-	-	-	-	-
L07 12	-	-	-	-	-	-
L07 13	-	-	-	-	-	-
L07 14	-	-	-	-	-	-
L07 15	-	-	-	-	-	-
L07 16	-	-	-	-	-	-
L07 17	-	-	-	-	-	-
L07 18	-	-	-	-	-	-
L07 19	-	-	-	-	-	-
L07 20	-	-	-	-	-	-
L07 21	-	-	-	-	-	-
L07 22	-	-	-	-	-	-
L07 23	-	-	-	-	-	-
L07 24	-	-	-	-	-	-
L07 25	-	-	-	-	-	-
L07 26	-	-	-	-	-	-
L07 27	-	-	-	-	-	-
L07 28	-	-	-	-	-	-
L07 29	-	-	-	-	-	-
L07 30	-	-	-	-	-	-
L07 31	-	-	-	-	-	-
L07 32	-	-	-	-	-	-
L07 33	-	-	-	-	-	-
L07 34	-	-	-	-	-	-
L07 35	-	-	-	-	-	-
L07 36	-	-	-	-	-	-
L07 37	-	-	-	-	-	-
L07 38	-	-	-	-	-	-
L07 39	-	-	-	-	-	-
L07 40	-	-	-	-	-	-
L07 41	-	-	-	-	-	-
L07 42	-	-	-	-	-	-
L07 43	-	-	-	-	-	-
L07 44	-	-	-	-	-	-
L07 45	-	-	-	-	-	-
L07 46	-	-	-	-	-	-
L07 47	-	-	-	-	-	-
L07 48	-	-	-	-	-	-
L07 49	-	-	-	-	-	-
L07 50	-	-	-	-	-	-
L07 51	-	-	-	-	-	-
L07 52	-	-	-	-	-	-
L07 53	-	-	-	-	-	-
L07 54	-	-	-	-	-	-
L07 55	-	-	-	-	-	-
L07 56	-	-	-	-	-	-
L07 57	-	-	-	-	-	-
L07 58	-	-	-	-	-	-
L07 59	-	-	-	-	-	-
L07 60	-	-	-	-	-	-
L07 61	-	-	-	-	-	-
L07 62	-	-	-	-	-	-
L07 63	-	-	-	-	-	-
L07 64	-	-	-	-	-	-

Notes: - S: Slope = 1 FT finished floor; SF: surface; HT: height; STY: story; A DASHIC NOT ZERO: the elevation has not been established and must be set from a fixed point.

1. Pre-construction meeting	1 DAY
2. Obtain necessary permits	2 DAYS
3. Notify Miss Utility at 811 at least 48 hours prior to any excavation	1 DAY
4. Install stabilized construction entrance and perimeter sediment control	2 DAYS
5. Rough grade the lot	5 DAYS
6. Construct dwelling	6 MONTHS
7. Install water, sewer and storm services and the driveway	10 DAYS
8. Fine grade and stabilize all disturbed areas	5 DAYS
9. Remove sediment control once the inspector allows written permission	1 DAY

1. 48 HOURS PRIOR TO ANY EXCAVATION, FIELD VERIFY LOCATION AND DEPTH BY TEST PIT BEFORE CONSTRUCTION.
2. ALL EXISTING AND PROPOSED UTILITIES SHOWN PER P&G CODE REQUIREMENTS.
3. PROPOSED GRADE SHOWN SOLID; EXISTING GRADE SHOWN DASHED.
4. ROUGH AROUND GRADES AND UTILITY ELEVATIONS SHOWN TO TENTHS OF A FOOT.
5. BOUNDARY SHOWN IS THE RECORDED PLAT OF SUBDIVISION -- (ADMIN 19800) -- LOTS OF RECORD, PLAT, L48319 2/3 -- (OWNER RECORD) -- (CITY OF CHICAGO LEASE CONTRACT, 1980, 1981, 1982,

- BFL - BUILDING RESTRICTION LINE
- PROPOSED STRUCTURE LINE
- EXISTING CONTOUR - 5 FT INTERVAL NAVD83
- PROPOSED CONTOUR - 2 FT INTERVAL
- STREET CENTRELINE
- PROPOSED PAVEMENT - DRIVEWAY / WALK
- EASEMENT
- SANITARY LATERAL (SGL) - HEMEST
- WATER SERVICE (WWS)
- STORM DRAIN - TRUNK, RCP
- STORM - HOUSE CONNECTION TO TRUNK
- DRAINAGE SWALE - INVERT AND GRADED SECTION
- RETAINING WALL - TICKS ON THE RETAINED SIDE
- LIMIT OF GROUND COVER - TICKS ON THE STEEP SIDE
- 100 YR FLOODPLAIN LIMIT; EXISTING GROUND - FFS 770017; WSSC DATA, UNITED STATES FLOODPLAIN LIMIT; PROPOSED GROUND - SAME ELEVATION, REGRADED SURFACE
- ESD - STORMWATER PRACTICE


EVERGREEN VENTURES LLC (PGAtlas Address/Property)

- [illegible]


SOILS TABLE USDA NRCS SSURGO — PGC Code Sec. 32-130(a)(12)

MAP UNIT	MAP UNIT NAME	K-FACT	HYDRIC	HYD. GRP	DRAINAGE CLASS
AuB	Adelphi silt loam, 2 to 5 percent slopes complex	.37	No	C	Moderately well drained
AcA	Adelphi-Aquasol complex, 0 to 2 percent slopes	.43	No	D	Somewhat poorly drained
AdA	Adelphi-Holmud complex, 0 to 2 percent slopes	.24	No	B/D	Somewhat poorly drained
AdB	Adelphi-Holmud complex, 2 to 5 percent slopes	.24	No	B/D	Somewhat poorly drained
AOB	Adelphi-Holmud complex, 5 to 10 percent slopes	.24	No	B/D	Somewhat poorly drained

CONCRETE CURB AND GUTTER — PGC DPW&T STD. 300.01	CONCRETE SIDEWALK RAMP TYPE A — PGC DPW&T STD. 300.07
--	---

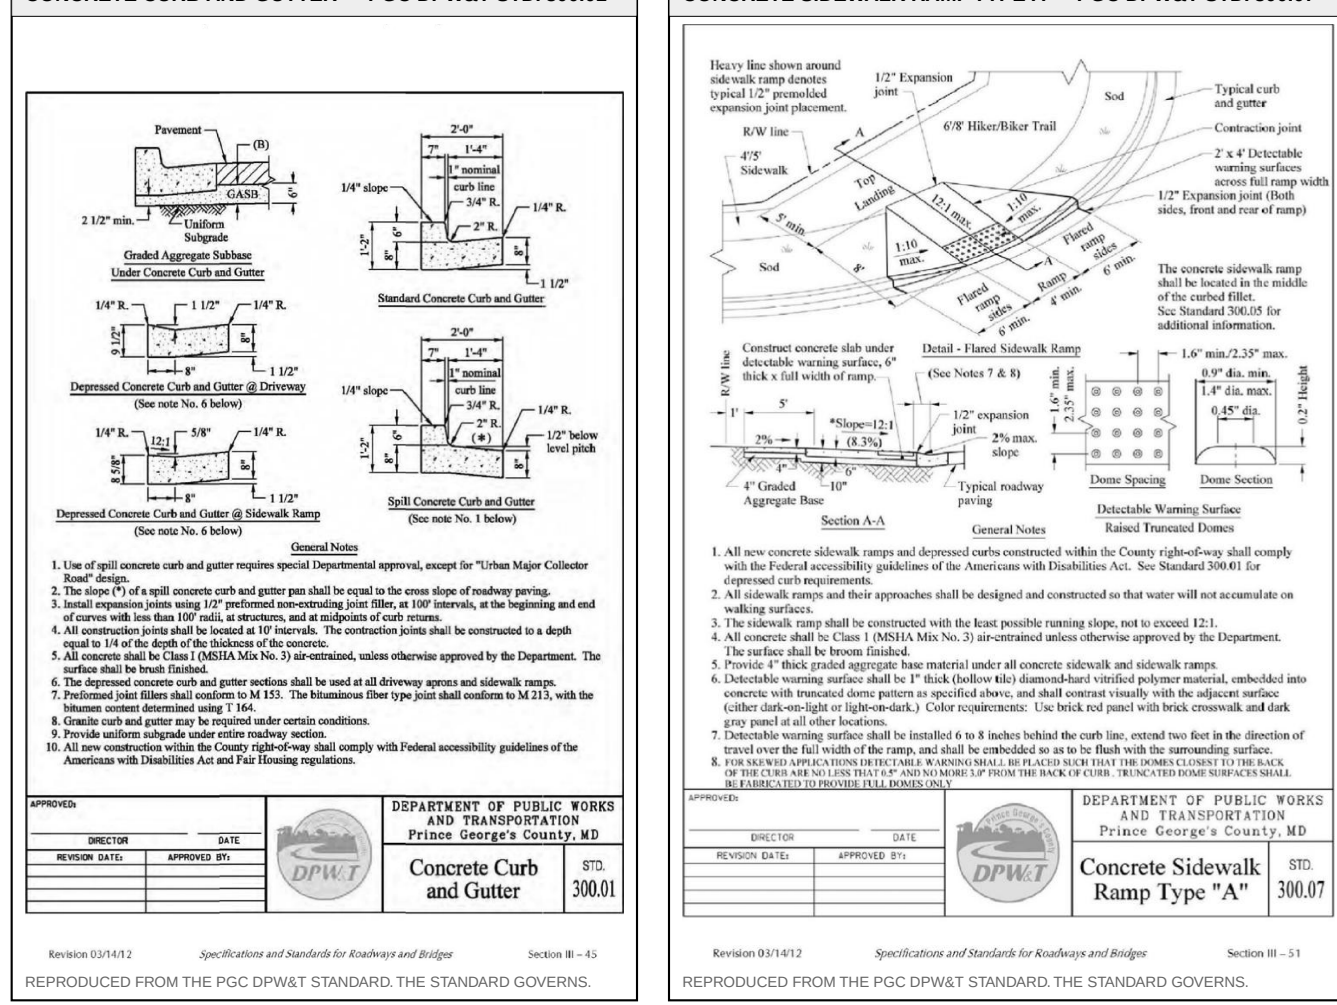


CONCRETE SIDEWALK RAMP TYPE A — PGC DPW&T STD. 303.07

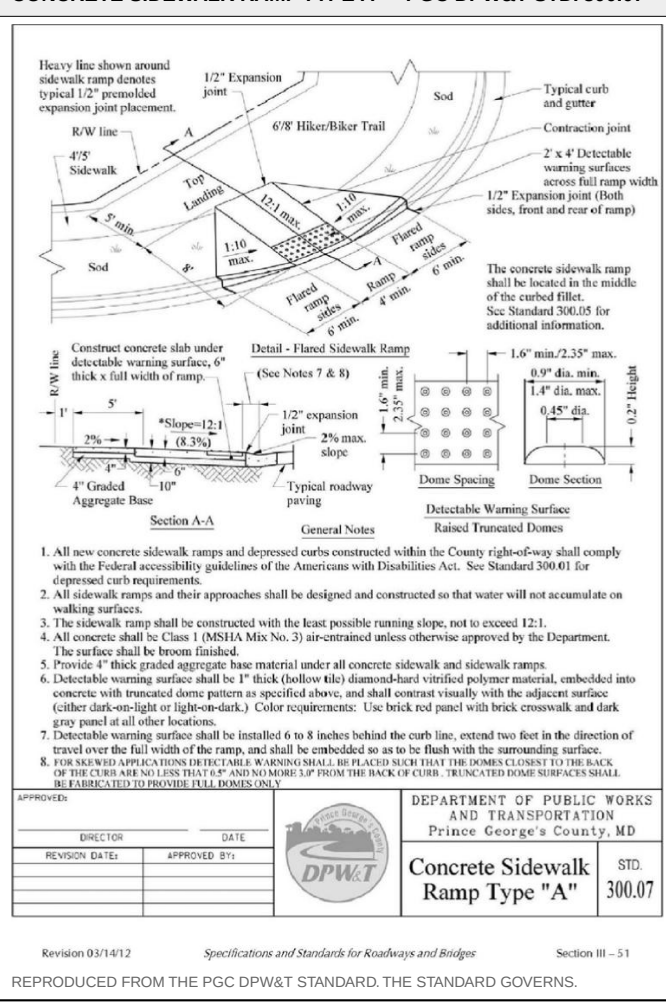

GRAPHIC SCALE - 1" = 100'

100 200 300 400 FEET

18. Sec. 27 (6200) parking lot within road (2.50s) northside and double on the W. 1/4 (1.50s two over two) are ASSUMED - the certified tables carried by this company are not shown the parking schedule, where parking at 0.50s is customer and not shown.

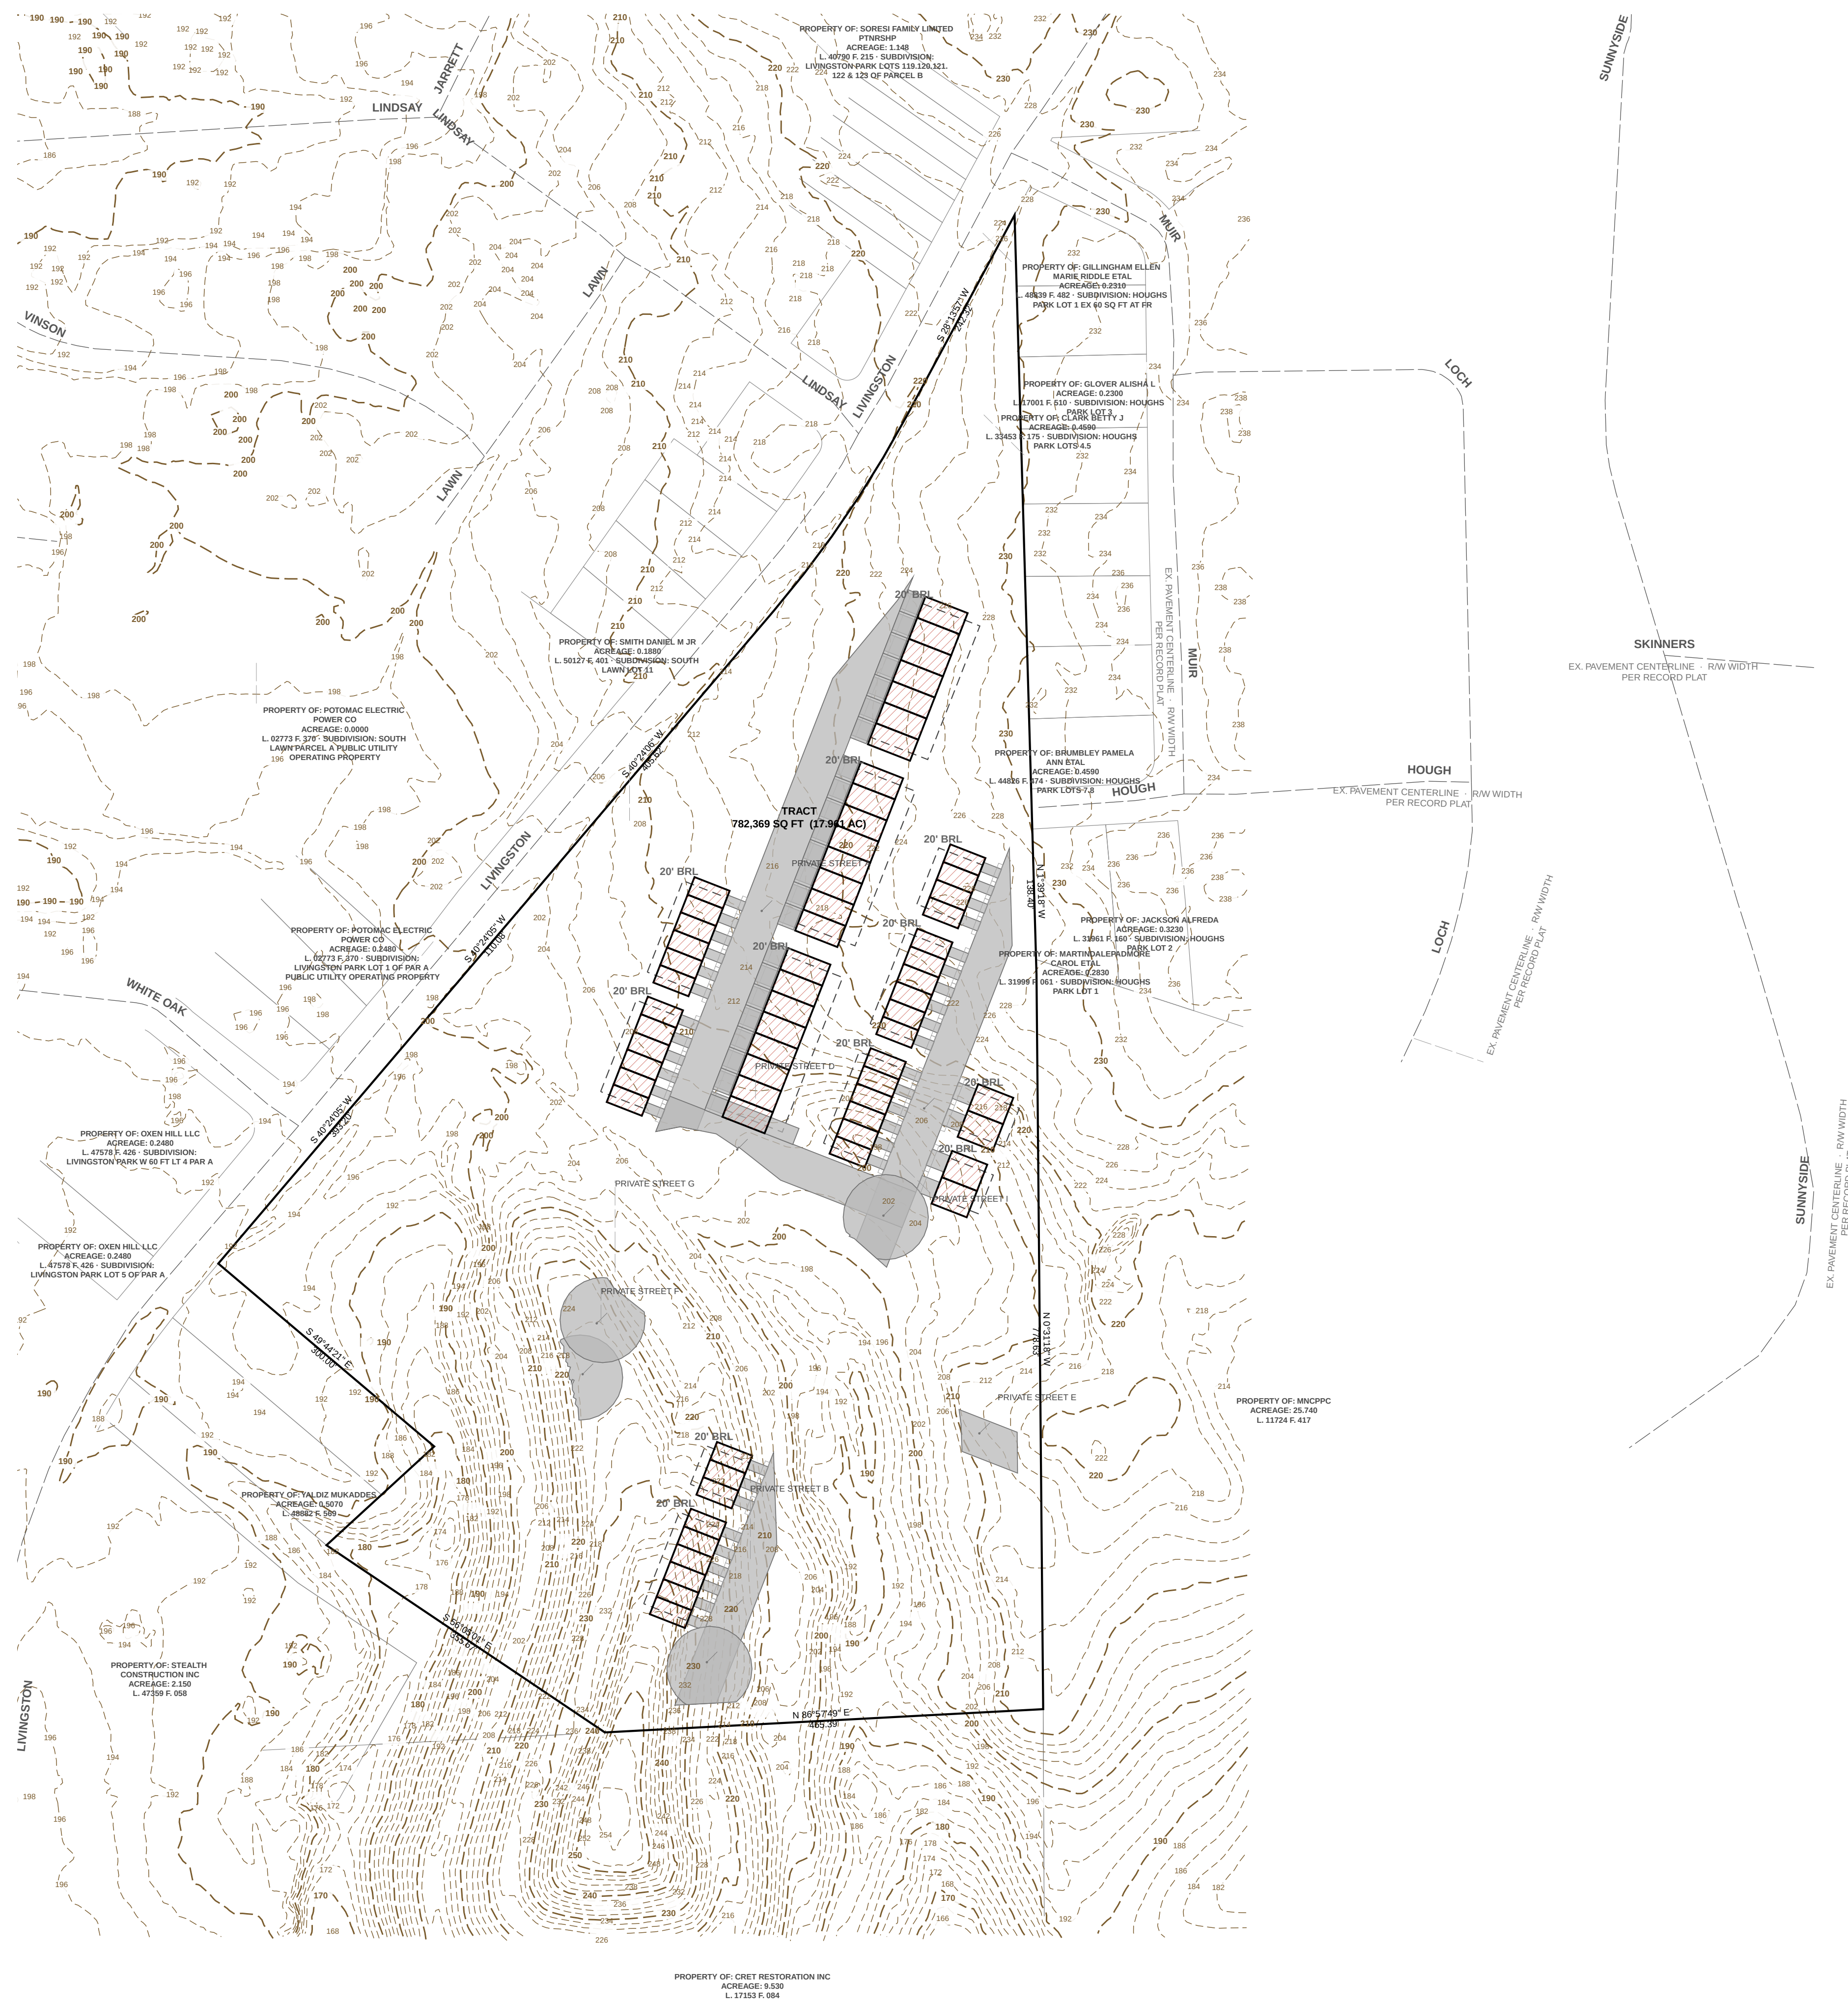

KEALEE
 (design, build, deliver)

PROJECT
 7720 Longstar Road (Parcel 049, 18.07 ac, RMF-20) — townhouses, two-over-tos and duplexes

OWNER
 (OWNER) 15800

ARCHITECT
 Prince George's County, Maryland

ZONE
 RMF-20

PHASE
 C-100 — Existing Conditions and Boundary Plan

SCALE
 1" = 100'

DATE
 PRELIMINARY

SHEET NO.
 2 OF 11

EXISTS PROJECT
 EPSG 2248
 NAD 83
 V. NAVD83 (feet)

INDEX OF DRAWINGS

1	C-000	Cover Sheet, Approvals and General Notes
2	C-100	Existing Conditions and Boundary Plan
3	C-200	Overall Site and Zoning Plan
4	C-300	Demolition Plan
5	C-400	Grading and Drainage Plan
6	C-500	Utility Plan
7	C-600	Stormwater Management Plan
8	C-700	Sediment and Erosion Control Plan
9	C-800	Road, Driveway and Paving Plan
10	C-900	Civil Details
11	L-100	Landscape and Tree Canopy Plan

SITE DATA	
ZONE	TRACT
TAX PARCEL ID	RM-2
CROSS TRACT AREA	782,369 SF 17,961 AC
TRACT AREA	782,369 SF 17,961 AC
NET LOT AREA	782,369 SF 17,961 AC
NET LOT AREA	297,648 SF 6.80 AC
LOT FRONTAGE	REQUIRED
FRONT YARD	PROPOSED
REAR YARD	---
SIDE YARD	---
REAR YARD	---
COVERAGE	MAX PROPOSED
LOT COVERAGE	7.8%
BUILDING FOOTPRINT	60,896 SF
DATUM	
HORIZONTAL	EPGS 2283
VERTICAL	NAD83

SITE ANALYSIS	
1. Gross tract area	782,369 SF
2. Area of dwelling	60,896 SF
3. Wooded area	NOT ESTABLISHED
4. Floodplain area	NOT ESTABLISHED
5. Net lot area	782,369 SF
6. TOTAL AREA DISTURBED	0 SF
7. SWM REQUIRED — Sec. 32-174(a)(3) EXEMPT — 5,000 SF OR	

BUILDING DATA	G	B	FF	SP	HT	STY
LOF 1	---	---	---	---	---	---
LOF 2	---	---	---	---	---	---
SEQUENCE OF CONSTRUCTION	
1. Pre-construction meeting	1 DAY
2. Obtain necessary permits	2 DAYS
3. Notify Miss Utility at 811 at least 48 hours prior to any excavation	1 DAY
4. Install impervious construction entrance and perimeter sediment control	2 DAYS
5. Rough grade the lot	5 DAYS
6. Construct dwelling	6 MONTHS
7. Install water, sewer and storm services and the driveway	1 DAY
8. Fine grade and stabilize all disturbed areas	5 DAYS
9. Remove sediment control once the inspector gives written permission	10 DAYS

TOTAL ESTIMATED TIME OF CONSTRUCTION: 8 MONTHS

GENERAL NOTES

1. CONTRACTOR SHALL CONTACT MISS UTILITY AT 811 A MINIMUM OF 48 HOURS PRIOR TO ANY EXCAVATION. FIELD-VERIFY LOCATION AND DEPTH BY TEST PIT BEFORE CONSTRUCTION.

[illegible]

LEGEND

- PROPERTY BOUNDARY
- BRL – BUILDING RESTRICTION LINE
- PROPOSED STRUCTURE
- EXISTING CONTOUR – 2 FT INTERVAL, NAVSIBS
- PROPOSED CONTOUR – 2 FT INTERVAL
- STREET CENTRELINE
- PROPOSED PAVEMENT – PPS INTERLOCK
- EASEMENT
- PROPERTY LATERAL DITCH – HEMLOCK
- WATER SERVICE (WWS)
- STORM DRAIN – TRUNK PIPE
- STORM – HOUSE CONNECTION TO TRUNK
- CHANGE WASTE – INVERT AND DRAINER SECTION
- RETAINING WALL – TIES ON THE RETAINED SIDE
- LIMIT OF SHEDS COVERED BY THE STORM DRAIN
- 10' FLOODPLAIN LIMIT EXISTING GROUND, FFS 7002; WSSIC DATA, UNITED
- 20' FLOODPLAIN LIMIT PROPOSED GROUND, FFS 7002; WSSIC DATA, UNITED
- STORMWATER PRACTICE

PLAT OF RECORD
(ADMIN # 19800) — 1 lots of record, plat, L49319 F213 — owner of record
ENERGEX VENTURES L.L.C. (RGAfile: 4426999) (RanzenoA)

1. PRELIMINARY. Boundaries are the county parcel layer (compiled from the recorded plats, not surveyed); a boundary survey precedes any final plat.

3. Layout: 67 dwelling units in 64 bays – 37 townhouse, 4 two-family (duplex), 46 two-over-two (stacked, 2 units per bay); 4.84 duap gross.

6. Sec. 24-134 mandatory dedication of parkland — 5% of the gross tract, provided on site as private recreation open space (HOA parcel) in lieu of dedication: 43,213 sq ft (gross) amount 79,118 sq ft

7. Sec. 24-121(a)(13): every lot fronts and takes access from one street only; (a) (8) corner lots truncated at platting; (a)(10) no unnecessary street — the approved access is raised.

right angles; (b)(5) public secondary streets 50 ft / primary 60 ft of right-of-way — these are private streets, so Sec. 24-128(b)(7) governs: "a 22-ft pavement (26 ft drawn), alleys "a 18 ft, a 10 ft public utility easement contiguous to the right-of-...

10. Sec. 27-42(3) (RMF-25) yards: front 15 ft, side 8 ft (end units; partly walls within a stick), rear 20 ft — drawn: build line 20 ft (the driveway apron for the

11. Pedestrian access: a 5-ft sidewalk runs along the front of every building at the street line (Sec. 23-135), on the lot in the front yard, crossed by the

12. Vehicular access: every townhouse, duplex and two-over-two lot fronts a street (the kept public right-of-way or a private street) and has its own driveway

PROFESSIONAL CERTIFICATION For 100 ft outside a Transit Oriented Development center, 25 ft of road frontage and 100 ft of street frontage. This was used by ME AND THAT I AM A DULY LICENSED PROFESSIONAL

14. Sec. 24-134 mandatory dedication of parkland: 5% of the gross tract (39,118 sf) — provided on site as recreation open space on an HOA parcel 63,713 sf drawn.

1.5. Sec. 24-121(a)(15): a DPE, approved stormwater concept precedes the preliminary plan — ESD to the WBP/WDE Manual Ch. 5: micro-bioremediation in the reserved areas down, bioswales along each private street; (a)(16) Subside 2S woodland conservancy by TCP2

DATE _____

1.6. Sec. 23-135: curb, gutter and 5-ft sidewalk on the street side of every lot (lot frontages ≥ 100 ft). DPE grading standards: lawns $\geq 2\%$, swales 2-4%, banks $\geq 3\%$ (residential), slopes steeper than 4:1 set back 10-20 ft from buildings.

18. Sec. 27-6300 parking: the ratios used (2.0 for townhouse and duplex on the

LOT n — proposed fee-sample lot - PRIVATE STREET A... — HIGH street, 2...

MAP UNIT	MAP UNIT NAME	K-FACT	HYDRIC	HYD. GRP	DRAINAGE CLASS
AdA	Adelphi silt loam, 2 to 5 percent slopes complex	.37	No	C	Moderately well drained
AdA	Adelphi-Agassico complex, 0 to 2 percent slopes	.43	No	D	Somewhat poorly drained
AdC	Adelphi-Holmclid complex, 0 to 2 percent slopes	.24	No	B/D	Somewhat poorly drained
AdC	Adelphi-Holmclid complex, 2 to 5 percent slopes	.24	No	B/D	Somewhat poorly drained
AdC	Adelphi-Holmclid complex, 5 to 10 percent slopes	.24	No	B/D	Somewhat poorly drained

[illegible]

GRAPHIC SCALE — 1" = 100'

A horizontal line with vertical tick marks at 0, 100, 200, 300, and 400. The word "FEET" is written below the 400 mark.

INDEX OF DRAWINGS			
C-100	Sheet 2-000 Approach and General Notes		
C-100	Existing Conditions and Boundary Plan		
C-100	Overall Site and Lining Plan		
C-100	Derivatives Plan		
C-400	Curb and Drainage Plan		
C-500	Utility Plan		
C-500	Stormwater Management Plan		
C-500	Grading and Erosion Control Plan		
C-600	Road, Driveway and Parking Plan		
10-C-600	Cost Details		
10-C-600	Landscape and Tree Canopy Plan		
SITE DATA			
ZONE	RP-01-D		
TAX/ PARCEL ID	TRACT		
GROSS TRACT AREA	782,369 SF	17,961 AC	
TRACT AREA	782,369 SF	17,961 AC	
NET LOT AREA	782,369 SF	17,961 AC	
LOT AREA/RANGE	207 MAR	NOT	
STREETS	REQUIRED	PROPOSED	
FRONT YARD	---	---	
SIDE YARD	---	---	
REAR YARD	---	---	
COVERAGE	MAX	PROPOSED	
LOT COVERAGE	---	7.8%	
REULING/FOOTPRINT	---	60,899 SF	
DATUM			
HORIZONTAL	EPSC 2248	NAD83	
VERTICAL	NAD83		

BUILDING DATA	G	B	FF	SP	HT	STY
LOF 1						
LOF 2						
ESTIMATED TIME OF CONSTRUCTION: 8 MONTHS

GENERAL NOTES

1. CONSTRUCTION SHALL COMPLY WITH ALL THE REQUIREMENTS OF 48 HOURS NOTICE OF AVOIDANCE, FIELD-VERIFIED LOCATION AND DEPTH TEST BY GEOTECH CONSULTANT.
2. ALL EXISTING AND PROPOSED UTILITIES SHOWN PER PGC CODE, SEE 30.06C.
3. PROPOSED GRADE SHOWN SLOES EXISTING GRADE SHOWN DASHED.
4. HOLDUP EARTHWORK, GRADES AND UTILITY ELEVATIONS SHOWN TO TOP OF ASPHALT.
5. BOUNDARY SHOWN IS THE PRECEDED PLAT OF A PREVIOUSLY OWNED TRACT. LOTS OF PREVIOUS PLATS ARE SHOWN FOR REFERENCE. THE BOUNDARY SHOWN IS NOT A GUARANTEE OF PROPERTY - TRANSFERRED AND CHECKED FOR CLOSURE. THE PLAT IS THE BOUNDARY EVIDENCE. NO FIELD VERIFICATION OF BOUNDARY EXISTING GRADE IS COUNTY LAND OFFICE MAP.
6. CONVEY TO EXISTING PAVEMENT: CEMENT CONCRETE DRIVEWAY AND SIDEWALK IN LINE AND GRADE.
7. NO EXISTING CURB/STREET IS REQUIRED. THIS PROVISION IS IN ORDER TO ALLOW FOR FUTURE CONSTRUCTION OF CURB AND DRIVEWAY.
8. GUTTER FLOW COLLECTS THROUGH BACK ENTRANCE BY THE REFERENCED CURB AT THE ASPHALT PAVEMENT ELEVATION. GUTTER DRAINAGE IS COLLECTED BY THE DRAINAGE DRAINAGE IN THE BACK ENTRANCE AND CARRYING DRAINAGE IN THE BACK ENTRANCE.

[illegible]

CONCRETE CURB AND GUTTER — PGCC DPWAT STD. 300.01

CONCRETE SIDEWALK RAMP TYPE A — PGCC DPWAT STD. 300.07

CONCRETE SIDEWALK RAMP TYPE B — PGCC DPWAT STD. 300.08

CONCRETE SIDEWALK RAMP TYPE C — PGCC DPWAT STD. 300.09

CONCRETE SIDEWALK RAMP TYPE D — PGCC DPWAT STD. 300.10

CONCRETE SIDEWALK RAMP TYPE E — PGCC DPWAT STD. 300.11

CONCRETE SIDEWALK RAMP TYPE F — PGCC DPWAT STD. 300.12

CONCRETE SIDEWALK RAMP TYPE G — PGCC DPWAT STD. 300.13

CONCRETE SIDEWALK RAMP TYPE H — PGCC DPWAT STD. 300.14

CONCRETE SIDEWALK RAMP TYPE I — PGCC DPWAT STD. 300.15

CONCRETE SIDEWALK RAMP TYPE J — PGCC DPWAT STD. 300.16

CONCRETE SIDEWALK RAMP TYPE K — PGCC DPWAT STD. 300.17

CONCRETE SIDEWALK RAMP TYPE L — PGCC DPWAT STD. 300.18

CONCRETE SIDEWALK RAMP TYPE M — PGCC DPWAT STD. 300.19

CONCRETE SIDEWALK RAMP TYPE N — PGCC DPWAT STD. 300.20

CONCRETE SIDEWALK RAMP TYPE O — PGCC DPWAT STD. 300.21

CONCRETE SIDEWALK RAMP TYPE P — PGCC DPWAT STD. 300.22

CONCRETE SIDEWALK RAMP TYPE Q — PGCC DPWAT STD. 300.23

CONCRETE SIDEWALK RAMP TYPE R — PGCC DPWAT STD. 300.24

CONCRETE SIDEWALK RAMP TYPE S — PGCC DPWAT STD. 300.25

CONCRETE SIDEWALK RAMP TYPE T — PGCC DPWAT STD. 300.26

CONCRETE SIDEWALK RAMP TYPE U — PGCC DPWAT STD. 300.27


CONCRETE SIDEWALK RAMP TYPE V — PGCC DPWAT STD. 300.28

CONCRETE SIDEWALK RAMP TYPE W — PGCC DPWAT STD. 300.29


CONCRETE SIDEWALK RAMP TYPE X — PGCC DPWAT STD. 300.30

CONCRETE SIDEWALK RAMP TYPE Y — PGCC DPWAT STD. 300.31

CONCRETE SIDEWALK RAMP TYPE Z — PGCC DPWAT STD. 300.32

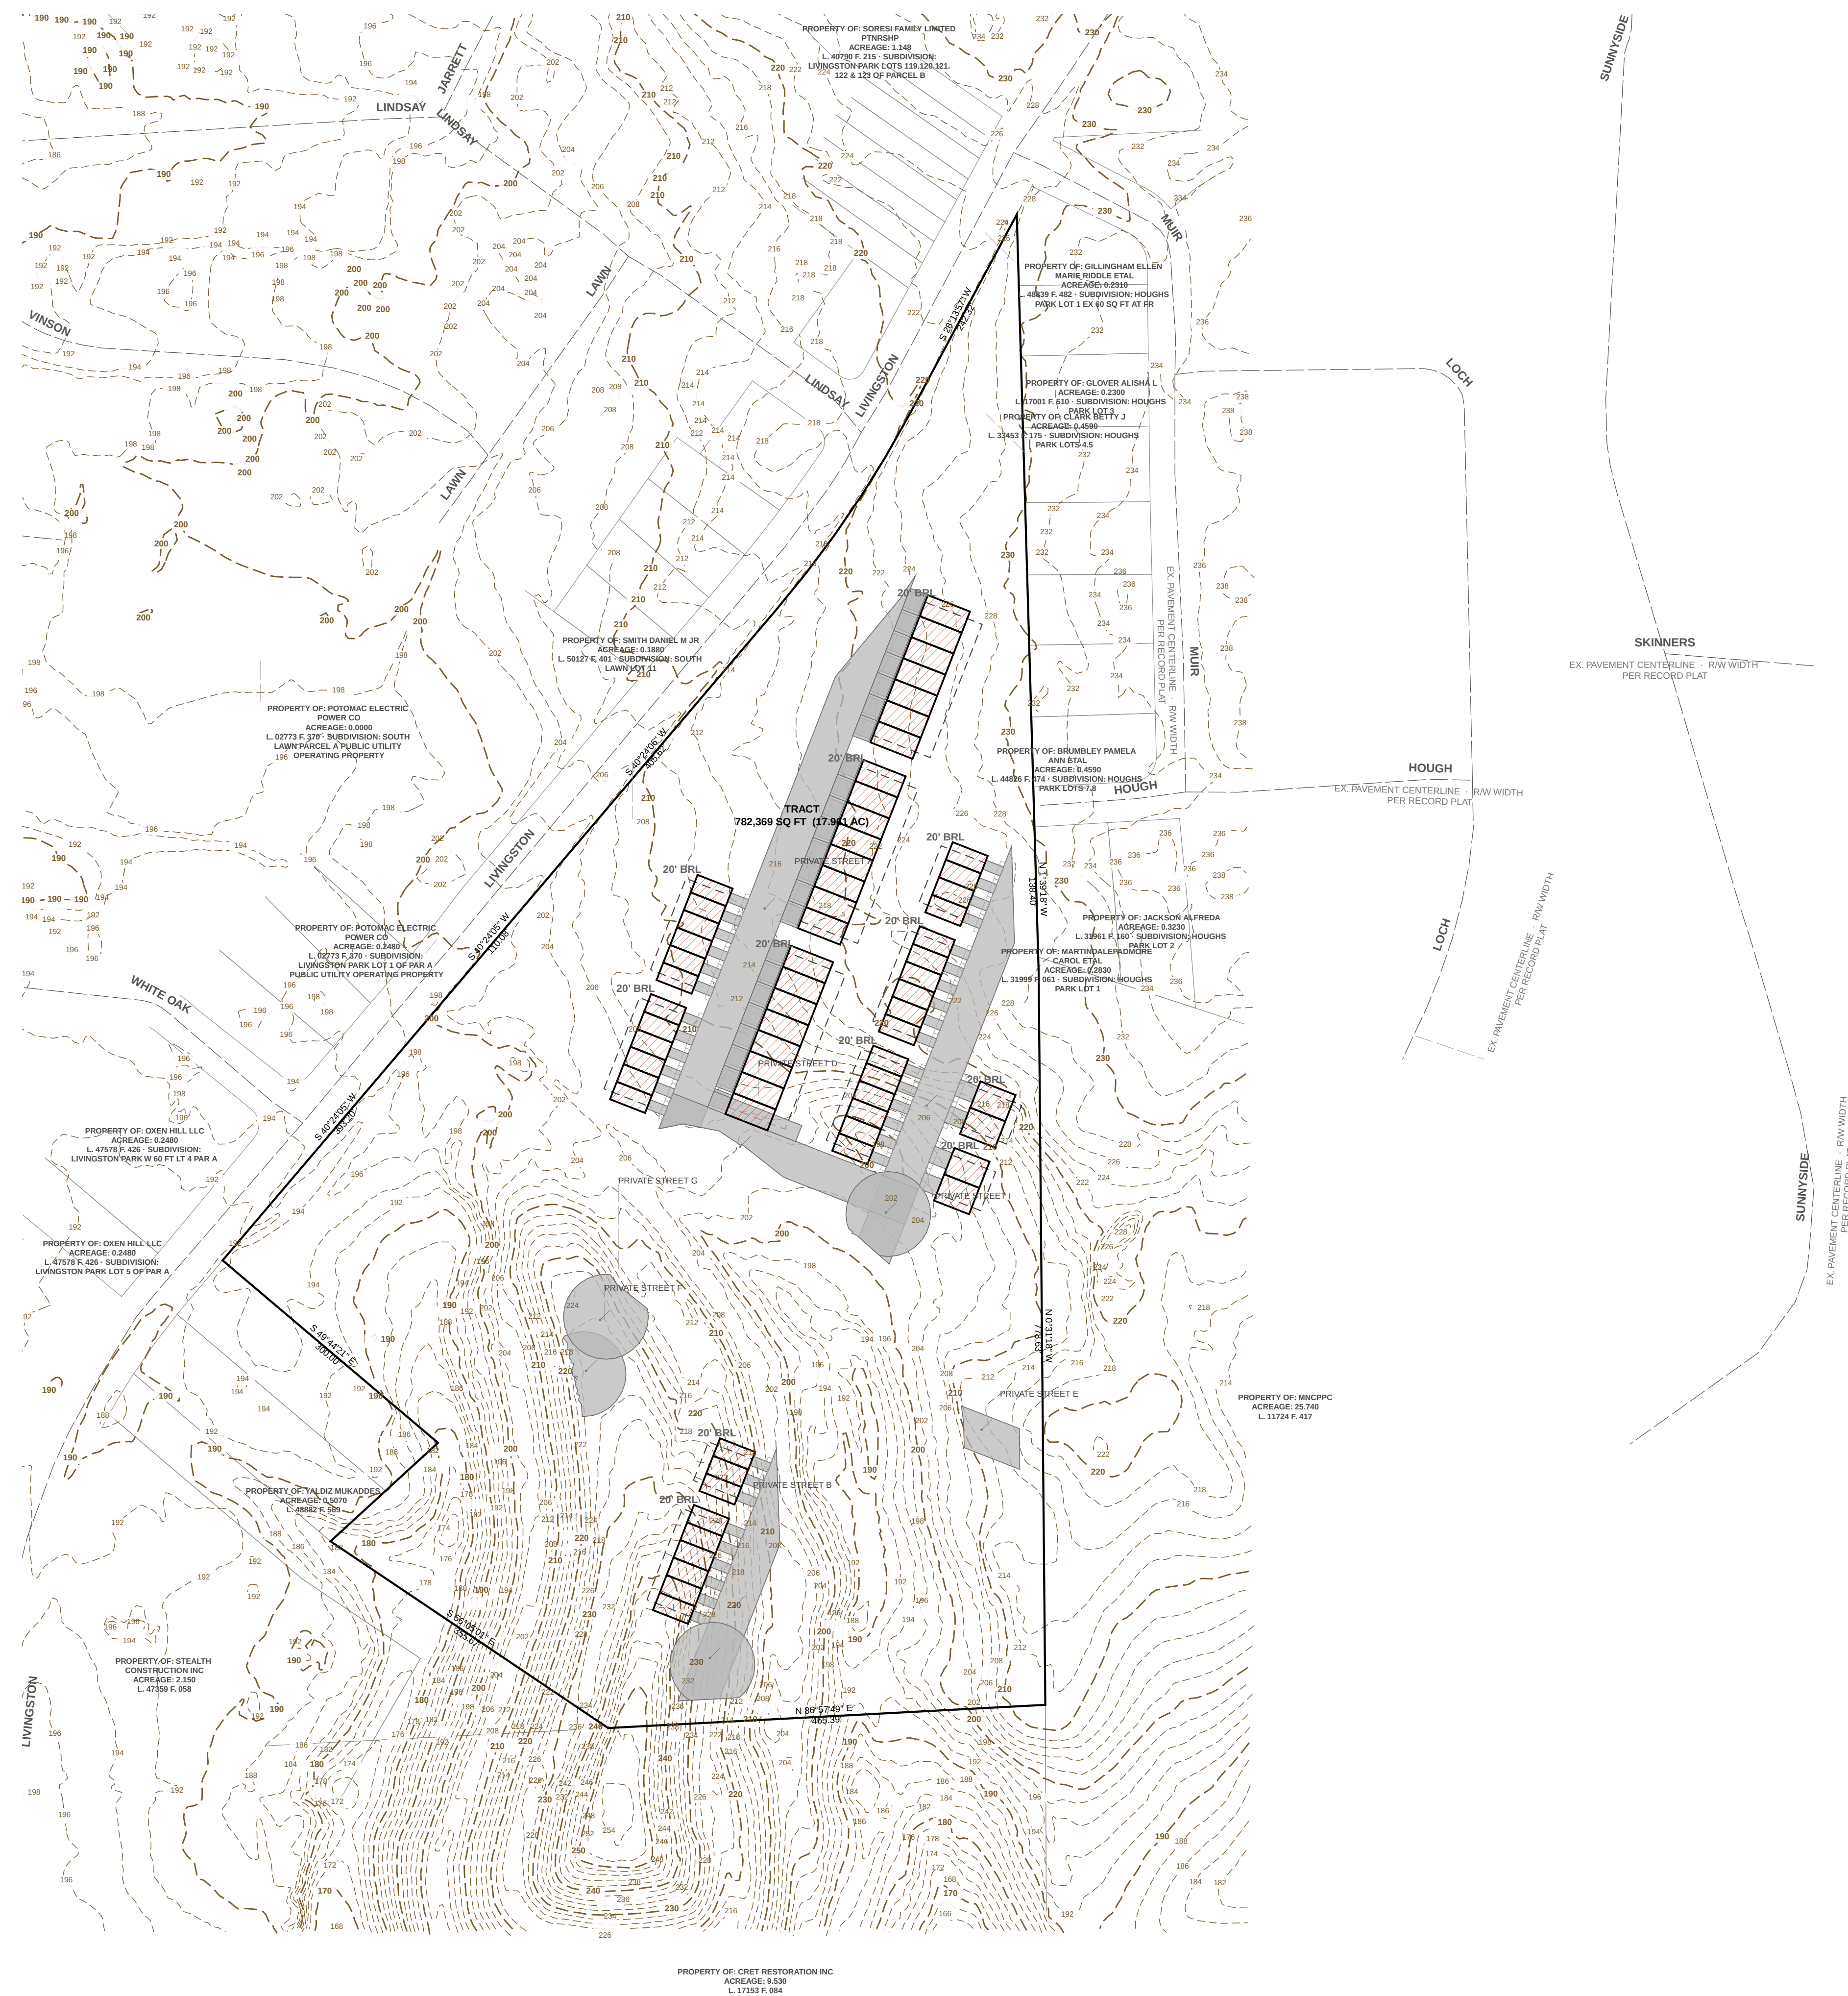

MAP UNIT	MAP UNIT NAME	K-FACT	HYDRIC	HYD. GRP	DRAINAGE CLASS
AuB	Adelphus silt loam, 2 to 5 percent slopes complex	.37	No	C	Modestly well drained
AuA	Adelphus-Agassiz complex, 0 to 2 percent slopes	.43	No	D	Somewhat poorly drained
AuB	Adelphus-Holmsted complex, 0 to 2 percent slopes	.24	No	BiD	Somewhat poorly drained
AuB	Adelphus-Holmsted complex, 2 to 5 percent slopes	.24	No	BiD	Somewhat poorly drained
AuC	Adelphus-Holmsted complex, 5 to 10 percent slopes	.24	No	BiD	Somewhat poorly drained

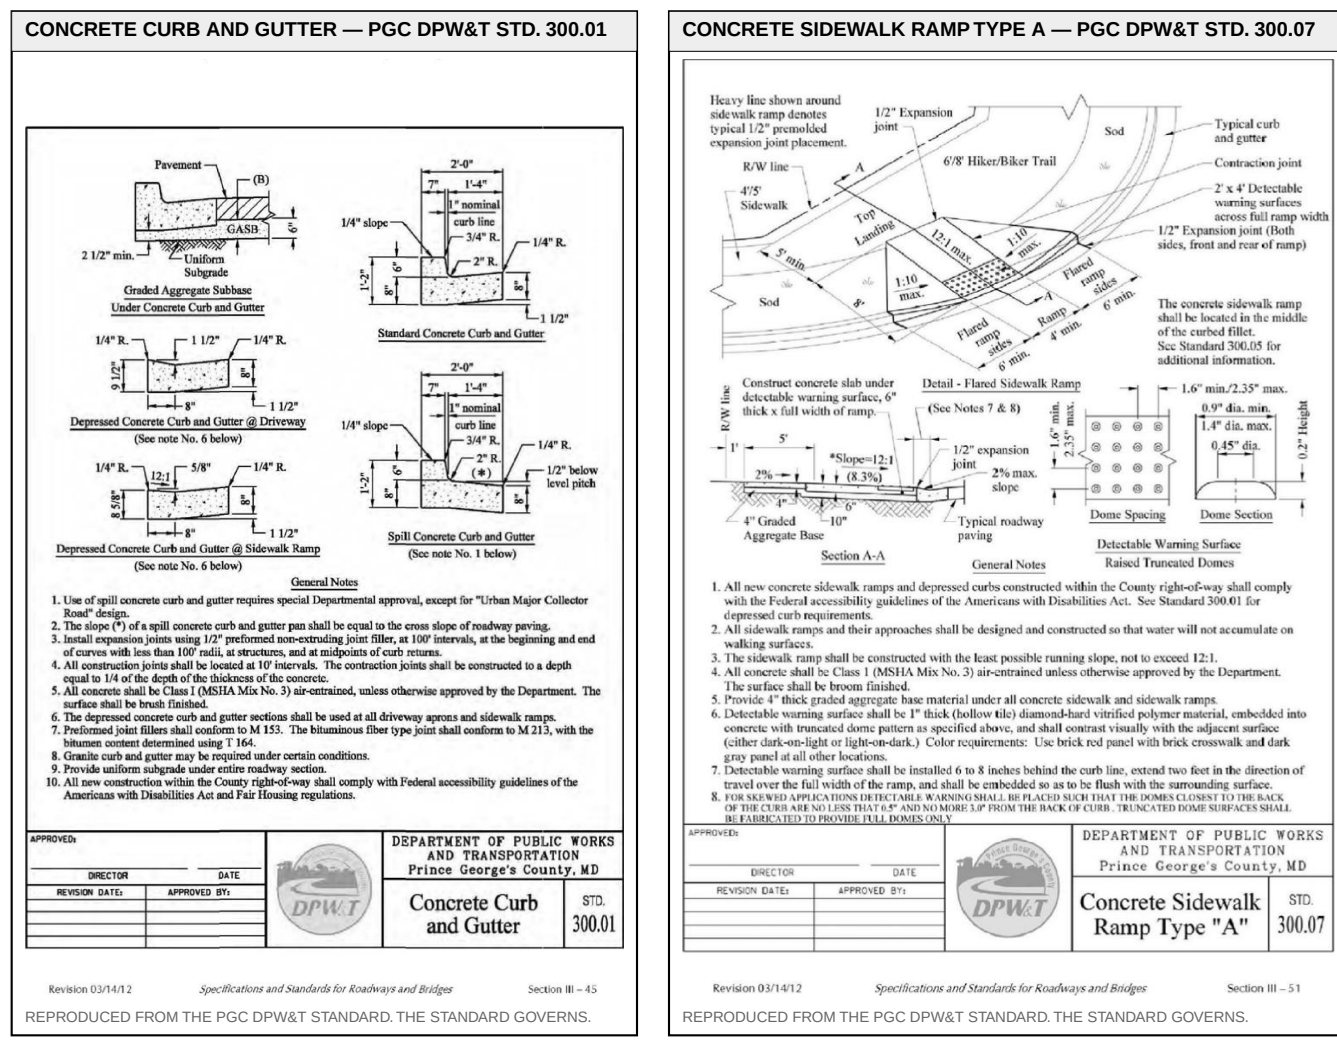

KEEALSE

design, build, deliver

PROJECT

7220 Livingston Road (Parcel 049, 18.07 ac, RMF-20) — townhouses, two-over-tens and duplexes

ADDRESS

ADJACENT (F 19800)

JURISDICTION

Prince George's County, Maryland

ZONE

RMF-20

PHASE

C-300 — Demolition Plan

SCALE

1" = 10'

DATE

REVISED

PRELIMINARY

SHEET NO.

4 OF 11

DOCUMENT REF.

EPSC0 2448

IN HANDS

V. NAVIG8 (net)

PLAN TYPE AND PREPARATION

PLAN TYPE

SITE DEVELOPMENT / FFE GRADING

SHEET

C-300 — Demolition Plan

DRAWN BY

Margaret Pridemore Engineer

DRAWN BY

KEEALSE SITE-PLAN ENGINEER

CHECKED BY

REVISIONS

NO.

DATE

DESCRIPTION

INDEX OF DRAWINGS

1 C-000	Cover Sheet, Approvals and General Notes
2 C-100	Existing Conditions and Boundary Plan
3 C-200	Overall Site and Zoning Plan
4 C-300	Demolition Plan
5 C-400	Grading and Drainage Plan
6 C-500	Utility Plan
7 C-600	Stormwater Management Plan
8 C-700	Sediment and Erosion Control Plan
9 C-800	Road, Driveway and Paving Plan
10 C-900	Civil Details
11 L-500	Landscape and Tree Canopy Plan

SITE DATA		
ZONE	RMF-20	
TAX / PARCEL ID	TRACT	
GROSS TRACT AREA	782,369 SF	17.961 AC
TRACT AREA	782,368 SF	17.961 AC
NET LOT AREA	782,368 SF	17.961 AC
LOT FRONTAGE	20 MIN	NOT
SETBACKS	REQUIRED	PROVIDED
FRONT YARD	—	—
SIDE YARD	—	—
REAR YARD	—	—
COVERAGE	MAX	PROPOSED
LOT COVERAGE	—	7.8%
BUILDING FOOTPRINT	—	60,896 SF
DATUM		
HORIZONTAL	EPSG 2248	NAD83
VERTICAL	NAVD88 (feet)	

SITE ANALYSIS	
1. Gross tract area	782,369 SF
2. Area of dwelling	60,896 SF
3. Wooded area	NOT ESTABLISHED
4. Floodplain area	NOT ESTABLISHED
5. Net lot area	782,369 SF
6. TOTAL AREA DISTURBED	0 SF
7. SWM REQUIRED — Sec. 32-174(a)(3) EXEMPT — 5,000 SF OR	

BUILDING DATA						
	G	B	FF	SP	RT	STY
LOFT 1						
LOFT 2						
SEQUENCE OF CONSTRUCTION	
1. Pre-construction meeting	1 DAY
2. Obtain necessary permits	2 DAYS
3. Notify Miss Utility at 811 at least 48 hours prior to any excavation	1 DAY
4. Install installed construction entrance and perimeter sediment control	2 DAYS
5. Rough grade the lot	5 DAYS
6. Construct dwelling	6 MONTHS
7. Install water, sewer and storm services and the driveway	10 DAYS
8. Fine grade and stabilize all disturbed areas	5 DAYS
9. Remove sediment control once the Inspector gives written permission	1 DAY

[illegible]


LEGEND

- PROPERTY BOUNDARY
- SBL – BUILDING RESTRICTION LINE
- PROPOSED STRUCTURE
- EXISTING CONTOUR – 2 FT INTERIOR, NAVIGABLE
- EXISTING CONTOUR – 2 FT INTERIOR
- STREET CENTRELINE
- PROPOSED PAVEMENT – DRIVEWAY / WALK
- EASEMENT
- SANITARY (LATERAL, DWO) – NEAREST
- WATER SERVICE (WKS)
- STORM DRAIN – TRUNK R/W
- STORM DRAIN – HOUSE CONNECTION TO TRUNK
- AVIATION SIDEWALK – INVERT AND GRADED SECTION
- RETAINING WALL – Ticks ON THE RETAINED SIDE
- 100 YD OF GRADED CORNER – TICKS ON THE EXPOSED SIDE
- 100 YD FLOODPLAIN LIMIT EXISTING GROUND – FPD 70077 WSSC DATUM, UNITED STATES
- 100 YD FLOODPLAIN LIMIT PROPOSED GROUND – SAME ELEVATION, DEGRADED SURFACE
- ESD – STORMWATER PRACTICE

[illegible]

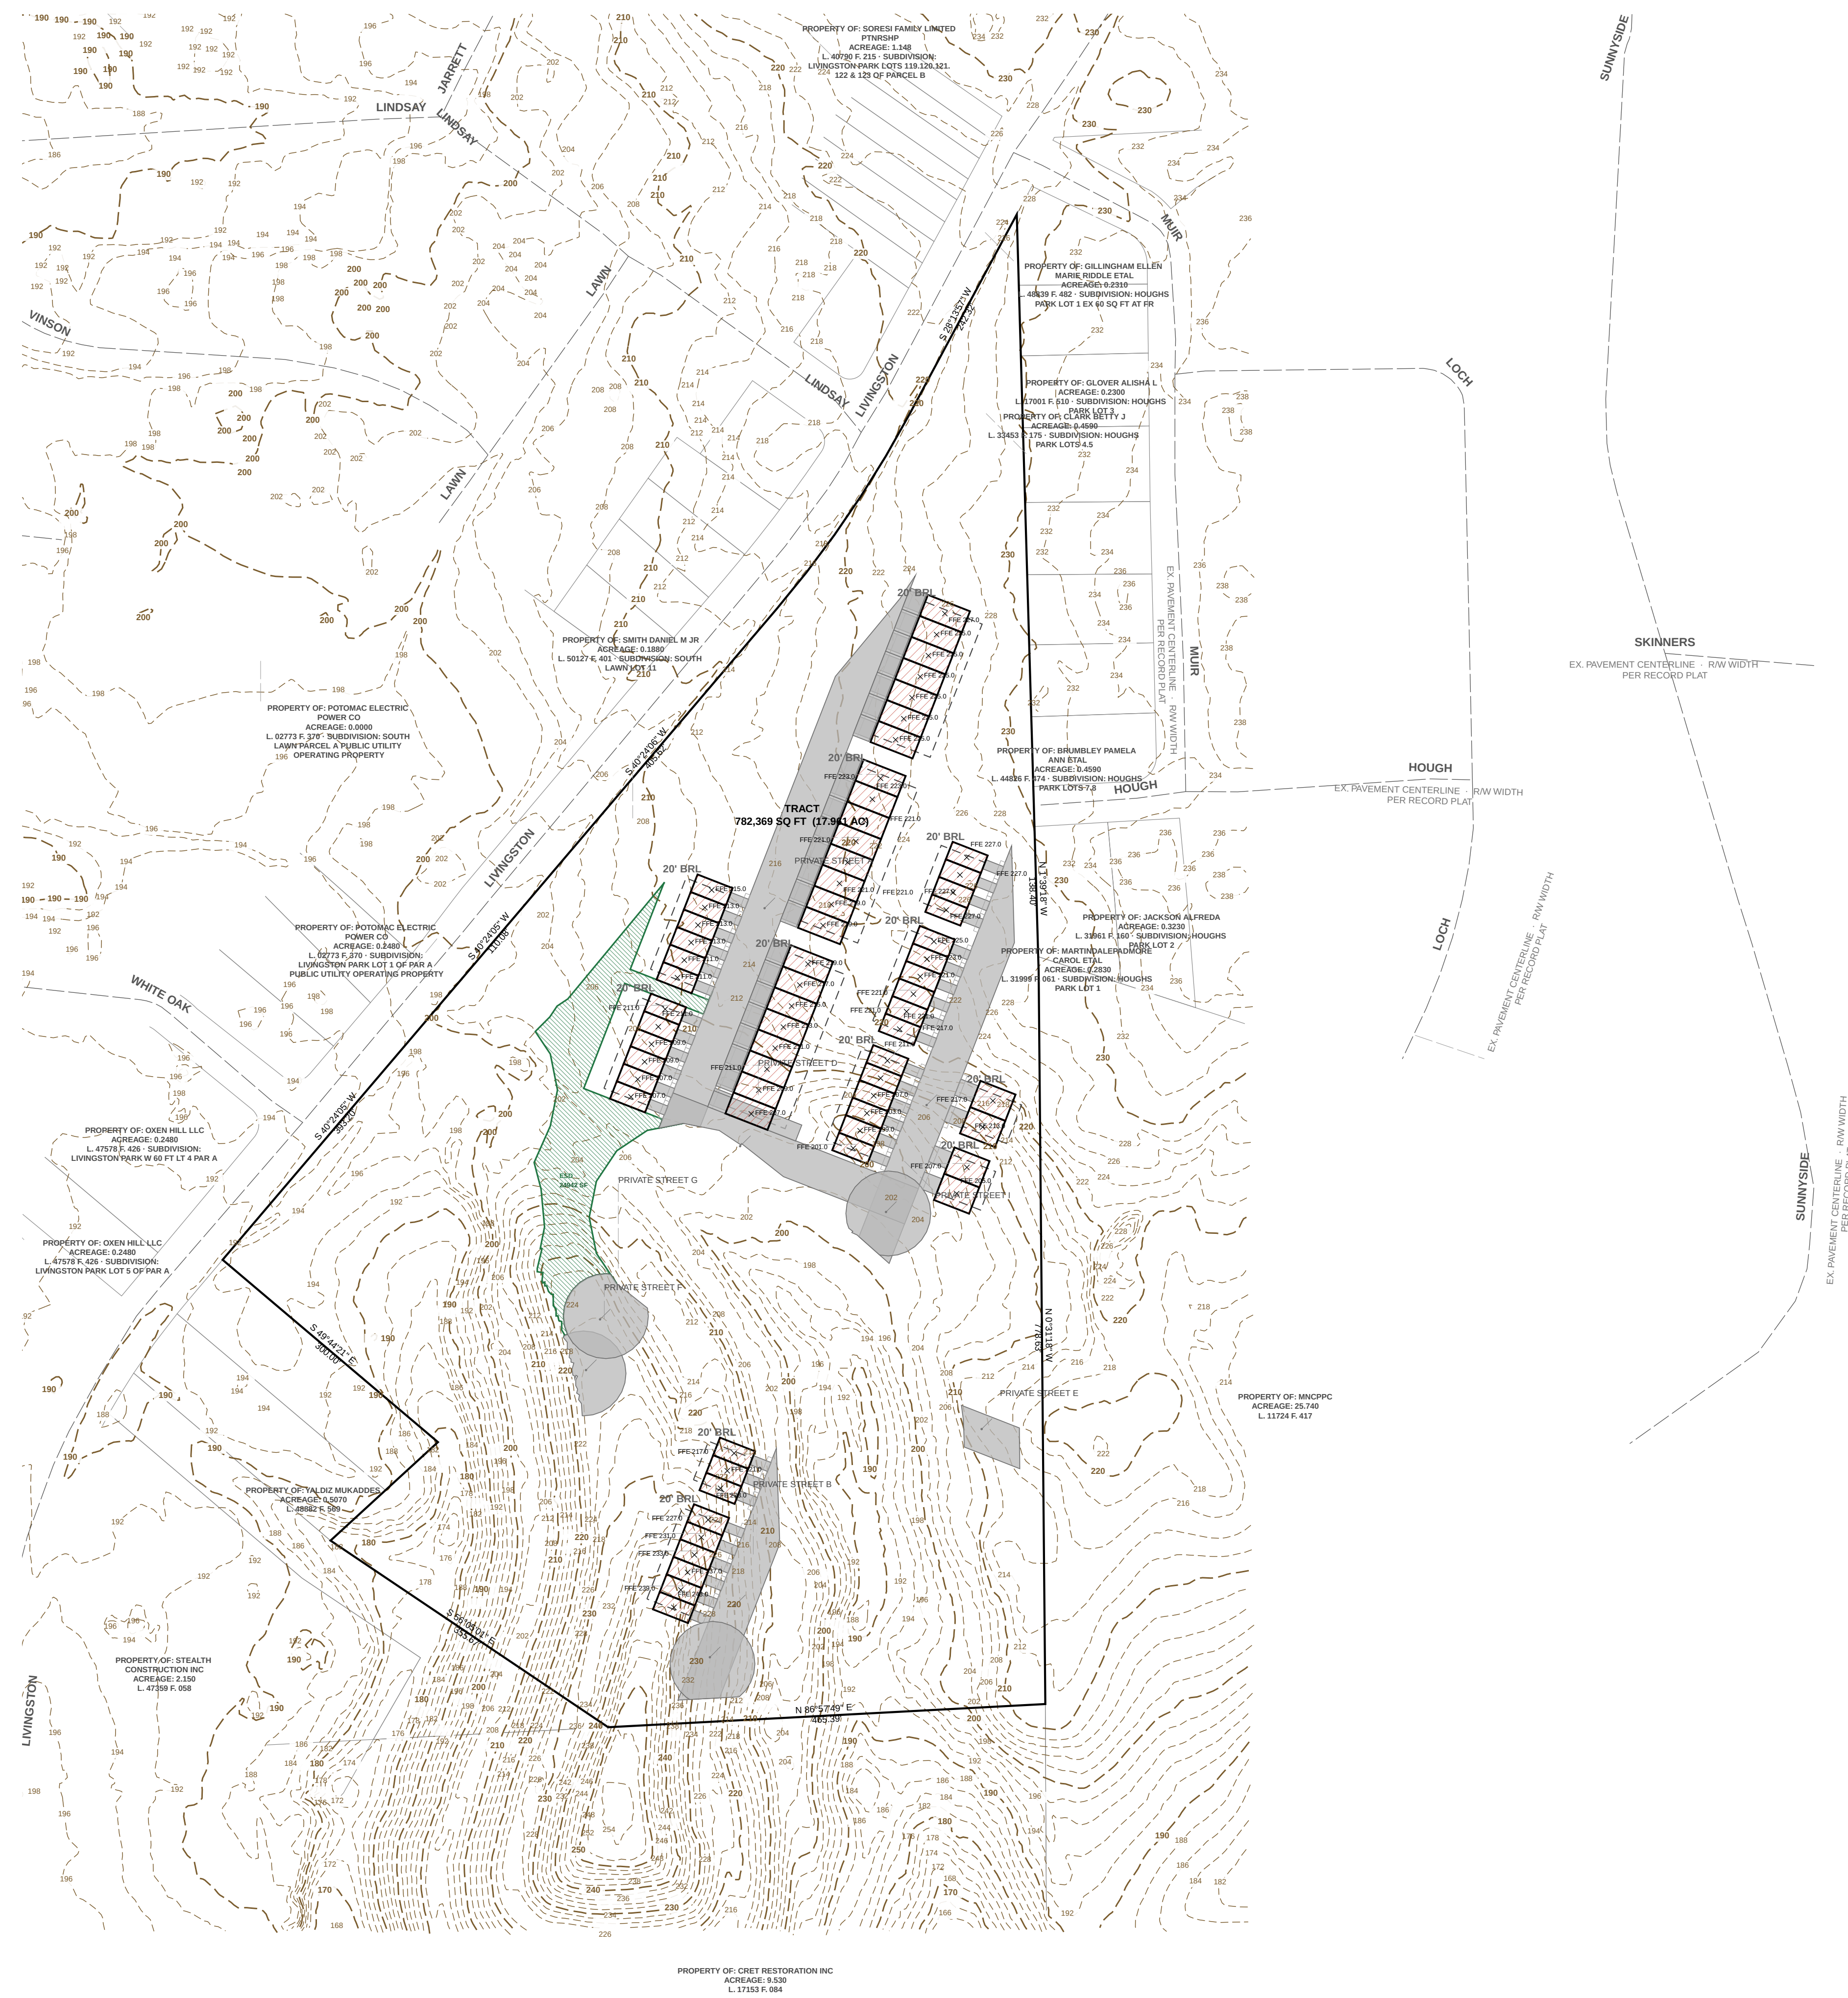

MAP UNIT	MAP UNIT NAME	K-FACT	HYDRIC	HYD. GRP	DRAINAGE CLASS
AuB	Adelphiya silt loam, 2 to 5 percent slopes complex	.37	No	C	Moderately well drained
AuA	Adelphiya-Ayazoo complex, 0 to 2 percent slopes	.43	No	D	Somewhat poorly drained
AuA	Adelphiya-Holmdel complex, 0 to 2 percent slopes	.24	No	B/D	Somewhat poorly drained
AuA	Adelphiya-Holmdel complex, 2 to 5 percent slopes	.24	No	B/D	Somewhat poorly drained
AuC	Adelphiya-Holmdel complex, 5 to 10 percent slopes	.24	No	B/D	Somewhat poorly drained

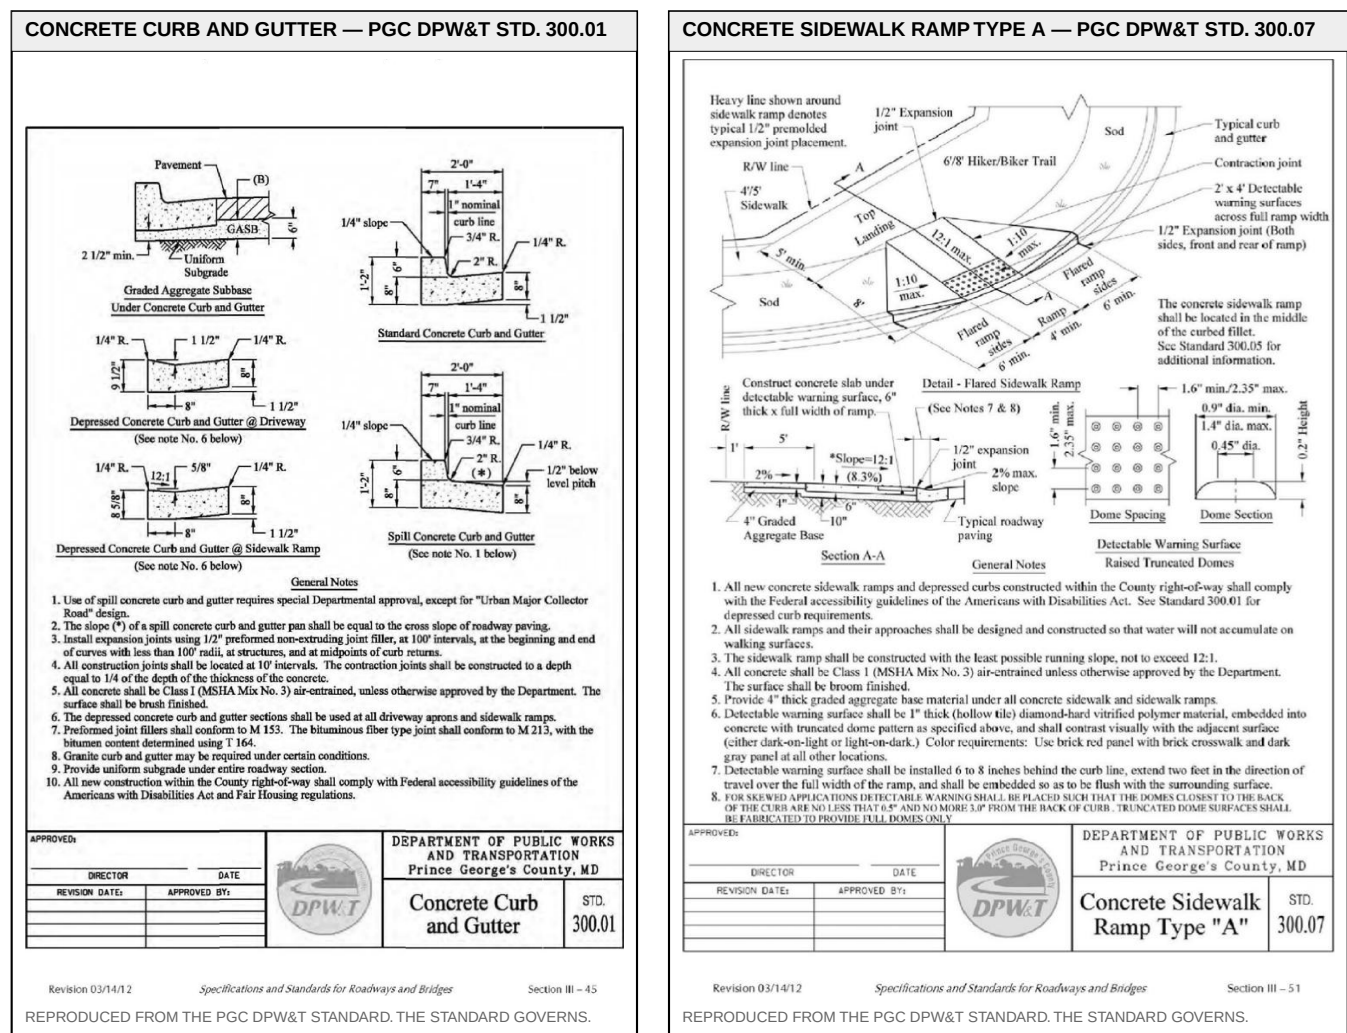

KEALEE design, build, deliver	
PROJECT	2220 Livingston Road (Parcel 049, 18.07 ac, RMF-20) — townhouses, two-over-tens and duplexes
ADDRESS	ADJUNCT 1 (19800)
JURISDICTION	Prince George's County, Maryland
ZONE	RMF-20
PHASE	C-400 — Grading and Drainage Plan
SCALE	1" = 100'
STUDIES	PRELIMINARY
DRAWN BY	5 OF 11
COORDINATED BY	
EPSCD 2448	
IN HANDS	V. NAVOS (net)

SITE DATA		
ZONE	RMF-20	
TAX / PARCEL ID	TRACT	
GROSS TRACT AREA	782,369 SF	17.961 AC
TRACT AREA	782,368 SF	17.961 AC
NET LOT AREA	782,368 SF	17.961 AC
LOT FRONTAGE	20' MIN	NOT
SETBACKS	REQUIRED	PROVIDED
FRONT YARD	—	—
SIDE YARD	—	—
REAR YARD	—	—
COVERAGE	MAX	PROPOSED
LOT COVERAGE	—	7.8%
BUILDING FOOTPRINT	—	60,896 SF
DATUM		
HORIZONTAL	NAD83 2248	NAD83
VERTICAL	EVSD88 (feet)	

SITE ANALYSIS	
1. Gross tract area	782,369 SF
2. Area of dwelling	60,896 SF
3. Wooded area	NOT ESTABLISHED
4. Floodplain area	NOT ESTABLISHED
5. Net lot area	782,369 SF
6. TOTAL AREA DISTURBED	0 SF
7. SWM REQUIRED — Sec. 32-174(a)(3) EXEMPT — 5,000 SF OR	

BUILDING DATA	G	B	FF	SF	HT	STY
LOFT 1	---	---	---	---	---	---
LOFT 2	---	---	---	---	---	---
LOFT 3	---	---	---	---	---	---
LOFT 4	---	---	---	---	---	---
LOFT 5	---	---	---	---	---	---
LOFT 6	---	---	---	---	---	---
LOFT 7	---	---	---	---	---	---
LOFT 8	---	---	---	---	---	---
LOFT 9	---	---	---	---	---	---
LOFT 10	---	---	---	---	---	---
LOFT 11	---	---	---	---	---	---
LOFT 12	---	---	---	---	---	---
LOFT 13	---	---	---	---	---	---
LOFT 14	---	---	---	---	---	---
LOFT 15	---	---	---	---	---	---
LOFT 16	---	---	---	---	---	---
LOFT 17	---	---	---	---	---	---
LOFT 18	---	---	---	---	---	---
LOFT 19	---	---	---	---	---	---
LOFT 20	---	---	---	---	---	---
LOFT 21	---	---	---	---	---	---
LOFT 22	---	---	---	---	---	---
LOFT 23	---	---	---	---	---	---
LOFT 24	---	---	---	---	---	---
LOFT 25	---	---	---	---	---	---
LOFT 26	---	---	---	---	---	---
LOFT 27	---	---	---	---	---	---
LOFT 28	---	---	---	---	---	---
LOFT 29	---	---	---	---	---	---
LOFT 30	---	---	---	---	---	---
LOFT 31	---	---	---	---	---	---
LOFT 32	---	---	---	---	---	---
LOFT 33	---	---	---	---	---	---
LOFT 34	---	---	---	---	---	---
LOFT 35	---	---	---	---	---	---
LOFT 36	---	---	---	---	---	---
LOFT 37	---	---	---	---	---	---
LOFT 38	---	---	---	---	---	---
LOFT 39	---	---	---	---	---	---
LOFT 40	---	---	---	---	---	---
LOFT 41	---	---	---	---	---	---
LOFT 42	---	---	---	---	---	---
LOFT 43	---	---	---	---	---	---
LOFT 44	---	---	---	---	---	---
LOFT 45	---	---	---	---	---	---
LOFT 46	---	---	---	---	---	---
LOFT 47	---	---	---	---	---	---
LOFT 48	---	---	---	---	---	---
LOFT 49	---	---	---	---	---	---
LOFT 50	---	---	---	---	---	---
LOFT 51	---	---	---	---	---	---
LOFT 52	---	---	---	---	---	---
LOFT 53	---	---	---	---	---	---
LOFT 54	---	---	---	---	---	---
LOFT 55	---	---	---	---	---	---
LOFT 56	---	---	---	---	---	---
LOFT 57	---	---	---	---	---	---
LOFT 58	---	---	---	---	---	---
LOFT 59	---	---	---	---	---	---
LOFT 60	---	---	---	---	---	---
LOFT 61	---	---	---	---	---	---
LOFT 62	---	---	---	---	---	---
LOFT 63	---	---	---	---	---	---
LOFT 64	---	---	---	---	---	---

SEQUENCE OF CONSTRUCTION	
1. Pre-construction meeting	1 DAY
2. Obtain necessary permits	2 DAYS
3. Notify MCW Utility at 812 at least 48 hours prior to any excavation	1 DAY
4. Install stabilized construction entrance and perimeter sediment control	2 DAYS
5. Rough grade the lot	5 DAYS
6. Construct dwelling	6 MONTHS
7. Install water, sewer and storm services and the driveway	10 DAYS
8. Fine grade and stabilize all disturbed areas	5 DAYS
9. Remove sediment control once the Inspector gives written permission	1 DAY

GENERAL NOTES

1. CONTRACTOR SHALL CONTACT MISSISSAUGA UTILITIES AT 905.874.1400 FOR ALL INFORMATION OF RECORDS PRIOR TO ANY EXCAVATION. ERECTION, REMOVAL AND REPAIR BY TEST PIT WORKING CONTRACTOR SHALL BE AT HIS OWN RISK.

SEC 30-146


2. PROPOSED GRADE SHOWN SLOWS EXISTING GRADE SHOWN DRAINAGE.

3. ROADSIDE/PAVEMENT GRADINGS AND UTILITIES EXISTENCES SHOWN TO BE CORRECT.

4. BOUNDARY SURVEY IS THE RECORDED PLAT FOR SUBDIVISION OF BROWN EMBERS - 1 LITTLE BEAR CREEK PLAT 133-1, 133-2, 133-3, 133-446,

- LEADING
 - PROPERTY BOUNDARY
 - BRL – BUILDING RESTRICTION LINE
 - PROPOSED STRUCTURE
 - EXISTING CONTOUR – 2 FT INTERNAL, NAVD83
 - PROPOSED CONTOUR – 2 FT INTERNAL
 - STREET CENTRELINE
 - PROPOSED PAVEMENT – DRIVEWAY / WALK
 - EASEMENT
 - ENTRITY (LATERAL, CONC) – NEAREST
 - WATER SERVICE (WAP)
 - STORM DRAIN – TRUNK RCP
 - STORM – HOUSE CONNECTION TO TRUNK
 - ADVANCE SLIDE – INVERT AND GRADED SECTION
 - RETAINING WALL – Ticks ON THE RETAINED SIDE
 - 100' FT ADVANCE CROWN – NORTH ON THE EXISTING
 - 100' FT FLOODPLAIN LIMIT EXISTING GROUND – FPS-7707; WISC DRAIN, UNITED
 - 20' FT FLOODPLAIN LIMIT PROPOSED GROUND – SAME ELEVATION, REDUCED SLOPE
 - STORMWATER PRACTICE

[illegible]

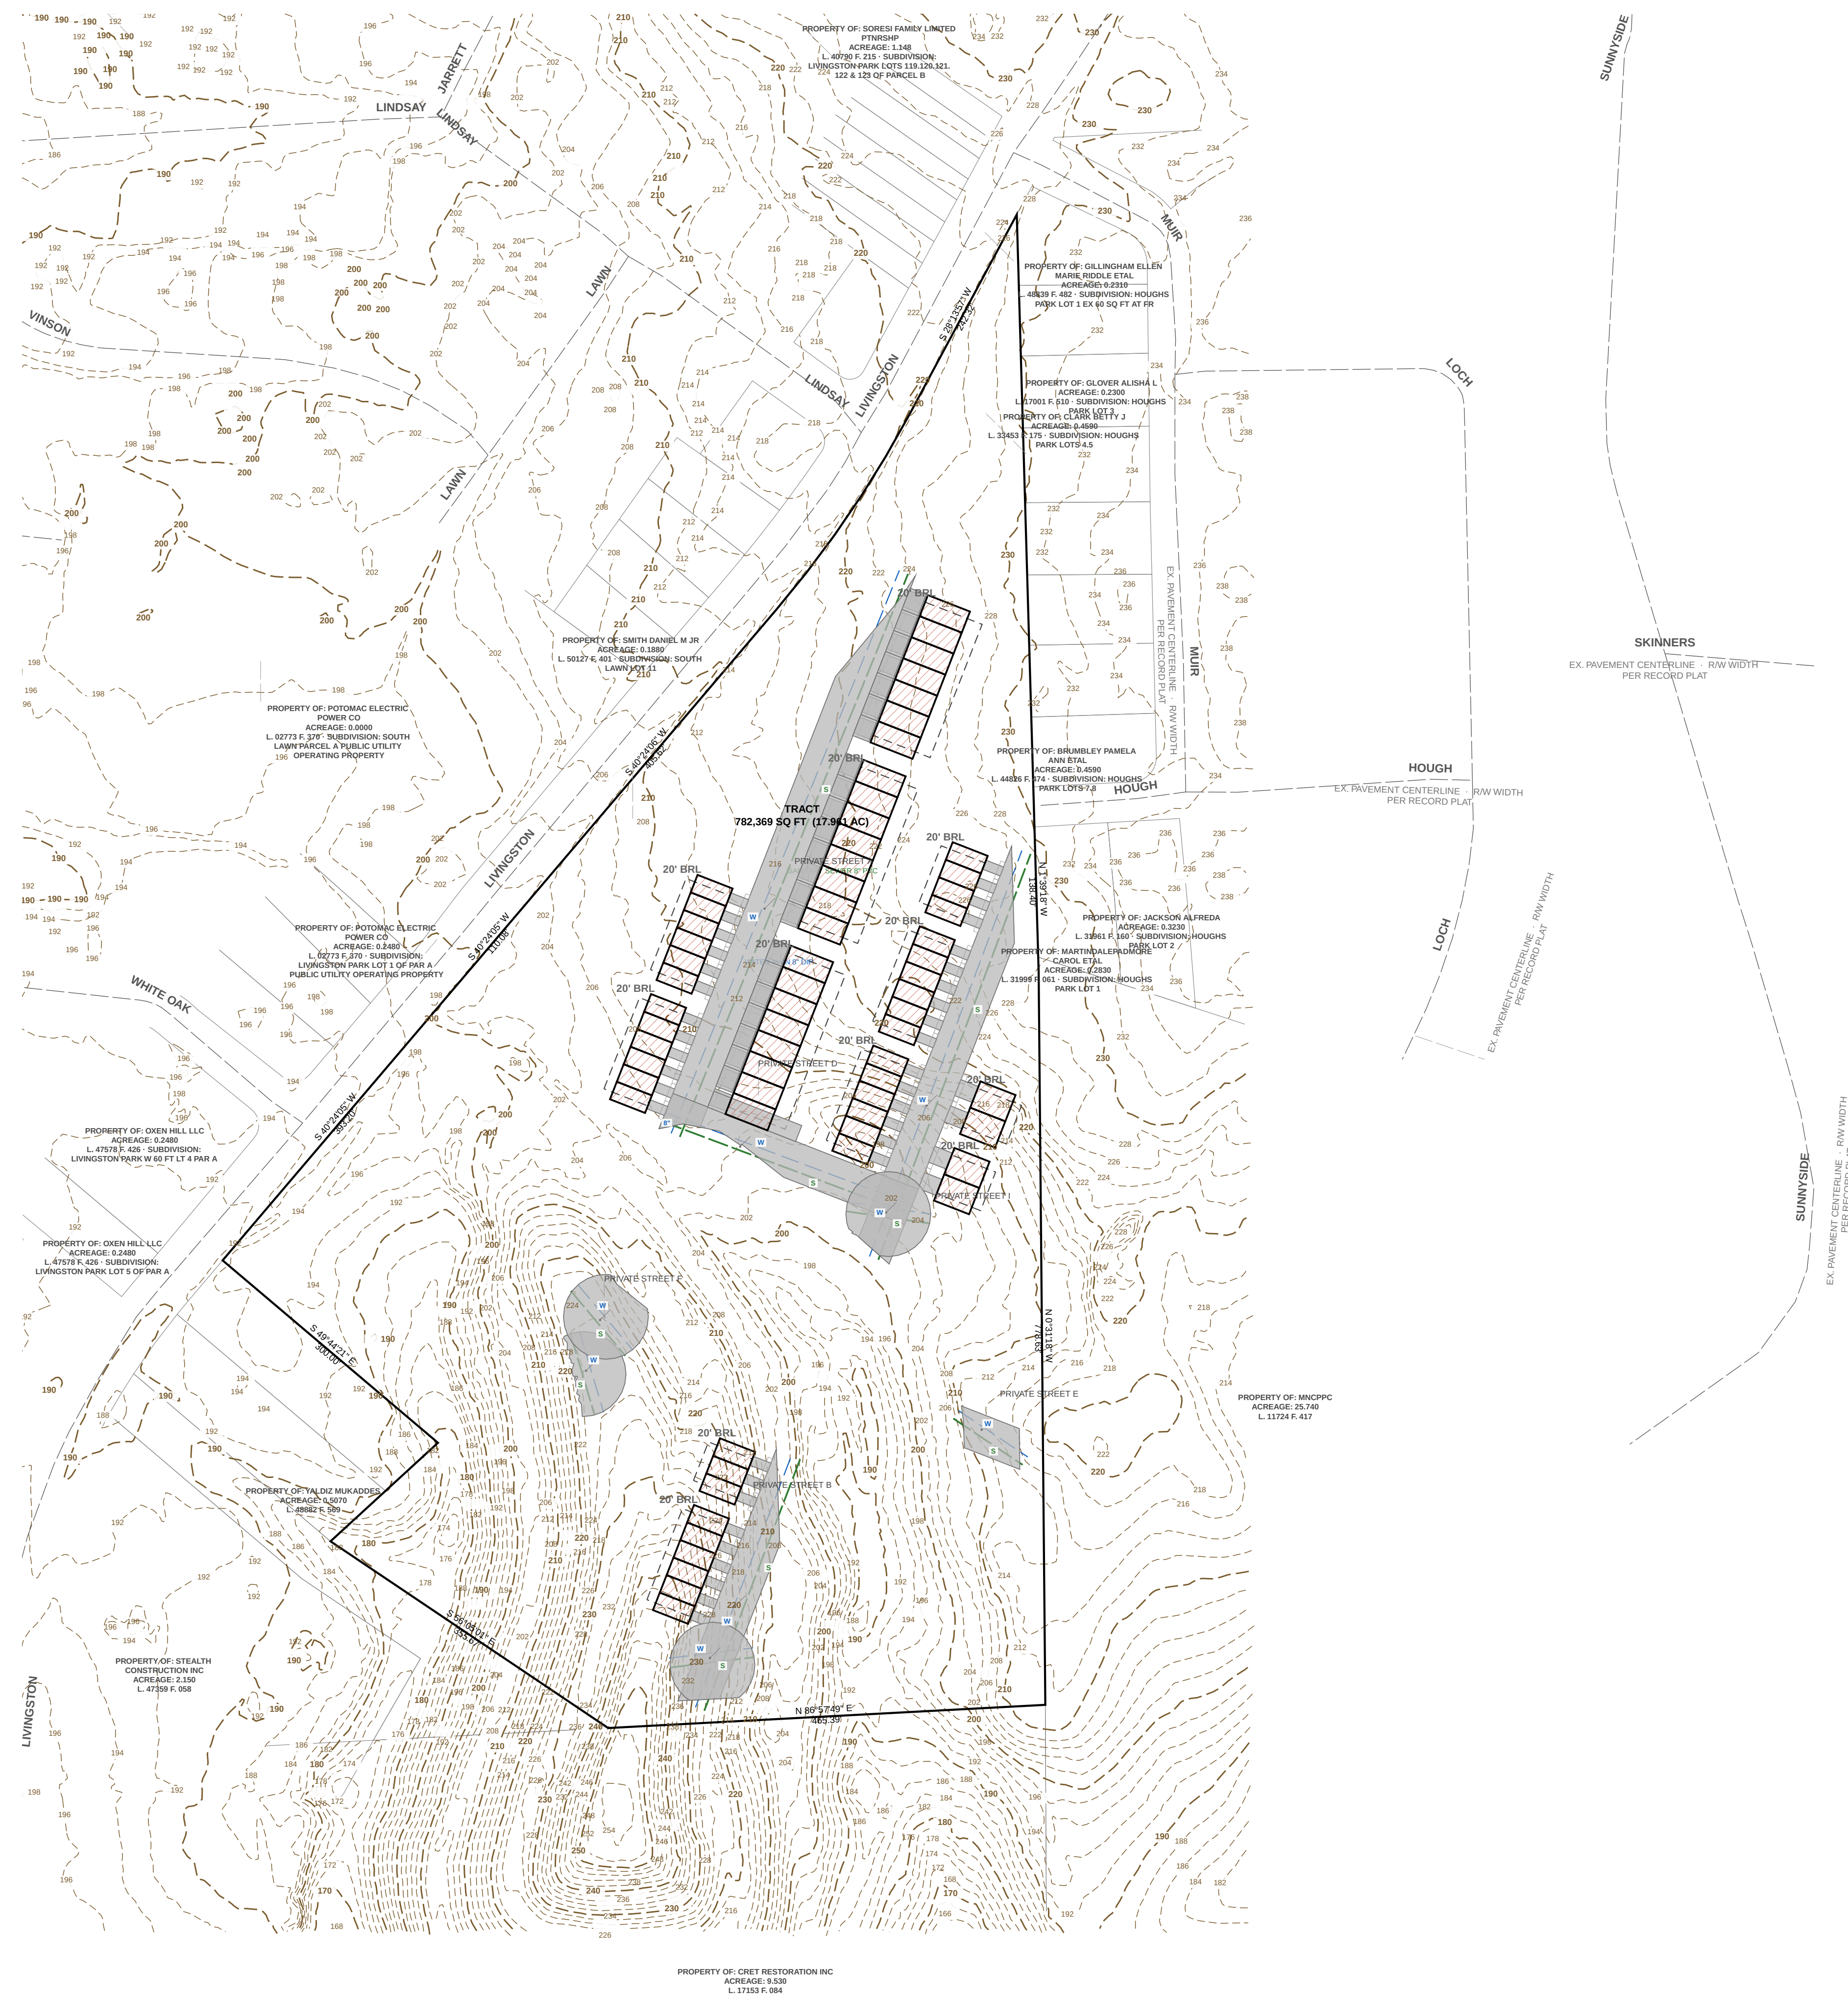

KEELEE
 (design, build, deliver)
 PROJECT
 7720 Langston Road (Parcel 049, 18.07 ac, RMF-20) — townhouses, two-over-tos and duplexes
 ADDRESS
 (OWNER: F 15800)
 APPROXIMATE
 Prince George's County, Maryland
 ZONE
 RMF-20
 PHASE
 C-500 — Utility Plan
 SCALE
 1" = 100'
 DRAWN BY
 PRELIMINARY
 SHEET NO.
 6 OF 11
 EPOCH PROJECT
 EPOCH 2048
 N. H. NABER
 V. NAVOSB (rev)

INDEX OF DRAWINGS

1	C-000	Cover Sheet, Approvals and General Notes
2	C-100	Existing Conditions and Boundary Plan
3	C-200	Overall Site and Zoning Plan
4	C-300	Demolition Plan
5	C-400	Grading and Drainage Plan
6	C-500	Utility Plan
7	C-600	Stormwater Management Plan
8	C-700	Sediment and Erosion Control Plan
9	C-800	Road, Driveway and Paving Plan
10	C-900	Civil Details
11	L-100	Landscape and Tree Canopy Plan

SITE DATA	
ZONE	TRACT
TAX PARCEL ID	RW-2
CROSS TRACT AREA	782.569 SF 17,961 AC
TRACT AREA	782.569 SF 17,961 AC
NET LOT AREA	782.365 SF 17,961 AC
NET LOT AREA	29' MIN
LOT FRONTAGE	REQUIRED
FRONT YARD	PROPOSED
REAR YARD	---
SIDE YARD	---
REAR YARD	---
COVERAGE	MAX PROPOSED
LOT COVERAGE	7.8%
BUILDING FOOTPRINT	60,896 SF
DATUM	
HORIZONTAL	EPSC 2248
VERTICAL	NAD83

SITE ANALYSIS	
1. Gross tract area	782,369 SF
2. Area of dwelling	60,896 SF
3. Wooded area	NOT ESTABLISHED
4. Floodplain area	NOT ESTABLISHED
5. Net lot area	782,369 SF
6. TOTAL AREA DISTURBED	0 SF
7. SWM REQUIRED — Sec. 32-174(a)(3) EXEMPT — 5,000 SF OR	

BUILDING DATA	G	B	#F	SP	ST	STY
LOFT 1						
LOFT 2						
SEQUENCE OF CONSTRUCTION

1. Pre-construction meeting	1 DAY
2. Obtain necessary permits	2 DAYS
3. Notify Miss Utility at 811 at least 48 hours prior to any excavation	2 DAYS
4. Install stabilized construction entrance and perimeter sediment control	1 DAY
5. Rough grade the lot	5 DAYS
6. Construct dwelling	6 MONTHS
7. Install water, sewer and storm services and the driveway	10 DAYS
8. Fine grade and stabilize all disturbed areas	5 DAYS
9. Remove sediment control once the inspector gives written permission	1 DAY

[illegible]

LEGEND

- PROPERTY BOUNDARY
- BRL – BUILDING RESTRICTION LINE
- PROPOSED STRUCTURE
- EXISTING CONTOUR – 2 FT INTERVAL, NAVSIBS
- PROPOSED CONTOUR – 2 FT INTERVAL
- STREET CENTRELINE
- PROPOSED PAVEMENT – PPS INTERLOCK
- EASEMENT
- WATER LATERAL (DW) – HIGHEST
- WATER SERVICE (WWS)
- STORM DRAIN – TRUNK PIPE
- STORM – HOUSE CONNECTION TO TRUNK
- CHANGE WASTE – INVERT AND DRAINER SECTION
- RETAINING WALL – TIES ON THE RETAINED SIDE
- LIMIT OF SHEDS COVERED BY THE STORM DRAIN
- 10' FLOODPLAIN LIMIT EXISTING GROUND, FFS 7002; WSSIC DATA, UNITED
- 20' FLOODPLAIN LIMIT PROPOSED GROUND, FFS 7002; WSSIC DATA, UNITED
- STORMWATER PRACTICE

PLAN OF RECORD

DATE: _____ LOTS: _____ TRACT: _____ LAR 9215 P 213 - parcel of record
EASTERN EQUITIES, L.L.C. (PMA#s Addressed)


NOTES OF RECORD

1. PRELIMINARY boundaries are the county parcel lines (compiled from the nearest plat, not surveyed). A boundary survey is required.

2. **2.1. 2000 +/-**

3. 1. 2. 3. 

| MAP UNIT | MAP UNIT NAME | K-FACT | HYDRIC | HYD. GRP | DRAINAGE CLASS |
|----------|---|--------|--------|----------|-------------------------|
| AdA | Adelphi silt loam, 2 to 5 percent slopes complex | .37 | No | C | Moderately well drained |
| AdA | Adelphi-Agassico complex, 0 to 2 percent slopes | .43 | No | D | Somewhat poorly drained |
| AdC | Adelphi-Holmcliff complex, 0 to 2 percent slopes | .24 | No | B/D | Somewhat poorly drained |
| AdC | Adelphi-Holmcliff complex, 2 to 5 percent slopes | .24 | No | B/D | Somewhat poorly drained |
| AdC | Adelphi-Holmcliff complex, 5 to 10 percent slopes | .24 | No | B/D | Somewhat poorly drained |

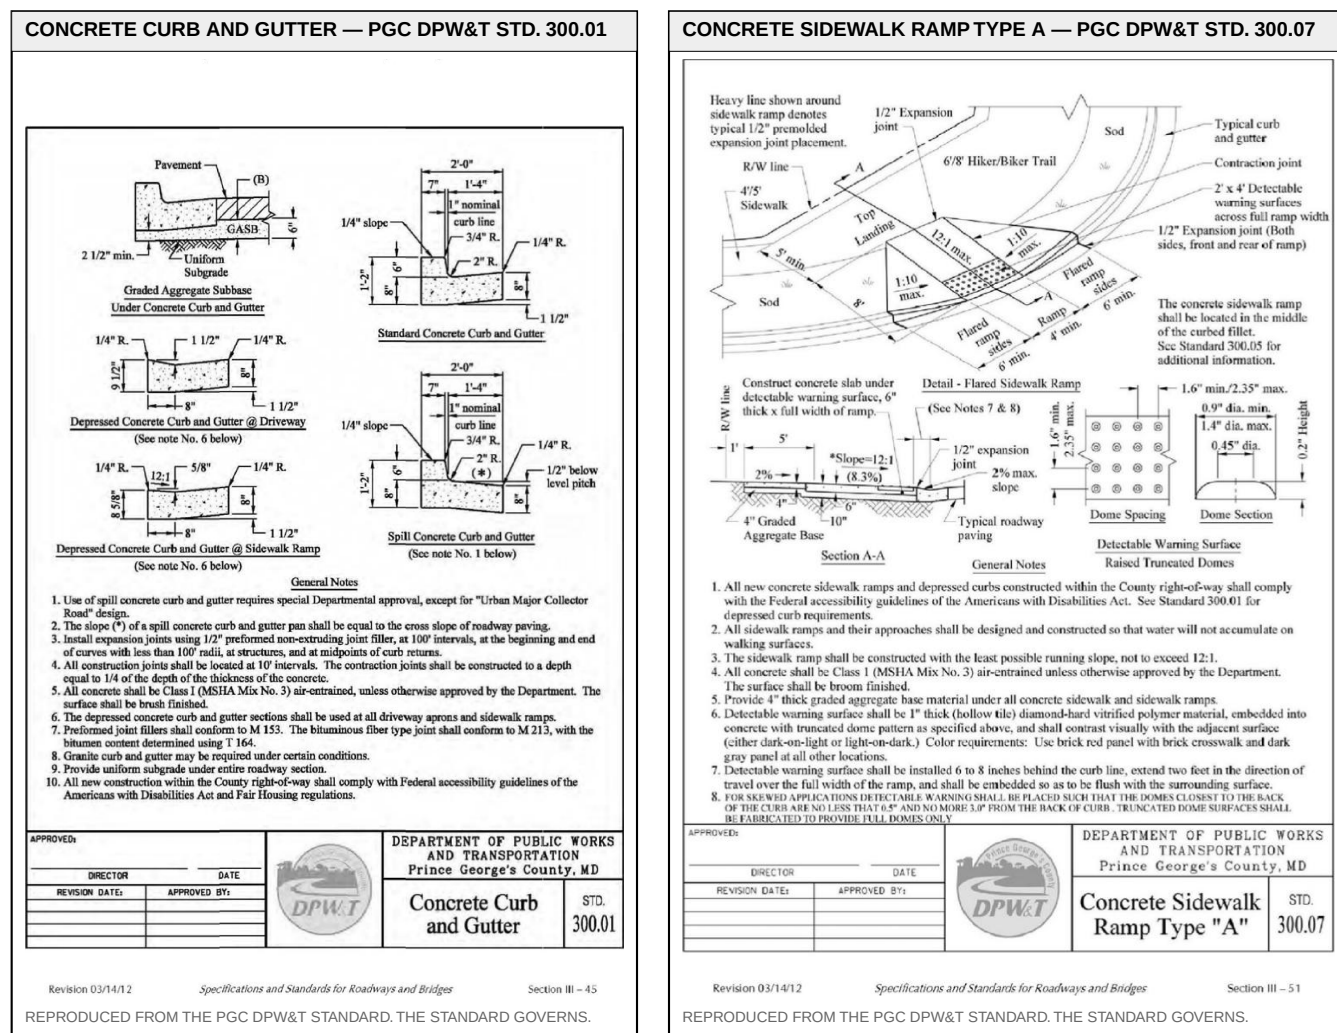

INDEX OF DRAWINGS

| | | |
|----|-------|--|
| 1 | C-000 | Cover Sheet, Approvals and General Notes |
| 2 | C-100 | Existing Conditions and Boundary Plan |
| 3 | C-200 | Overall Site and Zoning Plan |
| 4 | C-300 | Demolition Plan |
| 5 | C-400 | Grading and Drainage Plan |
| 6 | C-500 | Utility Plan |
| 7 | C-600 | Stormwater Management Plan |
| 8 | C-700 | Sediment and Erosion Control Plan |
| 9 | C-800 | Road, Driveway and Paving Plan |
| 10 | C-900 | Civil Details |
| 11 | L-100 | Landscape and Tree Canopy Plan |

| SITE ANALYSIS | |
|--------------------------------------|----------------------|
| 1. Gross tract area | 782,369 SF |
| 2. Area of dwelling | 60,896 SF |
| 3. Wooded area | NOT ESTABLISHED |
| 4. Floodplain area | NOT ESTABLISHED |
| 5. Net lot area | 782,369 SF |
| 6. TOTAL AREA DISTURBED | 0 SF |
| 7. SWIM REQUIRED — Sec. 32-174(a)(3) | EXEMPT — 5,000 SF OR |

C garage slab - B basement - FF finished floor - SF subfloor - HT height - STY stoneys. A DASH IS NOT ZERO; the elevation has not been established and must be set from a field-run topographic survey before construction.

TOTAL ESTIMATED TIME OF CONSTRUCTION: 8 MONTHS

LEGEND

PLAT OF RECORD
(ADMIN is 10000) — 1. date of record plat 1. 40210 E 213 — number of record

LOT n — proposed fee-sample lot - PRIVATE STREET A... — HSA street, 2...

| | | | | | |
|-----|--|-----|----|-----|----------------------------|
| AUC | Aspirin/Protinase complex, 0.12-10 percent slaps | .24 | NO | BLD | serum/urine poorly drained |
|-----|--|-----|----|-----|----------------------------|



KEALEE

design, title, deliver
7720 Langston Road (Parcel 048, 18.07 ac, RMF-20) — townhouses, two-over-two and outposts
ADDRESS
(ACORN # 19800)
ADMINISTRATION
Prince George's County, Maryland
DATE
RMF-20
SHEET
C-700 — Sediment and Erosion Control Plan
SCALE
1" = 100'
DATE
PRELIMINARY
SHEET NO.
8 OF 11
COORDINATES
EPSG:2248
H NAD83
V NAD83 (Bv)

| PLANTYPE AND PREPARATION | |
|--------------------------|---|
| PLAN TYPE | SITE DEVELOPMENT / FINE GRADING |
| SHEET | C-700 — Sediment and Erosion Control Plan |
| SUBPLAN | Maryland Professional Engineer |
| DRAWN BY | KEALEE SITE PLAN ENGINE |
| DESIGNED BY | |
| CHECKED BY | |

| REVISIONS | | |
|-----------|------|-------------|
| NO. | DATE | DESCRIPTION |
| | | |
| | | |
| | | |

| INDEX OF DRAWINGS | |
|-------------------|--|
| 1. C-000 | Lower Street Approvals and General Notes |
| 2. C-001 | Grading Constraints and Boundary Plan |
| 3. C-002 | Overall Site and Zoning Plan |
| 4. C-003 | Drainage Plan |
| 5. C-004 | Grading and Drainage Plan |
| 6. C-005 | Utility Plan |
| 7. C-006 | Stormwater Management Plan |
| 8. C-700 | Sediment and Erosion Control Plan |
| 9. C-007 | Road, Curbs and Thruway Plan |
| 10. C-008 | Site Details |
| 11. C-009 | Landscaping and Tree Canopy Plan |

| SITE DATA | |
|--------------------|------------|
| ZONE | RMF-20 |
| TAX PARCEL ID | TRACT |
| GROSS TRACT AREA | 782,369 SF |
| TRACT AREA | 782,369 SF |
| NET LOT AREA | 782,369 SF |
| LOT FRONTAGE | 29' MIN |
| RETRACTS | REQUIRED |
| FRONT YARD | — |
| SIDE YARD | — |
| REAR YARD | — |
| COVERAGE | MAX |
| LOT COVERAGE | 7.8% |
| BUILDING FOOTPRINT | 60,896 SF |
| DATUM | EPSG:2248 |
| HORIZONTAL | NAD83 (Bv) |
| VERTICAL | — |

| SITE ANALYSIS | |
|-------------------------------------|---------------------------|
| 1. Gross lot area | 782,369 SF |
| 2. Gross lot area | 60,896 SF |
| 3. Wooded area | NOT ESTABLISHED |
| 4. Non wooded area | NOT ESTABLISHED |
| 5. Net lot area | 782,369 SF |
| 6. TOTAL AREA DISTURBED | 0.0% |
| 7. SWM REQUIRED — Sec. 32.174(a)(3) | EXEMPT — 5,000 SF OR LESS |

| BUILDING DATA | |
|---------------|----|
| LOT | GT |
| LOT 1 | — |
| LOT 2 | — |
0: contour (m); 5: spot elev; 10: finished floor; 15: subfloor; 17: height; 20: STY; 25: STY; 30: ST

INDEX OF DRAWINGS

| | | |
|----|-------|--|
| 1 | C-000 | Cover Sheet, Approvals and General Notes |
| 2 | C-100 | Existing Conditions and Boundary Plan |
| 3 | C-200 | Overall Site and Zoning Plan |
| 4 | C-300 | Demolition Plan |
| 5 | C-400 | Grading and Drainage Plan |
| 6 | C-500 | Utility Plan |
| 7 | C-600 | Stormwater Management Plan |
| 8 | C-700 | Sediment and Erosion Control Plan |
| 9 | C-800 | Road, Driveway and Paving Plan |
| 10 | C-900 | Civil Details |
| 11 | L-100 | Landscape and Tree Canopy Plan |

| SITE ANALYSIS | |
|------------------------------------|----------------------|
| 1. Gross tract area | 782,369 SF |
| 2. Area of dwelling | 60,896 SIF |
| 3. Wooded area | NOT ESTABLISHED |
| 4. Floodplain area | NOT ESTABLISHED |
| 5. Net lot area | 782,369 SF |
| 6. TOTAL AREA DISTURBED | 0 SF |
| 7. SWM REQUIRED — Sec. 32-174a)(3) | EXEMPT — 5,000 SF OR |



topographic survey before construction.

TOTAL ESTIMATED TIME OF CONSTRUCTION: 8 MONTHS

LEGEND

PLAT OF RECORD

LOC n. = recessed kn-saddle int. - Recessed 5100FT & - 10" stream 2

 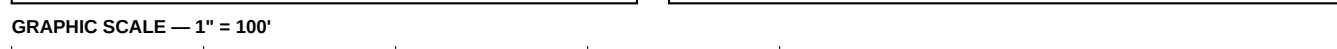

INDEX OF DRAWINGS

| | | |
|----|-------|--|
| 1 | C-000 | Cover Sheet, Approvals and General Notes |
| 2 | C-100 | Existing Conditions and Boundary Plan |
| 3 | C-200 | Overall Site and Zoning Plan |
| 4 | C-300 | Demolition Plan |
| 5 | C-400 | Grading and Drainage Plan |
| 6 | C-500 | Utility Plan |
| 7 | C-600 | Stormwater Management Plan |
| 8 | C-700 | Sediment and Erosion Control Plan |
| 9 | C-800 | Road, Driveway and Paving Plan |
| 10 | C-900 | Civil Details |
| 11 | L-100 | Landscape and Tree Canopy Plan |

| SITE ANALYSIS | |
|--------------------------------------|----------------------|
| 1. Gross tract area | 782,369 SF |
| 2. Area of dwelling | 60,896 SF |
| 3. Wooded area | NOT ESTABLISHED |
| 4. Floodplain area | NOT ESTABLISHED |
| 5. Net lot area | 782,369 SF |
| 6. TOTAL AREA DISTURBED | 0 SF |
| 7. SWIM REQUIRED — Sec. 32-174(a)(3) | EXEMPT — 5,000 SF OR |



SEQUENCE OF CONSTRUCTION

GENERAL NOTES

LEGEND
 PROPERTY BOUNDARY

PLAT OF RECORD
(ADMIN # 19800) — 1 lots of record, plat, L 49319 F213 — owner of record
EVERGREEN VENTURES, L.L.C. (D/G) (tax & delinquent payments)

LOT n — proposed fee-sample lot - PRIVATE STREET A... — HSA street, 2...

 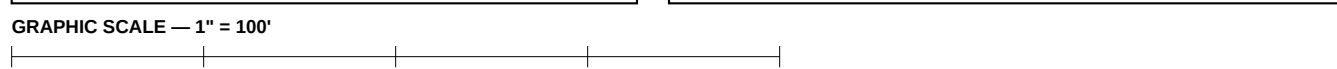

KEALEE

design, title, deliver
7720 Livingston Road (Parcel 048, 18.07 ac, RMF-20) — townhouses, two-over-two and duplexes
ADDRESS
(ACORN # 19800)
ADMINISTRATION
Prince George's County, Maryland
DATE
RMF-20
SHEET
L-100 — Landscape and Tree Canopy Plan
SCALE
1" = 100'
STATUS
PRELIMINARY
SHEET NO.
11 OF 11
COORDINATES
EPSG:2248
H NAD83
V NAD83 (Bv)

| PLANT TYPE AND PREPARATION | |
|----------------------------|--|
| PLANT TYPE | SITE DEVELOPMENT / FINE GRADING |
| SHEET | L-100 — Landscape and Tree Canopy Plan |
| SUBPLANE | Landscape Architect / Qualified Professional |
| DRAWN BY | KEALEE SITE PLAN ENGINE |
| DESIGNED BY | |
| CHECKED BY | |

| REVISIONS | | |
|-----------|------|-------------|
| NO. | DATE | DESCRIPTION |
| | | |
| | | |
| | | |

| INDEX OF DRAWINGS | |
|-------------------|--|
| 1 | C-000 Cover Sheet, Approvals and General Notes |
| 2 | C-001 Existing Conditions and Boundary Plan |
| 3 | C-002 Overall Site and Zoning Plan |
| 4 | C-003 Elevation Plan |
| 5 | C-004 Grading and Drainage Plan |
| 6 | C-005 Utility Plan |
| 7 | C-006 Stormwater Management Plan |
| 8 | C-007 Sediment and Erosion Control Plan |
| 9 | C-008 Road, Curbs and Driveway Plan |
| 10 | C-009 Plant Details |
| 11 | C-000 Landscape and Tree Canopy Plan |

| SITE DATA | |
|--------------------|------------|
| ZONE | RMF-20 |
| TAX PARCEL ID | TRACT |
| GROSS TRACT AREA | 782,369 SF |
| TRACT AREA | 782,369 SF |
| NET LOT AREA | 782,369 SF |
| LOT FRONTAGE | 20' MIN |
| RETRACTS | REQUIRED |
| FRONT YARD | — |
| SIDE YARD | — |
| REAR YARD | — |
| COVERAGE | MAX |
| LOT COVERAGE | 7.8% |
| BUILDING FOOTPRINT | 60,896 SF |
| DATUM | EPSG:2248 |
| HORIZONTAL | NAD83 |
| VERTICAL | NAD83 (Bv) |

| SITE ANALYSIS | |
|-------------------------------------|---------------------------|
| 1. Gross lot area | 782,369 SF |
| 2. Gross lot area | 60,896 SF |
| 3. Wooded area | NOT ESTABLISHED |
| 4. Non wooded area | NOT ESTABLISHED |
| 5. Net lot area | 782,369 SF |
| 6. TOTAL AREA DISTURBED | 0.0% |
| 7. SWM REQUIRED — Sec. 32.174(a)(3) | EXEMPT — 5,000 SF OR LESS |

| BUILDING DATA | |
|---------------|---|
| LOT | Q |
| LOT 1 | — |
| LOT 2 | — |
0: contour; 10: 5: spot; 15: 10: 15: 20: 7