


N SCALE 1" = 100' GRAPHIC: | = 200 FT

LEGEND — red parcels with dark-red buildings at the street line; mixed use (retail at grade, dwellings above) - dashed grey; surface parking - yellow; townhouse lots - blue; two-family (duplex) lots - violet; two-over-two (stacked) bays - grey; ps/ate street strip 40 ft (25-ft pavement) with 45-ft-radius turnarounds at dead ends - grey dashed with BRL; bldg: building restriction line per stick (front / side at the stick ends / rear yards per Sec. 27-4203, front deepened to the 20-ft driveway apron) - tan dashed; existing 2-ft contours (PG&AS, NAVD88; index contours labelled) - dark blocks (on the lots); dwelling footprints on a 20-ft build line (driveway apron; CGO front yard min. 10 ft); light grey stubs: driveways to the front-load garages (townhouse 1-car, duplex and two-over-two 2-car), 5-ft sidewalk along the front of every building at the street line - no street on the property line (25-ft landscape strip kept) - circles: turnarounds at dead-end streets - teal dashed; ESD micro-bioretentation reserved - green; recreation open space (Sec. 24-134, 5% on site) - green; woodland conservation (approved TCP) - red; slopes >25% (dashed = graded banks, regraded) - blue band; 50-ft stream buffer - olive; Primary Management Area, light blue; wetlands and their 25-ft buffer, pink dashed; slopes 15–25%, dashed green; forest conservation easement (all from the approved plan where one is supplied)

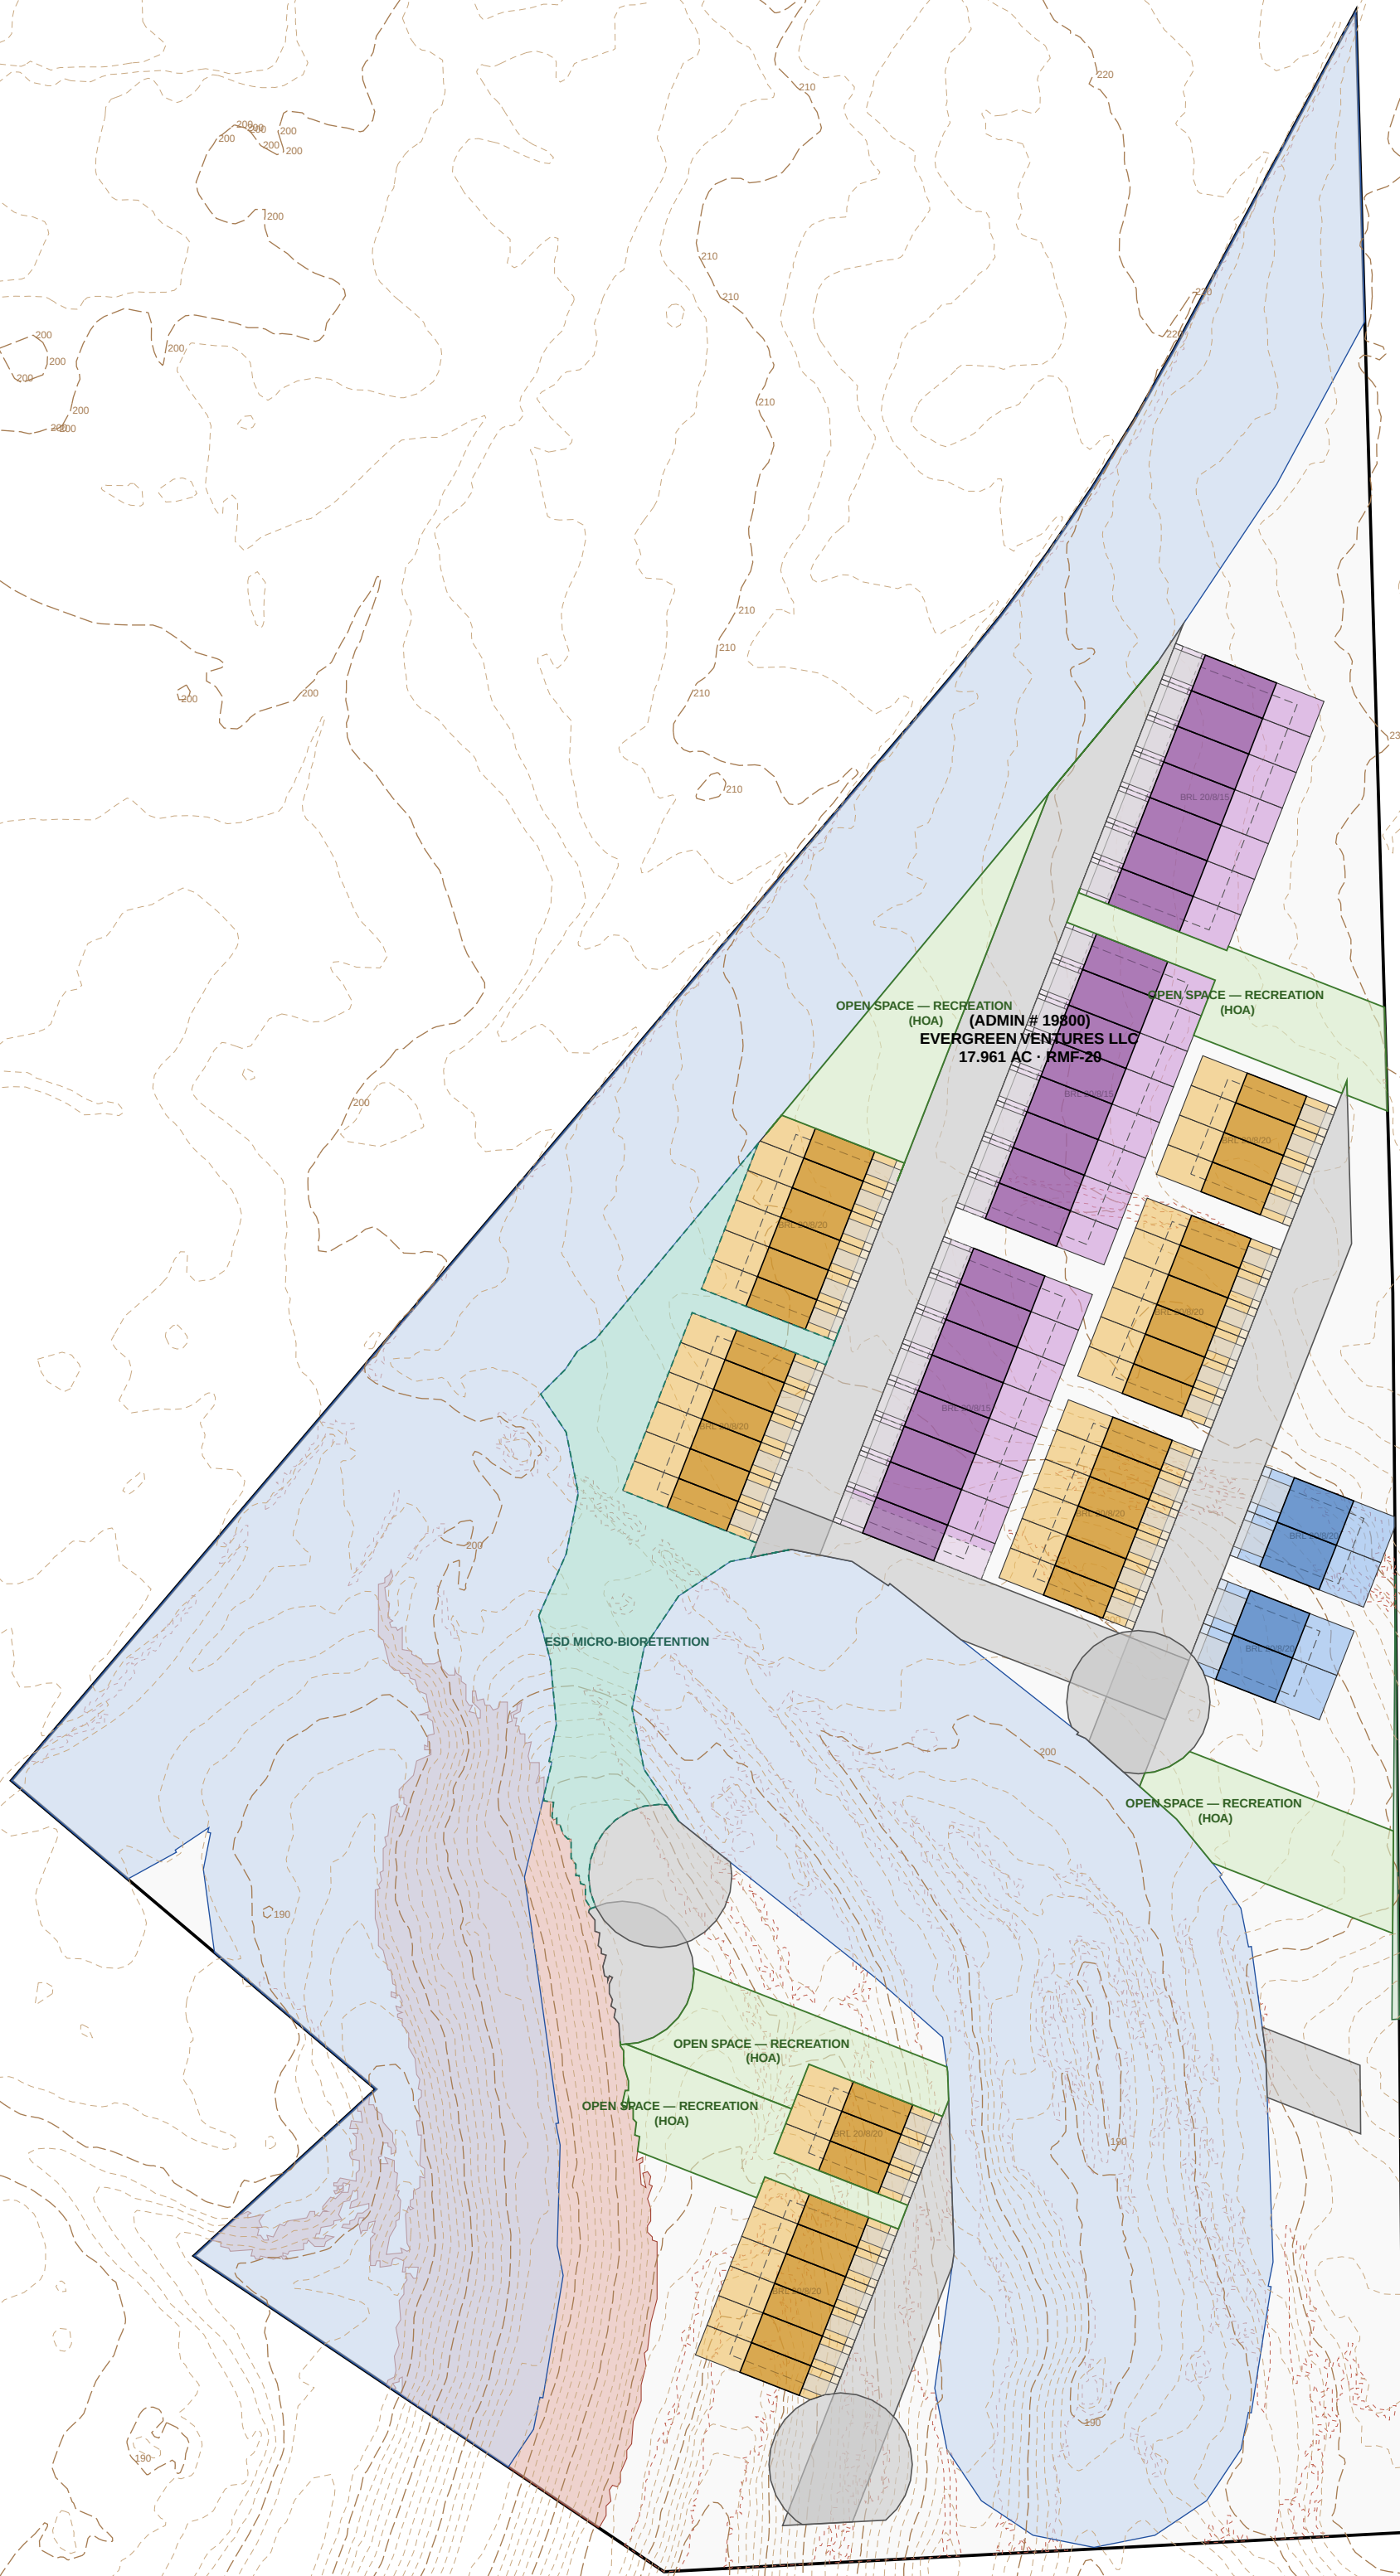

KEALEE

ATTACHED HOUSING YIELD STUDY — PRELIMINARY, NOT A SITE PLAN

7220 Livingston Road (Parcel 049, 18.07 ac, RMF-20) — townhouses, two-over-twos and duplexes

Zone RMF-20 - certified intensity table Sec. 27-4202 - generated 2026-09-18

PARCELS (PG&AS Address/Property — owner of record, assessment)

Act L293448 (ADMIN # 19800) EVERGREEN VENTURES LLC 18.07 ac assessed / 17,961 ac GIS - plat — L 49319 F213

Street 782.368 ft (17.961 ac) Boundary is the county parcel layer — not a survey.

WHAT CANNOT BE BUILT ON (county layers, clipped to the tract)

Woodland conservation (approved TCP areas) 0.02 ac - slopes >25% in bodes 1.54 ac (graded banks 1.97 ac, regraded) - 15–25% 2.24 ac (built with grading) - stream buffer 8.25 ac - floodplain 0.00 ac - wetlands 0.00 ac Developable 400,424 sf (9.192 ac).

The Primary Management Area, the woodland conservation threshold and any expanded buffers are set by an approved Natural Resources Inventory and TCP; not by these layers. A 50-ft stream buffer and slopes over 25% are the minimum that would be taken; the RMF may take more.

RMF-20 STANDARDS BY DWELLING TYPE (Sec. 27-4202)

Townhouse: 20 du/ac net - lot "e 20 ft wide - coverage "d 40% - yards 15/8/20 ft - height "d 50 ft

Two-family (duplex): 40 du/ac net - lot "e 60 ft wide - coverage "d 35% - yards 15/8/20 ft - height "d 50 ft

Two-over-two (stacked, 2 units per bay): null du/ac net - lot "e null ft wide - coverage "d null% - yards null/null/null ft - height "d null ft

Mixed use (retail below, dwellings above): null du/ac net - lot "e null ft wide - coverage "d null% - yards null/null/null ft - height "d null ft

YIELD — THIS LAYOUT

Townhouse: 37 bays / 37 du - 14.96 du/ac on 2.473 net ac (cap 20) - lot coverage 44.4% (cap 40%) - parking 74 at 20/du ASSUMED — 1-car front-load garage + 1 driveway space on the lot

Two-family (duplex): 4 bays / 4 du - 10.02 du/ac on 0.399 net ac (cap 40) - lot coverage 44.4% (cap 35%) - parking 8 at 20/du ASSUMED — 2-car front-load garage + 2 driveway spaces on each lot

Two-over-two (stacked, 2 units per bay): 23 bays / 46 du - 22.39 du/ac on 2.054 net ac (cap null) - lot coverage 48% (cap null%) - parking 69 at 1.50/du ASSUMED — a 2-car front-load garage per bay (one space per unit) + 1 driveway space + surface bays along the street

Parking 26 surface spaces (drawn (dashed) + 102 in garages and driveways = 208 against 151 required at the assumed ratios.

TOTAL 87 DWELLING UNITS in 64 bays - 4.84 du/ac gross on the 17.961-ac tract

CEILINGs if the whole developable ground were one type (x 0.8 for streets, parking, open space):

Townhouse: 147 du

Two-family (duplex): 294 du

Two-over-two (stacked, 2 units per bay): — du

STORMWATER MANAGEMENT (ESD, MDE Ch. 5)

Impervious 153,622 sf (39.6%), Rv 0.2267, ESDv 14,782 cf at P_E 1.0 in 1" 18,478 sf of micro-bioretentation. Reserved for stormwater: 24,942 sf.

24,942 sf is reserved for ESD practices (1 micro-bioretentation areas in the ground the rows left, drawn) against the 18,478 sf footprint at P_E 1.0 in; the higher P_E the soils may require (Table 5.3) is met by bioswales along the private streets and the DP/E concept.

Micro-bioretentation in every surface parking lot island and a bioswale along each private street, credited under ESD; rooftop disconnection is not available over parking. Design per the DP/E stormwater concept approval that precedes the DSP.

UNIT ASSUMPTIONS

Townhouse: 20' x 30' ft lot, 20' x 40' ft footprint, 1 du per bay, sticks of "d 6

Two-family (duplex): 30' x 90' ft lot, 30' x 40' ft footprint, 1 du per bay, sticks of "d 8

Two-over-two (stacked, 2 units per bay): 24' x 100' ft lot, 24' x 48' ft footprint, 2 du per bay, sticks of "d 8

Mixed use (retail below, dwellings above): 100' x 200' ft lot, 100' x 70' ft footprint, 22 du per bay, 7,000 sf retail, 5 stories "H 60 ft

Private streets: 40-ft strips (20-ft pavement, walk one side). Visitor parking, open space and the Landscape Manual 4.7 buffer to the RE lots are DSP work not drawn here.

DESIGN STANDARDS APPLIED (Subtitle 24 Subdivision Regulations, Subtitle 27, DP/E, IFC)

Sec. 24-121(a)(13): every lot fronts and takes access from one street only; (a)(8) corner lots truncated at plating; (a)(10) no unnecessary street — the approved access is reused.

Sec. 24-121(a)(2): new streets are continuous, tee off the existing street at right angles; (a)(3) public secondary streets 50 ft primary 60 ft of right-of-way — these are private streets, so Sec. 24-128(b)(7) governs: "e 22-ft pavement (26 ft drawn), sidewalks 18 ft, a 10-ft public utility easement contiguous to the right-of-way (24-128(b)(12)), maintained by the HOA/condominium with Fire Chief approval of emergency access.

Turnarounds: a dead end over 150 ft ends in a 45-ft-radius bulb (40-ft pavement) — IFC D10.3.4 as adopted by Subtitle 11-4 drawn.

Sec. 27-4203 (RMF-20) yards: front 15 ft, side 8 ft (end units: party walls within a stick), rear 20 ft — drawn, build line 20 ft (the driveway apron for the front-load garage governs over the 15-ft minimum), 16-ft breaks between sticks of "d 6 (8' ft end yards), rear 20 ft on a 30-ft lot; lot width, coverage, height per the certified table above.

Pedestrian access: a 5-ft sidewalk runs along the front of every building at the street line (Sec. 23-135), on the lot in the front yard, crossed by the driveways; every building front faces a street and its walk. No street is laid on the property line — a 25-ft landscape strip is kept between any street and the tract boundary (Landscape Manual Sec. 4.7 sets the buffer/yard at DSP).

Vehicle access: every townhouse, duplex and two-over-two lot fronts a street (the kept public right-of-way or a private street) and has its own driveway to a front-load garage — 1-car for the 20-ft townhouse, 2-car for the 30-ft duplex and the 24-ft two-over-two bay; no lot is bulldozed and none takes access from an adjoining lot (Sec. 24-128(a)).

Table 24-430(c): regulated stream buffer 100' outside a Transit Oriented Center; slopes over 25%, 100-year floodplain and wetlands taken out of the developable ground (county layers; the NRITCP2 governs a preliminary plan).

Sec. 24-134 mandatory dedication of parkland 5% of the gross tract (39,118 sf) — provided on site as recreation open space on an HOA parcel: 43,713 sf drawn.

Sec. 24-121(a)(15): a DP/E-approved stormwater concept precedes the preliminary plan — ESD to the MEP (MDE Manual Ch. 5); micro-bioretentation in the reserved areas drawn, bioswales along each private street; (a)(16) Subtitle 25 woodland conservation by TCP2.

Sec. 25-135 curb, gutter and 5-ft sidewalk on the street side of every lot (lot frontages "d 100 ft); DP/E grading checklist: lawns "e 2.5%, swales 2–4%, banks "d 3.1 (residential), slopes steeper than 4:1 set back 10–20 ft from buildings.

Landscape Manual Sec. 4.7 buffer/yard against the adjoining RE lots and Sec. 4.5 street trees along every street; Sec. 25-128 tree canopy on the gross tract — DSP work, the widths are not drawn here.

Sec. 27-4300 parking: the ratios used (2.0/du townhouse and duplex on the lot, 1.5/du two-over-two) are ASSUMED — the certified tables carried by this engine do not include the parking schedule; visitor parking at 0.5/du is customary and not drawn.

APPROVALS

RMF-20: townhouse, two-family and multifamily (two-over-two) dwellings are listed uses with their own intensity standards in the certified Sec. 27-4203 table; a Detailed Site Plan is the approval path for residential in the commercial zones (confirm the use table entry for each type — the y/x table is not carried by this engine).

Sec. 27-4300 parking: Sec. 27-4400 landscaping (Landscape Manual 4.7 buffers against the RE lots); Sec. 25-121 woodland conservation; Sec. 24 subdivision (a preliminary plan of subdivision approval creates fee-simple townhouse and duplex lots; two-over-twos are condominium or fee-simple with a DSP, stormwater concept (DP/E), WSSC hydraulic planning analysis).

This is a yield study prepared by the Kealee site-plan engine from county GIS and the certified zoning table. It is not a Detailed Site Plan, not a survey and not a determination of what the Planning Board will approve.