

KEALEE

design, build, deliver

PROJECT
1009 Rollins Ave
ADDRESS
1009 Rollins Ave
JURISDICTION
prince georges md
ZONE
RSF-65

SHEET

C-100 — Existing Conditions and Boundary Plan

SCALE

1" = 10'

STATUS

PRELIMINARY

SHEET NO.

1 OF 5

COORDINATES

EPSG:2248

H: NAD83

V: NAVD83 (feet)

PROFESSIONAL RESPONSIBILITY

Maryland Licensed Surveyor

certifies boundary determination, topographic survey

SEAL AND SIGNATURE

All content on this sheet falls within one professional scope.

SITE DATA			
ZONE	RSF-65		
TAX / PARCEL ID	348855		
GROSS LOT AREA	8,007 SF	0.184 AC	
LOT FRONTAGE	45' MIN	134.64'	
SETBACKS	REQUIRED	PROVIDED	
FRONT YARD	25'	25'	
SIDE YARD	8'	8'	
REAR YARD	20'	20'	
COVERAGE	MAX	PROPOSED	
LOT COVERAGE	35%	12.8%	
BUILDING FOOTPRINT	—	1,025 SF	
DATUM			
HORIZONTAL	EPSG:2248	NAD83	
VERTICAL	NAVD83 (feet)		

SITE ANALYSIS	
1. Gross tract area	8,007 SF
2. Area of dwelling	1,025 SF
3. Wooded area	NOT ESTABLISHED
4. Floodplain area	NOT ESTABLISHED
5. Net tract area	8,007 SF
6. TOTAL AREA DISTURBED	NOT QUANTIFIED

SEQUENCE OF CONSTRUCTION	
1. Pre-construction meeting	1 DAY
2. Obtain necessary permits	2 DAYS
3. Notify Miss Utility at 811 at least 48 hours prior to any excavation	1 DAY
4. Construct stabilized construction entrance and perimeter sediment control	2 DAYS
5. Rough grade, construct dwelling, utilities and driveway	12 MONTHS
6. Fine grade and stabilize all disturbed areas	1 DAY
7. Remove sediment control devices when written permission has been granted	1 DAY
TOTAL ESTIMATED TIME OF CONSTRUCTION: 12 MONTHS	

GENERAL NOTES	
1. CONTRACTOR SHALL CONTACT MISS UTILITY AT 811 A MINIMUM OF 48 HOURS PRIOR TO ANY EXCAVATION.	
2. ALL EXISTING AND PROPOSED UTILITIES SHOWN PER PGC CODE SEC. 30-106.	
3. PROPOSED GRADE SHOWN SOLID. EXISTING GRADE SHOWN DASHED.	
4. ROUGH EARTHWORK GRADES AND UTILITY ELEVATIONS SHOWN TO TENTHS OF A FOOT.	
5. BOUNDARY SHOWN IS COMPILED JURISDICTION GIS, NOT A BOUNDARY SURVEY.	

PLAT OF RECORD
PORTER SUBDIVISION, LOTS 1 AND 2 — Plot Book PM 231, p. 50 (MSA, C2381, 19950), Seat Pleasant (Belt) Election District, Prince George's County, Maryland. Tax Map 73, Unit B3, 2004 May 202 SE 06, Zone R-95 as recorded (RSP-45 under the 2022 reversion). Scale 1" = 20', November 2007. M. NCPSPC Record File S-04213, Proposed by Capital Development Design, Inc., Beltsville, Maryland. Basis of bearings: Maryland State Plane Coordinate System (NAD 83). Lot 1 = 9,588 sq ft (0.2203 ac). Lot 2 = 8,007 sq ft (0.184 ac). 42.25 sq ft (0.0096 ac) dedicated to public use.

NOTES OF RECORD
1. Development of this property shall be in accordance with the approved Stormwater Management Control Plan (C225-250-05, or any approved revision thereafter).
2. Approval of this plan is based upon a reasonable expectation that public water and sewer service will be available when needed, and is conditioned on lifting of all of the Washington Suburban Sanitary Commission authorization DA-4023 2-05 commitments.
3. The applicant, his heirs, successors and/or assignees shall utilize an abutting driveway design, constructed per CPMAT standards and requirements. Separate, standard residential driveway aprons shall be provided along Rollins Avenue. If deemed appropriate by DPWS, upon the issuance of street construction permits.
PUE — Public Utility Easement IPF — Iron Pipe Found For Public Water and Sewer Only
The surveyor certifies, under declaration and approved signature of the recorded plat are NOT reproduced here; they appear in the instruments, not in this drawing.

LEGEND	
— — — — —	PROPERTY BOUNDARY
- - - - -	BRL — BUILDING RESTRICTION LINE
—	PROPOSED STRUCTURE
- - - - -	EXISTING CONTOUR — PGATLAS 2 FT (2023), NAVD83
—	STREET CENTRELINE
—	PROPOSED PAVEMENT — DRIVEWAY / WALK
- - - - -	EASEMENT

PRINCE GEORGE'S COUNTY SOIL CONSERVATION DISTRICT APPROVAL

SIGNATURE	DATE

DPE SITE/ROAD PLAN REVIEW DIVISION APPROVAL

SIGNATURE	DATE


REVISIONS

— NONE —

SOILS TABLE


MAP UNIT	MAP UNIT NAME	K-FACTOR	HYDRIC	HYD. GROUP	DRAINAGE CLASS
AaB	Adelphia silt loam, 2 to 5 percent slopes complex	37	No	C	Moderately well drained
ACA	Adelphia-Aquasco complex, 0 to 2 percent slopes	43	No	D	Somewhat poorly drained
ACB	Adelphia-Aquasco complex, 0 to 2 percent slopes	37	No	C	Moderately well drained
ADA	Adelphia-Hairdel complex, 0 to 2 percent slopes	24	No	BD	Somewhat poorly drained
ADB	Adelphia-Hairdel complex, 0 to 2 percent slopes	37	No	C	Moderately well drained
AaB	Adelphia-Hairdel complex, 2 to 5 percent slopes	24	No	BD	Somewhat poorly drained
AaB	Adelphia-Hairdel complex, 2 to 5 percent slopes	37	No	C	Moderately well drained
AaC	Adelphia-Hairdel complex, 5 to 10 percent slopes	24	No	BD	Somewhat poorly drained

SOURCE AND ACCURACY
Parcel boundary — Jurisdiction gis — Prince George's County / M-NCPPC — PGAtlas Property — level 1
Existing contours — Prince George's County / M-NCPPC — PGAtlas — level 1
Contours: PGAtlas Elevation/MapServer1 — Contour = 2 Ft (2023), 2 ft interval, NAVD83 (feet)

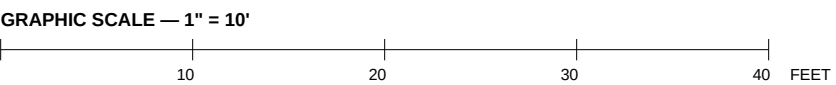

SOILS TABLE					
USDA NRCS SSURGO — required by POC Code Sec. 30-130(a)(13)					
MAP UNIT	MAP UNIT NAME	K-FACTOR	HYDRIC	HYD. GROUP	DRAINAGE CLASS
AaB	Adelphia silt loam, 2 to 5 percent slopes complex	37	No	C	Moderately well drained
ACA	Adelphia-Aquasco complex, 0 to 2 percent slopes	43	No	D	Somewhat poorly drained
AA	Adelphia-Aquasco complex, 0 to 2 percent slopes	37	No	C	Moderately well drained
ADA	Adelphia-Hairdel complex, 0 to 2 percent slopes	24	No	BD	Somewhat poorly drained
AGA	Adelphia-Hairdel complex, 0 to 2 percent slopes	37	No	C	Moderately well drained
AB	Adelphia-Hairdel complex, 2 to 5 percent slopes	24	No	BD	Somewhat poorly drained
AB	Adelphia-Hairdel complex, 2 to 5 percent slopes	37	No	C	Moderately well drained
AAC	Adelphia-Hairdel complex, 5 to 10 percent slopes	24	No	BD	Somewhat poorly drained

SOURCE AND ACCURACY
Parcel boundary — Jurisdiction gis — Prince George's County / M-ACPPC — PGAtlas Property — level 1
Existing contours — Prince George's County / M-NCPPC — PGAtlas — level 1
Contours: PGAtlas Elevation/MapServer1 — Contour - 2 Ft (2023), 2 ft interval, NAVD83 (feet)

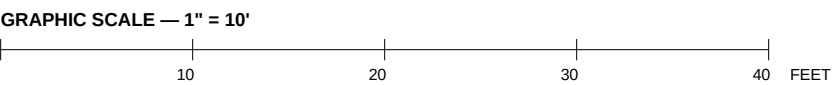

KEALEE

design, build, deliver

PROJECT
1009 Rollins Ave
ADDRESS
1009 Rollins Ave
JURISDICTION
prince georges md
ZONE
RSF-65
SHEET
C-200 — Overall Site and Zoning Plan
SCALE
1" = 10'
STATUS
PRELIMINARY
SHEET NO.
2 OF 5
COORDINATES
EPSG:2248
H: NAD83
V: NAVD83 (feet)

PROFESSIONAL RESPONSIBILITY
Maryland Professional Engineer

certificat: sig_49949

SEAL AND SIGNATURE

Architect

certificat: architectural_footprint

SEAL AND SIGNATURE

This sheet carries content from more than one professional discipline. Each seal below applies only to the subjects listed beside it. No professional certifies content outside their stated scope, and the sheet is not divided into separate drawings for that purpose.

SITE DATA		
ZONE	RSF-65	
TAX / PARCEL ID	348855	
GROSS LOT AREA	8,007 SF	0.184 AC
LOT FRONTAGE	45 MIN	134.64'
SETBACKS		
FRONT YARD	25'	25'
SIDE YARD	8'	8'
REAR YARD	20'	20'
COVERAGE		
LOT COVERAGE	35%	12.8%
BUILDING FOOTPRINT	—	1,025 SF
DATUM		
HORIZONTAL	EPSG:2248	NAD83
VERTICAL	NAVD83 (feet)	

SITE ANALYSIS	
1. Gross lot area	8,007 SF
2. Area of dwelling	1,025 SF
3. Wooded area	NOT ESTABLISHED
4. Floodplain area	NOT ESTABLISHED
5. Net tract area	8,007 SF
6. TOTAL AREA DISTURBED	NOT QUANTIFIED

SEQUENCE OF CONSTRUCTION	
1. Pre-construction meeting	1 DAY
2. Obtain necessary permits	2 DAYS
3. Notify Mass Utility at B11 at least 48 hours prior to any excavation	1 DAY
4. Construct stabilized construction entrance and perimeter sediment control	2 DAYS
5. Rough grade, construct dwelling, utilities and driveway	12 MONTHS
6. Fine grade and establish all disturbed areas	1 DAY
7. Remove sediment control devices when written permission has been granted	1 DAY
TOTAL ESTIMATED TIME OF CONSTRUCTION: 12 MONTHS	

GENERAL NOTES

- CONTRACTOR SHALL CONTACT MSS UTILITY AT B11 A MINIMUM OF 48 HOURS PRIOR TO ANY EXCAVATION.
- ALL EXISTING AND PROPOSED UTILITIES SHOWN PER POC CODE SEC. 30.106.
- PROPOSED GRADE SHOWN SOLID; EXISTING GRADE SHOWN DASHED.
- ROUGH EARTHWORK, GRADES AND UTILITY ELEVATIONS SHOWN TO TENTHS OF A FOOT.
- BOUNDARY SHOWN IS COMPILED JURISDICTION GIS, NOT A BOUNDARY SURVEY.

PLAT OF RECORD

PORTER SUBDIVISION, LOTS 1 AND 2 — Plat Book PM 211, p. 50 (MSA, C2381, 19950), State Property (BRI) Election District, Prince George's County, Maryland, Tax Map T3, GSR ES, 200 May 202 SE 86, Zone R-55 as recorded (RSF-65 under the 2022 rewrite), Scale 1" = 20', November 2007. M-NCPPC, Record File 9-05121. Prepared by Capital Development Design, Inc., Bethesda, Maryland. Basis of bearings: Maryland State Plane Coordinate System (NAD 83), Lot 1 = 9,598 sq ft (0.2203 ac), Lot 2 = 8,008 sq ft (0.1838 ac), 4,719 sq ft (0.10860 ac) dedicated to public use.

NOTES OF RECORD

- Development of this property shall be in accordance with the approved Stormwater Management Concept Plan 41250-2008-00, or any approved revisions thereto.
- Approval of this plat is based upon a reasonable representation that public water and sewer service will be available when needed, and is conditioned on fulfilling all of the Washington Suburban Sanitary Commission authorization on 404(d) 2-00 comments.
- The applicant, his heirs, successors and or assigns shall utilize an existing driveway design, constructed per DPWNET standards and requirements. Separate, standard residential driveway approvals shall be provided along Rollins Avenue, if deemed appropriate by DPWNET upon the issuance of street construction permits.

PUE — Public Utility Easement · IPF — Iron Pipe Found · For Public Water and Sewer Only

The surveyor certifies, under declaration and approval signatures of the recorded plat and NOT reproduced here, they shall be the true and correct, and to the plat.

LEGEND

—	PROPERTY BOUNDARY
- - - -	BRL — BUILDING RESTRICTION LINE
—	PROPOSED STRUCTURE
—	EXISTING CONTOUR — PGATLAS 2 FT (2023), NAVD83
- - - -	STREET CENTRELINE
—	PROPOSED PAVEMENT — DRIVEWAY / WALK
- - - -	EASEMENT

PRINCE GEORGE'S COUNTY SOIL CONSERVATION DISTRICT APPROVAL
SEDIMENT CONTROL, CRACKING, SOILS & DRAINAGE

SIGNATURE DATE

DPE SITEROAD PLAN REVIEW DIVISION APPROVAL

SIGNATURE DATE

REVISIONS

— NONE —

KEALEE

design, build, deliver

PROJECT
1009 Rollins Ave
ADDRESS
1009 Rollins Ave
JURISDICTION
prince georges md
ZONE
RSF-65

SHEET
C-500 — Utility Plan
SCALE
1" = 10'
STATUS
PRELIMINARY
SHEET NO.
4 OF 5

COORDINATES
EPSG:2248
H: NAD83
V: NAVD83 (feet)

PROFESSIONAL RESPONSIBILITY
Maryland Professional Engineer
certificat_utilty_design

SEAL AND SIGNATURE

All content on this sheet falls within one professional scope.

SITE DATA			
ZONE	RSF-65		
TAX / PARCEL ID	348855		
GROSS LOT AREA	8,007 SF	0.184 AC	
LOT FRONTAGE	45' MIN	134.64'	
SETBACKS	REQUIRED	PROVIDED	
FRONT YARD	25'	25'	
SIDE YARD	8'	8'	
REAR YARD	20'	20'	
COVERAGE	MAX	PROPOSED	
LOT COVERAGE	35%	12.8%	
BUILDING FOOTPRINT	—	1,025 SF	
DATUM			
HORIZONTAL	EPSG:2248	NAD83	
VERTICAL	NAVD83 (feet)		

SITE ANALYSIS	
1. Gross tract area	8,007 SF
2. Area of dwelling	1,025 SF
3. Wooded area	NOT ESTABLISHED
4. Floodplain area	NOT ESTABLISHED
5. Net tract area	8,007 SF
6. TOTAL AREA DISTURBED	NOT QUANTIFIED

SEQUENCE OF CONSTRUCTION	
1. Pre-construction meeting	1 DAY
2. Obtain necessary permits	2 DAYS
3. Notify Miss Utility at 811 at least 48 hours prior to any excavation	1 DAY
4. Construct stabilized construction entrance and perimeter sediment control	2 DAYS
5. Rough grade, construct dwelling, utilities and driveway	12 MONTHS
6. Fine grade and stabilize all disturbed areas	1 DAY
7. Remove sediment control devices when written permission has been granted	1 DAY
TOTAL ESTIMATED TIME OF CONSTRUCTION: 12 MONTHS	

- GENERAL NOTES**
- CONTRACTOR SHALL CONTACT MISS UTILITY AT 811 A MINIMUM OF 48 HOURS PRIOR TO ANY EXCAVATION.
 - ALL EXISTING AND PROPOSED UTILITIES SHOWN PER POC CODE SEC. 30-106.
 - PROPOSED GRADE SHOWN SOLID. EXISTING GRADE SHOWN DASHED.
 - ROUGH EARTHWORK GRADES AND UTILITY ELEVATIONS SHOWN TO TENTHS OF A FOOT.
 - BOUNDARY SHOWN IS COMPILED JURISDICTION GIS, NOT A BOUNDARY SURVEY.

PLAT OF RECORD
PORTER SUBDIVISION, LOTS 1 AND 2 — Plot Book PM 231, p. 50 (MSA, C2381, 19950), Seat Pleasant (Belt) Election District, Prince George's County, Maryland, Tax Map 73, G16 R3, 2020 May 202 SE 06, Zone R-95 as recorded (RSP-45 under the 2022 rewrite), Scale 1" = 20', November 2007. M. NCPPC Record File S-08213, Proposed by Capital Development Design, Inc., Beltsville, Maryland. Basis of bearings: Maryland State Plane Coordinate System (NAD 83). Lot 1 = 9,588 sq ft (0.2203 ac). Lot 2 = 8,007 sq ft (0.184 ac). 4,215 sq ft (0.0969 ac) dedicated to public use.

- NOTES OF RECORD**
- Development of this property shall be in accordance with the approved Stormwater Management Control Plan (C220-2050-05, or any approved revision thereto).
 - Approval of this plat is based upon a reasonable expectation that public water and sewer service will be available when needed, and is conditioned on fulfillment of the Washington Suburban Sanitary Commission authorization DA-4023-2-05 commitments.
 - The applicant, his heirs, successors and/or assignees shall utilize an abutting driveway design constructed per CPMAT standards and requirements. Separate, standard residential driveway aprons shall be provided along Rollins Avenue, if deemed appropriate by DPWSD, upon the issuance of street construction permits.

PUE — Public Utility Easement IPF — Iron Pipe Found For Public Water and Sewer Only
The surveyor certifies, under declaration and approved signature of the recorded plat are NOT reproduced here; they appear in the instruments, not in this drawing.

LEGEND

- PROPERTY BOUNDARY
- BRL — BUILDING RESTRICTION LINE
- PROPOSED STRUCTURE
- EXISTING CONTOUR — PGATLAS 2 FT (2023), NAVD83
- STREET CENTRELINE
- PROPOSED PAVEMENT — DRIVEWAY / WALK
- EASEMENT

PRINCE GEORGE'S COUNTY SOIL CONSERVATION DISTRICT APPROVAL

SIGNATURE DATE

DPE SITE/ROAD PLAN REVIEW DIVISION APPROVAL

SIGNATURE DATE

REVISIONS

— NONE —

SOILS TABLE

MAP UNIT	MAP UNIT NAME	K-FACTOR	HYDRIC	HYD. GROUP	DRAINAGE CLASS
AaB	Adelphia silt loam, 2 to 5 percent slopes complex	37	No	C	Moderately well drained
ACA	Adelphia-Aquasco complex, 0 to 2 percent slopes	43	No	D	Somewhat poorly drained
ACA	Adelphia-Aquasco complex, 0 to 2 percent slopes	37	No	C	Moderately well drained
ADA	Adelphia-Hairdel complex, 0 to 2 percent slopes	24	No	BD	Somewhat poorly drained
ADA	Adelphia-Hairdel complex, 0 to 2 percent slopes	37	No	C	Moderately well drained
AaB	Adelphia-Hairdel complex, 2 to 5 percent slopes	24	No	BD	Somewhat poorly drained
AaB	Adelphia-Hairdel complex, 2 to 5 percent slopes	37	No	C	Moderately well drained
AaC	Adelphia-Hairdel complex, 5 to 10 percent slopes	24	No	BD	Somewhat poorly drained

SOURCE AND ACCURACY
Parcel boundary — Jurisdiction gis — Prince George's County / M-NCPPC — PGAtlas Property — level 1
Existing contours — Prince George's County / M-NCPPC — PGAtlas — level 1
Contours: PGAtlas Elevation/MapServer1 — Contour = 2 Ft (2023), 2 ft interval, NAVD83 (feet)

GRAPHIC SCALE — 1" = 10'

0 10 20 30 40 FEET

KEALEE

design, build, deliver

PROJECT
1009 Rollins Ave
ADDRESS
1009 Rollins Ave
JURISDICTION
prince georges md
ZONE
RSF-65

SHEET

L-100 — Landscape and Tree Canopy Plan

SCALE

1" = 10'

STATUS

PRELIMINARY

SHEET NO.

5 OF 5

COORDINATES

EPSG:2248

H: NAD83

V: NAVD83 (feet)

PROFESSIONAL RESPONSIBILITY

Qualified Environmental Professional

certified tree_conservation

SEAL AND SIGNATURE

All content on this sheet falls within one professional scope.

SITE DATA

ZONE	RSF-65
TAX / PARCEL ID	348855
GROSS LOT AREA	8,007 SF 0.184 AC
LOT FRONTAGE	45' MIN 134.64'
SETBACKS	REQUIRED PROVIDED
FRONT YARD	25' 25'
SIDE YARD	8' 8'
REAR YARD	30' 30'
COVERAGE	MAX PROPOSED
LOT COVERAGE	35% 12.8%
BUILDING FOOTPRINT	— 1,025 SF
DATUM	
HORIZONTAL	EPSG:2248 NAD83
VERTICAL	NAVD83 (feet)

SITE ANALYSIS

1. Gross tract area	8,007 SF
2. Area of dwelling	1,025 SF
3. Wooded area	NOT ESTABLISHED
4. Floodplain area	NOT ESTABLISHED
5. Net tract area	8,007 SF
6. TOTAL AREA DISTURBED	NOT QUANTIFIED

SEQUENCE OF CONSTRUCTION

1. Pre-construction meeting	1 DAY
2. Obtain necessary permits	2 DAYS
3. Notify Miss Utility at 811 at least 48 hours prior to any excavation	1 DAY
4. Construct stabilized construction entrance and perimeter sediment control	2 DAYS
5. Rough grade, construct dwelling, utilities and driveway	12 MONTHS
6. Fine grade and stabilize all disturbed areas	1 DAY
7. Remove sediment control devices when written permission has been granted	1 DAY

TOTAL ESTIMATED TIME OF CONSTRUCTION: 12 MONTHS

GENERAL NOTES

- CONTRACTOR SHALL CONTACT MISS UTILITY AT 811 A MINIMUM OF 48 HOURS PRIOR TO ANY EXCAVATION.
- ALL EXISTING AND PROPOSED UTILITIES SHOWN PER PGC CODE SEC. 30-106.
- PROPOSED GRADE SHOWN SOLID. EXISTING GRADE SHOWN DASHED.
- ROUGH EARTHWORK GRADES AND UTILITY ELEVATIONS SHOWN TO TENTHS OF A FOOT.
- BOUNDARY SHOWN IS COMPILED JURISDICTION GIS, NOT A BOUNDARY SURVEY.

PLAT OF RECORD

PORTER SUBDIVISION, LOTS 1 AND 2 — Plot Book PM 231, p. 50 (MSA, C2381, 19950), Seat Pleasant (Belt) Election District, Prince George's County, Maryland. Tax Map 73, Unit B3, 2020 May 202 SE 06, Zone R-95 as recorded (RSP-65 under the 2022 reversion). Scale 1" = 20', November 2007. M. NCPPC Record File S-08123, Proposed by Capital Development Design, Inc., Baltimore, Maryland. Basis of bearings: Maryland State Plane Coordinate System (NAD 83). Lot 1 = 9,588 sq ft (0.2203 ac). Lot 2 = 8,007 sq ft (0.184 ac). 42.25 sq ft (0.00096 ac) dedicated to public use.

NOTES OF RECORD

- Development of this property shall be in accordance with the approved Stormwater Management Control Plan (2220-2050-05, or any approved revision thereafter).
- Approval of this plan is based upon a reasonable expectation that public water and sewer service will be available when needed, and is conditioned on fulfillment of the Washington Suburban Sanitary Commission authorization DA-4023-2-05 commitments.
- The applicant, his heirs, successors and/or assignees shall utilize an abutting driveway design constructed per CPMAT standards and requirements. Separate, standard residential driveway aprons shall be provided along Eastern Avenue, if deemed appropriate by DPWSD, upon the issuance of street construction permits.

PUE — Public Utility Easement IPE — Iron Pipe Easement For Public Water and Sewer Only

The surveyor certifies, under declaration and approved signature of the recorded plat are NOT reproduced here; they appear in the instrument, not in this drawing.

LEGEND

— — — — —	PROPERTY BOUNDARY
- - - - -	BRL — BUILDING RESTRICTION LINE
—	PROPOSED STRUCTURE
- - - - -	EXISTING CONTOUR — PGATLAS 2 FT (2023), NAVD83
—	STREET CENTRELINE
—	PROPOSED PAVEMENT — DRIVEWAY / WALK
- - - - -	EASEMENT

PRINCE GEORGE'S COUNTY SOIL CONSERVATION DISTRICT APPROVAL

SEEDMENT CONTROL, GRADING, SLOPE & DRAINAGE

SIGNATURE DATE

DPE SITE/ROAD PLAN REVIEW DIVISION APPROVAL

SIGNATURE DATE

REVISIONS

— NONE —

SOILS TABLE

USDA NRCS SSURGO — required by POC Code Sec. 30-130(a)(13)

MAP UNIT	MAP UNIT NAME	K-FACTOR	HYDRIC	HYD. GROUP	DRAINAGE CLASS
AaB	Adelphia silt loam, 2 to 5 percent slopes complex	37	No	C	Moderately well drained
ACA	Adelphia-Aquasco complex, 0 to 2 percent slopes	43	No	D	Somewhat poorly drained
ACB	Adelphia-Aquasco complex, 0 to 2 percent slopes	37	No	C	Moderately well drained
ADA	Adelphia-Hairdel complex, 0 to 2 percent slopes	24	No	BD	Somewhat poorly drained
ADB	Adelphia-Hairdel complex, 0 to 2 percent slopes	37	No	C	Moderately well drained
AaB	Adelphia-Hairdel complex, 2 to 5 percent slopes	24	No	BD	Somewhat poorly drained
AaB	Adelphia-Hairdel complex, 2 to 5 percent slopes	37	No	C	Moderately well drained
AaC	Adelphia-Hairdel complex, 5 to 10 percent slopes	24	No	BD	Somewhat poorly drained

SOURCE AND ACCURACY
Parcel boundary — Jurisdiction gis — Prince George's County / M-ACPPC — PGAtlas Property — level 1
Existing contours — Prince George's County / M-NCPPC — PGAtlas — level 1
Contours: PGAtlas Elevation/MapServer1 — Contour = 2 Ft (2023), 2 ft interval, NAVD83 (feet)

GRAPHIC SCALE — 1" = 10'

0 10 20 30 40 FEET