
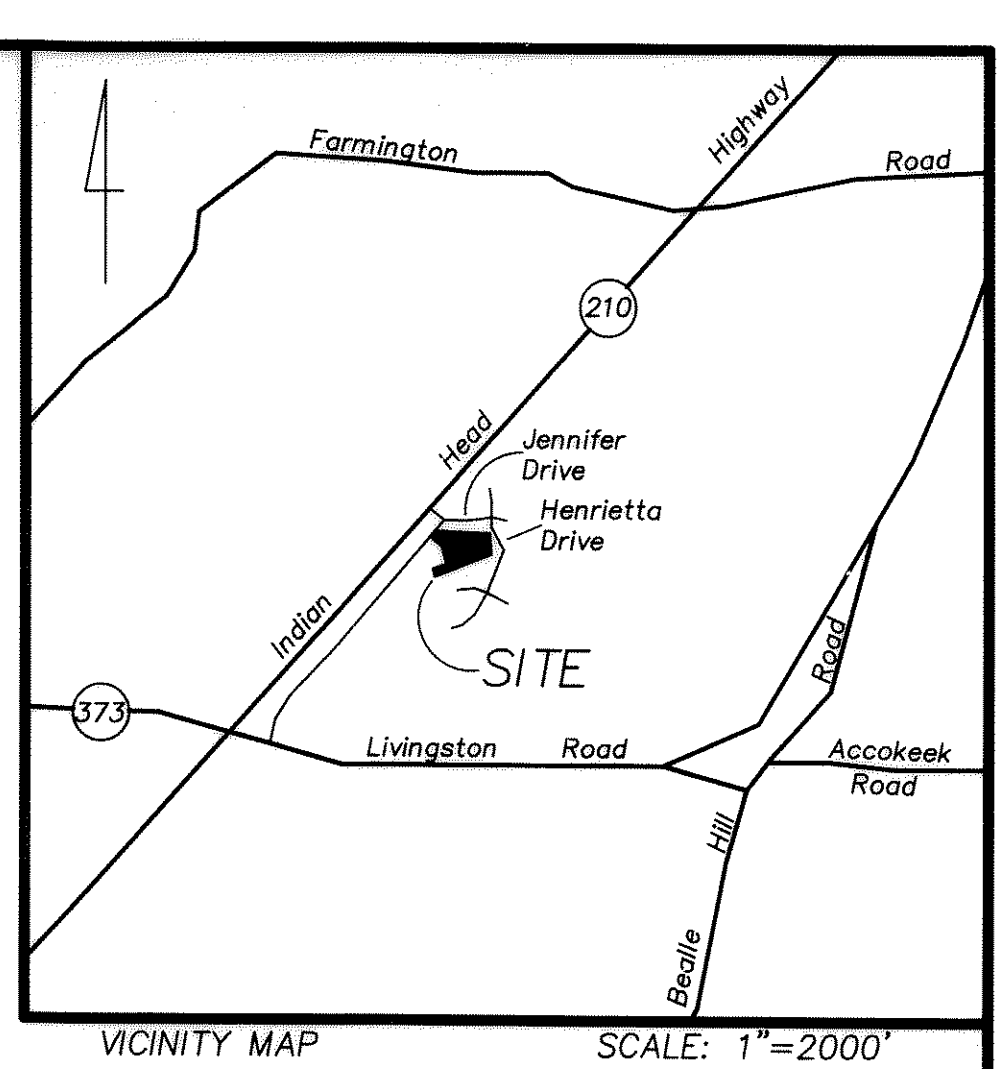


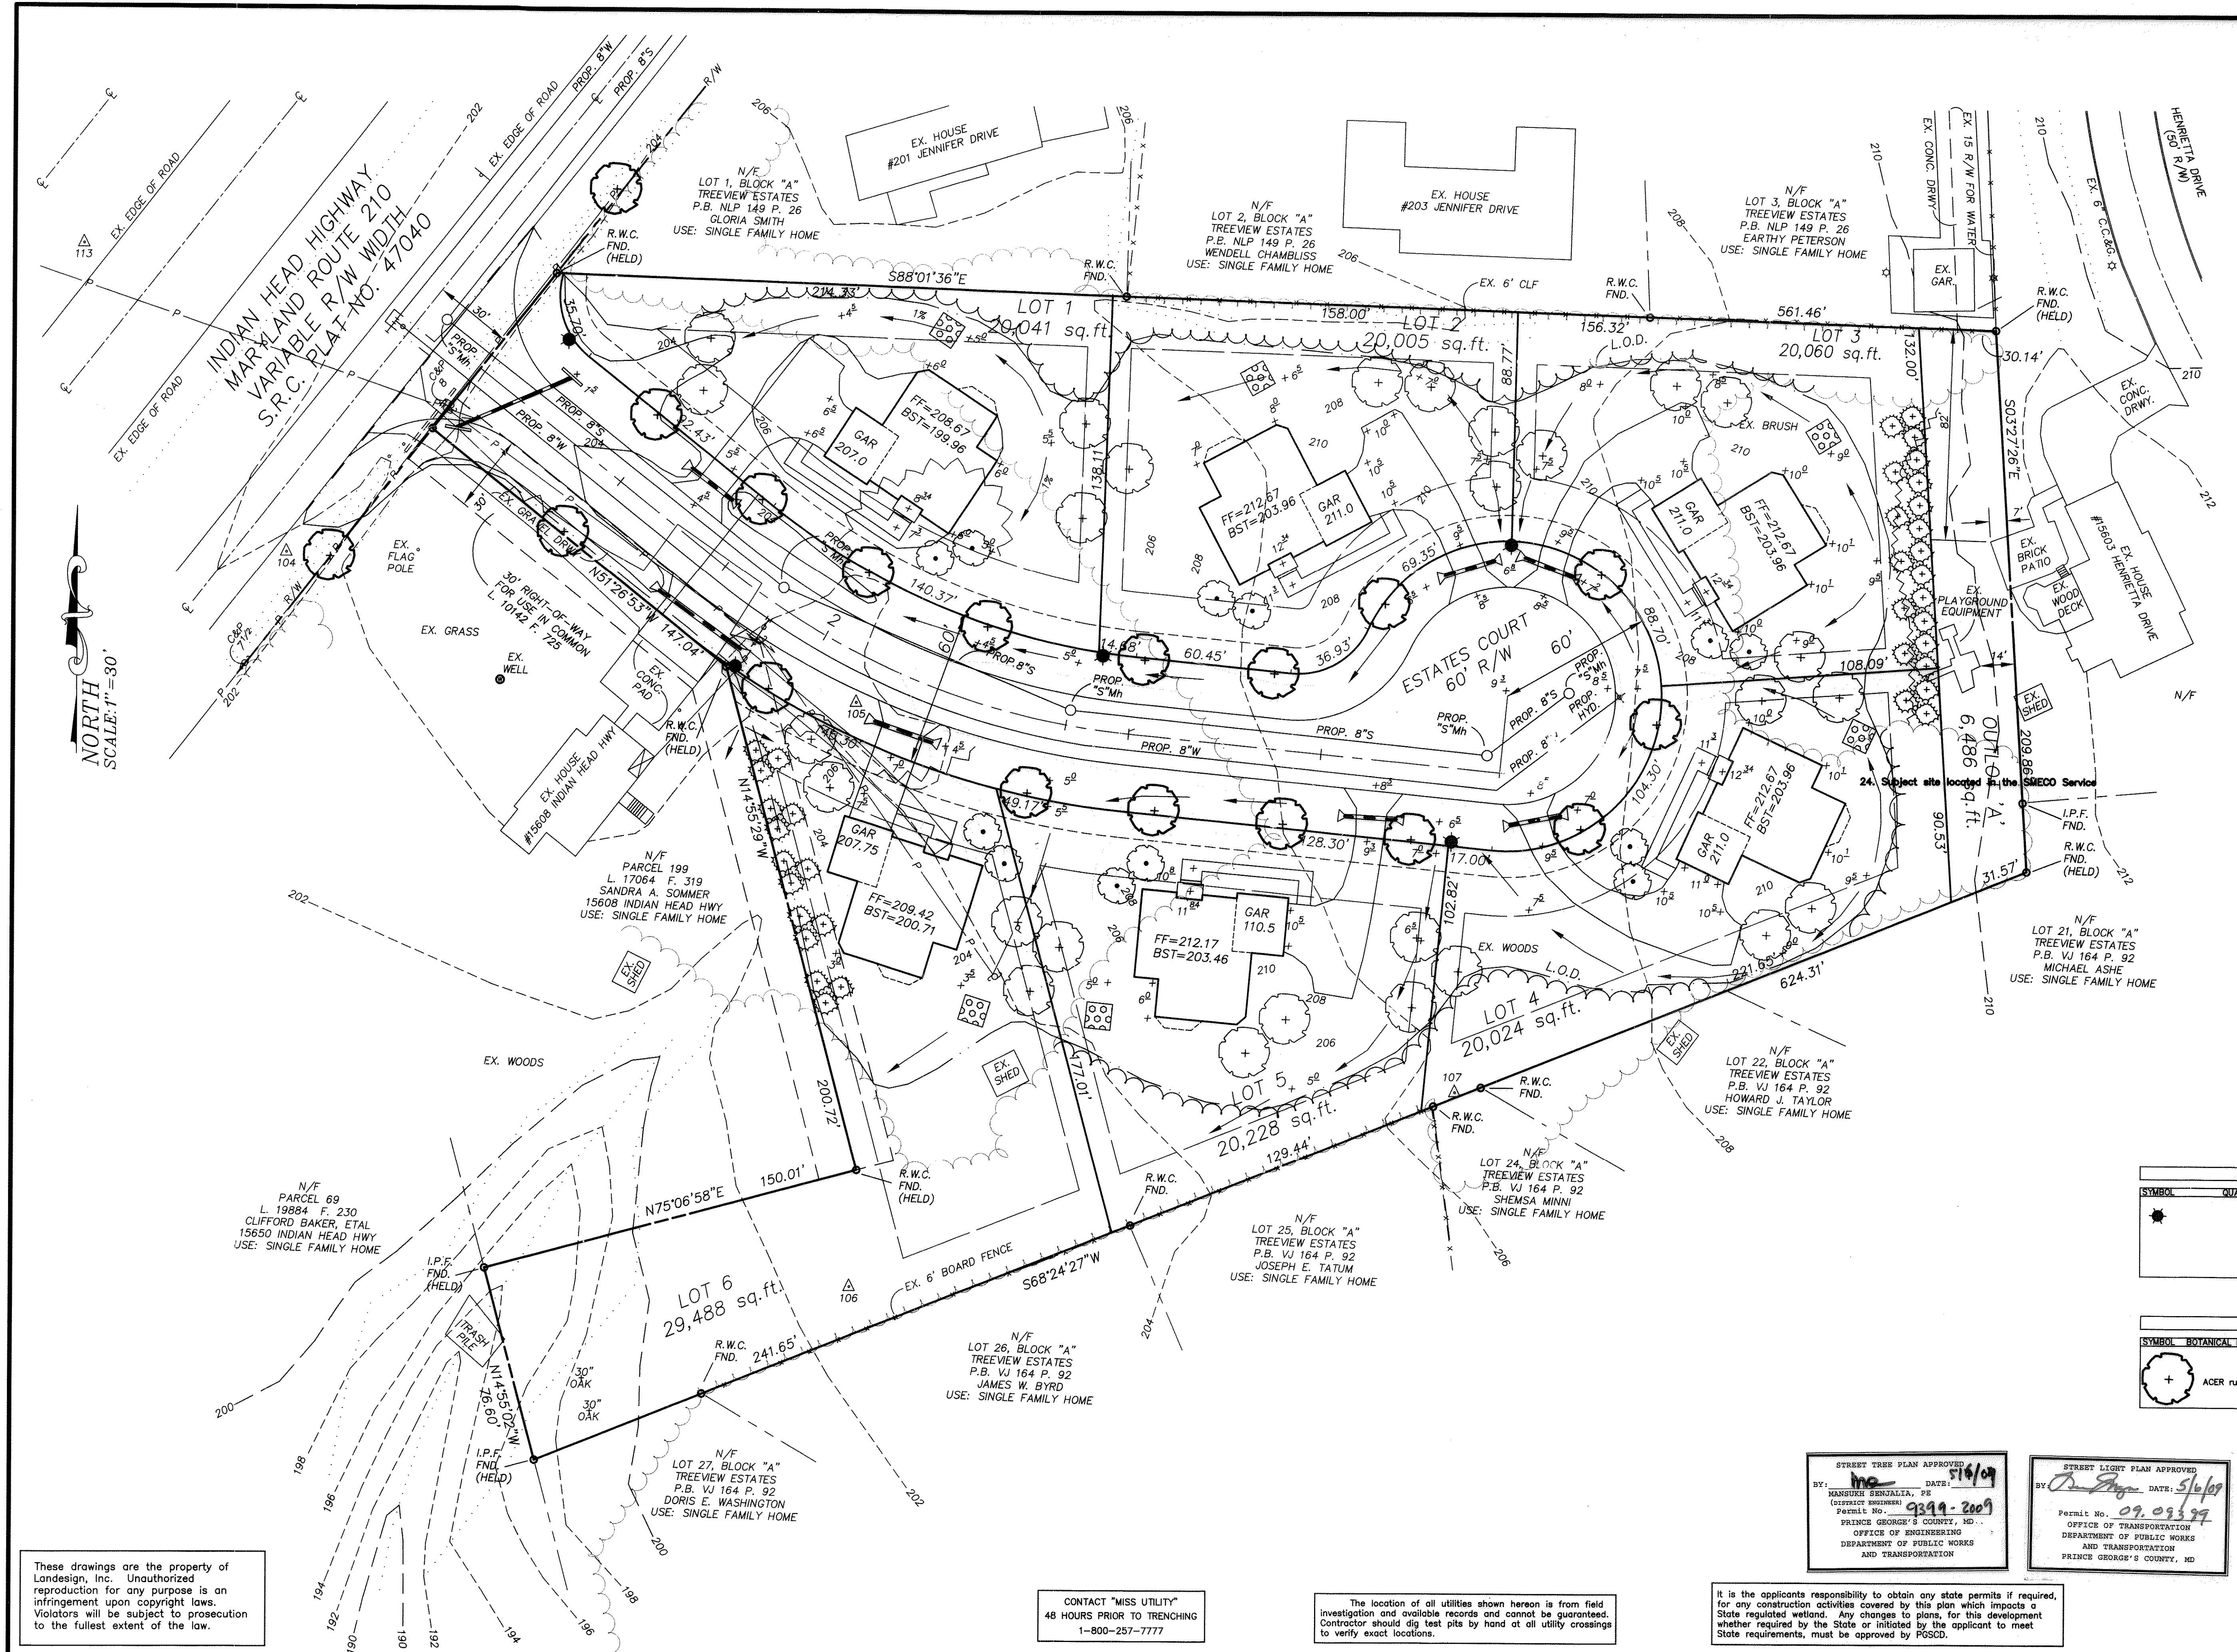

- GENERAL NOTES**
1. Subject Site Description: Lots 1-6, Outlot 'A' Estates at Indian Head Plot Book: PM 228 @ Plat: 83 Tax Map 151 Grid F-3
 2. Total Site Area: 171,505 sq.ft. or 3.9372 acres
 3. Existing Site Use: single family home
 4. Property Zoned: R-R
 5. Property located on Prince George's County Tax Map 151 Grid F-3
 6. Property located on Prince George's County Street Map 37 Grid D-2
 7. Property located on Prince George's County Soils Survey Map 50
 8. Soil Types 100% B1B2 - Beltsville silt loam, 2-5% slopes, mod. eroded
 9. Property located on Prince George's County 200' scale Topography 220 SE 01
 10. Property located on U.S.G.S. Map Mount Vernon Quadrangle
 11. Electric service: PEPCO
 12. Telephone service: Verizon
 13. Sewage disposal: Public Sewer
 14. Water supply: Public Water
 15. Sewer and Water Categories: S-3, W-3
 16. Vertical Datum: W.S.S.C.
 17. Horizontal Datum: Liber 10142 Folio 725
 18. Boundary Survey performed by Landesign, Inc. Sept. 2005
 19. Topographic Survey performed by Landesign, Inc. Sept. 2005
 20. The subject site is located in Zone "C" of the Flood Insurance Program's Flood Insurance Rate Map on Community Panel #245208 0095 C.
 21. This boundary survey was performed without the benefit of a title report.
 22. Area Statement:
 - Lot 1: 20,041 sq.ft. or 0.4600 acre
 - Lot 2: 20,005 sq.ft. or 0.4593 acre
 - Lot 3: 20,060 sq.ft. or 0.4605 acre
 - Lot 4: 20,024 sq.ft. or 0.4597 acre
 - Lot 5: 20,228 sq.ft. or 0.4644 acre
 - Lot 6: 29,488 sq.ft. or 0.6769 acre
 - Outlot "A": 6,486 sq.ft. or 0.1489 acre
 - Public Dedication: 35,173 sq.ft. or 0.8075 acre
 23. Proposed Site Conditions:
 - A. Proposed Grass: 92,458 sq.ft. or 2.1225 acres
 - B. Proposed Woods: 33,948 sq.ft. or 0.7793 acre
 - C. Proposed Impervious Material: 45,099 sq.ft. or 1.0353 acre
 24. Subject site located in the SMECO Service Area.

STREET LIGHT SCHEDULE		
SYMBOL	QUANTITY	TYPE
	5	PROP. 100 WHPVS COLONIAL POST- TOP TYPE IV BLACK FIBERGLASS / DIRECT BURIED
(Subject Site located in the SMECO Service Area)		

STREET TREE SCHEDULE					
SYMBOL	BOTANICAL NAME	COMMON NAME	QNTY	SIZE	ROOT SPACING REMARKS
	ACER rubrum	Red Maple	18	2 1/2"-3" cal.	B&B As-shown -

STREET TREE PLAN APPROVED
BY: DATE: 5/16/09
MANSURU SENJALIA, PE
(SUPERVISOR)
Permit No. 09-093-2009
PRINCE GEORGE'S COUNTY, MD
OFFICE OF ENGINEERING
DEPARTMENT OF PUBLIC WORKS
AND TRANSPORTATION

STREET LIGHT PLAN APPROVED
BY: DATE: 5/16/09
Permit No. 09-093-2009
OFFICE OF TRANSPORTATION
DEPARTMENT OF PUBLIC WORKS
AND TRANSPORTATION
PRINCE GEORGE'S COUNTY, MD

DEPARTMENT OF PUBLIC WORKS AND TRANSPORTATION (DPW&T)
ENGINEERING AND INSPECTION SERVICES DIVISION
PRINCE GEORGE'S COUNTY, MARYLAND

APPROVAL DATE: ☐ PAVING ☐ STREET TREES

BY: _____
DISTRICT ENGINEER

PERMIT NUMBER: 9399-2009-00

LOTS/BLOCKS: _____


These drawings are the property of Landesign, Inc. Unauthorized reproduction for any purpose is an infringement upon copyright laws. Violators will be subject to prosecution to the fullest extent of the law.

CONTACT "MISS UTILITY"
48 HOURS PRIOR TO TRENCHING
1-800-257-7777

The location of all utilities shown hereon is from field investigation and available records and cannot be guaranteed. Contractor should dig test pits by hand at all utility crossings to verify exact locations.

It is the applicants responsibility to obtain any state permits if required, for any construction activities covered by this plan which impacts a State regulated wetland. Any changes to plans, for this development whether required by the State or initiated by the applicant to meet State requirements, must be approved by PGSCD.

DATE	REVISION
04/28/09	Address Street Light Comments

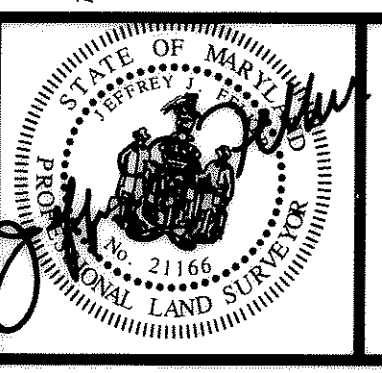


Landesign
ENGINEERS * SURVEYORS * PLANNERS
2905 MITCHELLVILLE ROAD SUITE NO. 111
BOWIE, MARYLAND 20716
(301) 249-8802

OWNER/DEVELOPER
GERALD WALDMAN
2700 VIRGINIA AVENUE N.W. #501
WASHINGTON D.C. 20037
202-338-0153

STREET TREE AND LIGHTING PLAN

LOTS 1-6 AND OUTLOT "A"
ESTATES AT INDIAN HEAD
PLAT BOOK: PM 228 AT PLAT: 83
TAX MAP 151 GRID F-3
PISCATAWAY ELECTION DISTRICT No. 5
PRINCE GEORGE'S COUNTY, MARYLAND

DATE: March, 2009	SCALE: 1"=30'
DESIGN BY: J.C.	DRAWN BY: D.H.
CHECKED BY: J.F.	SHEET No: 1 of 2
COMPUTER: "C"	JOB No: 05-019
FIELD BOOK: 105	

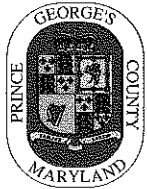

Jack Johnson
County Executive

PRINCE GEORGE'S COUNTY GOVERNMENT



Department of Public Works and Transportation
Office of Engineering



MEMORANDUM

May 4, 2009

TO: Manny Senjalia, P.E., District Engineer
Office of Engineering and Inspection Services

FROM: *AA* Armen Abrahamian, Chief
Traffic Safety Division

RE: Estates @ Indian Head, 09.09399

CR: Street Lighting

The Street Lighting Plan has been approved. Attached is the permittee's approved print. Before returning the plan, please make copies for the utility company, Southern Maryland Electric Company, and your file.

The permittee's next step is to submit the plan to the local utility company and arrange for the installation and payment of the lighting improvements. The permittee must provide the Office of Engineering, Traffic Safety Division, with a receipt or other proof-of-payment before the bond is released.

If you have any questions concerning this matter, please contact Lee Ingram at (301) 883-5650.

Attachment

AA:LWI:dar

cc: Dawit Abraham, P.E., Associate Director, OE, DPW&T
Erv Beckert, P.E., Chief, Utility Section, OE, DPW&T
Vivian Branson, Chief, Permits Section, OE, DPW&T
Lee Ingram, Engineering Technician, Utility Section, DPW&T
Gerald Waldman, 2700 Virginia Avenue, Suite 501, Washington,
DC 20037 (w/1-attachment)
William Lawman, District Manager, Southern Maryland Electric
Company, P.O. Box 1937, Hughesville, Maryland 20637
(w/1-attachment)