

SITE DEVELOPMENT CONCEPT PLAN
ESTATES AT INDIAN HEAD — LOTS 1-6

200-205 ESTATES COURT, ACCOKEEK, MD 20607 · PLAT BOOK PM 228 PLAT 83 · TAX MAP 151 F-3 · WSSC 220SE01 · ELECTION DIST. 5 · COUNCIL DIST. 9 · ZONE RR
Stormwater management by Environmental Site Design to the Maximum Extent Practicable (MDE Design Manual Ch. 5; PGC Subtitle 32). Layout per the approved 2009 Street Tree & Lighting Plan, DPW&T 9399-2009-00.

PRINCE GEORGE'S COUNTY BMP SUMMARY TABLE — ESD BY POINT OF INVESTIGATION (A-15, C-9)

| BMP                    | PRACTICE                  | MDE | LOCATION                 | OWNERSHIP / MAINT.                          | POI   | DA SF   | IMP SF | %I   | HSG | P_E IN | Rv    | ESDv REQ CF | ESDv PROV CF | Rev REQ CF | SURFACE SF | COORDINATES (NAD 83)  |
|------------------------|---------------------------|-----|--------------------------|---------------------------------------------|-------|---------|--------|------|-----|--------|-------|-------------|--------------|------------|------------|-----------------------|
| ESD-1                  | Micro-bioretentation      | M-6 | Lot 1                    | Private — lot owner (maintenance agreement) | POI-1 | 19,999  | 4,500  | 22.5 | C   | 1.2    | 0.253 | 505         | 505          | 55         | 525        | N 367.417 E 1,311.143 |
| ESD-2                  | Micro-bioretentation      | M-6 | Lot 2                    | Private — lot owner (maintenance agreement) | POI-1 | 20,015  | 2,422  | 12.1 | C   | 1.0    | 0.159 | 265         | 265          | 34         | 330        | N 367.396 E 1,311.250 |
| ESD-3                  | Micro-bioretentation      | M-6 | Lot 3                    | Private — lot owner (maintenance agreement) | POI-1 | 20,051  | 3,008  | 15.0 | C   | 1.0    | 0.185 | 309         | 309          | 40         | 386        | N 367.379 E 1,311.388 |
| ESD-4                  | Micro-bioretentation      | M-6 | Lot 4                    | Private — lot owner (maintenance agreement) | POI-1 | 20,021  | 2,062  | 10.3 | C   | 1.0    | 0.143 | 238         | 238          | 31         | 298        | N 367.217 E 1,311.299 |
| ESD-5                  | Micro-bioretentation      | M-6 | Lot 5                    | Private — lot owner (maintenance agreement) | POI-1 | 20,235  | 2,489  | 12.3 | C   | 1.0    | 0.161 | 271         | 272          | 35         | 340        | N 367.173 E 1,311.171 |
| ESD-6                  | Micro-bioretentation      | M-6 | Lot 6                    | Private — lot owner (maintenance agreement) | POI-1 | 29,536  | 2,511  | 8.5  | C   | 1.0    | 0.127 | 311         | 311          | 40         | 389        | N 367.082 E 1,310.950 |
| ESD-S1                 | Dry swale with check dams | M-8 | Estates Ct R/W, roadside | Public — DPiE                               | POI-1 | 11,212  | 6,600  | 58.9 | C   | 2.0    | 0.580 | 1,084       | 1,864        | 70         | 1,243      | N 367.379 E 1,311.111 |
| ESD-S2                 | Dry swale with check dams | M-8 | Estates Ct R/W, roadside | Public — DPiE                               | POI-1 | 457     | 269    | 58.9 | C   | 2.0    | 0.580 | 44          | 76           | 3          | 51         | N 367.375 E 1,311.268 |
| ESD-S3                 | Dry swale with check dams | M-8 | Estates Ct R/W, roadside | Public — DPiE                               | POI-1 | 14,063  | 8,279  | 58.9 | C   | 2.0    | 0.580 | 1,359       | 2,338        | 88         | 1,559      | N 367.342 E 1,311.097 |
| ESD-S4                 | Dry swale with check dams | M-8 | Estates Ct R/W, roadside | Public — DPiE                               | POI-1 | 4,957   | 2,918  | 58.9 | C   | 2.0    | 0.580 | 479         | 824          | 31         | 549        | N 367.310 E 1,311.331 |
| ESD-S5                 | Dry swale with check dams | M-8 | Estates Ct R/W, roadside | Public — DPiE                               | POI-1 | 5,352   | 3,150  | 58.9 | C   | 2.0    | 0.580 | 517         | 890          | 34         | 593        | N 367.412 E 1,311.326 |
| SUBTOTAL POI-1         |                           |     |                          |                                             |       |         |        |      |     |        |       | 5,382       | 7,892        |            |            |                       |
| TOTAL 11 ESD practices |                           |     |                          |                                             |       | 165,098 | 38,208 |      |     |        |       | 5,382       | 7,892        | 461        | 6,263      |                       |

P, E from MDE Stormwater Design Manual (2000, Supp. 1 2009), Ch. 5, Table 5-3 — rainfall targets for ESD; HSG C governing; Rv = 0.05 + 0.009·t; ESDv = P·E·Rv·A12; Rev = 5·Rv·A12 (5 = 0.13 in; HSG CL met within ESDv; M-8 provided = 6 cf per ft; (4-ft bottom; 0" ponding; 2.5" media at 0.4-0.9).

SITE DATA

| ITEM              | DATA                                                                                               |
|-------------------|---|
| Project           | Estates at Indian Head, Lots 1-6 and Estates Court                                                 |
| Location          | S. side of MD 210 ±3,000 ft NE of MD 210 / MD 373; 200-205 Estates Ct, Accokeek 20607              |
| Record            | Plat Book PM 228 Plat 83 (final plat 5-08238); Tax Map 151 F-3; WSSC 200' 220SE01                  |
| Accounts          | 3987666, 3987674, 3987682, 3987690, 3987708, 3987716                                               |
| Owner             | Gerald Waldman Revocable Trust, L 32062 F.043                                                      |
| Zone / use        | RR (no change) — 6 single-family detached dwellings                                                |
| Tract             | 165,019 sf of record (3.788 ac) = plat 171,505 sf less Outlot A (6,486 sf, conveyed L 51565 F.455) |
| Public dedication | Estates Court 60' R/W, 35,173 sf of record — rural open section, 24' pavement, cul-de-sac          |
| Water / sewer     | W-3 / S-3 (WSSC) — mains from Henrietta Dr via 30' WSSC esmt L 51799 F.399 and prop. Lot 4 esmt    |
| Watershed         | Piscataway Creek, MD 021402030798; not Tier II; not CBCA; FEMA Zone X                              |
| Master plan       | 2013 Subregion 5 Master Plan & SMA; Planning Area 84; Council Dist. 9; Election Dist. 5            |
| Datum             | NAD 83 MD State Plane (US ft); NAVD 88 (M-NCPPC 2-ft); 2009 spot grades on WSSC datum              |

APPROVALS OF RECORD

| CASE               | STATUS                                               |
|--------------------|------------------------------------------------------|
| NRI-015-06         | Approved — current                                   |
| TCP1-018-06        | Current                                              |
| TCP2-016-09        | Approved — current                                   |
| 5-08238            | Final plat, PM 228 @ 83 — recorded                   |
| DPW&T 9399-2009-00 | Street tree & lighting plan (2009) — layout followed |
| L 51799 F.399      | 30' WSSC easement (Outlot A, Lot 20) — recorded 2025 |


GENERAL NOTES

- Boundary per recorded plat PM 228 @ 83; lot lines reproduce the plat to the second. A Maryland licensed surveyor shall confirm the boundary and the MD 210 R/W before technical plans.
- Horizontal datum: Maryland State Plane NAD 83 (US ft). Vertical datum: NAVD 88 (M-NCPPC 2-ft contours). 2009 spot grades are on WSSC datum (= NAVD 88 + 1.6 ft, to be confirmed by the field-run survey). DPiE prefers NGVD 29 — the survey shall state the conversion.
- The layout follows the approved 2009 Street Tree & Lighting Plan (DPW&T 9399-2009-00): dwellings, side-load garages and courts, street trees and street lights. Lot 4 is front-load (garage to the cul-de-sac) to clear the WSSC easement.
- Estates Court is a rural open section (DPW&T Std. 500.10 / 600.02 / 600.04): 24' pavement, shoulders, roadside swales; driveways cross the swale on 15" RCP culverts with flared end sections.
- Entrance to MD 210 (SHA) with 50' returns as the 2009 plan; SHA access permit and sight-distance analysis required. MD 210 auxiliary lanes shown for SHA review; R/W dedication may be required.
- Water and sewer: WSSC mains from Henrietta Dr through the recorded 30' WSSC easement (L 51799 F.399) and a 30' WSSC easement to be granted across Lot 4. Record discrepancies in the easement description to be resolved with WSSC.
- Approvals of record NRI-015-06, TCP1-018-06 and TCP2-016-09 are current. No streams, wetlands, floodplain, PMA or Chesapeake Bay Critical Area on the property.
- Contact Miss Utility (811) at least 48 hours before any excavation.

DPIE SITE DEVELOPMENT CONCEPT PLAN DESIGN REVIEW CHECKLIST (REV. 08/25/2021) — CONSULTANT RESPONSE (C = SHOWN · X = N/A · O = OBTAINING/INDETERMINANT)

| ITEM | REQUIREMENT   | REF.    | C/X/O | RESPONSE / WHERE SHOWN   | SHEET |
|------|---|---------|-------|---|-------|
| A-1  | Plan is labeled as Site Development Concept Plan (aka Concept Plan from MDE Step 1)                                                                  |         | C     | Every sheet is titled SITE DEVELOPMENT CONCEPT PLAN.   | ALL   |
| A-2  | Plan sheet size does not exceed 30" x 42" and all sheets are printed on same size paper.                                                             | 5.3.2   | C     | All sheets 24" x 36" (ARCH D).   | ALL   |
| A-3  | A 5-inch, full-height open area is provided on the right-hand side of the drawing for County approval block.                                         | 2.2.1.A | C     | 5-inch full-height strip at the right edge, kept clear for DPiE.   | ALL   |
| A-4  | If more than 4 plan sheets: composite plan showing match lines and sheet numbers (scale not to exceed 1"=200'); key map on each plan sheet.          | 2.2.1.O | C     | 7 sheets: the whole site is on each plan sheet at one scale, so no match lines; key map in every title block.                                                                               | ALL   |
| A-5  | Match lines have a minimum length of 4 inches and identify the matching sheet number.                                                                | 2.2.1.M | X     | No match lines — the entire site fits one viewpoint.   |       |
| A-6  | Vicinity map at a minimum scale of 1"=2,000' with north arrow and scale, upper right hand corner of cover sheet.                                     | 2.2.1.B | C     | Vicinity map at 1" = 2,000' with north arrow and bar scale, upper right.   | C-000 |
| A-7  | A bar scale is provided on every sheet.   |         | C     | Graphic bar scale in every plan viewpoint.   | ALL   |
| A-8  | Three grid ticks are provided as described in the manual.                                                                                            | 2.2.1.E | C     | Three State Plane grid ticks with N/E values on each plan.   | C-200 |
| A-9  | Horizontal M/D Coordinate System, NAD 83 and vertical (NGVD 29 preferred) datum is stated on the plan.                                               |         | C     | Horizontal Maryland State Plane, NAD 83 (EPSG 2248); US ft; vertical NAVD 88 (M-NCPPC 2-ft); 2009 spot grades WSSC datum as noted. NGVD 29 conversion to be stated by the field-run survey. | ALL   |
| A-10 | General notes about the project are provided.   |         | C     | General notes on the cover sheet.   | C-000 |
| A-11 | The entire property is shown at a maximum plan scale of 1 inch = 30 feet (preferred) within the plan set.                                            | 5.3.2   | C     | Entire property at 1" = 30'.   | C-200 |
| A-12 | All existing structures and site features including cultural features, historic sites and easements, and any visible foundations or ruins are shown. | 5.3.2   | C     | Existing structures, adjoining houses, fences, sheds, well, easements of record shown; no historic sites or ruins.                                                                          | C-100 |
| A-13 | Topographic contours at maximum 2 foot interval, extending at least 100 feet beyond the property.                                                    | 32-182  | C     | M-NCPPC 2-ft contours, 100 ft beyond the property.   | C-100 |
| A-14 | All existing utilities and utility easements are shown.                                                                                              |         | C     | WSSC easement L 51799 F.399 and the proposed Lot 4 WSSC easement; public utility easements along the frontage; existing mains in Henrietta Dr noted (sizes to verify on WSSC 220SE01).      | C-300 |
| A-15 | The County BMP Summary Table is provided. Preferred location is on the cover sheet.                                                                  | 5.3.1   | C     | County BMP Summary Table, 11 practices.   | C-000 |
| B-1  | Banks of all regulated streams or a centerline if the banks are too close together to graphically show.                                              | MDE 5.7 | X     | No streams on site, NRI-015-06 approved (current); TCP1-018-06 and TCP2-016-09 (current).                                                                                                   |       |
| B-2  | Location of stream and stream buffers and/or enhanced buffers per MNCPPC and SCD criteria.                                                           | MDE 5.7 | X     | No streams, no stream buffers.   |       |
| B-3  | Location of wetlands and/or wetlands of special state concern and appropriate wetland buffers.                                                       | MDE 5.7 | X     | No wetlands on or within 100 ft (DNR, NRI).   |       |
| B-4  | Delineation of the 100-year floodplain, per Techno-Gram 004-2020.                                                                                    | MDE 5.7 | X     | FEMA Zone X; no 100-yr floodplain on or within 100 ft.   |       |
| B-5  | Location of steep slopes (15% and greater) clearly shown on the plan and in the legend.                                                              | M-NCPPC | C     | Slopes 15-25%; 2,757 sf, >25%; 520 sf — shown and in the legend.   | C-100 |
| B-6  | The Primary Management Area is delineated.   | MDE 5.7 | X     | No PMA on the property.   |       |
| B-7  | Existing woodland is delineated on the property.   | MDE 5.7 | C     | Woodland per approved NRI-015-06 and TCP2-016-09 (current); woodland conservation per the approved TCP2.                                                                                    | C-100 |
| B-8  | Existing environmental features extend off the property 100 feet in all directions.                                                                  | MNCPPC  | C     | Environmental layers drawn 100 ft beyond the property.   | C-100 |
| B-9  | Soil types and soil boundaries from USDA NRCS Soil Survey (Dec. 2009 or latest).                                                                     |         | C     | Soil types and boundaries from USDA NRCS (PGAtlas Soil layer): CwE (HSG C); UdaF (HSG —); BaB (HSG C); BuB (HSG CL).                                                                        | C-100 |
| B-10 | Plan notes identify TMDL watershed (sediment, nitrogen, phosphorus) and Tier II waters/watershed.                                                    |         | C     | Chesapeake Bay TMDL (nitrogen, phosphorus, sediment) applies; MD 12-digit watershed 021402030798, Piscataway Creek (02140203). Tier II: no.                                                 | C-000 |
| B-11 | Highly erodible soils noted.   | MDE 5.7 | C     | Beltsville silt loam (K 0.37) is highly erodible where slopes are 15% or more; those areas are stabilized within 3 days.                                                                    | C-000 |
| B-12 | Springs and seeps noted.   | MDE 5.7 | X     | None observed or mapped.   |       |
| B-13 | Bedrock and Marlboro Clay outcrops noted.   | MDE 5.7 | X     | No bedrock or Marlboro clay mapped (PGAtlas); geotechnical report to confirm (E-2).   |       |
| B-14 | Chesapeake Bay Critical Areas delineated.   | MDE 5.7 | X     | Not in the Chesapeake Bay Critical Area.   |       |

| ITEM | REQUIREMENT   | REF.                                    | C/X/O | RESPONSE / WHERE SHOWN   | SHEET |
|------|---|-----------------------------------------|-------|---|-------|
| C-1  | Project layout is shown, including roads, buildings, parking, sidewalk and other improvements and associated grading.                                | 32-182                                  | C     | Estates Court, 6 dwellings, driveways and courts, entrance at MD 210, grading.                                                                | C-200 |
| C-2  | Preliminary locations of ESD and structural stormwater practices: grading for devices where slopes exceed 15%.                                       | 32-182                                  | C     | 11 ESD practices (micro-bioretentation M-6 per lot; roadside dry swales M-8).                                                                 | C-400 |
| C-3  | Preliminary locations of storm drain inlets and culverts; entrance and outfall structures located beyond project limits (easements may be required). | 5.2.4.4.2B / 32-162.A.6                 | C     | Open section — no inlets; 6 driveway culverts (15" RCP) with end sections; swales outfall at the entrance to the MD 210 roadside ditch (SHA). | C-400 |
| C-4  | Limit of Disturbance shown for all site work, incl. water, sewer, storm drain, SWM, road improvements, sediment control, stockpile.                  | 32-182                                  | C     | LOD 22,317 sf incl. mains, easement work off site, sediment control and stockpile.                                                            | C-500 |
| C-5  | Existing easements shown and any required offsite proposed easements.                                                                                |                                         | C     | Recorded WSSC easement (Outlot A, Lot 20) and proposed Lot 4 WSSC easement; private SWM easements over ESD practices.                         | C-300 |
| C-6  | Locations, names and widths of existing and ultimate rights-of-way of adjacent streets and alleys; public vs. private noted.                         |                                         | C     | MD 210 (variable R/W, SHA), Estates Ct (60' public), Henrietta Dr and Jennifer Dr (50' public), 30' R/W in common L 10142 F.723 (recorded).   | C-200 |
| C-7  | Existing and proposed water well and septic field locations are shown.                                                                               |                                         | C     | No wells or septic proposed (public water and sewer). Existing well on Parcel 199 (15608 Indian Head Hwy), off site, shown.                   | C-100 |
| C-8  | Proposed public dedication area including any proposed parkland is shown and labelled.                                                               |                                         | C     | Estates Court public dedication 36,041 sf (plat PM 228 @ 83); no parkland.                                                                    | C-200 |
| C-9  | Point(s) of investigation shown; ESDv computations and BMP Summary Table broken out to show ESD Required is Provided within each POI.                |                                         | C     | 1 POI(s); ESDv required vs. provided tabulated per POI.                                                                                       | C-400 |
| C-10 | The ultimate 100-year stormwater overflow path is shown throughout the site using flow arrows.                                                       |                                         | C     | 100-yr overflow arrows from every practice to its POI (11).                                                                                   | C-400 |
| C-11 | Drainage areas to each device, offsite drainage onto the site, and to site outfalls; diverted areas analysed for no increase in 100-yr discharge.    |                                         | C     | Drainage area to each practice; off-site area onto the site 0.49 ac; no diversion between POIs.                                               | C-400 |
| C-12 | Where grading blocks a drainage course, ponding limits before and after grading are shown.                                                           |                                         | X     | No fill across a drainage course.   |       |
| D-1  | Report addresses natural resource protection, natural flow patterns, impervious reduction, ESC integration, ESD planning to the MEP.                 | MDE 5.11                                | O     | SWM concept narrative (ESD to the MEP, flow patterns, ESC integration) — to accompany the plans.                                              |       |
| D-2  | If in the Chesapeake Bay Critical Area, discussion of flow requirements are met; preliminary computations.                                           |                                         | X     | Not in the Chesapeake Bay Critical Area.   |       |
| D-3  | Outfalls located outside the site, to existing storm drain or 100-yr floodplain; otherwise the discharge area is described.                          |                                         | O     | Narrative: outfalls at the POIs; swales discharge to the MD 210 roadside ditch; describe receiving areas.                                     |       |
| D-4  | Stabilization at downstream outfall and upstream inflow evaluated; measures against gully formation discussed.                                       |                                         | O     | Narrative: outfall stabilization (level spreaders / riprap) at each POI.                                                                      |       |
| D-5  | Photographs of the stream at the downstream outfall and upstream property line; eroded slopes.                                                       |                                         | X     | No stream at the outfalls.   |       |
| D-6  | If outfall is to an existing SWM facility, its capacity for the added area and flow is documented.                                                   |                                         | X     | No existing SWM facility receives the site.                                                                                                   |       |
| D-7  | If rezoned to higher imperviousness, effects on downstream properties analysed.                                                                      |                                         | X     | No rezoning (RR remains RR).   |       |
| D-8  | Floodplain ordinance discussion (drainage courses, buildings within 25 ft of floodplain, dams, downstream crossings).                                |                                         | X     | No floodplain or drainage course on or downstream within the site, no dams.                                                                   |       |
| D-9  | If a waiver of water quality or quantity is requested, the basis is provided.                                                                        |                                         | X     | No waiver requested.   |       |
| D-10 | Computations: ESD/WDv required and provided; 100-yr existing and proposed runoff; downstream storm drain analysis with 10-yr control if inadequate.  | 5.3.3 / 5.2.6.1 / 5.2.4.2 / TG 002-2019 | O     | ESDv computations are on the cover; 100-yr existing/proposed runoff at each POI and downstream analysis to follow in the report.              |       |
| E-1  | A Geotechnical Report for SWM is provided to support concept development and feasibility.                                                            | 5.3.3 / TG 004-2018                     | O     | Geotechnical report for SWM (borings and Sec. 32-131 infiltration tests at each practice) — to be submitted.                                  |       |
| E-2  | Geotechnical Report addresses Marlboro and Christiana clays, silt/clay, and diatomaceous soils.                                                      | 5.3.3 / TG 005-2018 / PGSCD I-8         | O     | Geotechnical report to address Marlboro/Christiana clays, silt/clay, and diatomaceous soils.                                                  |       |
| E-3  | Affidavit of Public Informational mailing is provided with second submission.                                                                        | 32-182(g)                               | O     | Affidavit of the adjacent-owner mailing (within 7 days of submission) — with second submission.                                               |       |
| E-4  | A draft Natural Resource Inventory is provided with initial submission (approved copy required prior to approval).                                   | 32-182(a)                               | C     | NRI-015-06 approved (current); TCP1-018-06 and TCP2-016-09 (current).                                                                         |       |

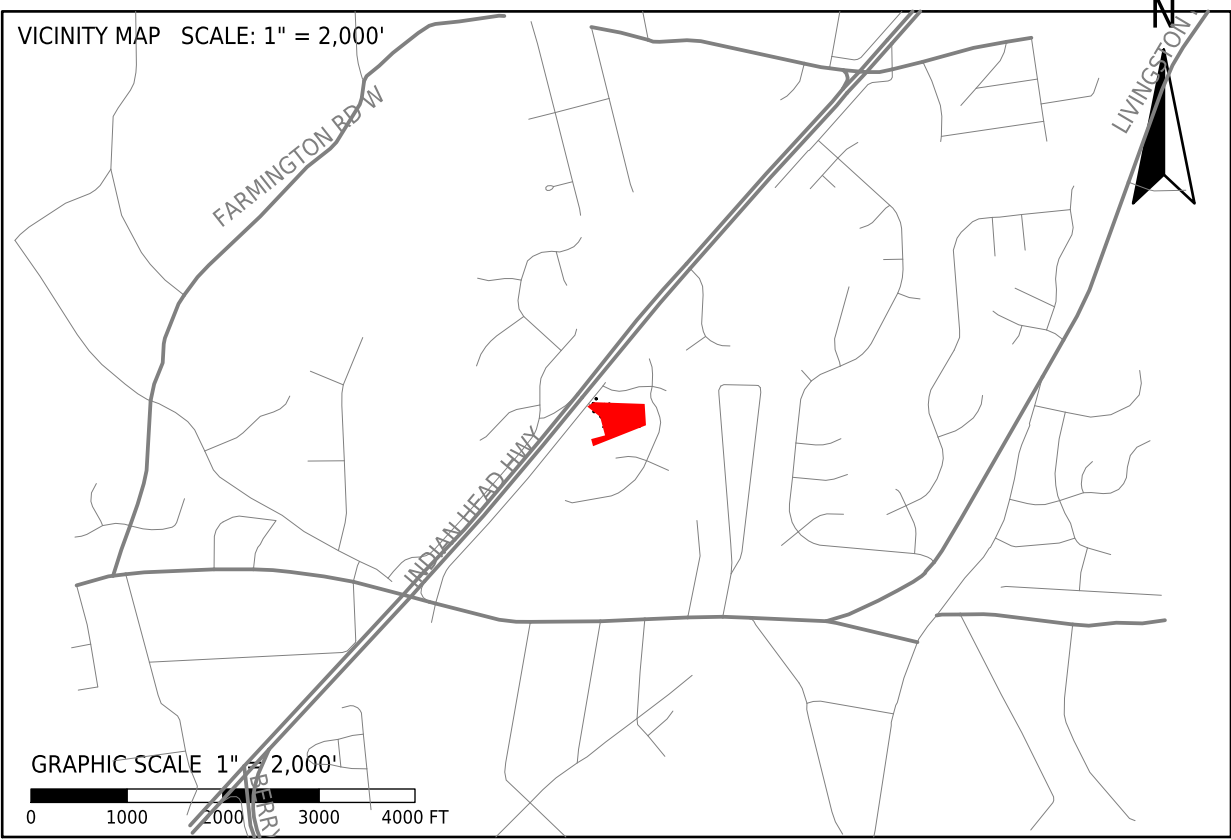

PLAN TYPE  
SITE DEVELOPMENT CONCEPT PLAN

PROJECT  
ESTATES AT INDIAN HEAD — LOTS 1-6  
200-205 ESTATES COURT, ACCOKEEK, MD 20607  
PLAT BOOK PM 228 PLAT 83 · TAX MAP 151 F-3 · WSSC 220SE01  
ELECTION DIST. 5 · COUNCIL DIST. 9 · ZONE RR

OWNER / APPLICANT  
GERALD WALDMAN REVOCABLE TRUST, 400 N. FLAGLER DR., WEST PALM BEACH, FL 33401 (L 32062 F.043)

ENGINEER OF RECORD  
W.L. MECKINS, INC. — BILL MECKINS, JR., 3101 RITCHIE ROAD, FORESTVILLE, MD 20747 · 301-736-7115

SHEET TITLE  
COVER SHEET — BMP SUMMARY, DPiE CHECKLIST AND NOTES

KEY MAP

SCALE  
AS NOTED  
DATUM: NAD 83 MD STATE PLANE (US FT) / NAVD 88

REVISIONS  
NO. DATE DESCRIPTION  
1 2026-09-30 CONCEPT SUBMISSION 1

PROFESSIONAL CERTIFICATION  
I hereby certify that these documents were prepared or approved by me, and that I am a duly licensed professional engineer under the laws of the State of Maryland. License No. \_\_\_\_\_ Exp. \_\_\_\_\_


SEAL

CONCEPT SUBMISSION 1 — NOT SEALED

SHEET INDEX  
C-000 COVER SHEET — BMP SUMMARY, DPiE CHECKLIST AND NOTES  
C-100 EXISTING CONDITIONS AND ENVIRONMENTAL FEATURES  
C-200 SITE LAYOUT, GRADING AND PAVING PLAN  
C-300 UTILITY, STREET LIGHT AND STREET TREE PLAN  
C-400 STORMWATER MANAGEMENT CONCEPT AND DRAINAGE AREA MAP  
C-500 SEDIMENT AND EROSION CONTROL PLAN  
C-600 DETAILS

RESERVED FOR PRINCE GEORGE'S COUNTY DPiE APPROVAL BLOCK  
(5-IN FULL-HEIGHT AREA KEPT OPEN — CHECKLIST A-3)

EXISTING CONDITIONS AND ENVIRONMENTAL FEATURES

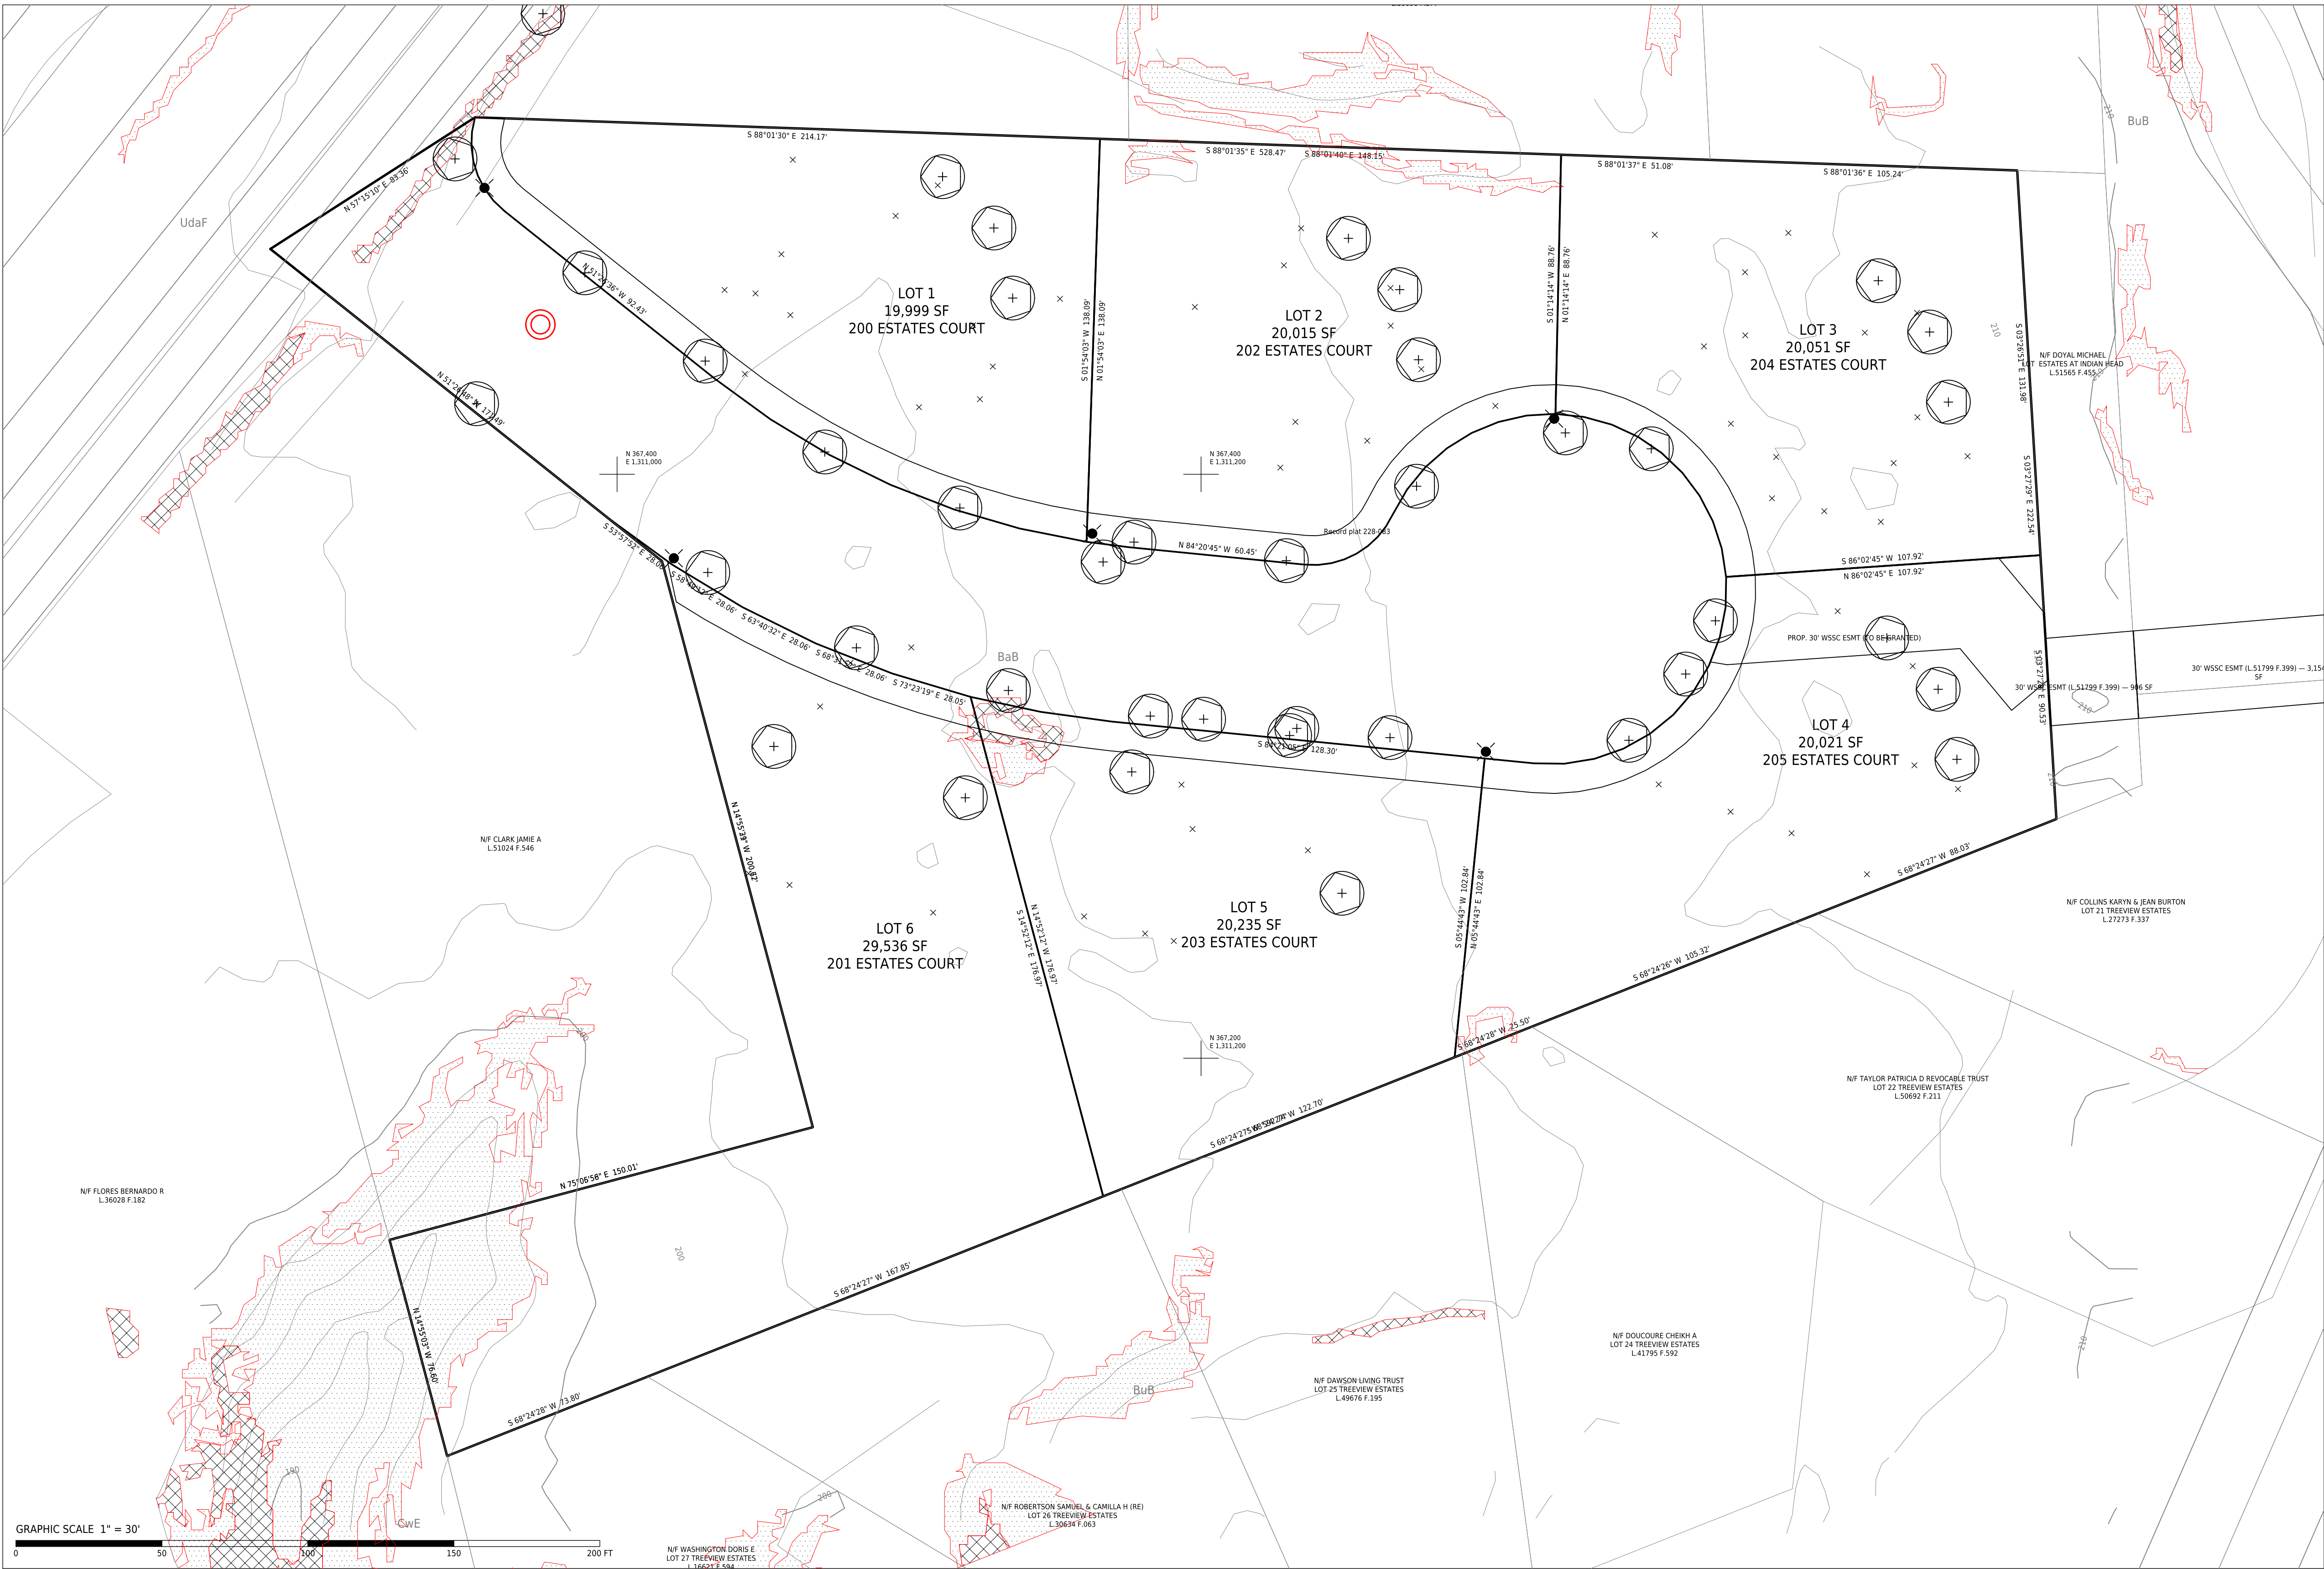

LEGEND

- Boundary of record (plat PM 228 @ 83)
- Lot line
- Adjoining property
- Existing contour, 10-ft (NAVD 88)
- Existing contour, 2-ft
- Existing edge of road
- Existing right-of-way
- Slopes 15-25% (dots) / > 25% (hatch)
- Soil boundary (USDA NRCS)
- Easement

SOILS (USDA NRCS)

| SYMBOL | NAME                                                 | HSG | K   | HIGHLY ERODIBLE        |
|--------|------------------------------------------------------|-----|-----|------------------------|
| CwE    | Croom-Marr complex, 15 to 25 percent slopes          | C   | .15 | NO                     |
| UdaF   | Udorthents, highway, 0 to 65 percent slopes          | —   | —   | NO                     |
| BaB    | Beltsville silt loam, 2 to 5 percent slopes          | C   | .37 | YES (on slopes >= 15%) |
| BuB    | Beltsville-Urban land complex, 0 to 5 percent slopes | C   | .37 | YES (on slopes >= 15%) |

ENVIRONMENTAL FEATURES — DPE CHECKLIST B


| ITEM | CX/DX | FINDING   |
|------|-------|---|
| B-1  | X     | No streams on site. NRI-015-06 approved (current); TCP1-018-06 and TCP2-016-09 (current).                                                   |
| B-2  | X     | No streams, no stream buffers.   |
| B-3  | X     | No wetlands on or within 100 ft (DNR; NRI).                                                                                                 |
| B-4  | X     | FEMA Zone X; no 100-yr floodplain on or within 100 ft.                                                                                      |
| B-5  | C     | Slopes 15-25%; 2,757 sf; >25%; 520 sf — shown and in the legend.                                                                            |
| B-6  | X     | No PMA on the property.   |
| B-7  | C     | Woodland per approved NRI-015-06 and TCP2-016-09 (current); woodland conservation per the approved TCP2.                                    |
| B-8  | C     | Environmental layers drawn 100 ft beyond the property.                                                                                      |
| B-9  | C     | Soil types and boundaries from USDA NRCS (PDAlex Soil layer): CwE (HSG C); UdaF (HSG C); BaB (HSG C); BuB (HSG C).                          |
| B-10 | C     | Chesapeake Bay TMDL (nitrogen, phosphorus, sediment) applies; MD 12-digit watershed 021402030798, Piscataway Creek (02140203). Tier II: no. |
| B-11 | C     | Beltsville silt loam (K 0.37) is highly erodible where slopes are 15% or more; those areas are stabilized within 3 days.                    |
| B-12 | X     | None observed or mapped.   |
| B-13 | X     | No bedrock or Marlboro clay mapped (PGAtlas); geotechnical report to confirm (E-3).                                                         |
| B-14 | X     | Not in the Chesapeake Bay Critical Area.   |

PLAN TYPE  
SITE DEVELOPMENT CONCEPT PLAN

PROJECT  
ESTATES AT INDIAN HEAD — LOTS 1-6  
200-205 ESTATES COURT, ACCOKEEK, MD 20607  
PLAT BOOK PM 228 PLAT 83 - TAX MAP 151 F-3 - WSSC  
220501  
ELECTION DIST. 5 - COUNCIL DIST. 9 - ZONE RR  
OWNER / APPLICANT  
GERALD WALDMAN REVOCABLE TRUST, 400 N. FLAGLER DR., WEST  
PALM BEACH, FL 33401 (L 32062 F 043)  
ENGINEER OF RECORD  
W.L. MEEKINS, INC. — BILL MEEKINS, JR., 3101 RITCHIE ROAD,  
FORESTVILLE, MD 20747-301-736-7115

SHEET TITLE  
EXISTING CONDITIONS AND ENVIRONMENTAL  
FEATURES


KEY MAP

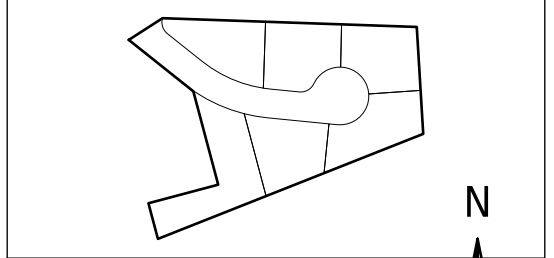

SCALE  
1" = 30'  
DATUM: NAD 83 MD STATE PLANE (US FT) / NAVD 88

| REVISIONS | NO.        | DATE                 | DESCRIPTION |
|-----------|------------|----------------------|-------------|
| 1         | 2026-09-30 | CONCEPT SUBMISSION 1 |             |

PROFESSIONAL CERTIFICATION  
I hereby certify that these documents were prepared or approved by me,  
and that I am a duly licensed professional engineer under the laws of  
the State of Maryland. License No. \_\_\_\_\_ Exp. \_\_\_\_\_

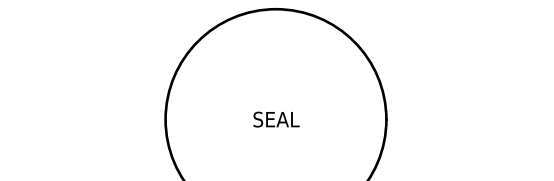

CONCEPT SUBMISSION 1 — NOT SEALED


DATE: 2026-09-30 JOB: KEA-EH-2026

PREPARED WITH: SCALE: 1"=30' (US FT) / NAVD 88

SHEET INDEX

- C-100 COVER SHEET — BMP SUMMARY, DPE CHECKLIST AND NOTES
- C-100 EXISTING CONDITIONS AND ENVIRONMENTAL FEATURES
- C-200 SITE LAYOUT, GRADING AND PAVING PLAN
- C-300 UTILITY, STREET LIGHT AND STREET TREE PLAN
- C-400 STORMWATER MANAGEMENT CONCEPT AND DRAINAGE AREA MAP
- C-500 SEDIMENT AND EROSION CONTROL PLAN
- C-600 DETAILS

SITE LAYOUT, GRADING AND PAVING PLAN

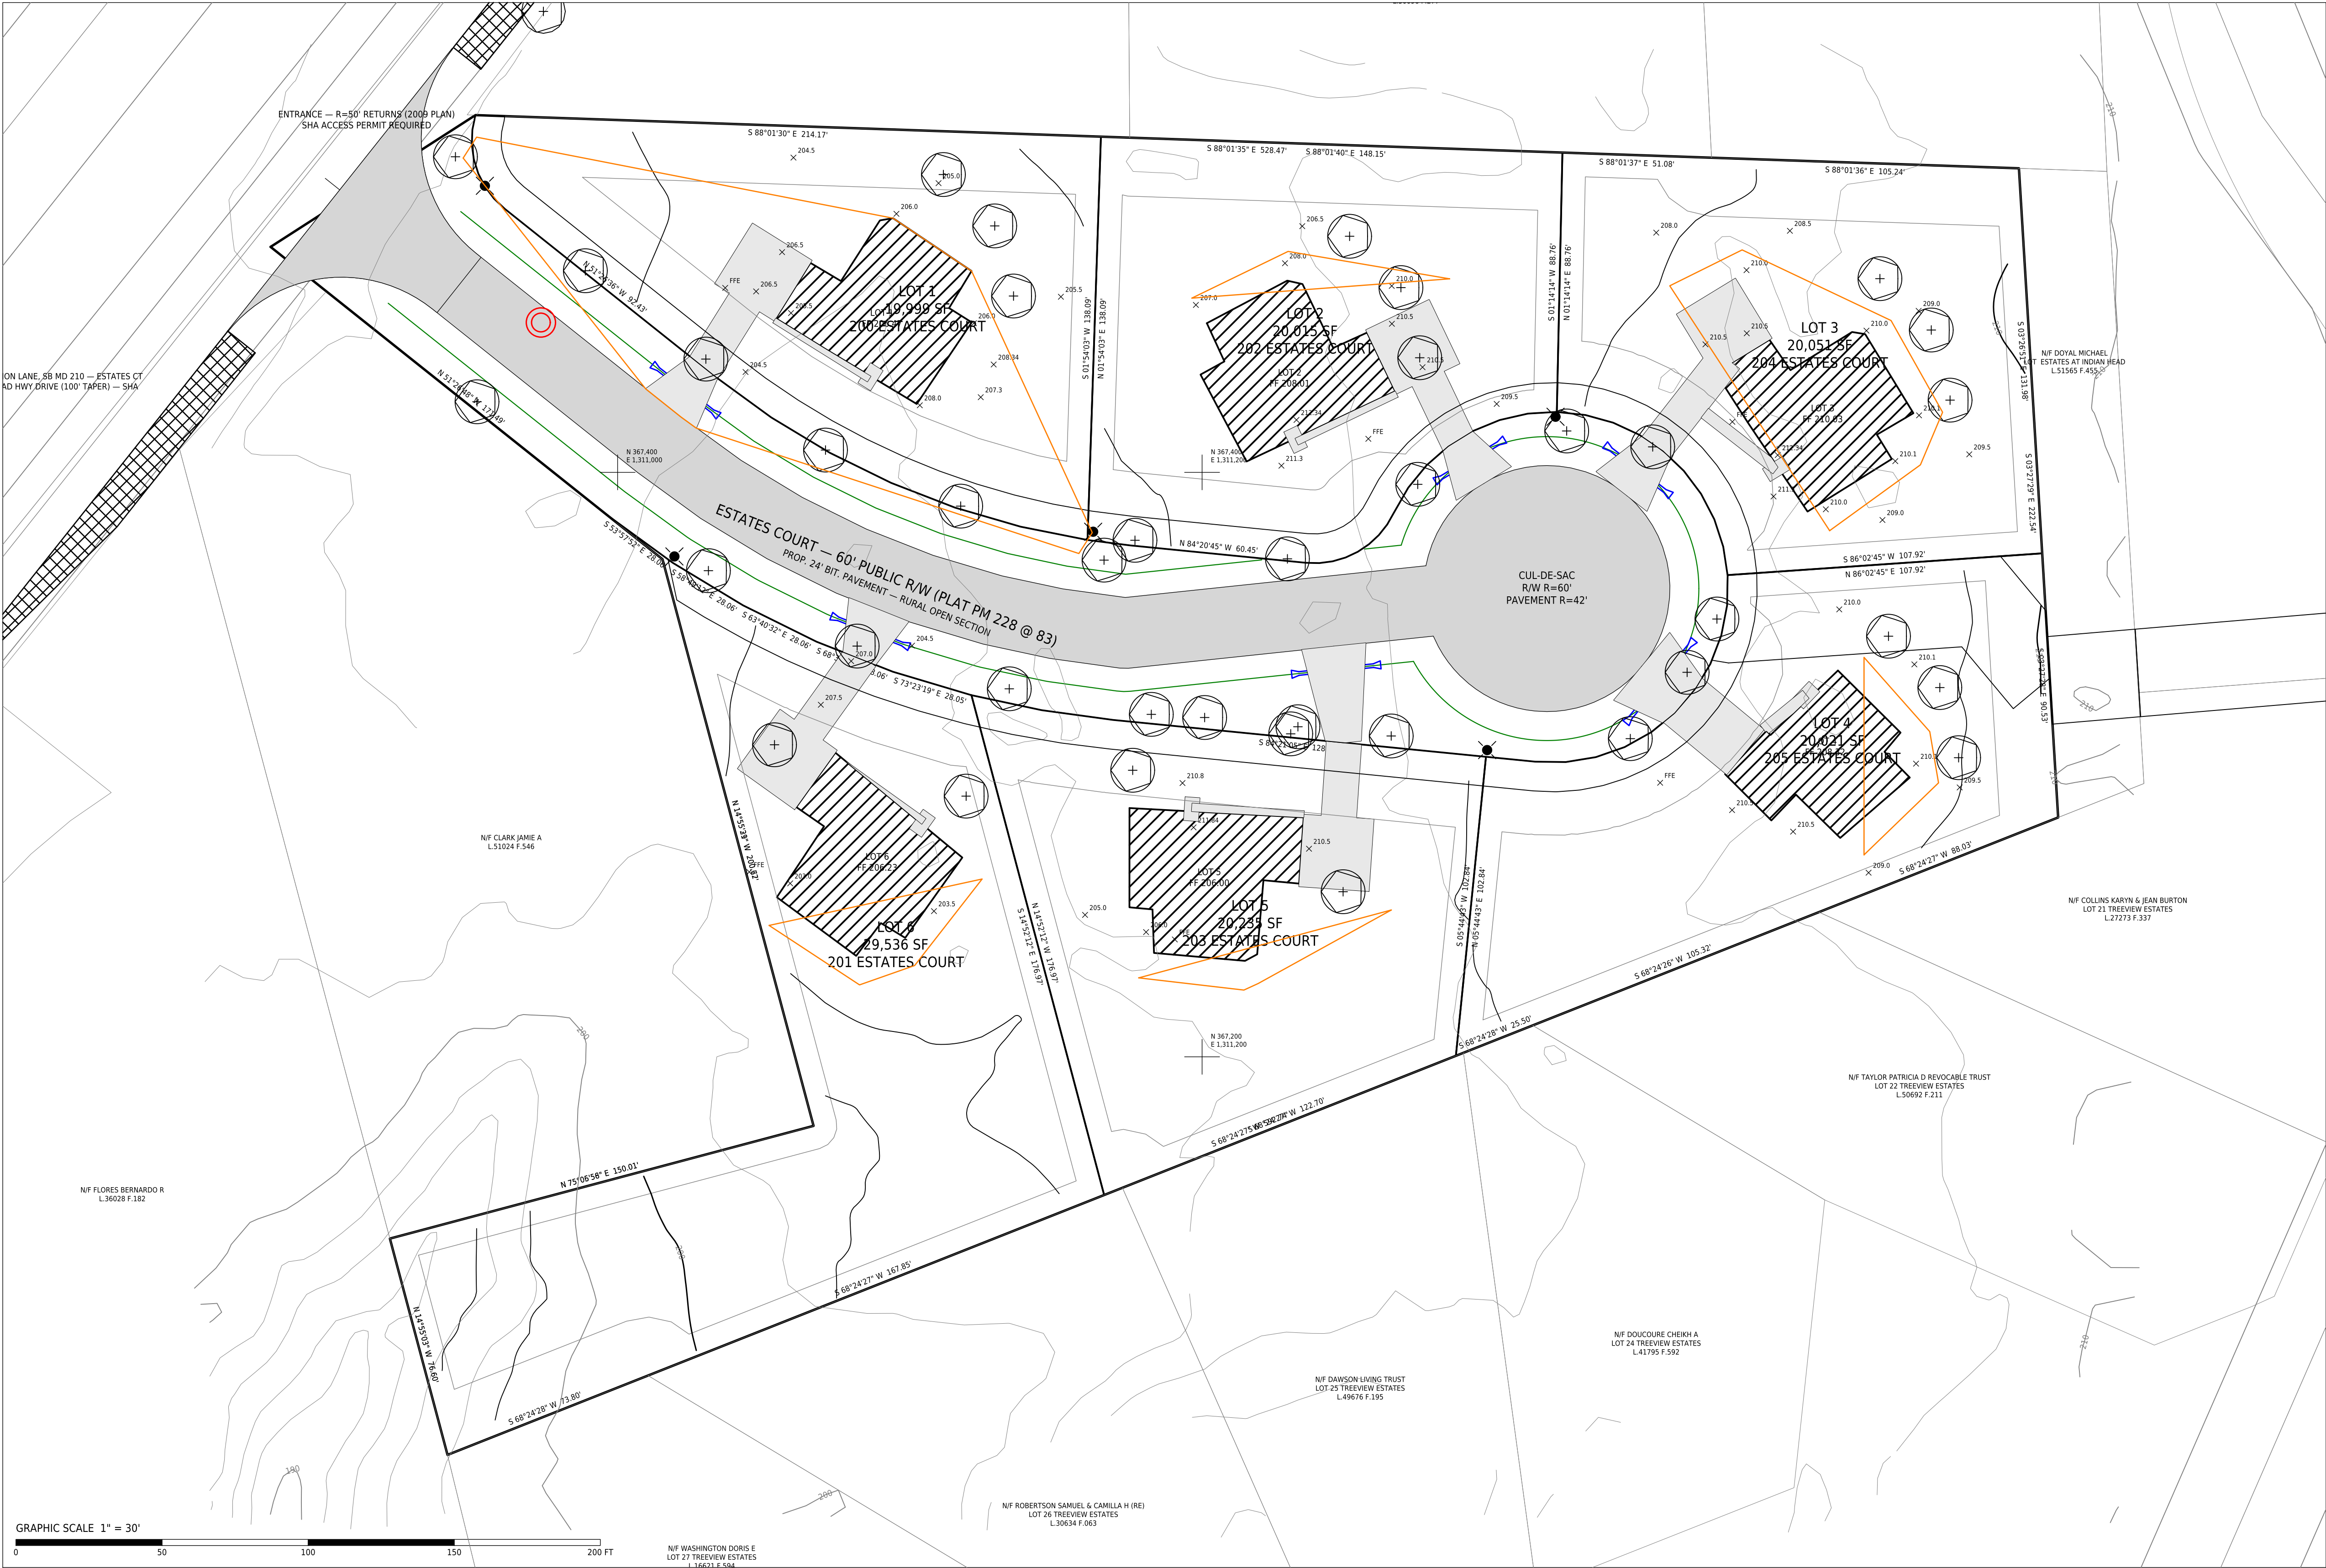

LEGEND

- Boundary of record
- Estates Ct right-of-way
- Proposed pavement
- Roadside swale (flowline)
- Driveway culvert, 15" RCP w/ end sections
- Proposed dwelling
- Building restriction line
- Proposed contour
- Existing contour
- Spot elevation (2009 plan, WSSC datum)
- Limit of disturbance
- MD 210 auxiliary lane (SHA)

BUILDING DATA

| LOT   | ADDRESS                | FOOTPRINT SF | GARAGE | FF (NAVD 88) | B (NAVD 88) |
|-------|------------------------|--------------|--------|--------------|-------------|
| LOT 1 | 200 ESTATES COURT 2349 |              |        | 206.47       | 197.47      |
| LOT 2 | 202 ESTATES COURT 2325 |              |        | 208.01       | 199.01      |
| LOT 3 | 204 ESTATES COURT 2313 |              |        | 210.03       | 201.03      |
| LOT 4 | 205 ESTATES COURT 1902 |              |        | 208.32       | 199.32      |
| LOT 5 | 203 ESTATES COURT 2408 |              |        | 206.00       | 197.00      |
| LOT 6 | 201 ESTATES COURT 2333 |              |        | 206.23       | 197.23      |

SITE, ROAD AND GRADING NOTES

- Boundary per recorded plat PM 228 @ 83; lot lines reproduce the plat to the second. A Maryland licensed surveyor shall confirm the boundary and the MD 210 R/W before technical plans.
- Horizontal datum: Maryland State Plane NAD 83 (US ft). Vertical datum: NAVD 88 (M-NCPPC 2-ft contours). 2009 spot grades are on WSSC datum ( $\approx$  NAVD 88 + 1.6 ft, to be confirmed by the field-run survey). DPJE prefers NGVD 29 — the survey shall state the conversion.
- The layout follows the approved 2009 Street Tree & Lighting Plan (DPW&T 9399-2009-00); dwellings, side-load garages and courts, street trees and street lights. Lot 4 is front-load (garage to the cul-de-sac) to clear the WSSC easement.
- Estates Court is a rural open section (DPW&T Std. 500.10 / 600.02 / 600.04); 24" pavement, shoulders, roadside swales; driveways cross the swale on 15" RCP culverts with flared end sections.
- Entrance to MD 210 (SHA) with 50' returns as the 2009 plan; SHA access permit and sight-distance analysis required. MD 210 auxiliary lanes shown for SHA review; R/W dedication may be required.
- MD 210 frontage improvements are shown for SHA review. At the entrance the MD 210 R/W line lies about 6 ft off the edge of road (2009 sheet), so a 12-ft lane needs R/W dedication along Lots 1 and 6 or SHA agreement. Lane lengths and tapers are set by SHA's access-permit review and traffic study.


PLAN TYPE  
SITE DEVELOPMENT CONCEPT PLAN

PROJECT  
ESTATES AT INDIAN HEAD — LOTS 1-6  
200-205 ESTATES COURT, ACCOKEEK, MD 20607  
PLAT BOOK PM 228 PLAT 83 - TAX MAP 151 F-3 - WSSC  
2205001  
ELECTION DIST. 5 - COUNCIL DIST. 9 - ZONE RR

OWNER / APPLICANT  
GERALD WALDMAN REVOCABLE TRUST, 400 N. FLAGLER DR., WEST  
PALM BEACH, FL 33401 (L 32062 F 043)

ENGINEER OF RECORD  
W.L. MECKINS, INC. — BILL MECKINS, JR., 3101 RITCHIE ROAD,  
FORESTVILLE, MD 20747-301-736-7115


SHEET TITLE  
SITE LAYOUT, GRADING AND PAVING PLAN

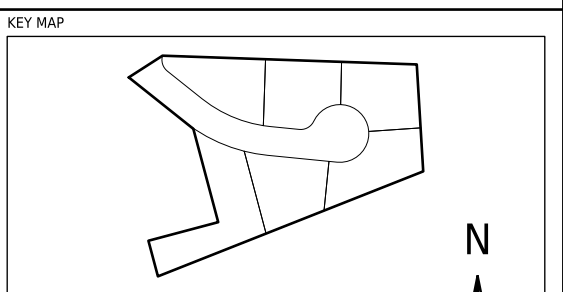

SCALE  
1" = 30'  
DATUM: NAD 83 MD STATE PLANE (US FT) / NAVD 88

| REVISIONS | NO. | DATE       | DESCRIPTION          |
|-----------|-----|------------|----------------------|
|           | 0   | 2026-09-30 | CONCEPT SUBMISSION 1 |


PROFESSIONAL CERTIFICATION  
I hereby certify that these documents were prepared or approved by me,  
and that I am a duly licensed professional engineer under the laws of  
the State of Maryland. License No. \_\_\_\_\_ Exp. \_\_\_\_\_

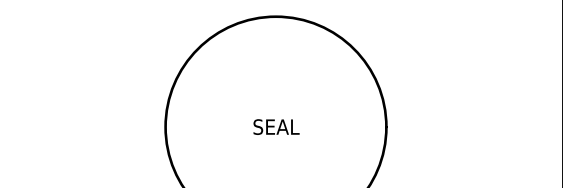

CONCEPT SUBMISSION 1 — NOT SEALED  
DATE 2026-09-30 - JOB KEA-EH-2026  
PREPARED WITH READER SPATIAL ENGINE / CAD-R-IT

SHEET INDEX  
C-000 COVER SHEET — BMP SUMMARY, DPJE CHECKLIST AND NOTES  
C-100 EXISTING CONDITIONS AND ENVIRONMENTAL FEATURES  
C-200 SITE LAYOUT, GRADING AND PAVING PLAN  
C-300 UTILITY, STREET LIGHT AND STREET TREE PLAN  
C-400 STORMWATER MANAGEMENT CONCEPT AND DRAINAGE AREA MAP  
C-500 SEDIMENT AND EROSION CONTROL PLAN  
C-600 DETAILS

UTILITY, STREET LIGHT AND STREET TREE PLAN

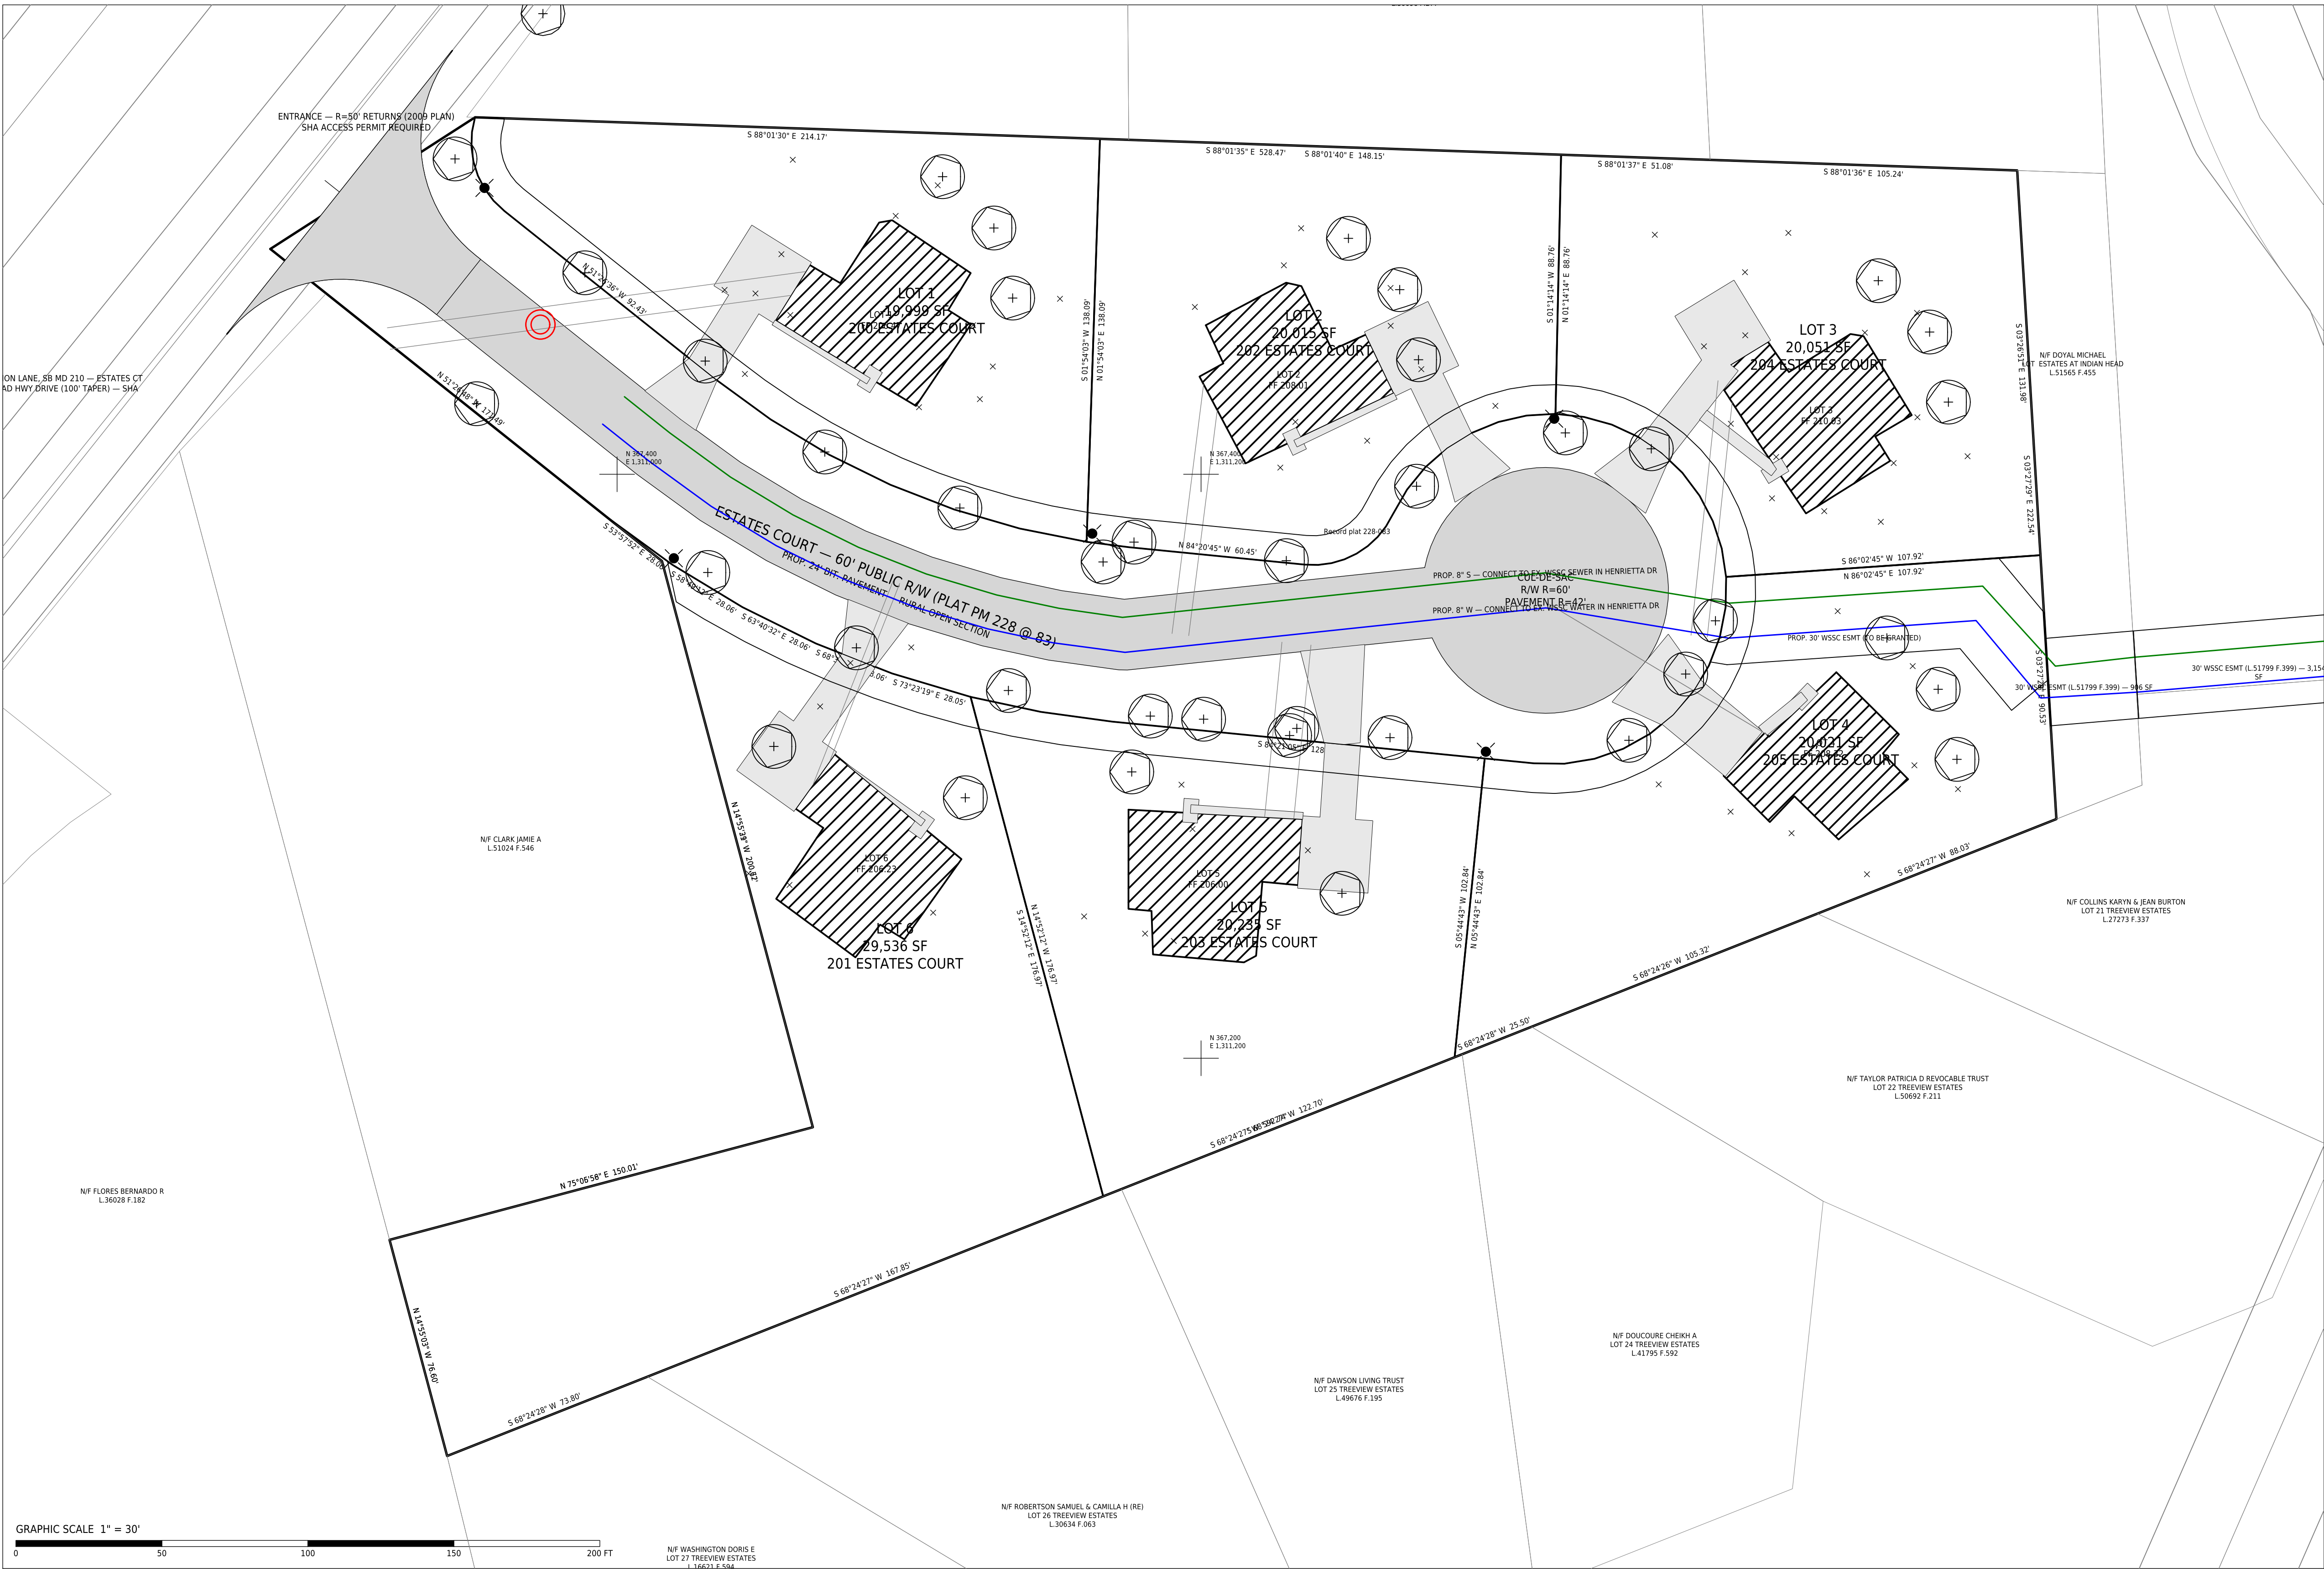

LEGEND

- Proposed 8" water main
- Proposed 8" sanitary sewer
- House connection
- WSSC easement (recorded / proposed)
- Street tree — Red Maple (2009 plan)
- Street light (2009 plan)

STREET TREE AND STREET LIGHT SCHEDULE (2009 PLAN)

| SYMBOL | QTY | ITEM                    | SIZE / TYPE                                            | STANDARD              |
|--------|-----|-------------------------|--------------------------------------------------------|-----------------------|
| TREE   | 16  | ACER RUBRUM — RED MAPLE | 1/2"-3" CAL., B&B                                      | DPW&T 600.02 / 600.04 |
| LIGHT  | 5   | STREET LIGHT (SMECO)    | 100 W MPS COLONIAL POST-TOP, TYPE IV, BLACK FIBERGLASS | DPW&T 500.10          |

UTILITY NOTES

- Water and sewer by WSSC (W-3 / S-3). Mains from the existing WSSC mains in Henrietta Drive through the recorded 30' WSSC easement (L51799 F.399, Outlot A and Lot 20) and a 30' WSSC easement to be granted across Lot 4 along the Lot 3/4 line.
- Sizes and inverts of the Henrietta Drive mains to be verified on WSSC 200' sheet 220501 before technical design.
- Street lights and street trees follow the approved 2009 Street Tree & Lighting Plan (DPW&T 9399-2009; light permit 09.09399); electric service by SMECO.
- Keep street trees 10 ft from water meters and storm structures and 15 ft from street lights (DPW&T 600.02).
- Contact Miss Utility (811) at least 48 hours before excavation.

PLAN TYPE  
SITE DEVELOPMENT CONCEPT PLAN


PROJECT  
ESTATES AT INDIAN HEAD — LOTS 1-6  
200-205 ESTATES COURT, ACCOKEEK, MD 20607  
PLAT BOOK PM 228 PLAT 83 - TAX MAP 151 F-3 - WSSC  
220501  
ELECTION DIST. 5 - COUNCIL DIST. 9 - ZONE RR

OWNER / APPLICANT  
GERALD WALDMAN REVOCABLE TRUST, 400 N. FLAGLER DR., WEST  
PALM BEACH, FL 33401 (L 32062 F.043)

ENGINEER OF RECORD  
W.L. MEEKINS, INC. — BILL MEEKINS, JR., 3101 RITCHIE ROAD,  
FORESTVILLE, MD 20747-301-736-7115

SHEET TITLE  
UTILITY, STREET LIGHT AND STREET TREE  
PLAN


KEY MAP

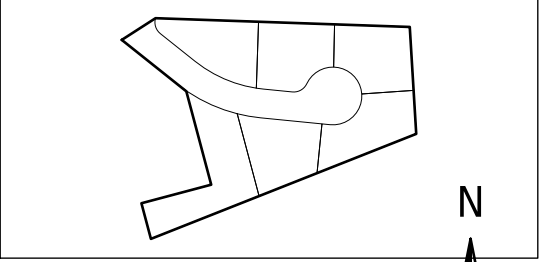

SCALE  
1" = 30'  
DATUM: NAD 83 MD STATE PLANE (US FT) / NAVD 88

| REVISIONS | NO.        | DATE                 | DESCRIPTION |
|-----------|------------|----------------------|-------------|
| 1         | 2026-09-30 | CONCEPT SUBMISSION 1 |             |

PROFESSIONAL CERTIFICATION  
I hereby certify that these documents were prepared or approved by me,  
and that I am a duly licensed professional engineer under the laws of  
the State of Maryland, License No. \_\_\_\_\_, Exp. \_\_\_\_\_

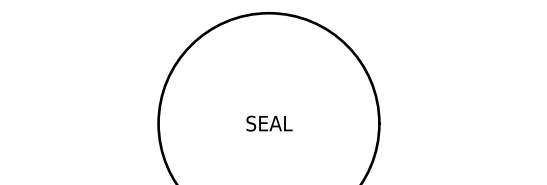

CONCEPT SUBMISSION 1 — NOT SEALED

DATE: 2026-09-30 - JOB: KEA-EIH-2026


PREPARED WITH: SCALE: 1/4" = 1' - 1/4" = 1' - 1/4" = 1'

SHEET INDEX

- C-000 COVER SHEET — BMP SUMMARY, DRIE CHECKLIST AND NOTES
- C-100 EXISTING CONDITIONS AND ENVIRONMENTAL FEATURES
- C-200 SITE LAYOUT, GRADING AND PAVING PLAN
- C-300 UTILITY, STREET LIGHT AND STREET TREE PLAN
- C-400 STORMWATER MANAGEMENT CONCEPT AND DRAINAGE AREA MAP
- C-500 SEDIMENT AND EROSION CONTROL PLAN
- C-600 DETAILS

RESERVED FOR PRINCE GEORGE'S COUNTY DRIE APPROVAL BLOCK  
(5-IN FULL-HEIGHT AREA KEPT OPEN — CHECKLIST A.3)

STORMWATER MANAGEMENT CONCEPT AND DRAINAGE AREA MAP

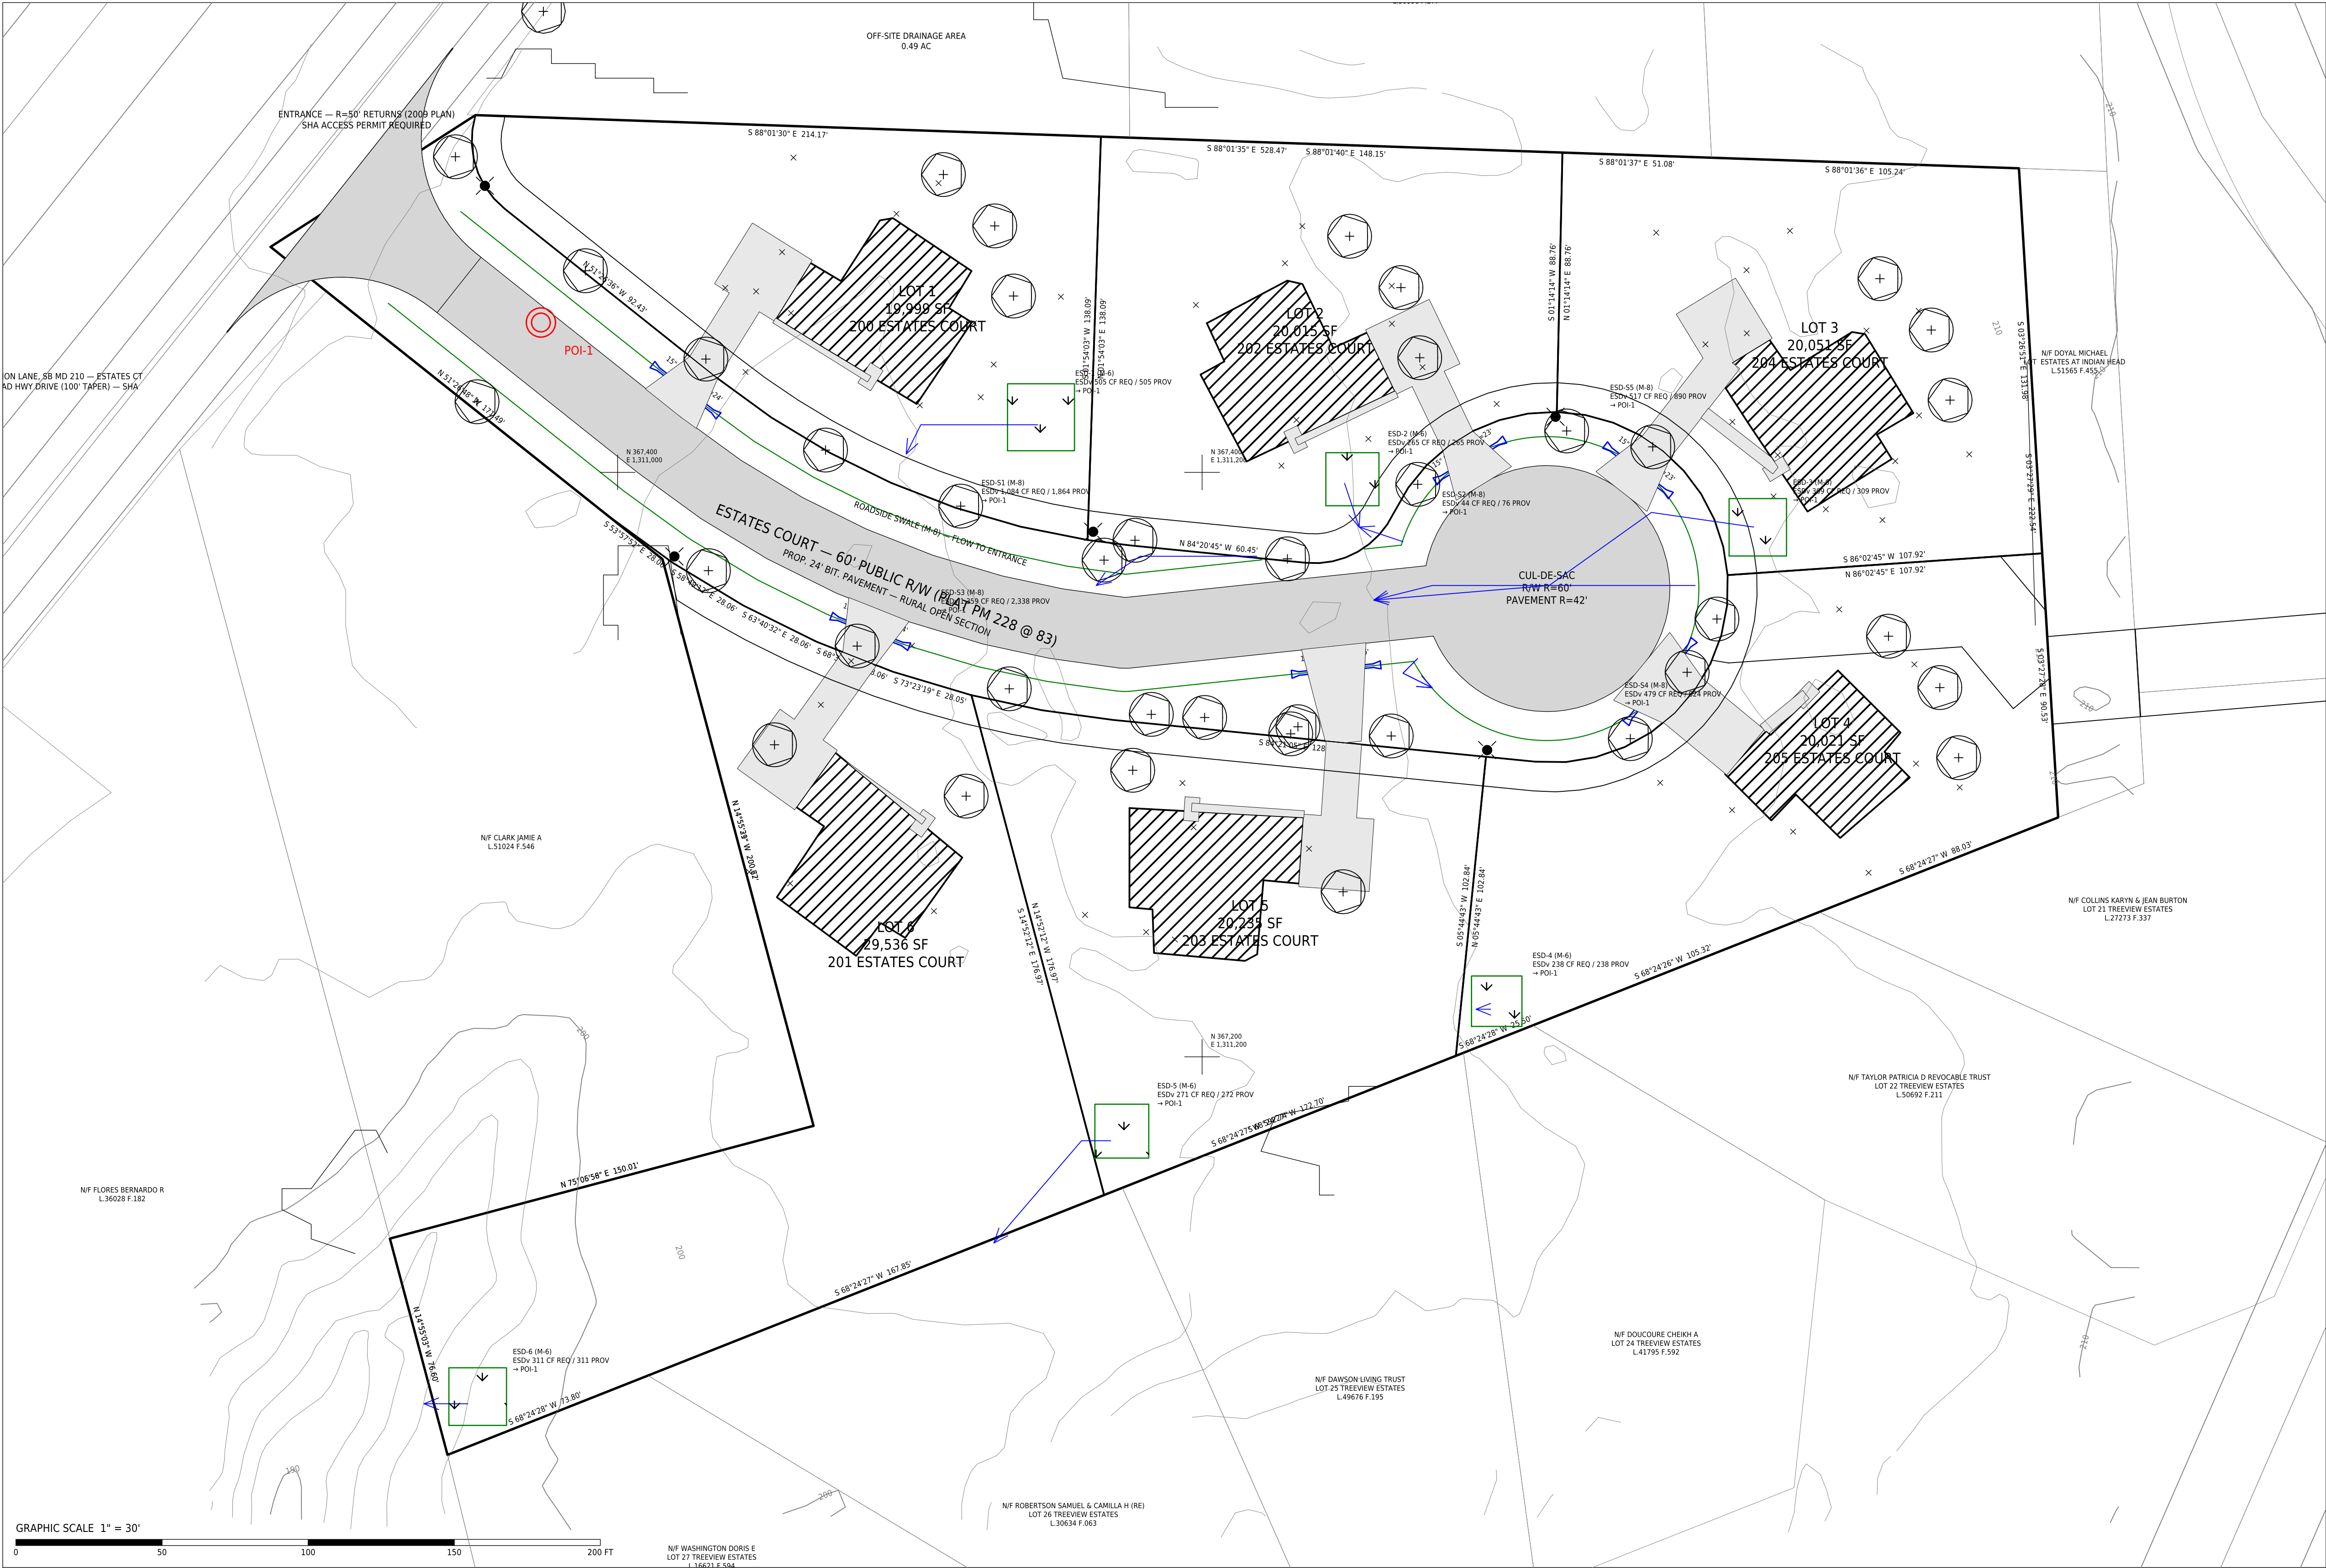

- LEGEND**
- ESD practice — micro-bioretenion (M-6)
  - Roadside dry swale (M-8)
  - Drainage area to practice
  - Off-site area draining onto site
  - 100-yr overflow path
  - Point of investigation
  - Driveway culvert

| ESD PER PRACTICE (FULL TABLE ON C-000) |     |                          |       |        |      |     |          |           |  |
|----------------------------------------|-----|--------------------------|-------|--------|------|-----|----------|-----------|--|
| BMP                                    | MDE | LOCATION                 | POI   | DA SF  | %    | P.E | ESDv REQ | ESDv PROV |  |
| ESD-1                                  | M-6 | Lot 1                    | POI-1 | 19,999 | 22.5 | 1.2 | 505      | 505       |  |
| ESD-2                                  | M-6 | Lot 2                    | POI-1 | 20,015 | 12.1 | 1.0 | 265      | 265       |  |
| ESD-3                                  | M-6 | Lot 3                    | POI-1 | 20,051 | 15.0 | 1.0 | 309      | 309       |  |
| ESD-4                                  | M-6 | Lot 4                    | POI-1 | 20,021 | 10.3 | 1.0 | 238      | 238       |  |
| ESD-5                                  | M-6 | Lot 5                    | POI-1 | 20,235 | 12.3 | 1.0 | 271      | 272       |  |
| ESD-6                                  | M-6 | Lot 6                    | POI-1 | 29,536 | 8.5  | 1.0 | 311      | 311       |  |
| ESD-1                                  | M-8 | Estates CL/R/W, roadside | POI-1 | 11,212 | 58.9 | 2.0 | 1,084    | 1,864     |  |
| ESD-2                                  | M-8 | Estates CL/R/W, roadside | POI-1 | 457    | 58.9 | 2.0 | 44       | 76        |  |
| ESD-3                                  | M-8 | Estates CL/R/W, roadside | POI-1 | 14,063 | 58.9 | 2.0 | 1,359    | 2,338     |  |
| ESD-4                                  | M-8 | Estates CL/R/W, roadside | POI-1 | 4,957  | 58.9 | 2.0 | 479      | 824       |  |
| ESD-5                                  | M-8 | Estates CL/R/W, roadside | POI-1 | 5,352  | 58.9 | 2.0 | 517      | 890       |  |

| POINTS OF INVESTIGATION (C-9) |                       |       |                      |
|-------------------------------|-----------------------|-------|----------------------|
| POI                           | LOCATION              | SHARE | ESDv REQ / ESDv PROV |
| POI-1                         | N 367,451 E 1,310,974 | 100%  | 5,382 / 7,892        |

- SWM NOTES**
- SWM by Environmental Site Design to the MEP (Md. Stormwater Management Act of 2007; MDE Design Manual Ch. 5; PGC Subtitle 32). Target rainfall P.E from MDE Table 5.3 for HSG C at each drainage area's imperviousness.
  - Each lot drains to one micro-bioretenion cell (M-6). 12-in max. ponding, 2.5-ft filter media, underdrain to a stable outfall. Estates Court drains to roadside dry swales (M-8) with check dams.
  - Rooftop and non-rooftop disconnection (M-1, M-2) to be credited at technical design. Infiltration credit only where Sec. 32.1.3.3 berms show a 0.52 in/yr.
  - Private ESD practices: maintenance agreement recorded before permit; public swales in the R/W maintained by DPPE.
  - D8 flow routing on a 5-ft surface interpolated from the existing 2-ft contours; ext. points clustered at 120 ft; POIs carrying under 4% of the site omitted. Concept-level — reset from the field-run survey.

PLAN TYPE  
SITE DEVELOPMENT CONCEPT PLAN


PROJECT  
ESTATES AT INDIAN HEAD — LOTS 1-6  
200-205 ESTATES COURT, ACCOKEEK, MD 20607  
PLAT BOOK PM 228 PLAT 83 — TAX MAP 151 F-3 — WSSC  
220501  
ELECTION DIST. 5 — COUNCIL DIST. 9 — ZONE RR

OWNER / APPLICANT  
GERALD WALDMAN REVOCABLE TRUST, 400 N. FLAGLER DR., WEST  
PALM BEACH, FL 33401 (L 32062 F.043)

ENGINEER OF RECORD  
W.L. MECKINS, INC. — BILL MECKINS, JR., 3101 RITCHIE ROAD,  
FORESTVILLE, MD 20747-301-738-7115

SHEET TITLE  
STORMWATER MANAGEMENT CONCEPT AND  
DRAINAGE AREA MAP

KEY MAP

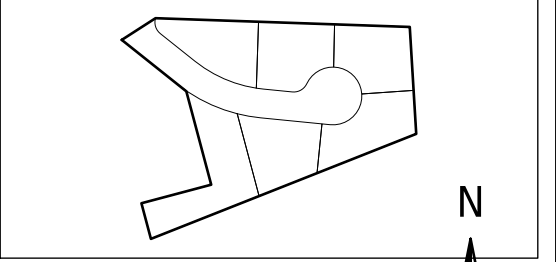


SCALE  
1" = 30'

DATUM: NAD 83 MD STATE PLANE (US FT) / NAVD 88

| REVISIONS | NO.        | DATE                 | DESCRIPTION |
|-----------|------------|----------------------|-------------|
| 1         | 2026-09-30 | CONCEPT SUBMISSION 1 |             |

PROFESSIONAL CERTIFICATION  
I hereby certify that these documents were prepared or approved by me,  
and that I am a duly licensed professional engineer under the laws of  
the State of Maryland, License No. \_\_\_\_\_, Exp. \_\_\_\_\_

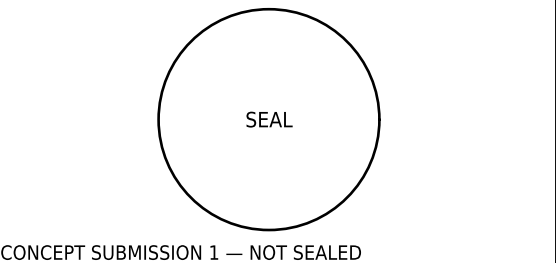

CONCEPT SUBMISSION 1 — NOT SEALED

DATE: 2026-09-30 — JOB: KEA-EIH-2026  
PREPARED WITH: SCALE: 1"=30', ENGINE: C-400-PL01

SHEET INDEX

- C-000 COVER SHEET — BMP SUMMARY, DPE CHECKLIST AND NOTES
- C-100 EXISTING CONDITIONS AND ENVIRONMENTAL FEATURES
- C-200 SITE LAYOUT, GRADING AND PAVING PLAN
- C-300 UTILITY, STREET LIGHT AND STREET TREE PLAN
- C-400 STORMWATER MANAGEMENT CONCEPT AND DRAINAGE AREA MAP
- C-500 SEDIMENT AND EROSION CONTROL PLAN
- C-600 DETAILS

SEDIMENT AND EROSION CONTROL PLAN



- LEGEND**
- Limit of disturbance
  - Super silt fence
  - Stabilized construction entrance
  - Proposed contour
  - Existing contour

- SEDIMENT AND EROSION CONTROL NOTES**
- Sediment and erosion control per the 2011 Maryland Standards and Specifications for Soil Erosion and Sediment Control and PGSCD requirements.
  - Stabilized construction entrance at the Estates Court entrance; super silt fence along the down-gradient limit of disturbance; inlet and swale protection.
  - Stabilize disturbed areas within 3 days on slopes  $\geq 3:1$  and within 7 days elsewhere.

- SEQUENCE OF CONSTRUCTION**
- Pre-construction meeting with the PGSCD / DPE inspector; Miss Utility.
  - Install stabilized construction entrance and perimeter controls; inspector approval.
  - Clear and grub within the LID; rough grade Estates Court and swales.
  - Install water and sewer (Henrietta Dr to Estates Ct) and house connections.
  - Construct pavement, shoulders, culverts and entrance; stabilize swales.
  - Build dwellings, driveways and courts; construct ESD practices after the contributing area is stable.
  - Fine grade, permanent stabilization, street trees and lights; remove controls with inspector approval.

PLAN TYPE  
**SITE DEVELOPMENT CONCEPT PLAN**

PROJECT  
ESTATES AT INDIAN HEAD — LOTS 1-6  
200-205 ESTATES COURT, ACCOKEEK, MD 20607  
PLAT BOOK PM 228 PLAT 83 - TAX MAP 151 F-3 - WSSC  
220501  
ELECTION DIST. 5 - COUNCIL DIST. 9 - ZONE RR

OWNER / APPLICANT  
GERALD WALDMAN REVOCABLE TRUST, 400 N. FLAGLER DR., WEST  
PALM BEACH, FL 33401 (L 32062 F 043)

ENGINEER OF RECORD  
W.L. MECKINS, INC. — BILL MECKINS, JR., 3101 RITCHIE ROAD,  
FORESTVILLE, MD 20747-301-738-7115

SHEET TITLE  
**SEDIMENT AND EROSION CONTROL PLAN**

KEY MAP

SCALE  
**1" = 30'**  
DATUM: NAD 83 MD STATE PLANE (US FT) / NAVD 88

REVISIONS

| NO. | DATE       | DESCRIPTION          |
|-----|------------|----------------------|
| 0   | 2026-09-30 | CONCEPT SUBMISSION 1 |

PROFESSIONAL CERTIFICATION  
I hereby certify that these documents were prepared or approved by me,  
and that I am a duly licensed professional engineer under the laws of  
the State of Maryland. License No. \_\_\_\_\_ Exp. \_\_\_\_\_

SEAL




CONCEPT SUBMISSION 1 — NOT SEALED  
DATE 2026-09-30 - JOB KEA-EH-2026  
PREPARED WITH READER SPATIAL PLOTTING / CAD-PILOT

SHEET INDEX

- C-000 COVER SHEET — BMP SUMMARY, DPE CHECKLIST AND NOTES
- C-100 EXISTING CONDITIONS AND ENVIRONMENTAL FEATURES
- C-200 SITE LAYOUT, GRADING AND PAVING PLAN
- C-300 UTILITY, STREET LIGHT AND STREET TREE PLAN
- C-400 STORMWATER MANAGEMENT CONCEPT AND DRAINAGE AREA MAP
- C-500 SEDIMENT AND EROSION CONTROL PLAN
- C-600 DETAILS

RESERVED FOR PRINCE GEORGE'S COUNTY DPE APPROVAL BLOCK  
(5-IN FULL-HEIGHT AREA KEPT OPEN — CHECKLIST A-3)

DETAILS

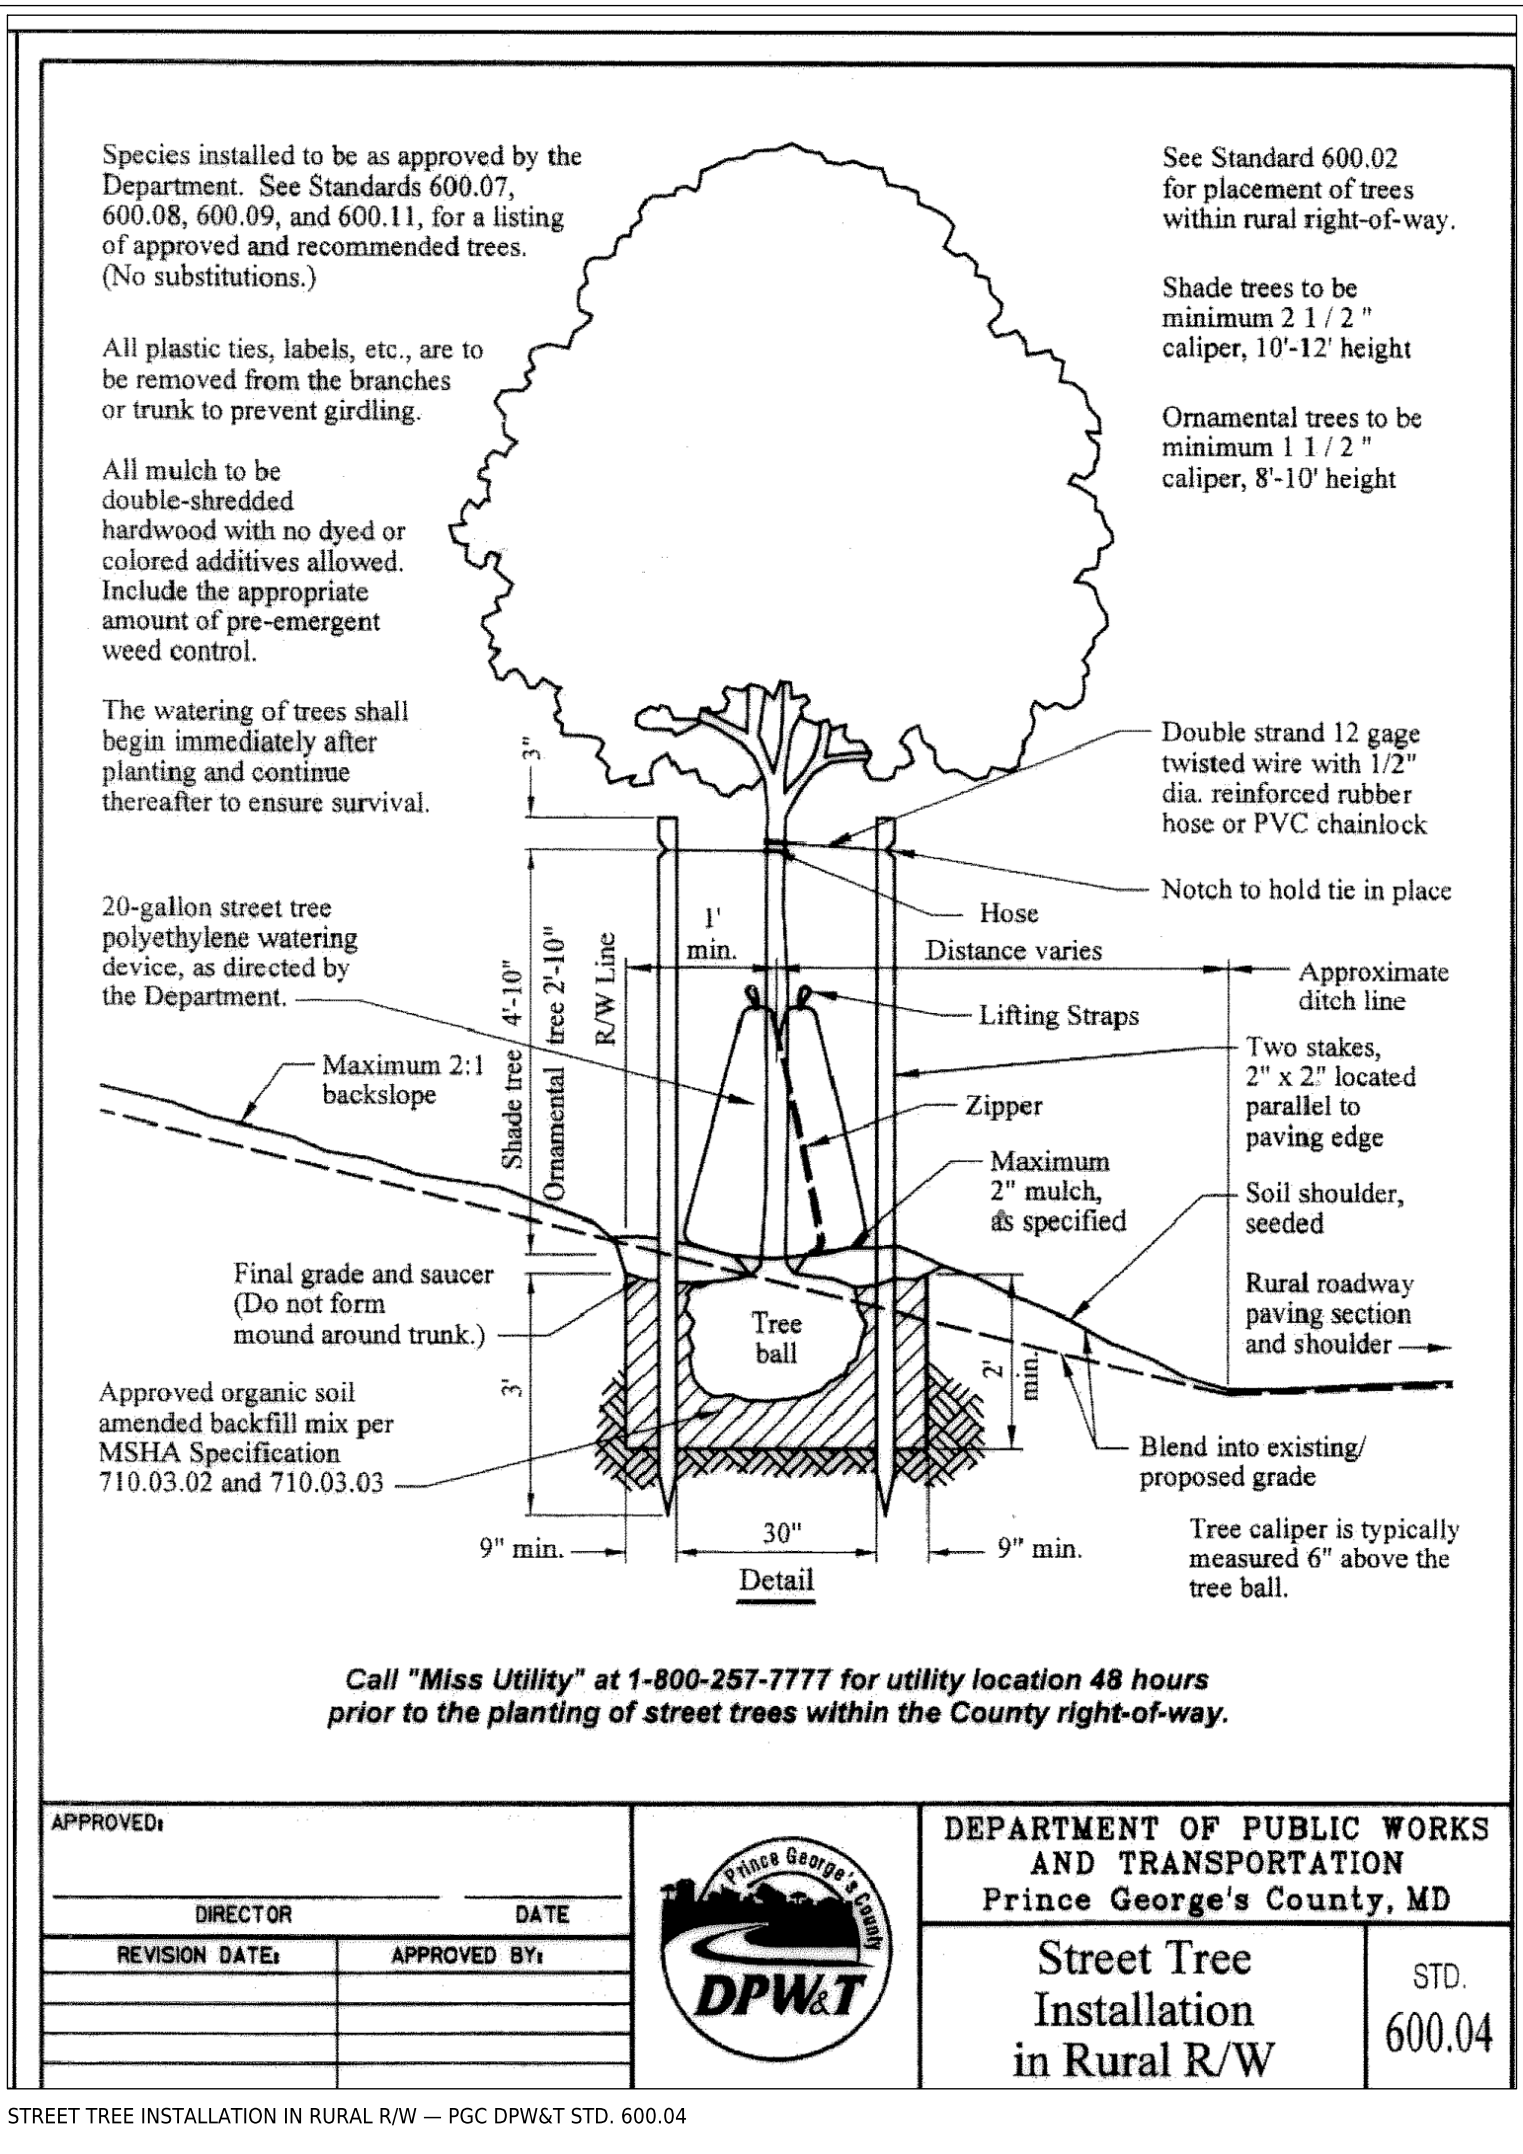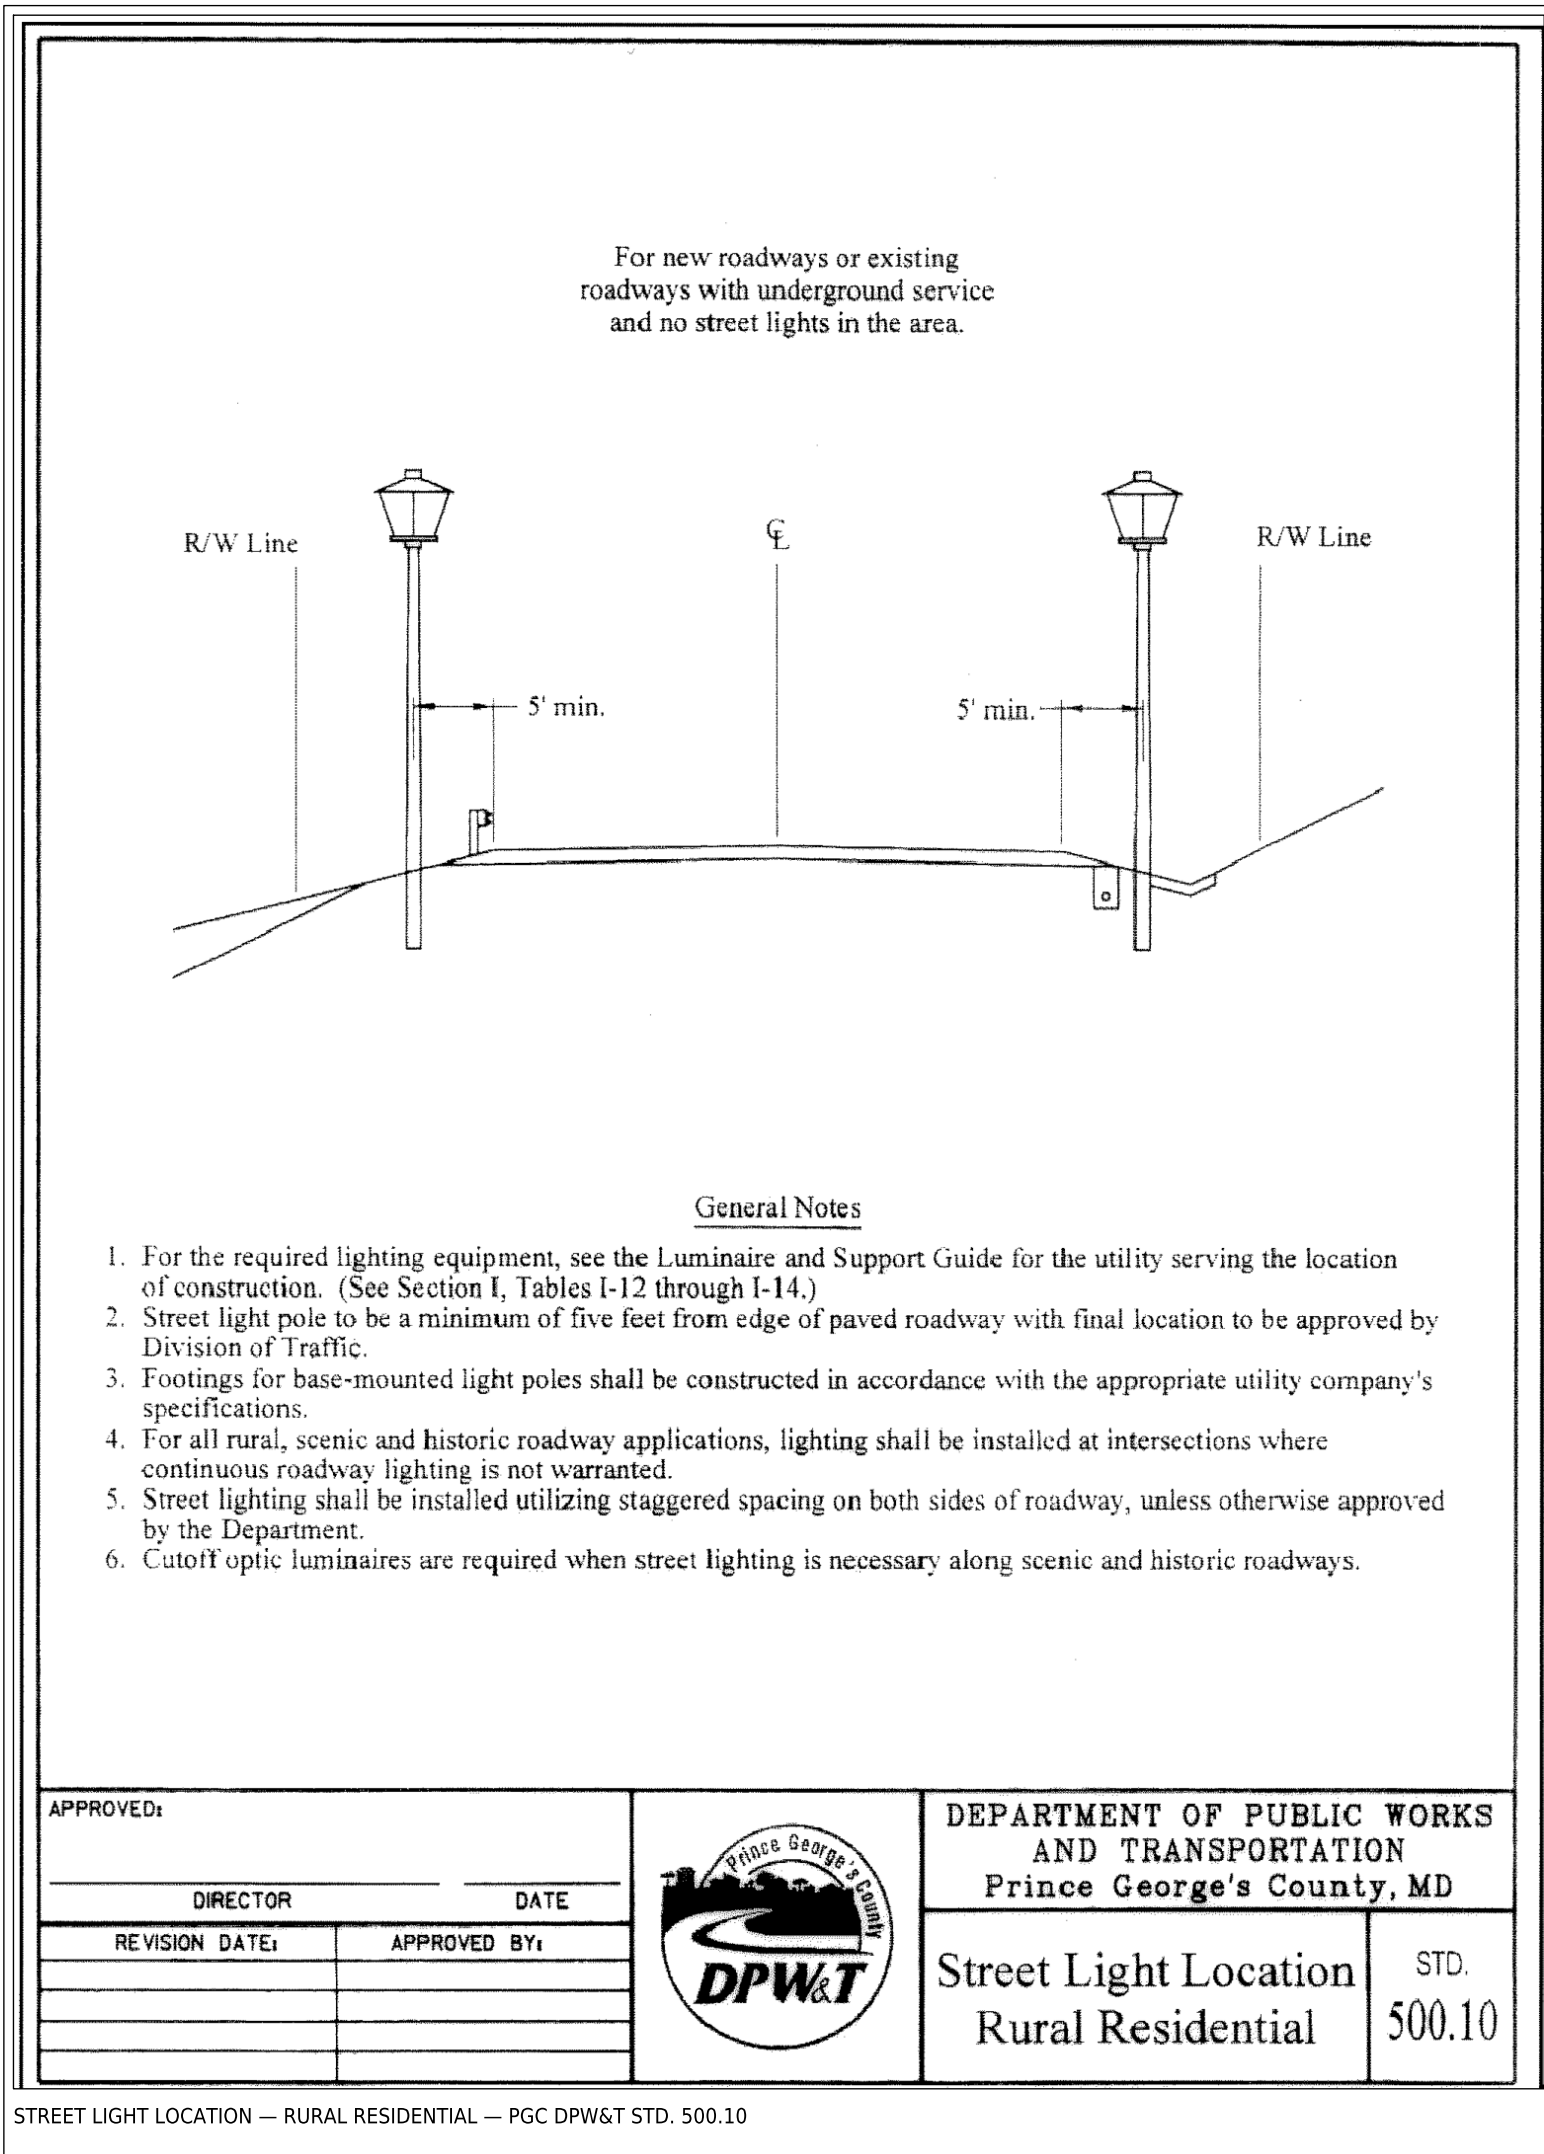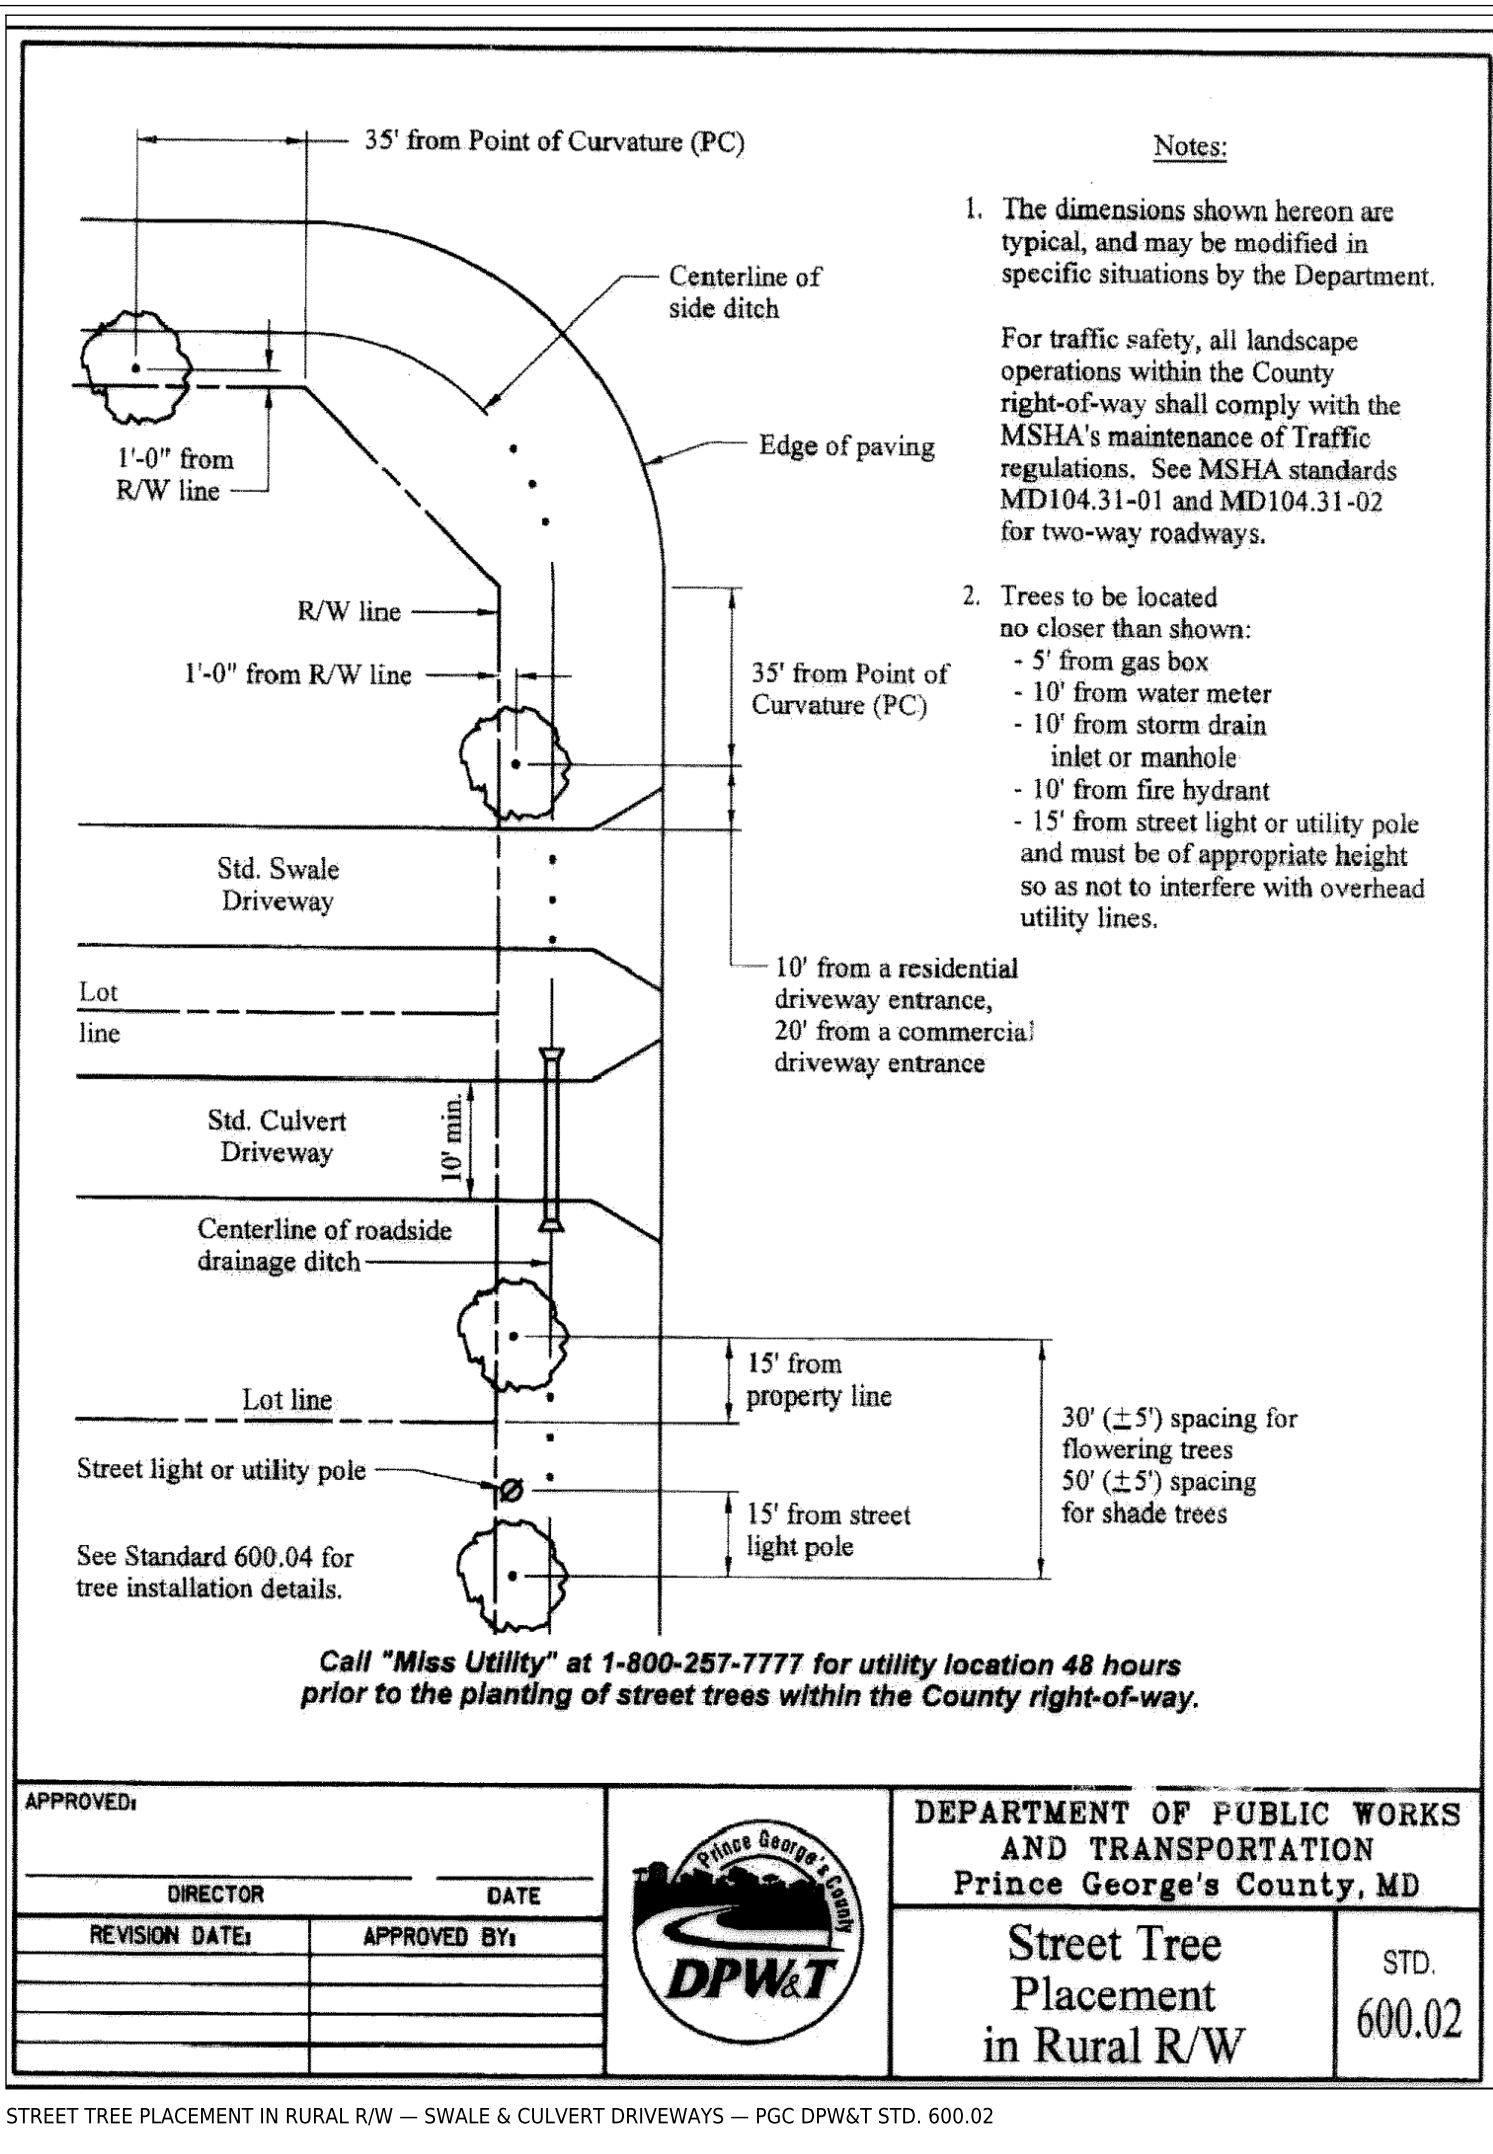

PLAN TYPE  
**SITE DEVELOPMENT CONCEPT PLAN**

PROJECT  
ESTATES AT INDIAN HEAD — LOTS 1-6  
200-205 ESTATES COURT, ACCOKEEK, MD 20607  
PLAT BOOK PW 228 PLAT 83 - TAX MAP 151 F-3 - WSSC  
220501  
ELECTION DIST. 5 - COUNCIL DIST. 9 - ZONE RR

OWNER / APPLICANT  
GERALD WALDMAN REVOCABLE TRUST, 400 N. FLAGLER DR., WEST PALM BEACH, FL 33401 (L 32062 F 043)

ENGINEER OF RECORD  
W.L. MEEKINS, INC. — BILL MEEKINS, JR., 3101 RITCHIE ROAD, FORESTVILLE, MD 20747 - 301-736-7115

SHEET TITLE  
**DETAILS**

KEY MAP

SCALE  
**AS NOTED**  
DATUM: NAD 83 MD STATE PLANE (US FT) / NAVD 88

REVISIONS

| NO. | DATE       | DESCRIPTION          |
|-----|------------|----------------------|
| 0   | 2026-09-30 | CONCEPT SUBMISSION 1 |

PROFESSIONAL CERTIFICATION  
I hereby certify that these documents were prepared or approved by me, and that I am a duly licensed professional engineer under the laws of the State of Maryland. License No. \_\_\_\_\_ Exp. \_\_\_\_\_


SEAL

CONCEPT SUBMISSION 1 — NOT SEALED  
DATE 2026-09-30 - JOB KEA-EH-2026  
PREPARED WITH READER SPATIAL PLOTTING / CAD/PLOT

SHEET INDEX  
C-600 COVER SHEET — BMP SUMMARY, DPE CHECKLIST AND NOTES  
C-601 EXISTING CONDITIONS AND ENVIRONMENTAL FEATURES  
C-602 SITE LAYOUT, GRADING AND PAVING PLAN  
C-603 UTILITY, STREET LIGHT AND STREET TREE PLAN  
C-604 STORMWATER MANAGEMENT CONCEPT AND DRAINAGE AREA MAP  
C-605 SEDIMENT AND EROSION CONTROL PLAN  
• C-600 DETAILS


RESERVED FOR PRINCE GEORGE'S COUNTY DPE APPROVAL BLOCK  
(5-IN FULL-HEIGHT AREA KEPT OPEN — CHECKLIST A-3)

ESTATES COURT — TYPICAL SECTION (RURAL OPEN SECTION, 60' R/W)

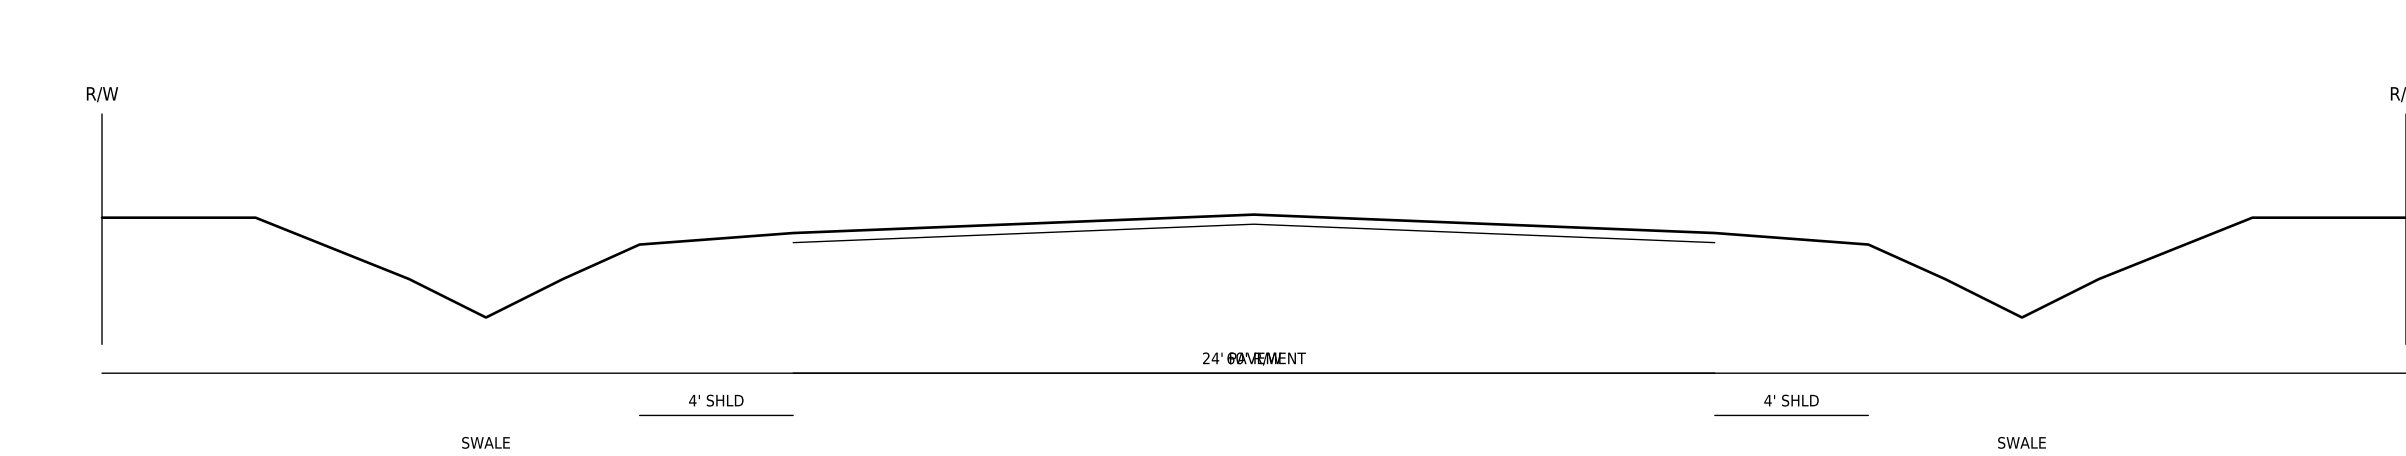

1 1/2" SURFACE + 2 1/2" BASE BIT, CONC. ON 6" GAB (DPW&T PAVEMENT SCHEDULE FOR RURAL RESIDENTIAL — CONFIRM)  
CROSS SLOPE 2%; 4-FT STABILIZED SHOULDERS; SWALE FLOWLINE 20 FT OFF CENTRELINE, 3:1 SIDE SLOPES  
DRIVEWAYS CROSS THE SWALE ON 15" RCP CULVERTS WITH FLARED END SECTIONS (DPW&T STD. 600.02)

MICRO-BIORETENTION (M-6) — TYPICAL SECTION

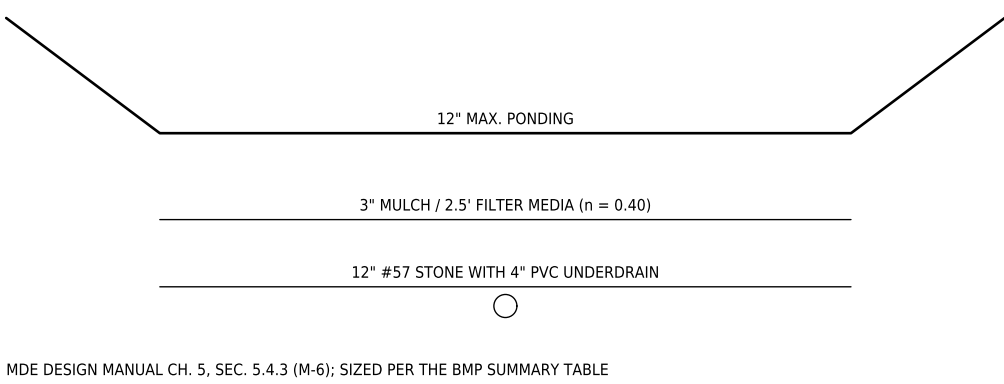

DRY SWALE (M-8) WITH CHECK DAM

