


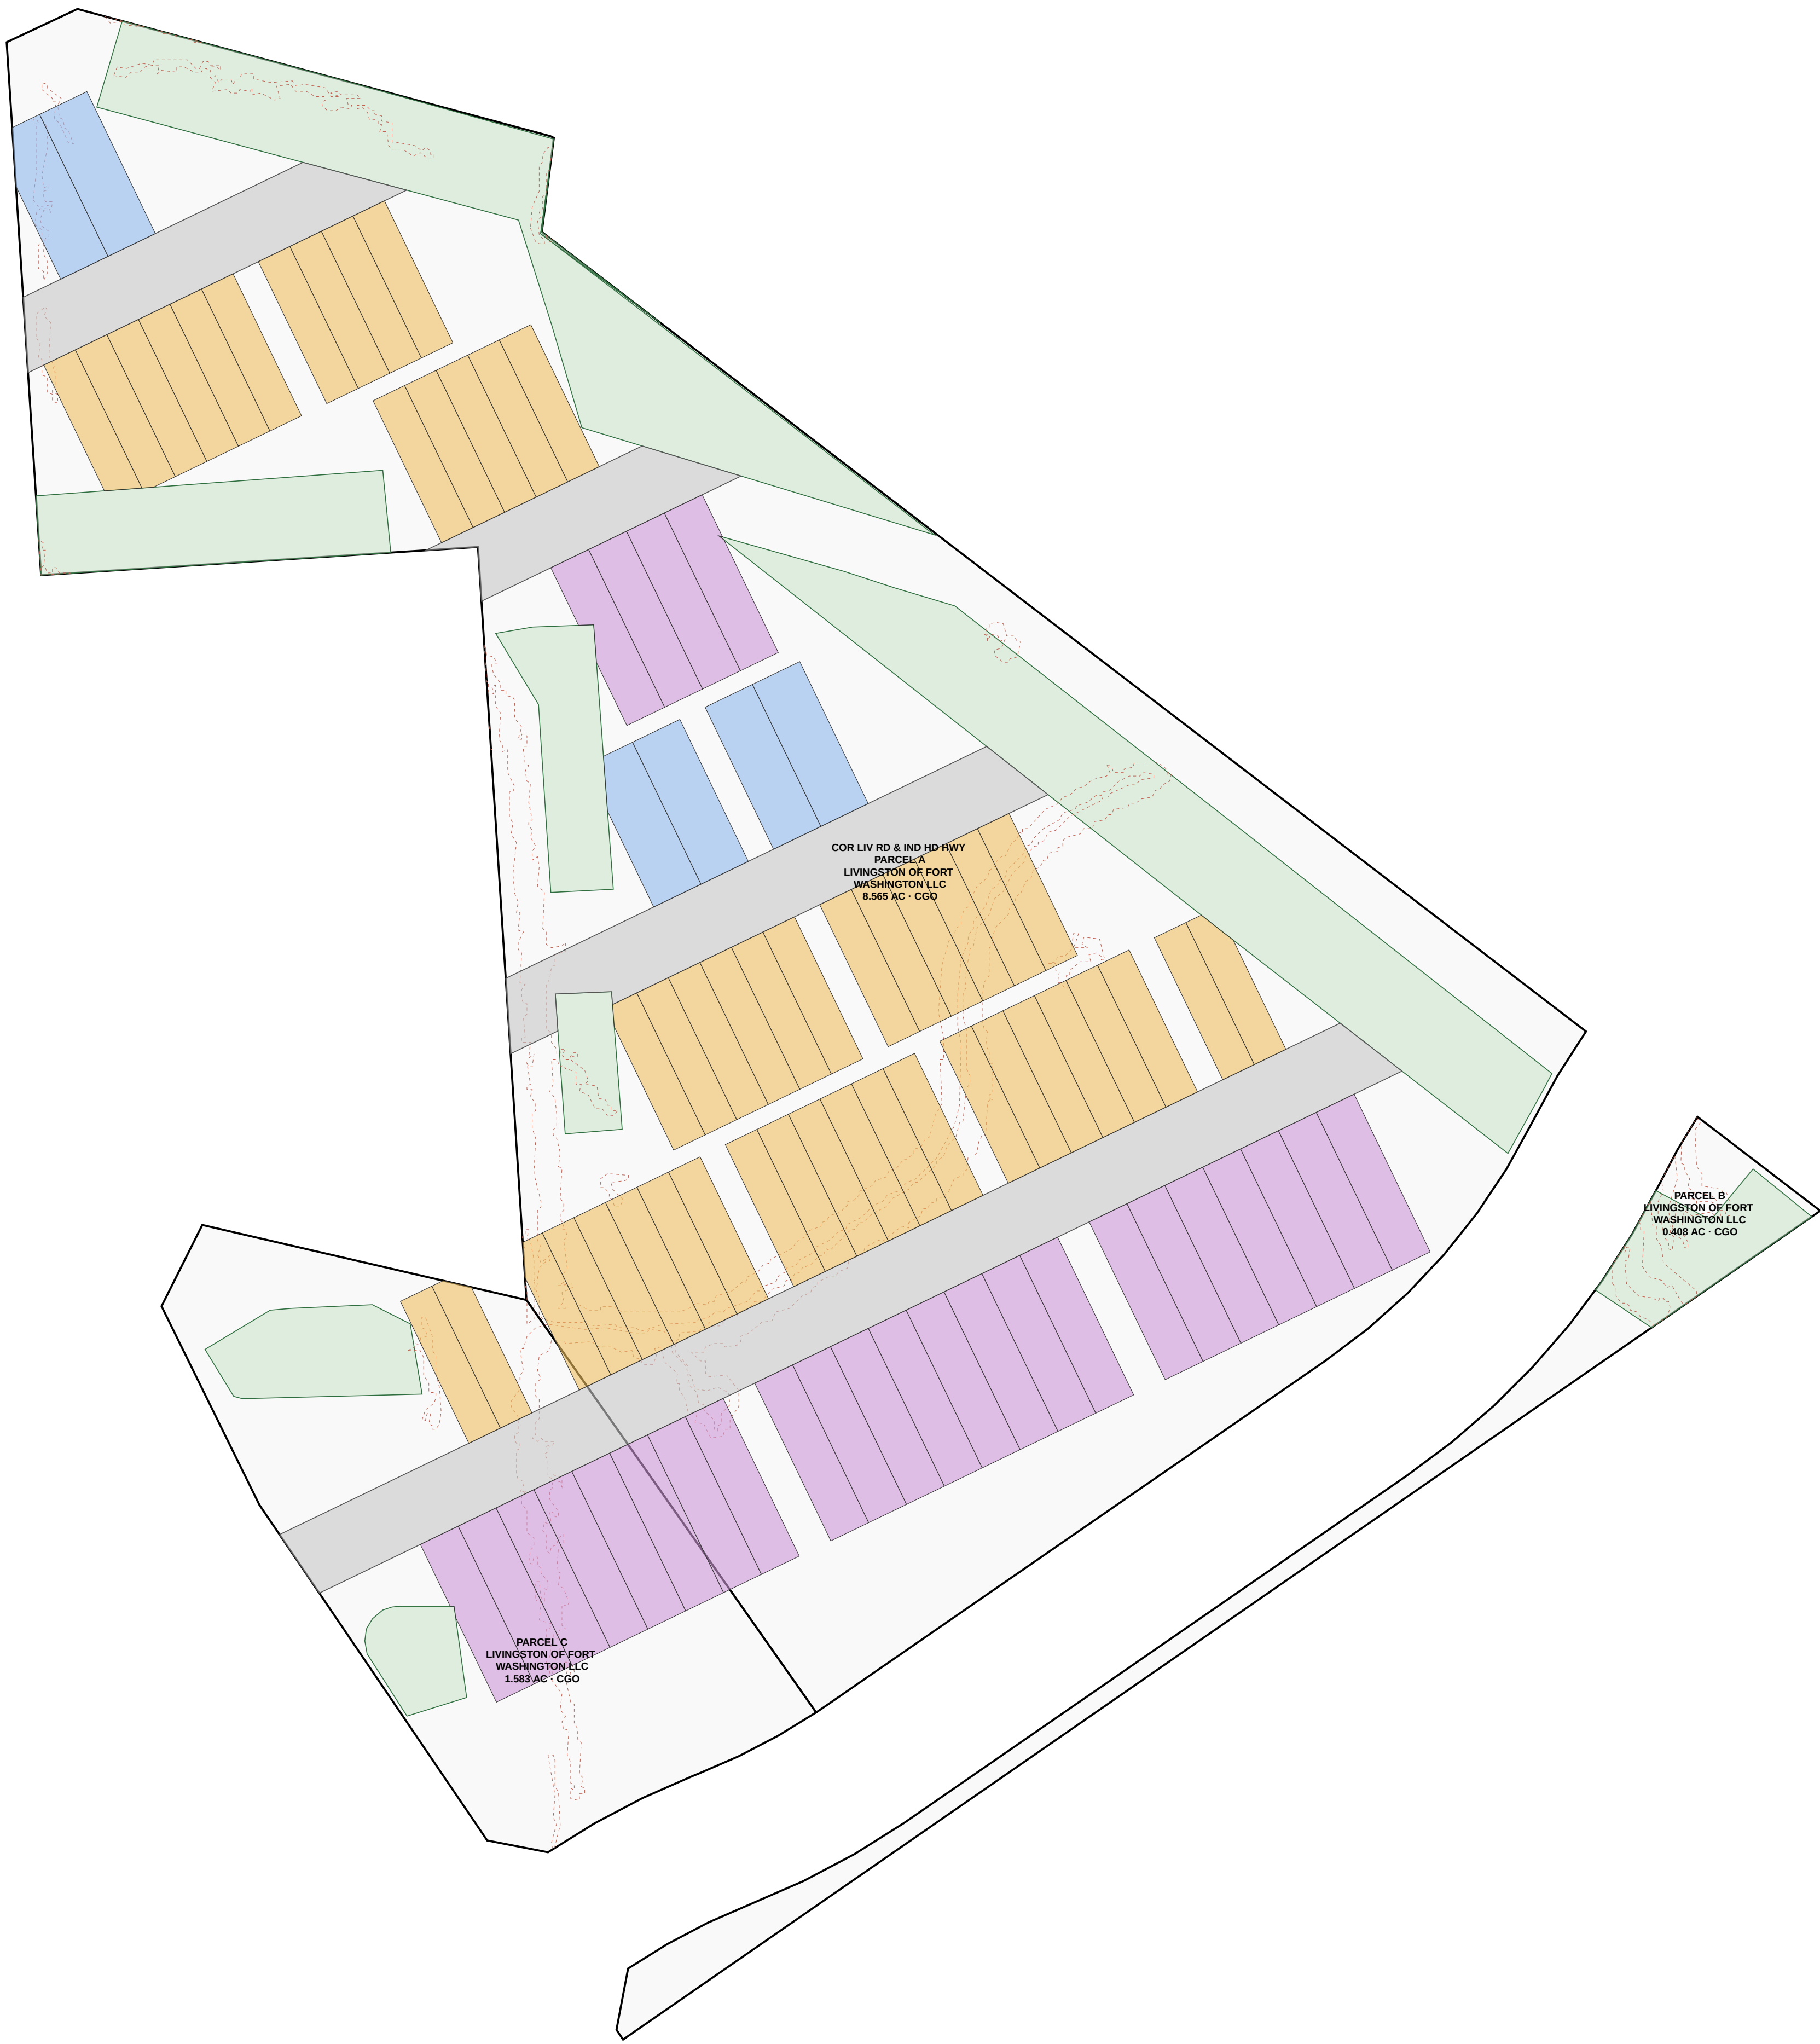

KEALEE

ATTACHED HOUSING YIELD STUDY — PRELIMINARY, NOT A SITE PLAN
Livingston of Fort Washington — CGO attached housing yield study

Zone CGO · certified intensity table Sec. 27-4203 · generated 2026-09-16

PARCELS (PGAtlas Address/Property — owner of record, assessment)
Act 0412007 · COR LIV RD & IND HD HWY PARCEL A · LIVINGSTON OF FORT WASHINGTON LLC · 8.558 ac assessed / 8.565 ac GIS · plat 05267017 · L 20797 F529
Act 0770967 · PARCEL B · LIVINGSTON OF FORT WASHINGTON LLC · 0.408 ac assessed / 0.408 ac GIS · plat 05267017 · L 20797 F529
Act 0770375 · PARCEL C · LIVINGSTON OF FORT WASHINGTON LLC · 1.583 ac assessed / 1.583 ac GIS · plat 05267017 · L 20797 F529
Tract 459.822 sf (10.556 ac). Boundary is the county parcel layer — not a survey.

WHAT CANNOT BE BUILT ON (county layers, clipped to the tract)
Woodland conservation (approved TCP areas) 1.96 ac · slopes >25% in bodies 0.00 ac (graded banks 0.59 ac, regraded) · 15–25% 0.41 ac (built with grading) · stream buffer 0.00 ac · floodplain 0.00 ac · wetlands 0.00 ac · Developable 378,644 sf (8,692 ac).

The Primary Management Area, the woodland conservation threshold and any expanded buffers are set by an approved Natural Resources Inventory and TCP; not by these layers. A 50-ft stream buffer and slopes over 25% are the minimum this would be taken; the lot may take more.

CGO STANDARDS BY DWELLING TYPE (Sec. 27-4203)
Townhouse: 20 du/ac net · lot "e" 20 ft wide · coverage "d" 65% · yards 108/215 ft · height "d" 50 ft
Two-family (duplex): 40 du/ac net · lot "e" 20 ft wide · coverage "d" 65% · yards 108/215 ft · height "d" 50 ft
Two-over-two (stacked, 2 units per bay): 48 du/ac net · lot "e" 50 ft wide · coverage "d" 70% · yards 108/215 ft · height "d" 86 ft

YIELD — THIS LAYOUT
Townhouse: 49 bays / 48 du · 18.44 du/ac on 2.657 net ac (cap 29) · lot coverage 44.4% (cap 65%) · parking 98 at 20du ASSUMED — front-load garage + driveway on the lot
Two-family (duplex): 6 bays / 6 du · 12.52 du/ac on 0.479 net ac (cap 40) · lot coverage 44.4% (cap 65%) · parking 12 at 20du ASSUMED — garage + driveway on each lot
Two-over-two (stacked, 2 units per bay): 27 bays / 54 du · 27.58 du/ac on 1.958 net ac (cap 48) · lot coverage 48% (cap 70%) · parking 81 at 1.50du ASSUMED — one garage space per unit + surface bays along the street
TOTAL 109 DWELLING UNITS in 82 bays · 10.33 du/ac gross on the 10.556-ac tract

CEILINGs if the whole developable ground were one type (≈ 0.8 for streets, parking, open space):

Townhouse: 139 du
Two-family (duplex): 278 du
Two-over-two (stacked, 2 units per bay): 333 du

UNIT ASSUMPTIONS
Townhouse: 20 × 90 ft lot, 20 × 40 ft footprint, 1 du per bay, sticks of "d" 8
Two-family (duplex): 30 × 90 ft lot, 30 × 40 ft footprint, 1 du per bay, sticks of "d" 2
Two-over-two (stacked, 2 units per bay): 24 × 100 ft lot, 24 × 48 ft footprint, 2 du per bay, sticks of "d" 8
Private streets in 40-ft strips (28-ft pavement, walk one side). Streets are drawn as parallel segments; the connecting street, entrance from the public road, visitor parking, open space and the Landscape Manual 4.7 buffer to the RE lots are DSP work not drawn here.

APPROVALS
CGO: townhouse, two-family and multifamily (two-over-two) dwellings are listed uses with their own intensity standards in the certified Sec. 27-4203 table; a Detailed Site Plan is the approval path for residential in the commercial zones (confirm the use table entry for each type — the use table is not carried by this engine).
Sec. 27-8300 parking, Sec. 27-8400 landscaping (Landscape Manual 4.7 buffers against the RE lots), Sec. 25-121 woodland conservation, Sec. 24 subdivision (a preliminary plan of subdivision creates fee-simple townhouse and duplex lots; two-over-tws are condominium or fee-simple with a DSP), stormwater concept (DPPE), WSSC hydraulic planning analysis.

This is a yield study prepared by the Kealee site-plan engine from county GIS and the certified zoning table. It is not a Detailed Site Plan, not a survey and not a determination of what the Planning Board will approve.