




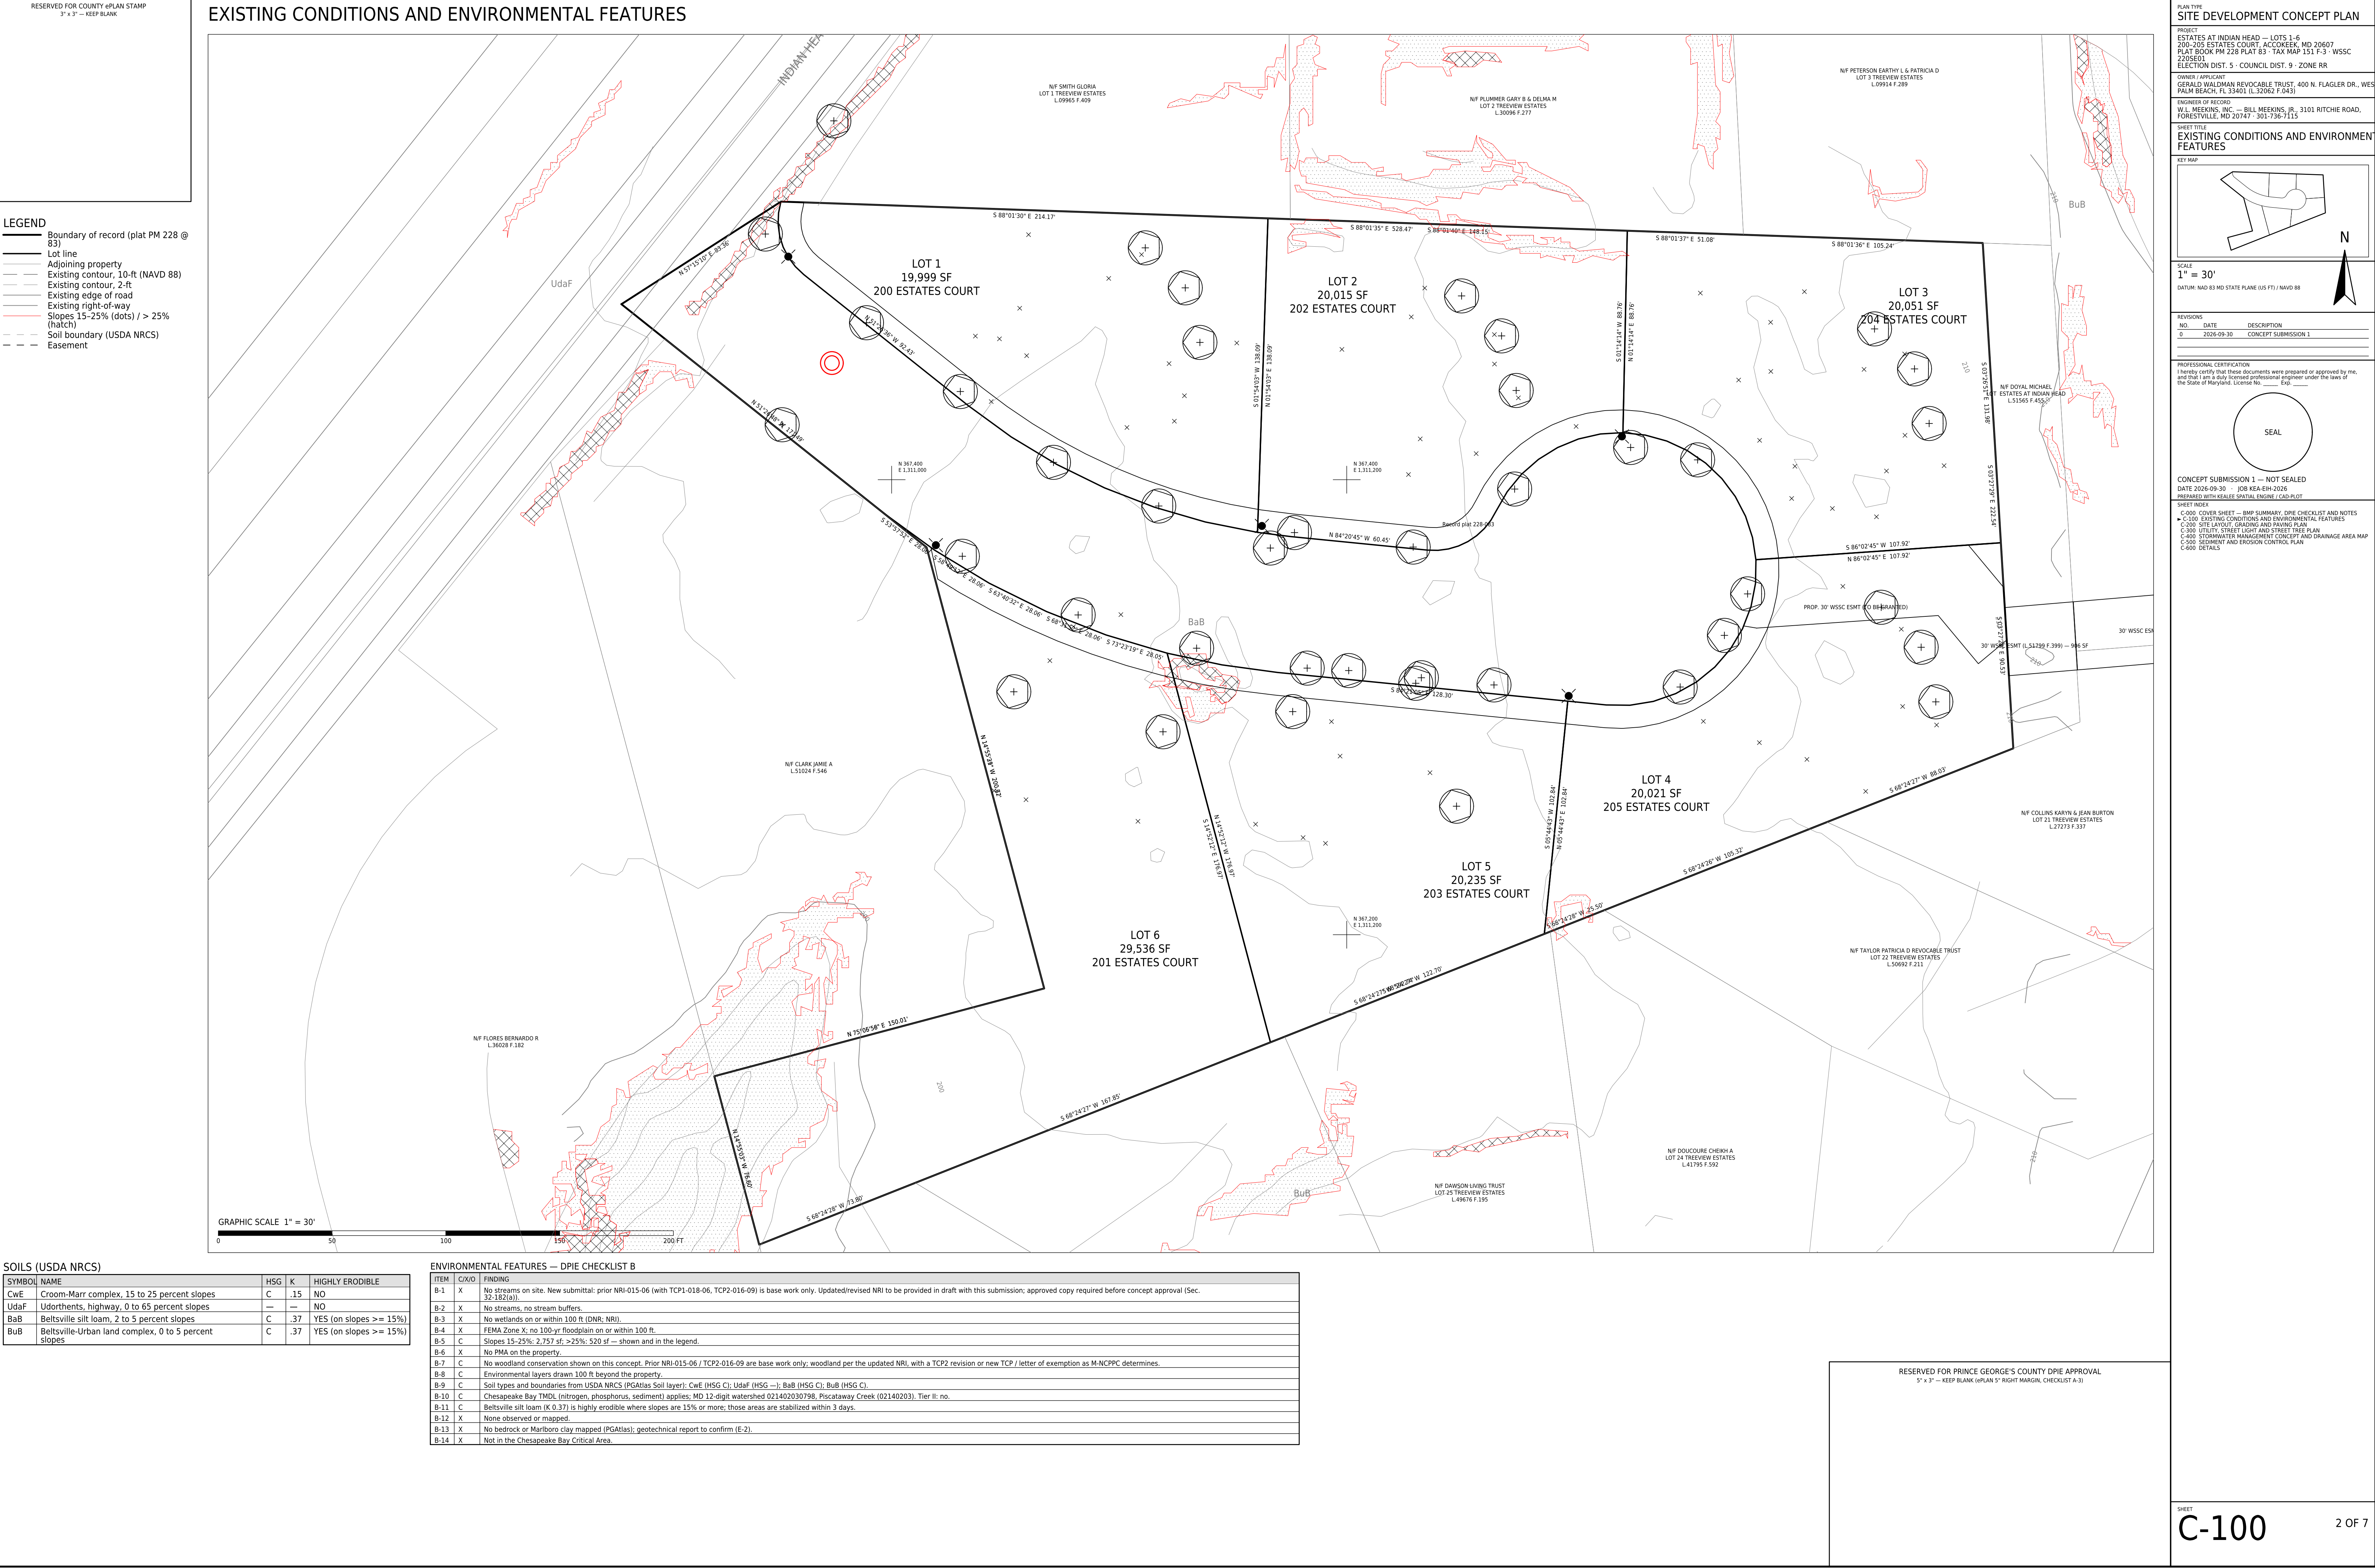


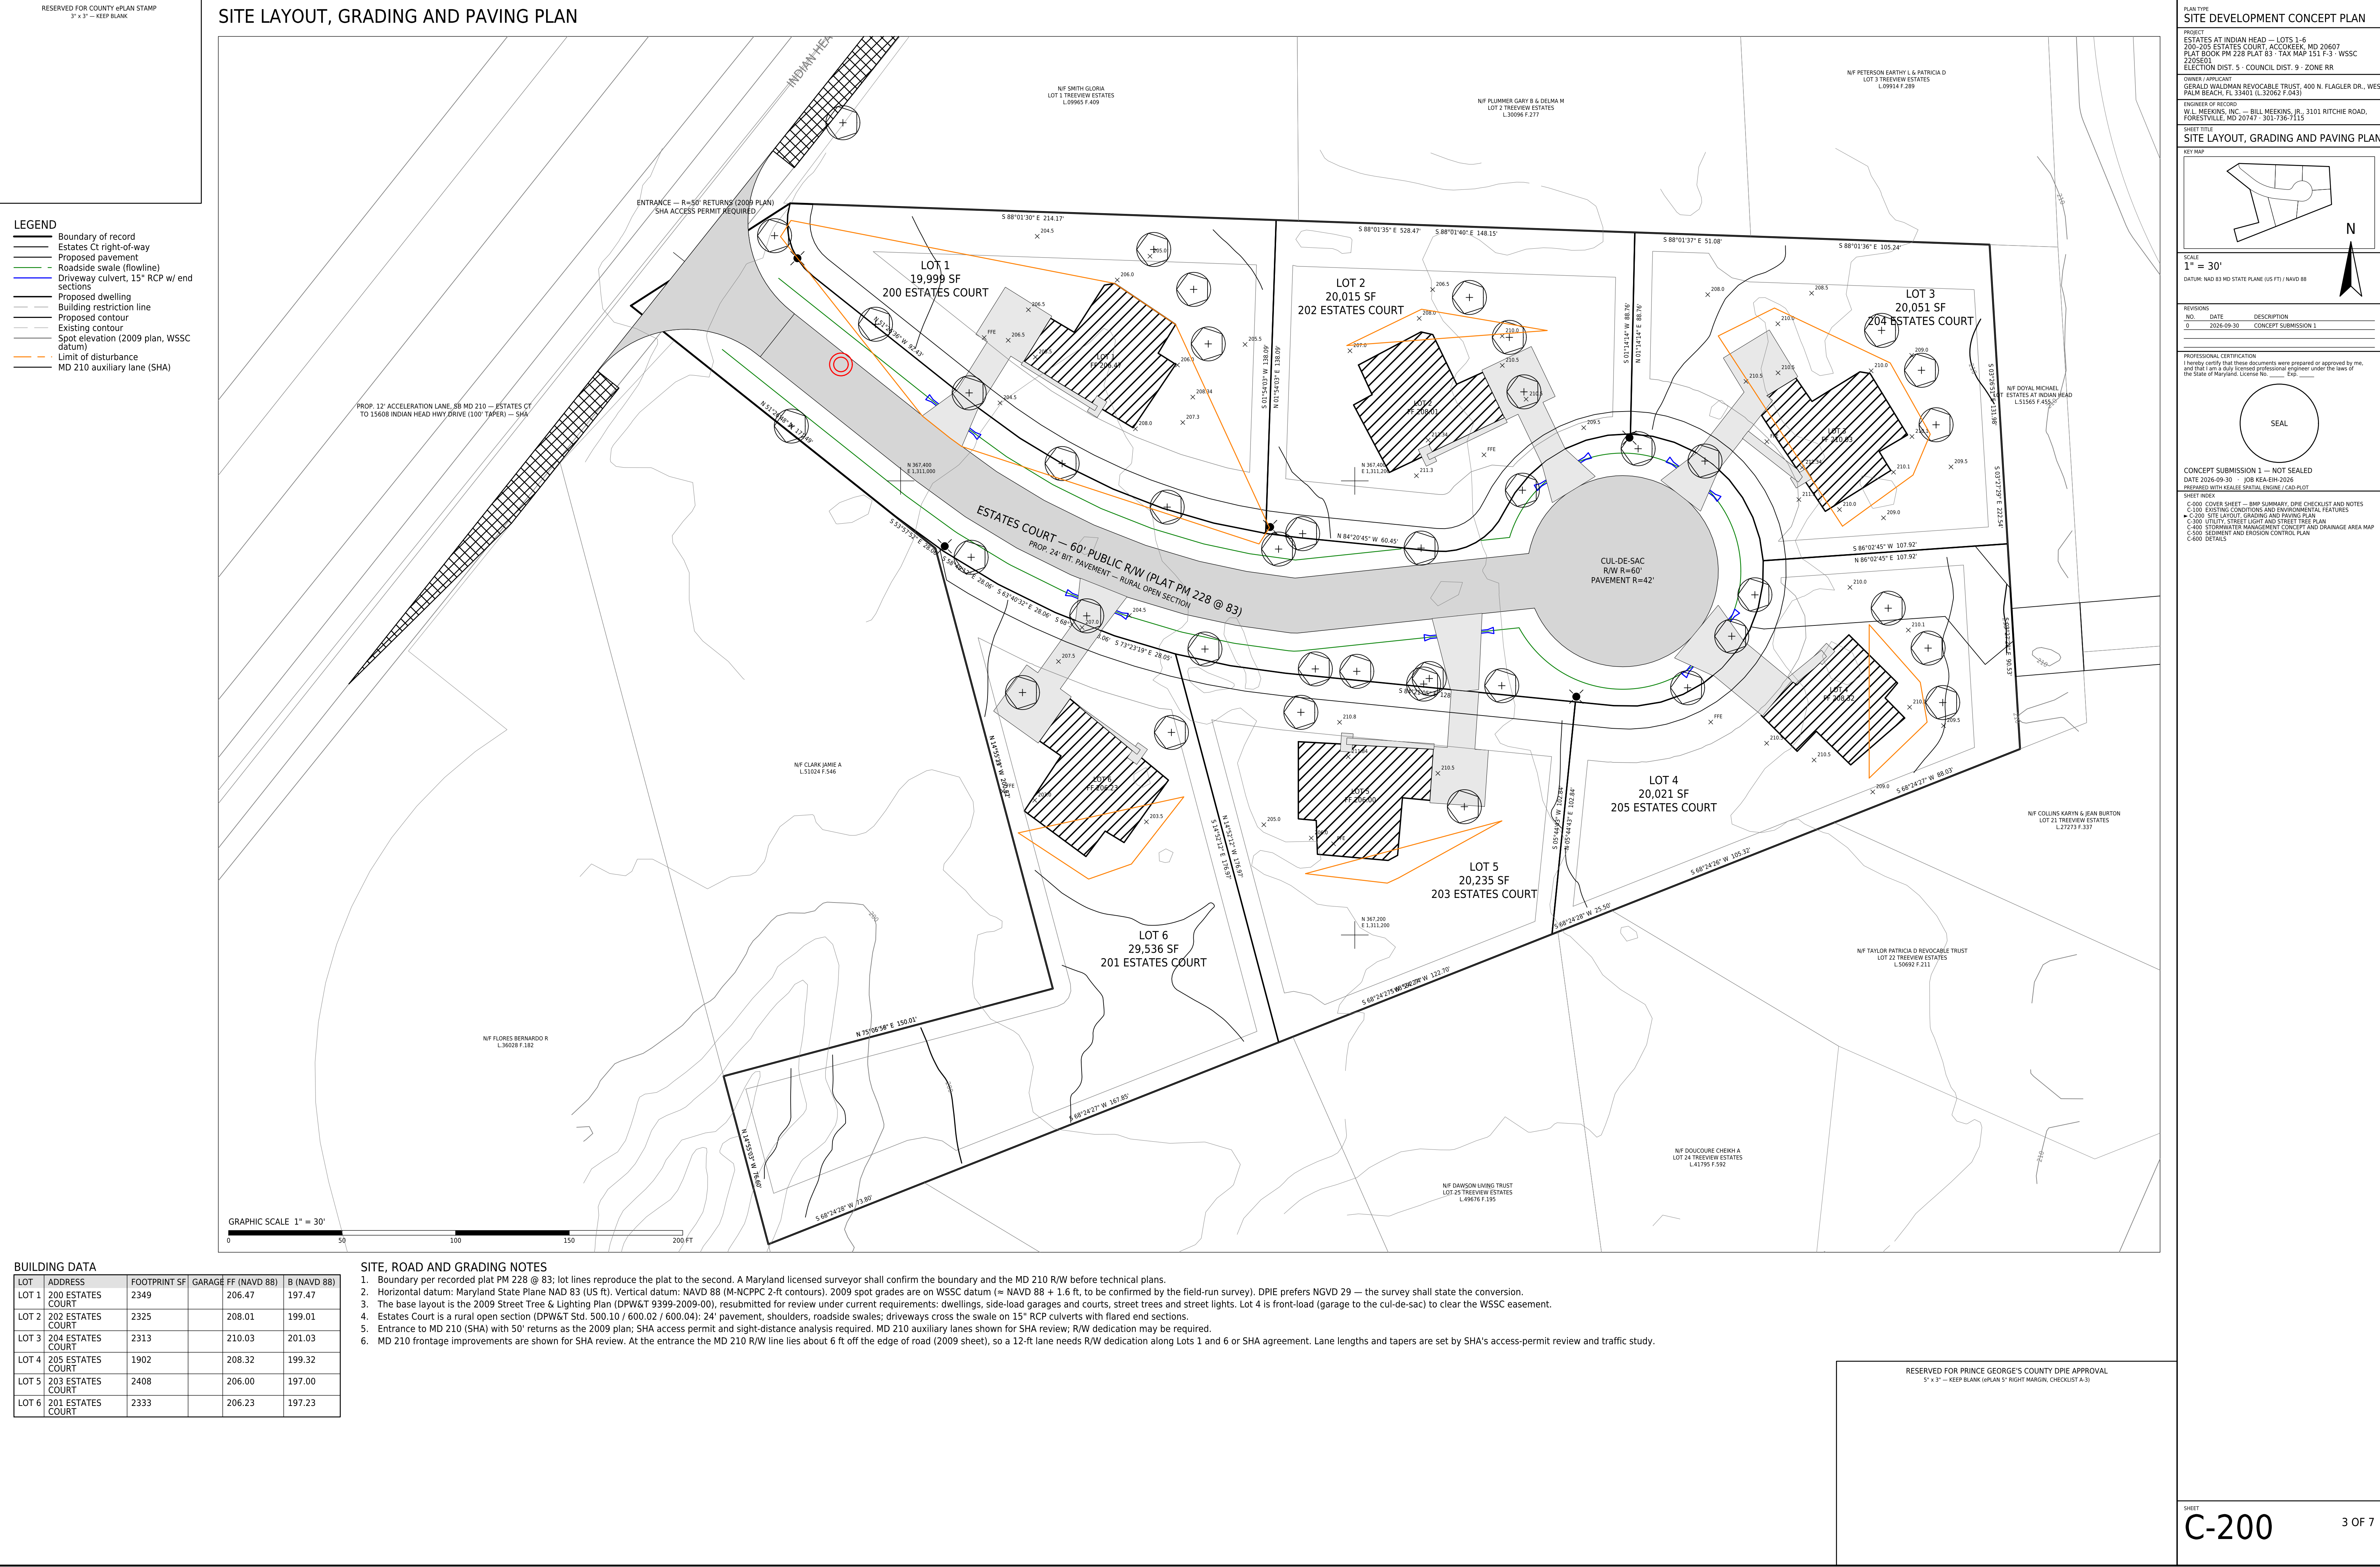

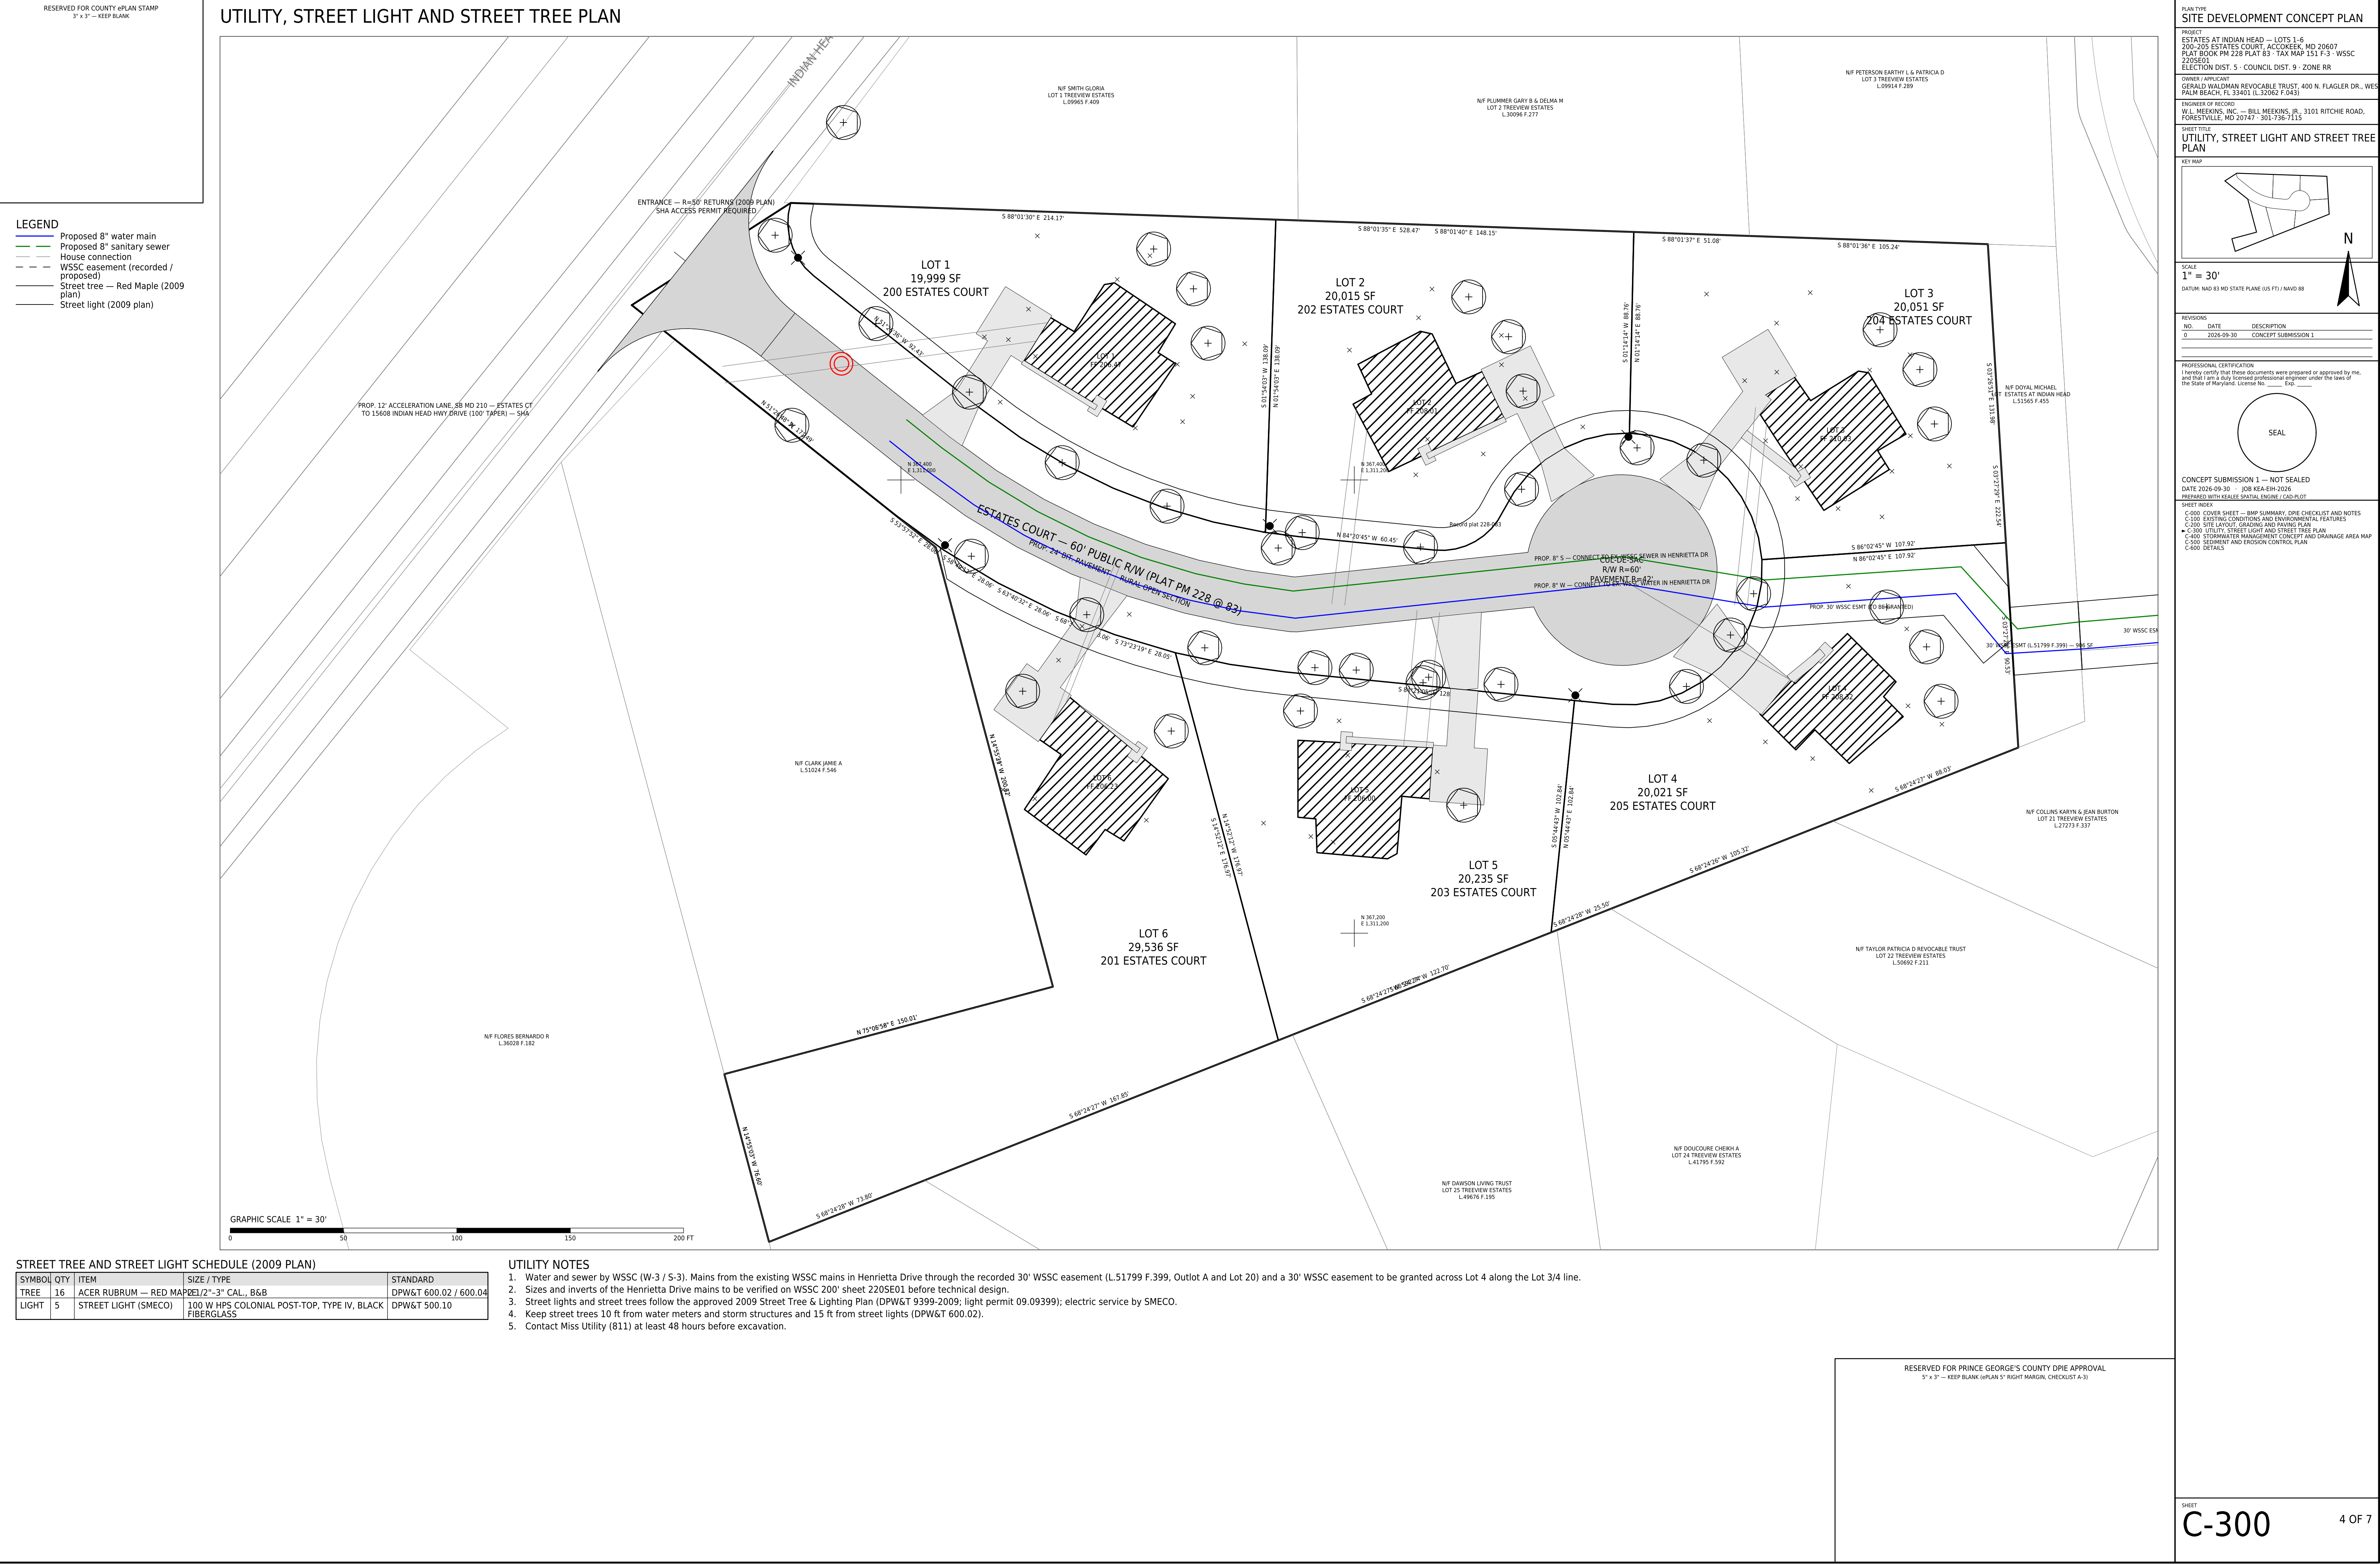

STORMWATER MANAGEMENT CONCEPT AND DRAINAGE AREA MAP

- LEGEND
- ESD practice — micro-bioretenction (M-6)
 - Roadside dry swale (M-8)
 - Drainage area to practice
 - Off-site area draining onto site
 - 100-yr overflow path
 - Point of investigation
 - Driveway culvert

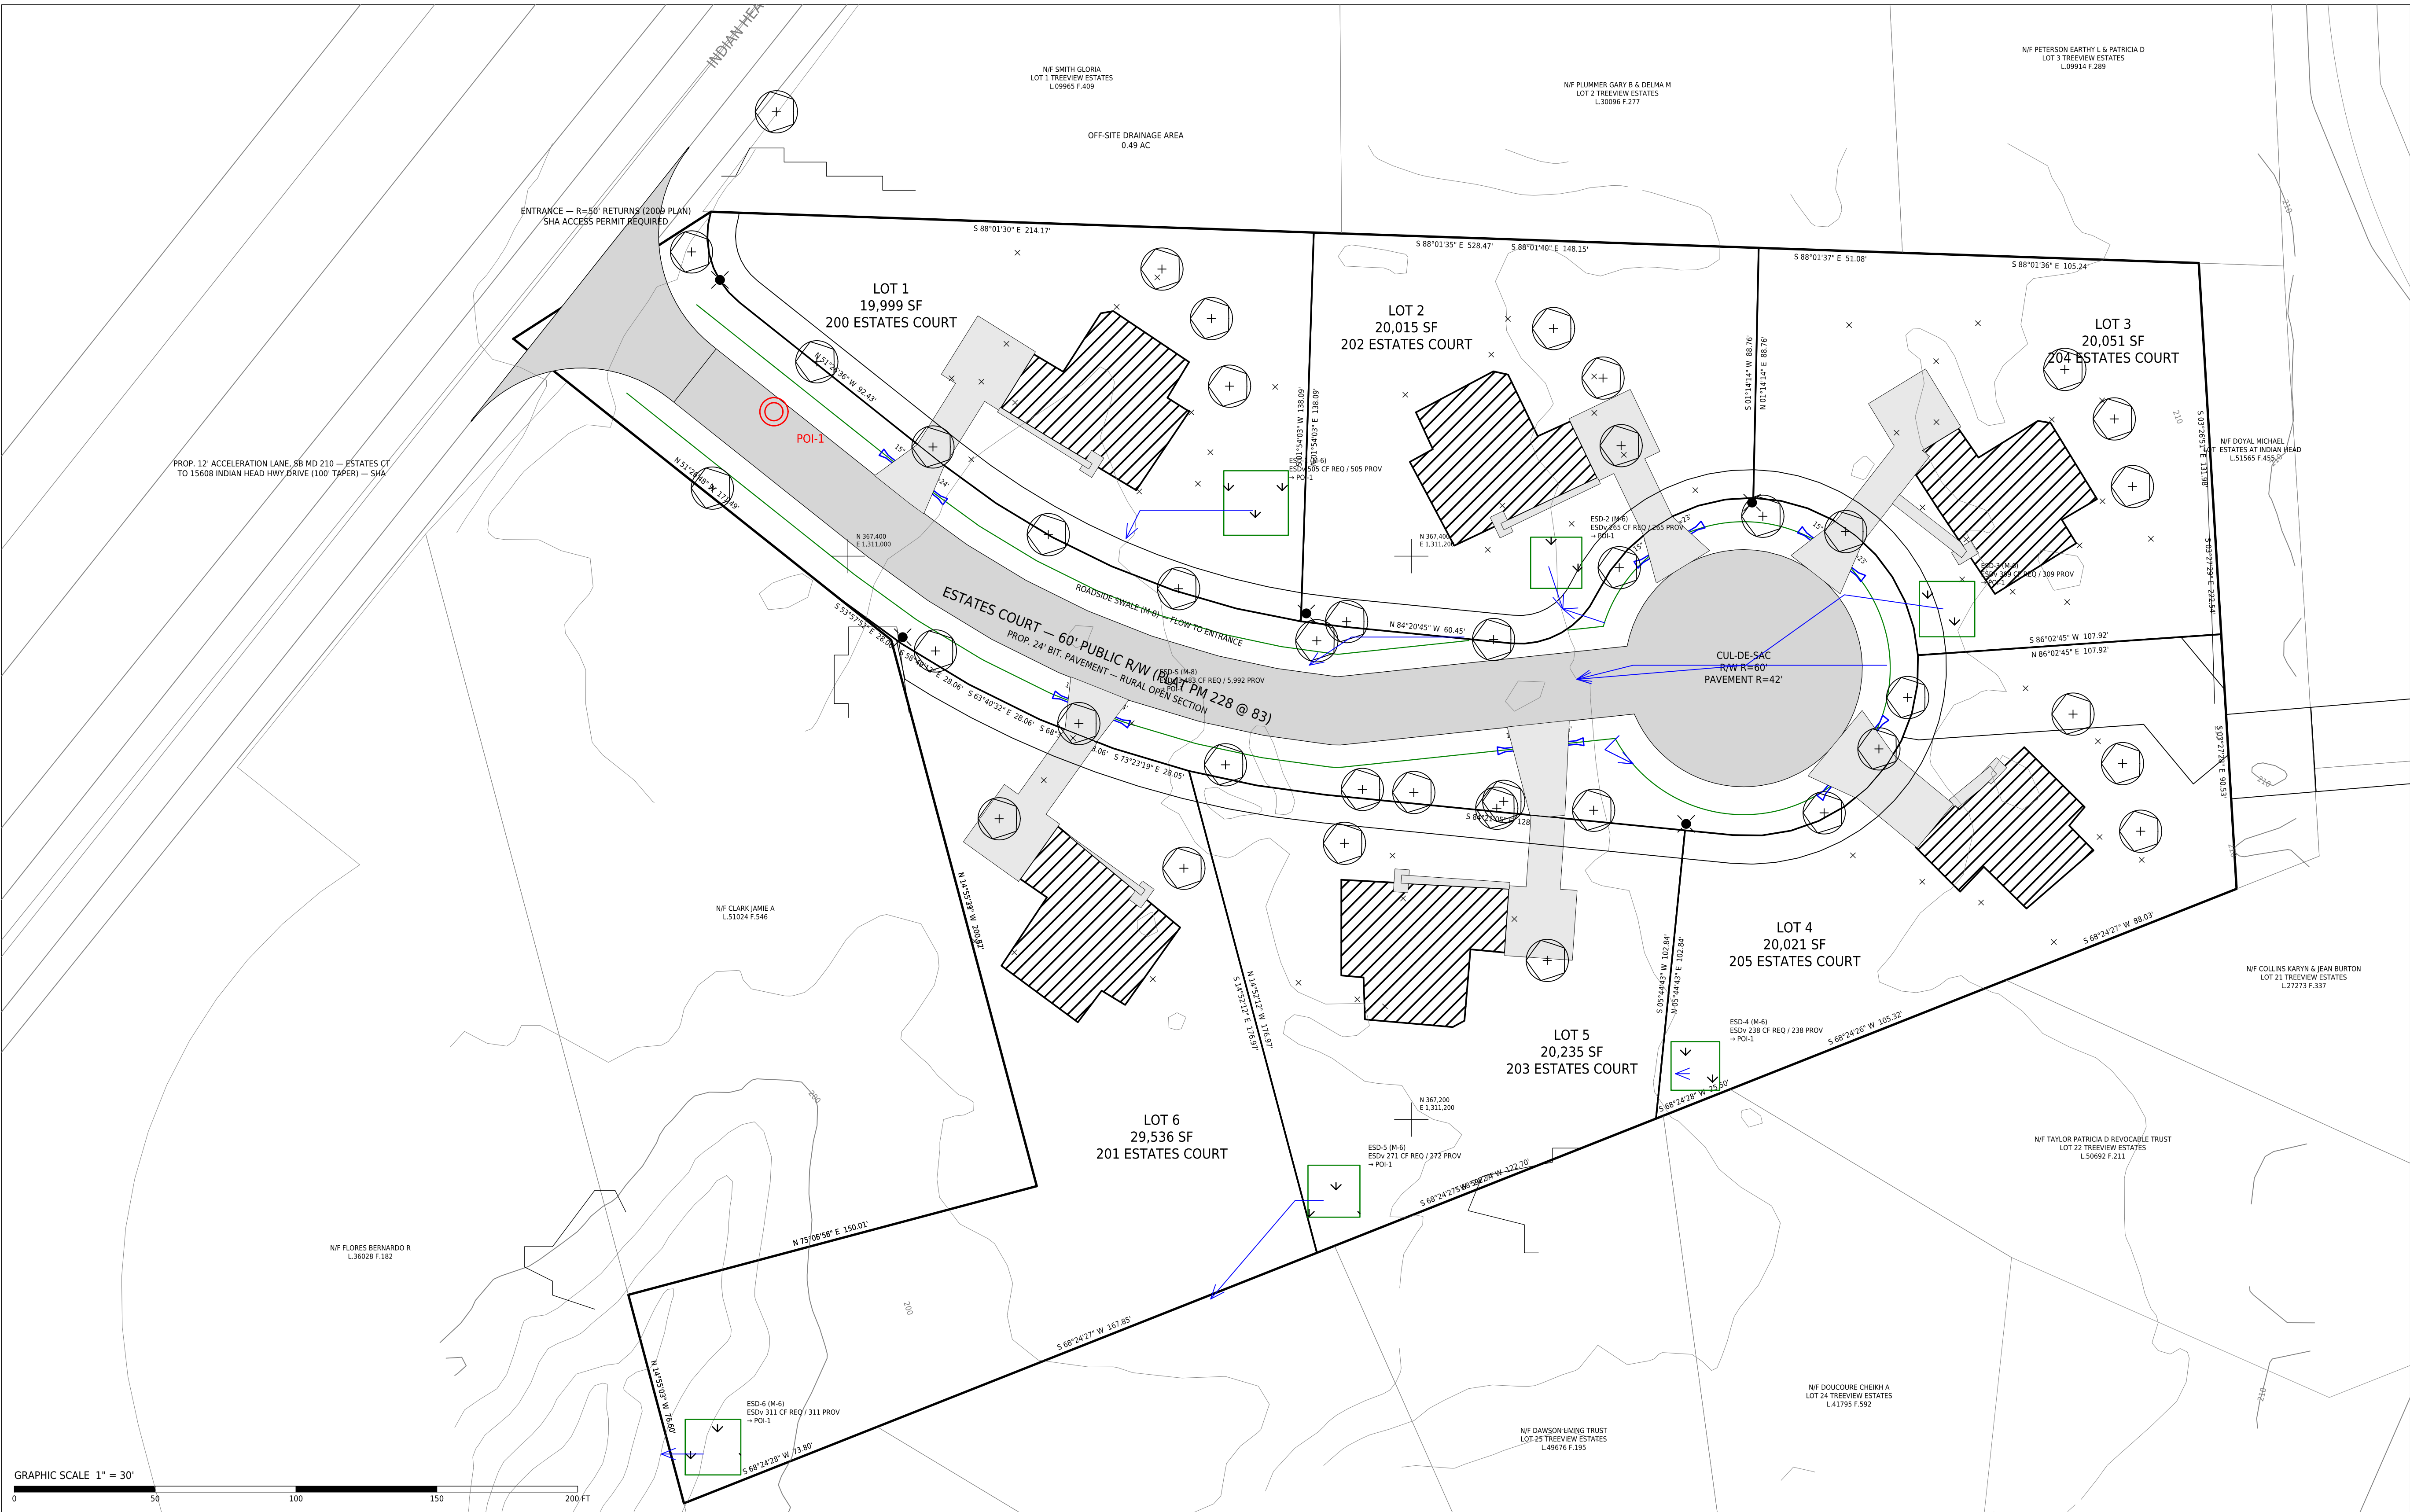

ESD PER PRACTICE (FULL TABLE ON C-000)

BMP	MDE	LOCATION	POI	DA SF	%I	P_E	ESDv REQ	ESDv PROV
ESD-1	M-6	Lot 1	POI-1	19,999	22.5	1.2	505	505
ESD-2	M-6	Lot 2	POI-1	20,015	12.1	1.0	265	265
ESD-3	M-6	Lot 3	POI-1	20,051	15.0	1.0	309	309
ESD-4	M-6	Lot 4	POI-1	20,021	10.3	1.0	238	238
ESD-5	M-6	Lot 5	POI-1	20,235	12.3	1.0	271	272
ESD-6	M-6	Lot 6	POI-1	29,536	8.5	1.0	311	311
ESD-5	M-8	Estates Ct R/W, both sides	POI-1	36,041	58.9	2.0	3,483	5,992

POINTS OF INVESTIGATION (C-9)

POI	LOCATION	SHARE	ESDv REQ	ESDv PROV
POI-1	N 367,451 E 1,310,974	100%	5,382	7,892

SWM NOTES

- SWM by Environmental Site Design to the MEP (Md. Stormwater Management Act of 2007; MDE Design Manual Ch. 5; PCG Subtitle 32). Target rainfall P_E from MDE Table 5.3 for HSG C at each drainage area's imperviousness.
- Each lot drains to one micro-bioretenction cell (M-6): 12-in max. ponding; 2.5-ft filter media; underdrain to a stable outfall. Estates Court drains to roadside dry swales (M-8) with check dams.
- Rooftop and non-rooftop disconnection (N-1, N-2) to be credited at technical design. Infiltration credit only where Sec. 32-131 borings show ≥ 0.52 in/hr.
- Private ESD practices: maintenance agreement recorded before permit; public swales in the R/W maintained by DPIE.
- D8 flow routing on a 5-ft surface interpolated from the existing 2-ft contours; exit points clustered at 120 ft; POIs carrying under 4% of the site omitted. Concept-level — reset from the field-run survey.

PLAN TYPE
SITE DEVELOPMENT CONCEPT PLAN


PROJECT
ESTATES AT INDIAN HEAD — LOTS 1-6
200-205 ESTATES COURT, ACCOKEEK, MD 20607
PLAT BOOK PM 228 PLAT 83 TAX MAP 151 F-3 - WSSC
220501
ELECTION DIST. 5 COUNCIL DIST. 9 ZONE RR

OWNER / APPLICANT
GERALD WALDMAN REVOCABLE TRUST, 400 N. FLAGLER DR., WEST PALM BEACH, FL 33403 (L32062 F.043)

ENGINEER OF RECORD
W.L. MECKINS, INC. — BILL MECKINS, JR., 3101 RITCHIE ROAD, FORESTVILLE, MD 20747 301-736-7115

SHEET TITLE
STORMWATER MANAGEMENT CONCEPT AND DRAINAGE AREA MAP


KEY MAP

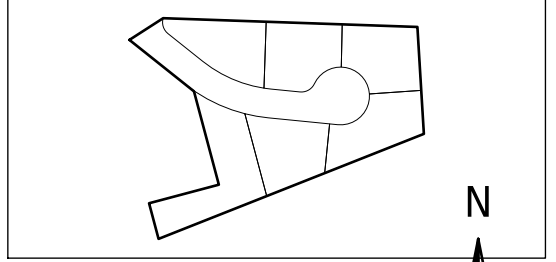

SCALE
1" = 30'
DATUM: NAD 83 MD STATE PLANE (US FT) / NAD83

REVISIONS		
NO.	DATE	DESCRIPTION
0	2026-09-30	CONCEPT SUBMISSION 1


PROFESSIONAL CERTIFICATION
I hereby certify that these documents were prepared or approved by me, and that I am a duly licensed professional engineer under the laws of the State of Maryland. License No. _____ E.O. _____

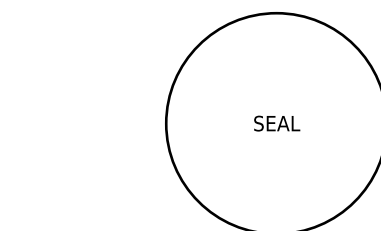




CONCEPT SUBMISSION 1 — NOT SEALED

DATE 2026-09-30 JOB KEA-EH-2026
PREPARED WITH SCALE 3/32" = 1" ENGINEER / C-000-001


SHEET INDEX
C-000 COVER SHEET — BMP SUMMARY, DPIE CHECKLIST AND NOTES
C-100 EXISTING CONDITIONS AND ENVIRONMENTAL FEATURES
C-200 SITE LAYOUT, GRADING AND PAVING PLAN
C-300 UTILITY, STREET LIGHT AND STREET TREE PLAN
C-400 STORMWATER MANAGEMENT CONCEPT AND DRAINAGE AREA MAP
C-500 SEDIMENT AND EROSION CONTROL PLAN
C-600 DETAILS

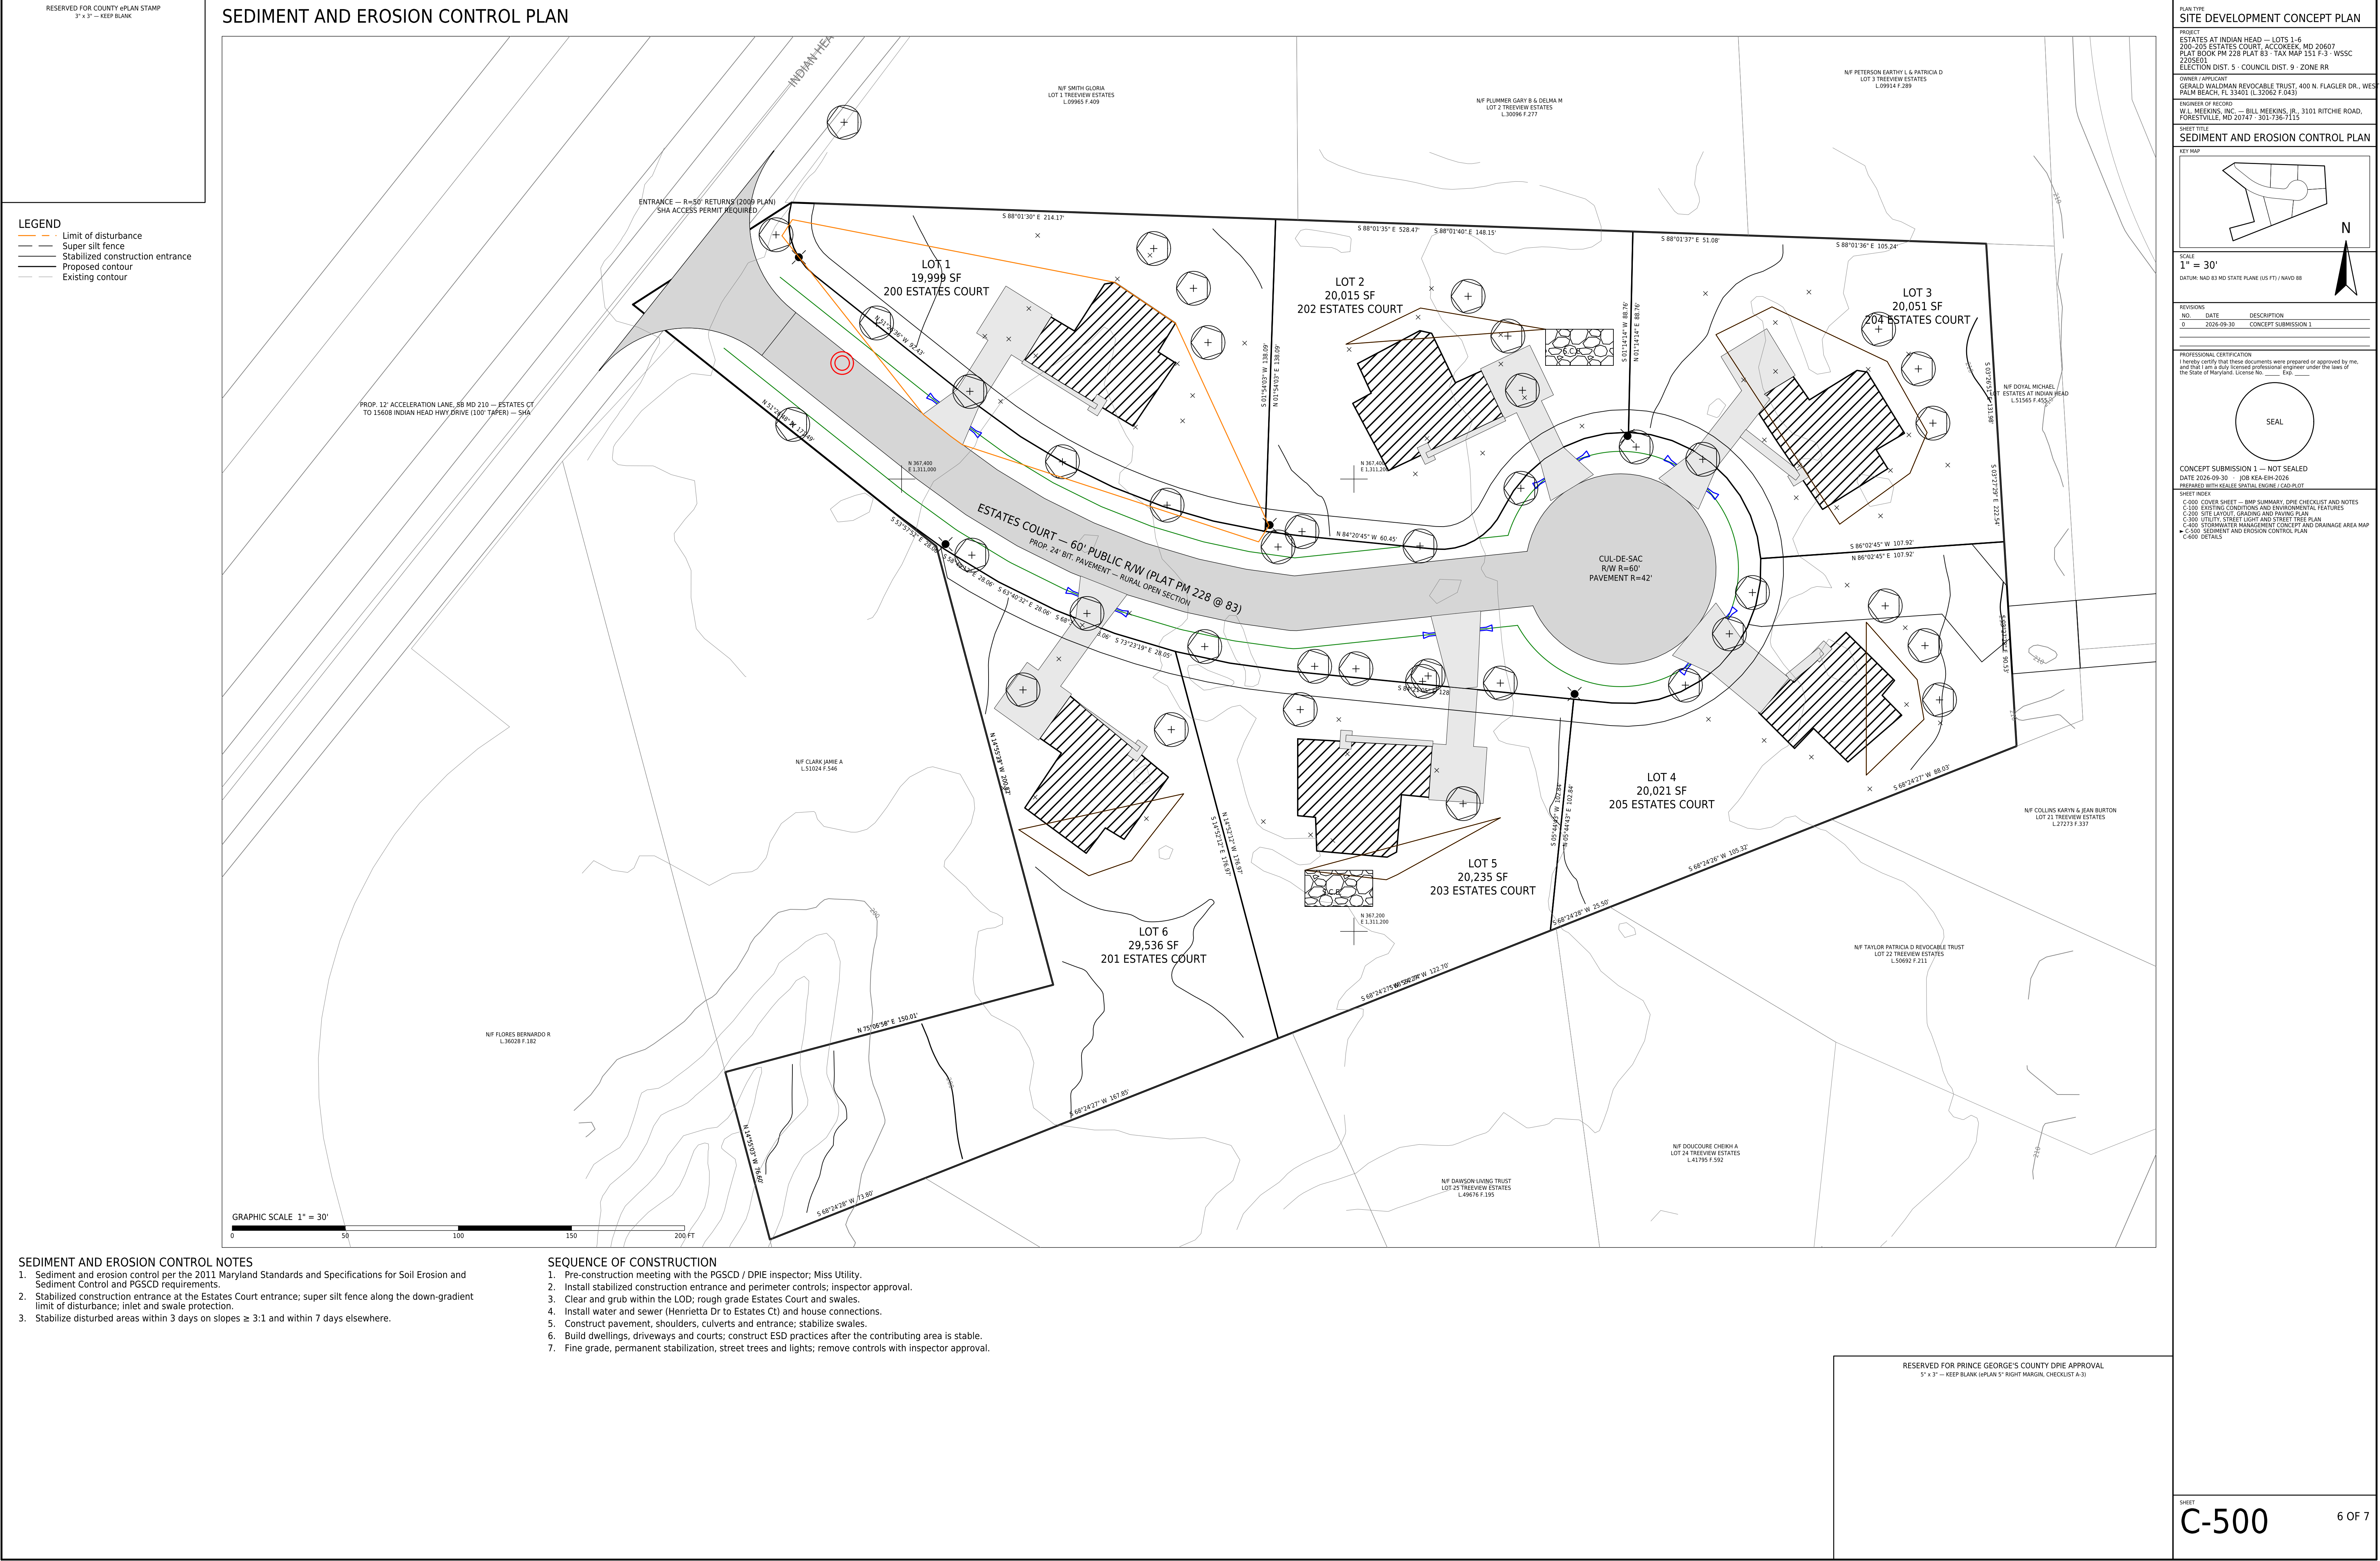

DETAILS

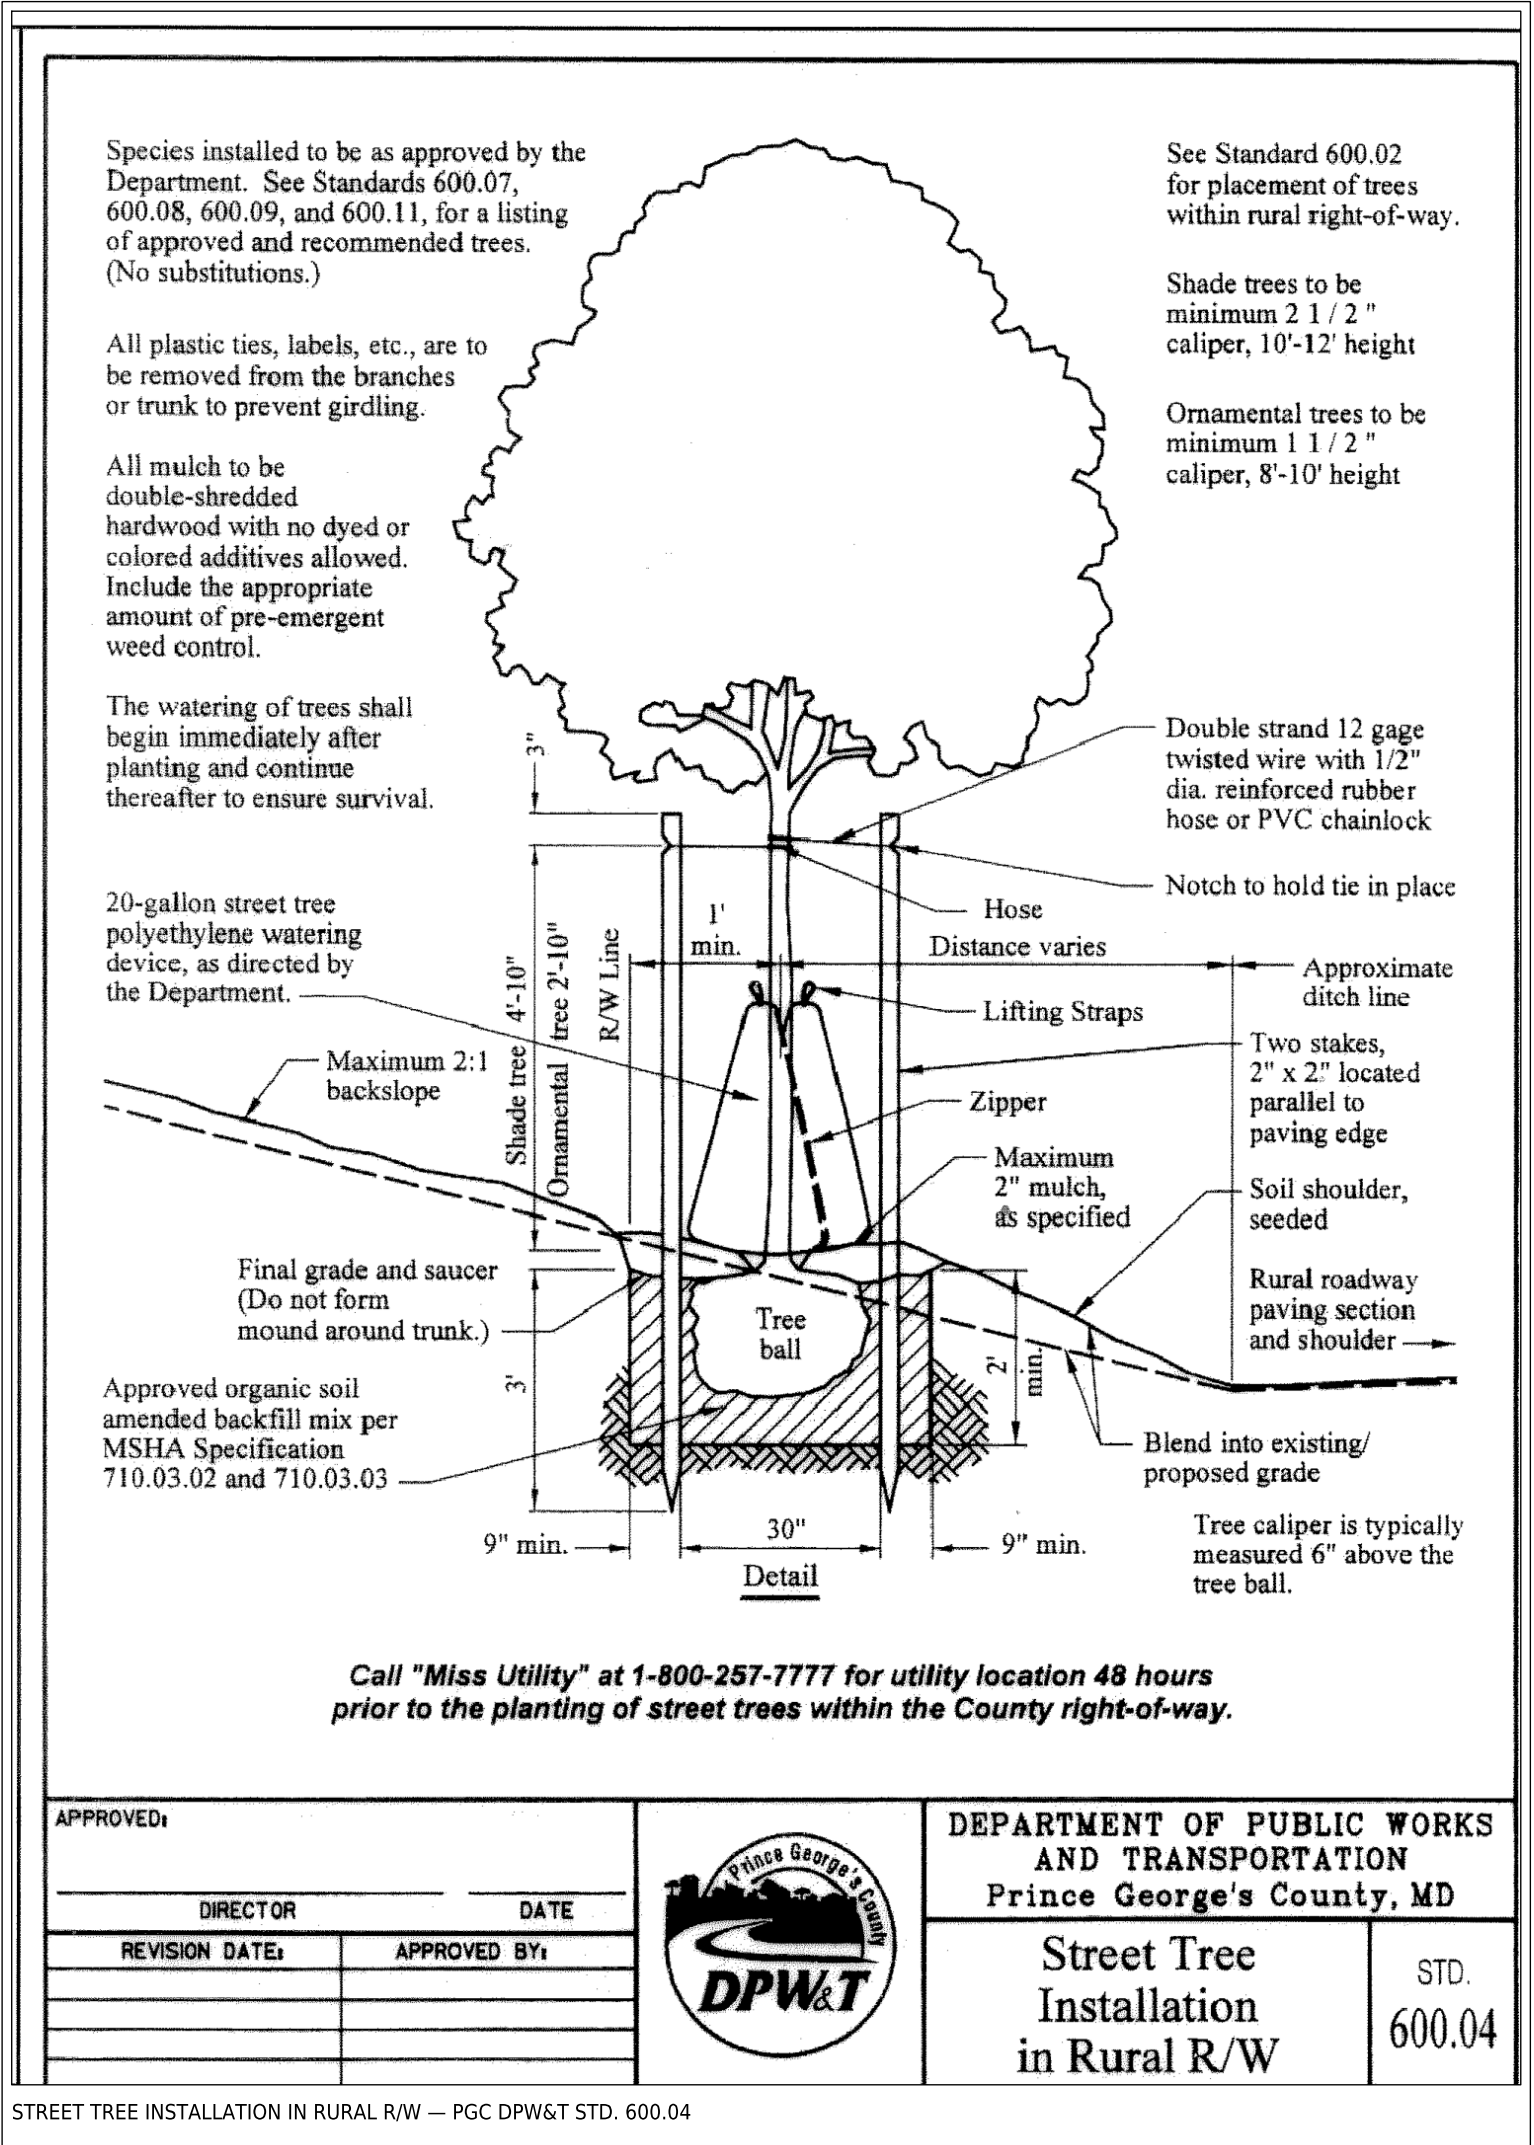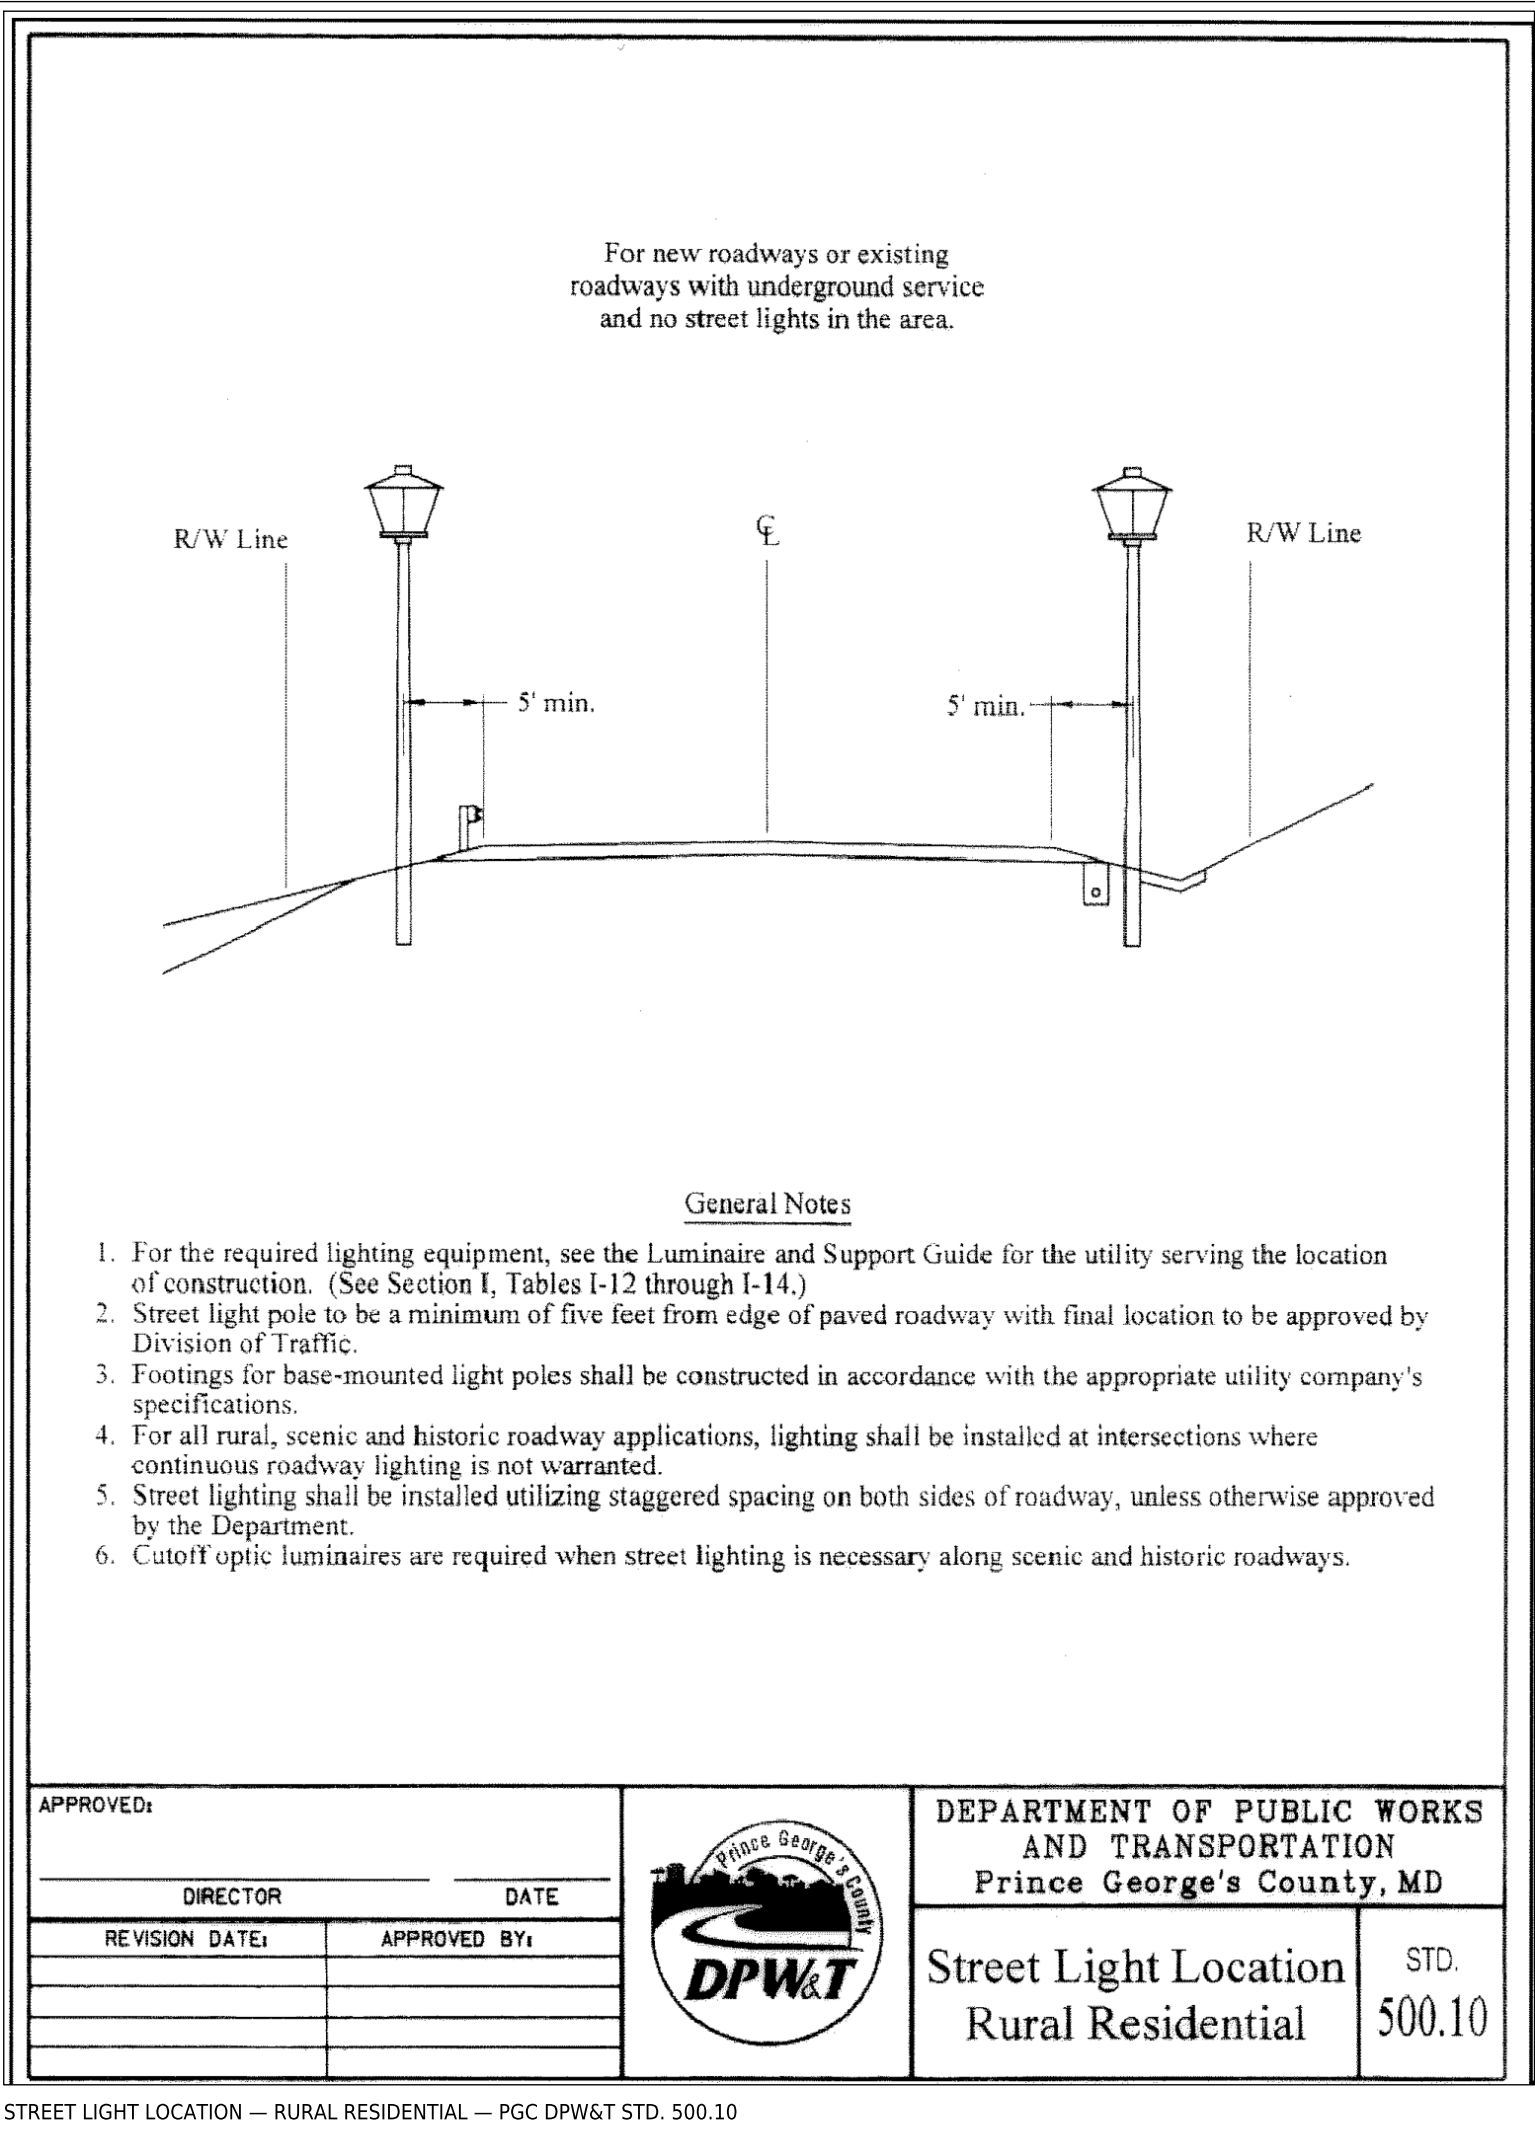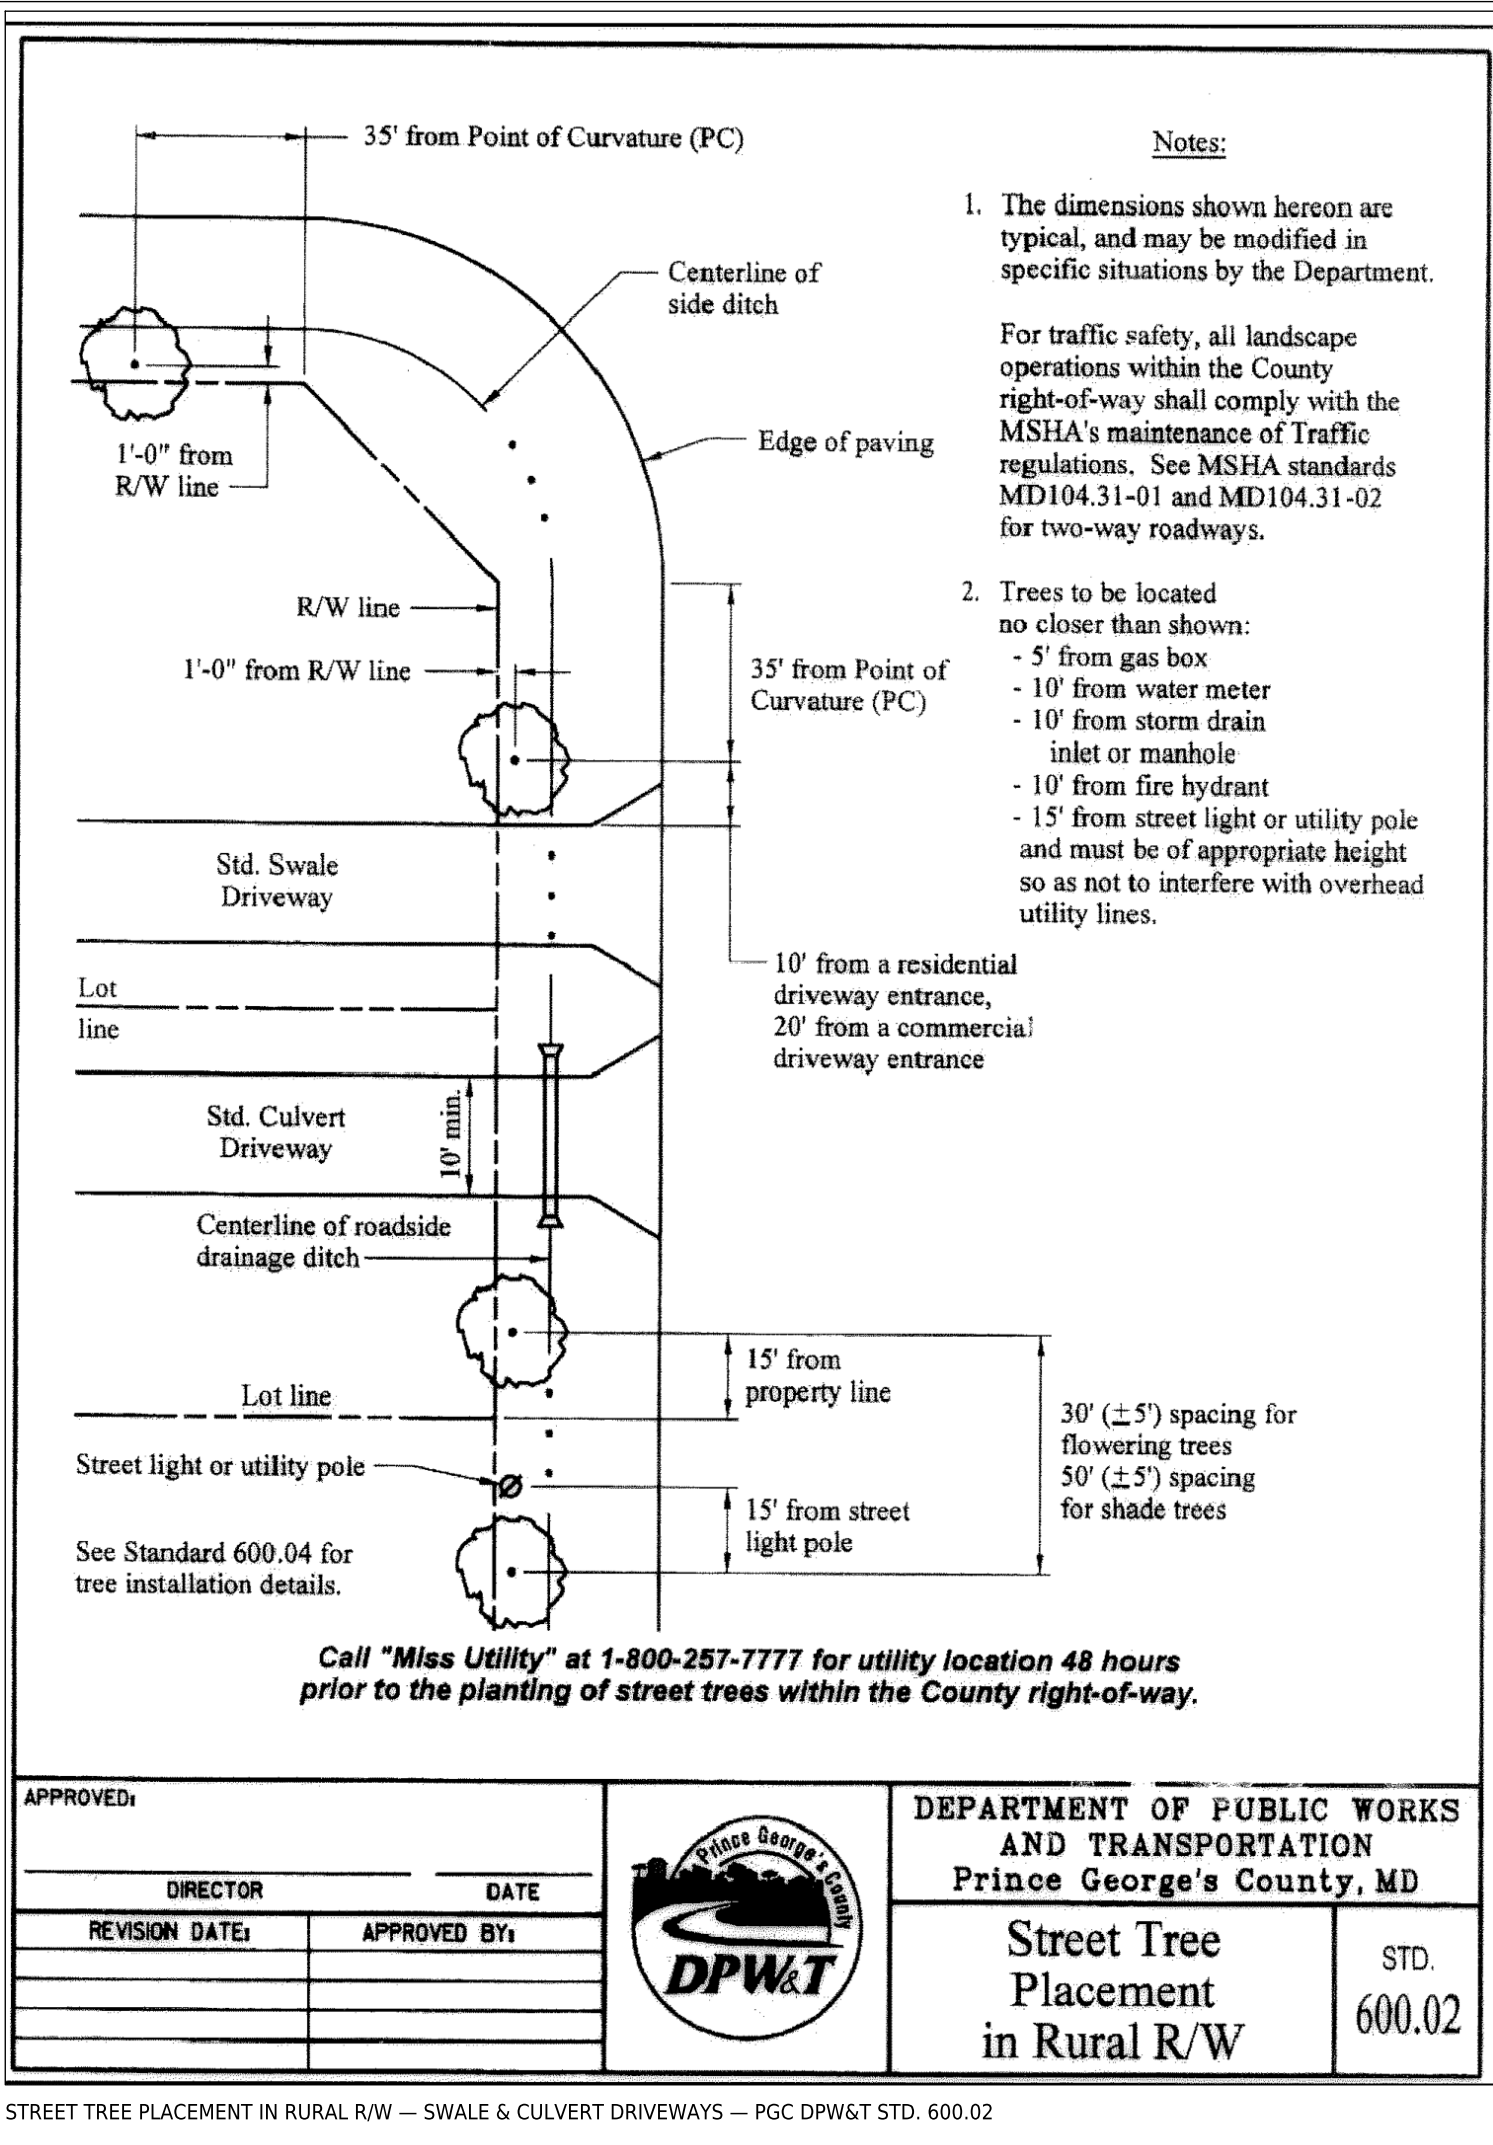


ESTATES COURT — TYPICAL SECTION (RURAL OPEN SECTION, 60' R/W)

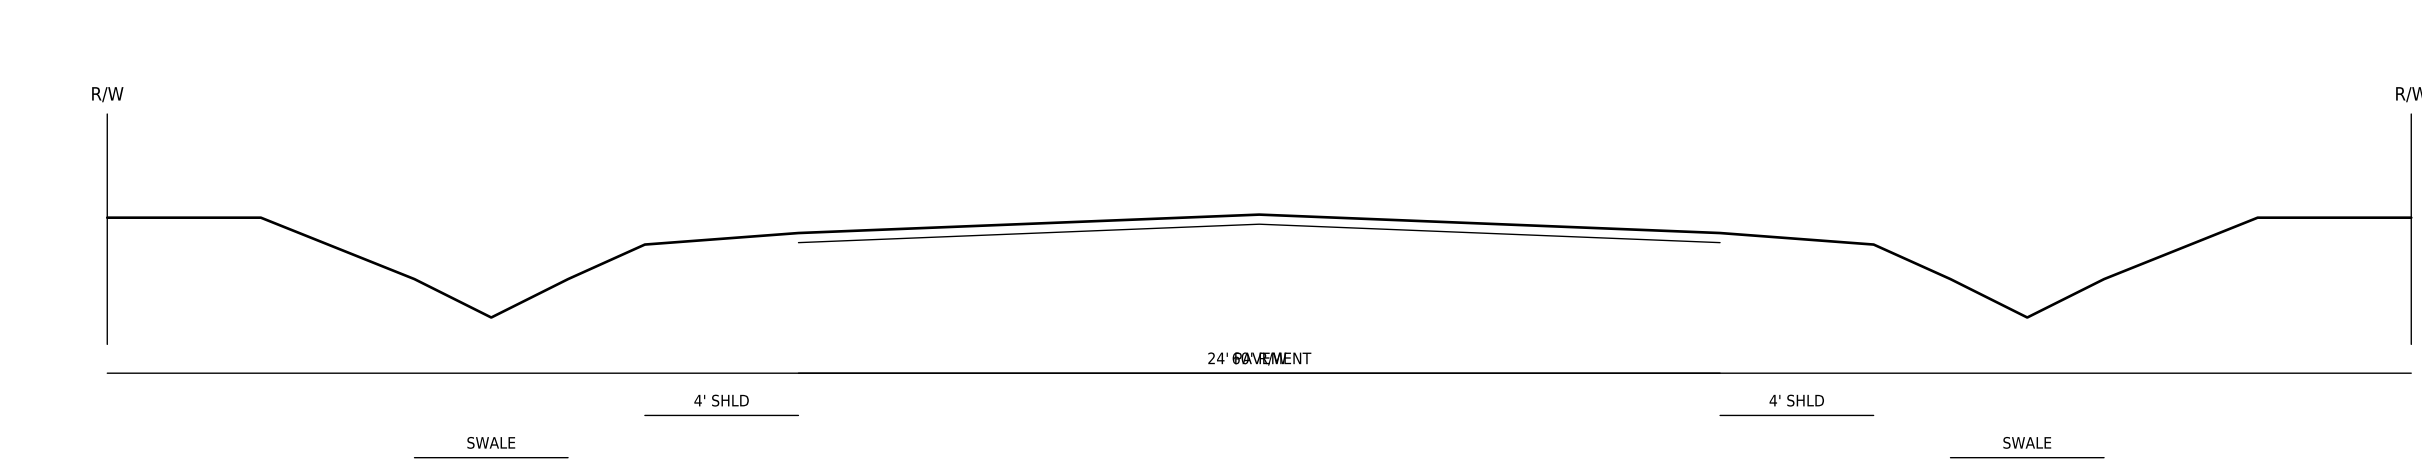


1.1/2" SURFACE + 2.1/2" BASE BIT. CONC. ON 6" GAB (DPW&T PAVEMENT SCHEDULE FOR RURAL RESIDENTIAL — CONFIRM)
CROSS SLOPE 2%; 4-FT STABILIZED SHOULDERS, SWALE FLOWLINE 20 FT OFF CENTRELINE, 3:1 SIDE SLOPES
DRIVEWAYS CROSS THE SWALE ON 15" RCP CULVERTS WITH FLARED END SECTIONS (DPW&T STD. 600.02)

MICRO-BIORETENTION (M-6) — TYPICAL SECTION

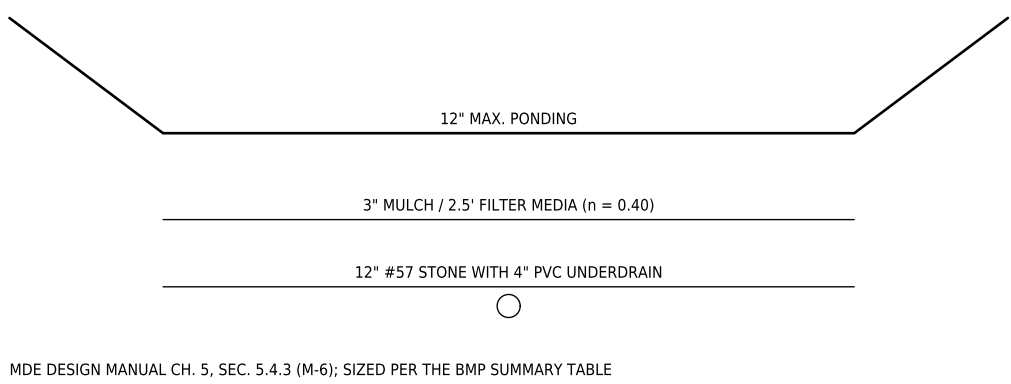

DRY SWALE (M-8) WITH CHECK DAM

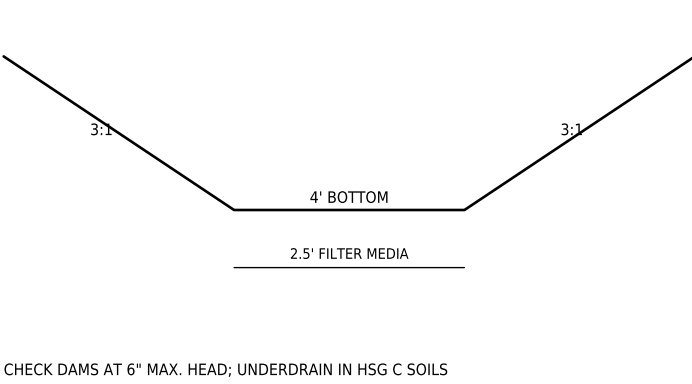

PLAN TYPE
SITE DEVELOPMENT CONCEPT PLAN

PROJECT
ESTATES AT INDIAN HEAD — LOTS 1-6
200-205 ESTATES COURT, ACCOKEEK, MD 20607
PLAT BOOK PM 226 PLAT 83 TAX MAP 151 P-3 WSSC
2206E01
ELECTION DIST. 5 - COUNCIL DIST. 9 - ZONE RR

OWNER / APPLICANT
GERALD WALDMAN REVOCABLE TRUST, 400 N. FLAGLER DR., WEST
PALM BEACH, FL 33401 (L-32062.F-043)

ENGINEER OF RECORD
W.L. MEEKINS, INC. — BILL MEEKINS, JR., 3101 RITCHIE ROAD,
FONTSVILLE, MD 20747 - 301-736-7115

SHEET TITLE
DETAILS

KEY MAP

SCALE
AS NOTED

DATUM: NAD 83 MD STATE PLANE (US FT) / NAVD 88

REVISIONS

NO.	DATE	DESCRIPTION
0	2026-09-30	CONCEPT SUBMISSION 1

PROFESSIONAL CERTIFICATION
I hereby certify that these documents were prepared or approved by me,
and that I am a duly licensed professional engineer under the laws of
the State of Maryland. License No. _____ Exp. _____

SEAL

CONCEPT SUBMISSION 1 — NOT SEALED
DATE 2026-09-30 JOB KEA-EH-2026
PREPARED WITH KRAUSE SPOTIAL ENGINE / CAD-PILOT

SHEET INDEX
C-600 COVER SHEET — BMP SUMMARY, DPE CHECKLIST AND NOTES
C-200 EXISTING CONDITIONS AND ENVIRONMENTAL FEATURES
C-300 SITE EROSION, GRADING AND PAVING PLAN
C-300 UTILITY, STREET LIGHT AND STREET TREE PLAN
C-400 STORMWATER MANAGEMENT CONCEPT AND DRAINAGE AREA MAP
C-500 SEDIMENT AND EROSION CONTROL PLAN
C-600 DETAILS