

ESTATES AT INDIAN HEAD — LOTS 1-6

200-205 ESTATES COURT, ACCOKEEK, MD 20607 · PLAT BOOK PM 228 PLAT 83 · TAX MAP 151 F-3 · WSSC 220SE01 · ELECTION DIST. 5 · COUNCIL DIST. 9 · ZONE RR
Stormwater management by Environmental Site Design to the Maximum Extent Practicable (MDE Design Manual Ch. 5; PGC Subtitle 32). Layout per the approved 2009 Street Tree & Lighting Plan, DPW&T 9399-2009-00.

PRINCE GEORGE'S COUNTY BMP SUMMARY TABLE — ESD BY POINT OF INVESTIGATION (A-15, C-9)

BMP	PRACTICE	MDE	LOCATION	OWNERSHIP / MAINT.	POI	DA SF	IMP SF	%	HSG	P_E IN	Rv	ESDv RE CF	ESDv PROV CF	Rev REQ CF	SURFACE SF	COORDINATES (NAD 83)
ESD-1	Micro-bioretentation	M-6	Lot 1	Private -- lot owner (maintenance agreement)	POI-1	19,999	4,500	22.5	C	1.2	0.253	505	505	55	525	N 367,417 E 1,311,143
ESD-2	Micro-bioretentation	M-6	Lot 2	Private -- lot owner (maintenance agreement)	POI-1	20,015	2,422	12.1	C	1.0	0.159	265	265	34	330	N 367,396 E 1,311,250
ESD-3	Micro-bioretentation	M-6	Lot 3	Private -- lot owner (maintenance agreement)	POI-1	20,051	3,008	15.0	C	1.0	0.185	309	309	40	386	N 367,378 E 1,311,388
ESD-4	Micro-bioretentation	M-6	Lot 4	Private -- lot owner (maintenance agreement)	POI-1	20,021	2,062	10.3	C	1.0	0.143	238	238	31	298	N 367,217 E 1,311,299
ESD-5	Micro-bioretentation	M-6	Lot 5	Private -- lot owner (maintenance agreement)	POI-1	20,235	2,489	12.3	C	1.0	0.161	271	272	35	340	N 367,373 E 1,311,371
ESD-6	Micro-bioretentation	M-6	Lot 6	Private -- lot owner (maintenance agreement)	POI-1	29,536	2,511	8.5	C	1.0	0.127	311	311	40	389	N 367,102 E 1,310,950
ESD-5	Roadside dry swales w/ check dams (999 LF)	M-8	Estates Ct R/W, both sides	Public -- DPJE	POI-1	36,041	21,216	58.9	C	2.0	0.580	3,483	5,992	226	3,995	N 367,342 E 1,311,097
SUBTOTAL POI-1					POI-1							5,382	7,892			
TOTAL 7 ESD practices													5,382	7,892	461	6,263

P. E from MDE Stormwater Design Manual (2000, Supp. 1 2009), Ch. 5, Table 5.3 — rainfall targets for ESD; HSG C governing. $R_v = 0.05 + 0.009-I$; $ESD_v = P \cdot E \cdot R_v / A / 12$; $Rev = S \cdot R_v / A / 12$ ($S = 0.13$ in, HSG C), met within ESDv. M-8 provided = 6 cf per ft (4-ft bottom, 6" ponding, 2.5' media at n 0.40)

SITE DATA

ITEM	DATA
Project	Estates at Indian Head, Lots 1-6 and Estates Court
Location	S. side of MD 210, 23600 ft NE of MD 210 / MD 373; 200-205 Estates Ct., Arcookeek 26701
Record	Plat Book PM 228 Plat 83 (final plat 5-08238); Tax Map 151 F-3; WSSC 200 220501
Accounts	3987636, 3987674, 3987698, 3987699, 3987708, 3987716
Owner	General Wadsworth Reversible Trust, L32062 F 0043
Zone / use	RR (no change) – 6 single-family detached dwellings
Tract	165,019 sq. record of 3788 ac) = plat 171,505 of 565 Outlot A (6.486 sf, C.151565 6.1555)
Public dedication	Estates Court 60' RW, 55,173 of record – rural open section, 24' pavement, cul-de-sac
Water / sewer	W-5 (WSSC) – main from Henrietta Dr via 30' WSSC, 15,739 ft WSS9 and prop. Lot 4 esmt
Watershed	Piscataway Creek, MD 012402303789; not Tier II; not CBFA; EMEA Zone X
Master plan	2013 Subregion 5 Master Plan & SMA; Planning Area 84; Council District 9; Election Dist. 5
Datum	NAD 83 MD State Plane (US IR); NAVD 88 (N-NCPPC 2-84); 2009 spot grades on WSSC datum

APPROVALS OF RECORD

CASE	STATUS
NRI-015-06	Prior approval – base work; updated NRI required
TCPI-018-06	Prior approval – base work
TCPI-016-09	Prior approval – base work; revision or new TCP per M-NCPPC
5-08238	Final plat, PM 228 @ 93 – recorded
DW5&T 9399-2009-08	Street tree & lighting plan (2009) – base layout; re-revision to current standards
L51799 F.399	30' WSSC easement (Outlot A, Lot 20) – recorded 2025

GENERAL NOTES


1. Boundary per recorded plat PM 228 @ 83; lot lines reproduce the plat to the second. A Maryland licensed surveyor shall confirm the boundary and the MD 210 ROW before technical plans.
2. Horizontal datum: Maryland State Plane NAD 83 (US Ft). Vertical datum: NAVD 98 (M-KNCPAC 2' contours). 2009 spot grades are on WSSC datum (+ NAVD 88 + 1.6 ft. to be confirmed by the field-run survey). DPWET permits NGVD 29 — the survey shall state the conversion.
3. The base layout will be the 2009 Street Tree & Lighting Plan (DPWET 93909-2009-00), resubmitted for review under current requirements; dwellings, side-lawn garages and courts, street trees and street lights. Lot 4 is front-lawn (garage) to the cul-de-sac to clear the WSSC easement.
4. Estates Court is a rural open section (DPWSET Std. 500.10 / 600.02 / 600.04); 24' pavement, shoulders, roadside swales; driveways cross the swale and cross the front-lawn / front-lawn sections.
5. Entrance to MD 210 (SHA) with 50' returns as the 2009 plan; SHA access permit and sight-distance analysis required. MD 210 auxiliary lanes shown for SHA review; ROW dedication may be required.
6. Water and sewer: WSSC mains from Henrietta Dr through the recorded 30' WSSC easement (L51799 F.399) and a 30' WSSC easement to be granted across Lot 4. Red circled lines in the easement dedication to be resolved with WSSC.
7. NEW SUBMITTAL (2026). Prior approvals NRI-015-06, TCP2-018-06, TCP2-016-09 and DPWET 93909-2009-00 are used as base work only and do not carry this submittal. Additional work: an updated/drafted NRI (draft with this submittal, approved copy before contract approval, Sec. 32.182(a)); a TCP2-016-09 revision or new TCP / letter of exemption as M-KNCPAC Environmental Planning determines; street tree and lighting plan re-reviewed to meet the requirements of Maryland State SWP by ESD to the NEP review and contract Submittal 32.
8. No streams, wetlands, floodplain, PMA or Chesapeake Bay Critical Area on the property (prior NRI-015-06; updated NRI required).
9. Contact Miss Utility (811) at least 48 hours before any excavation.

DPIE CONCEPT PLAN DESIGN REVIEW CHECKLIST (08/25/2021) — C = SHOWN · X = N/A · O = OUTSTANDING

A-1	REQUIREMENT	REF.	C/O	RESPONSE / WHERE SHOWN	SHEET
A-1	Plan is labeled as site Development Concept Plan (aka Concept Plan from MDPS 2013)			Every sheet is titled SITE DEVELOPMENT CONCEPT PLAN.	ALL
A-2	Printed sheet size does not exceed 30" x 42" and all sheets are plan sheet same size paper.	5.3.2	C	All sheets 24" x 36" (ARCH D).	ALL
A-3	A 5-inch, full-height open area is provided on the right-hand side of the drawing for County approval block.	2.2.1.0	C	5-inch full-height strip at the right edge, kept clear for DPW.	ALL
A-4	If more than 4 plan sheets; composite plan showing match lines and sheet numbers (scale not to exceed 1"=200'; key map on each plan sheet).	2.2.1.0	C	7 sheets: the whole site is on each plan sheet at one scale, so no match lines; key map in every title block.	ALL
A-5	Match lines have a minimum length of 4 inches and identify the matching sheet number.	2.2.1.M	X	No match lines – the entire site fits one viewport.	
A-6	Vicinity map at a minimum scale of 1"=2,000' with north arrow and scale, upper right hand corner of cover sheet.	2.2.1.B	C	Vicinity map at 1" = 2,000' with north arrow and bar scale, upper right.	C-000
A-7	A bar scale is provided on every sheet.		C	Graphic bar scale in every plan viewport.	C-200
A-8	Three grid ticks are provided as described in the manual.	2.2.1.E	C	Three State Plane grid ticks with N/E values on each plan.	ALL
A-9	Horizontal (MD Coordinate System, NAD 83) and vertical (NGVD 29 preferred) datum is stated on the plan.		C	Horizontal Maryland State Plane, NAD 83 (EPSG 2248); UTM; vertical NAD 83 (MD MNCPC v.1-2009) and grades WSSC datum used. NGVD 29 conversions to be stated by the field surveyor.	ALL
A-10	General notes about the project are provided.		C	General notes on the cover sheet.	C-000
A-11	The entire property shown at a maximum plan scale of 1 inch = 50 feet (extended) within the plan.	5.3.2	C	Entire property at 1" = 30'.	C-200
A-12	All existing structures and site features including cultural features, historic sites (and easements), and any visible foundations or ruins are shown on the plan.	5.3.2	C	Existing structures, adjoining houses, fences, sheds, well, easements of record shown; no historic sites or ruins.	C-100
A-13	Topographic contours at maximum 2 foot interval, extending at least 100 feet beyond the property.	32-102	C	M-MNCPC 2-ft contours, 100 feet beyond the property.	C-100
A-14	All existing utilities and utility easements are shown.		C	WSSC easement, L51399 F 399 and the proposed L04 WSSC easement; public utility easements along the frontage; existing mains in Henrietta Dr noted (sizes to verify on WSSC 2205561).	C-300
A-15	The County BMP Summary Table is provided. Preferred location is on the cover sheet.	5.3.1	C	County BMP Summary Table, 7 pages.	C-000
B-1	Banks of all regulated streams or a centerline if the banks are too close together to graphically show.	MDE 5.7	X	No streams on site. New submittal: prior NR015-016 (with TCP-016-06, TCP-016-09) is base work only. Updated/revised NR01 to be provided in draft with this submission, approved copy required before concept approval (see TCP-18210a).	
B-2	Location of stream and stream criteria, order and enhanced buffers per MNCPC and SDC criteria.	MDE 5.7	X	No streams, no stream buffers.	
B-3	Location of wetlands and/or wetlands of special state concern and appropriate wetland buffers.	MDE 5.7	X	No wetlands on or 100-yd flood plain (DNK, NR).	
B-4	Delination of the 100-year floodplain, per Technical-gram 04a-2020.	MDE 5.7	X	FEMA Zone X; no 100-yd floodplain (or within 100 ft).	
B-5	Location of steep slopes (15% and greater) clearly shown on the plan and in the legend.	M-MNCPC	C	Slopes 15-25%; 2.757 sf; >25% 520 sf – shown and in the legend.	C-100
B-6	The Primary Management Area is delineated.	MDE 5.7	X	No PMA on the property.	
B-7	Existing woodland is delineated on the property.	MDE 5.7	X	No woodland conservation shown on this concept. Prior NR015-016 / TCP2-016-09 are base work only; woodland per the updated NR, with a TCP2 revision or new TCP2 / form of exemption as M-MNCPC determines.	C-100
B-8	Existing environmental features extend off the property 100 feet in all directions.	MNCPC	C	Environmental layers drawn 100 ft beyond the property.	C-100
B-9	Soils types and soil boundaries from USDA NRCS Soil Survey (Dec. 2009) or later.		C	Soil types and boundaries from USDA NRCS (PGAtlas Soil layer): CwE (HSG C); UdgF (HSG --); BaE (HSG C); Bw (HSG C).	C-100
B-10	Plan notes identify TMDL watershed (sediment, nitrogen, phosphorus) and Tier I waters/watershed.		C	C Chesapeake Bay TMDL (nitrogen, phosphorus, sediment) impacts; MD 12-021-watershed 02140200798, Piscataway Creek 0214020193. Tier II: no.	
B-11	Highly erodible and Tier I waters/watershed.		C	Beltville sill (loam C 0.37) is highly erodible where slopes are 15% or more; those areas are stabilized within 3 days.	C-000
B-12	Springs and seeps noted.	MDE 5.7	X	None observed or mapped.	
B-13	Bedrock and Marlboro Clay outcrops noted.	MDE 5.7	X	No bedrock or Marlboro clay mapped (PGAtlas); geotechnical reports to confirm (E-2).	
B-14	Chesapeake Bay Critical Areas delineated.	MDE 5.7	X	Not in the Chesapeake Bay Critical Area.	

CHECKLIST (CONT.)

C#	REQUIREMENT	REF.	C/Y/O	RESPONSE / WHERE SHOWN	SHEET
C-1	Project layout is shown, including roads, buildings, parking, sidewalk and other improvements and associated grading.	C-32-182	C	Estates Court, 6 dwellings, driveways and courts, entrance at MD 210, grading.	C-200
C-2	Preliminary locations of ESD and structural stormwater practices; grading for devices where slopes exceed 15%.	C-32-182	C	7 ESD practices (micro-bioretentation M-6 per lot; roadside dry swales M-8).	C-200
C-3	Preliminary locations of storm drain inlets and culverts; entrance and outfall structures located beyond project limits (assessments may be required).	5.2.4.4.2B / C-32-162.A.6	C	Open section – no inlets; 6 driveway culverts (15' RCP) with end sections; swales outfall at the entrance to the MD 210 roadside ditch (SHA).	C-400
C-4	Limit of Disturbance shown for all site work, incl. water, sewer, storm drain, SWM, road improvements, sediment control, stockpile.	C-32-182	C	LOD 22.317' ft incl. mains, easement work off site, sediment control and stockpile.	C-500
C-5	Existing easements shown and any required offsite proposed easement.		C	Confirmed WSSC easement (Outlet A, Lot 20) and proposed Lot 4 WSSC easement; private SWM improvements over ESD practices.	C-300
C-6	Locations, names and widths of existing and ultimate Dr and way of adjacent streets and alleys; public vs. private note.		C	MD 210 (variable RW, SHA), Estates Ct (60' public), 10' easement Dr and smaller Dr (public), 30' RW in common L10142 F725 (private).	C-200
C-7	Existing and proposed water wet and septic field locations are shown.		C	C No wells or septic proposed (public water and sewer). Existing well on Parcel 19 (1506B Indian Head Hwy), off site, shown.	C-100
C-8	Proposed public dedication area including any proposed parkland is shown and is labeled.		C	Estates Court public dedication 36,041 sf (plat PM 228 @ 83); no parkland.	C-200
C-9	Point(s) of investigation shown. ESDv computations and BMP Summary Table broken out to show ESD Required is Provided within each POI.		C	1 POI(s); ESDv required vs. provided tabulated per POI.	C-400
C-10	The ultimate 100-year stormwater overflow path is shown throughout the site using flow arrows.		C	100-y overflow arrows from every practice to its POI 131.	C-400
C-11	Drainage areas to each device, offsite drainage onto the site, and to site outfalls; diverted areas analysed for no increase in 100-yr discharge.		C	C Drainage area to each practice; off-site area onto the site @ 49 ac; no diversion between POIs.	C-400
C-12	Where grading blocks a drainage course, reporting limits before and after grading are shown.		X	No fill across a drainage course.	
D-1	Report addresses natural resource protection, natural flow patterns, impervious reduction, ESC integration, ESD planning to the MEP.	MDE 5.11	O	SWM concept narrative (ESD to the MEP, flow patterns, ESC integration) – to accompany the plans.	
D-2	If in the Chesapeake Bay Critical Area, discussion of how requirements are met; preliminary computations.		X	Not in the Chesapeake Bay Critical Area.	
D-3	Outfalls located outside the site, if existing storm drain or 100-yr floodplain; otherwise the discharge area is described.		O	Narrative: outfalls at the POIs; swales discharge to the MD 210 roadside ditch; describe receiving areas.	
D-4	Stabilization at downstream outfall and upstream inflow evaluated; measures against gully formation discussed.		O	Narrative: outfall stabilization (level spreaders / riprap) at each POI.	
D-5	Photographs of the stream at the downstream outfall and upstream property line; eroded slopes.		X	No stream at the outfalls.	
D-6	If outfall is to an existing SWM facility, its capacity for the added area and flow is documented.		X	No existing SWM facility receives the site.	
D-7	If rezoned to higher imperviousness, effects on downstream properties analysed.		X	No rezoning (RR remains RR).	
D-8	Floodplain ordinance discussion (drainage courses, buildings within 25 ft of floodplain, dams, downstream crossings).		X	No floodplain or drainage course on or downstream within the site; no dams.	
D-9	If a waiver of water quality or quantity is requested, the basis is provided.		X	No waiver requested.	
D-10	Computations: ESDv/EDW required and provided; proposed runoff is described; runoff: downstream storm drain analysis with 30-yr return if inadequate.	5.3.3 / 5.2.6.1 / 5.2.4.2 / TG 002-2019	O	ESDv computations are on the cover; 100-yr existing/proposed runoff at each POI and downstream analysis to follow in the report.	
E-1	A Geotechnical Report for SWM is provided to support concept development and feasibility.	5.3.3 / TG 004-2018	O	Geotechnical report for SWM (borings and Sec. 32-131 infiltration tests at each practice) – to be submitted.	
E-2	Geotechnical Report addresses Marlboro and Christina clays, sulfidic and diatomaceous soils.	5.3.3 / TG 005-2018 / PGSCD I-8	O	Geotechnical report to address Marlboro/Christina clays, sulfidic and diatomaceous soils.	
E-3	Affidavit of Public Information mailing is provided with second submission.	C-32-182(g)	O	Affidavit of the adjacent-owner mailing (within 7 days of submission) – with second submission.	
E-4	A draft Natural Resource Inventory is provided with initial submission (approved copy required prior to approval).	C-32-182(a)	O	Not submitted: prior NRI-015 (b/w TCPI 018-06, TCPI-016-09) is base work only. Updated/revised NRI to be provided in draft with this submission; approved copy required before concept approval (Sec. 32-350(a)).	

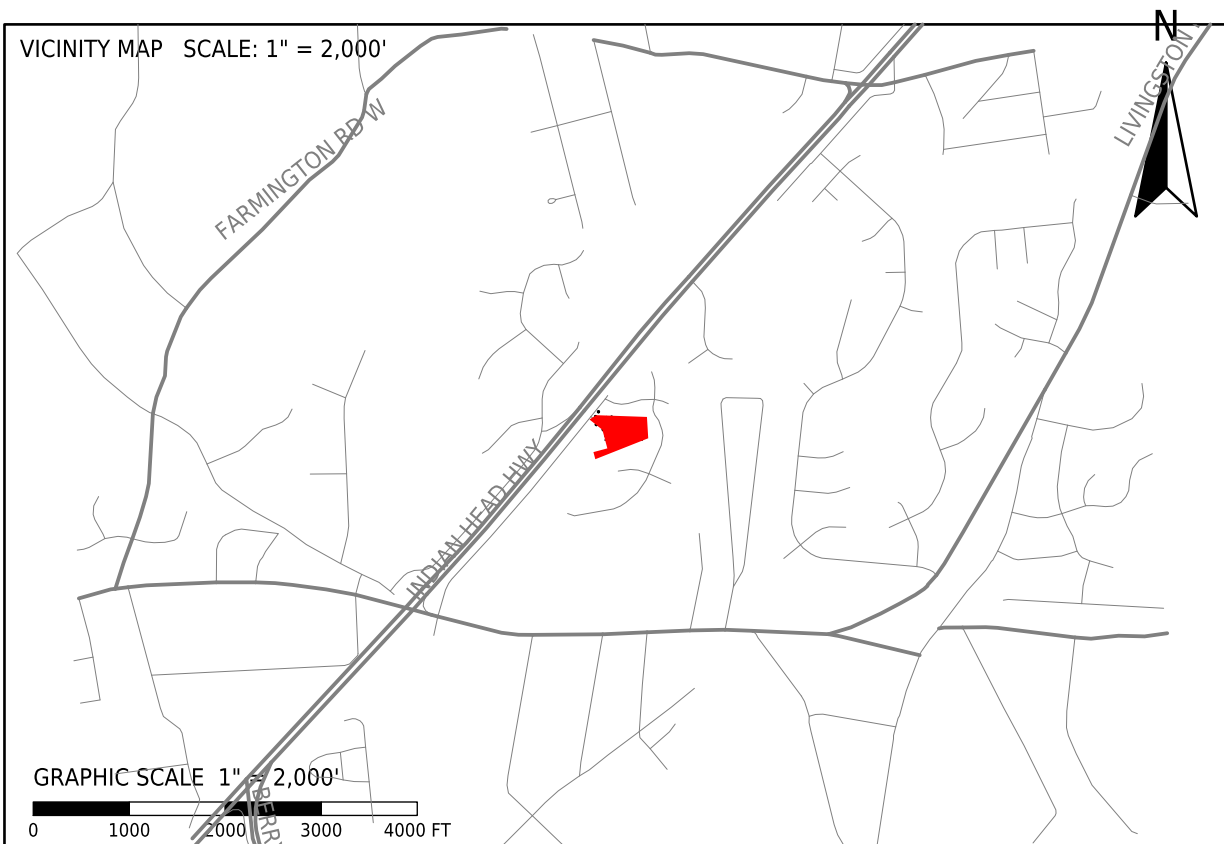

PLAN TYPE
SITE DEVELOPMENT CONCEPT PLAN


PROJECT
ESTATES AT INDIAN HEAD — LOTS 1-6
200-205 ESTATES COURT, ACCOKEEK, MD 20607
PLAT BOOK PM 228 PLAT 83 · TAX MAP 151 F-3 · WSSC
2205E01
ELECTION DIST. 5 · COUNCIL DIST. 9 · ZONE RR

OWNER / APPLICANT
GERALD WALDMAN REVOCABLE TRUST, 400 N. FLAGLER DR., WES
PALM BEACH, FL 33401 (L.32062 F.043)

ENGINEER OF RECORD
W.L. MEEKINS, INC. — BILL MEEKINS, JR., 3101 RITCHIE ROAD,
FORESTVILLE, MD 20747 · 301-736-7115

SHEET TITLE
COVER SHEET — BMP SUMMARY, DPIE
CHECKLIST AND NOTES

KEY MAP

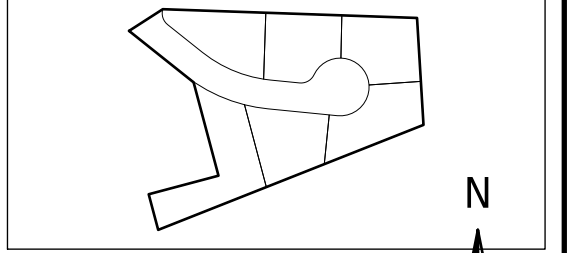

SCALE
AS NOTED

DATUM: NAD 83 MD STATE PLANE (US FT) / NAVD 88

REVISIONS		
NO.	DATE	DESCRIPTION
0	2026-09-30	CONCEPT SUBMISSION 1

PROFESSIONAL CERTIFICATION
I hereby certify that these documents were prepared or approved by me,
and that I am a duly licensed professional engineer under the laws of
the State of California.



CONCEPT SUBMISSION 1 — NOT SEALED
DATE 2026-09-30 · JOB KEA-EIH-2026
PREPARED WITH KEA'S CRATIAL ENGINE LOAD PLOT

SHEET INDEX

- C-100 COVER SHEET — BRP SUMMARY, DME CHECKLIST AND NOTES
- C-100 EXISTING CONDITIONS AND ENVIRONMENTAL FEATURES
- C-200 SITE LAYOUT, GRADING AND PAVING PLAN
- C-300 UTILITY, STREET LIGHT AND STREET TREE PLAN
- C-400 STORMWATER MANAGEMENT CONCEPT AND DRAINAGE AREA MAP
- C-500 SEDIMENT AND EROSION CONTROL PLAN
- C-600 DETAILS


RESERVED FOR PRINCE GEORGE'S COUNTY DPIE APPROVAL
5" x 3" — KEEP BLANK (ePLAN 5" RIGHT MARGIN, CHECKLIST A-3)

C-000

EXISTING CONDITIONS AND ENVIRONMENTAL FEATURES

LEGEND

- Boundary of record (plat PM 228 @ 53)
- Lot line
- Adjoining property
- Existing contour, 10-ft (NAVD 88)
- Existing contour, 2-ft
- Existing edge of road
- Existing right-of-way
- Slopes 15-25% (dots) / > 25% (hatch)
- Soil boundary (USDA NRCS)
- Easement

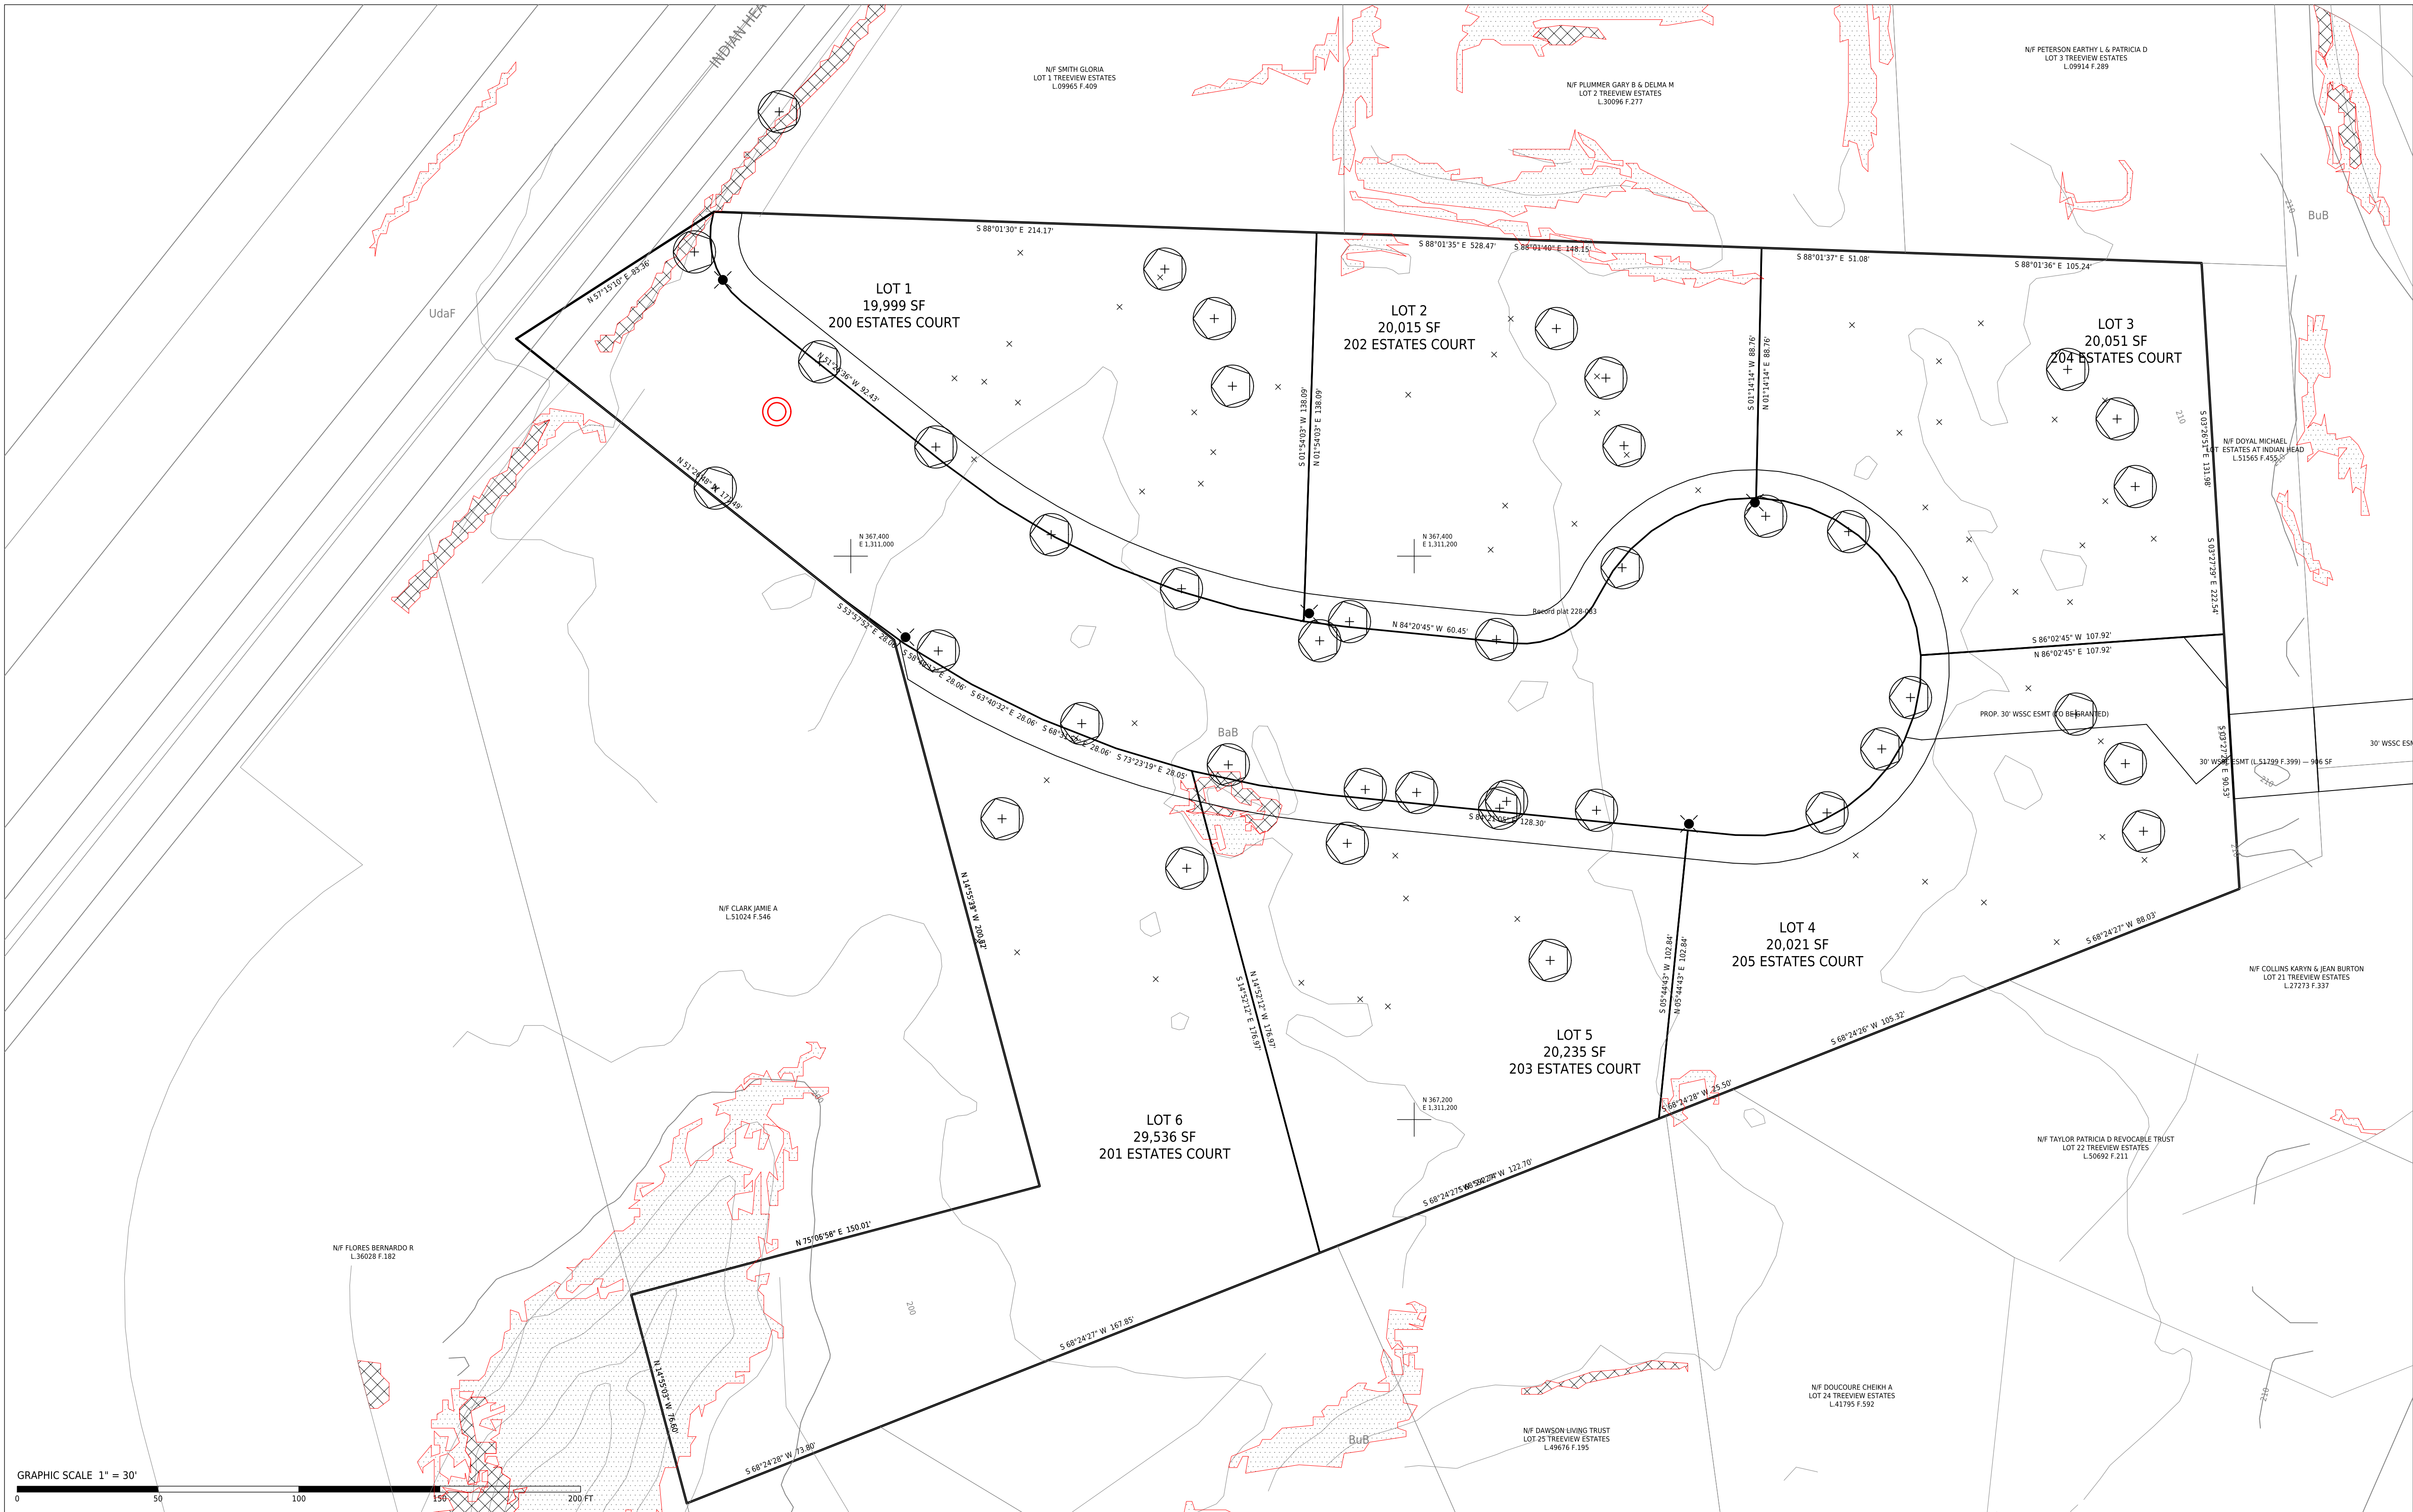

SOILS (USDA NRCS)

SYMBOL	NAME	HSG	K	HIGHLY ERODIBLE
CwE	Croom-Marr complex, 15 to 25 percent slopes	C	.15	NO
UdaF	Udorthents, highway, 0 to 65 percent slopes	—	—	NO
BaB	Beltsville silt loam, 2 to 5 percent slopes	C	.37	YES (on slopes >= 15%)
BuB	Beltsville-Urban land complex, 0 to 5 percent slopes	C	.37	YES (on slopes >= 15%)

ENVIRONMENTAL FEATURES — DPIE CHECKLIST B

ITEM	CX/D	FINDING
B-1	X	No streams on site. New submittal: prior NRI-015-06 (with TCP1-018-06, TCP2-016-09) is base work only. Updated/revised NRI to be provided in draft with this submission; approved copy required before concept approval (Sec. 32.182(a)).
B-2	X	No streams, no stream buffers.
B-3	X	No wetlands on or within 100 ft (DNR: NRI).
B-4	X	FEMA Zone X: no 100-yr floodplain on or within 100 ft.
B-5	C	Slopes 15-25%: 2,757 sf; >25%: 520 sf — shown and in the legend.
B-6	X	No PMA on the property.
B-7	C	No woodland conservation shown on this concept. Prior NRI-015-06 / TCP2-016-09 are base work only; woodland per the updated NRI, with a TCP2 revision or new TCP / letter of exemption as M-NCPPC determines.
B-8	C	Environmental layers drawn 100 ft beyond the property.
B-9	C	Soil types and boundaries from USDA NRCS (PGAtlas Soil layer): CwE (HSG C); UdaF (HSG C); BaB (HSG C); BuB (HSG C).
B-10	C	Chesapeake Bay TMDL (nitrogen, phosphorus, sediment) applies; MD 12-ditch watershed 021402030799; Piscataway Creek (02140203). Tier II: no.
B-11	C	Beltsville silt loam (K 0.37) is highly erodible where slopes are 15% or more; those areas are stabilized within 3 days.
B-12	X	None observed or mapped.
B-13	X	No bedrock or Marlboro clay mapped (PGAtlas); geotechnical report to confirm (E-2).
B-14	X	Not in the Chesapeake Bay Critical Area.


RESERVED FOR PRINCE GEORGE'S COUNTY DPIE APPROVAL
5" x 3" — KEEP BLANK (UPLAN 5" RIGHT MARGIN, CHECKLIST A-3)

PLAN TYPE
SITE DEVELOPMENT CONCEPT PLAN

PROJECT:
ESTATES AT INDIAN HEAD — LOTS 1-6
200-205 ESTATES COURT, ACCOKEEK, MD 20607
PLAT BOOK PM 228 PLAT 63 — TAX MAP 153 F-3 — WSSC
2205E01
ELECTION DIST. 5 — COUNCIL DIST. 9 — ZONE RA
OWNER / APPLICANT:
GERALD WALDMAN REVOCABLE TRUST, 400 N. FLAGLER DR., WEST PALM BEACH, FL 33401 (L32062 F.043)
ENGINEER OF RECORD:
W.L. MEEKINS, INC. — BILL MEEKINS, JR., 3101 RITCHIE ROAD, FORESTVILLE, MD 20747-301-736-7115

SHEET TITLE
EXISTING CONDITIONS AND ENVIRONMENTAL FEATURES


KEY MAP

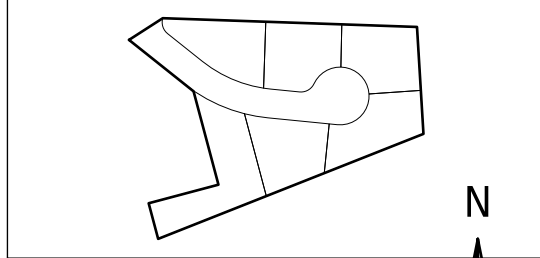

SCALE
1" = 30'
DATUM: NAD 83 MD STATE PLANE (US FT) / NAVD 88


REVISIONS	NO.	DATE	DESCRIPTION
0	2026-09-30		CONCEPT SUBMISSION 1

PROFESSIONAL CERTIFICATION
I hereby certify that these documents were prepared or approved by me, and that I am a duly licensed professional engineer under the laws of the State of Maryland. License No. _____ Exp. _____

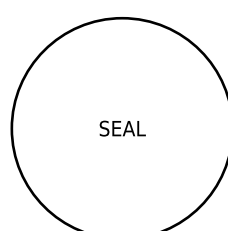


CONCEPT SUBMISSION 1 — NOT SEALED
DATE 2026-09-30 — JOB KEA-EIH-2026
PREPARED WITH SCALE SPATIAL ENGINE / C-00-PL01

SHEET INDEX
C-000 COVER SHEET — BMP SUMMARY, DPIE CHECKLIST AND NOTES
C-100 EXISTING CONDITIONS AND ENVIRONMENTAL FEATURES
C-100 SITE LAYOUT, GRADING AND DRIVING PLAN
C-300 UTILITY, STREET LIGHT AND STREET TREE PLAN
C-600 STORMWATER MANAGEMENT CONCEPT AND DRAINAGE AREA MAP
C-600 SEDIMENT AND EROSION CONTROL PLAN
C-600 DETAILS

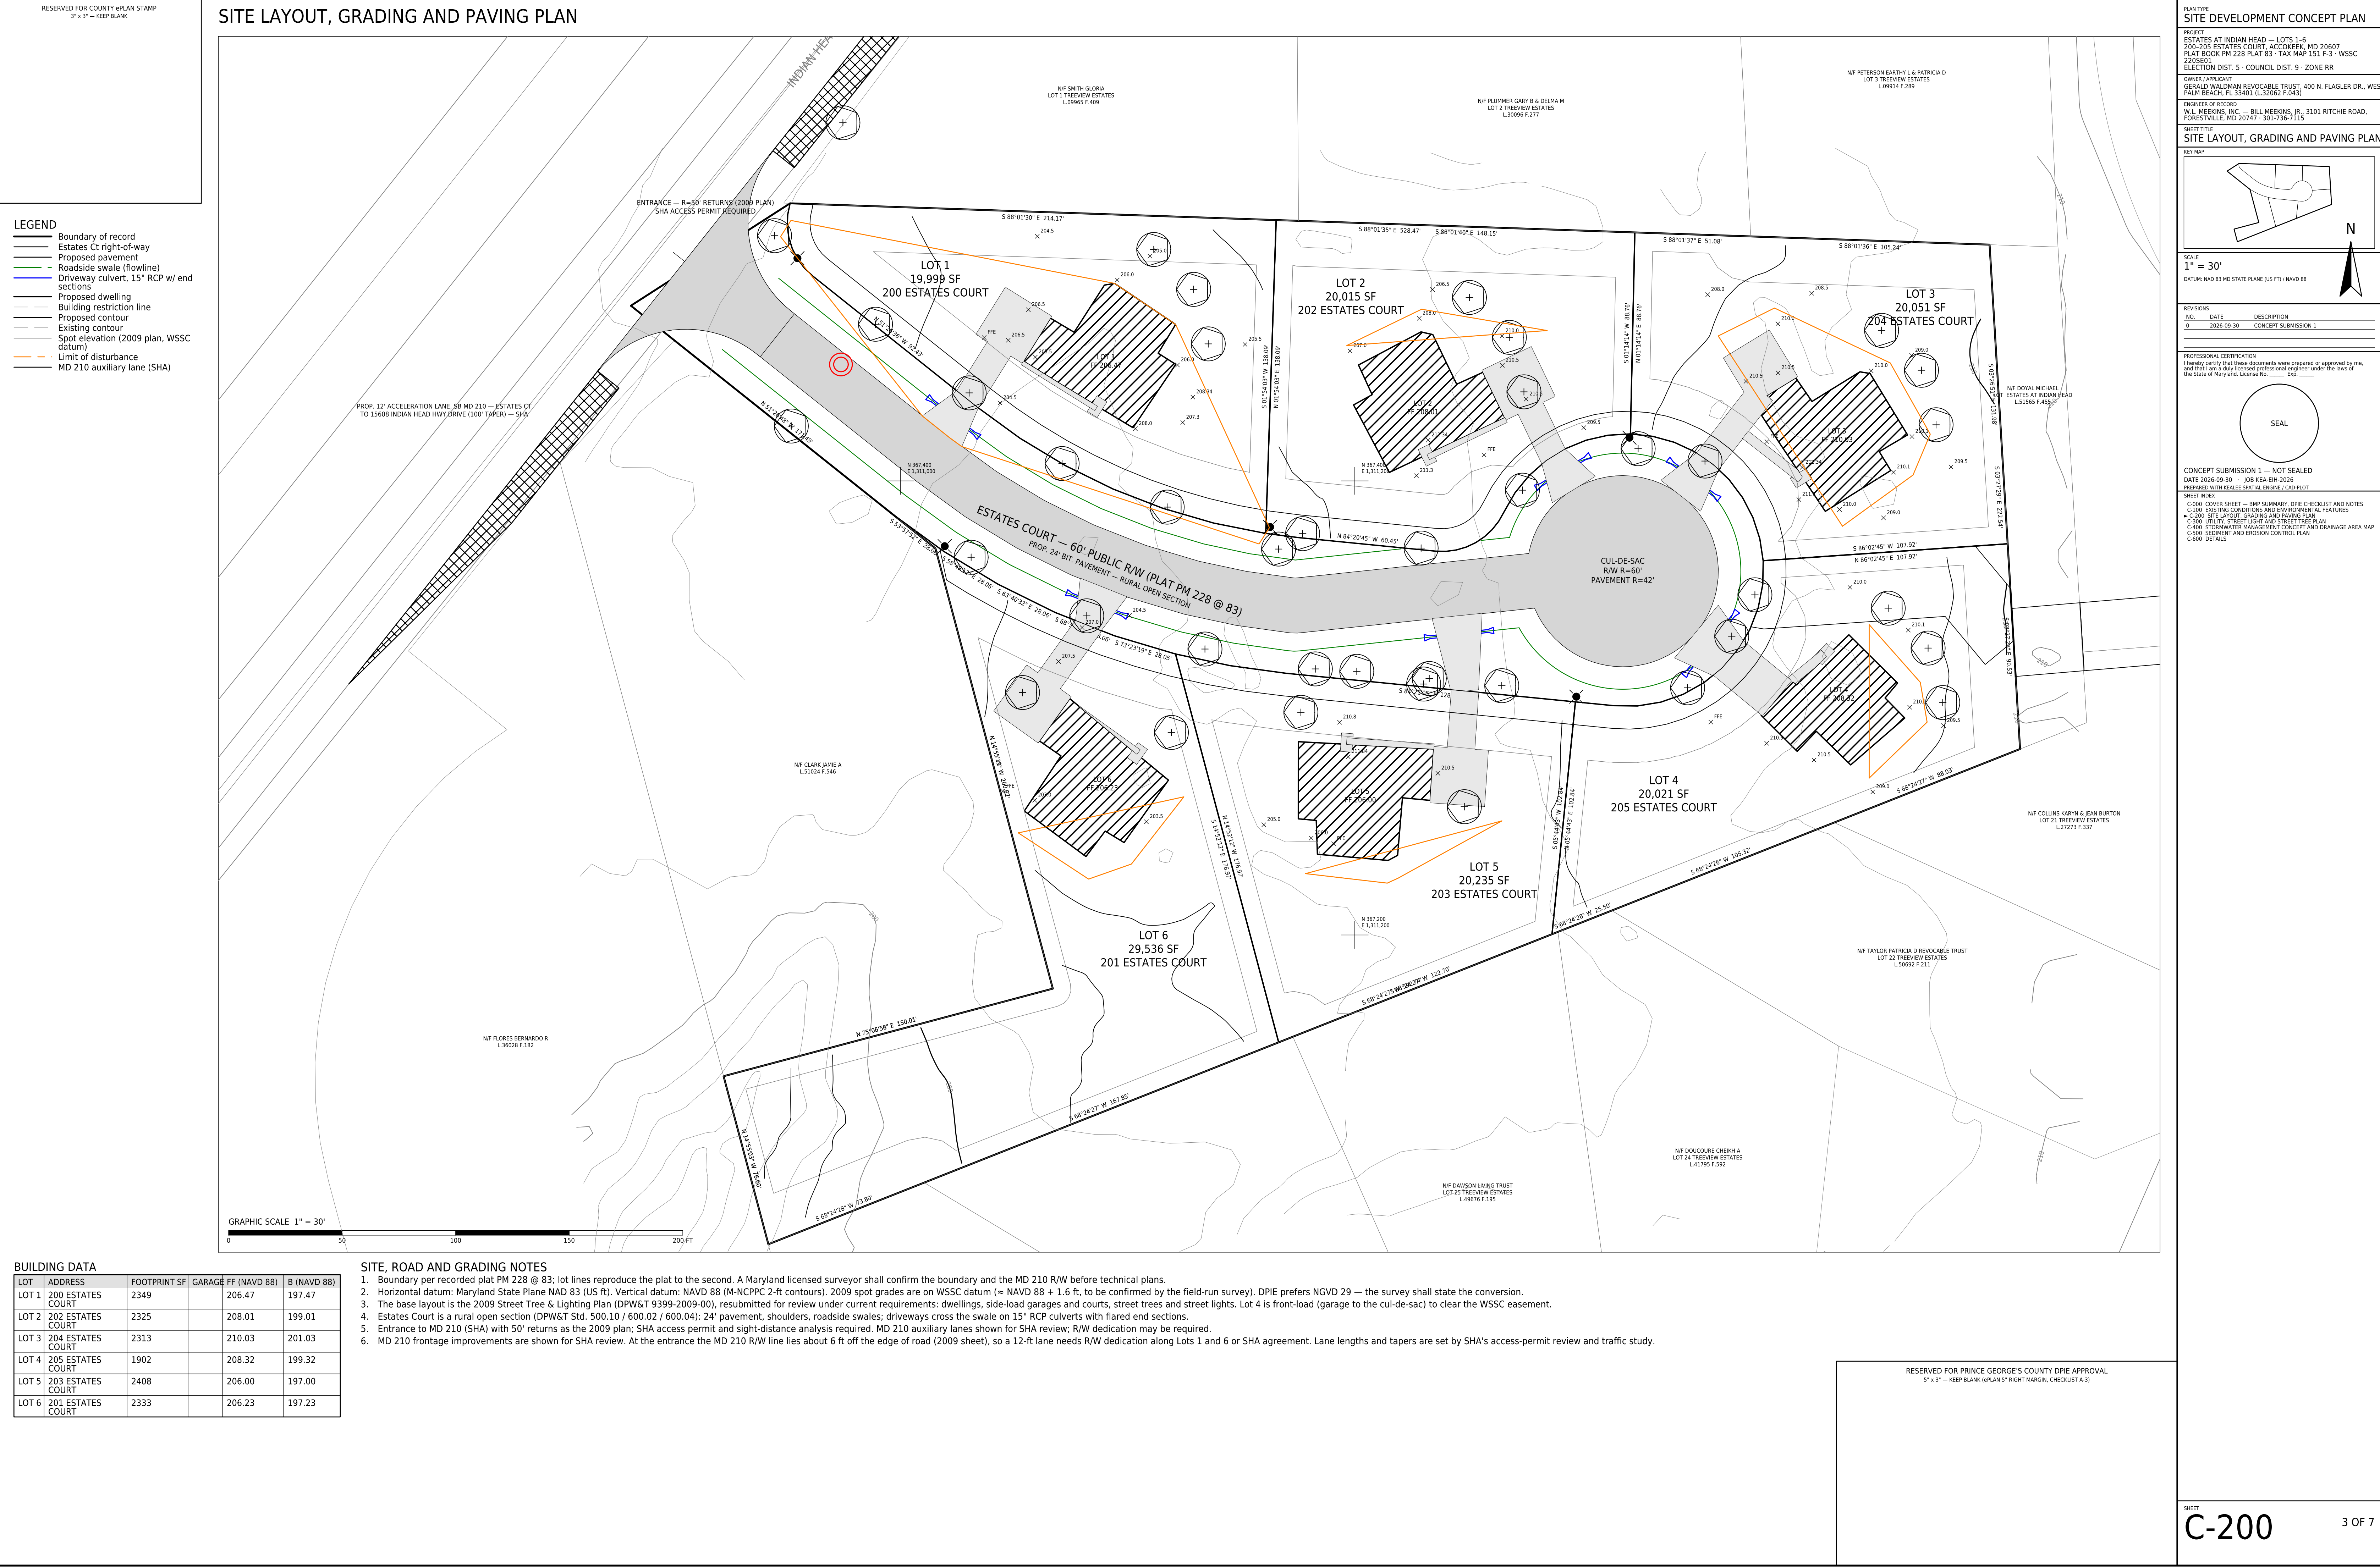

UTILITY, STREET LIGHT AND STREET TREE PLAN

- Proposed 8" water main
- Proposed 8" sanitary sewer
- House connection
- - - WSSC easement (recorded / proposed)
- Street tree — Red Maple (2009 plan)
- Street light (2009 plan)

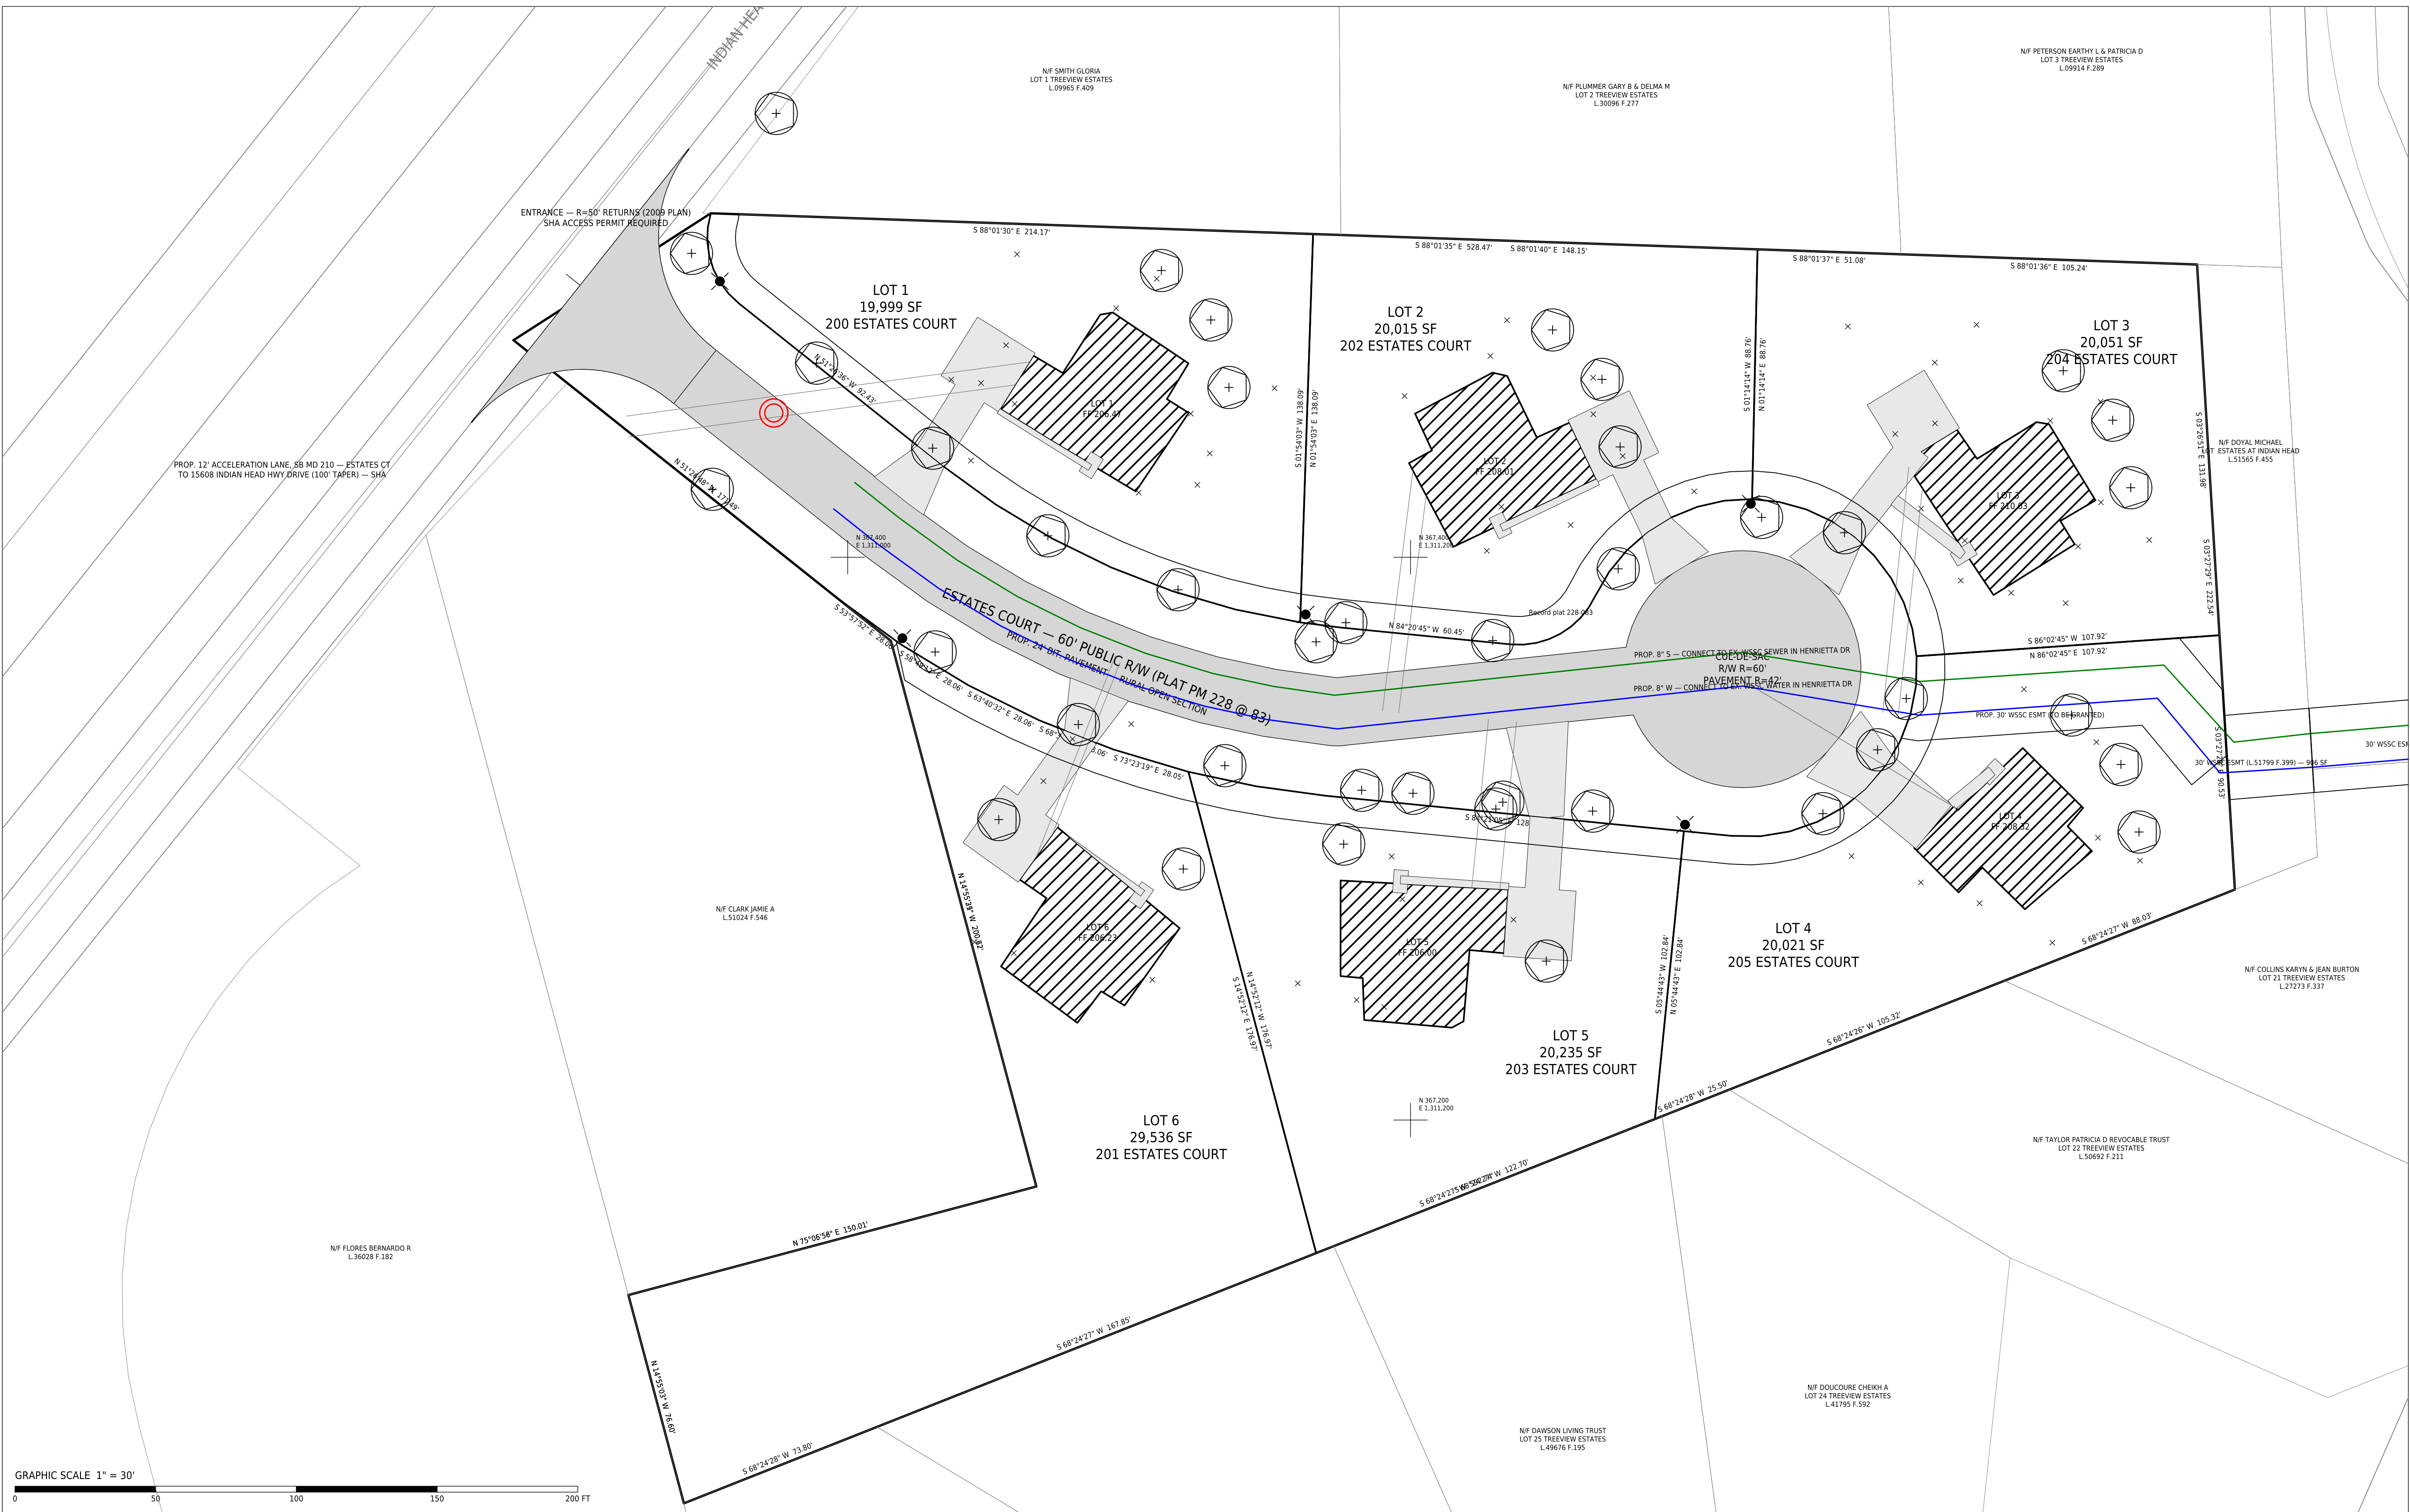


SYMBOL	QTY	ITEM	SIZE / TYPE	STANDARD
TREE	16	ACER RUBRUM — RED MAPLE	2 1/2" - 3" CAL., B&B	DPW&T 600.02 / 600.04
LIGHT	5	STREET LIGHT (SMECO)	100 W HPS COLONIAL POST-TOSS, TYPE IV, BLACK FINGERGLASS	DPW&T 500.10

1. Water and sewer by WSSC (W-3 / 5-3); Mains from the existing WSSC mains in Henrietta Drive through the recorded 30' WSSC easement (L51799 f.399, Outlot A and Lot 20) and a 30' WSSC easement to be granted across Lot 4 along the Lot 3/4 line.
2. Sizes and inverts of the Henrietta Drive mains to be verified on WSSC 200' sheet 220S01 before technical design.
3. Street lights and street trees follow the approved 2009 Street Tree & Lighting Plan (DPW&T 9399-2009; light permit 09.093999); electric service by SMECO.
4. Keep street trees 10 ft from water meters and storm structures and 15 ft from street lights (DPW&T 600.02).
5. Contact Miss Utility (811) at least 48 hours before excavation.

RESERVED FOR PRINCE GEORGE'S COUNTY DPIE APPROVAL
5" x 3" — KEEP BLANK (ePLAN 5" RIGHT MARGIN, CHECKLIST A-3)

STORMWATER MANAGEMENT CONCEPT AND DRAINAGE AREA MAP

- LEGEND
- ESD practice — micro-bioretenction (M-6)
 - Roadside dry swale (M-8)
 - Drainage area to practice
 - Off-site area draining onto site
 - 100-yr overflow path
 - Point of investigation
 - Driveway culvert

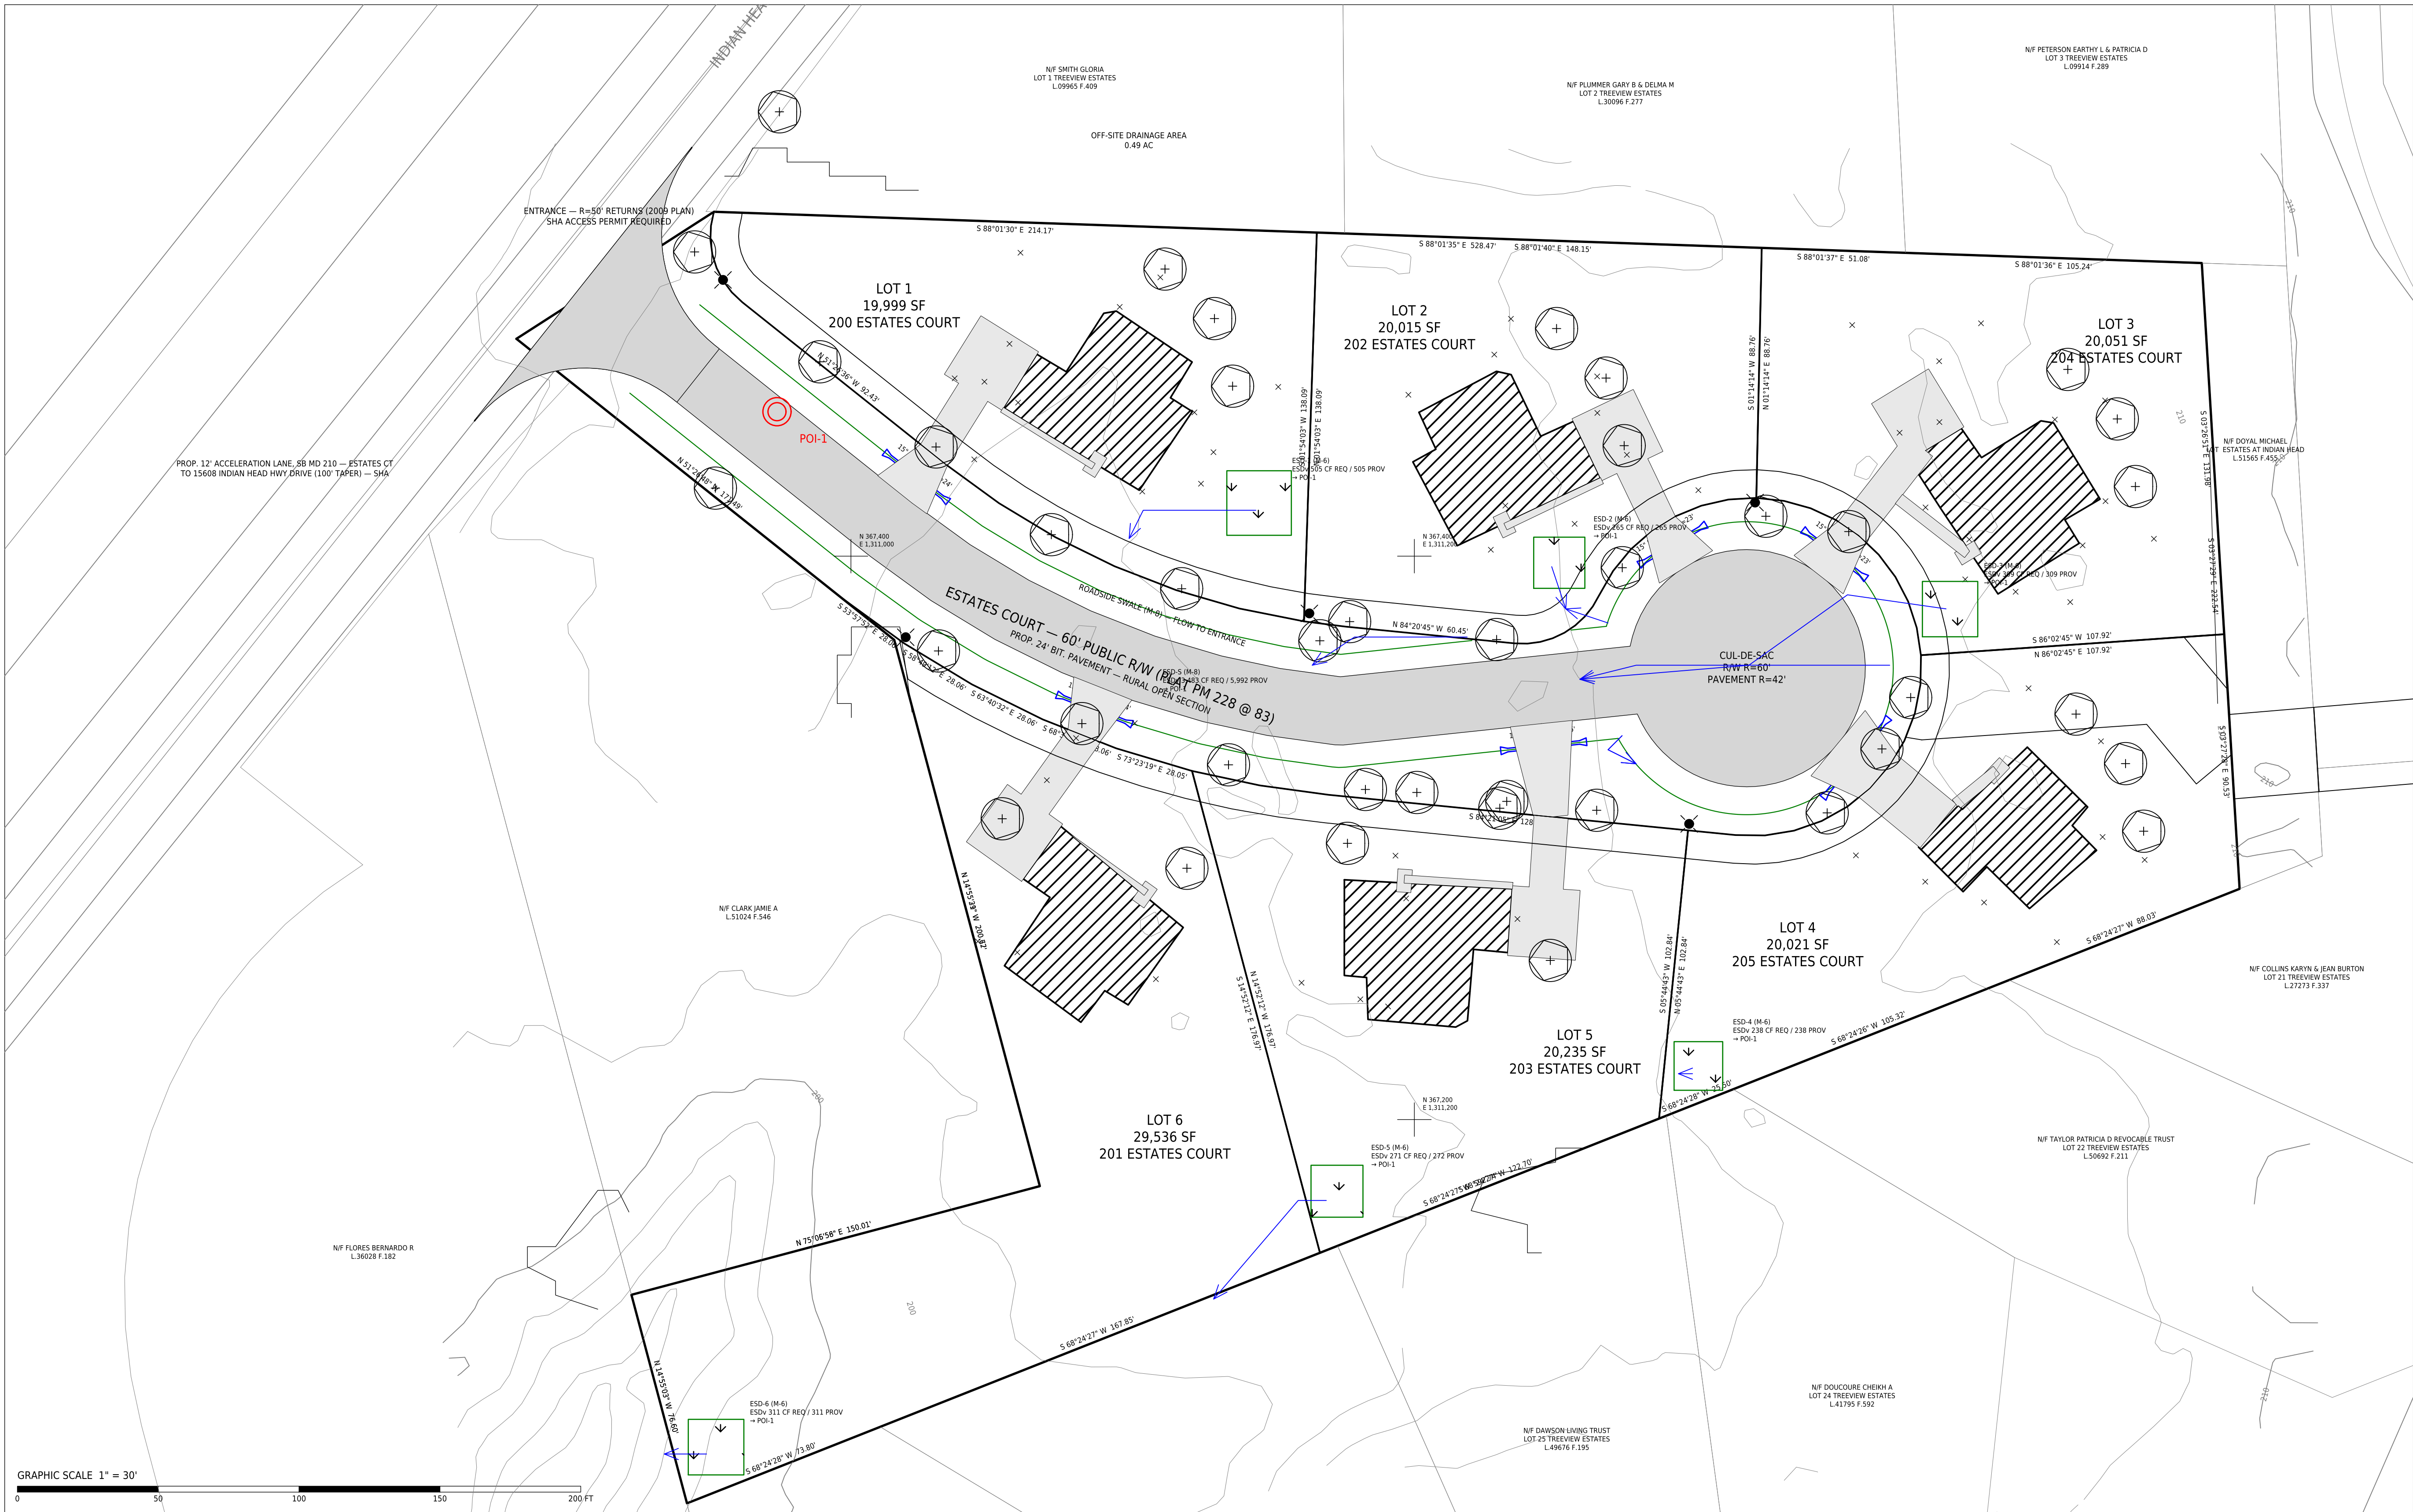

ESD PER PRACTICE (FULL TABLE ON C-000)

BMP	MDE	LOCATION	POI	DA SF	%I	P_E	ESDv REQ	ESDv PROV
ESD-1	M-6	Lot 1	POI-1	19,999	22.5	1.2	505	505
ESD-2	M-6	Lot 2	POI-1	20,015	12.1	1.0	265	265
ESD-3	M-6	Lot 3	POI-1	20,051	15.0	1.0	309	309
ESD-4	M-6	Lot 4	POI-1	20,021	10.3	1.0	238	238
ESD-5	M-6	Lot 5	POI-1	20,235	12.3	1.0	271	272
ESD-6	M-6	Lot 6	POI-1	29,536	8.5	1.0	311	311
ESD-5	M-8	Estates Ct R/W, both sides	POI-1	36,041	58.9	2.0	3,483	5,992

POINTS OF INVESTIGATION (C-9)

POI	LOCATION	SHARE	ESDv REQ	ESDv PROV
POI-1	N 367,451 E 1,310,974	100%	5,382	7,892

SWM NOTES

- SWM by Environmental Site Design to the MEP (Md. Stormwater Management Act of 2007; MDE Design Manual Ch. 5; PCG Subtitle 32). Target rainfall P_E from MDE Table 5.3 for HSG C at each drainage area's imperviousness.
- Each lot drains to one micro-bioretenction cell (M-6): 12-in max. ponding; 2.5-ft filter media; underdrain to a stable outfall. Estates Court drains to roadside dry swales (M-8) with check dams.
- Rooftop and non-rooftop disconnection (N-1, N-2) to be credited at technical design. Infiltration credit only where Sec. 32-131 borings show ≥ 0.52 in/hr.
- Private ESD practices: maintenance agreement recorded before permit; public swales in the R/W maintained by DPIE.
- D8 flow routing on a 5-ft surface interpolated from the existing 2-ft contours; exit points clustered at 120 ft; POIs carrying under 4% of the site omitted. Concept-level — reset from the field-run survey.

PLAN TYPE
SITE DEVELOPMENT CONCEPT PLAN


PROJECT
ESTATES AT INDIAN HEAD — LOTS 1-6
200-205 ESTATES COURT, ACCOKEEK, MD 20607
PLAT BOOK PW 228 PLAT 83 TAX MAP 151 F-3 - WSSC
220501
ELECTION DIST. 5 COUNCIL DIST. 9 ZONE RR

OWNER / APPLICANT
GERALD WALDMAN REVOCABLE TRUST, 400 N. FLAGLER DR., WEST PALM BEACH, FL 33403 (L32062 F.043)

ENGINEER OF RECORD
W.L. MECKINS, INC. — BILL MECKINS, JR., 3101 RITCHIE ROAD, FORESTVILLE, MD 20747 301-736-7115

SHEET TITLE
STORMWATER MANAGEMENT CONCEPT AND DRAINAGE AREA MAP

KEY MAP

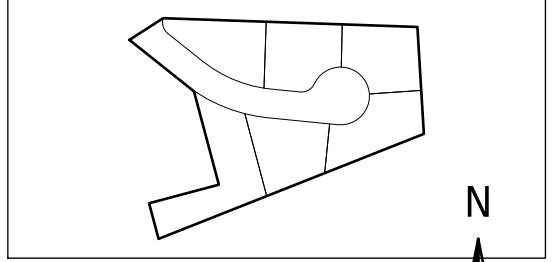

SCALE
1" = 30'
DATUM: NAD 83 MD STATE PLANE (US FT) / NAD 83

REVISIONS		
NO.	DATE	DESCRIPTION
0	2026-09-30	CONCEPT SUBMISSION 1

PROFESSIONAL CERTIFICATION
I hereby certify that these documents were prepared or approved by me, and that I am a duly licensed professional engineer under the laws of the State of Maryland. License No. _____ E.O. _____



CONCEPT SUBMISSION 1 — NOT SEALED

DATE 2026-09-30 JOB KEA-EH-2026

PREPARED WITH SCALE 3/32"=1' (US FT) / 1:3840

SHEET INDEX

C-000 COVER SHEET — BMP SUMMARY, DPIE CHECKLIST AND NOTES

C-100 EXISTING CONDITIONS AND ENVIRONMENTAL FEATURES

C-200 SITE LAYOUT, GRADING AND PAVING PLAN


C-300 UTILITY, STREET LIGHT AND STREET TREE PLAN

C-400 STORMWATER MANAGEMENT CONCEPT AND DRAINAGE AREA MAP




C-500 SEDIMENT AND EROSION CONTROL PLAN

C-600 DETAILS


RESERVED FOR PRINCE GEORGE'S COUNTY DPIE APPROVAL
3" x 3" — KEEP BLANK (UPAN 5 RIGHT MARGIN, CHECKLIST A-3)

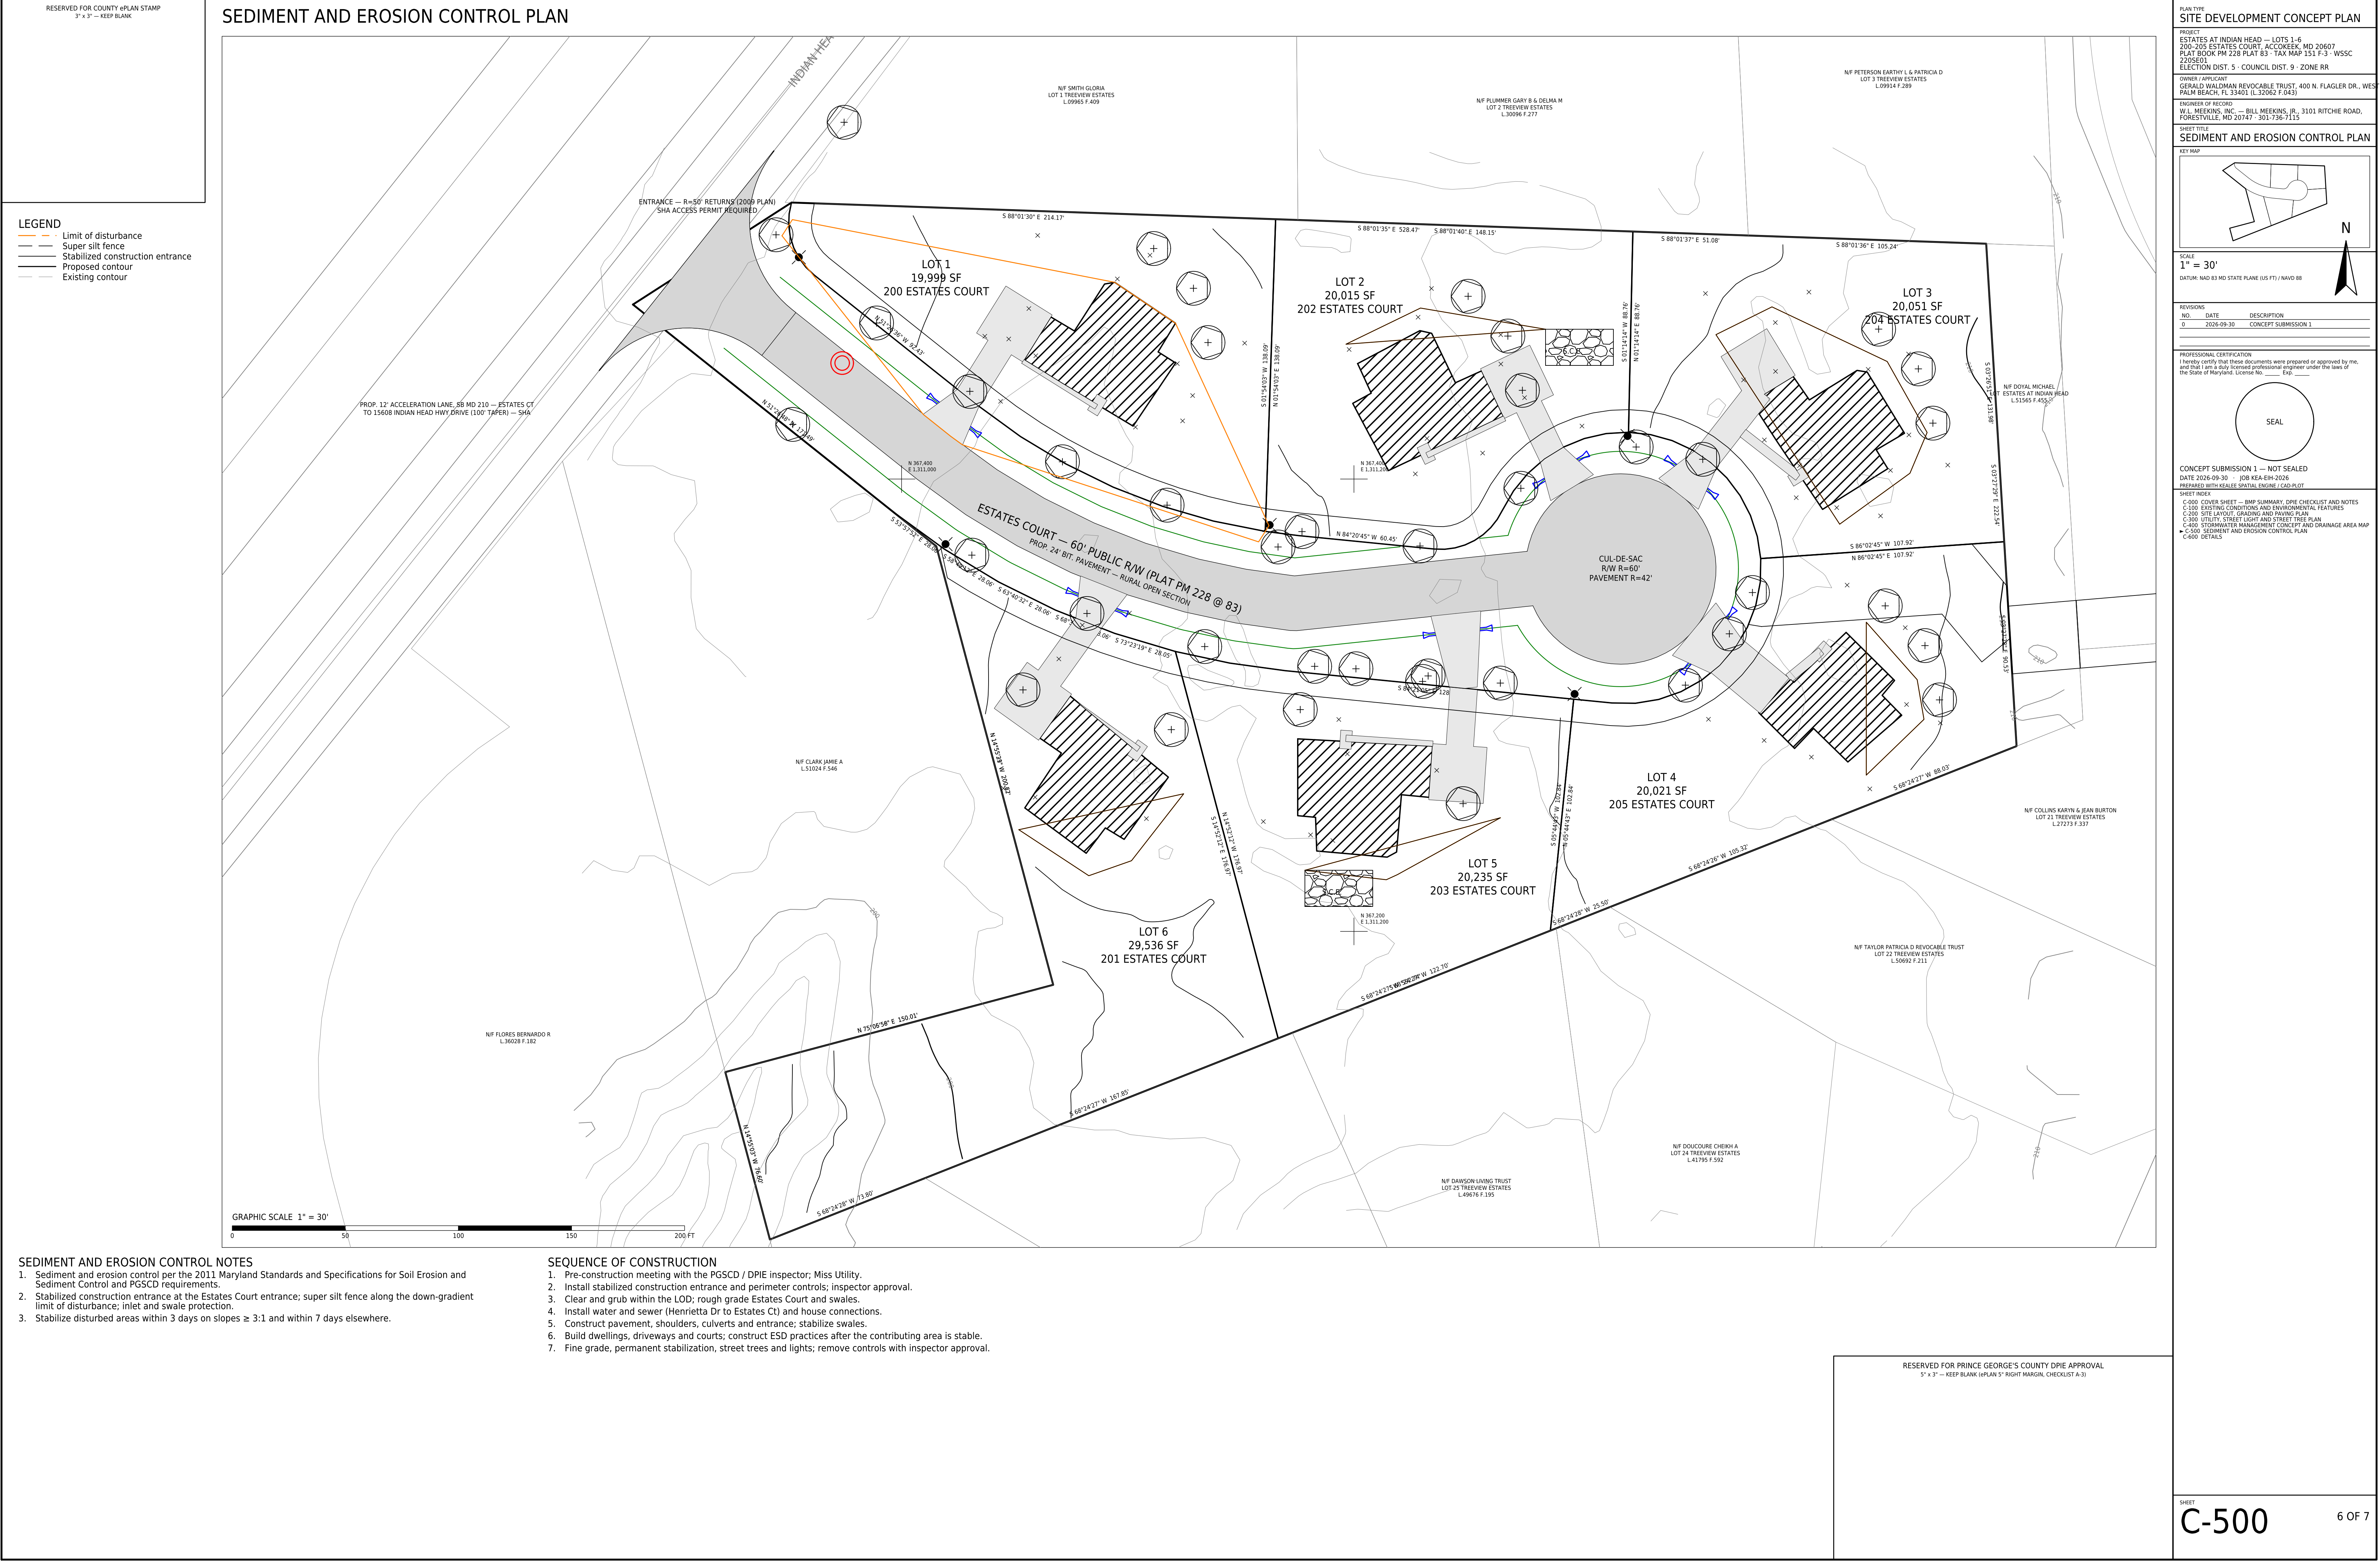

DETAILS

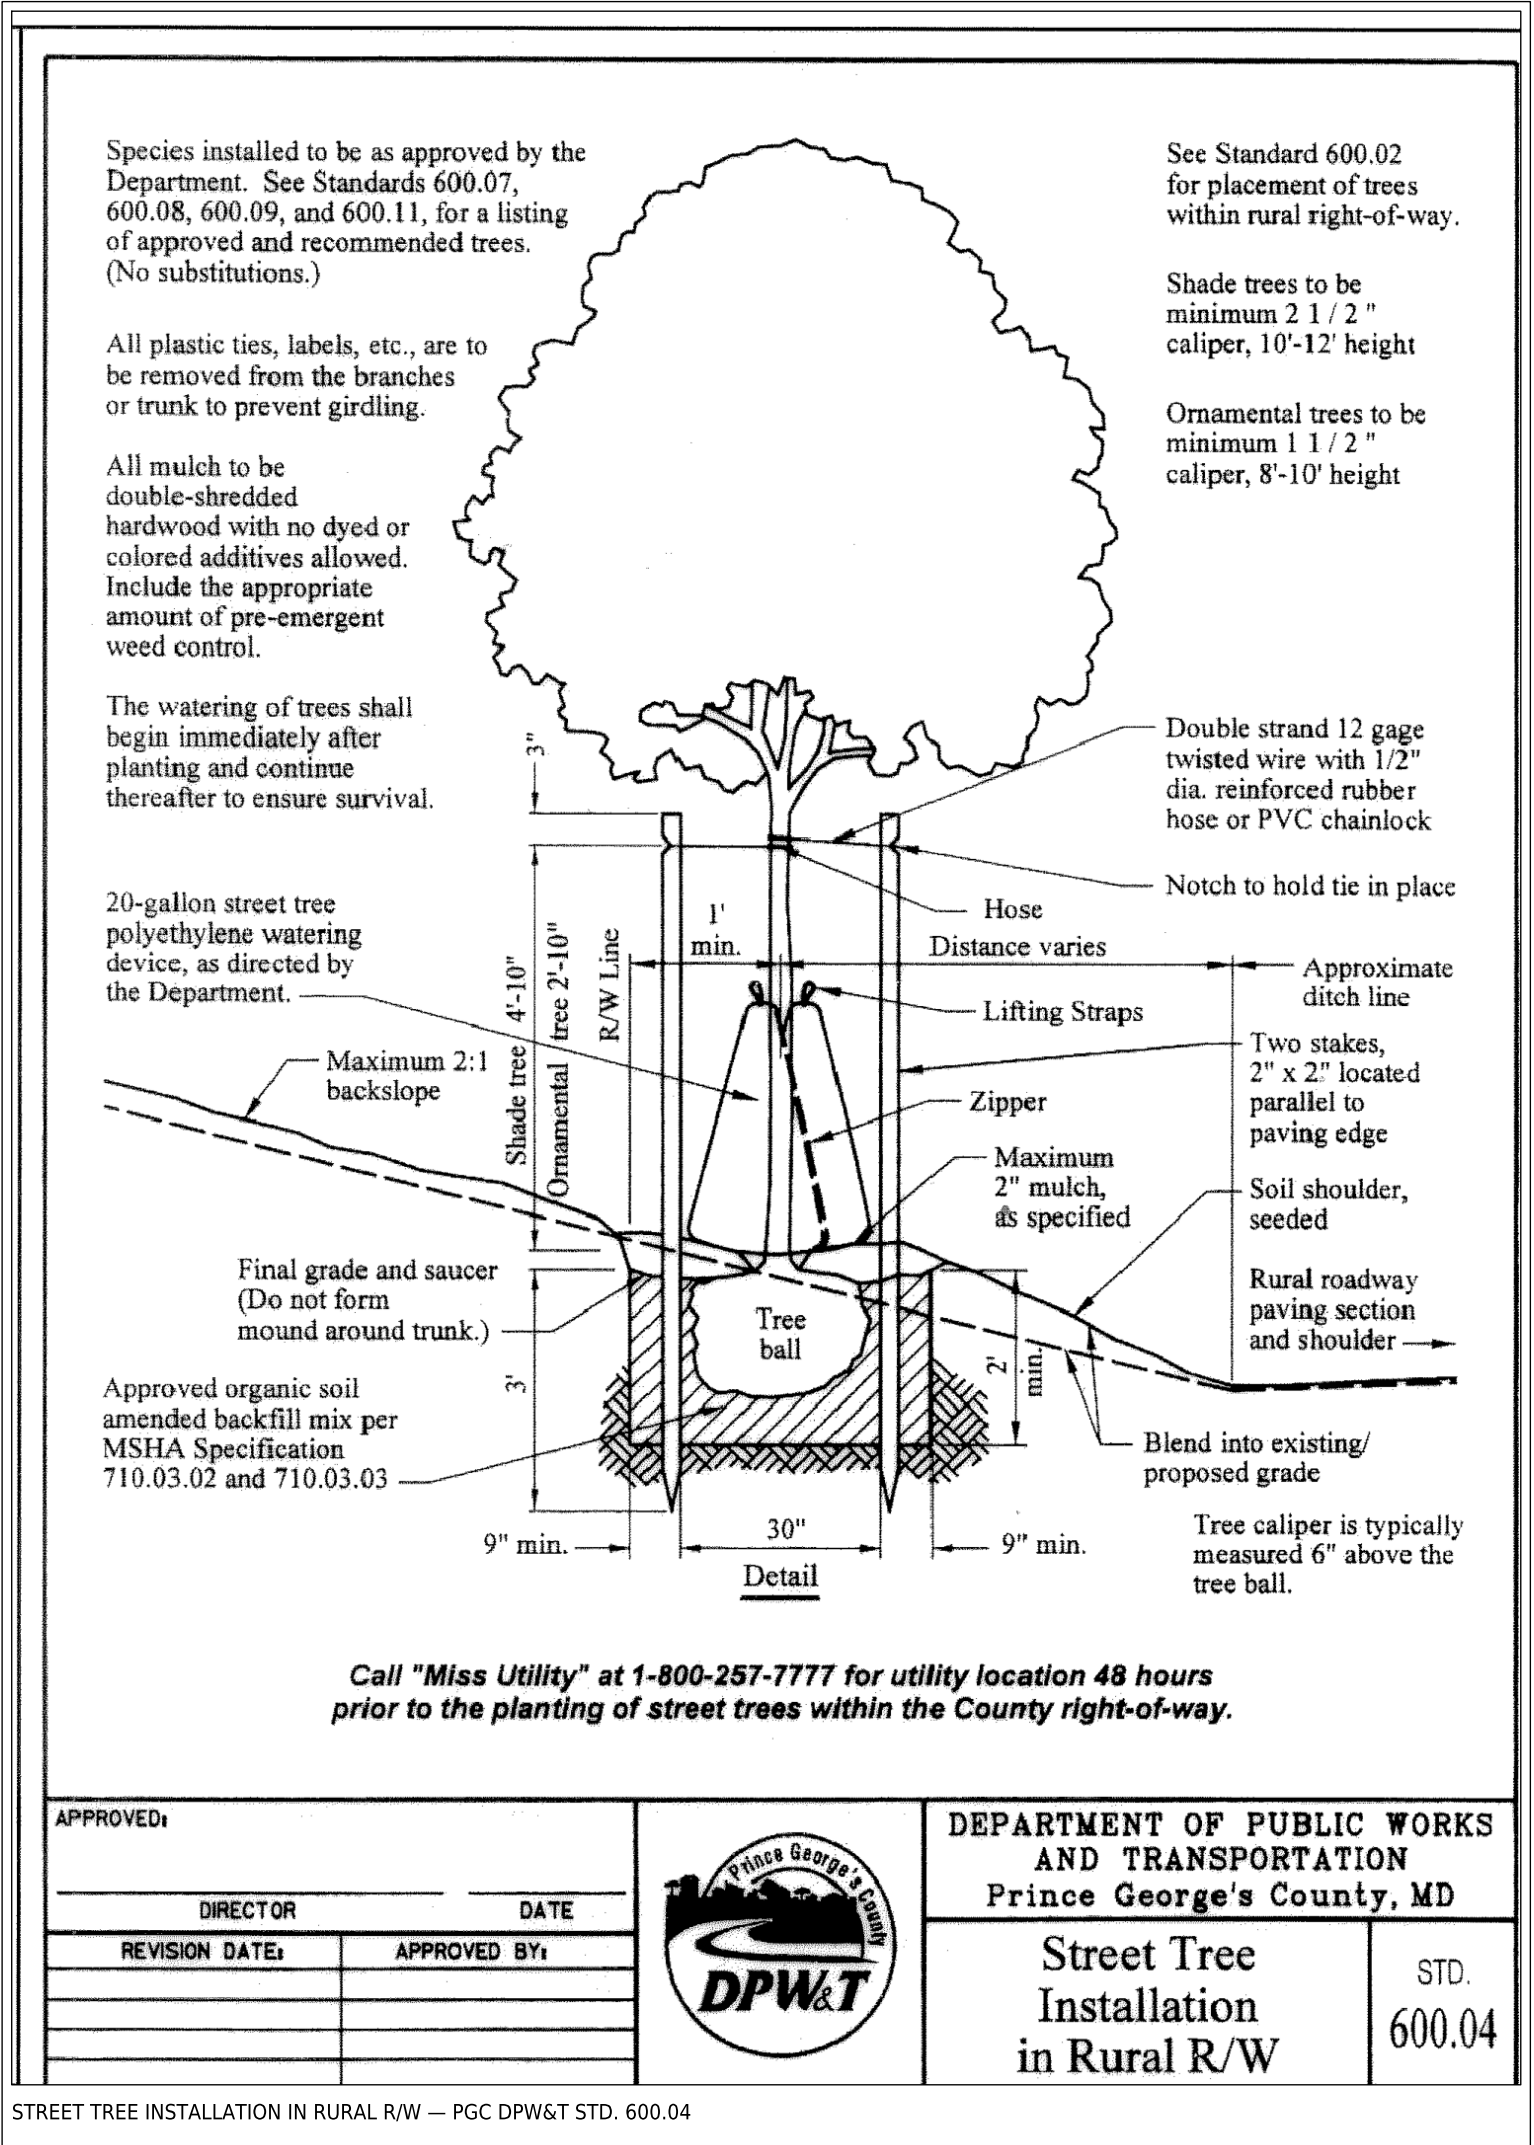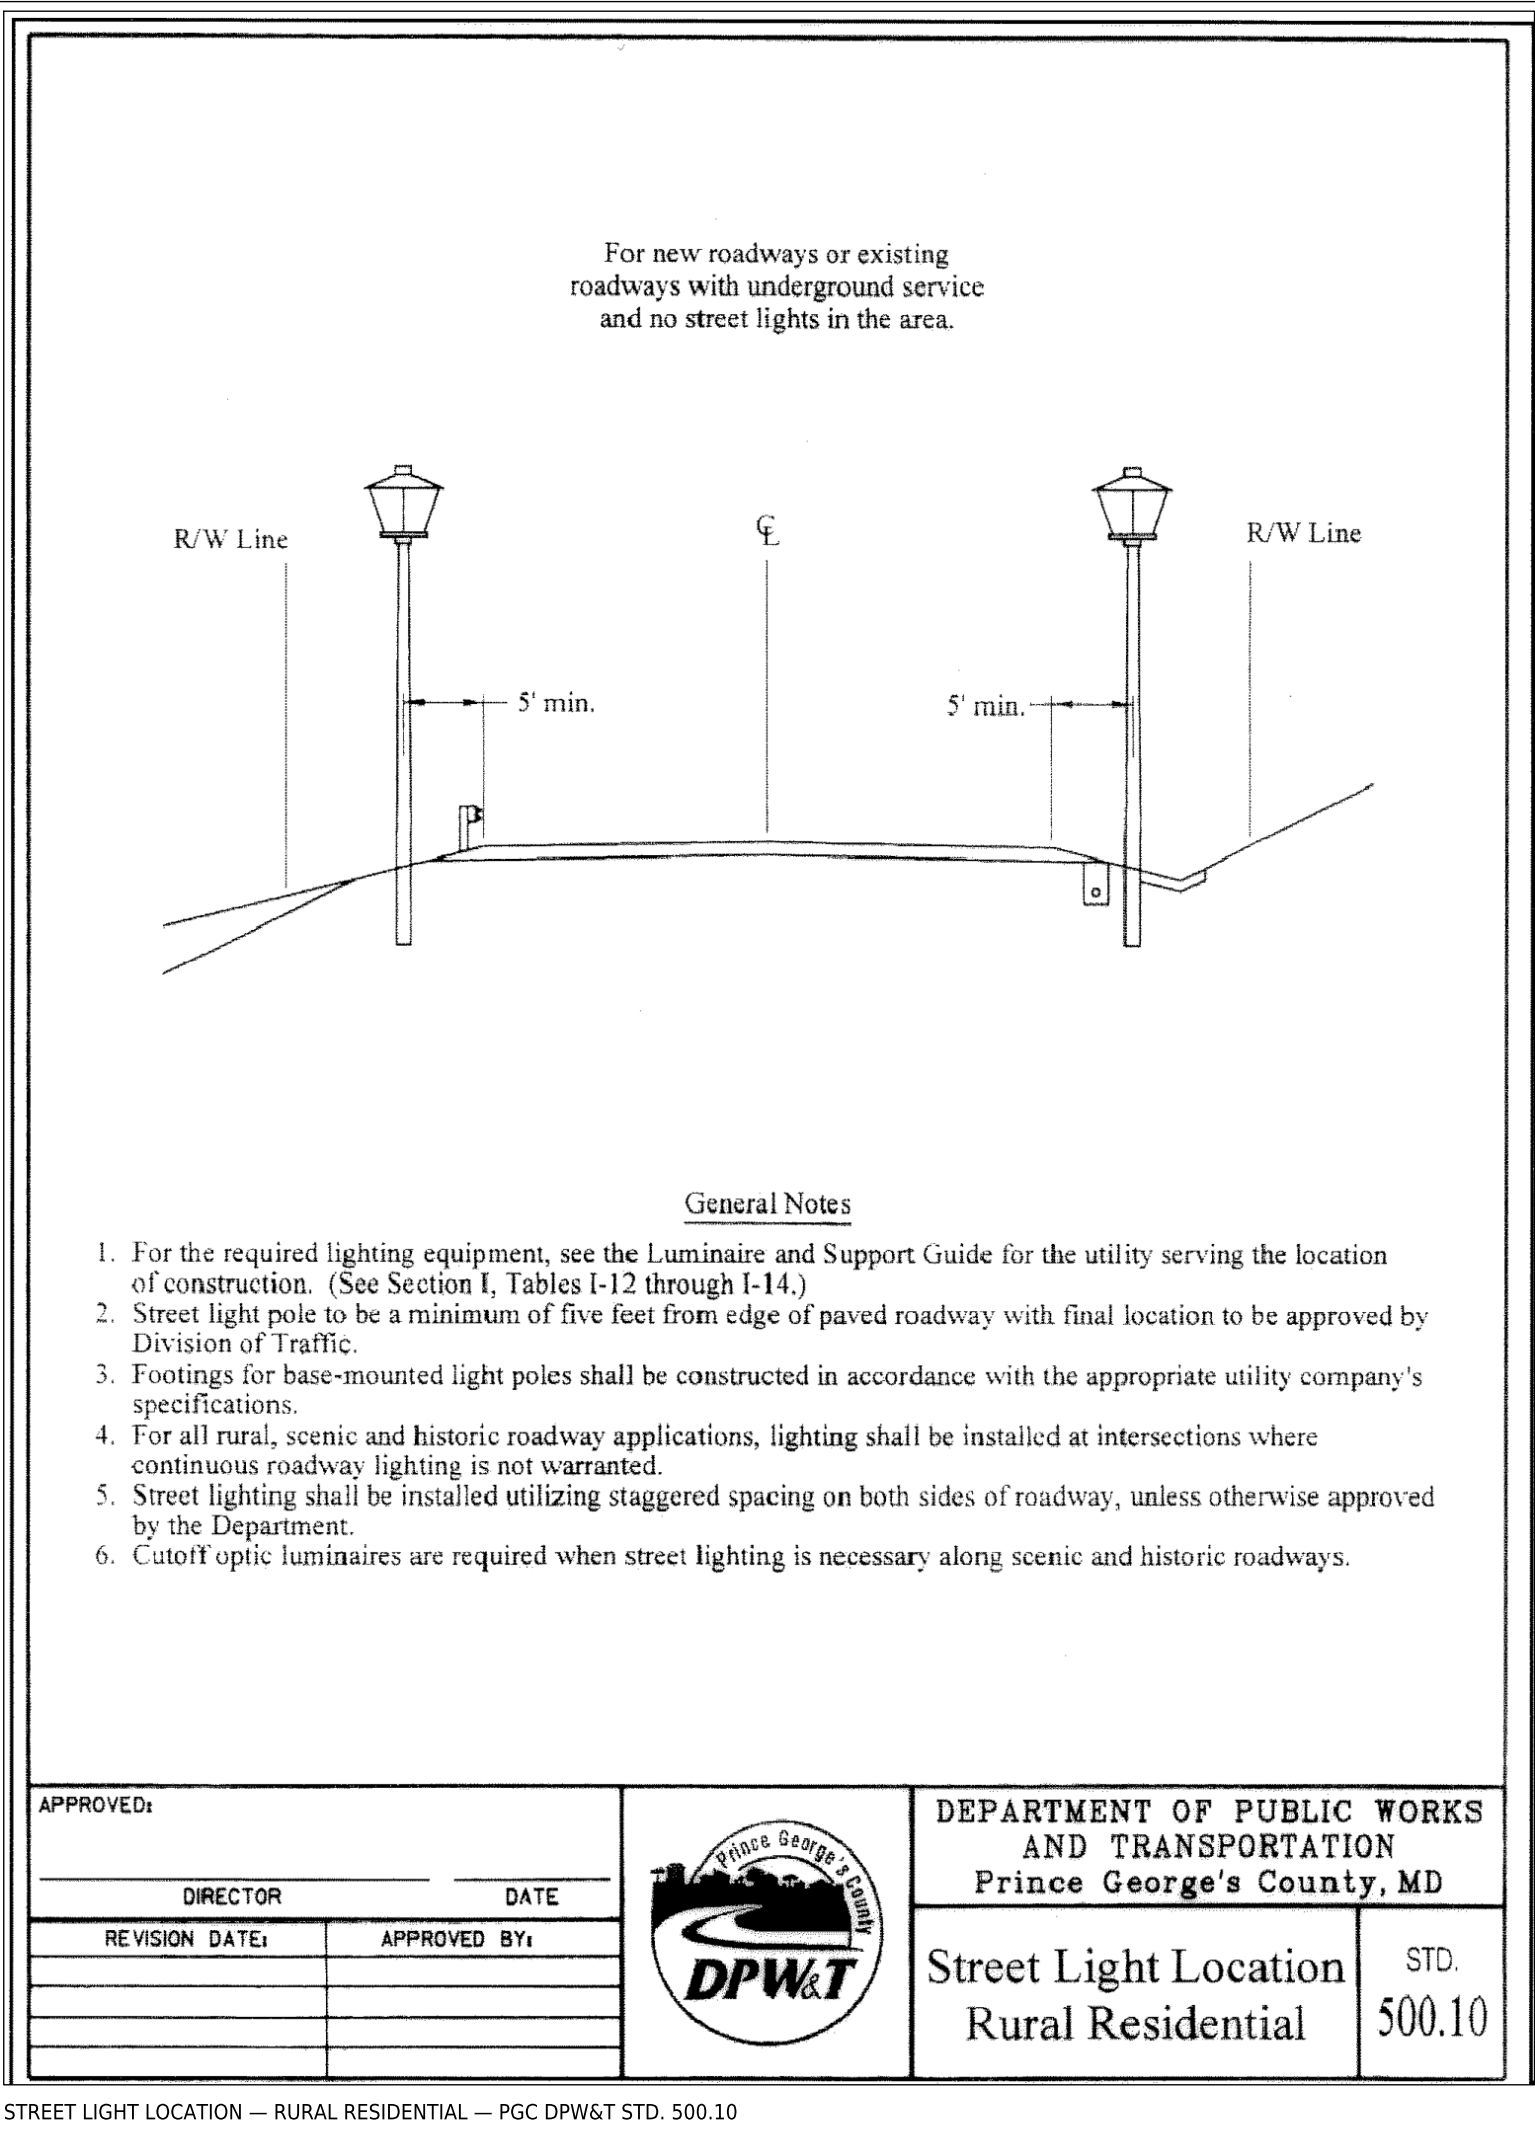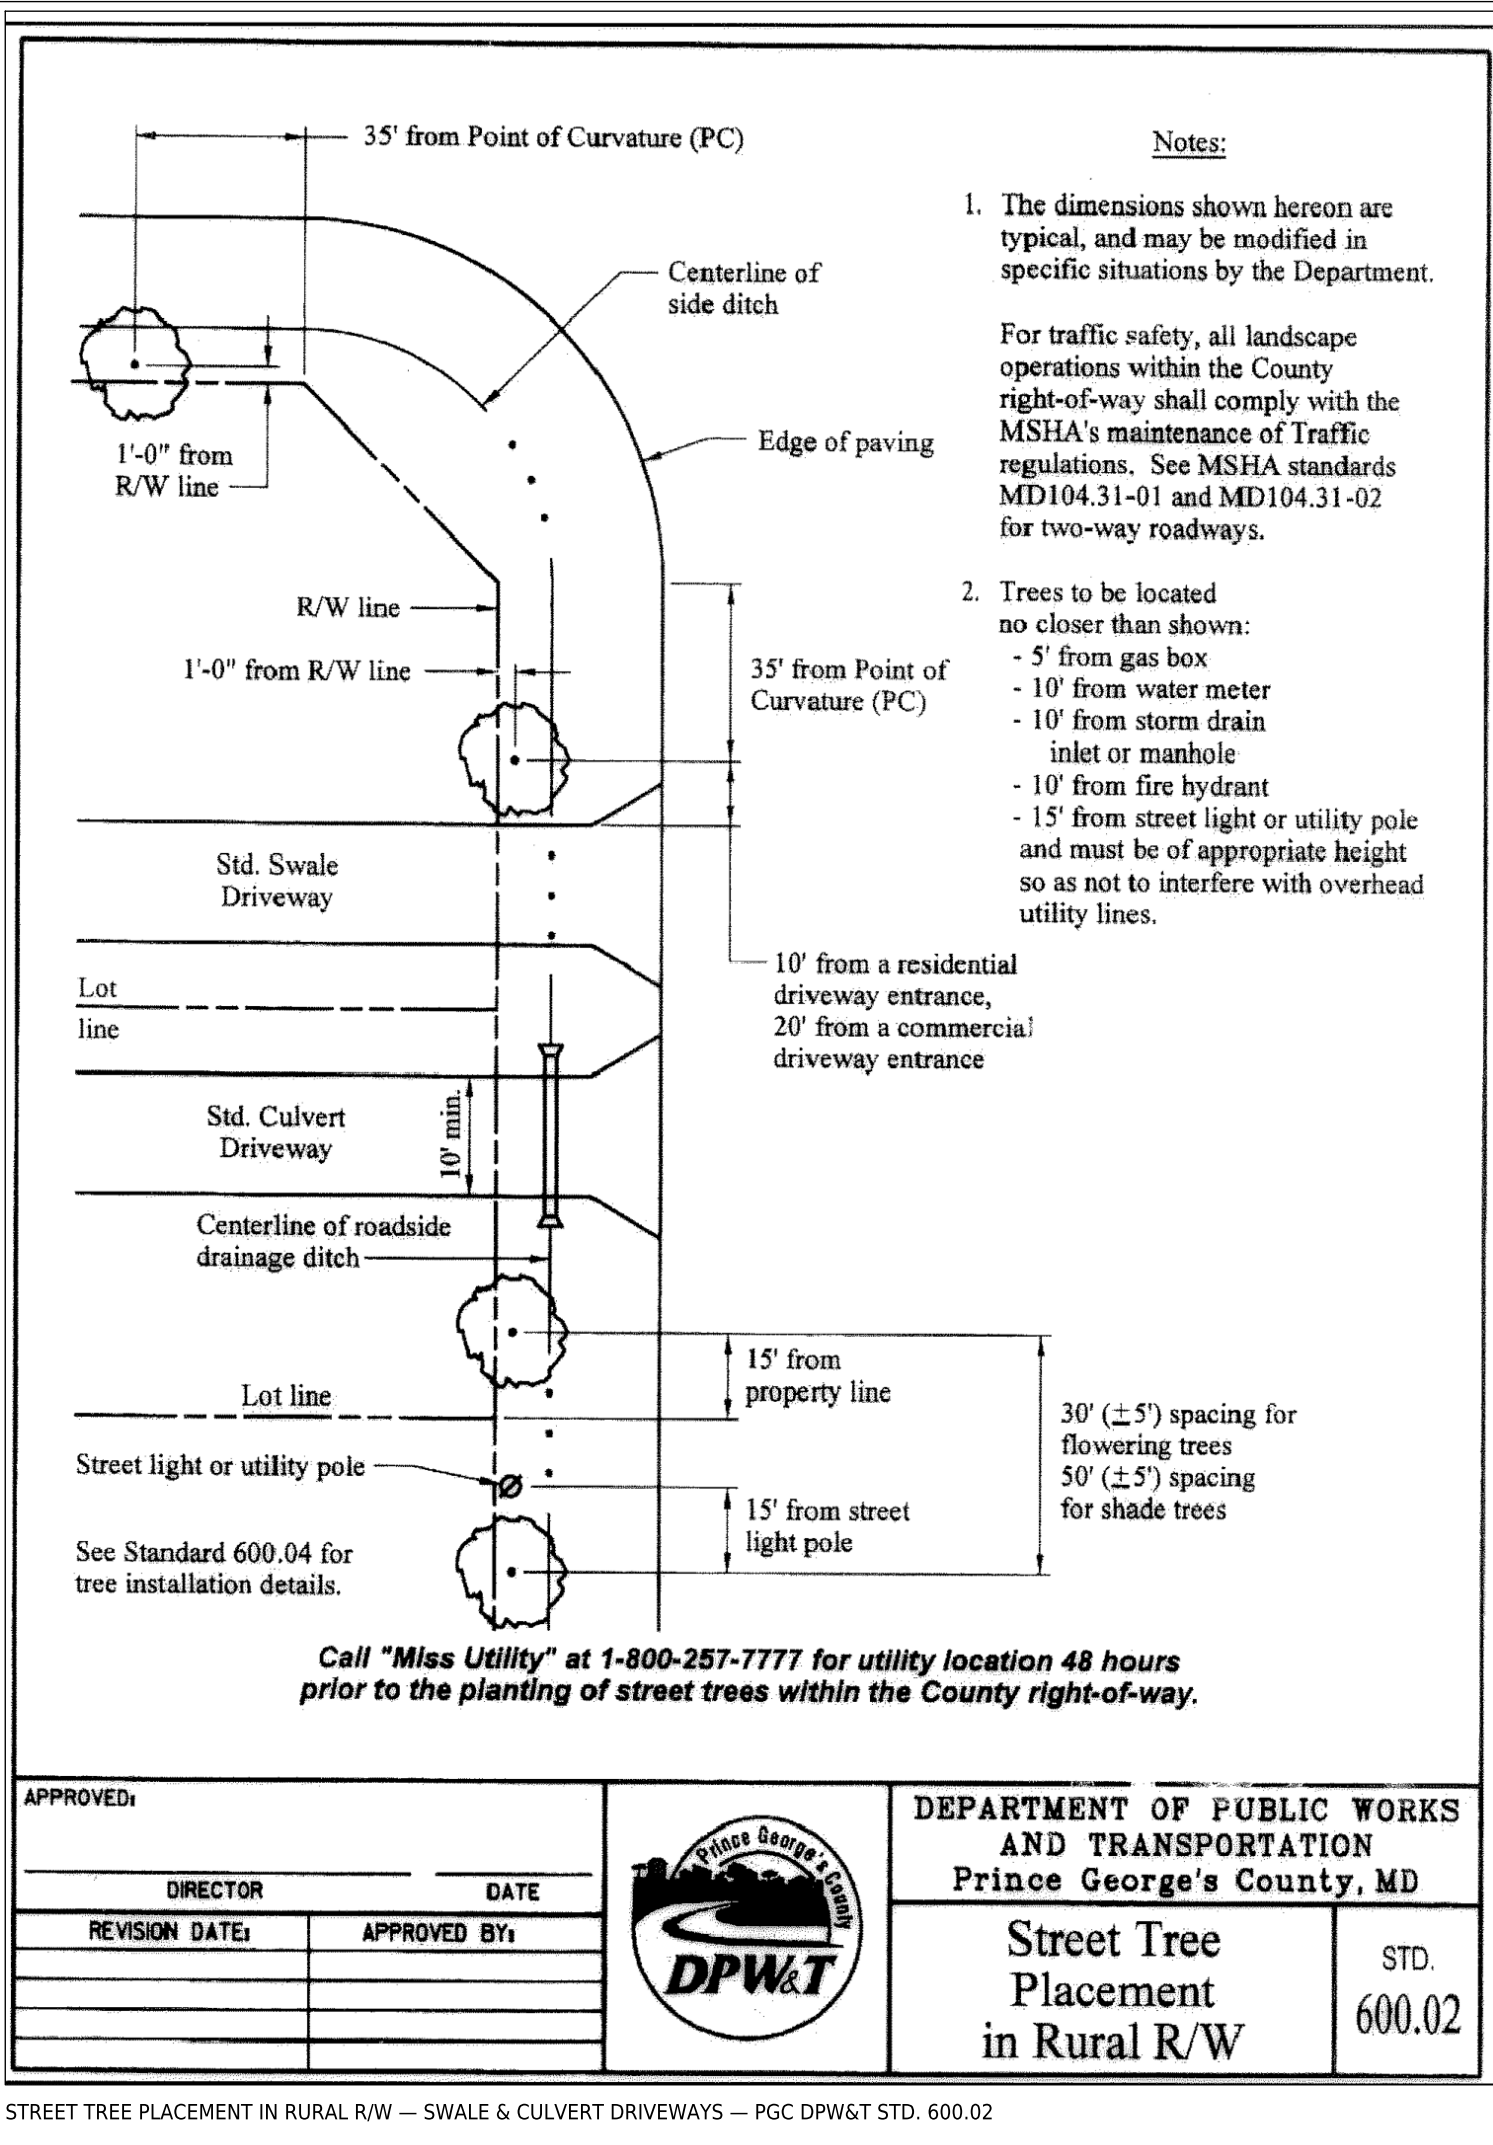


ESTATES COURT — TYPICAL SECTION (RURAL OPEN SECTION, 60' R/W)

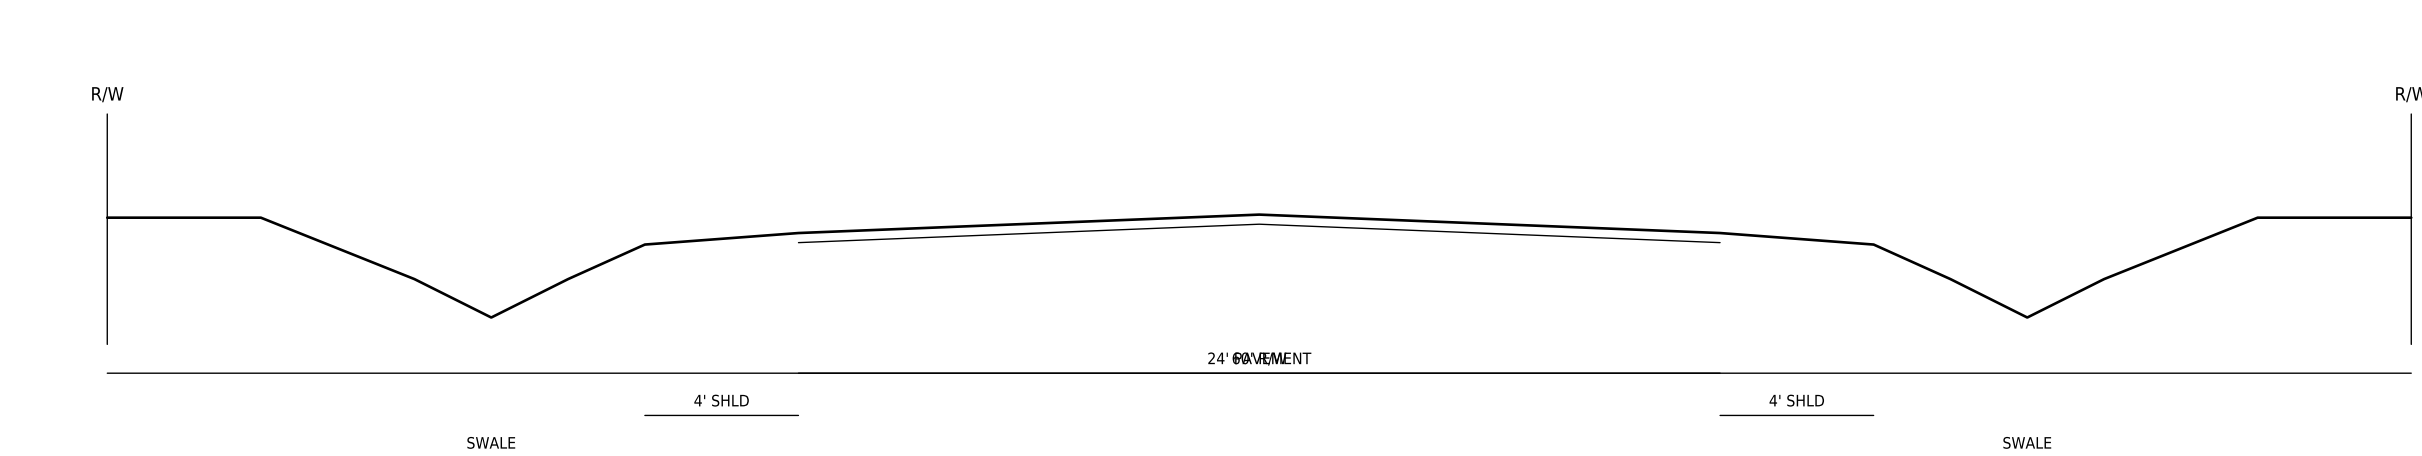


1 1/2" SURFACE + 2 1/2" BASE BIT. CONC. ON 6" GAB (DPW&T PAVEMENT SCHEDULE FOR RURAL RESIDENTIAL — CONFIRM)
CROSS SLOPE 2%; 4-FT STABILIZED SHOULDERS, SWALE FLOWLINE 20 FT OFF CENTRELINE, 3:1 SIDE SLOPES
DRIVEWAYS CROSS THE SWALE ON 15" RCP CULVERTS WITH FLARED END SECTIONS (DPW&T STD. 600.02)

MICRO-BIORETENTION (M-6) — TYPICAL SECTION

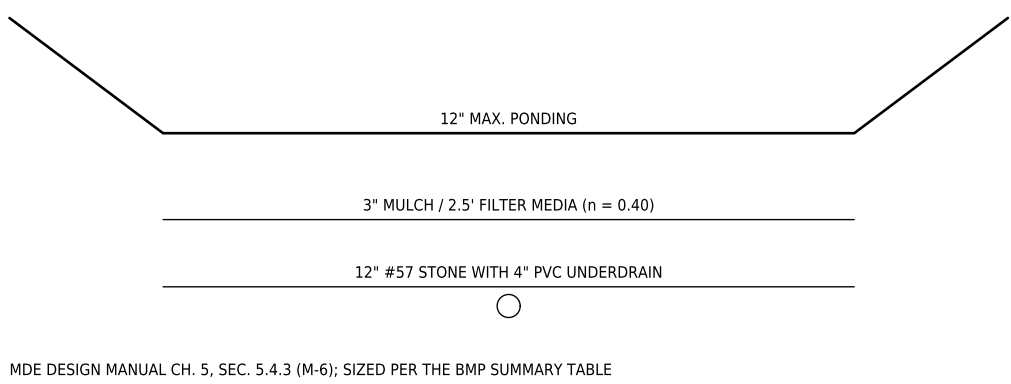

DRY SWALE (M-8) WITH CHECK DAM

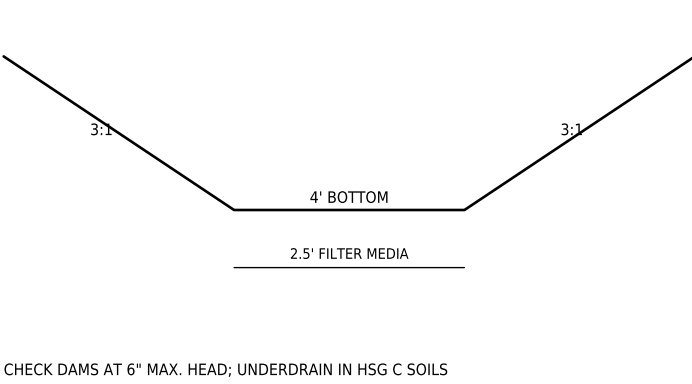

PLAN TYPE
SITE DEVELOPMENT CONCEPT PLAN

PROJECT
ESTATES AT INDIAN HEAD — LOTS 1-6
200-205 ESTATES COURT, ACCOKEEK, MD 20607
PLAT BOOK PM 226 PLAT 83 TAX MAP 151 P-3 WSSC
2206E01
ELECTION DIST. 5 - COUNCIL DIST. 9 - ZONE RR

OWNER / APPLICANT
GERALD WALDMAN REVOCABLE TRUST, 400 N. FLAGLER DR., WEST
PALM BEACH, FL 33401 (L-32062.F-043)

ENGINEER OF RECORD
W.L. MEEKINS, INC. — BILL MEEKINS, JR., 3101 RITCHIE ROAD,
FONTSVILLE, MD 20747 - 301-736-7115

SHEET TITLE
DETAILS

KEY MAP

SCALE
AS NOTED
DATUM: NAD 83 MD STATE PLANE (US FT) / NAVD 88

REVISIONS

NO.	DATE	DESCRIPTION
0	2026-09-30	CONCEPT SUBMISSION 1

PROFESSIONAL CERTIFICATION
I hereby certify that these documents were prepared or approved by me, and that I am a duly licensed professional engineer under the laws of the State of Maryland. License No. _____ Exp. _____

SEAL

CONCEPT SUBMISSION 1 — NOT SEALED
DATE 2026-09-30 JOB KEA-EH-2026
PREPARED WITH KRAUSE SPOTIAL ENGINE / CAD-PILOT

SHEET INDEX
C-600 COVER SHEET — BMP SUMMARY, DPE CHECKLIST AND NOTES
C-200 EXISTING CONDITIONS AND ENVIRONMENTAL FEATURES
C-300 SITE EROSION, GRADING AND PAVING PLAN
C-300 UTILITY, STREET LIGHT AND STREET TREE PLAN
C-400 STORMWATER MANAGEMENT CONCEPT AND DRAINAGE AREA MAP
C-500 SEDIMENT AND EROSION CONTROL PLAN
C-600 DETAILS