



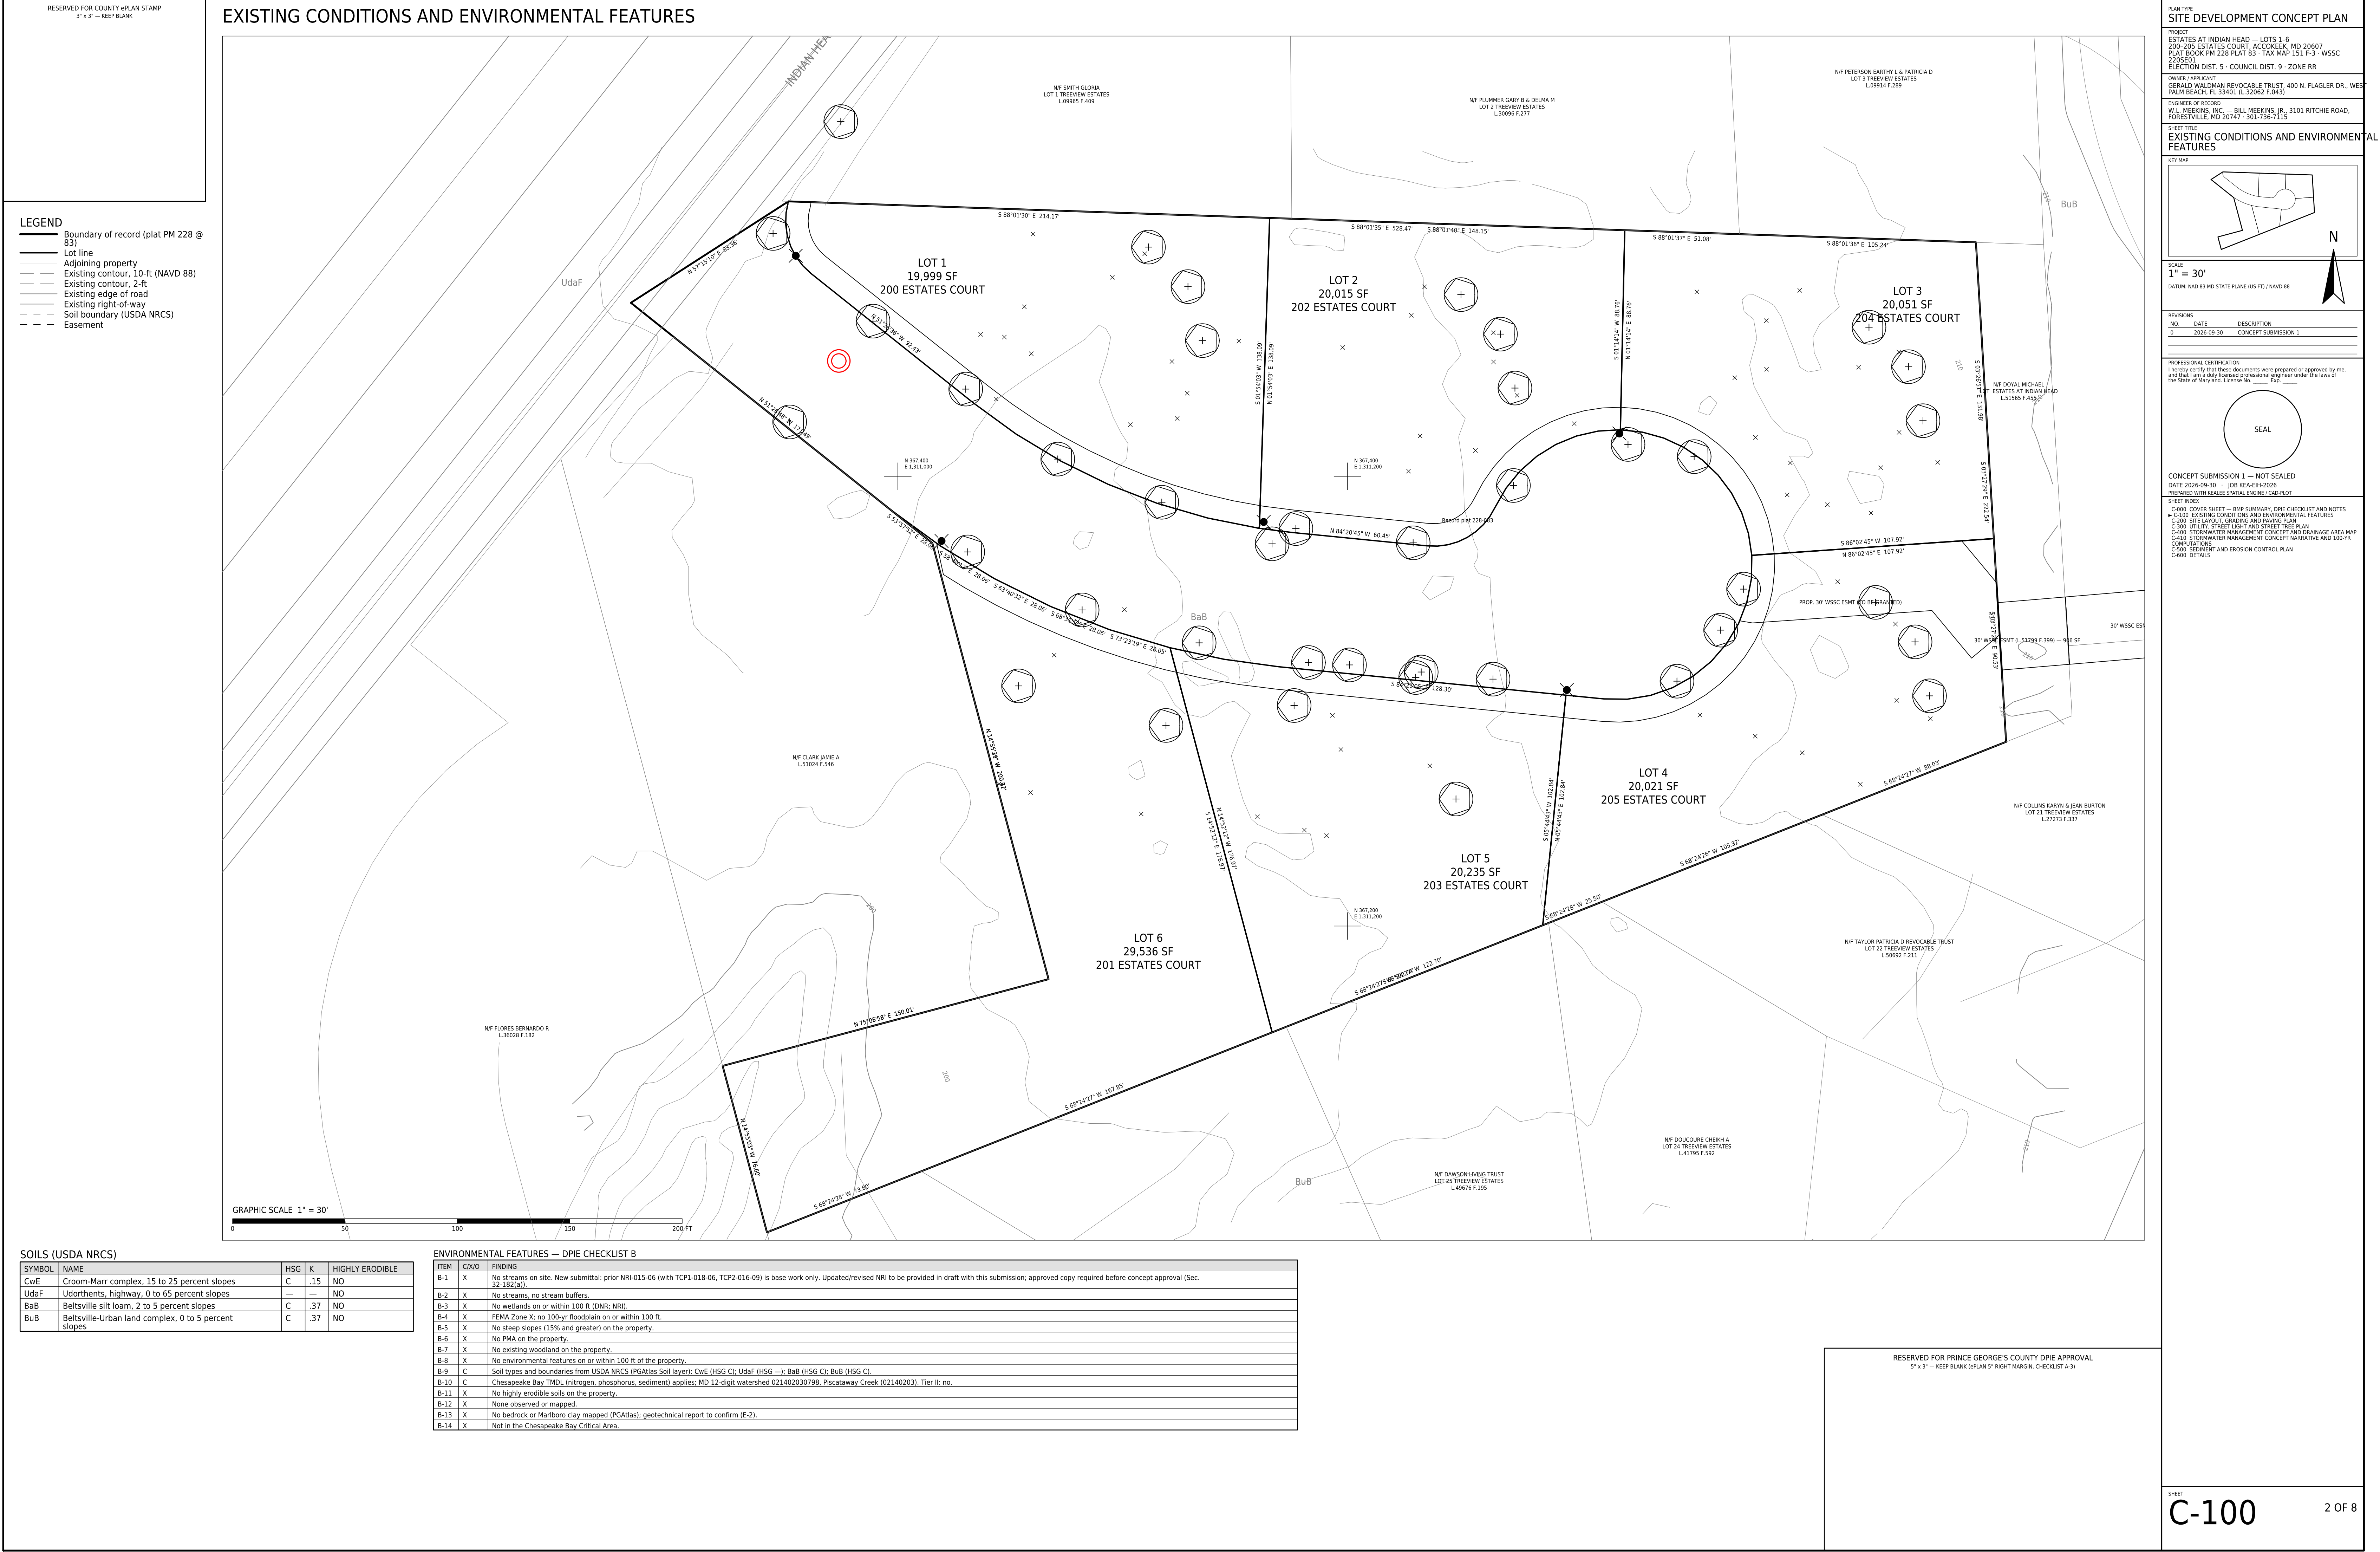

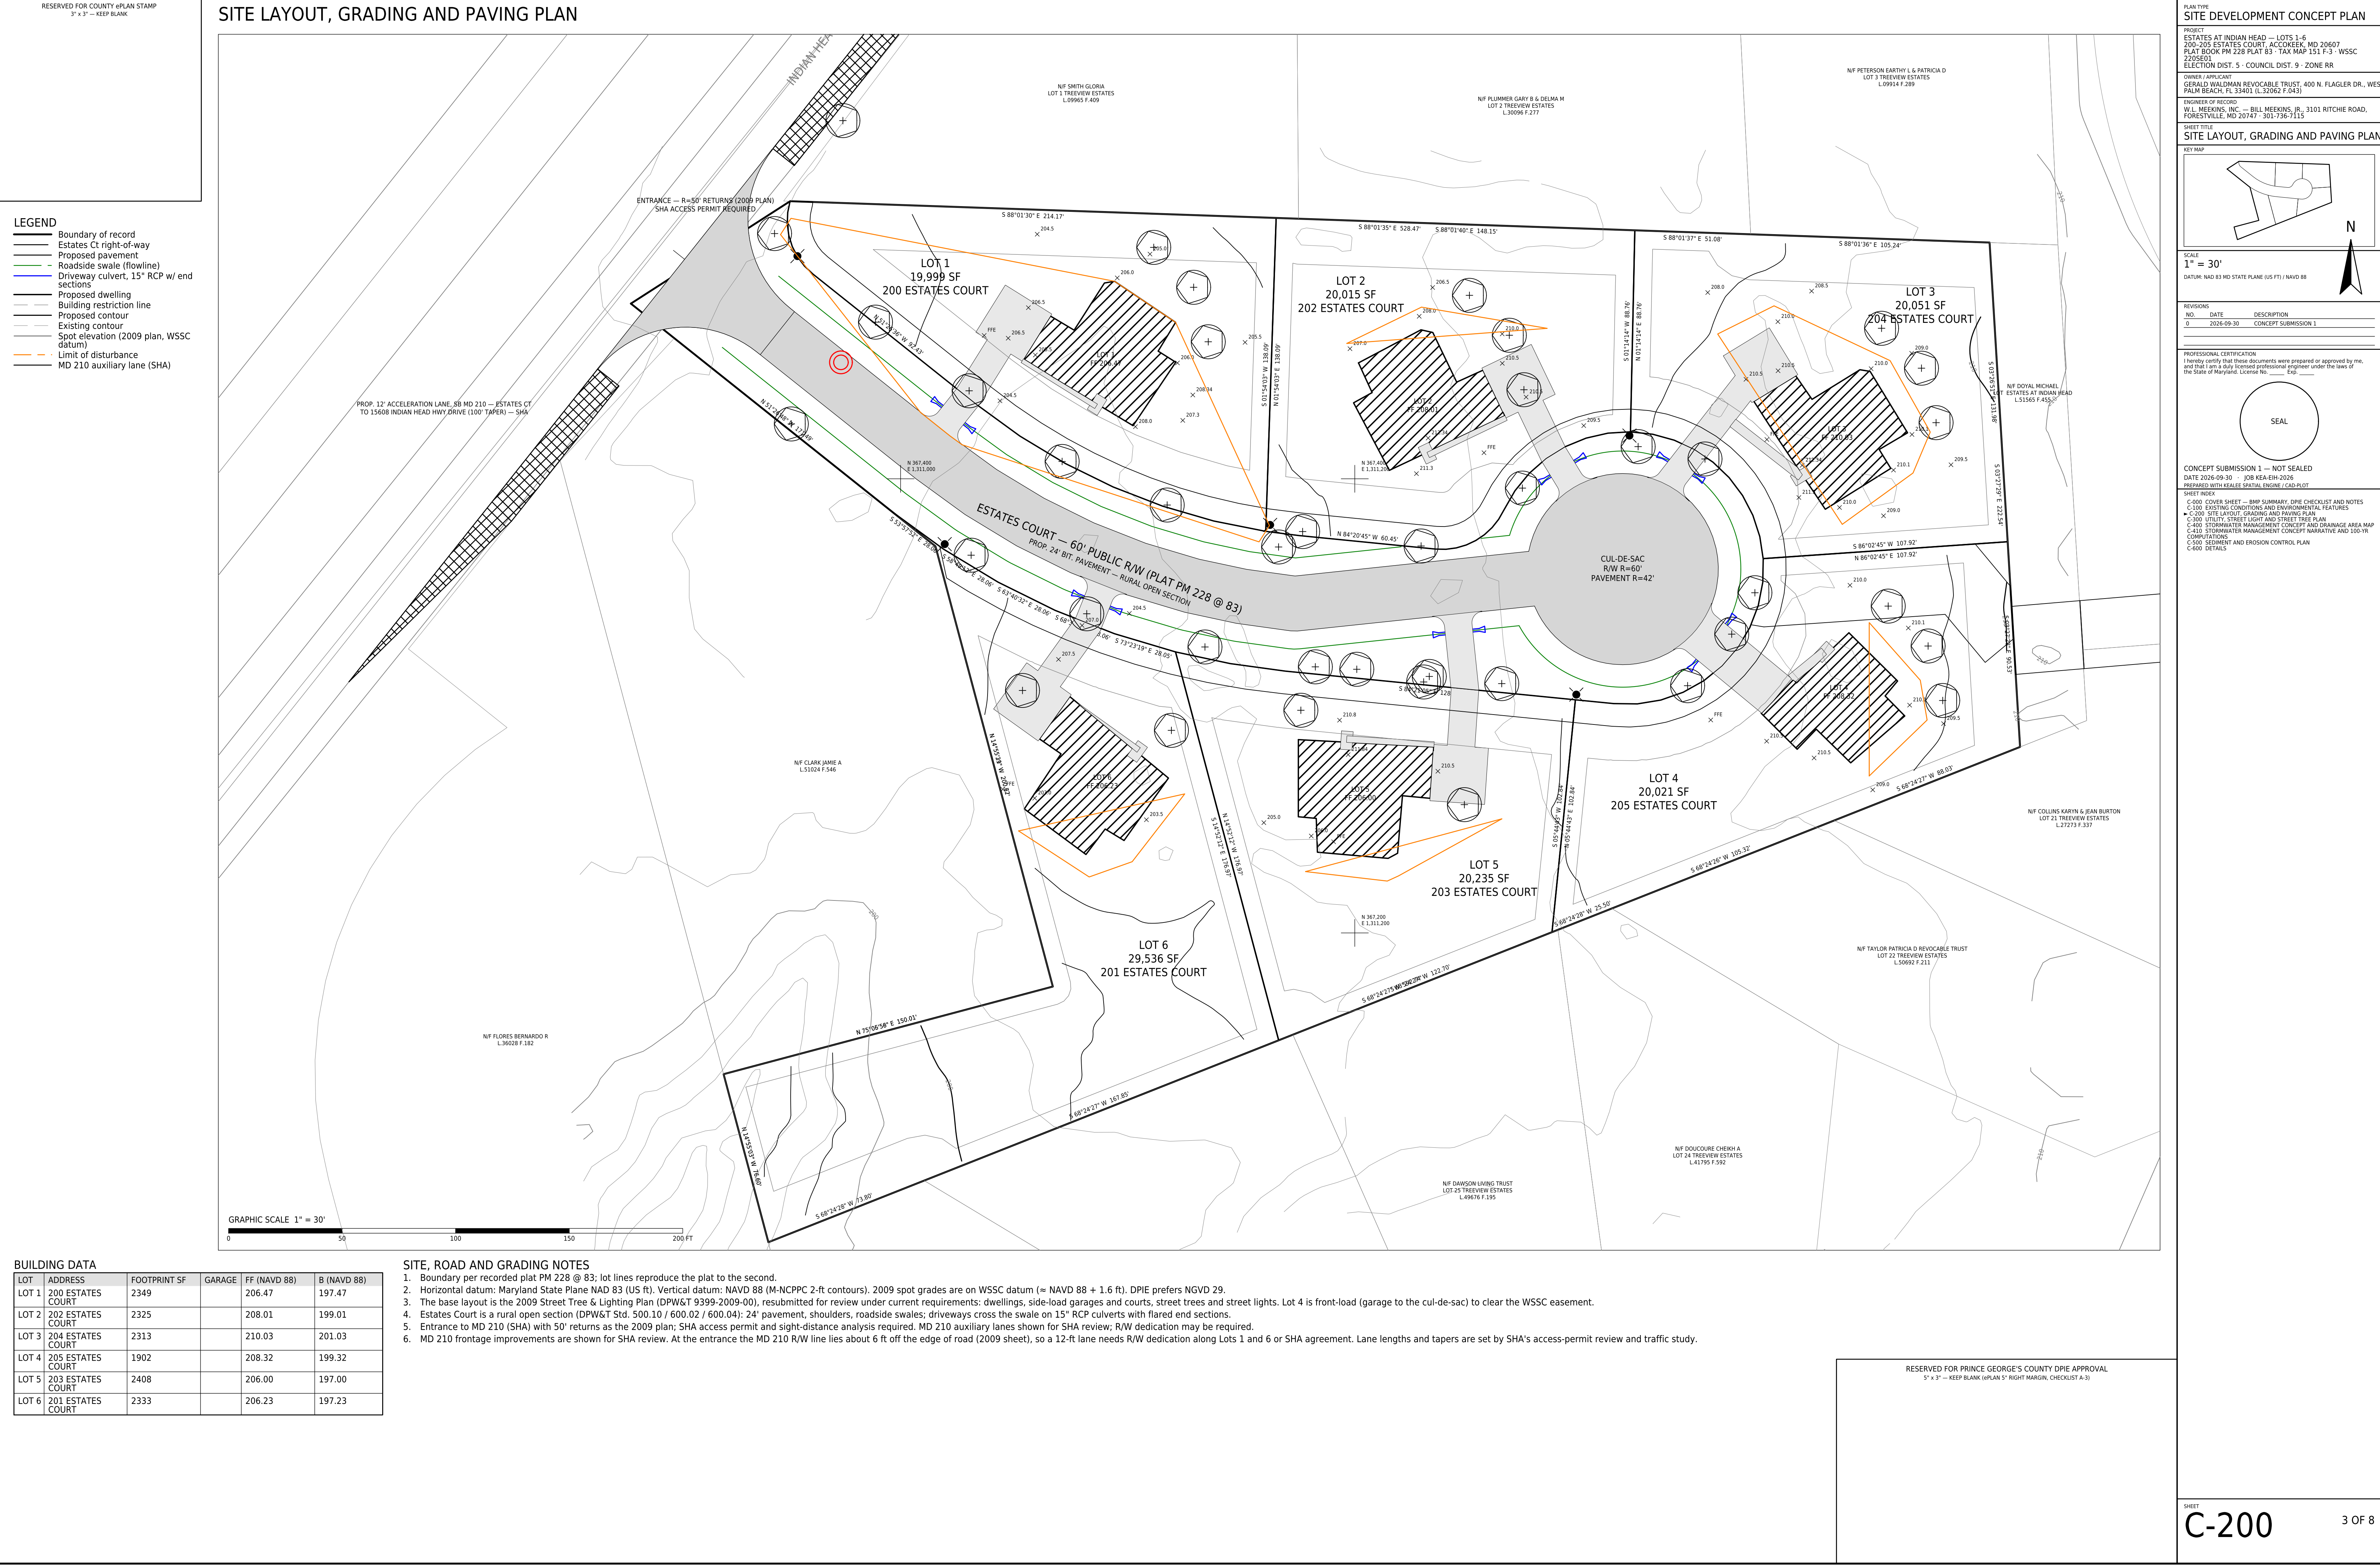

- Proposed 8" water main
- Proposed 8" sanitary sewer
- House connection
- - - WSSC easement (recorded / proposed)
- Street tree — Red Maple (2009 plan)
- Street light (2009 plan)



SYMBOL	QTY	ITEM	SIZE / TYPE	STANDARD
TREE	16	ACER RUBRUM - RED MAPLE	1 1/2"-3" CAL., B&B	DPW&T 600.02 / 600.04
LIGHT	5	STREET LIGHT (SMECO)	100 W HPS COLONIAL POST-TOP, TYPE IV, BLACK FIBERGLASS	DPW&T 500.10

1. Water and sewer by WSSC (W-3 1/2 - 3). Mains from the existing WSSC mains in Henrietta Drive through the recorded 30' WSSC easement (L.51799 F.399, Outlot A and Lot 20) and a 20' WSSC easement to be granted across Lot 4 along the Lot 3/4 line.
2. Sizes and inverts of the Henrietta Drive mains to be verified on WSSC 200' sheet '220SE01' before technical design.
3. Street lights and street trees follow the approved 2009 Street Tree & Lighting Plan (DPW&T 9399-2009; light permit 09.09399); electric service by SMECO.
4. Keep street trees 10 ft from water meters and storm structures and 15 ft from street lights (DPW&T 600.02).
5. House connections: 1" copper water service and 4" PVC sewer lateral per lot, each tapped on its own main and run to the dwelling clear of every driveway, apron, walk, stoop, culvert and ESD cell (3 ft min.), so no concrete or structure is removed to lay or repair them; water and sewer 10 ft apart (WSSC).
6. LOT 6: water and sewer in a COMMON TRENCH (no 10-ft corridor clear of the paving) — water on a shelf 12 in above the sewer, subject to WSSC approval at plumbing permit; otherwise relocate the lead walk.
7. Contact Miss Utility (811) at least 48 hours before excavation.

RESERVED FOR PRINCE GEORGE'S COUNTY DPIE APPROVAL
5" x 3" — KEEP BLANK (ePLAN 5" RIGHT MARGIN, CHECKLIST A-3)


- C-100 EXISTING CONDITIONS AND ENVIRONMENTAL FEATURES
- C-200 SITE LAYOUT, GRADING AND PAVING PLAN
- C-300 UTILITY, STREET LIGHT AND STREET TREE PLAN
- C-400 STORMWATER MANAGEMENT CONCEPT AND DRAINAGE AREA MAP
- C-410 STORMWATER MANAGEMENT CONCEPT NARRATIVE AND 100-YR COMPUTATIONS
- C-500 SEDIMENT AND EROSION CONTROL PLAN
- C-600 DETAILS

RESERVED FOR COUNTY ePLAN STAMP
3" x 3" — KEEP BLANK

STORMWATER MANAGEMENT CONCEPT AND DRAINAGE AREA MAP

LEGEND

- ESD practice — micro-bioretenction (M-6)
- Roadside dry swale (M-8)
- Drainage area to practice
- Off-site area draining onto site
- 100-yr overflow path
- Point of investigation
- Driveway culvert

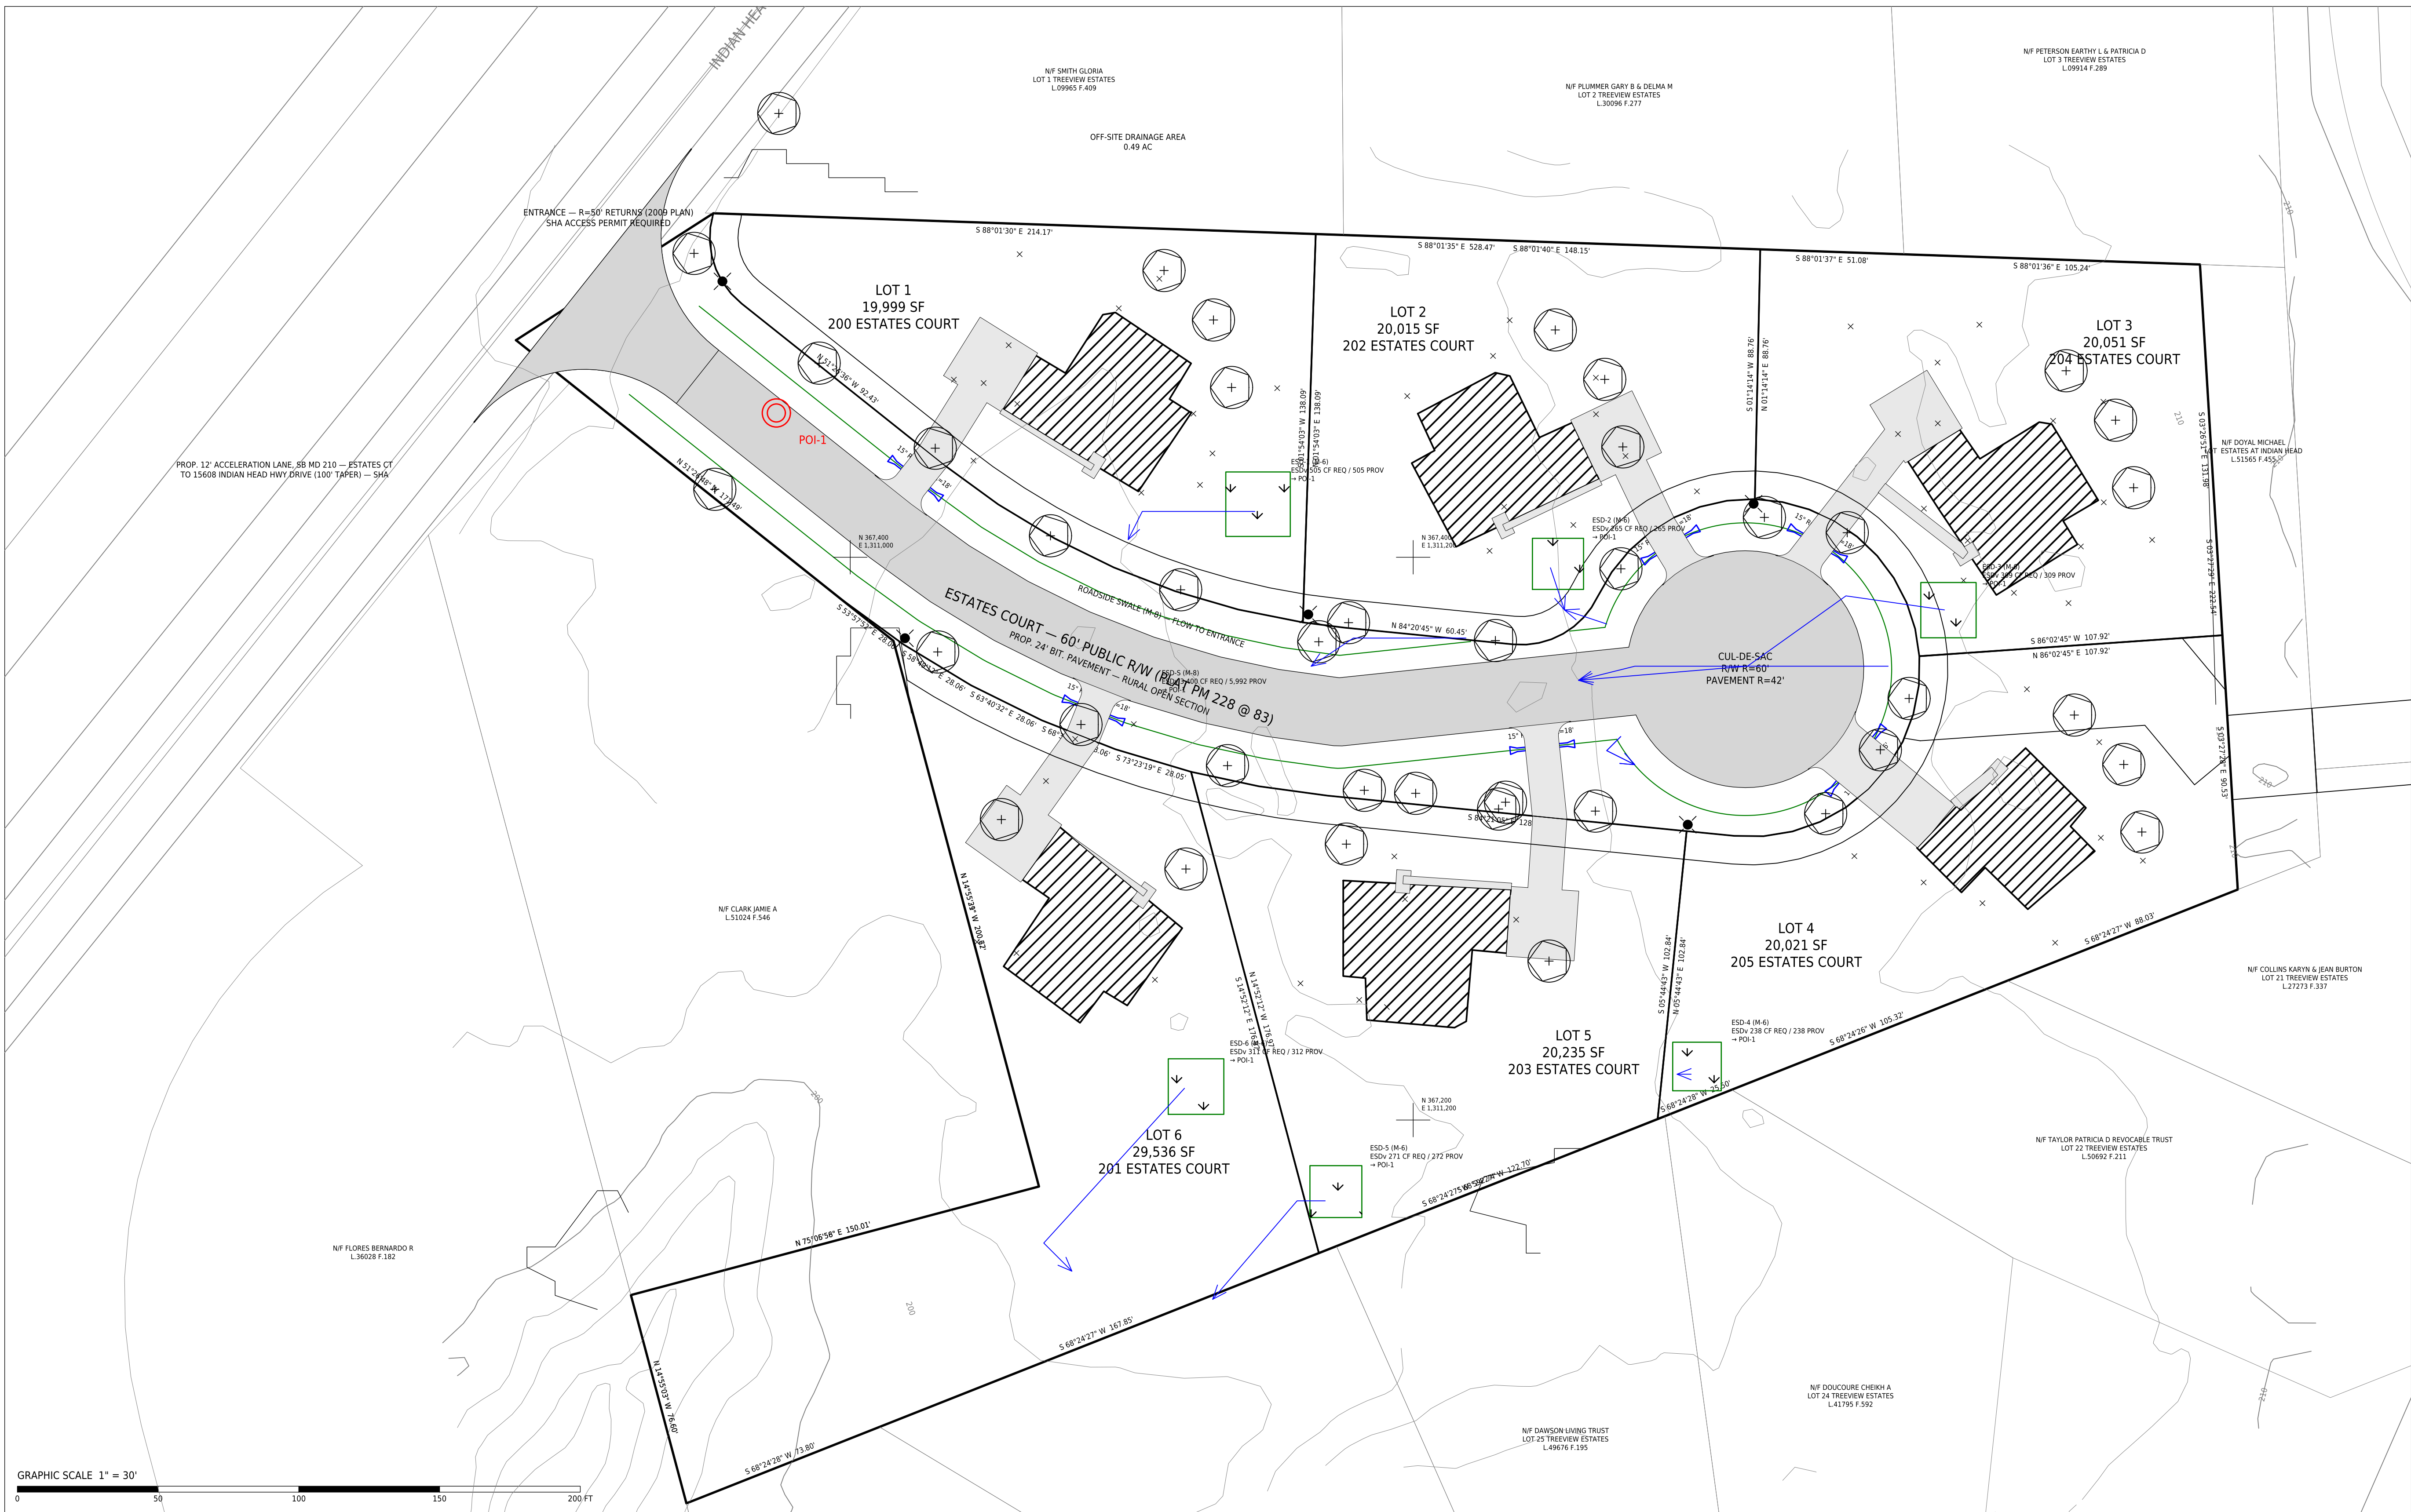

ESD PER PRACTICE (FULL TABLE ON C-000)

BMP	MDE	LOCATION	POI	DA SF	%I	P E	ESDv REQ	ESDv PROV
ESD-1	M-6	Lot 1	POI-1	19,999	22.5	1.2	505	505
ESD-2	M-6	Lot 2	POI-1	20,015	12.1	1.0	265	265
ESD-3	M-6	Lot 3	POI-1	20,051	15.0	1.0	309	309
ESD-4	M-6	Lot 4	POI-1	20,021	10.3	1.0	238	238
ESD-5	M-6	Lot 5	POI-1	20,235	12.3	1.0	271	272
ESD-6	M-6	Lot 6	POI-1	29,536	8.5	1.0	311	312
ESD-5	M-8	Estates Ct R/W, both sides	POI-1	36,041	57.3	2.0	3,400	5,992

POINTS OF INVESTIGATION (C-9)

POI	LOCATION	SHARE	ESDv REQ	ESDv PROV
POI-1	N 367.451 E 1,310.974	100%	5,299	7,893

SWM NOTES

- SWM by Environmental Site Design to the MEP (Md. Stormwater Management Act of 2007; MDE Design Manual Ch. 5; PGC Subtitle 32). Target rainfall P_E from MDE Table 5.3 for HSG C at each drainage area's imperviousness.
- Each lot drains to one micro-bioretenction cell (M-6): 12-in max. ponding, 2.5-ft filter media, underdrain to a stable outfall. Estates Court drains to roadside dry swales (M-8) with check dams.
- Rooftop and non-rooftop disconnection (N-1, N-2) to be credited at technical design. Infiltration credit only where Sec. 32-131 borings show ≥ 0.52 in/hr.
- Private ESD practices: maintenance agreement recorded before permit; public swales in the R/W maintained by DPPE.
- D8 flow routing on a 5-ft surface interpolated from the existing 2-ft contours; exit points clustered at 120 ft; POIs carrying under 4% of the site omitted.

PLAN TYPE SITE DEVELOPMENT CONCEPT PLAN


PROJECT
ESTATES AT INDIAN HEAD — LOTS 1-6
200-205 ESTATES COURT, ACCOKEEK, MD 20607
PLAT BOOK PW 228 PLAT 83 — TAX MAP 151 F-3 — WSSC
220501
ELECTION DIST. 5 — COUNCIL DIST. 9 — ZONE RR

OWNER / APPLICANT
GERALD WALDHAM REVOCABLE TRUST, 400 N. FLAGLER DR., WEST PALM BEACH, FL 33403 (L.32062 F.043)

ENGINEER OF RECORD
W.L. MECKINS, INC. — BILL MECKINS, JR., 3101 RITCHIE ROAD, FORESTVILLE, MD 20747-301-736-7115

SHEET TITLE STORMWATER MANAGEMENT CONCEPT AND DRAINAGE AREA MAP

KEY MAP

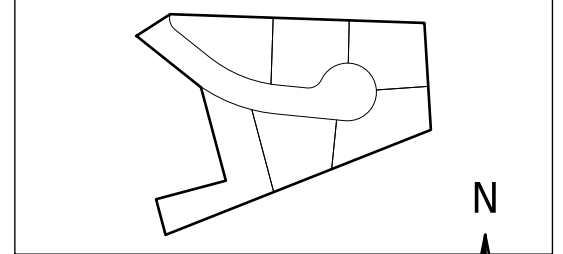

SCALE
1" = 30'
DATUM: NAD 83 MD STATE PLANE (US FT) / NAD83

REVISIONS		
NO.	DATE	DESCRIPTION
0	2026-09-30	CONCEPT SUBMISSION 1

PROFESSIONAL CERTIFICATION
I hereby certify that these documents were prepared or approved by me, and that I am a duly licensed professional engineer under the laws of the State of Maryland. License No. _____ E.O. _____



CONCEPT SUBMISSION 1 — NOT SEALED

DATE 2026-09-30 — JOB KEA-EH-2026

PREPARED WITH SCALE 30' HORIZONTAL ENGINEER / C-000-007

SHEET INDEX
C-000 COVER SHEET — BMP SUMMARY, DPE CHECKLIST AND NOTES
C-100 EXISTING CONDITIONS AND ENVIRONMENTAL FEATURES
C-200 SITE LAYOUT, GRADING AND PAVING PLAN
C-300 UTILITY, STREET LIGHT AND STREET TREE PLAN
C-400 STORMWATER MANAGEMENT CONCEPT AND DRAINAGE AREA MAP
C-410 STORMWATER MANAGEMENT CONCEPT NARRATIVE AND 100-YR COMPUTATIONS
C-500 SEDIMENT AND EROSION CONTROL PLAN
C-600 DETAILS

RESERVED FOR PRINCE GEORGE'S COUNTY DPE APPROVAL
3" x 3" — KEEP BLANK (PLAN 5" RIGHT MARGIN, CHECKLIST A-3)

RESERVED FOR COUNTY ePLAN STAMP
3" x 3" — KEEP BLANK

STORMWATER MANAGEMENT CONCEPT NARRATIVE AND 100-YR COMPUTATIONS

D-1 SWM CONCEPT NARRATIVE

1. Natural resources: there are no environmental features on the property — no streams, wetlands, 100-yr floodplain, PMA or woodland (prior NRI-015-06 as base work; updated NRI with this submittal). The layout follows the approved 2009 plan and disturbance is held to the limit shown on the sediment control plan.

2. Natural flow patterns: the tract falls toward MD 210 and leaves at one point of investigation, which the proposed grading keeps; no drainage is diverted between POIs.

3. Impervious reduction: rural open section (24-ft pavement, no curb and gutter), as approved in 2009; side-load courts sized to the 2009 aprons. Proposed impervious 37,658 sf (22.7%).

4. ESD to the MEP: 7 practices — micro-bioretenention (M-6) on each lot and roadside dry swales with check dams (M-8) in the R/W. ESDv required 5,299 cf, provided 7,893 cf (MDE Manual Ch. 5, Table 5.3, HSG C).

5. ESC integration: practice footprints are kept out of the sediment-trapping sequence and are built last, after the contributing area is stabilized; sediment control is shown on C-500.

D-3 OUTFALLS AND RECEIVING AREAS

1. POI-1 lies where the Estates Court swales and the overland flow from the lots leave the tract, discharging to the MD 210 roadside ditch (SHA). The outfall is not on a stream or within a 100-yr floodplain; the receiving area is the state highway drainage system, which SHA must accept under the access permit.

D-4 OUTFALL STABILIZATION

1. POI-1: 10-yr velocity 3.3 ft/s is within 4.0 ft/s for a grass-lined channel; rock outlet protection is still provided where the swale meets the MD 210 roadside ditch (SHA), so the 100-yr flow (4.0 ft/s) does not cut a gully at the transition. Normal depth at the 100-yr flow 1.14 ft in the grass-lined roadside swale, 2-ft bottom, 3:1 sides, n = 0.035 at 1.5% slope. Upstream inflow from off site (0.49 ac) enters as sheet flow along the tract line and is carried by the swales; no concentrated inflow point needs stabilization.

POI-1 — COVER, CURVE NUMBER AND Tc (165,902 SF, HSG C)

CONDITION	WOODS SF	OPEN SPACE SF	IMPERVIOUS SF	CN	Tc HR
Existing	0	165,902	0	74	0.285
Proposed	0	128,244	37,658	79.4	0.285

TIME OF CONCENTRATION — PROPOSED (TR-55)

SEGMENT	L FT	S FT/FT	V FPS	Tt HR
sheet flow, dense grass	100	0.0152	0.10	0.266
shallow concentrated, unpaved	137	0.0152	1.99	0.019

POI-1 — PEAK DISCHARGE, EXISTING VS. PROPOSED (NO ESD CREDIT)

STORM YR	P 24-HR IN	Q EXIST CFS	Q PROP CFS	CHANGE	RUNOFF EXIST CF	RUNOFF PROP CF
1	2.63	2.08	3.35	+1.27	9,439	13,130
2	3.19	3.48	5.06	+1.58	14,253	18,776
10	4.93	8.87	11.36	+2.49	31,916	38,459
100	8.51	22.16	24.85	+2.69	74,438	83,480

POI-1 — OUTFALL VELOCITY CHECK (MANNING, NORMAL DEPTH)

SECTION	S FT/FT	Q10 CFS	V10 FPS	Q100 CFS	V100 FPS	d100 FT	V ALLOW FPS
grass-lined roadside swale, 2-ft bottom, 3:1 sides, n = 0.035	0.0152	11.36	3.27	24.85	4.01	1.14	4.0

D-10 COMPUTATIONS

1. ESDv required and provided per POI: BMP Summary Table (C-000). Rainfall: NOAA Atlas 14 Vol. 2 Ver. 3, PFDS point estimate, 38.6752 N 77.0040 W, partial duration series, 24-hr, retrieved 2026-09-30.

2. POI-1: 3.81 ac, CN 74 → 79.4, Tc 0.285 → 0.285 hr; 100-yr 22.2 → 24.9 cfs (+2.7 cfs), runoff 74,438 → 83,480 cf.

3. No ESD credit is taken in the 100-yr comparison (conservative). ESD to the MEP satisfies channel protection where the Table 5.3 target is met.

4. Downstream adequacy of the MD 210 roadside ditch (SHA) for the 10- and 100-yr flows at each POI — requires the receiving system's section and capacity (SHA as-builts). If inadequate, 10-yr quantity control is added (checklist D-10).

OUTSTANDING FOR TECHNICAL DESIGN

1. Downstream adequacy of the MD 210 roadside ditch (SHA) for the 10- and 100-yr flows at each POI — requires the receiving system's section and capacity (SHA as-builts). If inadequate, 10-yr quantity control is added (checklist D-10).

METHOD AND SOURCES

NRCS TR-55 graphical peak discharge, Type II 24-hr; CN from TR-55 Table 2-2 (HSG C: woods 70, open space 74, impervious 98); Tc by TR-55 segments along the routed longest path; no ESD credit on the 100-yr. Topography: county 2-ft contour mapping.

NOAA Atlas 14 Vol. 2 Ver. 3, PFDS point estimate, 38.6752 N 77.0040 W, partial duration series, 24-hr, retrieved 2026-09-30

PLAN TYPE
SITE DEVELOPMENT CONCEPT PLAN

PROJECT
ESTATES AT INDIAN HEAD — LOTS 1-6
200-205 ESTATES COURT, ACCOKEEK, MD 20607
PLAT BOOK PM 226 PLAT 83 TAX MAP 151 P-3 WSSC 2206E01
ELECTION DIST. 5 - COUNCIL DIST. 9 - ZONE RR

OWNER / APPLICANT
GERALD WALDMAN REVOCABLE TRUST, 400 N. FLAGLER DR., WEST PALM BEACH, FL 33401 (L-52062.F-043)

ENGINEER OF RECORD
W.L. MEEKINS, INC. — BILL MEEKINS, JR., 3101 RITCHIE ROAD, FORESTVILLE, MD 20747 - 301-736-7115

SHEET TITLE
STORMWATER MANAGEMENT CONCEPT NARRATIVE AND 100-YR COMPUTATIONS

KEY MAP

SCALE
AS NOTED

DATUM: NAD 83 MD STATE PLANE (US FT) / NAVD 88

REVISIONS

NO.	DATE	DESCRIPTION
0	2026-09-30	CONCEPT SUBMISSION 1

PROFESSIONAL CERTIFICATION

I hereby certify that these documents were prepared or approved by me, and that I am a duly licensed professional engineer under the laws of the State of Maryland. License No. _____ Exp. _____

SEAL

CONCEPT SUBMISSION 1 — NOT SEALED

DATE 2026-09-30 JOB KEA-EIN 2026

DRAWN WITH SCALE: SPATIAL ENGINE CAD-PILOT

SHEET INDEX


C-000 COVER SHEET — BMP SUMMARY, DPE CHECKLIST AND NOTES
C-100 EXISTING CONDITIONS AND ENVIRONMENTAL FEATURES
C-200 SITE LAYOUT, GRADING AND PAVING PLAN
C-300 UTILITY, STREET LIGHT AND STREET TREE PLAN
C-400 STORMWATER MANAGEMENT CONCEPT AND DRAINAGE AREA MAP
★ C-410 STORMWATER MANAGEMENT CONCEPT NARRATIVE AND 100-YR COMPUTATIONS
C-500 SEDIMENT AND EROSION CONTROL PLAN
C-600 DETAILS

RESERVED FOR PRINCE GEORGE'S COUNTY DPE APPROVAL
5" x 3" — KEEP BLANK (PLAN 5" RIGHT MARGIN, CHECKLIST A.3)




SHEET

C-410


6 OF 8

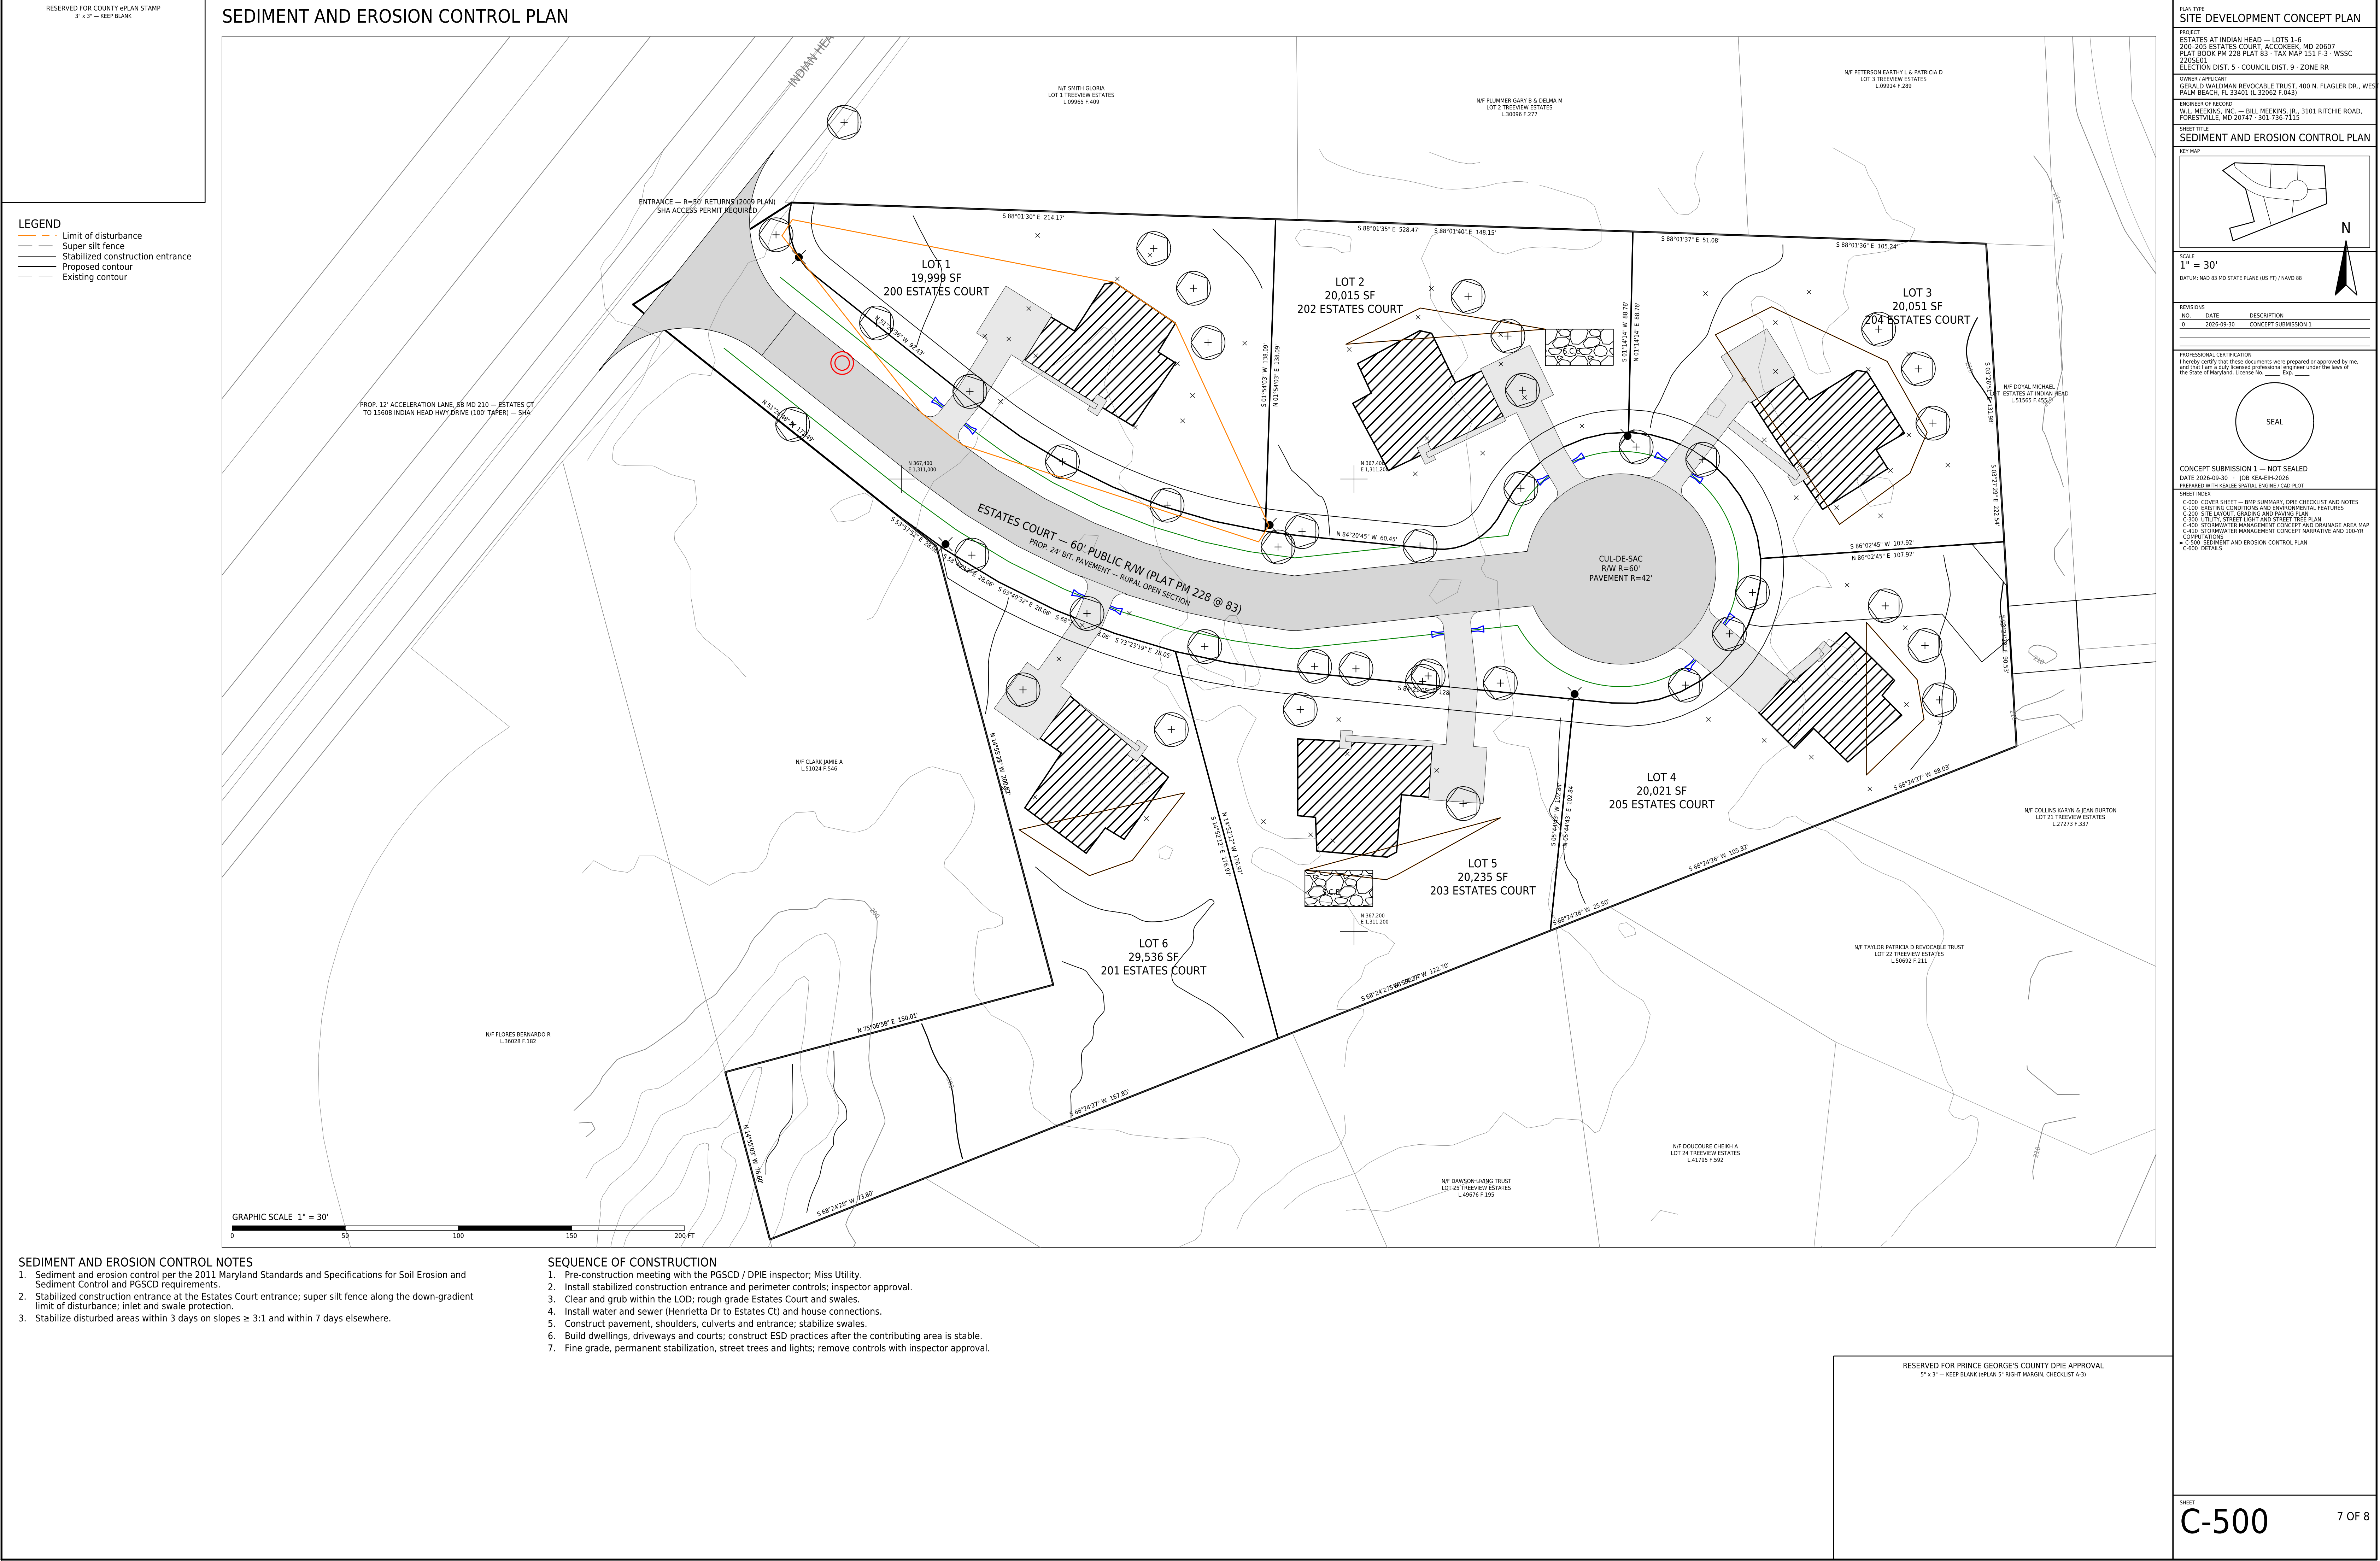

DETAILS

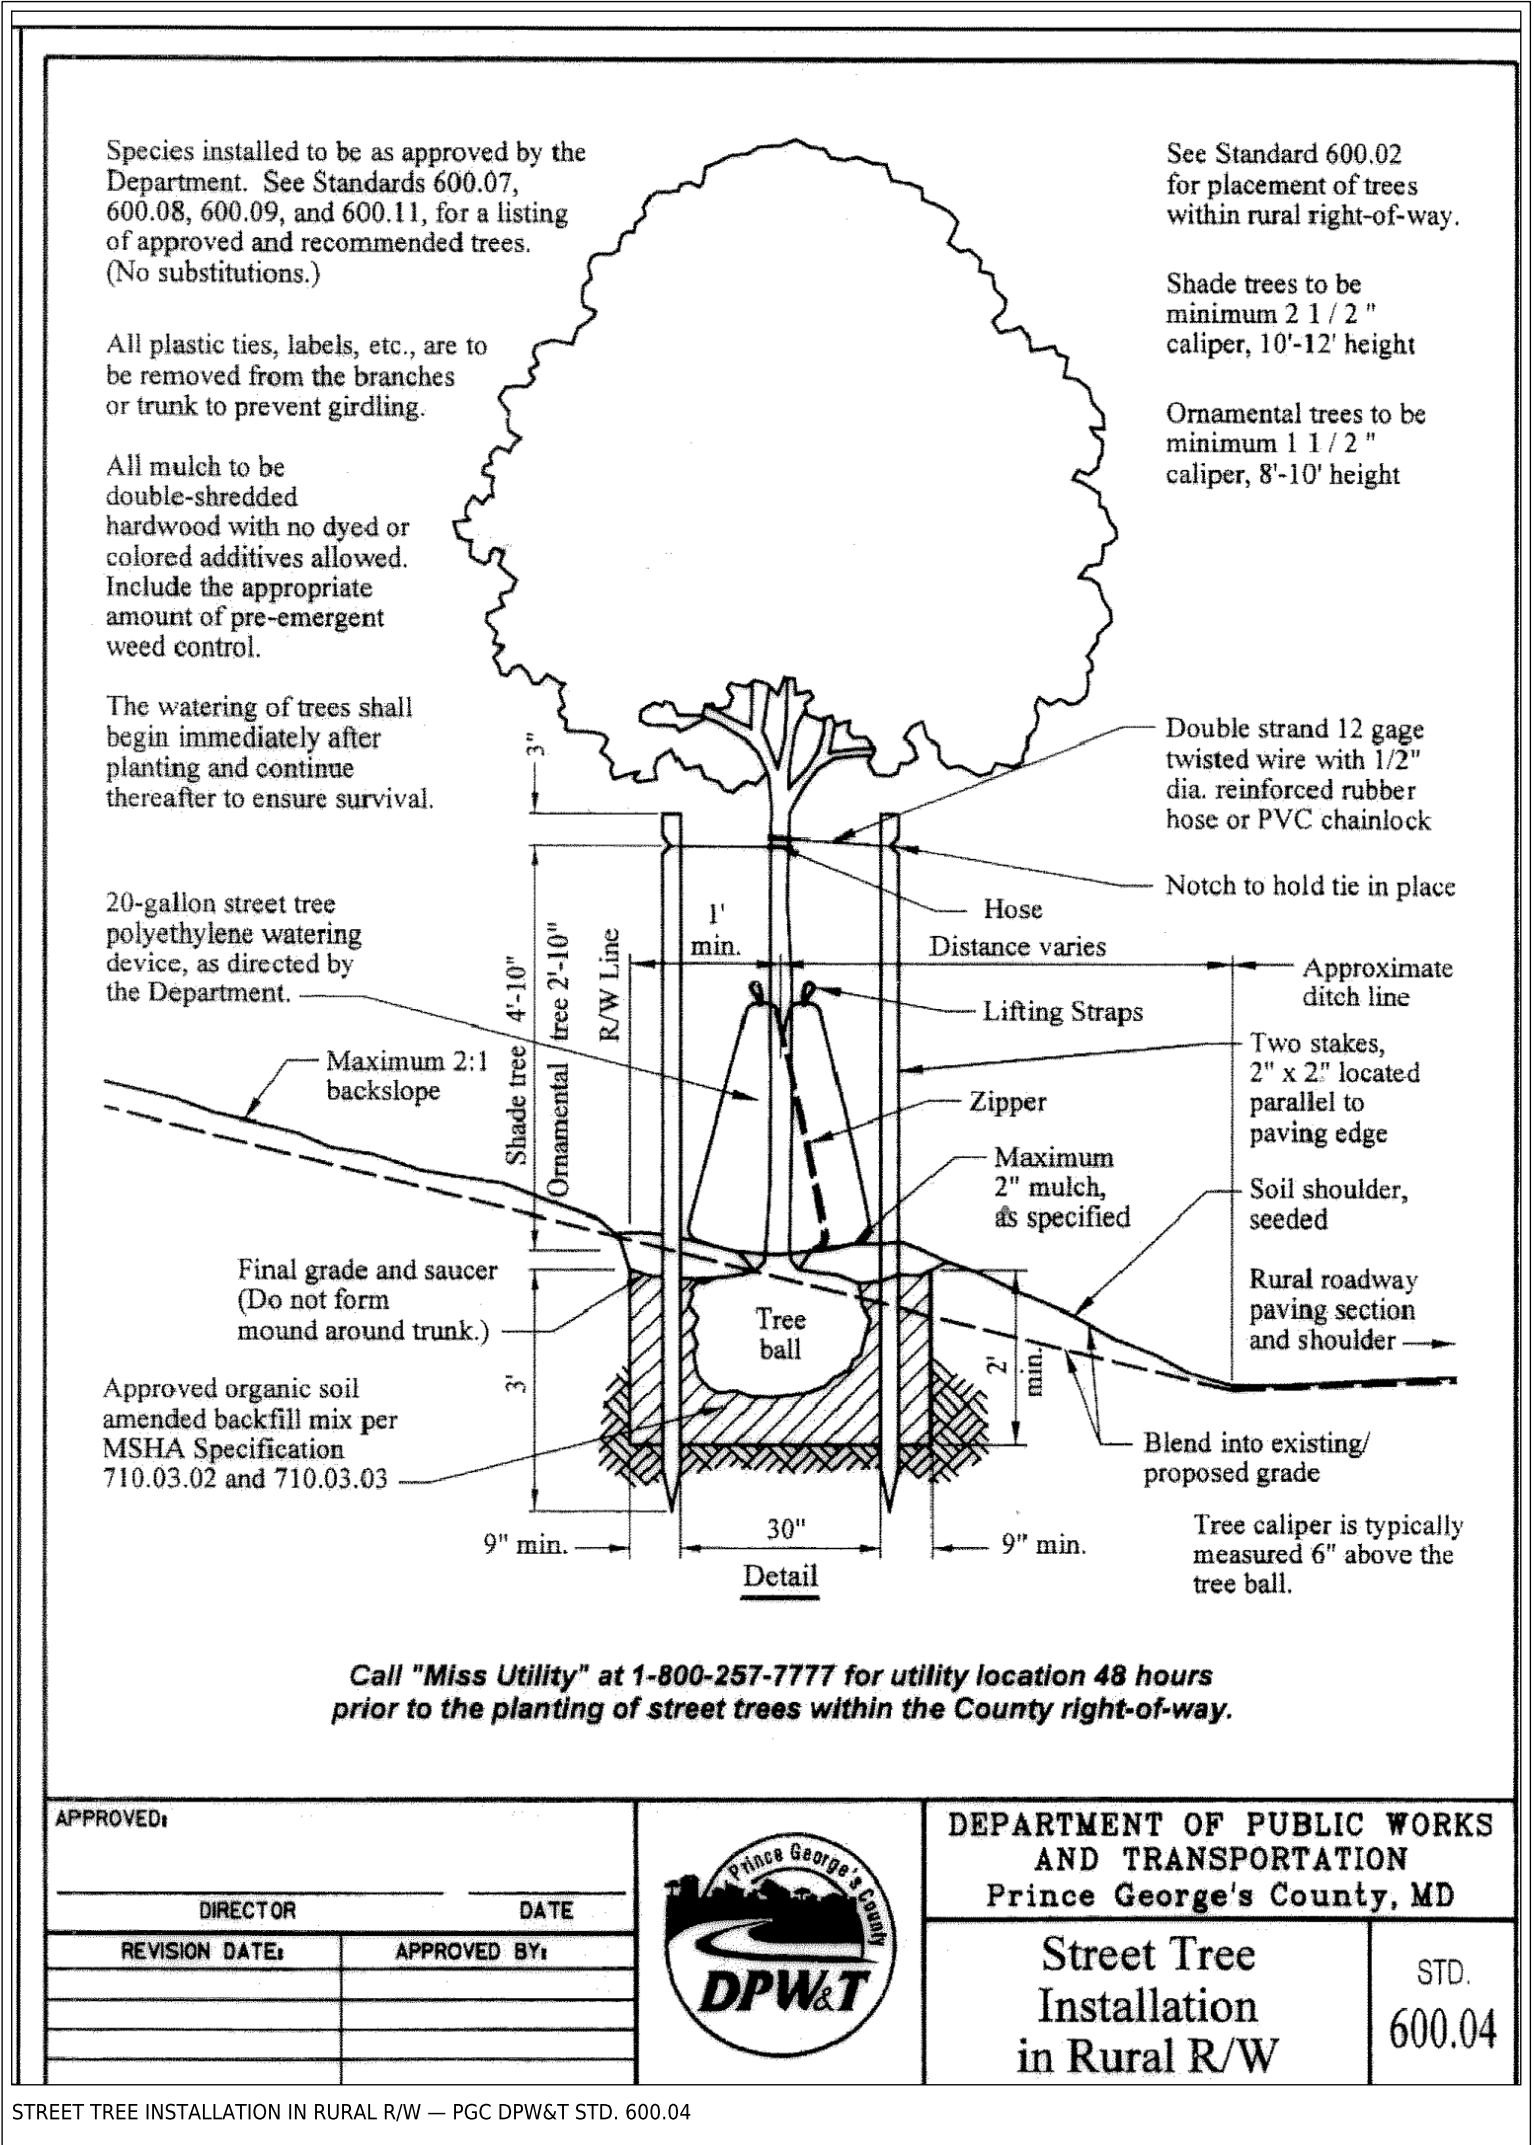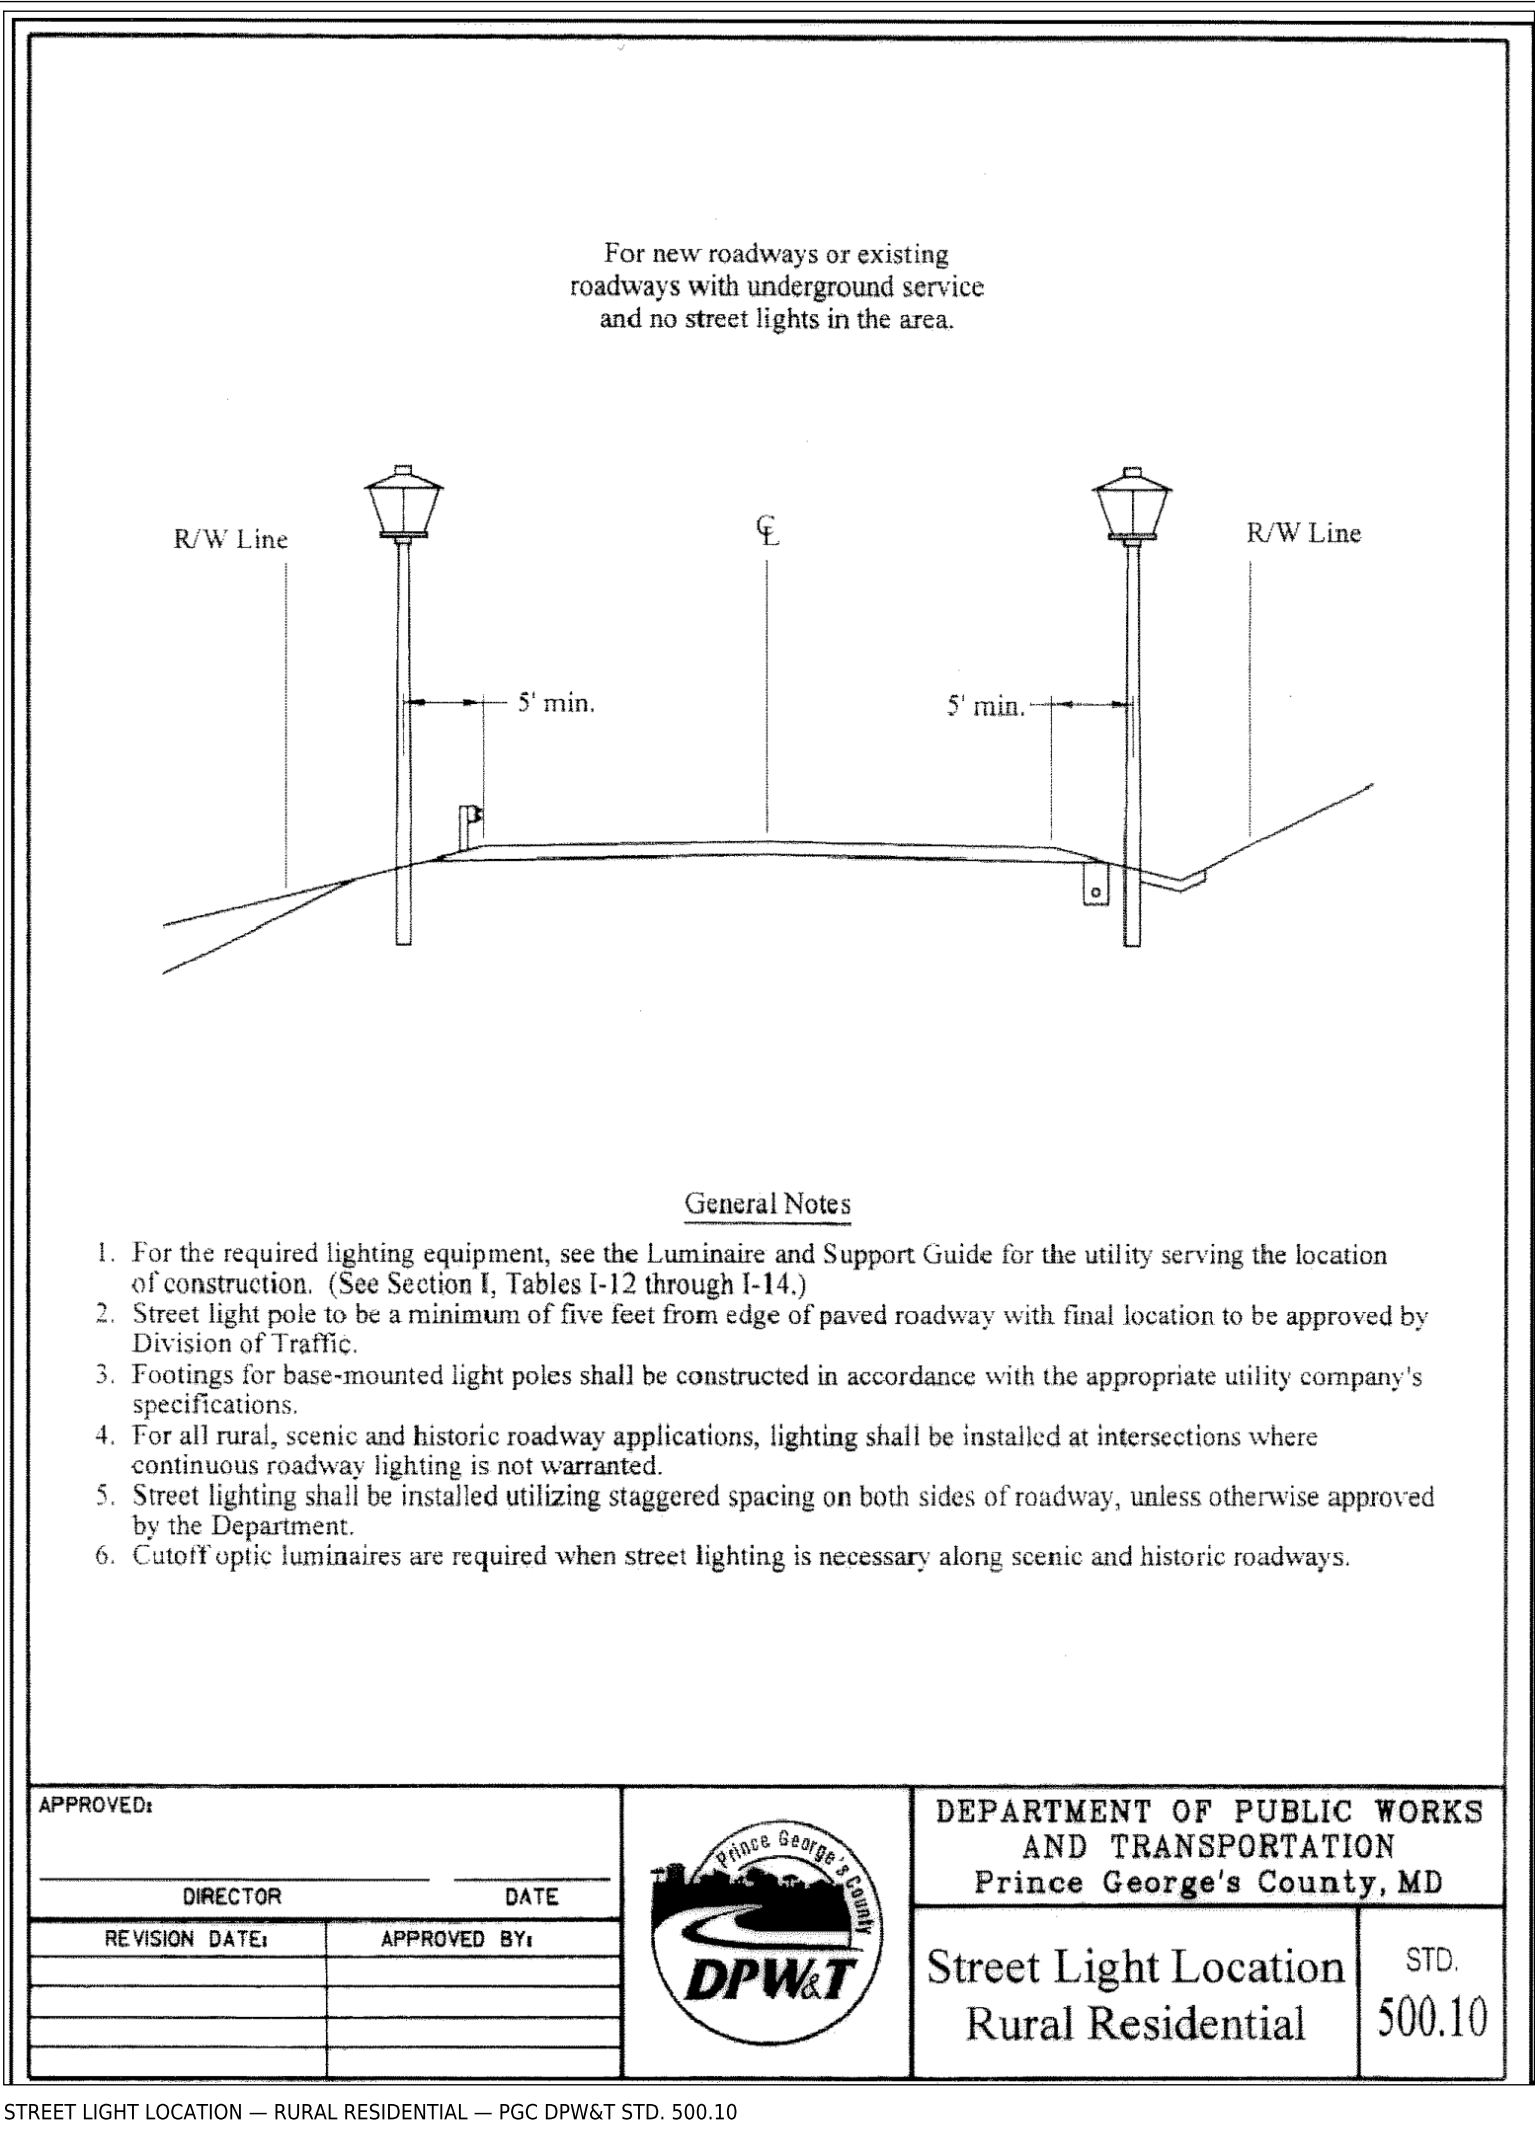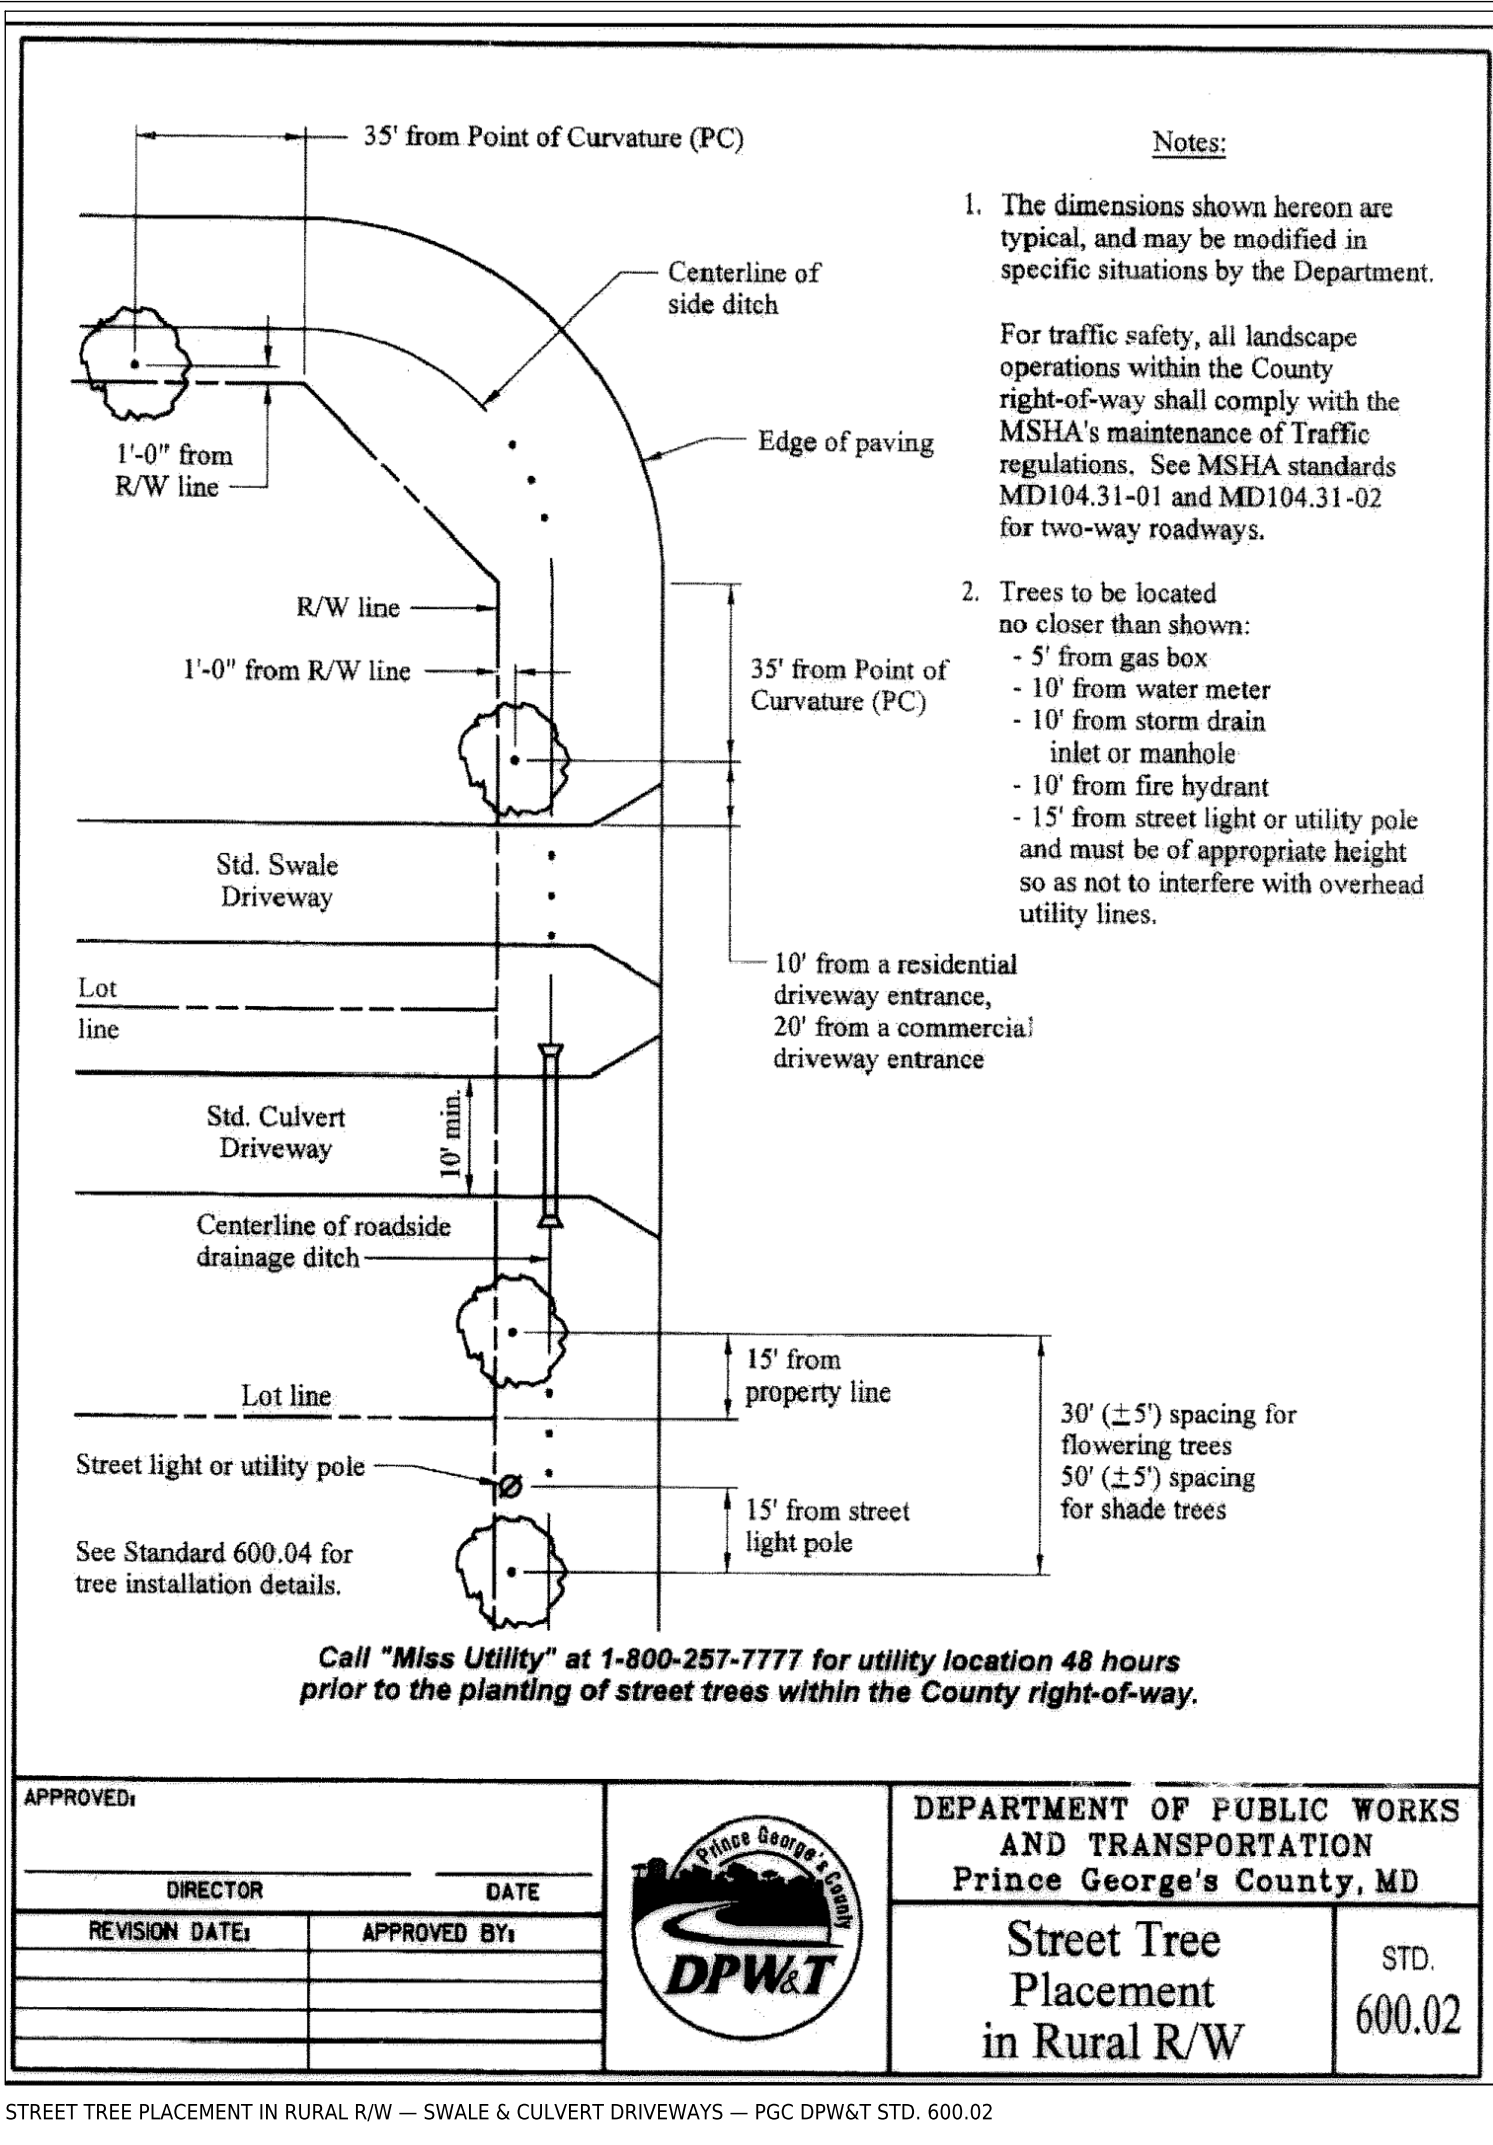


ESTATES COURT — TYPICAL SECTION (RURAL OPEN SECTION, 60' R/W)

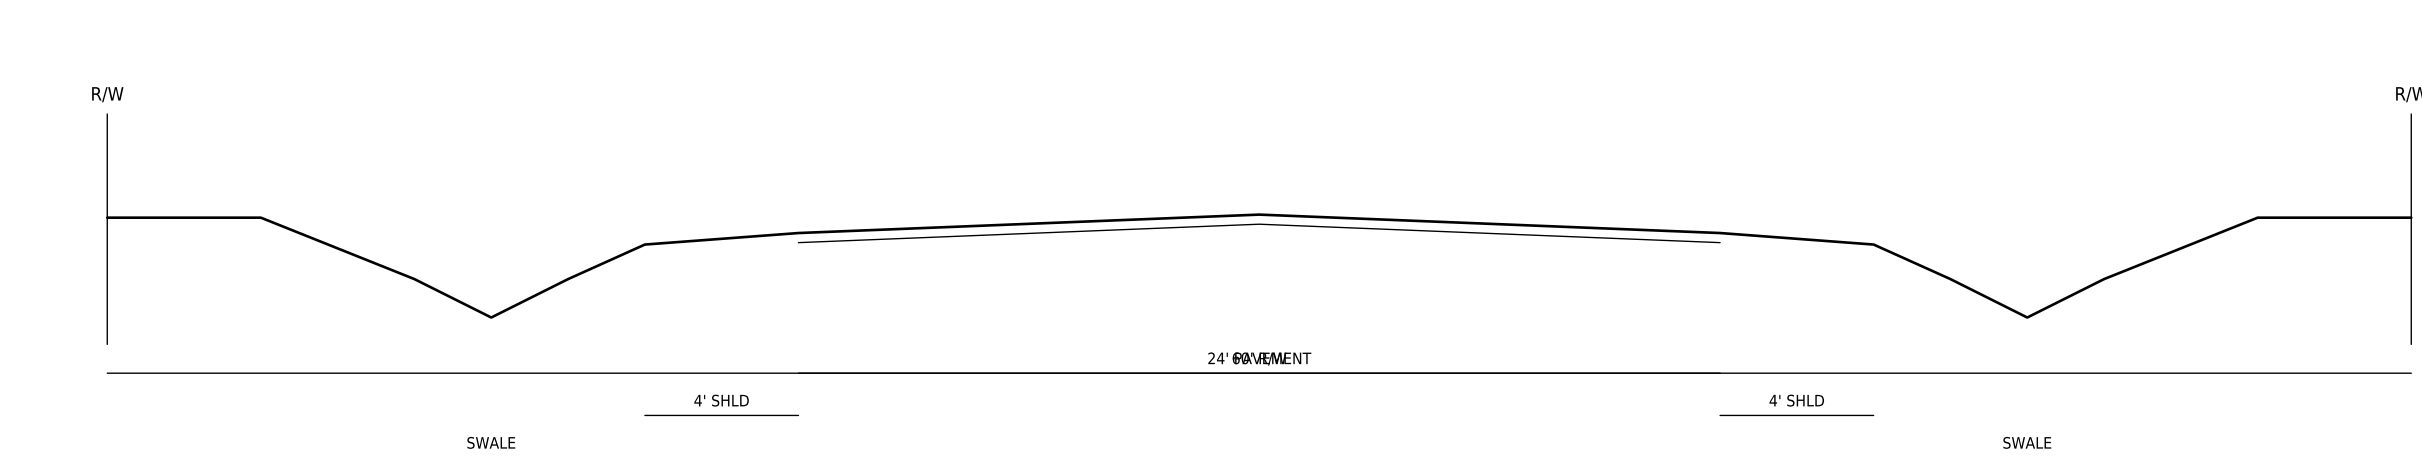


1 1/2" SURFACE + 2 1/2" BASE BIT. CONC. ON 6" GAB (DPW&T PAVEMENT SCHEDULE FOR RURAL RESIDENTIAL — CONFIRM)
CROSS SLOPE 2%; 4-FT STABILIZED SHOULDERS, SWALE FLOWLINE 20 FT OFF CENTRELINE, 3:1 SIDE SLOPES
DRIVEWAYS CROSS THE SWALE ON 15" RCP CULVERTS WITH FLARED END SECTIONS (DPW&T STD. 600.02)

MICRO-BIORETENTION (M-6) — TYPICAL SECTION

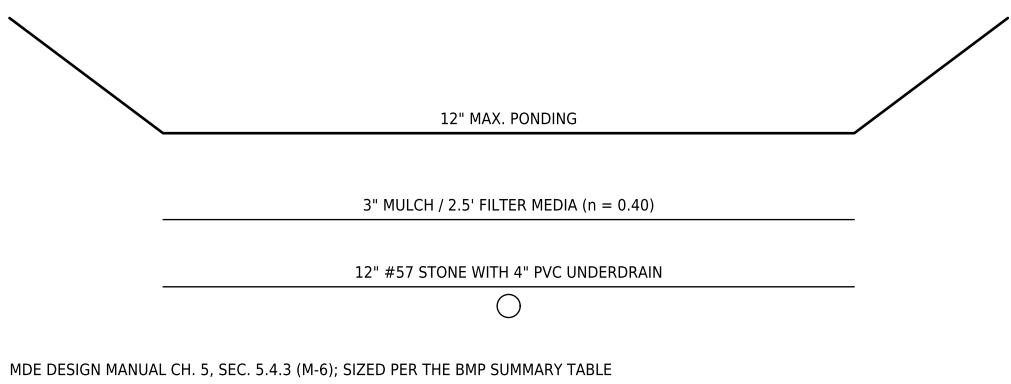

DRY SWALE (M-8) WITH CHECK DAM

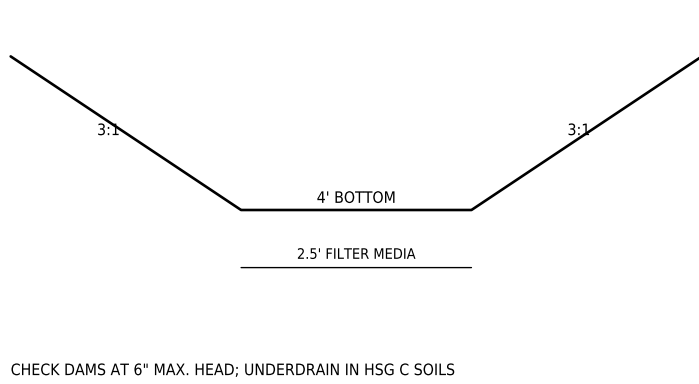

PLAN TYPE
SITE DEVELOPMENT CONCEPT PLAN

PROJECT
ESTATES AT INDIAN HEAD — LOTS 1-6
200-205 ESTATES COURT, ACCOKEEK, MD 20607
PLAT BOOK PM 226 PLAT 83 TAX MAP 253 P-3 WSSC
220620

OWNER / APPLICANT
GERALD WALDMAN REVOCABLE TRUST, 400 N. FLAGLER DR., WEST
PALM BEACH, FL 33401 (L-32062.F-043)

ENGINEER OF RECORD
W.L. MECKINS, INC. — BILL MECKINS, JR., 3101 RITCHIE ROAD,
FORESTVILLE, MD 20747 / 301-736-7115

SHEET TITLE
DETAILS

KEY MAP

SCALE
AS NOTED

DATUM: NAD 83 MD STATE PLANE (US FT) / NAVD 88

REVISIONS

NO.	DATE	DESCRIPTION
0	2026-09-30	CONCEPT SUBMISSION 1

PROFESSIONAL CERTIFICATION
I hereby certify that these documents were prepared or approved by me,
and that I am a duly licensed professional engineer under the laws of
the State of Maryland. License No. _____ Exp. _____

SEAL

CONCEPT SUBMISSION 1 — NOT SEALED
DATE 2026-09-30 JOB KEA-EH-2026
PREPARED WITH KHAZE SPOTIAL ENGINE / CAD-PILOT

SHEET INDEX

C-000	COVER SHEET — BMP SUMMARY, DPE CHECKLIST AND NOTES
C-100	SITING, CONDITIONS AND ENVIRONMENTAL FEATURES
C-200	SITE EROSION, GRADING AND PAVING PLAN
C-300	UTILITY, STREET LIGHT AND STREET TREE PLAN
C-400	STORMWATER MANAGEMENT CONCEPT AND DRAINAGE AREA MAP
C-500	STORMWATER MANAGEMENT CONCEPT NARRATIVE AND 100-YR CONSTRUCTIONS
C-600	SEDIMENT AND EROSION CONTROL PLAN

• C-600: DETAILS