



KEALEE


design, build, deliver

PROJECT
4102 Webster St
ADDRESS
4102 Webster St, Brentwood, MD 20722
JURISDICTION
prince georges md
ZONE
RSF-65
SHEET
C-000 — Cover Sheet, Approvals and General Notes
SCALE
1" = 10'
STATUS
PRELIMINARY
SHEET NO.
1 OF 10
COORDINATES
EPSG:2248
H: NAD83
V: NAVD83 (feet)

REVISIONS

— NONE —

SOURCE AND ACCURACY
Parcel boundary — Jurisdiction gis — Maryland Department of Information Technology — MD MAP — level 1
ElevationMapServer1 — Contour - 2 Ft (2023) — Prince George's County / M-NCPPC — PGAtlas — level 1

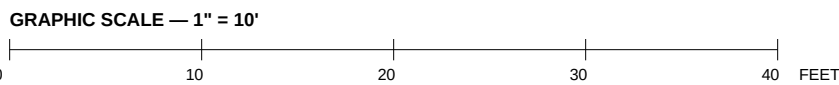

PRELIMINARY — BASED ON GIS/LIDAR DATA — NOT FOR
PERMIT OR CONSTRUCTION.



KEALEE

design, build, deliver

PROJECT

4102 Webster St

ADDRESS

4102 Webster St, Brentwood, MD 20722

JURISDICTION

prince georges md

ZONE

RSF-65

SHEET

C-100 — Existing Conditions and Boundary Plan

SCALE

1" = 10'

STATUS

PRELIMINARY

SHEET NO.

2 OF 10

COORDINATES

EPSG:2248

H: NAD83

V: NAVD83 (feet)

PROFESSIONAL RESPONSIBILITY

Maryland Licensed Surveyor

certifies boundary determination


SEAL AND SIGNATURE

All content on this sheet falls within one professional scope.

REVISIONS

— NONE —

SOURCE AND ACCURACY
Parcel boundary — Jurisdiction gis — Maryland Department of Information Technology — MD MAP — level 1
ElevationMapServer1 — Contour - 2 Ft (2023) — Prince George's County / M-NCPPC — PGAtlas — level 1

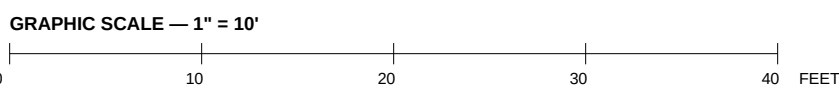

PRELIMINARY — BASED ON GIS/LIDAR DATA — NOT FOR
PERMIT OR CONSTRUCTION.



KEALEE

design, build, deliver

PROJECT

4102 Webster St

ADDRESS

4102 Webster St, Brentwood, MD 20722

JURISDICTION

prince georges md

ZONE

RSF-65

SHEET

C-200 — Overall Site and Zoning Plan

SCALE

1" = 10'

STATUS

PRELIMINARY

SHEET NO.

3 OF 10

COORDINATES


H: NAD83

V: NAVD88 (feet)

REVISIONS

— NONE —

SOURCE AND ACCURACY
Parcel boundary — Jurisdiction gis — Maryland Department of Information Technology — MD MAP — level 1
ElevationMapServer1 — Contour - 2 Ft (2023) — Prince George's County / M-NCPPC — PGAtlas — level 1

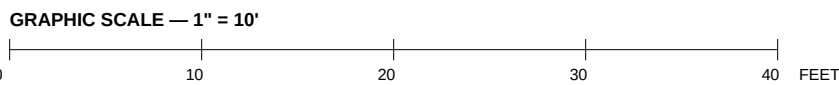


PRELIMINARY — BASED ON GIS/LIDAR DATA — NOT FOR
PERMIT OR CONSTRUCTION.

GRADING CERTIFICATE
I HEREBY CERTIFY THAT THIS PLAN CONFORMS TO THE REQUIREMENTS OF SUBTITLE 32, DIVISION 2 OF THE CODE OF PRINCE GEORGE'S COUNTY WATER RESOURCES PROTECTION AND GRADING CODE, AND THAT I OR MY STAFF HAVE INSPECTED THIS SITE AND THAT DRAINAGE FLOWS FROM UPHILL PROPERTIES ONTO THIS SITE, AND FROM THIS SITE ONTO DOWNHILL PROPERTIES, HAVE BEEN ADDRESSED IN SUBSTANTIAL ACCORDANCE WITH APPLICABLE CODES. SIGNED, SEALED AND DATED BY A PROFESSIONAL ENGINEER LICENSED IN THE STATE OF MARYLAND.
Prince George's County DPE, Site Rough Grading Design Review Checklist, Item A-10

STABILIZATION COMPLIANCE PREAMBLE
Stabilization practices on all projects must be in compliance with the requirements of COMAR 26.17.01 by January 9, 2013, regardless of when an erosion and sediment control plan was approved.
COMAR 26.17.03.06(2), Grandfathering of approved plans

STANDARD STABILIZATION NOTE
Following initial soil disturbance or re-disturbance, permanent or temporary stabilization must be completed within: a.) Three (3) calendar days as to the surface of all perimeter dikes, swales, ditches, perimeter slopes, and all slopes steeper than 3 horizontal to 1 vertical (3:1); and b.) Seven (7) calendar days as to all other disturbed or graded areas on the project site not under active grading.
2011 Maryland Standards and Specifications for Soil Erosion and Sediment Control, "Standard Stabilization Note" (adopted by COMAR 26.17.01.09A(1))

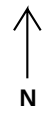

KEALEE
design, build, deliver

PROJECT
4102 Webster St

ADDRESS
4102 Webster St, Brentwood, MD 20722

JURISDICTION
prince georges md

ZONE
RSF-65

SHEET
C-400 — Grading and Drainage Plan

SCALE
1" = 10'


STATUS
PRELIMINARY

SHEET NO.
4 OF 10

COORDINATES
EPSG:2248
H: NAD83
V: NAVD83 (feet)

PRELIMINARY — BASED ON GIS/LIDAR DATA — NOT FOR
PERMIT OR CONSTRUCTION.

SOURCE AND ACCURACY
Parcel boundary — Jurisdiction gis — Maryland Department of Information Technology — MD MAP — level 1
ElevationMapServer — Contour - 2 Ft (2023) — Prince George's County / M-NCPPC — PGAtlas — level 1

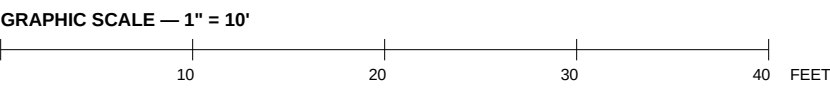

REVISIONS

— NONE —



KEALEE


design, build, deliver

PROJECT
4102 Webster St
ADDRESS
4102 Webster St, Brentwood, MD 20722
JURISDICTION
prince georges md
ZONE
RSF-65
SHEET
C-500 — Utility Plan
SCALE
1" = 10'
STATUS
PRELIMINARY
SHEET NO.
5 OF 10
COORDINATES
EPSG:2248
H: NAD83
V: NAVD83 (feet)

REVISIONS

— NONE —

SOURCE AND ACCURACY
Parcel boundary — Jurisdiction gis — Maryland Department of Information Technology — MD MAP — level 1
ElevationMapServer1 — Contour - 2 Ft (2023) — Prince George's County / M-NCPPC — PGAtlas — level 1

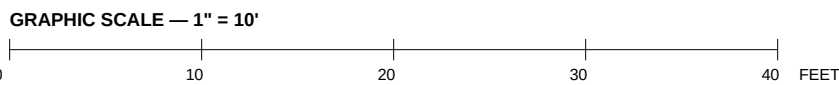

PRELIMINARY — BASED ON GIS/LIDAR DATA — NOT FOR
PERMIT OR CONSTRUCTION.




KEALEE
design, build, deliver

PROJECT
4102 Webster St
ADDRESS
4102 Webster St, Brentwood, MD 20722
JURISDICTION
prince georges md
ZONE
RSF-65
SHEET
C-600 — Stormwater Management Plan
SCALE
1" = 10'
STATUS
PRELIMINARY
SHEET NO.
6 OF 10
COORDINATES
EPSG:2248
H: NAD83
V: NAVD83 (feet)

REVISIONS

— NONE —

SOURCE AND ACCURACY
Parcel boundary — Jurisdiction gis — Maryland Department of Information Technology — MD MAP — level 1
ElevationMapServer1 — Contour - 2 Ft (2023) — Prince George's County / M-NCPPC — PGAtlas — level 1

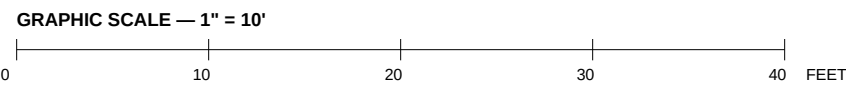

PRELIMINARY — BASED ON GIS/LIDAR DATA — NOT FOR
PERMIT OR CONSTRUCTION.

STABILIZATION COMPLIANCE PREAMBLE
Stabilization practices on all projects must be in compliance with the requirements of COMAR 26.17.01 by January 9, 2013, regardless of when an erosion and sediment control plan was approved.
COMAR 26.17.01.06(2), Grandfathering of approved plans

STANDARD STABILIZATION NOTE
Following initial soil disturbance or re-disturbance, permanent or temporary stabilization must be completed within: a.) Three (3) calendar days as to the surface of all perimeter dikes, swales, ditches, perimeter slopes, and all slopes steeper than 3 horizontal to 1 vertical (3:1); and b.) Seven (7) calendar days as to all other disturbed or graded areas on the project site not under active grading.
2011 Maryland Standards and Specifications for Soil Erosion and Sediment Control, "Standard Stabilization Note" (adopted by COMAR 26.17.01.06A(1))




KEALEE
design, build, deliver

PROJECT
4102 Webster St
ADDRESS
4102 Webster St, Brentwood, MD 20722
JURISDICTION
prince georges md
ZONE
RSF-65
SHEET
C-700 — Sediment and Erosion Control Plan
SCALE
1" = 10'
STATUS
PRELIMINARY
SHEET NO.
7 OF 10
COORDINATES
EPSG:2248
H: NAD83
V: NAVD83 (feet)

PRELIMINARY—BASED ON GIS/LIDAR DATA—NOT FOR
PERMIT OR CONSTRUCTION.

SOURCE AND ACCURACY
Parcel boundary — Jurisdiction gis — Maryland Department of Information Technology — MD MAP — level 1
ElevationMapServer1 — Contour - 2 Ft (2023) — Prince George's County / M-NCPPC — PGAtlas — level 1

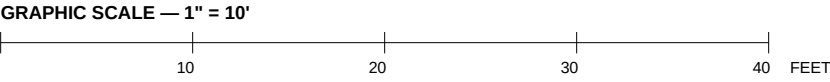

REVISIONS

— NONE —



KEALEE


design, build, deliver

PROJECT
4102 Webster St
ADDRESS
4102 Webster St, Brentwood, MD 20722
JURISDICTION
prince georges md
ZONE
RSF-65
SHEET
C-900 — Civil Details
SCALE
1" = 10'
STATUS
PRELIMINARY
SHEET NO.
8 OF 10
COORDINATES
EPSG:2248
H: NAD83
V: NAVD83 (feet)

REVISIONS

— NONE —

SOURCE AND ACCURACY
Parcel boundary — Jurisdiction gis — Maryland Department of Information Technology — MD MAP — level 1
ElevationMapServer1 — Contour - 2 Ft (2023) — Prince George's County / M-NCPPC — PGAtlas — level 1

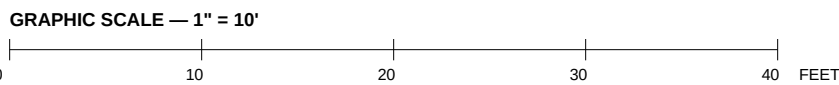

PRELIMINARY — BASED ON GIS/LIDAR DATA — NOT FOR
PERMIT OR CONSTRUCTION.



KEALEE

design, build, deliver

PROJECT

4102 Webster St

ADDRESS

4102 Webster St, Brentwood, MD 20722

JURISDICTION

prince georges md

ZONE

RSF-65

SHEET

L-100 — Landscape and Tree Canopy Plan

SCALE

1" = 10'

STATUS

PRELIMINARY

SHEET NO.

9 OF 10

COORDINATES


H: NAD83

V: NAVD88 (feet)

REVISIONS

— NONE —

SOURCE AND ACCURACY
Parcel boundary — Jurisdiction gis — Maryland Department of Information Technology — MD MAP — level 1
ElevationMapServer1 — Contour - 2 Ft (2023) — Prince George's County / M-NCPPC — PGAtlas — level 1

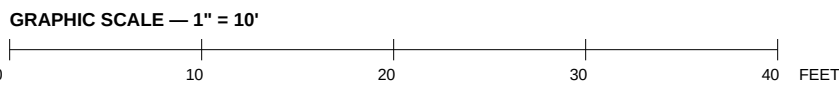

PRELIMINARY — BASED ON GIS/LIDAR DATA — NOT FOR
PERMIT OR CONSTRUCTION.



KEALEE


design, build, deliver

PROJECT
4102 Webster St
ADDRESS
4102 Webster St, Brentwood, MD 20722
JURISDICTION
prince georges md
ZONE
RSF-65
SHEET
TCP-NRI — Tree Conservation Plan / Natural Resource Inventory Coordination
SCALE
1" = 10'
STATUS
PRELIMINARY
SHEET NO.
10 OF 10
COORDINATES
EPSG:2248
H: NAD83
V: NAVD83 (feet)

REVISIONS

— NONE —

SOURCE AND ACCURACY
Parcel boundary — Jurisdiction gis — Maryland Department of Information Technology — MD MAP — level 1
ElevationMapServer1 — Contour - 2 Ft (2023) — Prince George's County / M-NCPPC — PGAdas — level 1

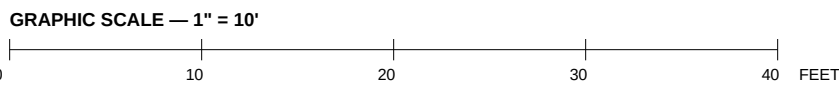

PRELIMINARY — BASED ON GIS/LIDAR DATA — NOT FOR
PERMIT OR CONSTRUCTION.