

KEALEE

design, build, deliver

PROJECT
1005 Rollins Ave

ADDRESS
1005 Rollins Ave

JURISDICTION
prince georges md

ZONE
RSF-65

SHEET
C-100 — Existing Conditions and Boundary Plan

SCALE
1" = 20'

STATUS
PRELIMINARY

SHEET NO.
1 OF 5

COORDINATES
EPSG:2248

H: NAD83

V: NAVD83 (feet)

PROFESSIONAL RESPONSIBILITY

Maryland Licensed Surveyor

certifies boundary_determination, topographic_survey

SEAL AND SIGNATURE

All content on this sheet falls within one professional scope.

SITE DATA

ZONE RSF-65

TAX / PARCEL ID 348854

GROSS LOT AREA 9,596 SF 0.220 AC

LOT FRONTAGE 45' MIN 65.07'

SETBACKS REQUIRED PROVIDED

FRONT YARD 25' 25'

SIDE YARD 8' 8'

REAR YARD 30' 30'

COVERAGE MAX PROPOSED

LOT COVERAGE 35% 17.1%

BUILDING FOOTPRINT — 1,640 SF

DATUM

HORIZONTAL EPSG:2248 NAD83

VERTICAL NAVD83 (feet)

SITE ANALYSIS

1. Gross tract area 9,596 SF

2. Area of dwelling 1,640 SF

3. Wooded area NOT ESTABLISHED

4. Floodplain area NOT ESTABLISHED

5. Net tract area 9,596 SF

6. TOTAL AREA DISTURBED NOT QUANTIFIED

SEQUENCE OF CONSTRUCTION

1. Pre-construction meeting 1 DAY

2. Obtain necessary permits 2 DAYS

3. Notify Miss Utility at 811 at least 48 hours prior to any excavation 1 DAY

4. Construct stabilized construction entrance and perimeter sidewalk control 2 DAYS

5. Rough grade, construct dwelling, utilities and driveway 12 MONTHS

6. Fine grade and stabilize all disturbed areas 1 DAY

7. Remove sediment control devices when written permission has been granted 1 DAY

TOTAL ESTIMATED TIME OF CONSTRUCTION: 12 MONTHS

GENERAL NOTES

1. CONTRACTOR SHALL CONTACT MISS UTILITY AT 811 A MINIMUM OF 48 HOURS PRIOR TO ANY EXCAVATION.

2. ALL EXISTING AND PROPOSED UTILITIES SHOWN PER PGC CODE SEC. 30-106.

3. PROPOSED GRADE SHOWN SOLID; EXISTING GRADE SHOWN DASHED.

4. ROUGH EARTHWORK GRADES AND UTILITY ELEVATIONS SHOWN TO TENTHS OF A FOOT.

5. BOUNDARY SHOWN IS COMPILED JURISDICTION GIS, NOT A BOUNDARY SURVEY.

LEGEND

— PROPERTY BOUNDARY

- - - - - BRL — BUILDING RESTRICTION LINE

— PROPOSED STRUCTURE

— EXISTING CONTOUR — PGATLAS 2 FT (2023), NAVD83

- - - - - STREET CENTRELINE

— PROPOSED PAVEMENT — DRIVEWAY / WALK

- - - - - EASEMENT

PRINCE GEORGE'S COUNTY SOIL CONSERVATION DISTRICT APPROVAL

SEDIMENT CONTROL, GRADING, SOILS & DRAINAGE

SIGNATURE DATE

DPE SITEROAD PLAN REVIEW DIVISION APPROVAL

SIGNATURE DATE

REVISIONS

— NONE —

SOILS TABLE

USDA NRCS SSURGO — required by POC Code Sec. 30-130(a)(13)

MAP UNIT	MAP UNIT NAME	K-FACTOR	HYDRIC	HYD. GROUP	DRAINAGE CLASS
AaB	Adelphia silt loam, 2 to 5 percent slopes complex	37	No	C	Moderately well drained
ACA	Adelphia Aquasol complex, 0 to 2 percent slopes	43	No	D	Somewhat poorly drained
ACB	Adelphia Aquasol complex, 0 to 2 percent slopes	37	No	C	Moderately well drained
ADA	Adelphia Hartsel complex, 0 to 2 percent slopes	24	No	BD	Somewhat poorly drained
ADB	Adelphia Hartsel complex, 0 to 2 percent slopes	37	No	C	Moderately well drained
AaB	Adelphia Hartsel complex, 2 to 5 percent slopes	24	No	BD	Somewhat poorly drained
AaB	Adelphia Hartsel complex, 2 to 5 percent slopes	37	No	C	Moderately well drained
AaC	Adelphia Hartsel complex, 5 to 10 percent slopes	24	No	BD	Somewhat poorly drained

SOURCE AND ACCURACY

Parcel boundary — Jurisdiction gis — Prince George's County / M-ACPPC — PGAtlas Property — level 1

Existing contours — Prince George's County / M-NCPPC — PGAtlas — level 1

Contours: PGAtlas ElevationMapServer1 — Contour = 2 Ft (2023), 2 ft interval, NAVD83 (feet)

GRAPHIC SCALE — 1" = 20'

0 20 40 60 80 FEET



KEALEE

design, build, deliver

PROJECT

1005 Rollins Ave

1005 Rollins Ave

JURISDICTION

prince georges m

RSF-65

SHEET
C-200 — Overall Site and Zoning Plan

SCALE
15 20

STATUS

PRELIMINARY

SHEET NO. 1111

2 OF 3

COORDINATE
ERSG-2249

H: NAD83

V: NAVD88 (feet)

PROFESSIONAL R

Maryland Professional Engineer
certifies: site layout

[illegible]

SEAL AND SIGNATURE

Architect

cermes, architectural_100print

100

This sheet carries content from

SITE DATA		
ZONE	RSF-65	
TAX / PARCEL ID	348854	
GROSS LOT AREA	9,596 SF	0.220 AC
LOT FRONTAGE	45 MIN	65.00'
SETBACKS REQUIRED		PROVIDED
FRONT YARD	25'	25'
SIDE YARD	5'	5'
REAR YARD	20'	20'
COVERAGE MAX		PROPOSED
LOT COVERAGE	35%	17.1%
BUILDING FOOTPRINT	—	1,640 SF
DATUM		
HORIZONTAL	EPSG-2248	NAD83
VERTICAL	NAVD88 (feet)	

SITE ANALYSIS

1. Gross tract area	9,596 SF
2. Area of dwelling	1,640 SF
3. Wooded area	NOT ESTABLISHED
4. Floodplain area	NOT ESTABLISHED
5. Net tract area	9,596 SF
6. TOTAL AREA DISTURBED	NOT QUANTIFIED

SEQUENCE OF CONSTRUCTION

1. Pre-construction meeting	1 DAY
2. Obtain necessary permits	2 DAYS
3. Notify Miss Utility at 811 at least 48 hours prior to any excavation	1 DAY
4. Construct stabilized construction entrance and perimeter sediment control	2 DAYS
5. Rough grade; construct dwelling, utilities and driveway	12 MONTHS
6. Fine grade and stabilize all disturbed areas	1 DAY
7. Remove sediment control devices when written permission has been granted by the inspector	1 DAY
TOTAL ESTIMATED TIME OF CONSTRUCTION: 12 MONTHS	

GENERAL NOTES

1. CONTRACTOR SHALL CONTACT MISS UTILITY AT 811 A MINIMUM OF 48 HOURS PRIOR TO ANY EXCAVATION.
2. ALL EXISTING AND PROPOSED UTILITIES SHOWN PER PGC CODE SEC. 32-106.
3. PROPOSED GRADE SHOWN SOLID; EXISTING GRADE SHOWN DASHED.
4. ROUGH EARTHWORK GRADES AND UTILITY ELEVATIONS SHOWN TO TENTHS OF A FOOT.
5. BOUNDARY SHOWN IS COMPILED JURISDICTION GIS, NOT A BOUNDARY SURVEY.

LEGEND

- PROPERTY BOUNDARY
 - - - - - BRL — BUILDING RESTRICTION LINE
 ——— PROPOSED STRUCTURE
 ——— EXISTING CONTOUR — PGATLAS 2 FT (2023), NAVD83
 - - - - - STREET CENTRELIN
 ——— PROPOSED PAVEMENT — DRIVEWAY / WALK
 - - - - - EASEMENT

PRINCE GEORGE'S COUNTY SOIL CONSERVATION DISTRICT APPROVAL
 EROSION CONTROL, GRADING, SOILS & DRAINAGE

SIGNATURE _____ DATE _____

DPIE SITE/ROAD PLAN REVIEW DIVISION APPROVAL _____

SIGNATURE _____ DATE _____


REVISION

— none —

SOLB TABLE					
USDA NRCS SLOUGRO — required by PGC Code Sec 30.130(a)(1)					
MAP UNIT	MAP UNIT NAME	K-FACTOR	HYDRIC	HYD. GROUP	DRAINAGE CLASS
AAB	Adelphi ss Aquas, 0 to 5 percent slopes complex	37	No	C	Moderately well drained
AB	Adelphi Aquas complex, 0 to 2 percent slopes	43	No	D	Very poorly drained
ABA	Adelphi-Aquas complex, 0 to 2 percent slopes	37	No	C	Moderately well drained
ADA	Adelphi-Hondol complex, 0 to 2 percent slopes	24	No	B/D	Somewhat poorly drained
AD	Adelphi-Hondol complex, 0 to 2 percent slopes	37	No	C	Moderately well drained
ADB	Adelphi-Hondol complex, 0 to 5 percent slopes	24	No	B/D	Somewhat poorly drained
ADH	Adelphi-Hondol complex, 0 to 5 percent slopes	37	No	C	Moderately well drained
ADH	Adelphi-Hondol complex, 0 to 5 percent slopes	24	No	B/D	Somewhat poorly drained

SOURCE AND ACCURACY
Parcel boundary — jurisdiction gis — Prince George's County / M-NCPPC — PGAtlas Property — level 1
Existing contours — Prince George's County / M-NCPPC — PGAtlas — level 1
Contours: PGAtlas Elevation/MapServer/1 — Contour - 2 Ft (2023), 2 ft interval, NAVD88 (feet)

GRAPHIC SCALE — 1" = 20'

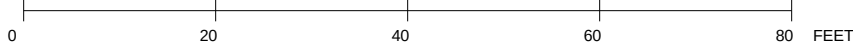

KEALEE

design, build, deliver

PROJECT
1005 Rollins Ave

ADDRESS
1005 Rollins Ave

JURISDICTION
prince georges md

ZONE
RSF-65

SHEET
C-500 — Utility Plan

SCALE
1" = 20'

STATUS
PRELIMINARY

SHEET NO.
4 OF 5

COORDINATES
EPSG:2248

H: NAD83

V: NAVD83 (feet)

PROFESSIONAL RESPONSIBILITY

Maryland Professional Engineer

certified utility design

SEAL AND SIGNATURE

All content on this sheet falls within one professional scope.

SITE DATA

ZONE RSF-65

TAX / PARCEL ID 34854

GROSS LOT AREA 9,596 SF

LOT FRONTAGE 45' MIN 65.07'

SETBACKS REQUIRED PROVIDED

FRONT YARD 25' 25'

SIDE YARD 8' 8'

REAR YARD 30' 30'

COVERAGE MAX PROPOSED

LOT COVERAGE 35% 17.1%

BUILDING FOOTPRINT — 1,640 SF

DATUM

HORIZONTAL EPSG:2248 NAD83

VERTICAL NAVD83 (feet)

SITE ANALYSIS

1. Gross tract area 9,596 SF

2. Area of dwelling 1,640 SF

3. Wooded area NOT ESTABLISHED

4. Floodplain area NOT ESTABLISHED

5. Net tract area 9,596 SF

6. TOTAL AREA DISTURBED NOT QUANTIFIED

SEQUENCE OF CONSTRUCTION

1. Pre-construction meeting 1 DAY

2. Obtain necessary permits 2 DAYS

3. Notify Miss Utility at 811 at least 48 hours prior to any excavation 1 DAY

4. Construct stabilized construction entrance and perimeter sidewalk control 2 DAYS

5. Rough grade, construct dwelling, utilities and driveway 12 MONTHS

6. Fine grade and stabilize all disturbed areas 1 DAY

7. Remove sediment control devices when written permission has been granted 1 DAY

TOTAL ESTIMATED TIME OF CONSTRUCTION: 12 MONTHS

GENERAL NOTES

1. CONTRACTOR SHALL CONTACT MISS UTILITY AT 811 A MINIMUM OF 48 HOURS PRIOR TO ANY EXCAVATION.

2. ALL EXISTING AND PROPOSED UTILITIES SHOWN PER PGC CODE SEC. 30-106.

3. PROPOSED GRADE SHOWN SOLID. EXISTING GRADE SHOWN DASHED.

4. ROUGH EARTHWORK GRADES AND UTILITY ELEVATIONS SHOWN TO TENTHS OF A FOOT.

5. BOUNDARY SHOWN IS COMPILED JURISDICTION GIS, NOT A BOUNDARY SURVEY.

LEGEND

PROPERTY BOUNDARY

BRL — BUILDING RESTRICTION LINE

PROPOSED STRUCTURE

EXISTING CONTOUR — PGATLAS 2 FT (2023), NAVD83

STREET CENTRELINE

PROPOSED PAVEMENT — DRIVEWAY / WALK

EASEMENT

PRINCE GEORGE'S COUNTY SOIL CONSERVATION DISTRICT APPROVAL

SEDIMENT CONTROL, GRADING, SOILS & DRAINAGE

SIGNATURE DATE

DPE SITEROAD PLAN REVIEW DIVISION APPROVAL

SIGNATURE DATE

REVISIONS

NOTE

SOILS TABLE

USDA NRCS SSURGO — required by POC Code Sec. 30-130(a)(13)

MAP UNIT	MAP UNIT NAME	K-FACTOR	HYDRIC	HYD. GROUP	DRAINAGE CLASS
AaB	Adelphia silt loam, 2 to 5 percent slopes complex	37	No	C	Moderately well drained
ACA	Adelphia Aquasol complex, 0 to 2 percent slopes	43	No	D	Somewhat poorly drained
ACB	Adelphia Aquasol complex, 0 to 2 percent slopes	37	No	C	Moderately well drained
ADA	Adelphia Haindel complex, 0 to 2 percent slopes	24	No	BD	Somewhat poorly drained
ADB	Adelphia Haindel complex, 0 to 2 percent slopes	37	No	C	Moderately well drained
AaB	Adelphia Haindel complex, 2 to 5 percent slopes	24	No	BD	Somewhat poorly drained
AaB	Adelphia Haindel complex, 2 to 5 percent slopes	37	No	C	Moderately well drained
AaC	Adelphia Haindel complex, 5 to 10 percent slopes	24	No	BD	Somewhat poorly drained

SOURCE AND ACCURACY

Parcel boundary — Jurisdiction gis — Prince George's County / M-ACPPC — PGAtlas Property — level 1

Existing contours — Prince George's County / M-NCPPC — PGAtlas — level 1

Contours: PGAtlas ElevationMapServer1 — Contour - 2 Ft (2023), 2 ft interval, NAVD83 (feet)

GRAPHIC SCALE — 1" = 20'

0 20 40 60 80 FEET

KEALEE

design, build, deliver

PROJECT
1005 Rollins Ave

ADDRESS
1005 Rollins Ave

JURISDICTION
prince georges md

ZONE
RSF-65

SHEET
L-100 — Landscape and Tree Canopy Plan

SCALE
1" = 20'

STATUS
PRELIMINARY

SHEET NO.
5 OF 5

COORDINATES
EPSG:2248

H: NAD83

V: NAVD83 (feet)

PROFESSIONAL RESPONSIBILITY

Qualified Environmental Professional

certified tree_conservation

SEAL AND SIGNATURE

All content on this sheet falls within one professional scope.

SITE DATA

ZONE RSF-65

TAX / PARCEL ID 34854

GROSS LOT AREA 9,596 SF 0.220 AC

LOT FRONTAGE 45' MIN 65.07'

SETBACKS REQUIRED PROVIDED

FRONT YARD 25' 25'

SIDE YARD 8' 8'

REAR YARD 30' 30'

COVERAGE MAX PROPOSED

LOT COVERAGE 35% 17.1%

BUILDING FOOTPRINT — 1,640 SF

DATUM

HORIZONTAL EPSG:2248 NAD83

VERTICAL NAVD83 (feet)

SITE ANALYSIS

1. Gross tract area 9,596 SF

2. Area of dwelling 1,640 SF

3. Wooded area NOT ESTABLISHED

4. Floodplain area NOT ESTABLISHED

5. Net tract area 9,596 SF

6. TOTAL AREA DISTURBED NOT QUANTIFIED

SEQUENCE OF CONSTRUCTION

1. Pre-construction meeting 1 DAY

2. Obtain necessary permits 2 DAYS

3. Notify Miss Utility at 811 at least 48 hours prior to any excavation 1 DAY

4. Construct stabilized construction entrance and perimeter sidewalk control 2 DAYS

5. Rough grade, construct dwelling, utilities and driveway 12 MONTHS

6. Fine grade and stabilize all disturbed areas 1 DAY

7. Remove sediment control device when written permission has been granted 1 DAY

TOTAL ESTIMATED TIME OF CONSTRUCTION: 12 MONTHS

GENERAL NOTES

1. CONTRACTOR SHALL CONTACT MISS UTILITY AT 811 A MINIMUM OF 48 HOURS PRIOR TO ANY EXCAVATION.

2. ALL EXISTING AND PROPOSED UTILITIES SHOWN PER PGC CODE SEC. 30-106.

3. PROPOSED GRADE SHOWN SOLID. EXISTING GRADE SHOWN DASHED.

4. ROUGH EARTHWORK GRADES AND UTILITY ELEVATIONS SHOWN TO TENTHS OF A FOOT.

5. BOUNDARY SHOWN IS COMPILED JURISDICTION GIS, NOT A BOUNDARY SURVEY.

LEGEND

PROPERTY BOUNDARY

BRL — BUILDING RESTRICTION LINE

PROPOSED STRUCTURE

EXISTING CONTOUR — PGATLAS 2 FT (2023), NAVD83

STREET CENTRELINE

PROPOSED PAVEMENT — DRIVEWAY / WALK

EASEMENT

PRINCE GEORGE'S COUNTY SOIL CONSERVATION DISTRICT APPROVAL

SEDIMENT CONTROL, GRADING, SOILS & DRAINAGE

SIGNATURE DATE

DPE SITEROAD PLAN REVIEW DIVISION APPROVAL

SIGNATURE DATE

REVISIONS

NOTE

SOILS TABLE

USDA NRCS SSURGO — required by POC Code Sec. 30-130(a)(13)

MAP UNIT	MAP UNIT NAME	K-FACTOR	HYDRIC	HYD. GROUP	DRAINAGE CLASS
AaB	Adelphia silt loam, 2 to 5 percent slopes complex	37	No	C	Moderately well drained
ACA	Adelphia Aquasol complex, 0 to 2 percent slopes	43	No	D	Somewhat poorly drained
ACB	Adelphia Aquasol complex, 0 to 2 percent slopes	37	No	C	Moderately well drained
ADA	Adelphia Haindel complex, 0 to 2 percent slopes	24	No	BD	Somewhat poorly drained
ADB	Adelphia Haindel complex, 0 to 2 percent slopes	37	No	C	Moderately well drained
AIB	Adelphia Haindel complex, 2 to 5 percent slopes	24	No	BD	Somewhat poorly drained
AIB	Adelphia Haindel complex, 2 to 5 percent slopes	37	No	C	Moderately well drained
AIC	Adelphia Haindel complex, 5 to 10 percent slopes	24	No	BD	Somewhat poorly drained

SOURCE AND ACCURACY

Parcel boundary — Jurisdiction gis — Prince George's County / M-ACPPC — PGAtlas Property — level 1

Existing contours — Prince George's County / M-NCPPC — PGAtlas — level 1

Contours: PGAtlas ElevationMapServer1 — Contour = 2 Ft (2023), 2 ft interval, NAVD83 (feet)

GRAPHIC SCALE — 1" = 20'

0 20 40 60 80 FEET